



(주) 동심원건축사사무소

TEL : 02)3452-0597
FAX : 02)3452-0598

설계명 PROJECT TITLE
동작구 상도동
SH매입임대주택 신축공사

주 기 NOTE

NO.	DATE	REVISION	DRAWN	APP.
1				
2				
3				

설 계	DRAWN	검 토	CHECK
심 사	SUBMIT	승 인	APPROVE

축 척	SCALE
A1	1 /
A3	1 / NONE

일 자	DATE

설계번호	PROJECT NO.

도면파일명	DWG. FILE NAME

도면번호	SHEET NO.
	A - 003

도면명	SUBJECT TITLE

조감도



(주) 동심원건축사사무소

TEL : 02)3452-0597
FAX : 02)3452-0598

설계명 PROJECT TITLE
동작구 상도동
SH매입임대주택 신축공사

주 기 NOTE

NO. DATE REVISION DRAWN APP.

1				
2				
3				

설 계 DRAWN 검토 CHECK

심 사 SUBMIT 승인 APPROVE

축 척 SCALE

A1 1 / 60
A3 1 / 120

일 자 DATE

설계번호 PROJECT NO.

도면파일명 DWG. FILE NAME


도면번호 SHEET NO.
A - 005

도면명 SUBJECT TITLE


대지종단면도

101동, 102동 대지 종단면도

축척=1/120

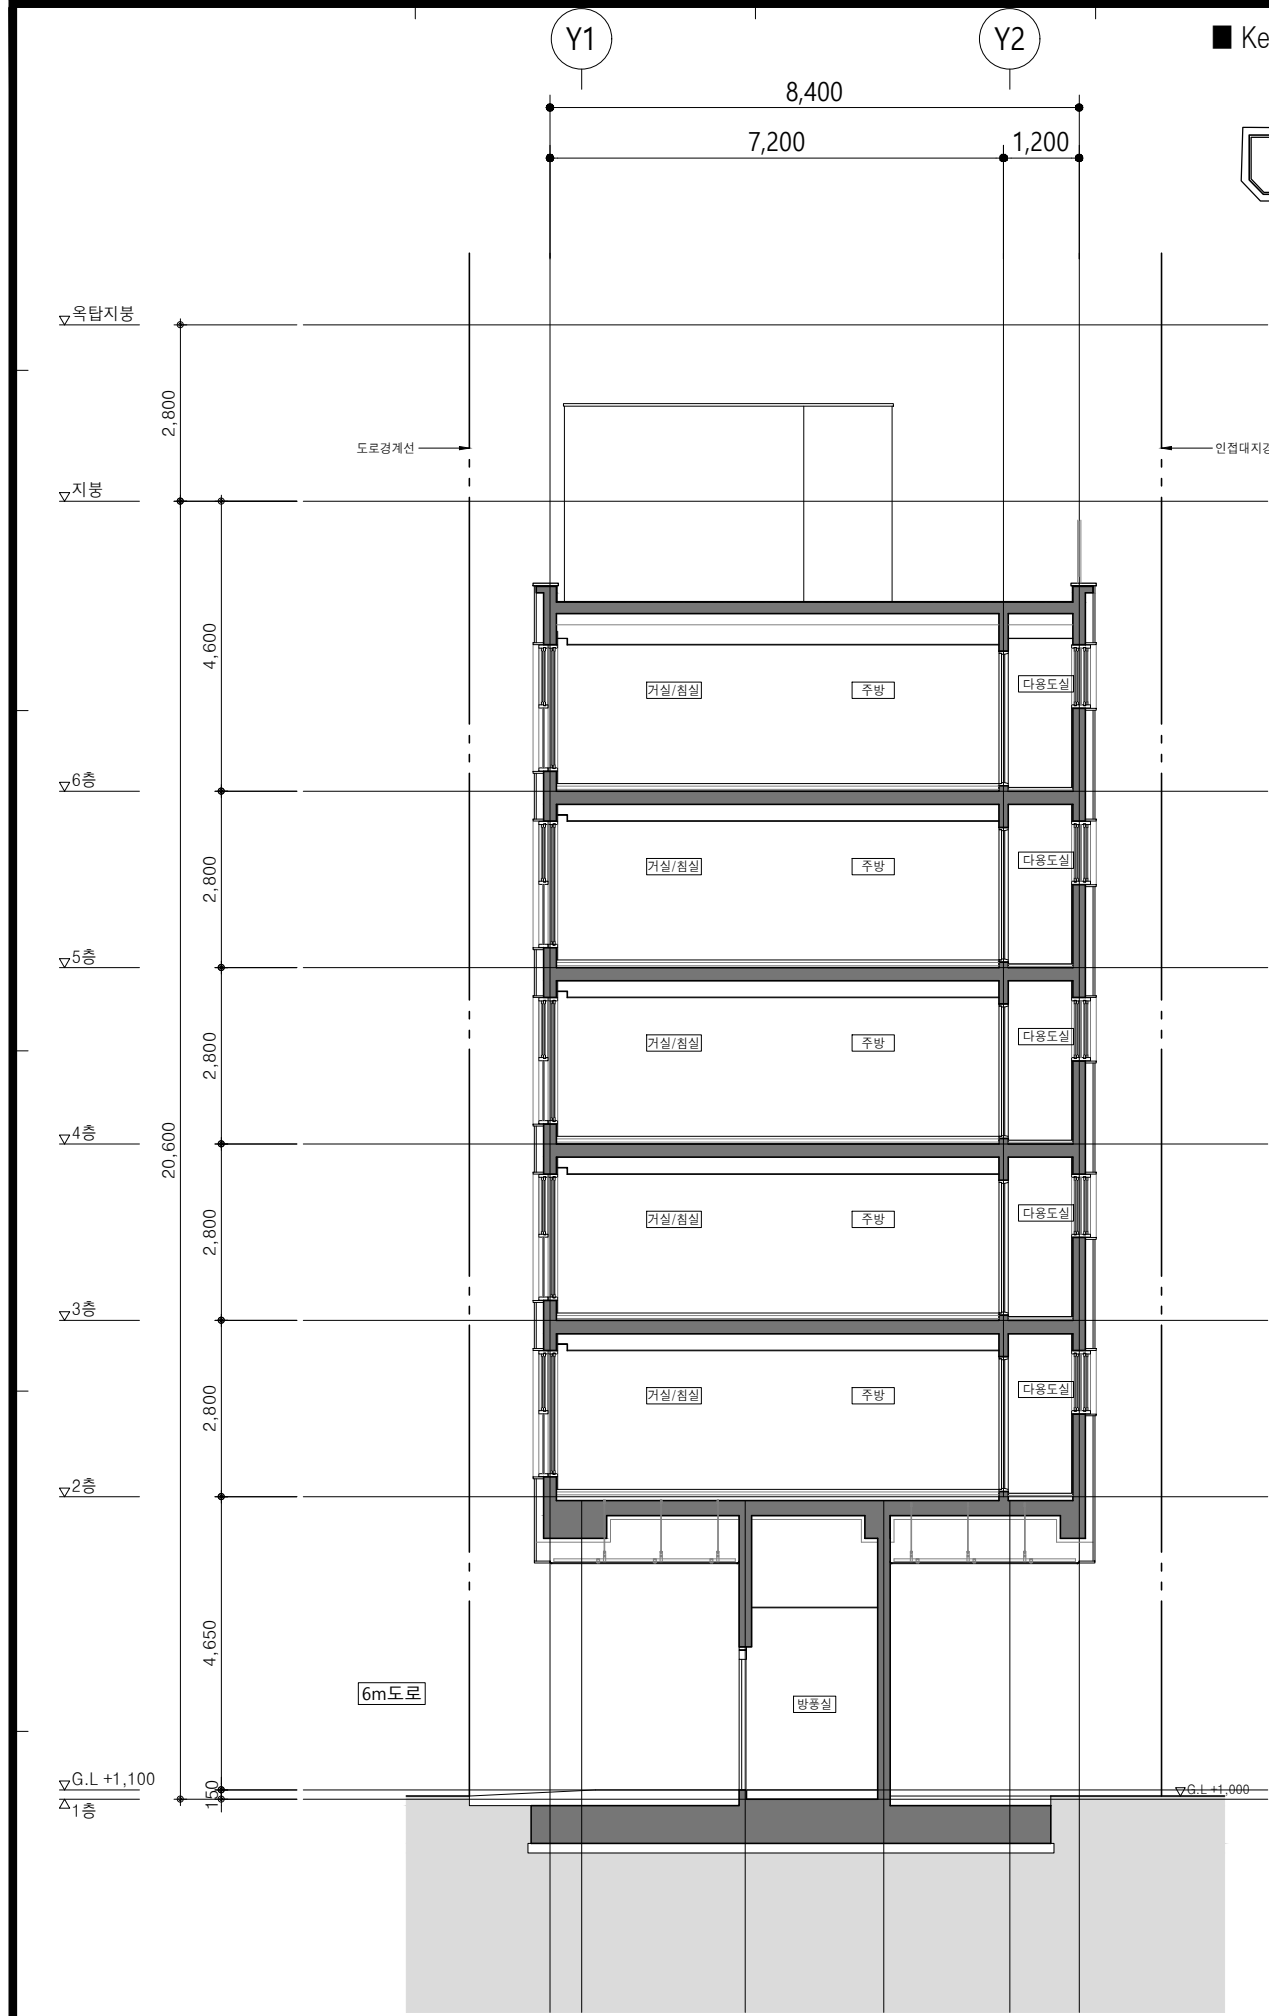

1 101동 대지형단면도
축척=1/120

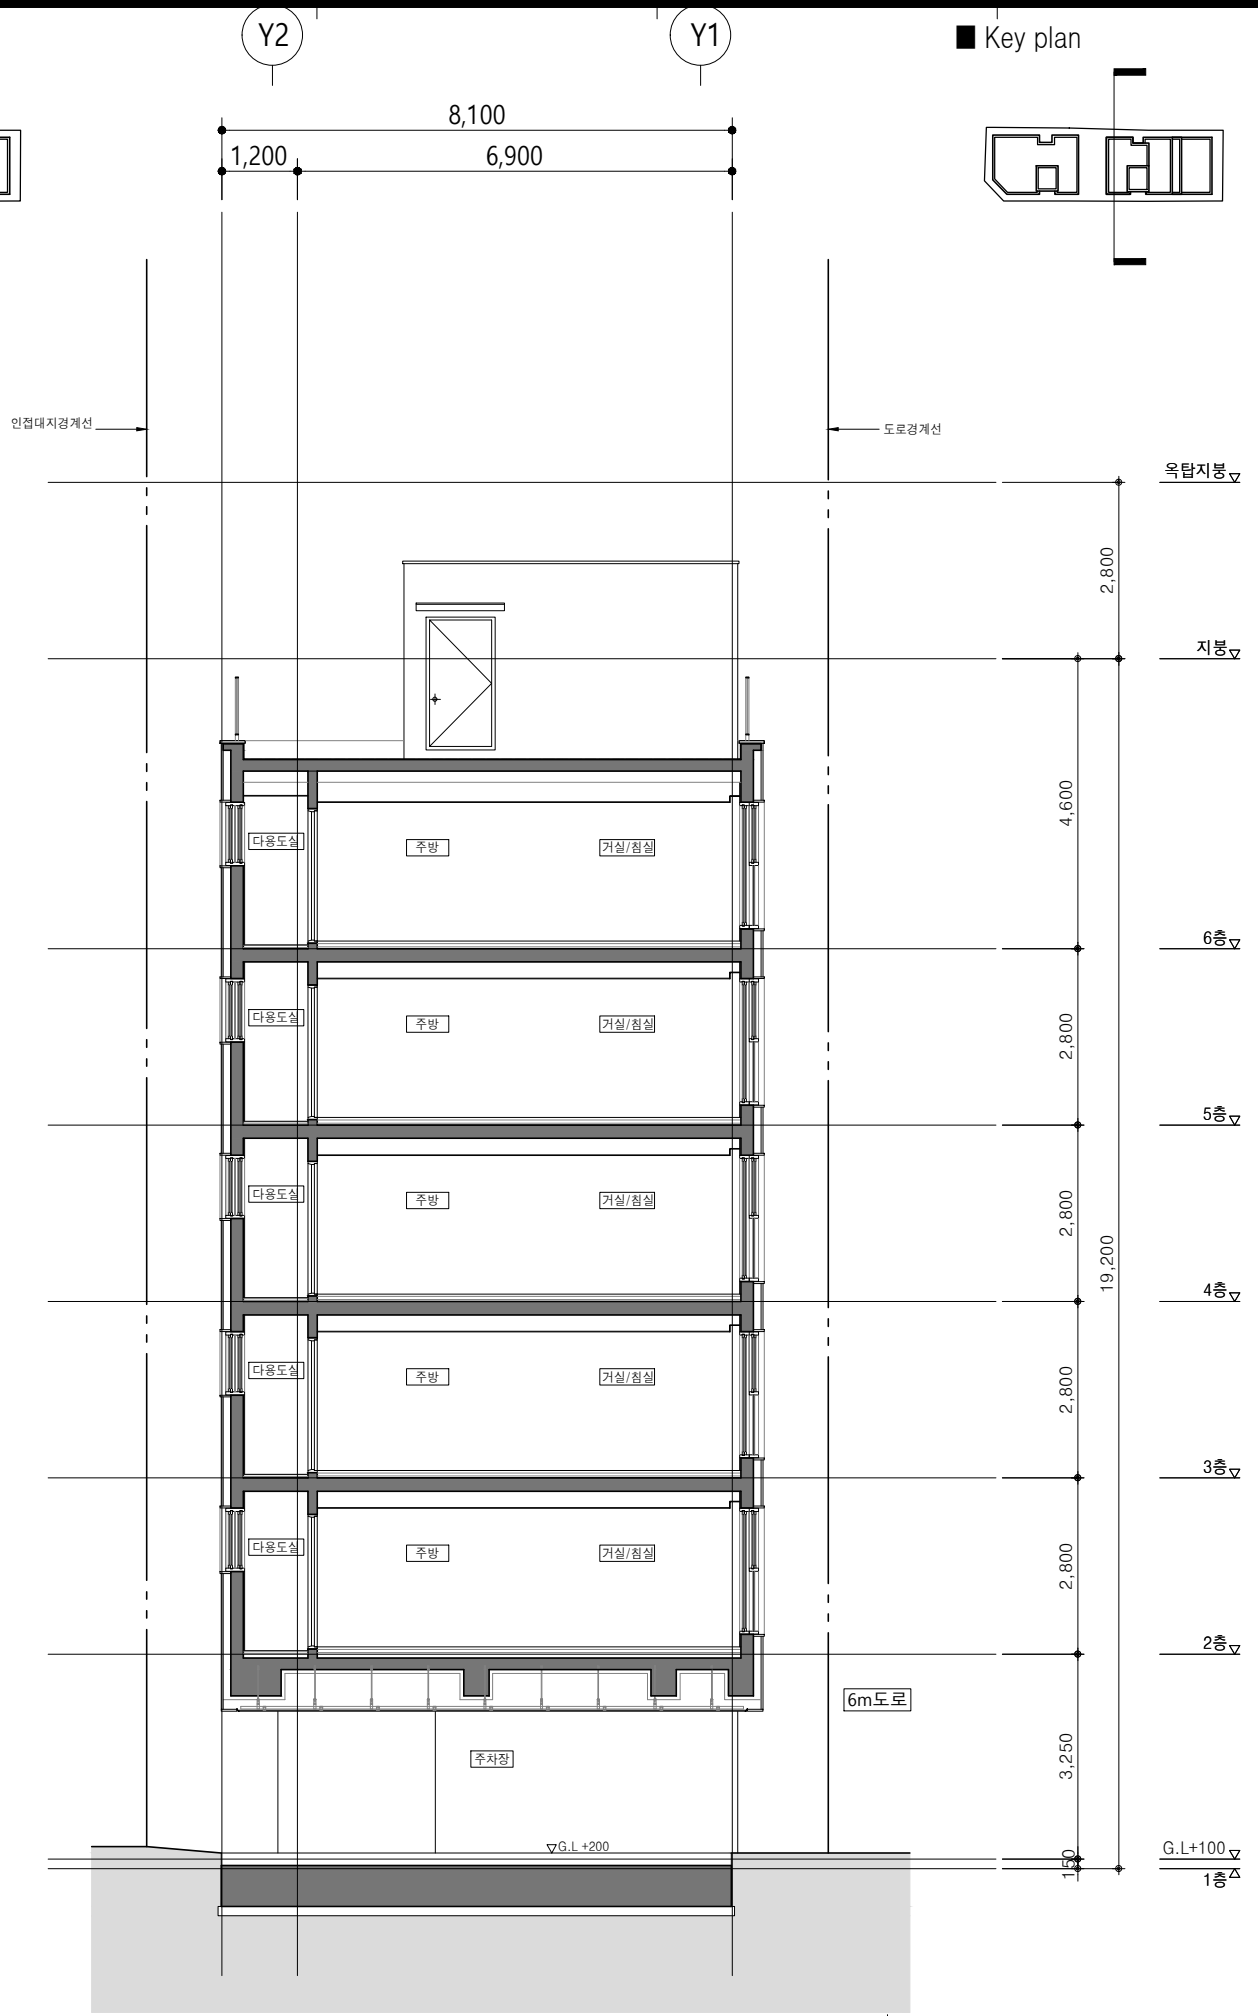

A 102동 대지형단면도
축척=1/120



(주) 동심원건축사사무소

TEL : 02)3452-0597
FAX : 02)3452-0598

설계명 PROJECT TITLE
동작구 상도동
SH매입임대주택 신축공사

주 기 NOTE

NO. DATE REVISION DRAWN APP.

1				
2				
3				

설 계 DRAWN 검토 CHECK

심 사 SUBMIT 승인 APPROVE

축 척 SCALE

A1	1 / 60
A3	1 / 120

일 자 DATE

설계번호 PROJECT NO.


도면파일명 DWG. FILE NAME

도면번호 SHEET NO.

A - 006

도면명 SUBJECT TITLE

대지형단면도

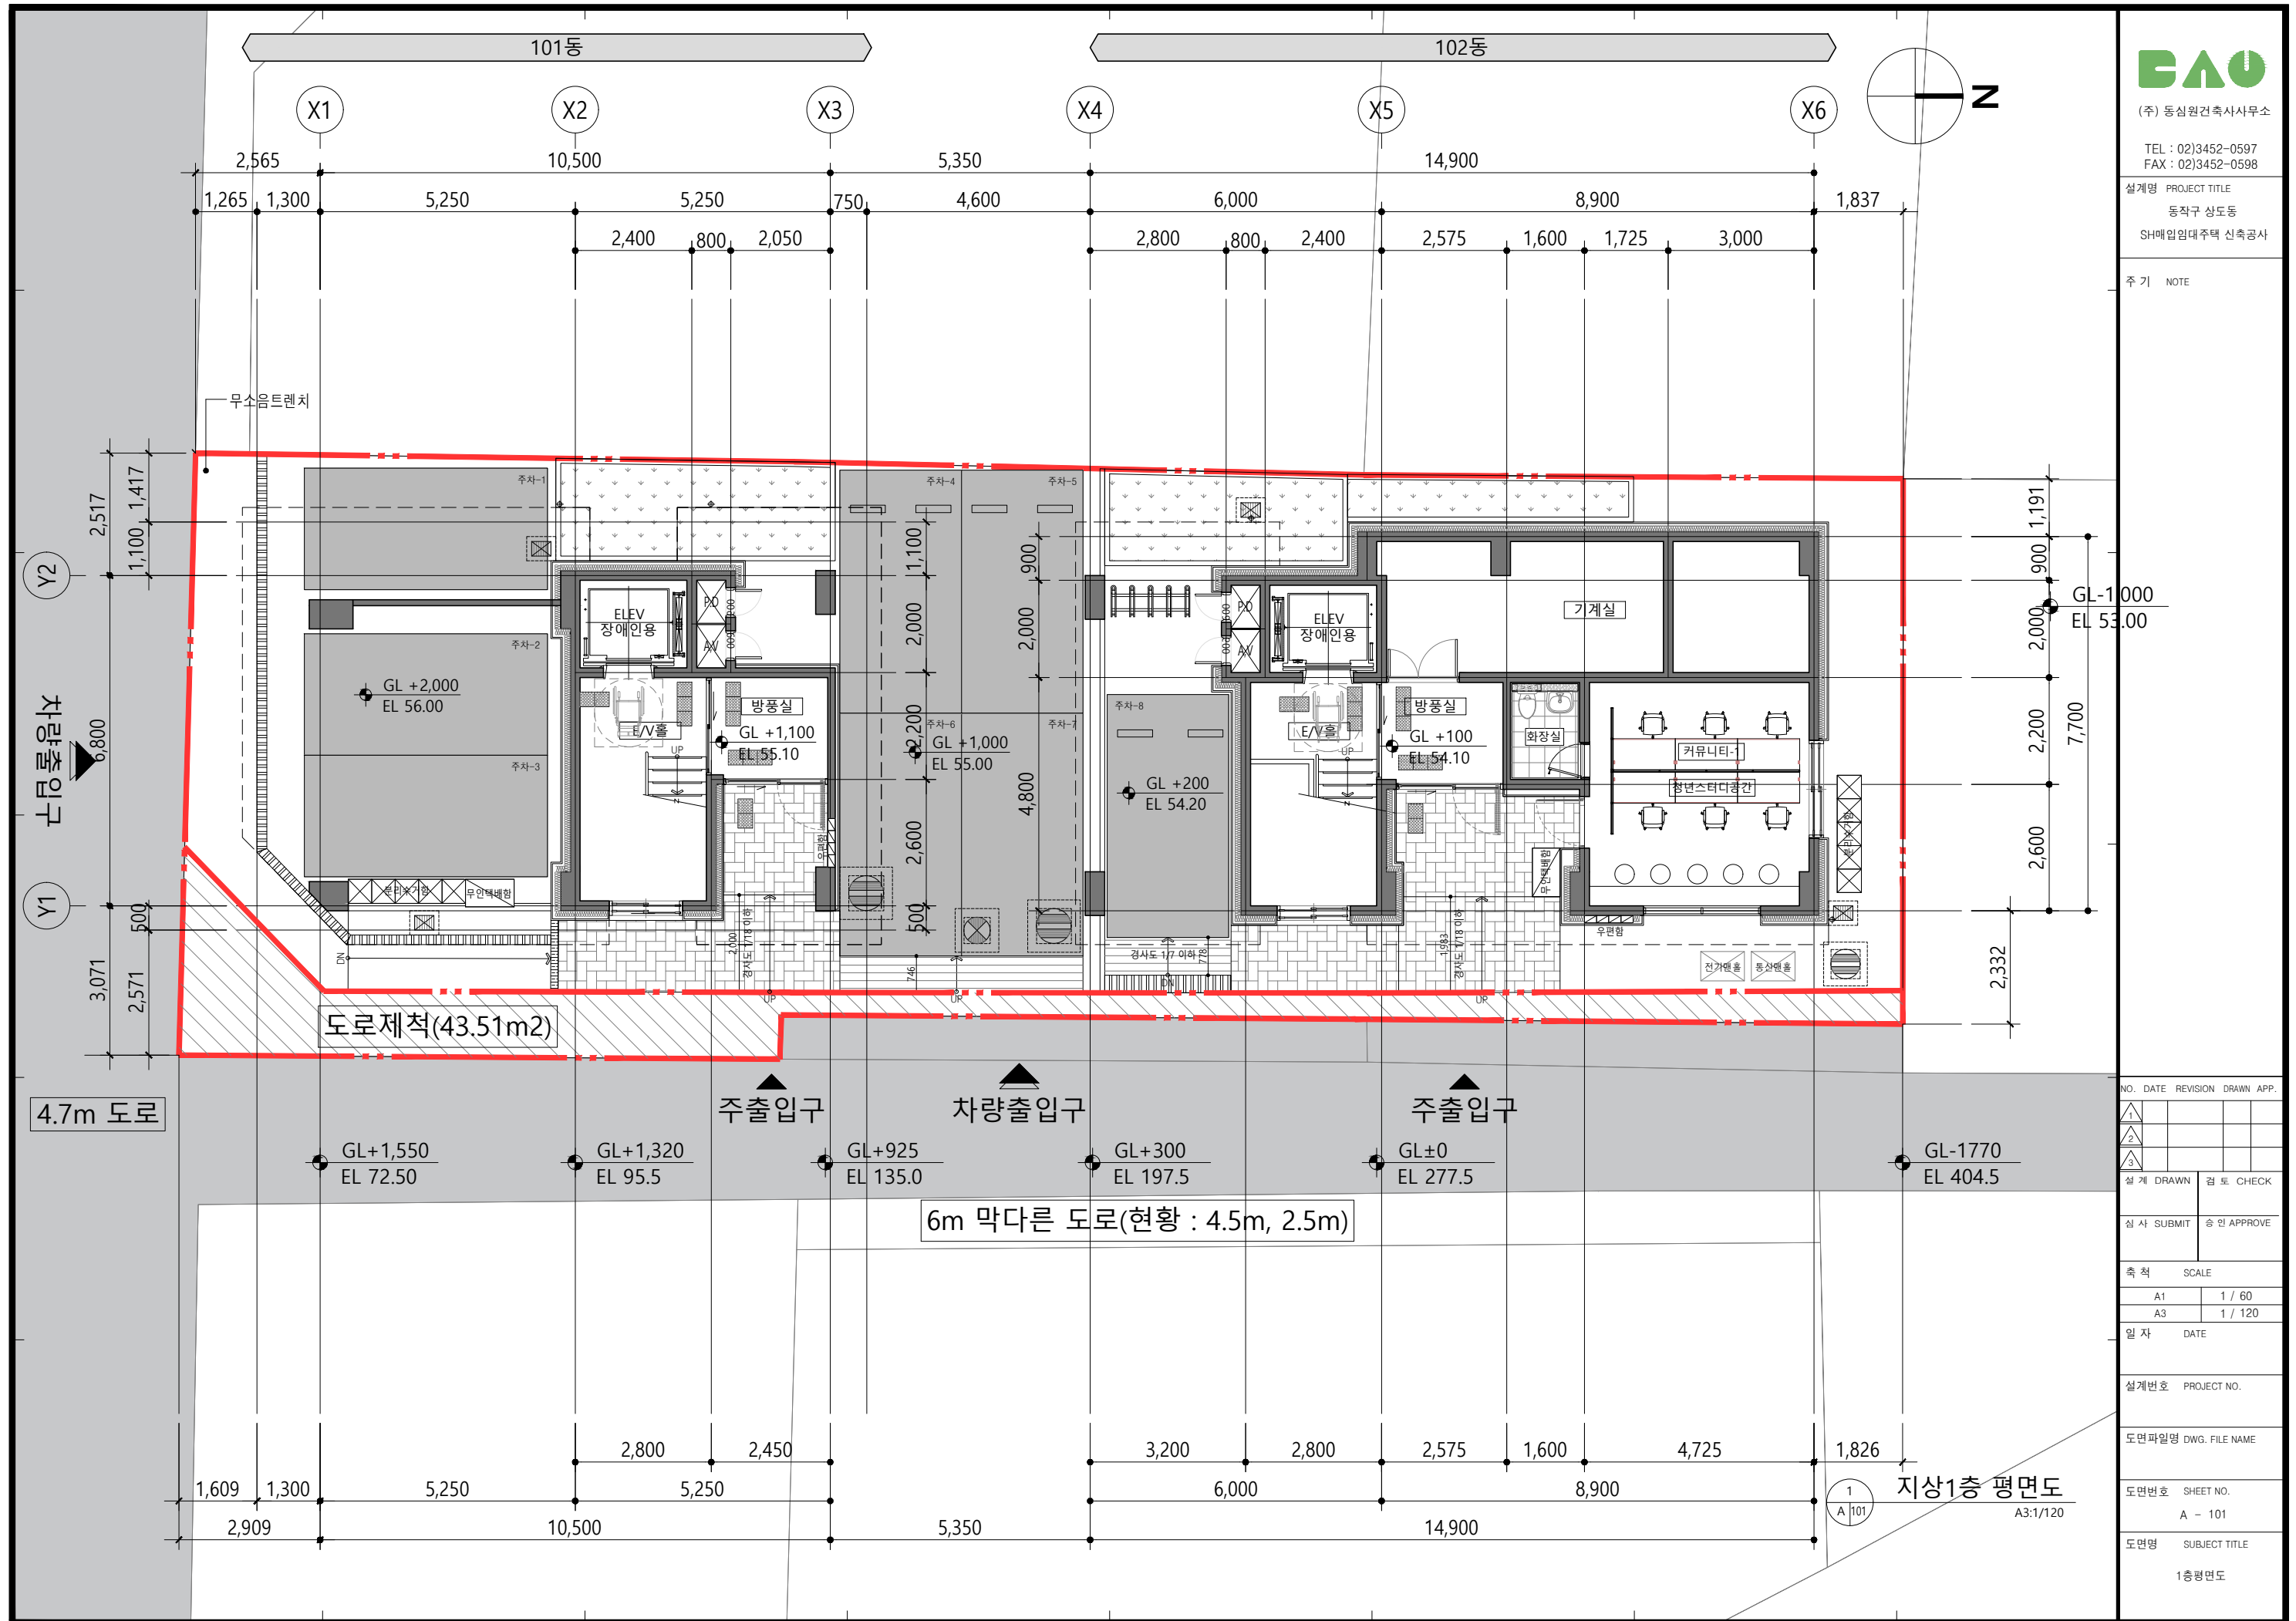

(주) 동심원건축사사무소

TEL : 02)3452-0597
FAX : 02)3452-0598

설계명 PROJECT TITLE

동작구 상도동

SH매입임대주택 신축공사

주 기 NOTE

NO. DATE REVISION DRAWN APP.

1				
2				
3				

설 계 DRAWN 검토 CHECK

심 사 SUBMIT 승인 APPROVE

축 척 SCALE

A1	1 / 60
A3	1 / 120

일 자 DATE

설계번호 PROJECT NO.

도면파일명 DWG. FILE NAME

도면번호 SHEET NO.

A - 101

도면명 SUBJECT TITLE

1층평면도



■ 빌트인설치 내역

구분	세탁기	냉장고	에어컨 (벽걸이)	전자 레인지
설치 유무	○	○	○	○

* 냉장고 상부 전자레인지 / 쿡탑 하부 세탁기 설치

지상2,3층 평면도
A3:1/120



(주) 동심원건축사사무소

TEL : 02)3452-0597
FAX : 02)3452-0598

설계명 PROJECT TITLE

동작구 상도동

SH매입임대주택 신축공사

주 기 NOTE

NO. DATE REVISION DRAWN APP.

1				
2				
3				

설 계 DRAWN 검토 CHECK

심 사 SUBMIT 승인 APPROVE

축 척 SCALE

A1	1 / 60
A3	1 / 120

일 자 DATE

설계번호 PROJECT NO.

도면파일명 DWG. FILE NAME

도면번호 SHEET NO.

A - 102

도면명 SUBJECT TITLE

2,3층평면도



1
A 지상5층 평면도
A3:1/120



(주) 동심원건축사사무소

TEL : 02)3452-0597
FAX : 02)3452-0598

설계명 PROJECT TITLE

동작구 상도동

SH매입임대주택 신축공사

주 기 NOTE

NO. DATE REVISION DRAWN APP.

1				
2				
3				

설 계 DRAWN 검토 CHECK

심 사 SUBMIT 승인 APPROVE

축 척 SCALE

A1	1 / 60
A3	1 / 120

일 자 DATE

설계번호 PROJECT NO.

도면파일명 DWG. FILE NAME

도면번호 SHEET NO.
A - 104

도면명 SUBJECT TITLE
5층평면도



■ 빌트인설치 내역

구분	세탁기	냉장고	에어컨 (벽걸이)	전자 레인지
설치 유무	○	○	○	○

* 냉장고 상부 전자레인지 / 쿡탑 하부 세탁기 설치



지상6층 평면도
A3:1/120



(주) 동심원건축사사무소

TEL : 02)3452-0597
FAX : 02)3452-0598

설계명 PROJECT TITLE

동작구 상도동

SH매입임대주택 신축공사

주 기 NOTE

NO. DATE REVISION DRAWN APP.

1				
2				
3				

설 계 DRAWN 검토 CHECK

심 사 SUBMIT 승인 APPROVE

축 척 SCALE

A1	1 / 60
A3	1 / 120

일 자 DATE

설계번호 PROJECT NO.

도면파일명 DWG. FILE NAME

도면번호 SHEET NO.
A - 105

도면명 SUBJECT TITLE
6층평면도

■ Key plan



(주) 동심원건축사사무소

TEL : 02)3452-0597
FAX : 02)3452-0598

설계명 PROJECT TITLE

동작구 상도동

SH매입임대주택 신축공사

주 기 NOTE



101동 정면도

축척=1/120



102동 정면도

축척=1/120

NO. DATE REVISION DRAWN APP.

1				
2				
3				

설 계 DRAWN 검토 CHECK

심 사 SUBMIT 승인 APPROVE

축 척 SCALE

A1 1 / 60

A3 1 / 120

일 자 DATE

설계번호 PROJECT NO.

도면파일명 DWG. FILE NAME


도면번호 SHEET NO.

A - 301

도면명 SUBJECT TITLE

입면도-1

■ Key plan

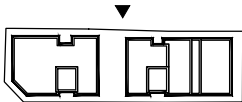

(주) 동심원건축사사무소


TEL : 02)3452-0597
FAX : 02)3452-0598

설계명 PROJECT TITLE

동작구 상도동


SH매입임대주택 신축공사

주 기 NOTE

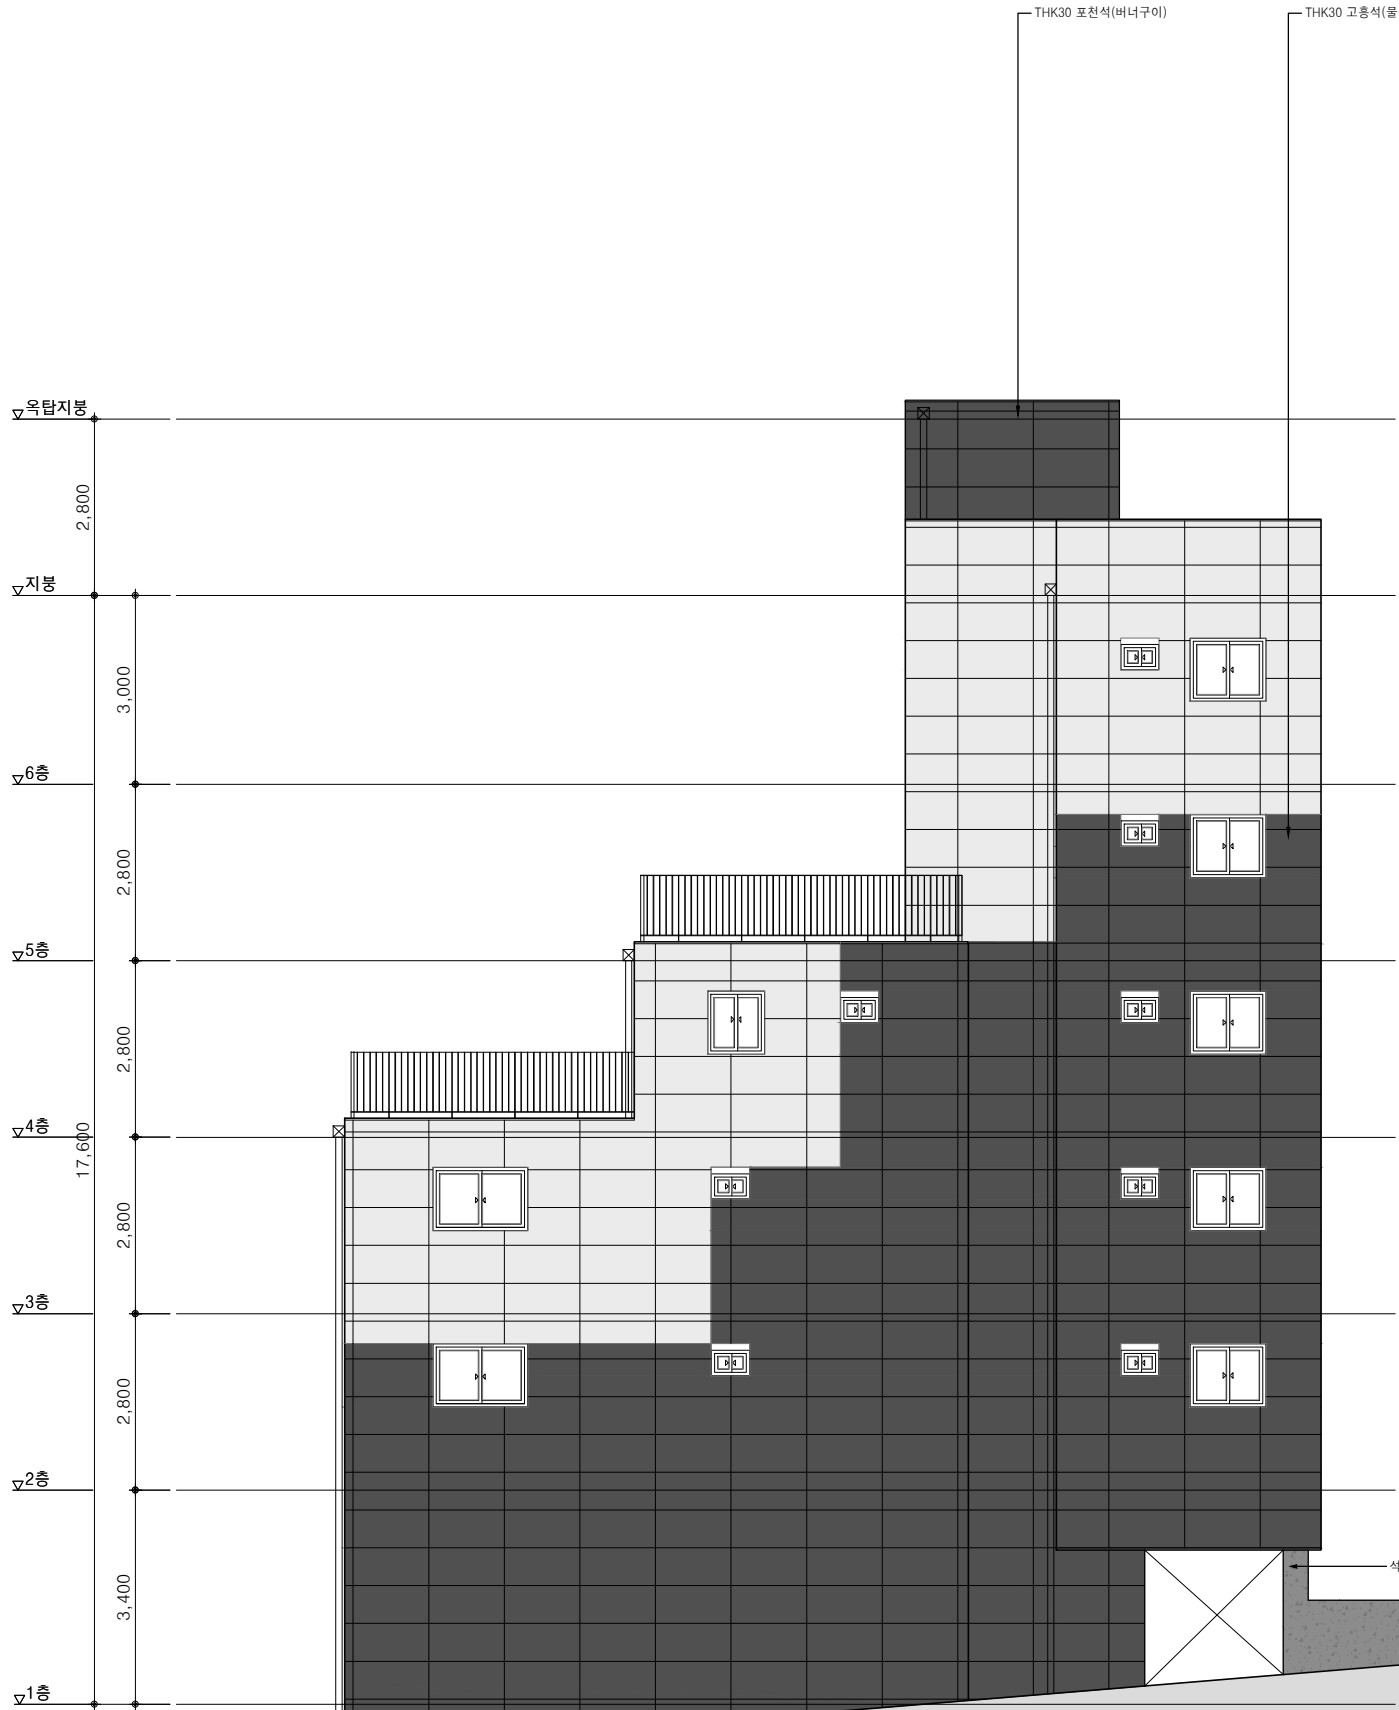

102동 배면도

축척=1/120

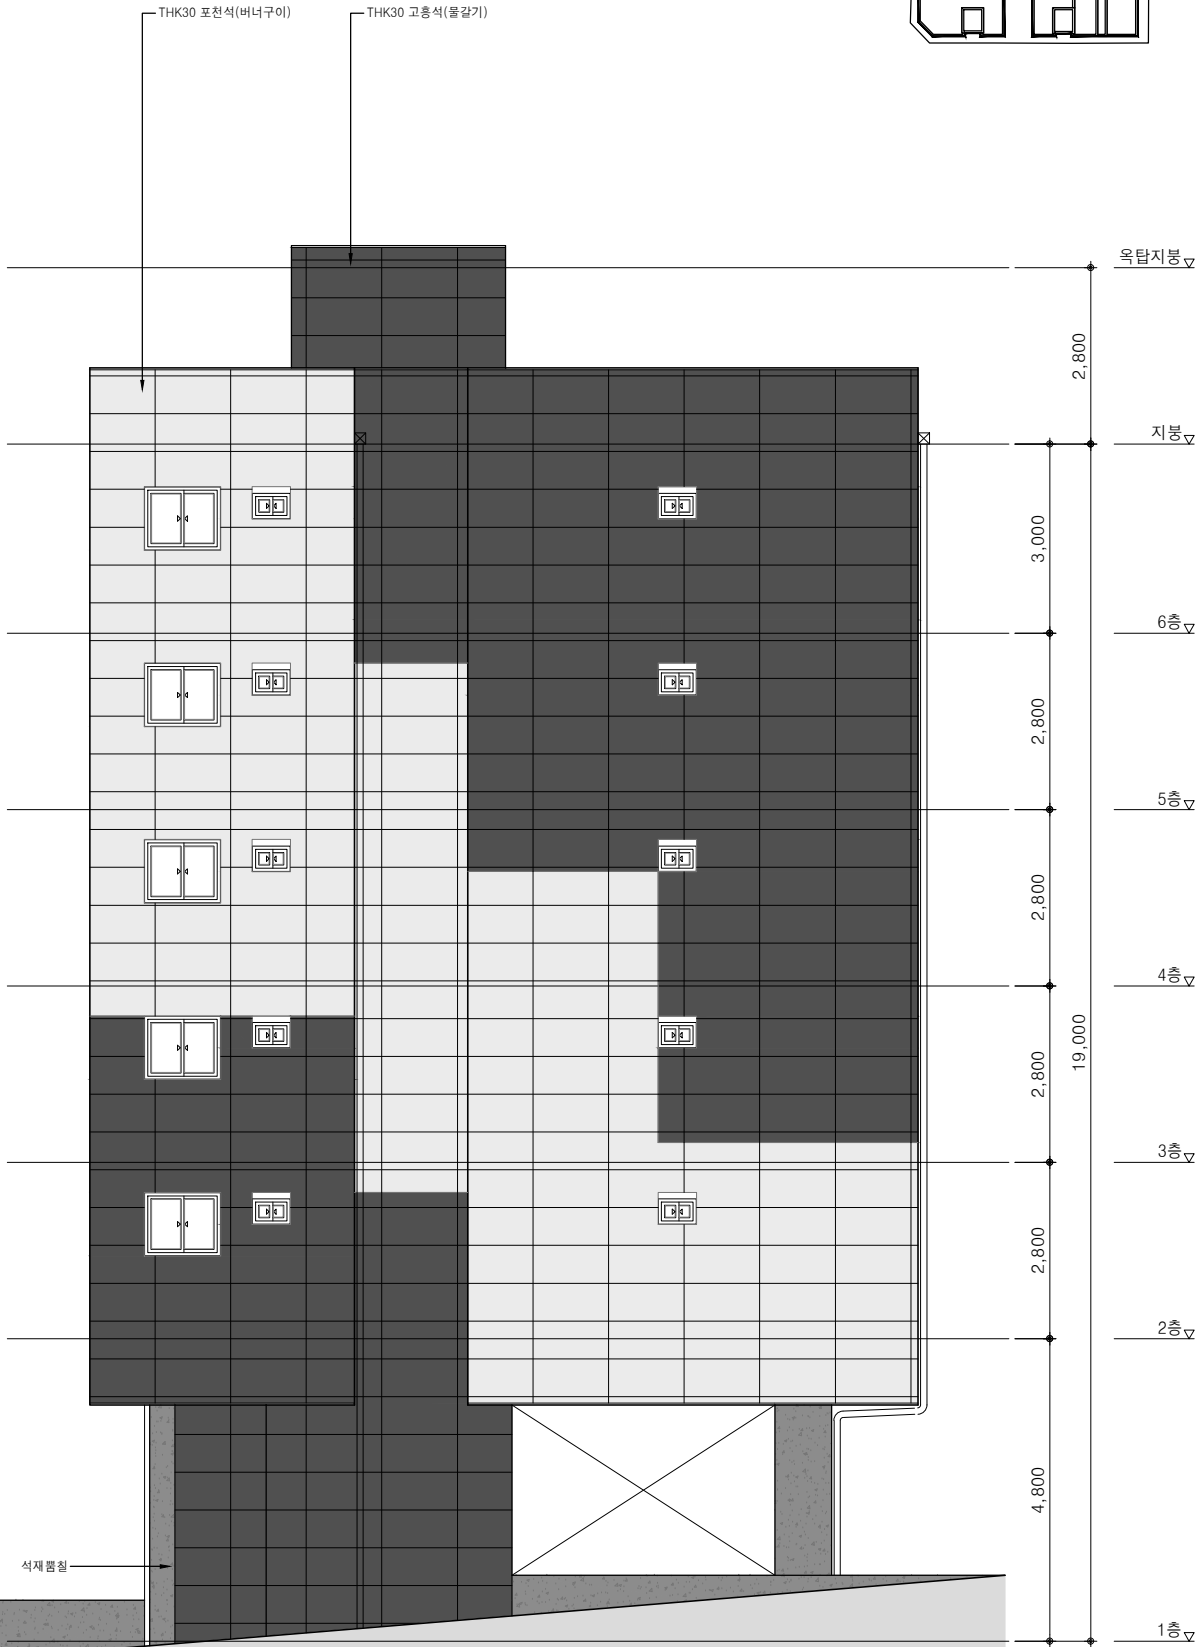

101동 배면도

축척=1/120

NO. DATE REVISION DRAWN APP.

1				
2				
3				

설 계 DRAWN 검토 CHECK

심 사 SUBMIT 승인 APPROVE

축 척 SCALE

A1	1 / 60
A3	1 / 120

일 자 DATE

설계번호 PROJECT NO.

도면파일명 DWG. FILE NAME

도면번호 SHEET NO.

A - 302

도면명 SUBJECT TITLE

입면도-2

■ Key plan



■ Key plan



(주) 동심원건축사사무소

TEL : 02)3452-0597
FAX : 02)3452-0598

설계명 PROJECT TITLE

동작구 상도동

SH매입임대주택 신축공사

주 기 NOTE

NO. DATE REVISION DRAWN APP.

1				
2				
3				

설 계 DRAWN

검 토 CHECK

심 사 SUBMIT

승 인 APPROVE

축 척 SCALE

A1 1 / 60

A3 1 / 120

일 자 DATE

설계번호 PROJECT NO.

도면파일명 DWG. FILE NAME


도면번호 SHEET NO.

A - 303



도면명 SUBJECT TITLE

입면도-3

■ Key plan

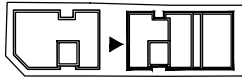

■ Key plan

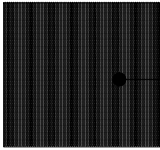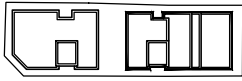

차면시설 설치
(불투명 PVC - 텍산쉬트)

▽ 옥탑지붕

▽ 지붕

▽ 6층

▽ 5층

▽ 4층

▽ 3층

▽ 2층

▽ 1층

THK30 고흥석(물갈기)

석재 폼질



102동 좌측면도

축척=1/120

THK30 고흥석(물갈기)



102동 좌측면도

축척=1/120

2,800

3,000

2,800

2,800

2,800

2,800

3,400

17,600



(주) 동심원건축사사무소

TEL : 02)3452-0597
FAX : 02)3452-0598

설계명 PROJECT TITLE

동작구 상도동

SH매입임대주택 신축공사

주 기 NOTE

NO. DATE REVISION DRAWN APP.

1				
2				
3				

설 계 DRAWN

검 토 CHECK

심 사 SUBMIT

승 인 APPROVE

축 척 SCALE

A1 1 / 60

A3 1 / 120

일 자 DATE

설계번호 PROJECT NO.


도면파일명 DWG. FILE NAME

도면번호 SHEET NO.

A - 304

도면명 SUBJECT TITLE

입면도-4

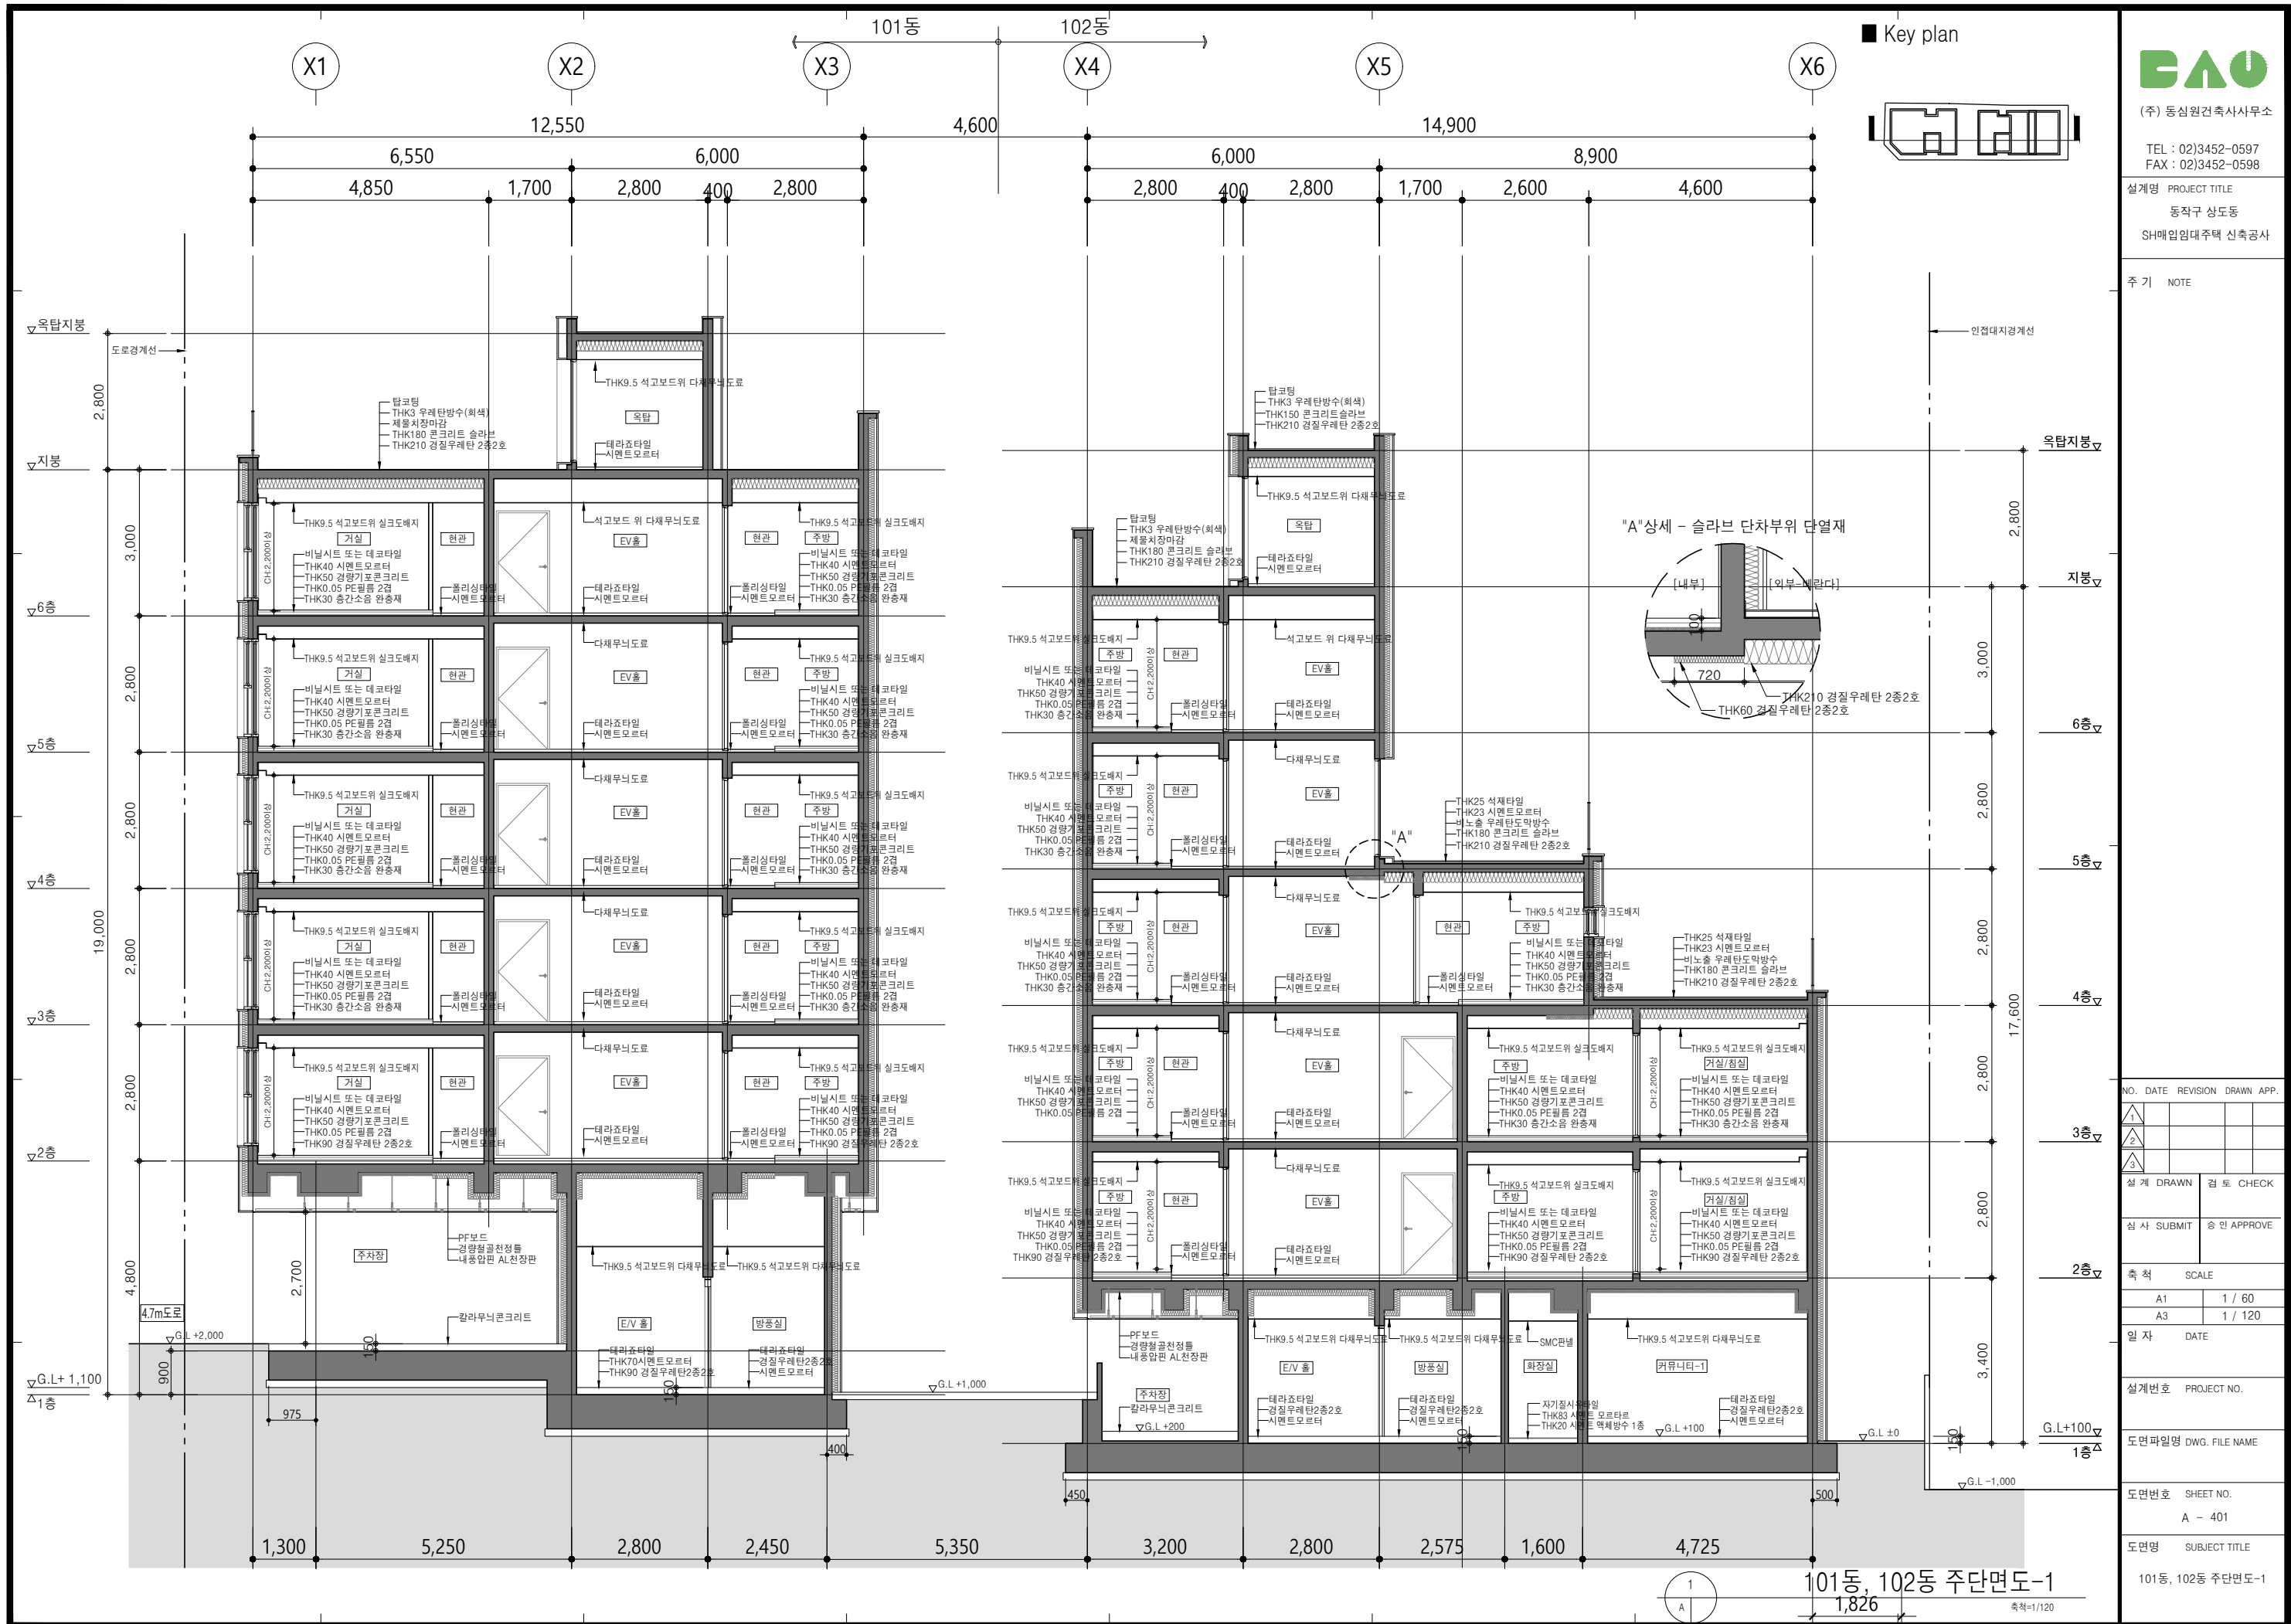

(주) 동심원건축사사무소

TEL : 02)3452-0597
FAX : 02)3452-0598

설계명 PROJECT TITLE

동작구 상도동

SH매입임대주택 신축공사

주 기 NOTE

NO. DATE REVISION DRAWN APP.

1				
2				
3				

설 계 DRAWN

검 토 CHECK

심 사 SUBMIT

승 인 APPROVE

축 척 SCALE

A1	1 / 60
A3	1 / 120

일 자 DATE

설계번호 PROJECT NO.

도면파일명 DWG. FILE NAME

도면번호 SHEET NO.



A - 401

도면명 SUBJECT TITLE

101동, 102동 주단면도-1

축척=1/120



■ Key plan

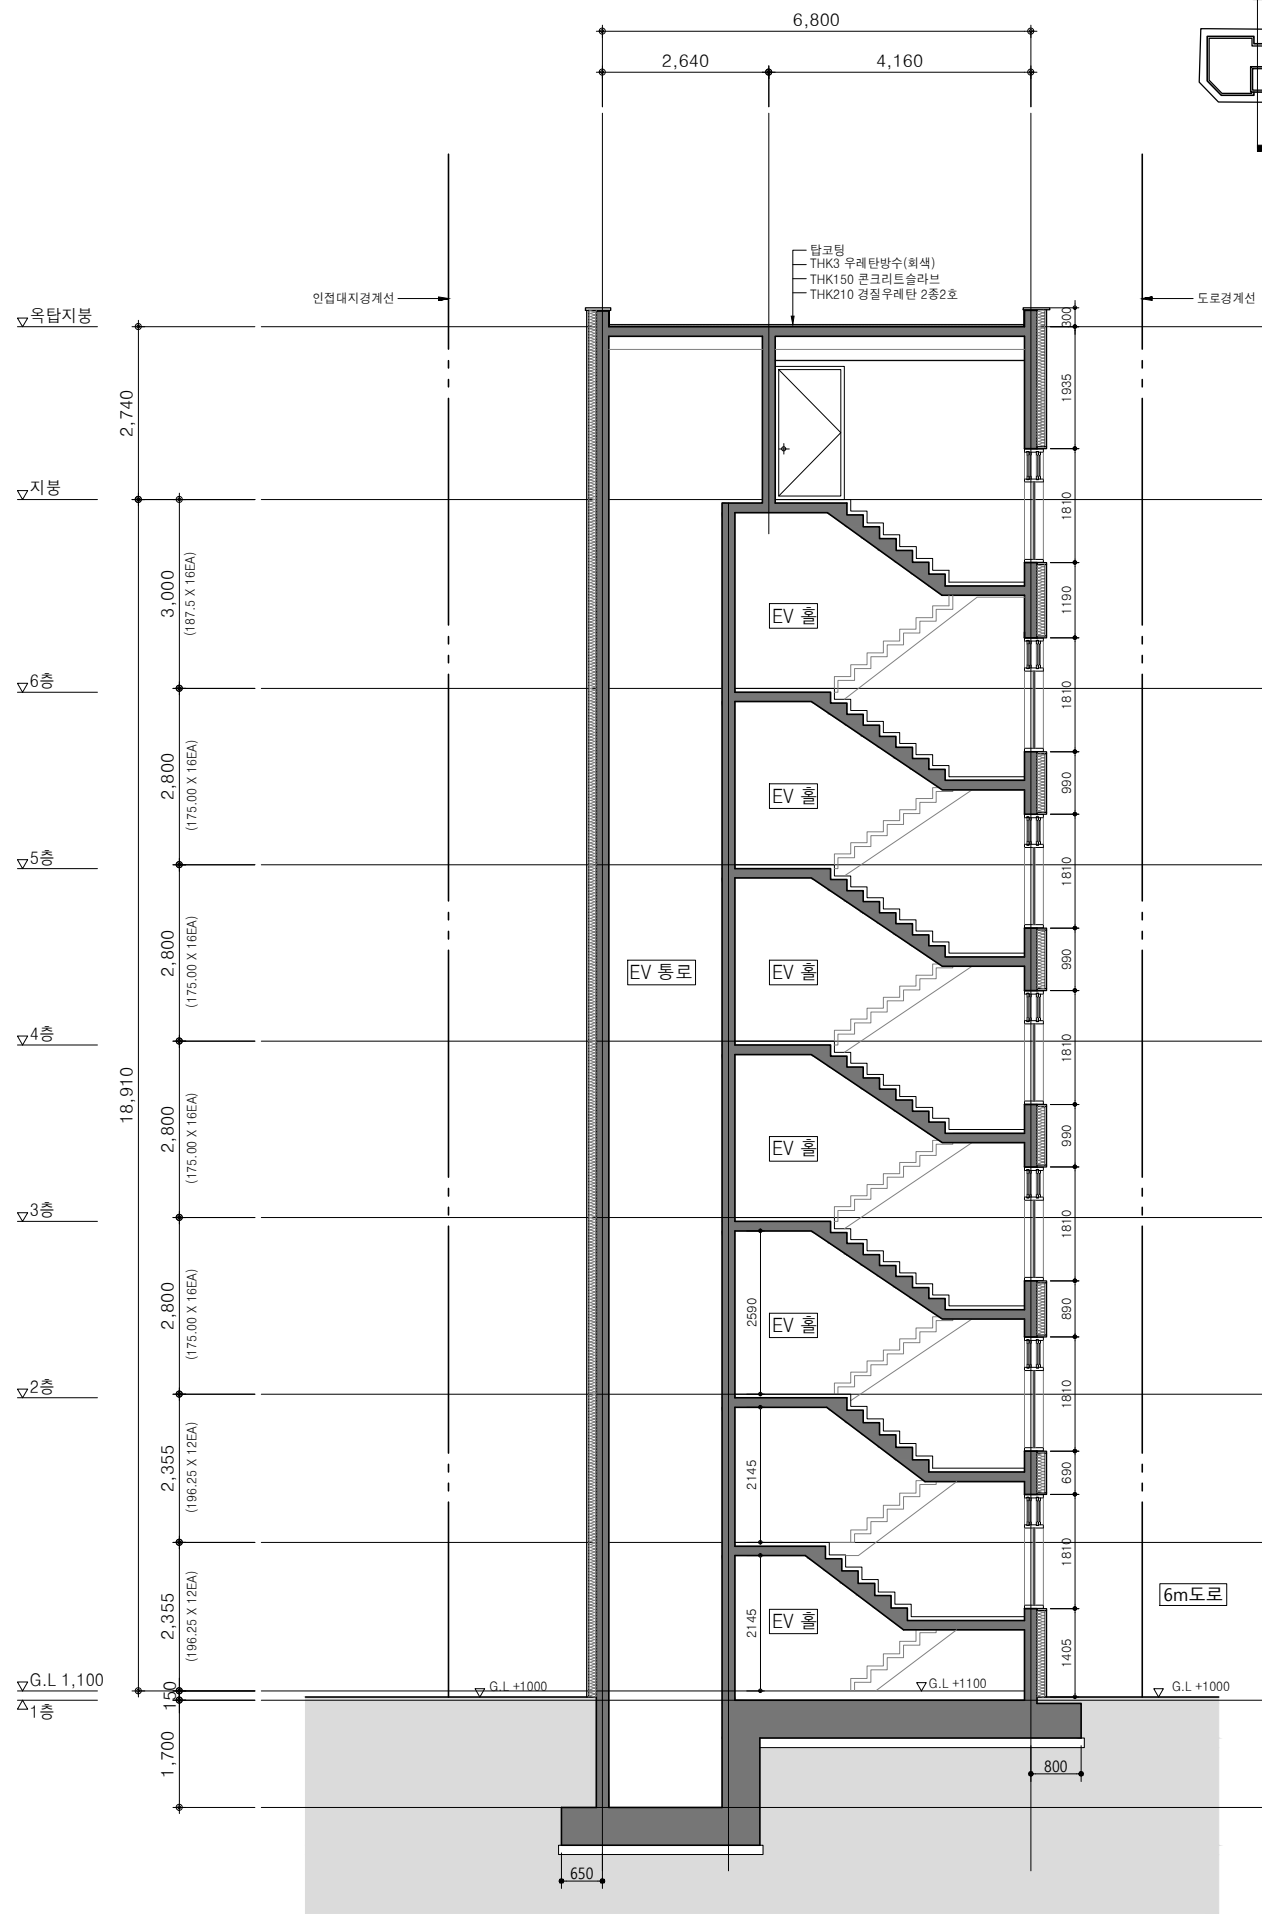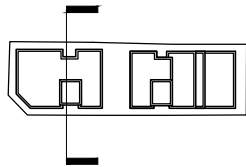

101동 계단단면도

축척=1/120

■ Key plan

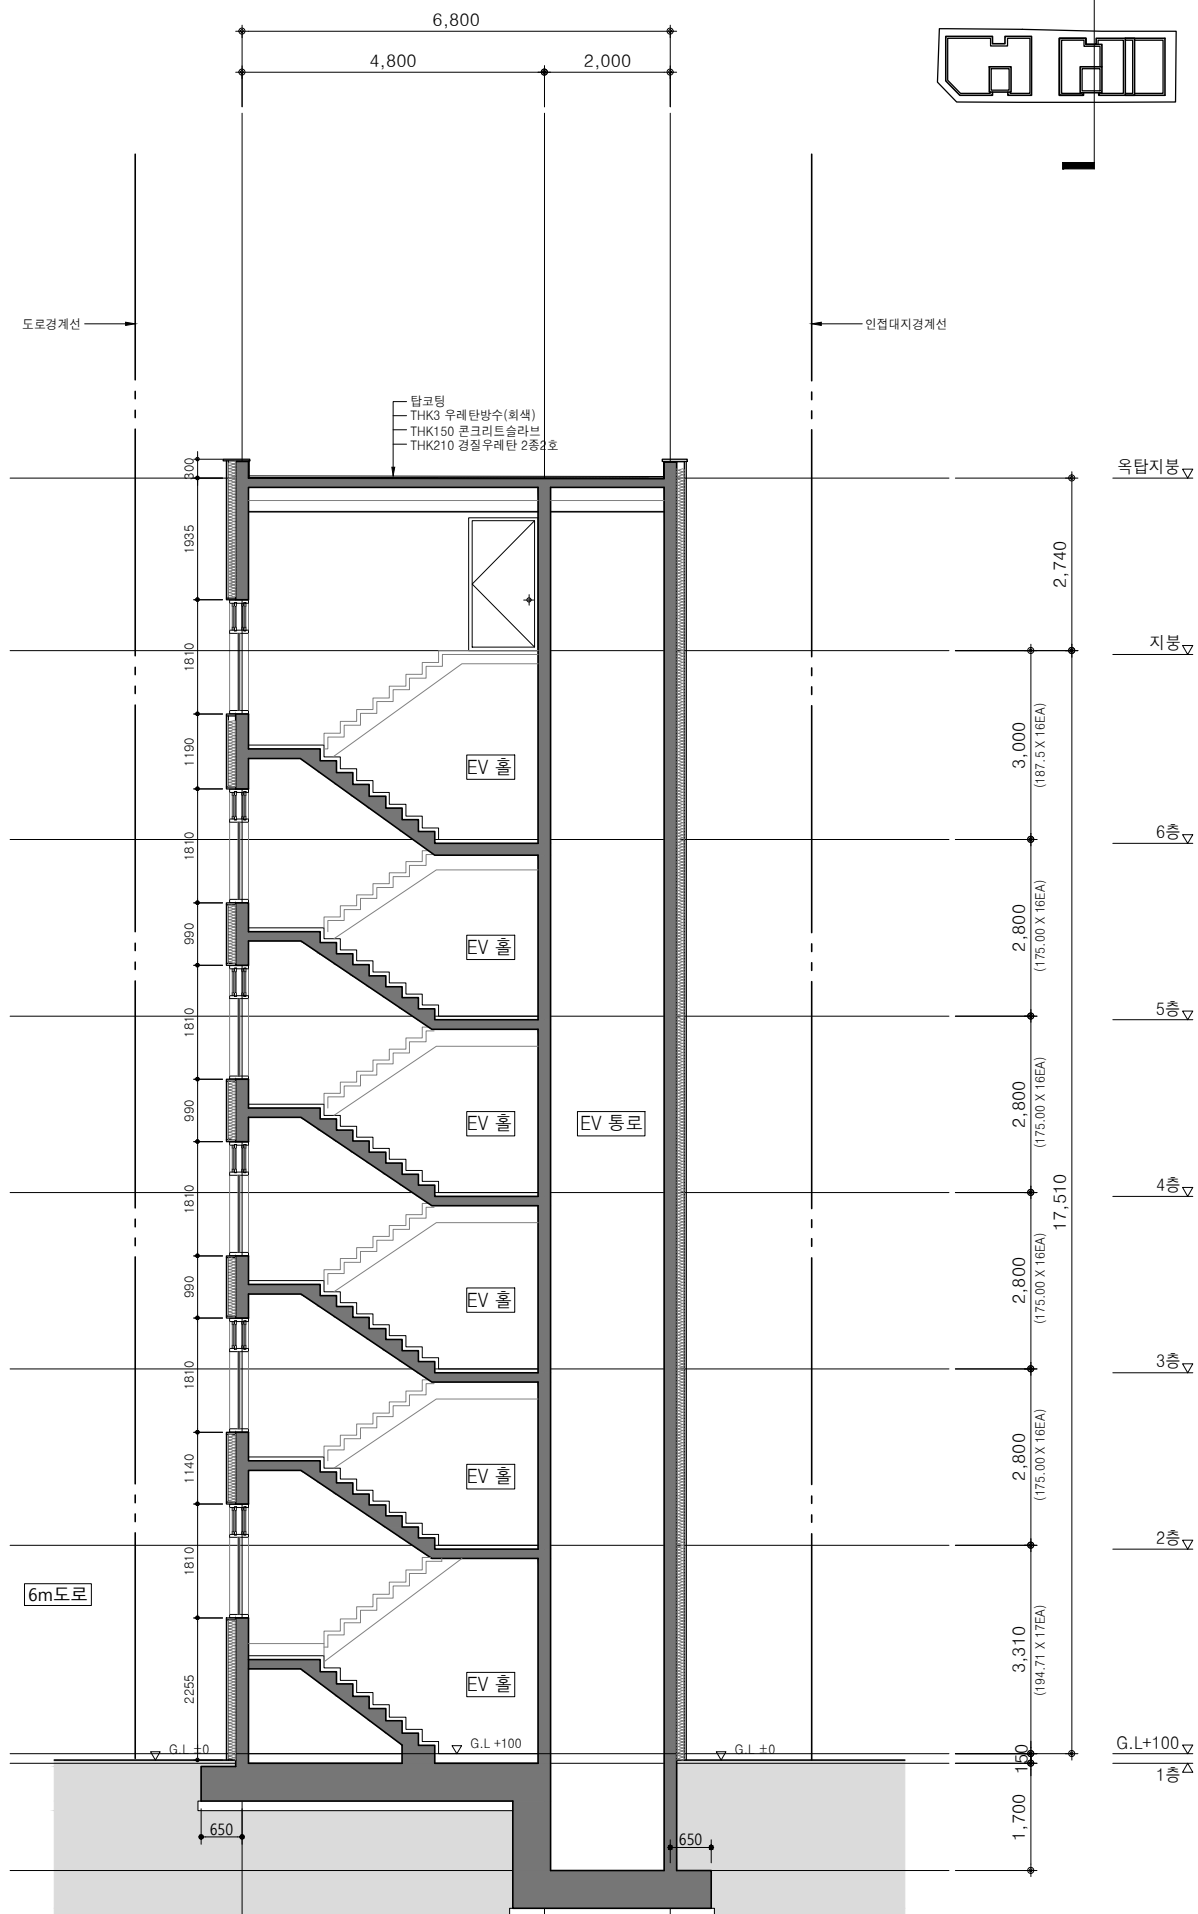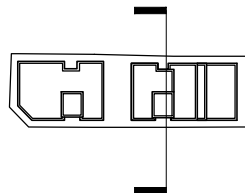

102동 계단단면도

축척=1/120



(주) 동심원건축사사무소

TEL : 02)3452-0597

FAX : 02)3452-0598

설계명 PROJECT TITLE

동작구 상도동

SH매입임대주택 신축공사

주 기 NOTE

NO. DATE REVISION DRAWN APP.

1				
2				
3				

설 계 DRAWN 검토 CHECK

심 사 SUBMIT 승인 APPROVE

축 척 SCALE

A1 1 / 60

A3 1 / 120

일 자 DATE

설계번호 PROJECT NO.

도면파일명 DWG. FILE NAME

도면번호 SHEET NO.

A - 403

도면명 SUBJECT TITLE

101동, 102동 계단단면도