


1. 조감도



2. 건축개요 및 현황도

대 지 위 치	서울특별시 동작구 상도동 335-155호	
대 지 면 적	466.00 M ²	
지 역 ,지 구	제2종 일반주거지역	
용 적 륜	법 정	200.00 %
	계 획	191.27 %
건 폐 율	법 정	60.00 %
	계 획	53.23 %
건 축 면 적	248.05 M ²	
지하층 연면적	98.76 M ²	
용적률산정연면적	891.34 M ²	
연 면 적	990.10 M ²	
최 고 높 이	16.05 M	
건 축 규 모	지하 1층, 지상 5층	
용 도	도시형생활주택(소형주택)-21세대	
조 경 면 적	법 정	466.00㎡ x 5.0% = 23.30㎡
	계 획	46.88㎡ (10.06 %)
정 화 조	법 정	(18세대 X 2.7인) + (3세대 X 2.0인) = 54.60인
	계 획	부패탱크식 60인조
주 차 대 수	법 정	(18세대 X 0.5대) + (3세대 X 0.3대) = 9.90대 *서울시 공공건설 및 공급 등에 관한 조례 제2조 및 제11조의 2에 의거 주차상한률 세대당 0.5대(전용면적이 30제곱미터 미만인 경우 세대당 0.4대) *공공주택 특별법 제43조3항 및 동법 시행령 제37조4항에 의거하여 세대당 30제곱미터 미만인 경우 세대당 주차대수 기준 0.3대 적용함.
	계 획	10대 설치
비 고		

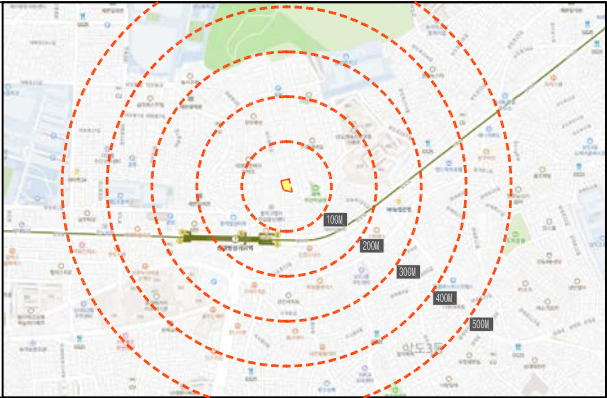

□ 위치도



□ 주변현황도

3. 입면도



PROJECT TITLE
사업 명칭

상도동 335-155호
도시형생활주택(소형주택)
연립주택 신축공사

설 계 개 요

NAME OF DRAWING
도 면 명

조감도, 건축개요, 입면도

NOTE
주 기

NO. ▲ REVISIONS ▲ DATE
번호 수정 일자

DESIGNED BY
설 계

CHECKED BY
심 사

APPROVED BY
승 인

CONSULTANTS
협 동 설 계

SCALE
축 척



DATE
일 자 2024. 11.

DWG NO.
도면 번호 A-01

SHEET NO.
일련 번호 □-□□□

DAWOO
건축사무소 다음건축

THE ARCHITECTS DESIGN GROUP
TEL. 02.414.6061 (代)
FAX. 02.414.6062

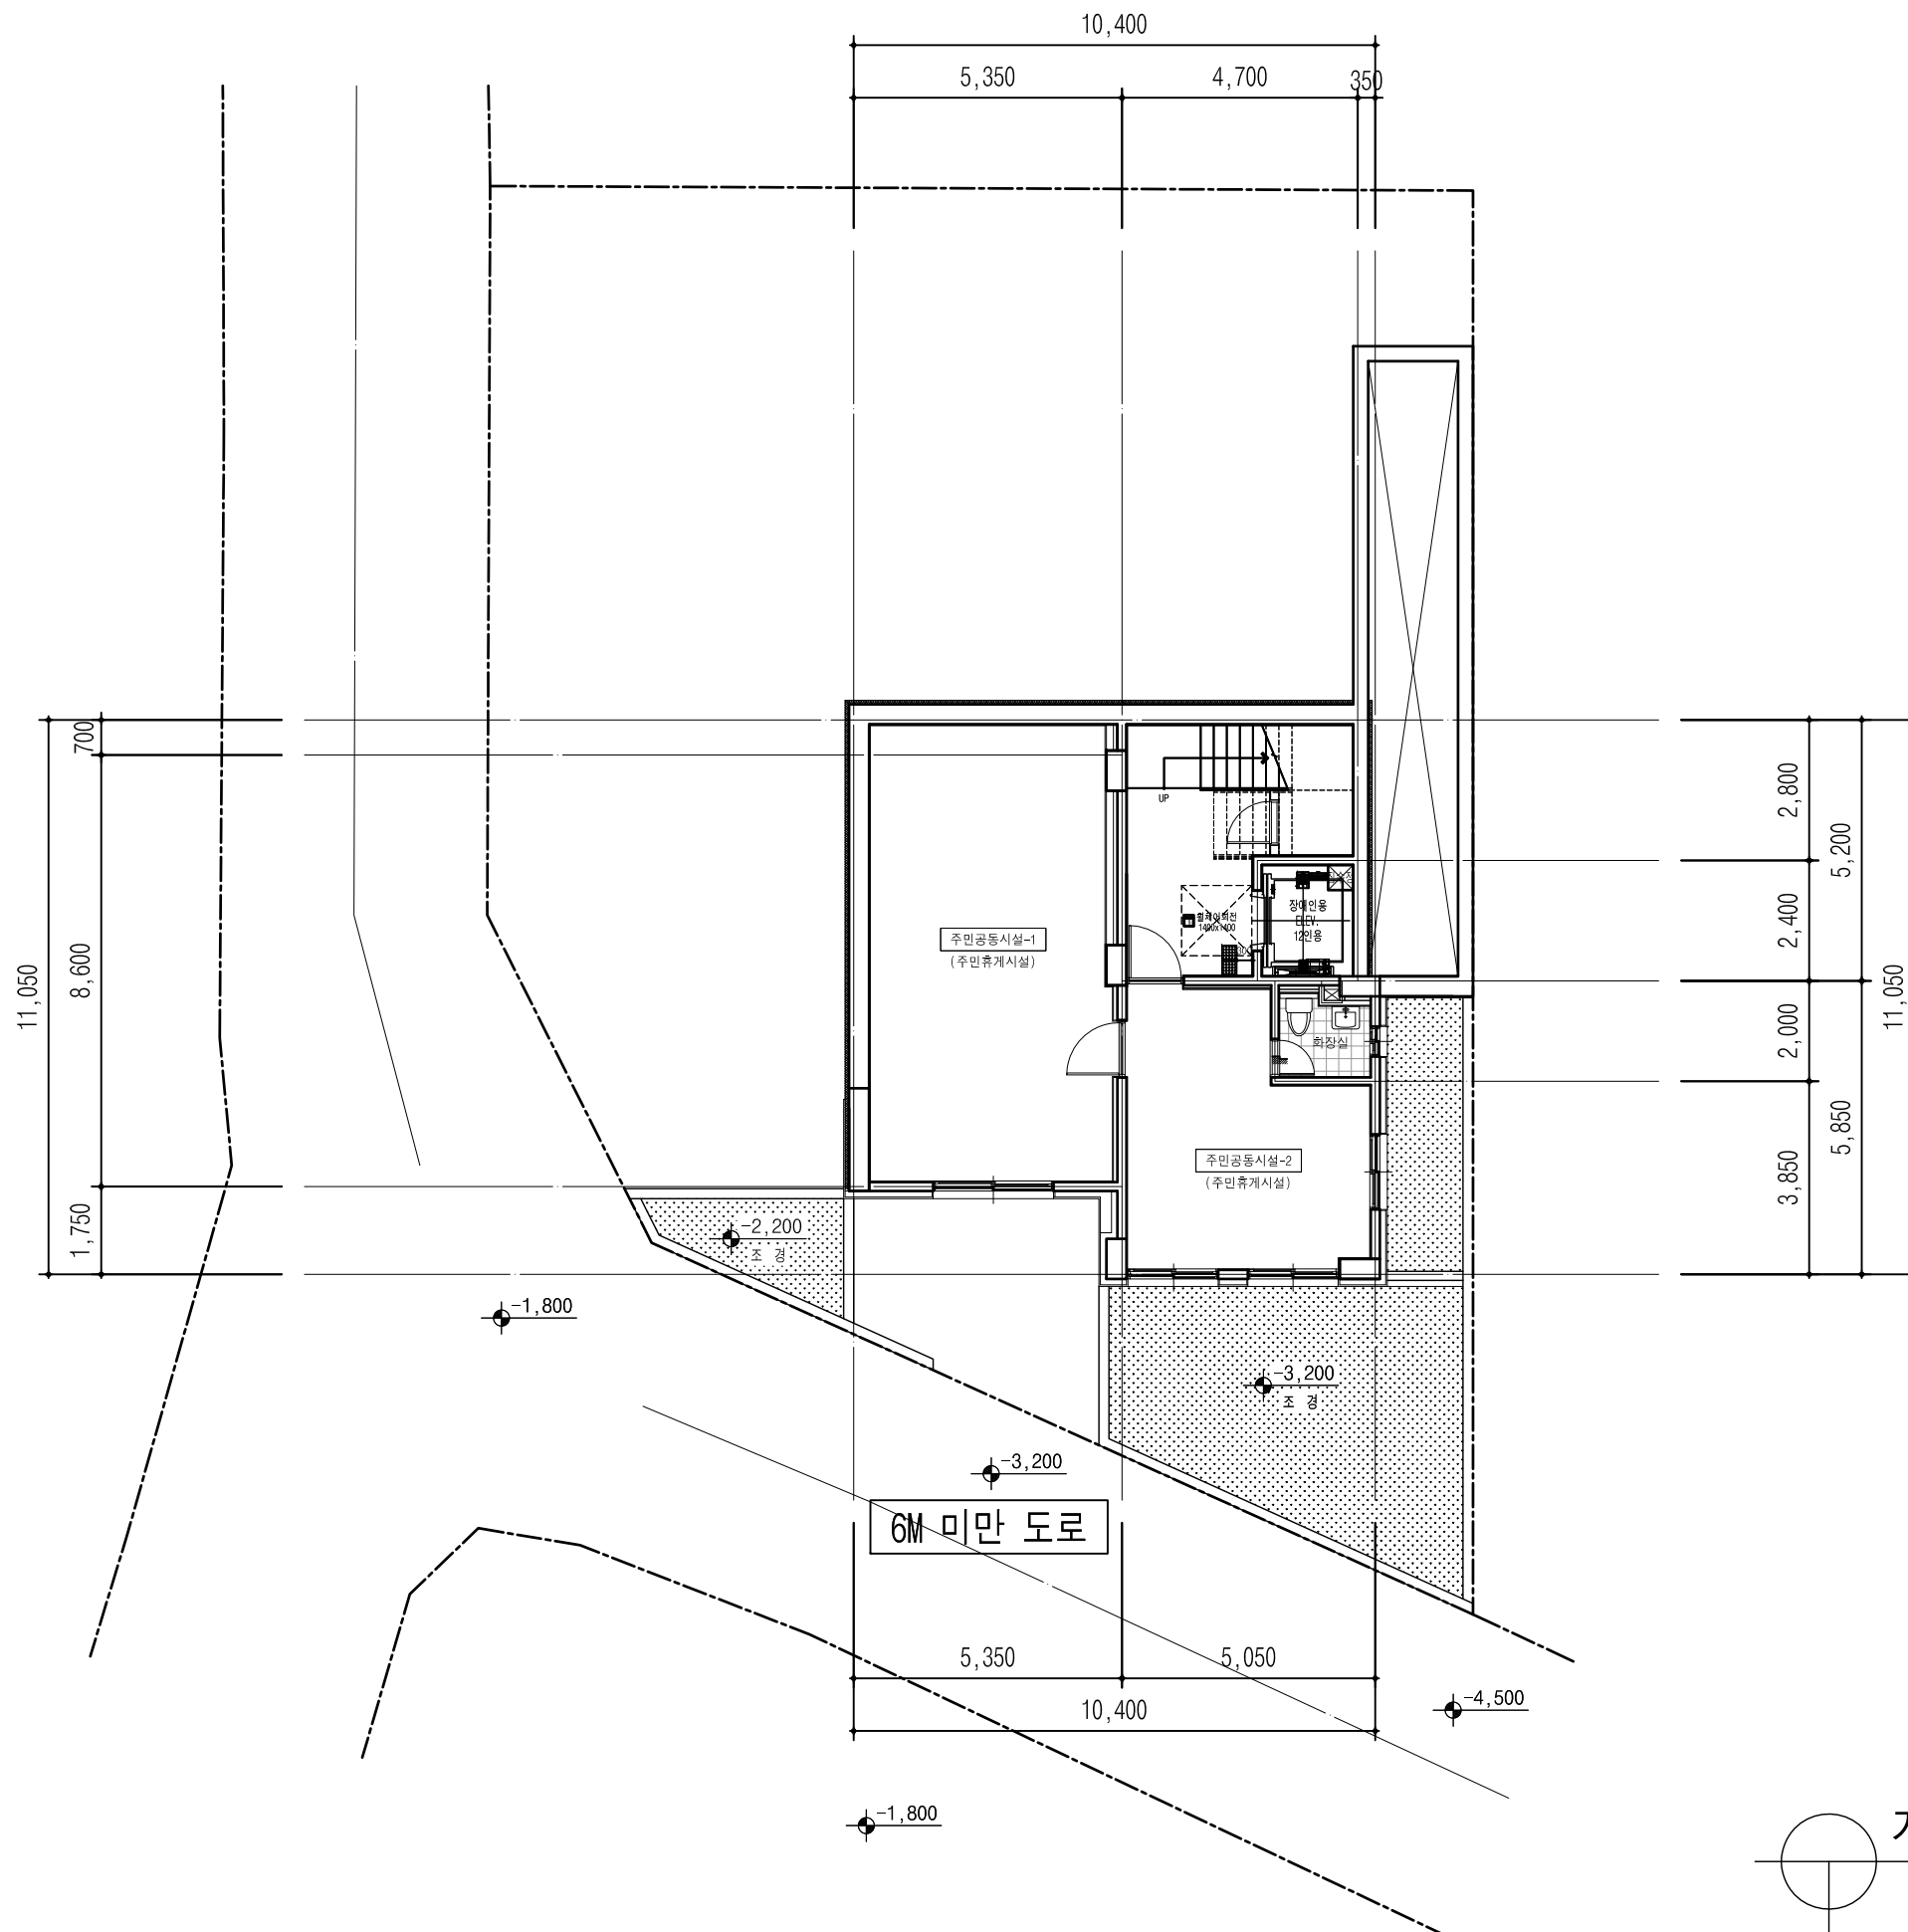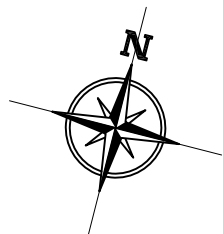

지하1층 평면도
SCALE : A3 : 1/150

PROJECT TITLE
사업명
상도동 335-155호
도시형생활주택(소형주택)
연립주택 신축공사

NAME OF DRAWING
도면명
지하1층 평면도

- NOTE
주 기
- 단독경보감지기(연기식)
 - 단독경보감지기(열감지)
 - ABC분말소화기(2.5KG)
 - 가스누설경보기
 - 일산화탄소경보기
 - 차면시설
 - 보일러
 - 에어컨 실외기

NO. 1
REVISIONS
수정
DATE
일자

DESIGNED BY
설계

CHECKED BY
심사

APPROVED BY
승인

CONSULTANTS
협동설계




SCALE
축척
A-21

DATE
일자
2024. 11.

DWG NO.
도면번호
A-11

SHEET NO.
일련번호
□-□□□

다움건축
dawoom
건축사무소 다움건축
THE ARCHITECTS DESIGN GROUP
TEL. 02.414.6061 (代)
FAX. 02.414.6062

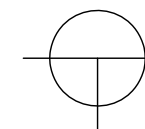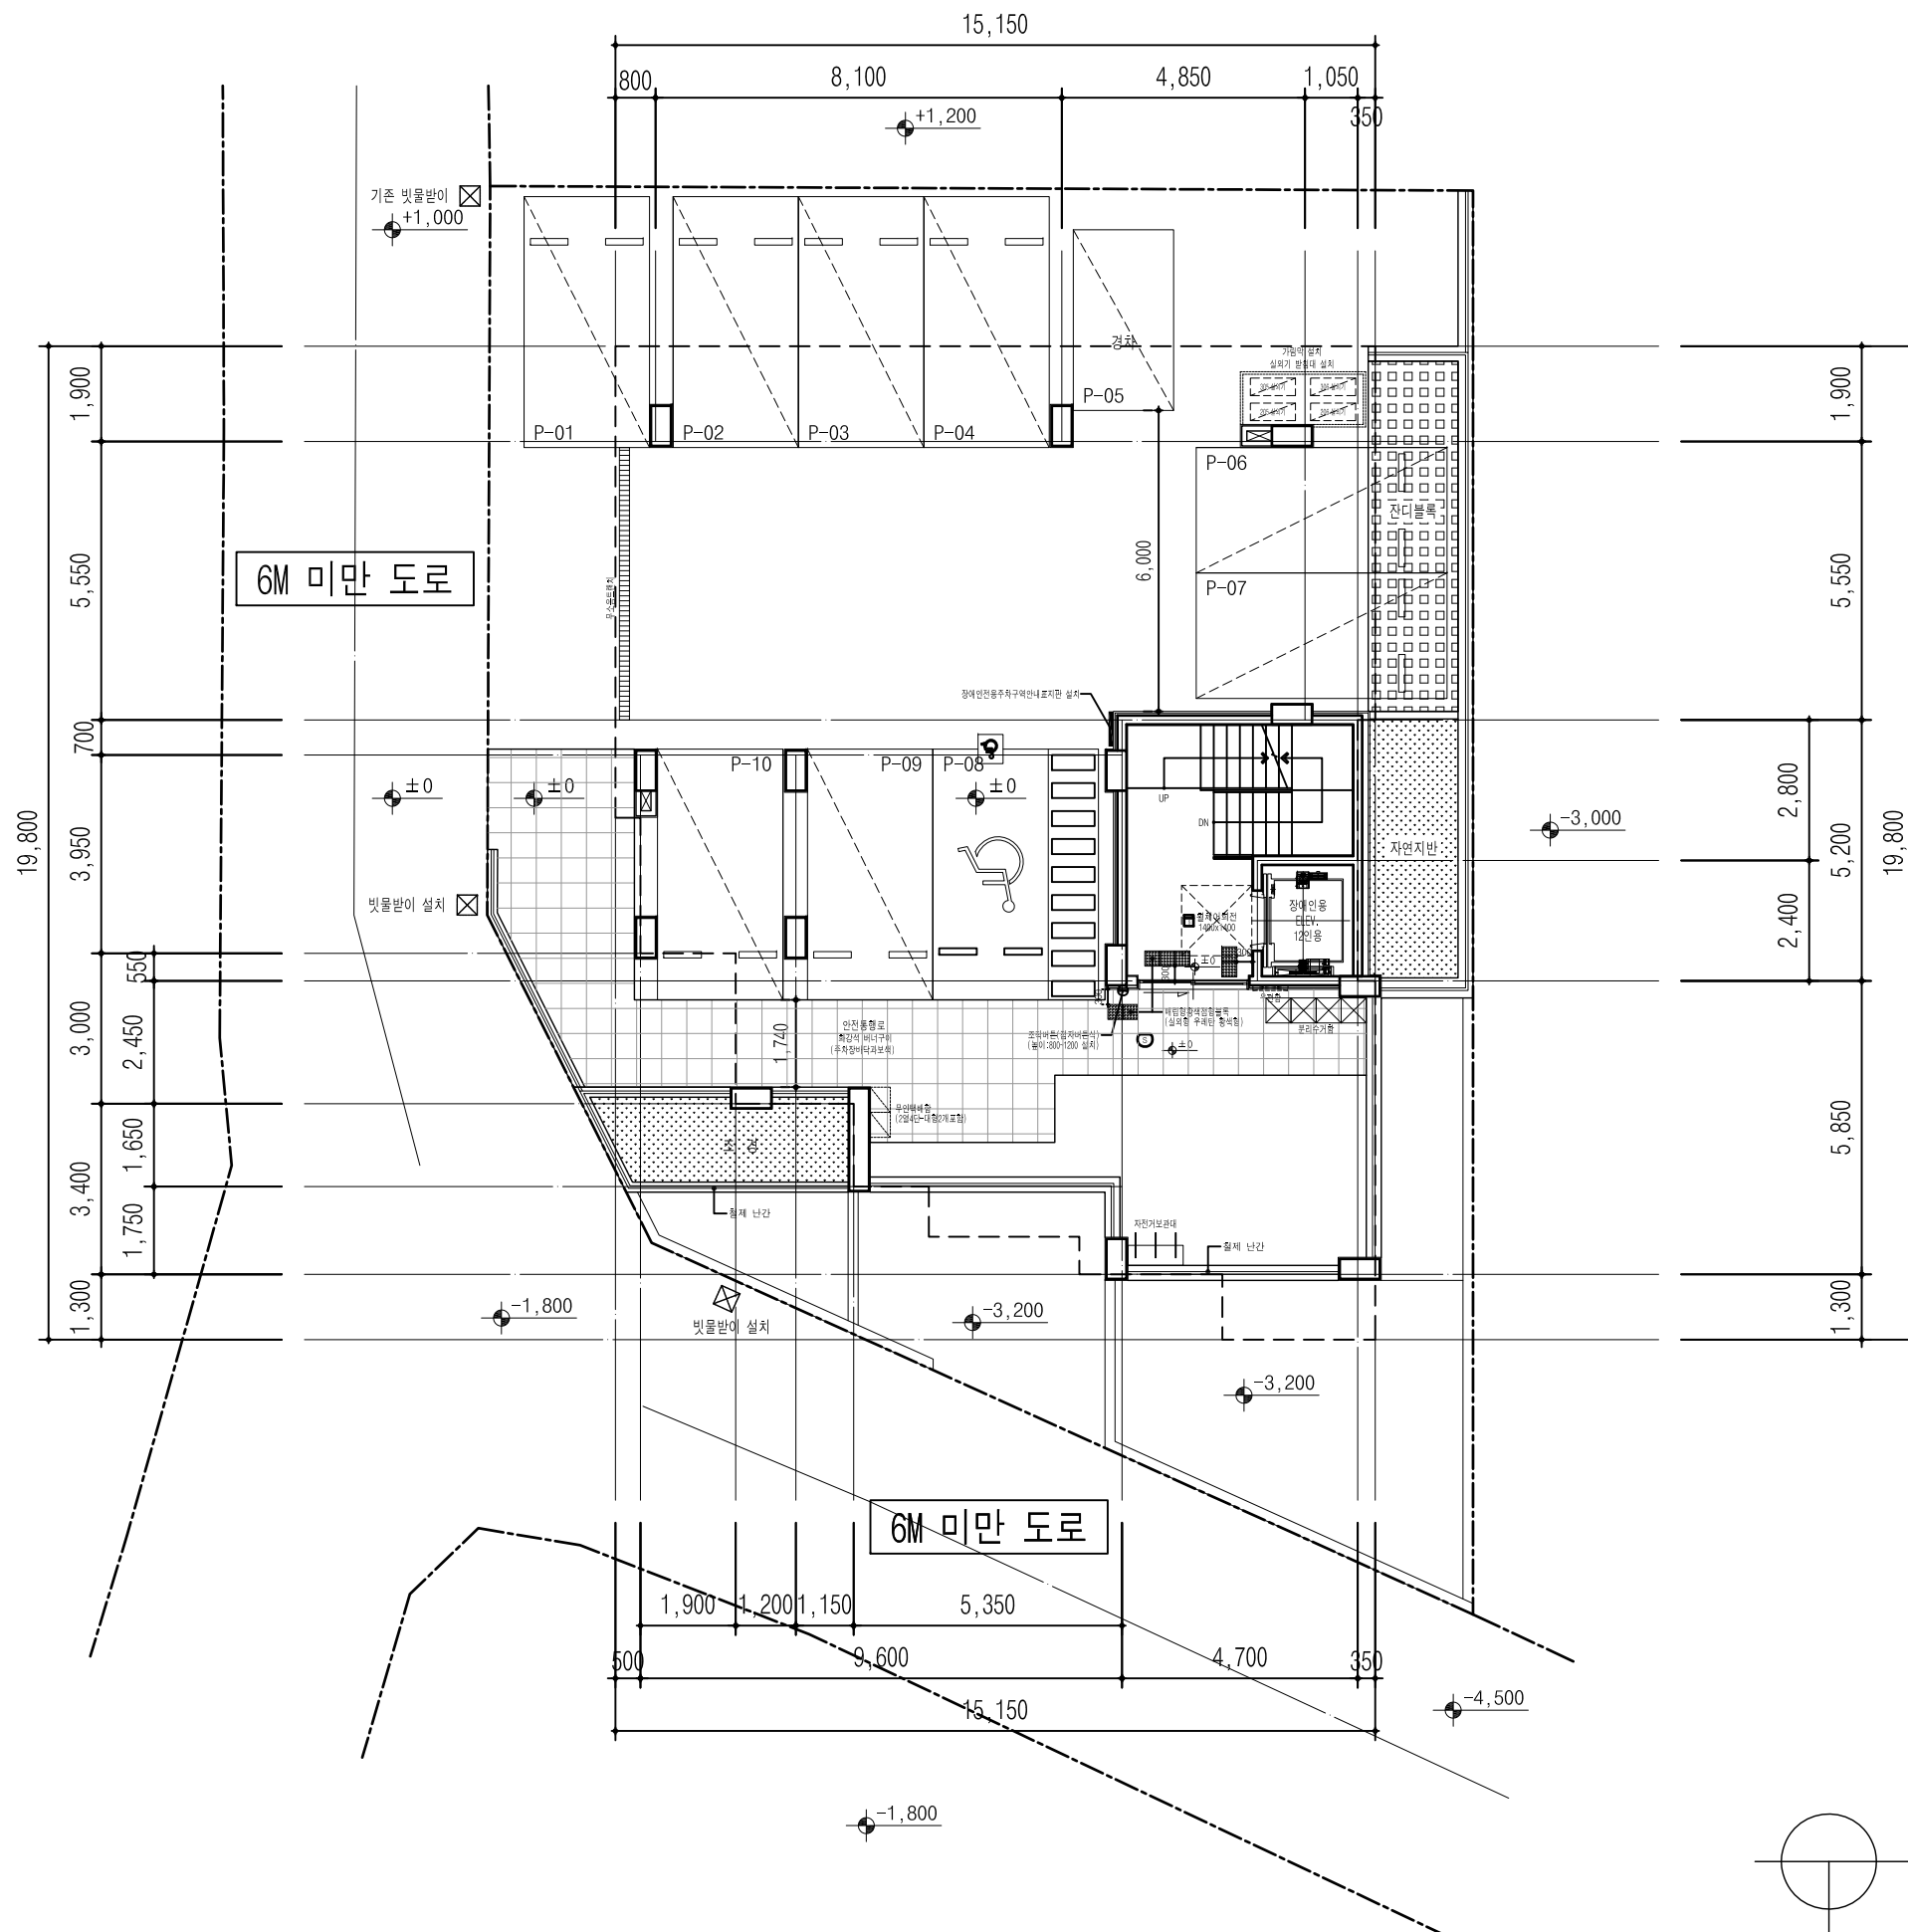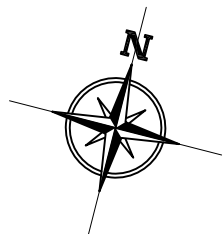

1층 평면도

SCALE : A3 : 1/150

PROJECT TITLE
사업명
상도동 335-155호
도시형생활주택(소형주택)
연립주택 신축공사

NAME OF DRAWING
도면명
1층 평면도

- NOTE
주 기
- 단독경보감지기(연기식)
 - 단독경보감지기(열감지)
 - ABC분말소화기(2.5KG)
 - 가스누설경보기
 - 일산화탄소경보기
 - 차면시설
 - 보일러
 - 에어컨 실외기

NO. 1
REVISIONS
수정
DATE
일자

DESIGNED BY
설계

CHECKED BY
심사

APPROVED BY
승인

CONSULTANTS
협동설계



SCALE
축척
1/150

DATE
일자
2024. 11.

DWG NO.
도면번호
A-22

SHEET NO.
일련번호
□-□□□

다움
dawoom
건축사무소 다움건축
THE ARCHITECTS DESIGN GROUP
TEL. 02.414.6061 (代)
FAX. 02.414.6062

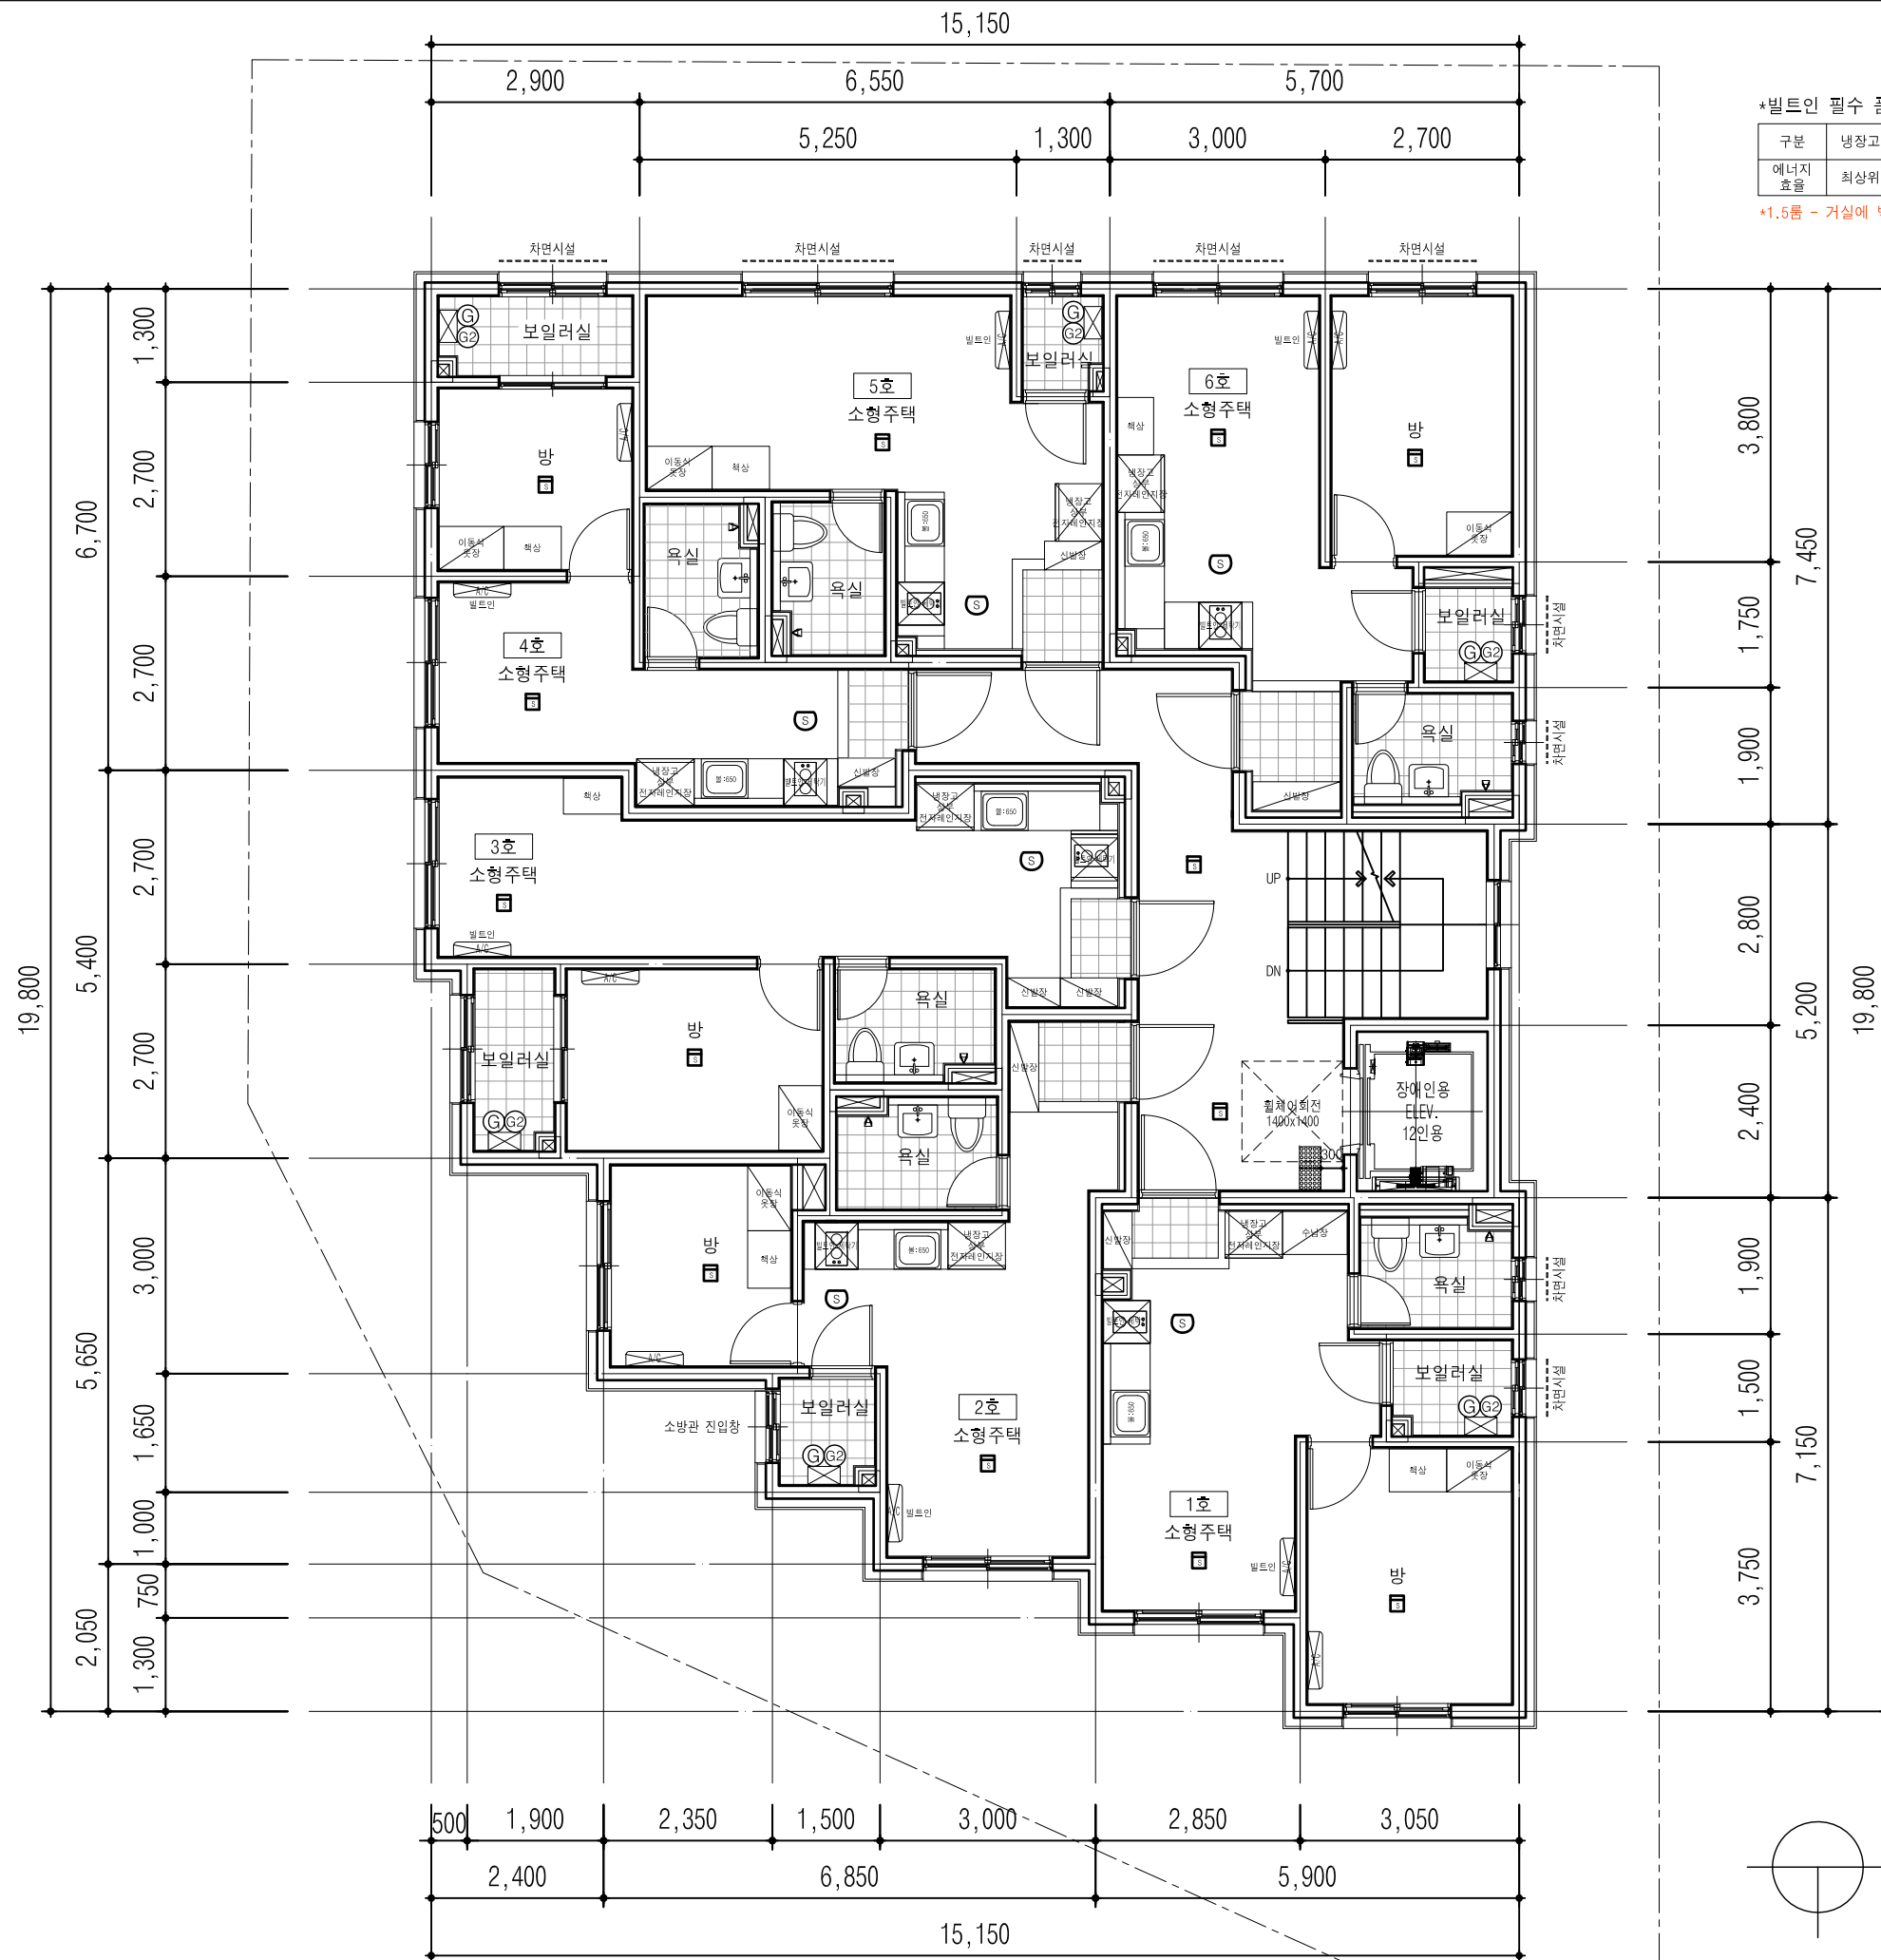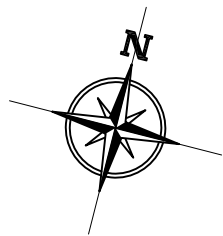

*빌트인 필수 품목					
구분	냉장고	벽걸이 에어컨	세탁기	책상	
에너지 효율	최상위	최상위	최상위	-	-

*1.5룸 - 거실에 벽걸이 에어컨 빌트인 설치 + 방에 에어컨 배관 설치

2~3층 평면도

SCALE : A3 : 1/100

PROJECT TITLE
사업 명칭

상도동 335-155호
도시형생활주택(소형주택)
연립주택 신축공사

NAME OF DRAWING
도면 명

2~3층 평면도

NOTE
주 기

단독경보감지기(연기식)

단독경보감지기(열감지)

ABC분말소화기(2.5KG)

가스누설경보기

일산화탄소경보기

차면시설

보일러

에어컨 실외기

NO. 1

REVISIONS

DATE

DESIGNED BY
설 계

CHECKED BY
심 사

APPROVED BY
승 인

CONSULTANTS
협 동 설 계

SCALE
축척 1/100




DATE
일 자 2024. 11.

DWG NO.
도면 번호 A-23

SHEET NO.
일련 번호

건축사무소 다움건축

THE ARCHITECTS DESIGN GROUP
TEL. 02.414.6061 (代)
FAX. 02.414.6062

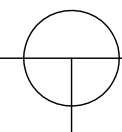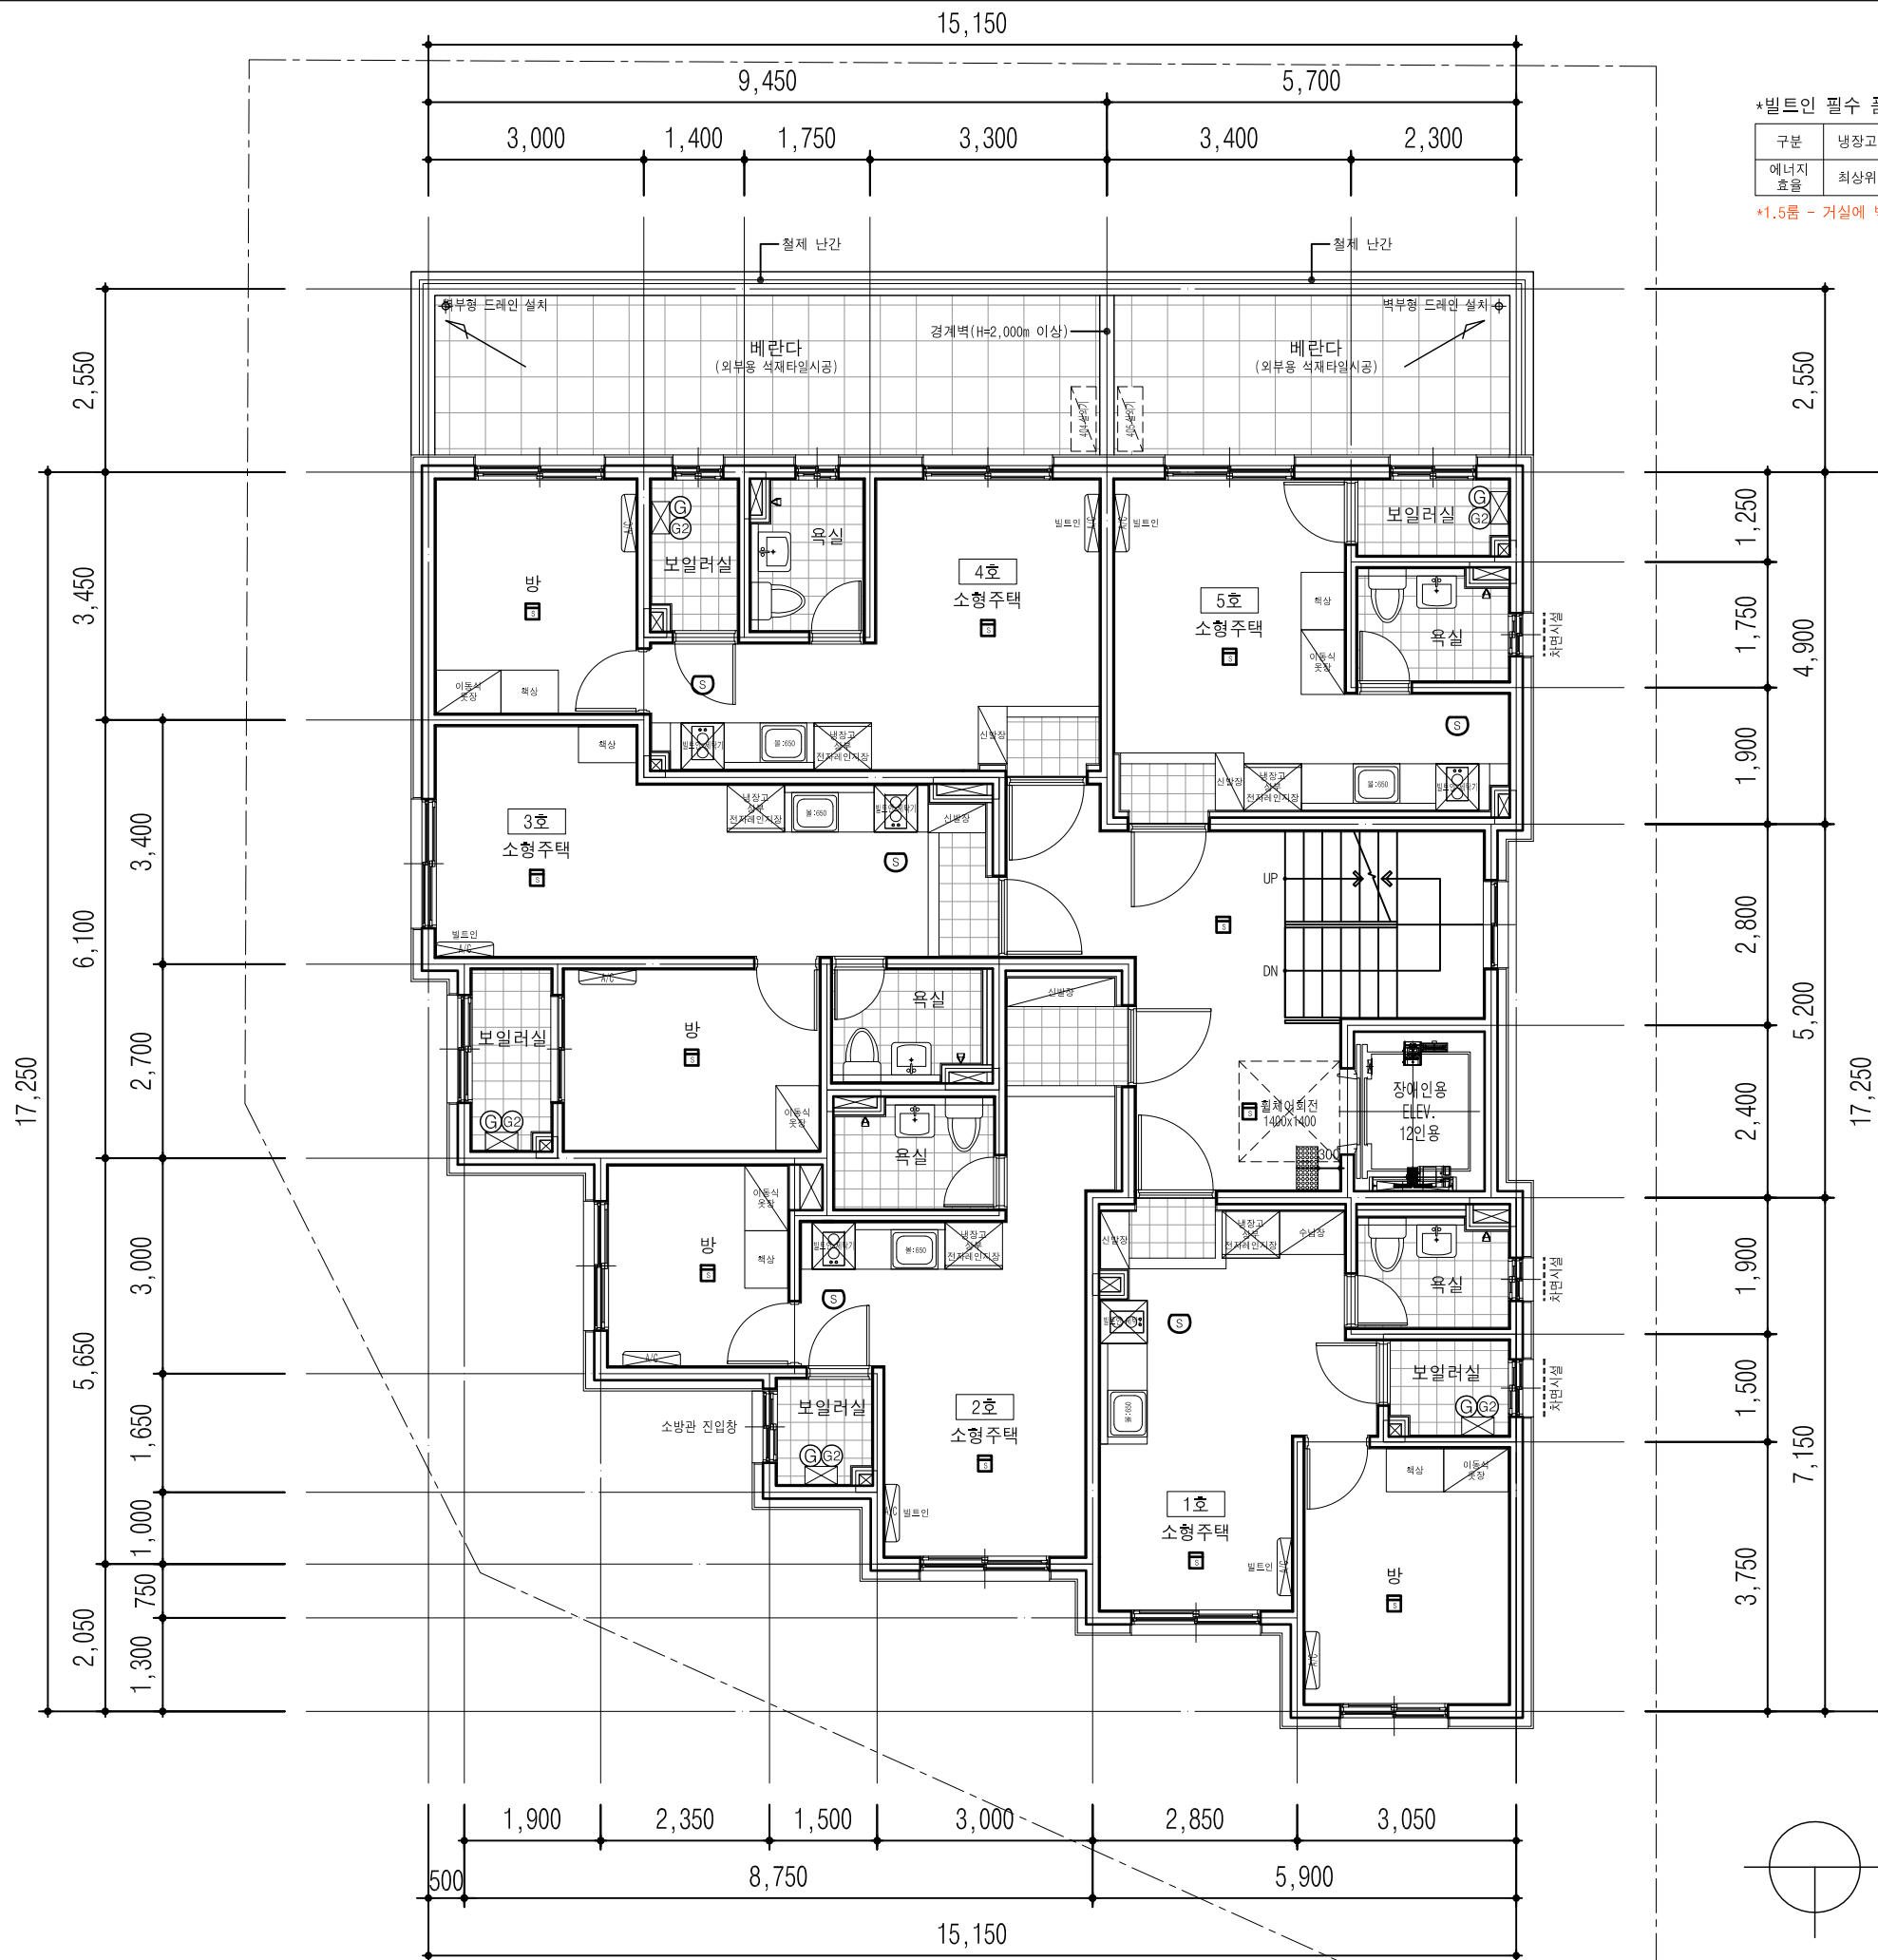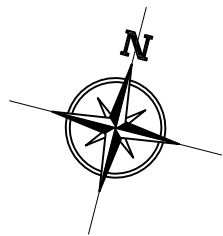

4층 평면도

SCALE : A3 : 1/100

*빌트인 필수 품목

구분	냉장고	벽걸이 에어컨	세탁기	책상	
에너지 효율	최상위	최상위	최상위	-	-

*1.5룸 - 거실에 벽걸이 에어컨 빌트인 설치 + 방에 에어컨 배관 설치

PROJECT TITLE
사업 명
상도동 335-155호
도시형생활주택(소형주택)
연립주택 신축공사

NAME OF DRAWING
도면 명

4층 평면도

NOTE
주 기

- 단독경보감지기(연기식)
- 단독경보감지기(열감지)
- ABC분말소화기(2.5KG)
- 가스누설경보기
- 일산화탄소경보기
- 차면시설
- 보일러
- 에어컨 실외기

NO. REVISIONS DATE
번호 수정 일자

DESIGNED BY
설 계

CHECKED BY
심 사

APPROVED BY
승 인

CONSULTANTS
협 동 설 계



SCALE
축척 1/100

DATE
일 자 2024. 11.

DWG NO.
도면 번호 A-24

SHEET NO.
일련 번호

건축사무소 다음건축
THE ARCHITECTS DESIGN GROUP
TEL. 02.414.6061 (代)
FAX. 02.414.6062

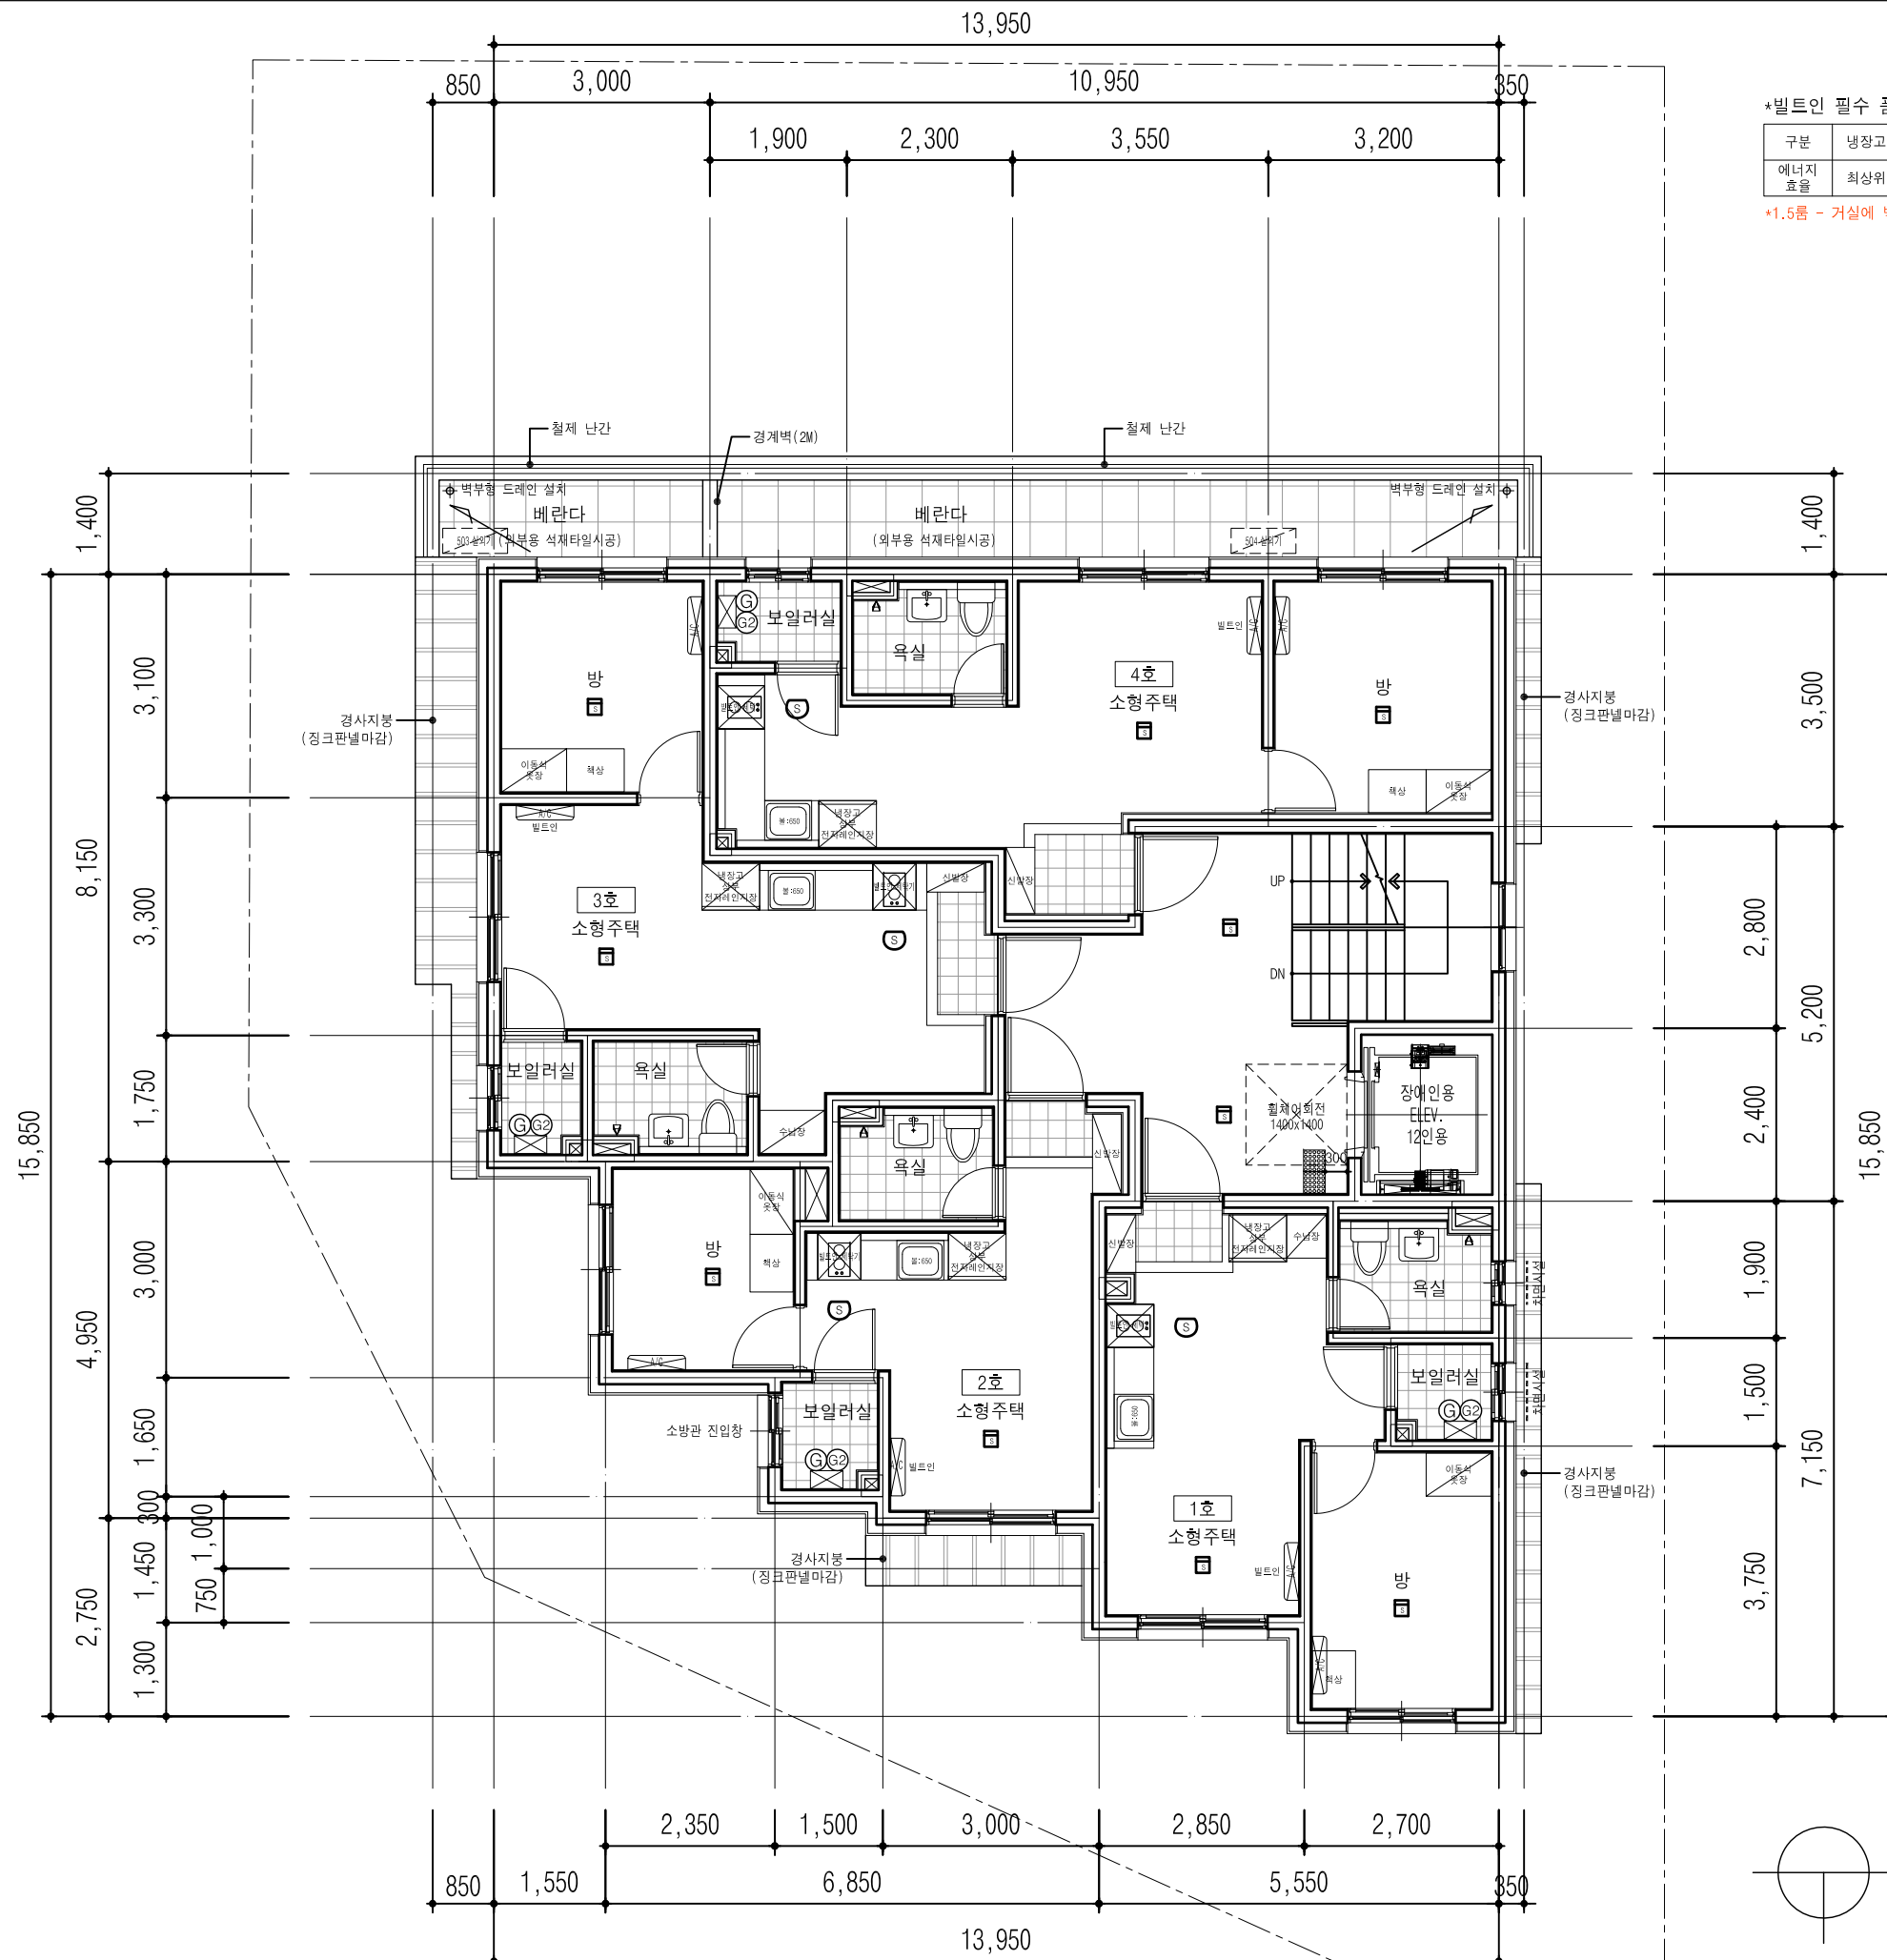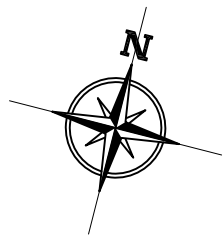

*빌트인 필수 품목

구분	냉장고	벽걸이 에어컨	세탁기	책상	
에너지 효율	최상위	최상위	최상위	-	-

*1.5룸 - 거실에 벽걸이 에어컨 빌트인 설치 + 방에 에어컨 배관 설치

5층 평면도

SCALE : A3 : 1/100

PROJECT TITLE
사업 명칭

상도동 335-155호
도시형생활주택(소형주택)
연립주택 신축공사

NAME OF DRAWING
도면 명

5층 평면도

NOTE
주 기

- 단독경보감지기(연기식)
- 단독경보감지기(열감지)
- ABC분말소화기(2.5KG)
- 가스누설경보기
- 일산화탄소경보기
- 차면시설
- 보일러
- 에어컨 실외기

NO. REVISIONS DATE
번호 수정 일자

DESIGNED BY
설 계

CHECKED BY
심 사

APPROVED BY
승 인

CONSULTANTS
협 동 설 계

SCALE
축척 1/100

DATE
일 자 2024. 11.




DWG NO.
도면 번호 A-25

SHEET NO.
일련 번호

DAWOM

건축사무소 다음건축

THE ARCHITECTS DESIGN GROUP
TEL. 02.414.6061 (代)
FAX. 02.414.6062

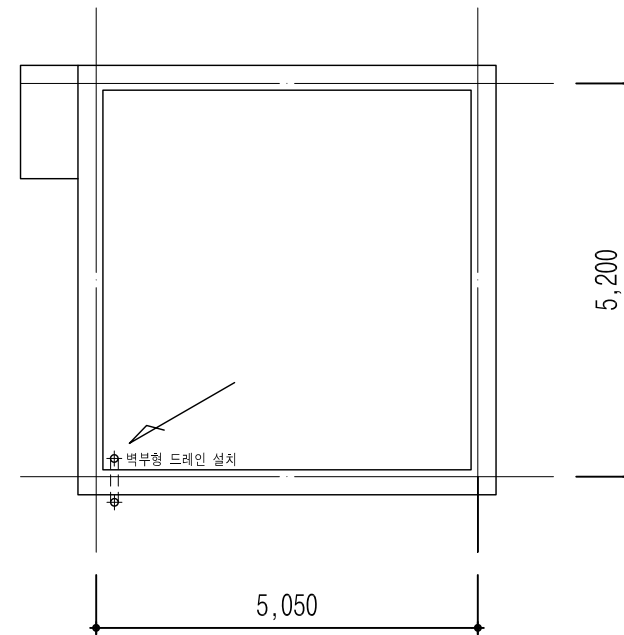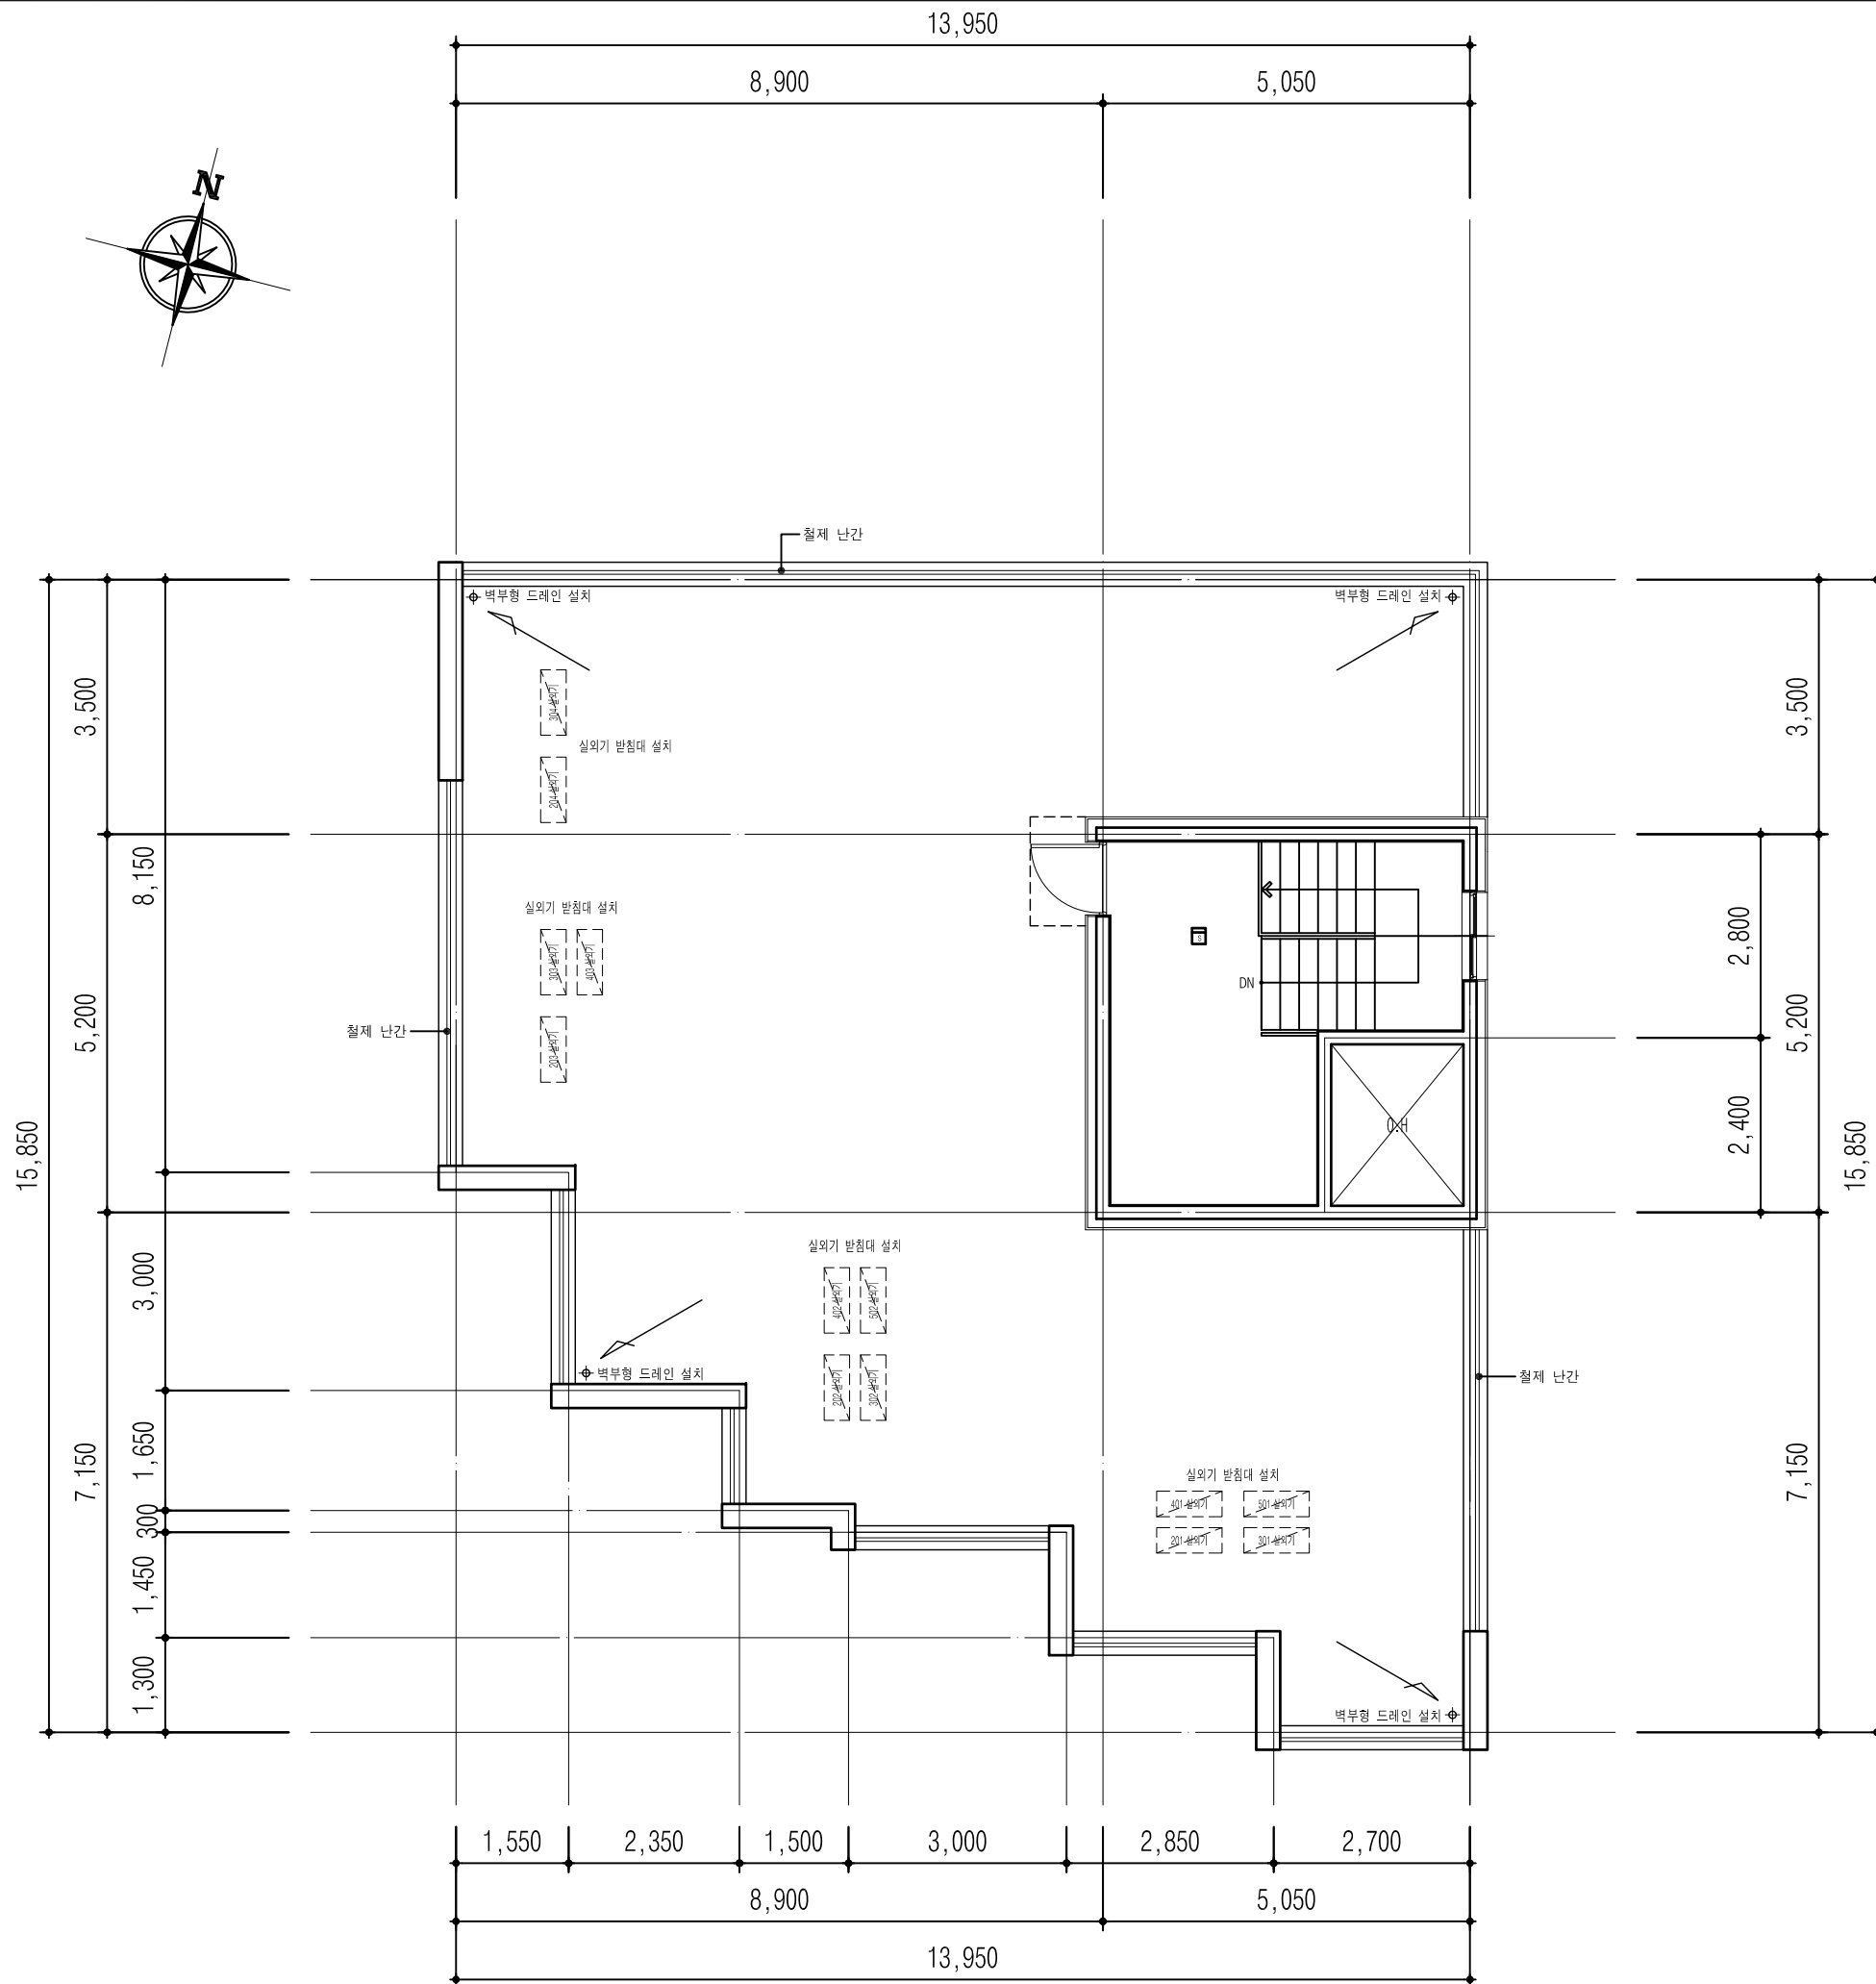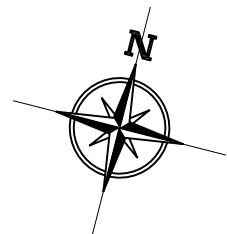

지붕및옥탑 평면도
SCALE : A3 : 1/100

PROJECT TITLE
사업 명
상도동 335-155호
도시형생활주택(소형주택)
연립주택 신축공사

NAME OF DRAWING
도면 명
지붕및옥탑 평면도

- NOTE
주 기
- 단독경보감지기(연기식)
 - 단독경보감지기(열감지)
 - ABC분말소화기(2.5KG)
 - 가스누설경보기
 - 일산화탄소경보기
 - 차면시설
 - 보일러
 - 에어컨 실외기

NO. REVISIONS DATE
번호 수정 일자

DESIGNED BY
설 계

CHECKED BY
심 사

APPROVED BY
승 인

CONSULTANTS
협 동 설 계


SCALE
축척 1/100

DATE
일 자 2024. 11.

DWG NO.
도면 번호 A-26

SHEET NO.
일련 번호

다움건축
건축사사무소 다움건축
THE ARCHITECTS DESIGN GROUP
TEL. 02.414.6061 (代)
FAX. 02.414.6062

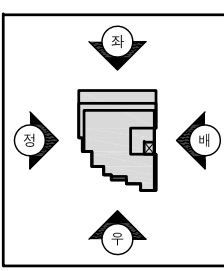

PROJECT TITLE
사업명칭

상도동 335-155호
도시형생활주택(소형주택)
연립주택 신축공사

NAME OF DRAWING
도면명

입면도-1

NOTE
주 기

창호 PVC 블랙
소방관진입창 - 스티커부착

NO. 번호	REVISIONS 수정	DATE 일자

DESIGNED BY
설 계

CHECKED BY
심 사

APPROVED BY
승 인

CONSULTANTS
협동설계

SCALE
축척 1/100



DATE
일자 2024. 11.

DWG NO.
도면번호 A-31

SHEET NO.
일련번호 □-□□□

 **DAWOO**
dawoo
건축사사무소 다움건축
THE ARCHITECTS DESIGN GROUP
TEL. 02.414.6061 (代)
FAX. 02.414.6062

정 면 도
SCALE : A3 : 1/100

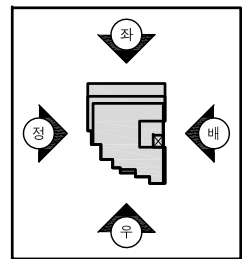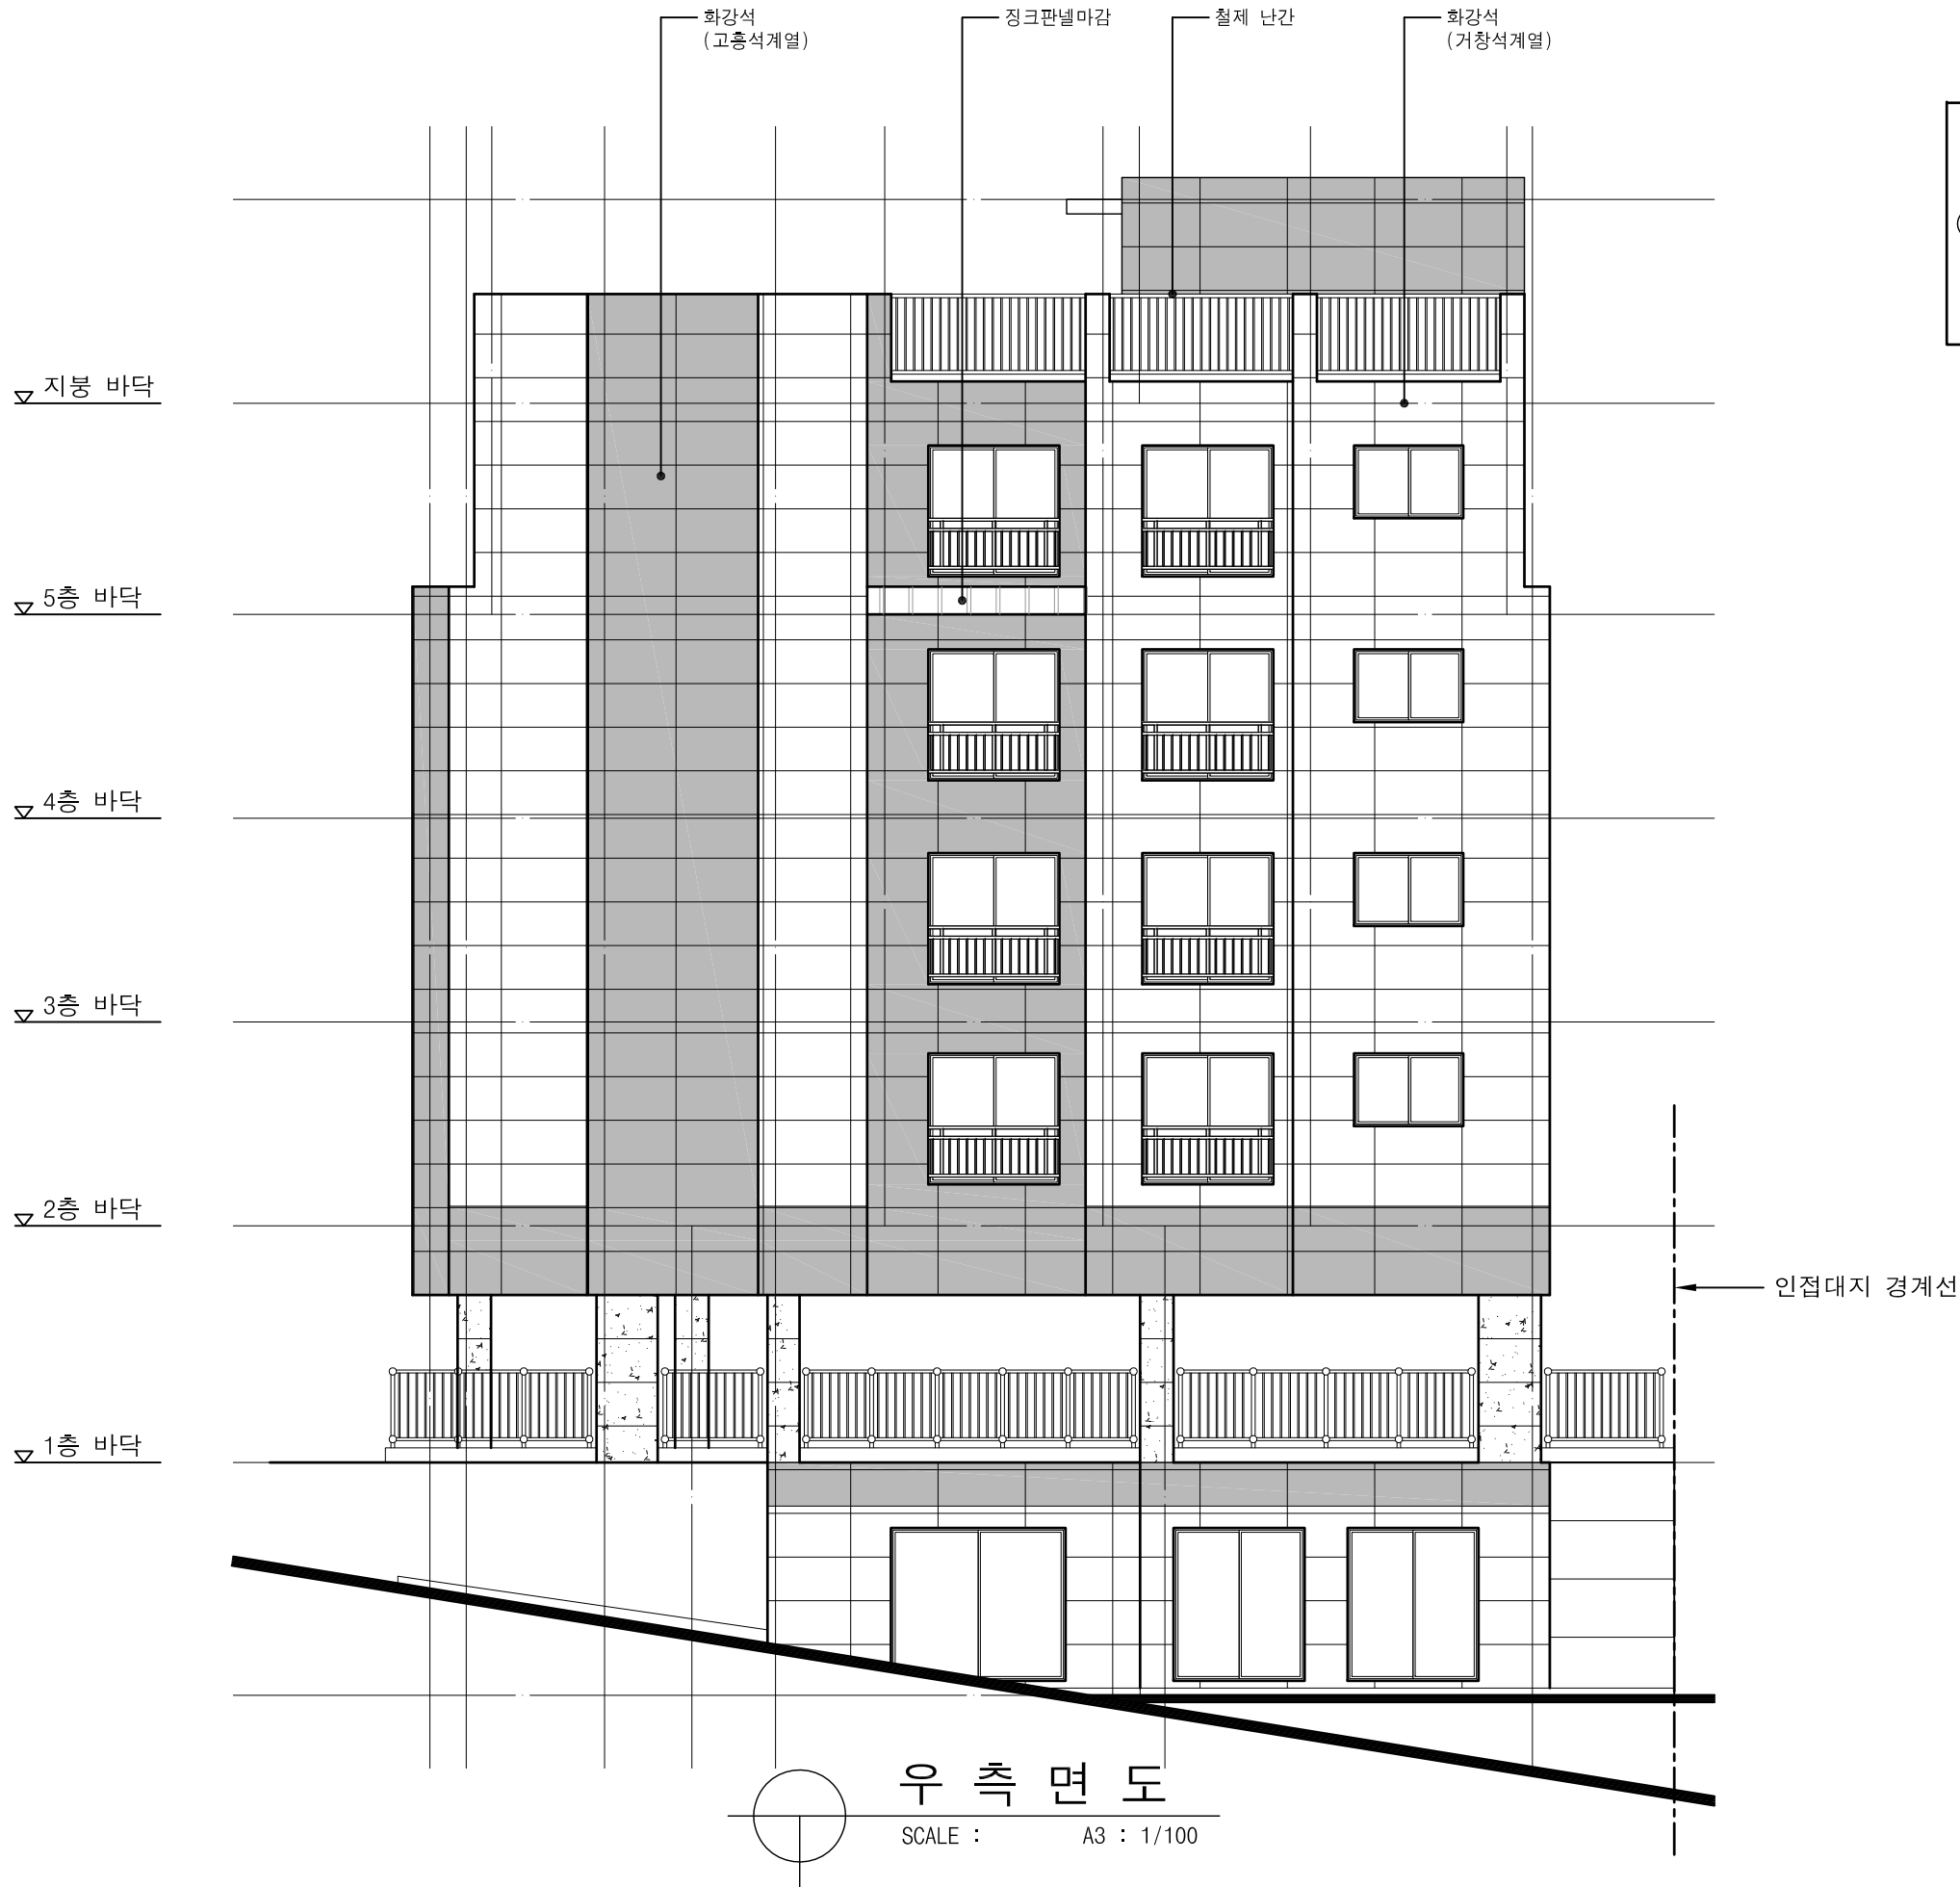

PROJECT TITLE
사업명칭

상도동 335-155호
도시형생활주택(소형주택)
연립주택 신축공사

NAME OF DRAWING
도면명

입면도-2

NOTE
주 기

창호 PVC 블랙

NO. ▲ REVISIONS ▲ DATE
번호 수정 일자

DESIGNED BY
설 계

CHECKED BY
심 사

APPROVED BY
승 인

CONSULTANTS
협동설계

SCALE
축척 1/100


DATE
일 자 2024. 11.

DWG NO.
도면번호 A-32

SHEET NO.
일련번호 □-□□□

 **dawoom**
건축사무소 다움건축

THE ARCHITECTS DESIGN GROUP
TEL. 02.414.6061 (代)
FAX. 02.414.6062

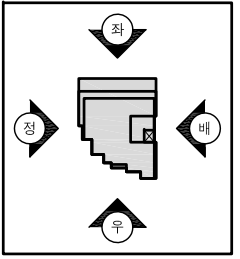

PROJECT TITLE
사업 명칭

상도동 335-155호
도시형생활주택(소형주택)
연립주택 신축공사

NAME OF DRAWING
도면 명

입면도-3

NOTE
주 기

창호 PVC 블랙

NO. ▲ REVISIONS ▲ DATE
번호 수정 일자

DESIGNED BY
설 계

CHECKED BY
심 사

APPROVED BY
승 인

CONSULTANTS
협 동 설 계



SCALE
축척 1/100

DATE
일 자 2024. 11.

DWG NO.
도면 번호 A-33

SHEET NO.
일련 번호 □—□□□

 **dawoom**
건축사사무소 다움건축
THE ARCHITECTS DESIGN GROUP
TEL. 02.414.6061 (代)
FAX. 02.414.6062

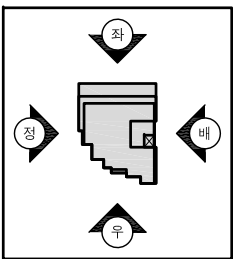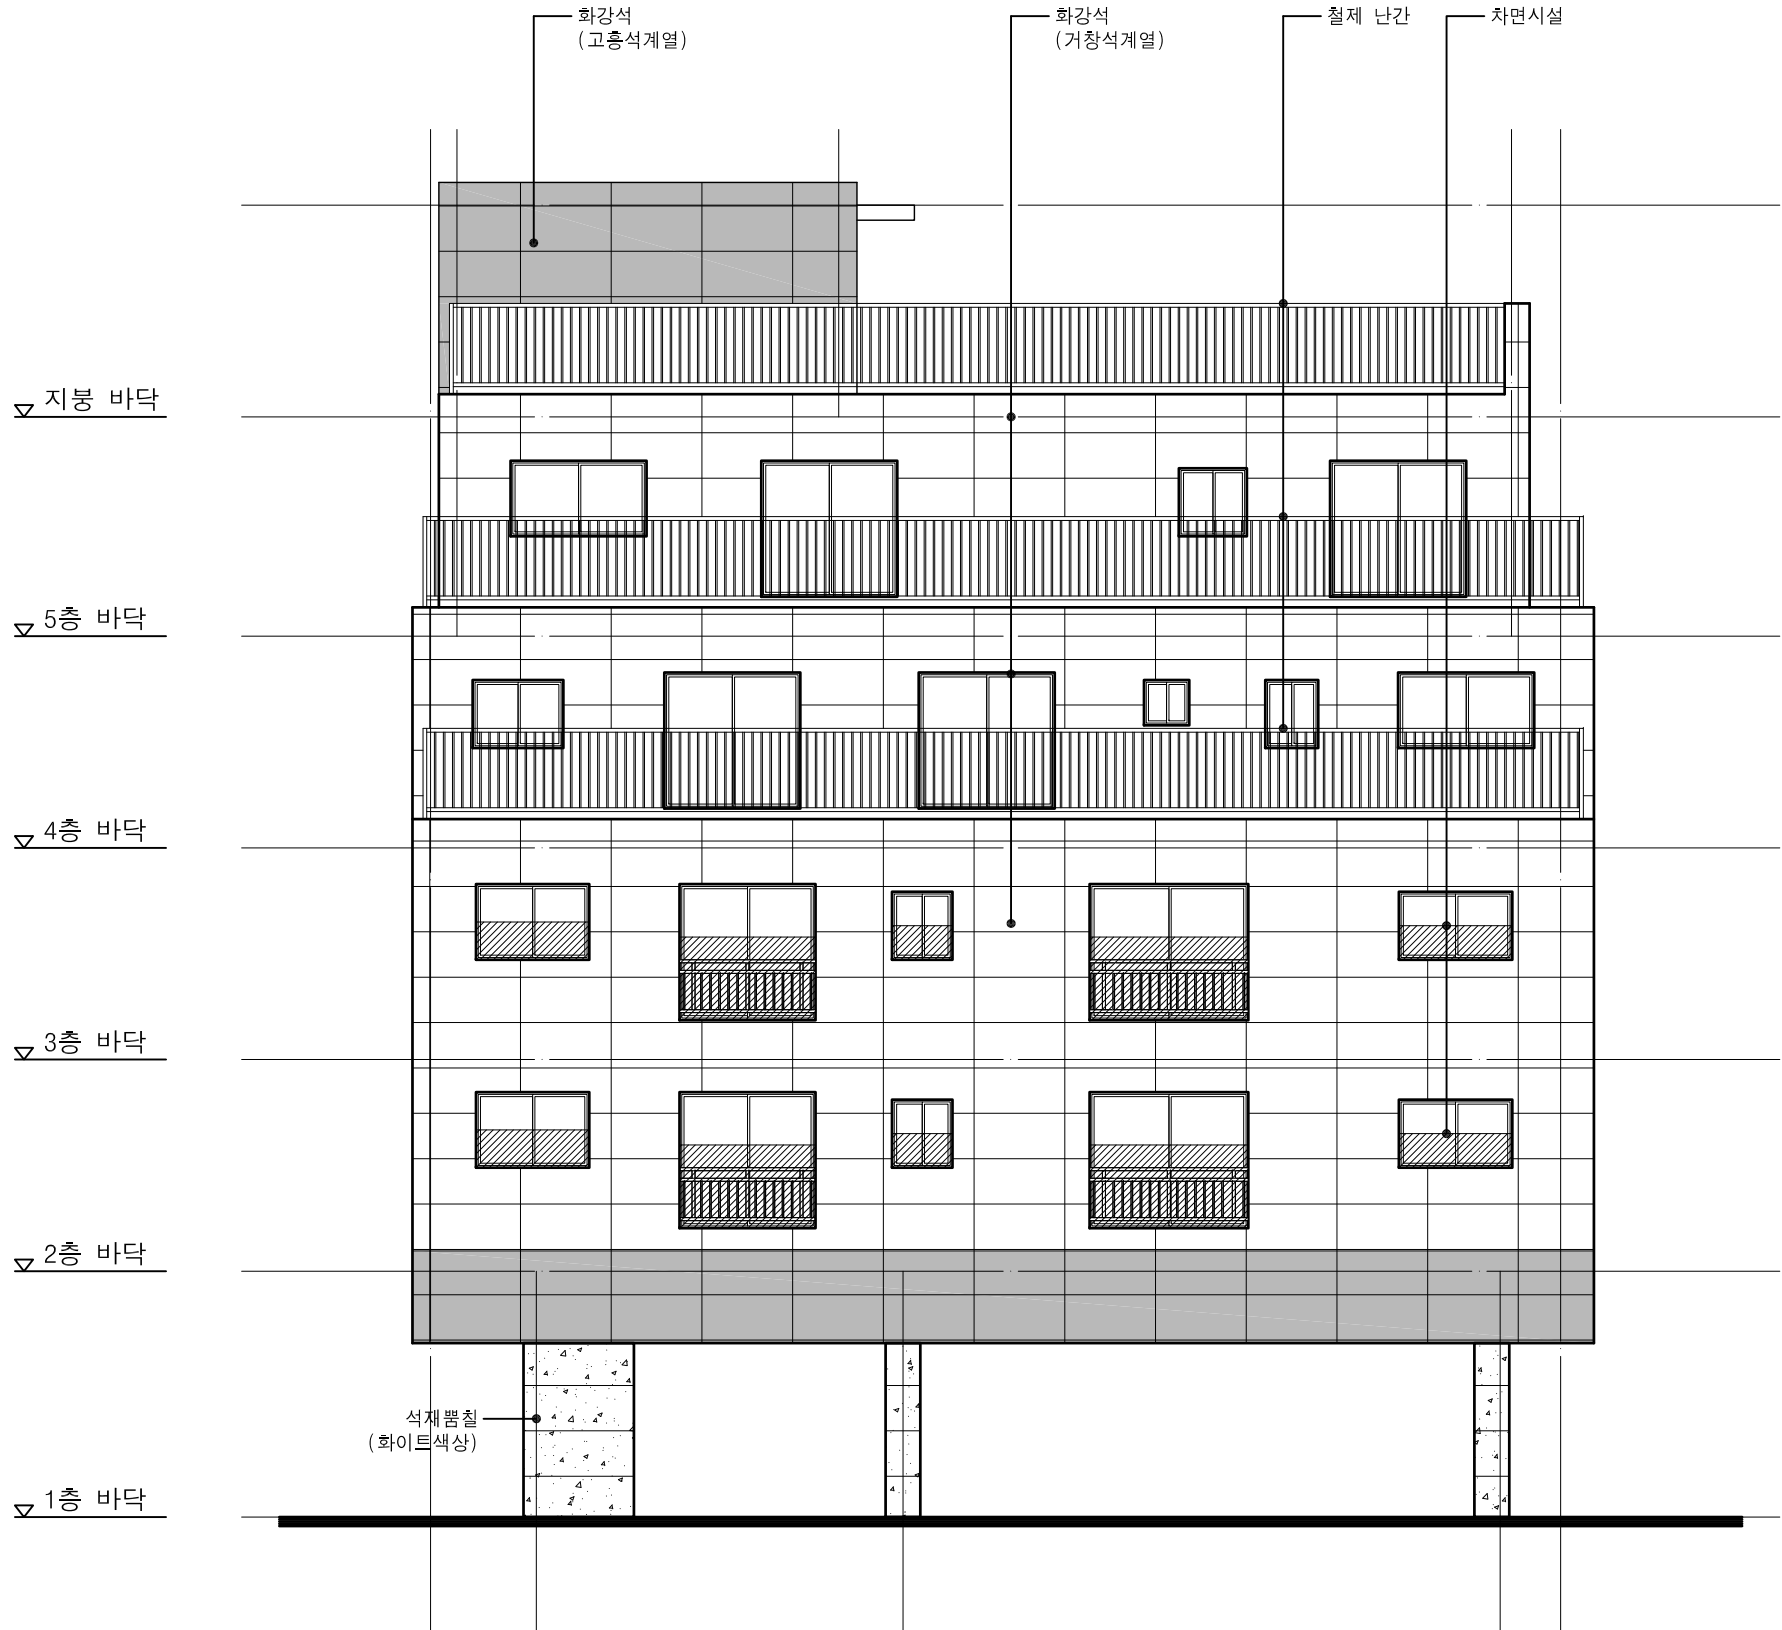

PROJECT TITLE
사업명칭
상도동 335-155호
도시형생활주택(소형주택)
연립주택 신축공사

NAME OF DRAWING
도면명
입면도-4

NOTE
주 기
창호 PVC 블랙

NO. ▲ REVISIONS ▲ DATE
번호 수정 일자

DESIGNED BY
설 계

CHECKED BY
심 사

APPROVED BY
승 인

CONSULTANTS
협동설계

SCALE
축척 1/100

DATE
일자 2024. 11.

DWG NO.
도면번호 A-34

SHEET NO.
입면번호 □—□□□


dawoon
건축사사무소 다움건축
THE ARCHITECTS DESIGN GROUP
TEL. 02.414.6061 (代)
FAX. 02.414.6062

좌 측 면 도
SCALE : A3 : 1/100