


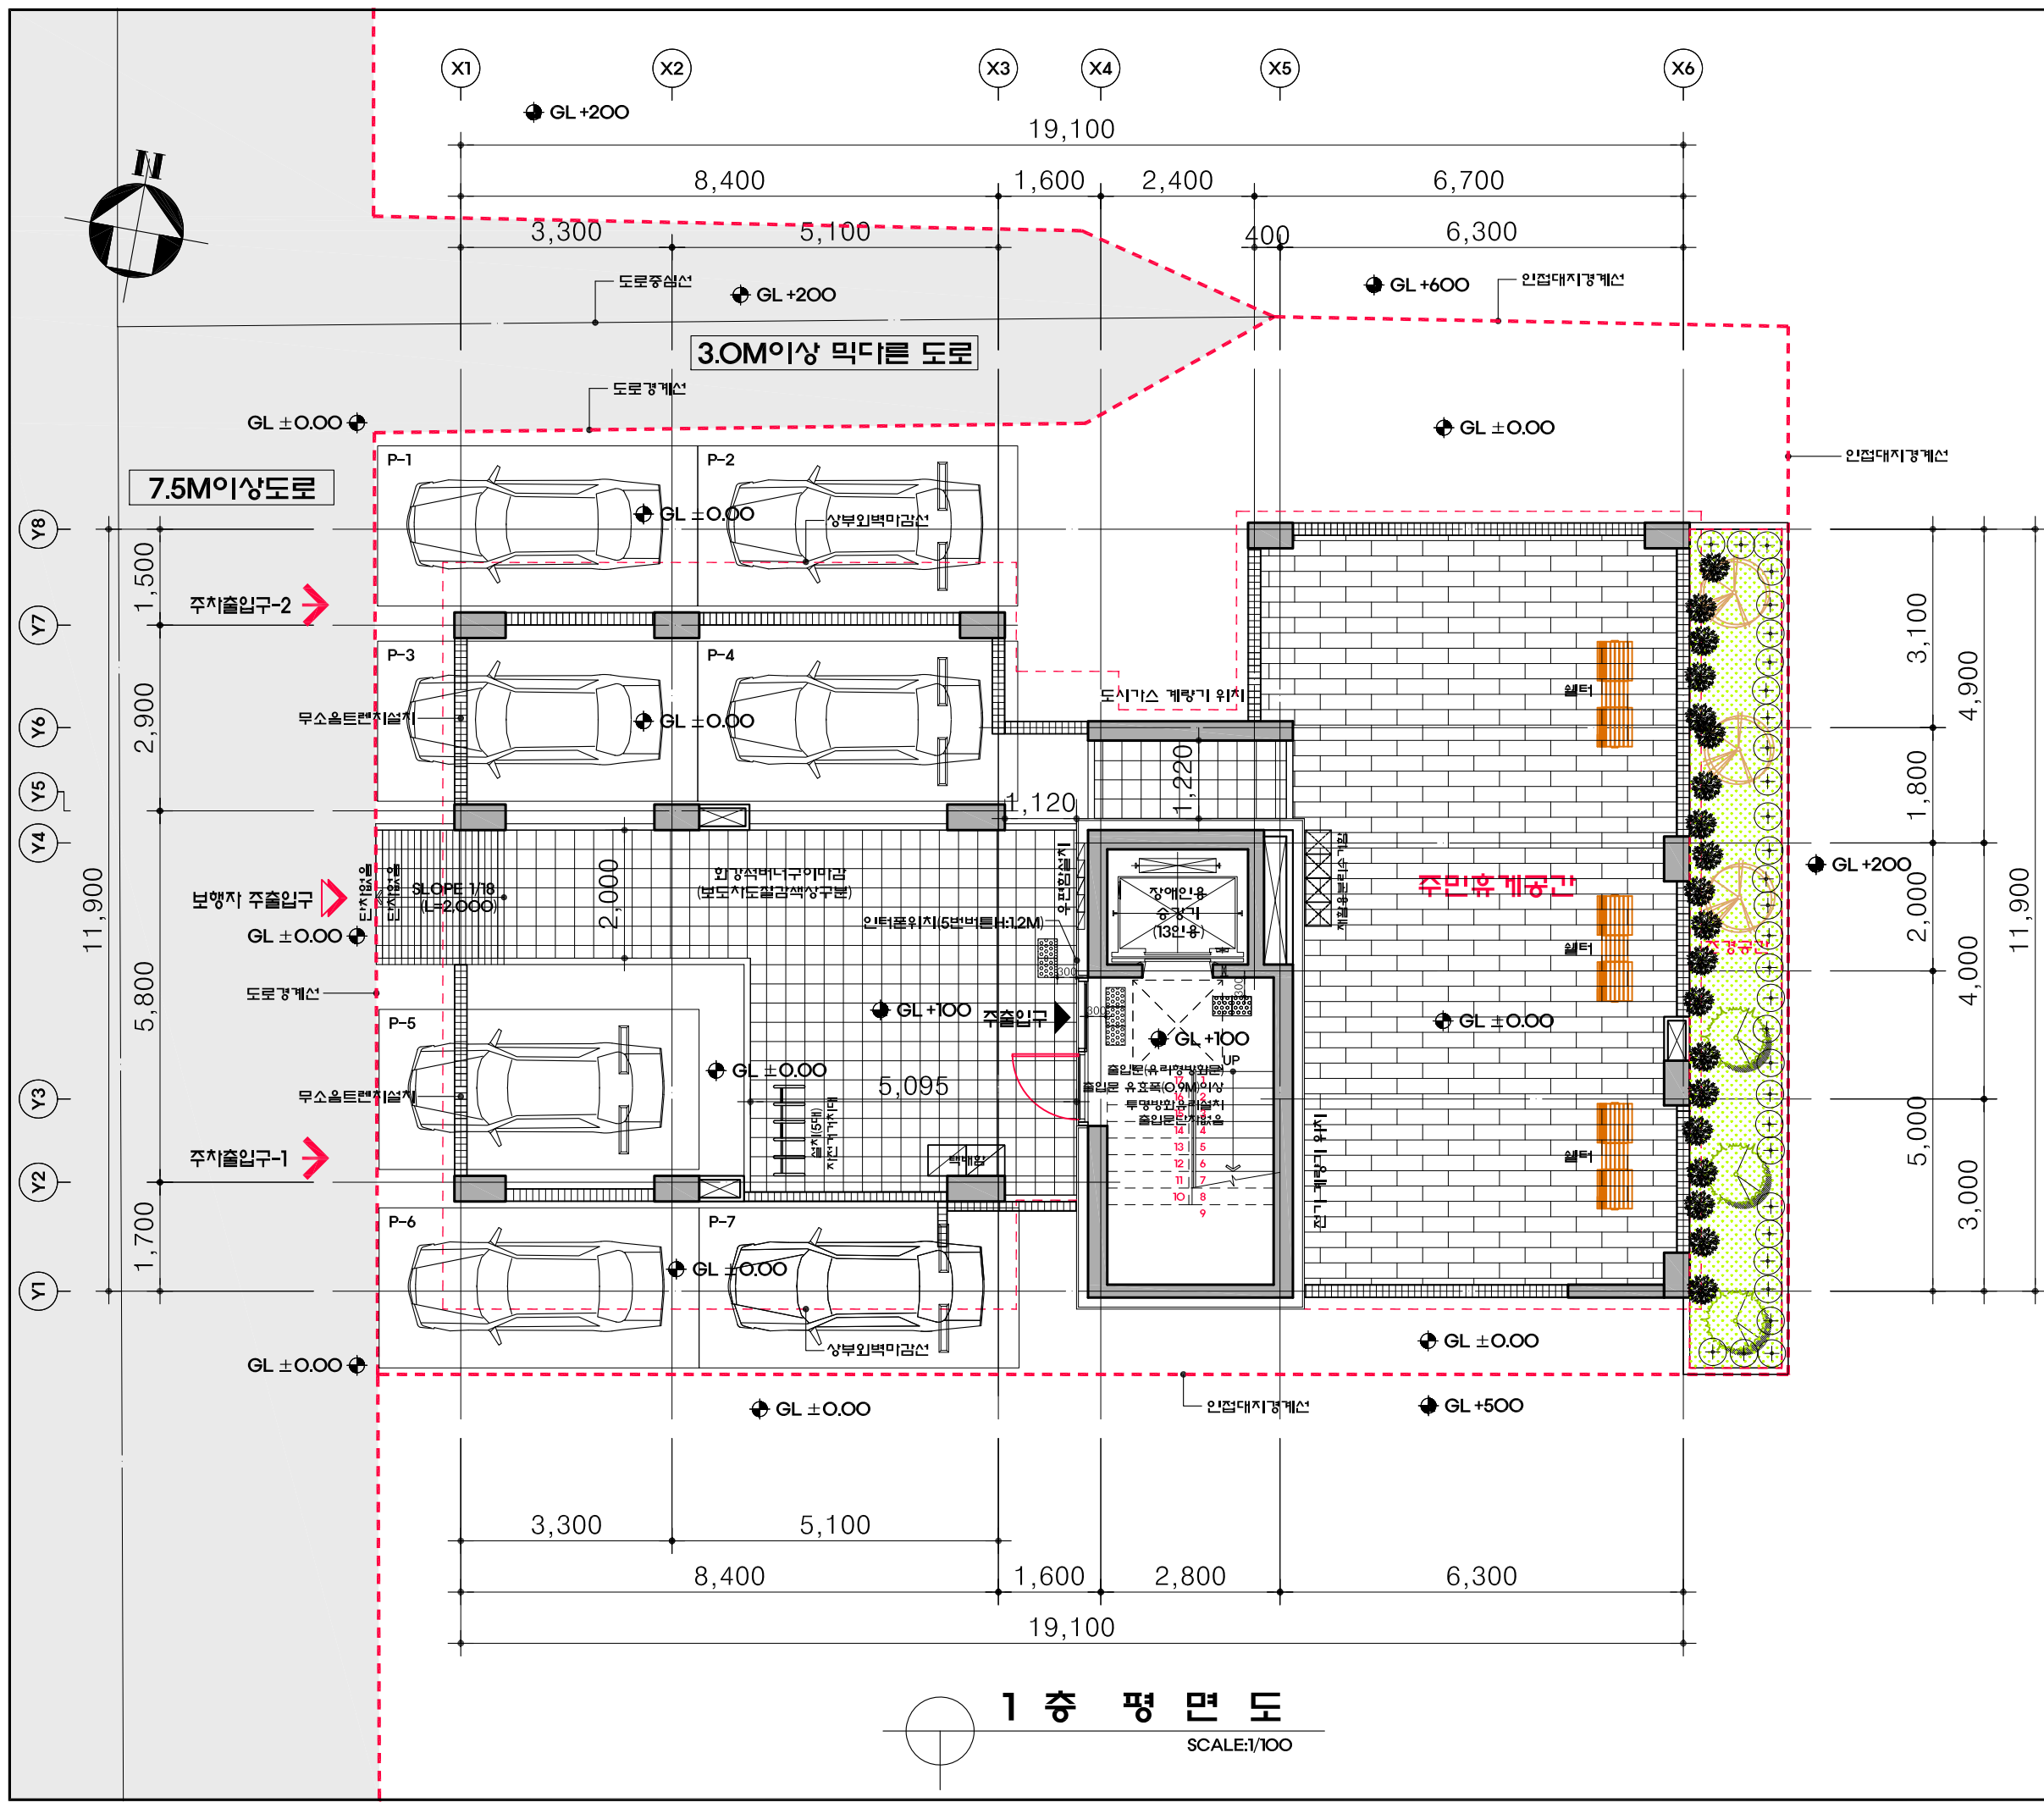


주 기	
1	접근로의 유효폭 12미터 이상 확보
2	접근로의 기울기는 1/18 이하로 설치
3	대지 내를 연결하는 주접근로에 단차가 있을 경우 그 높이는 2cm 이하가 되도록 설치
4	접근로는 지도와 색상과 재질을 달리하여 반드시 보자별리를 명확히 해주어야 함
5	접근로의 바닥표면은 질미끄러지지 않는 재료로 평탄하게 마감하여야 함
6	블록 등으로 접근로를 표상하는 경우에는 이음새의 틈이 벌어지지 아니하도록 하여 면이 평탄하게 시공하여야 함
7	완개를 설치할 경우 완개에 격자구멍 또는 물새의 양방향 간격이 2cm 이하가 되도록 설치
8	점형블록은 매립형으로 설치함(향색KS제품)
계단실 주출입문	
2,300 1,025 FL 유효폭, 유효높이=1,025X2,100 상시, 문틀, 부속철물일체(방한용)	
* 점형블록	
300 300 KS표준 황색매립형 우레탄재질로 설치 한다	

NOTE:

PROJECT	미포구 성산동 3-20번지 도시형 생활 주택 단지형 다세대주택 신축공사 (청년주택)
APPROVED BY	건축사 
 (주)유엔케이 건축사무소 Planners, Architects, Engineers, Consultants 서울특별시 서초구 미포로6길 29, 영성빌딩 4층 TEL : 070-7774-3988, FAX : 070-7966-3903 010-4422-4121	
TITLE	1 층 평 면 도
날짜 DATE:	2026. 03
SCALE	1 / 100
DWG NO.	A - 027
REV.	

1 층 평 면 도
SCALE:1/100

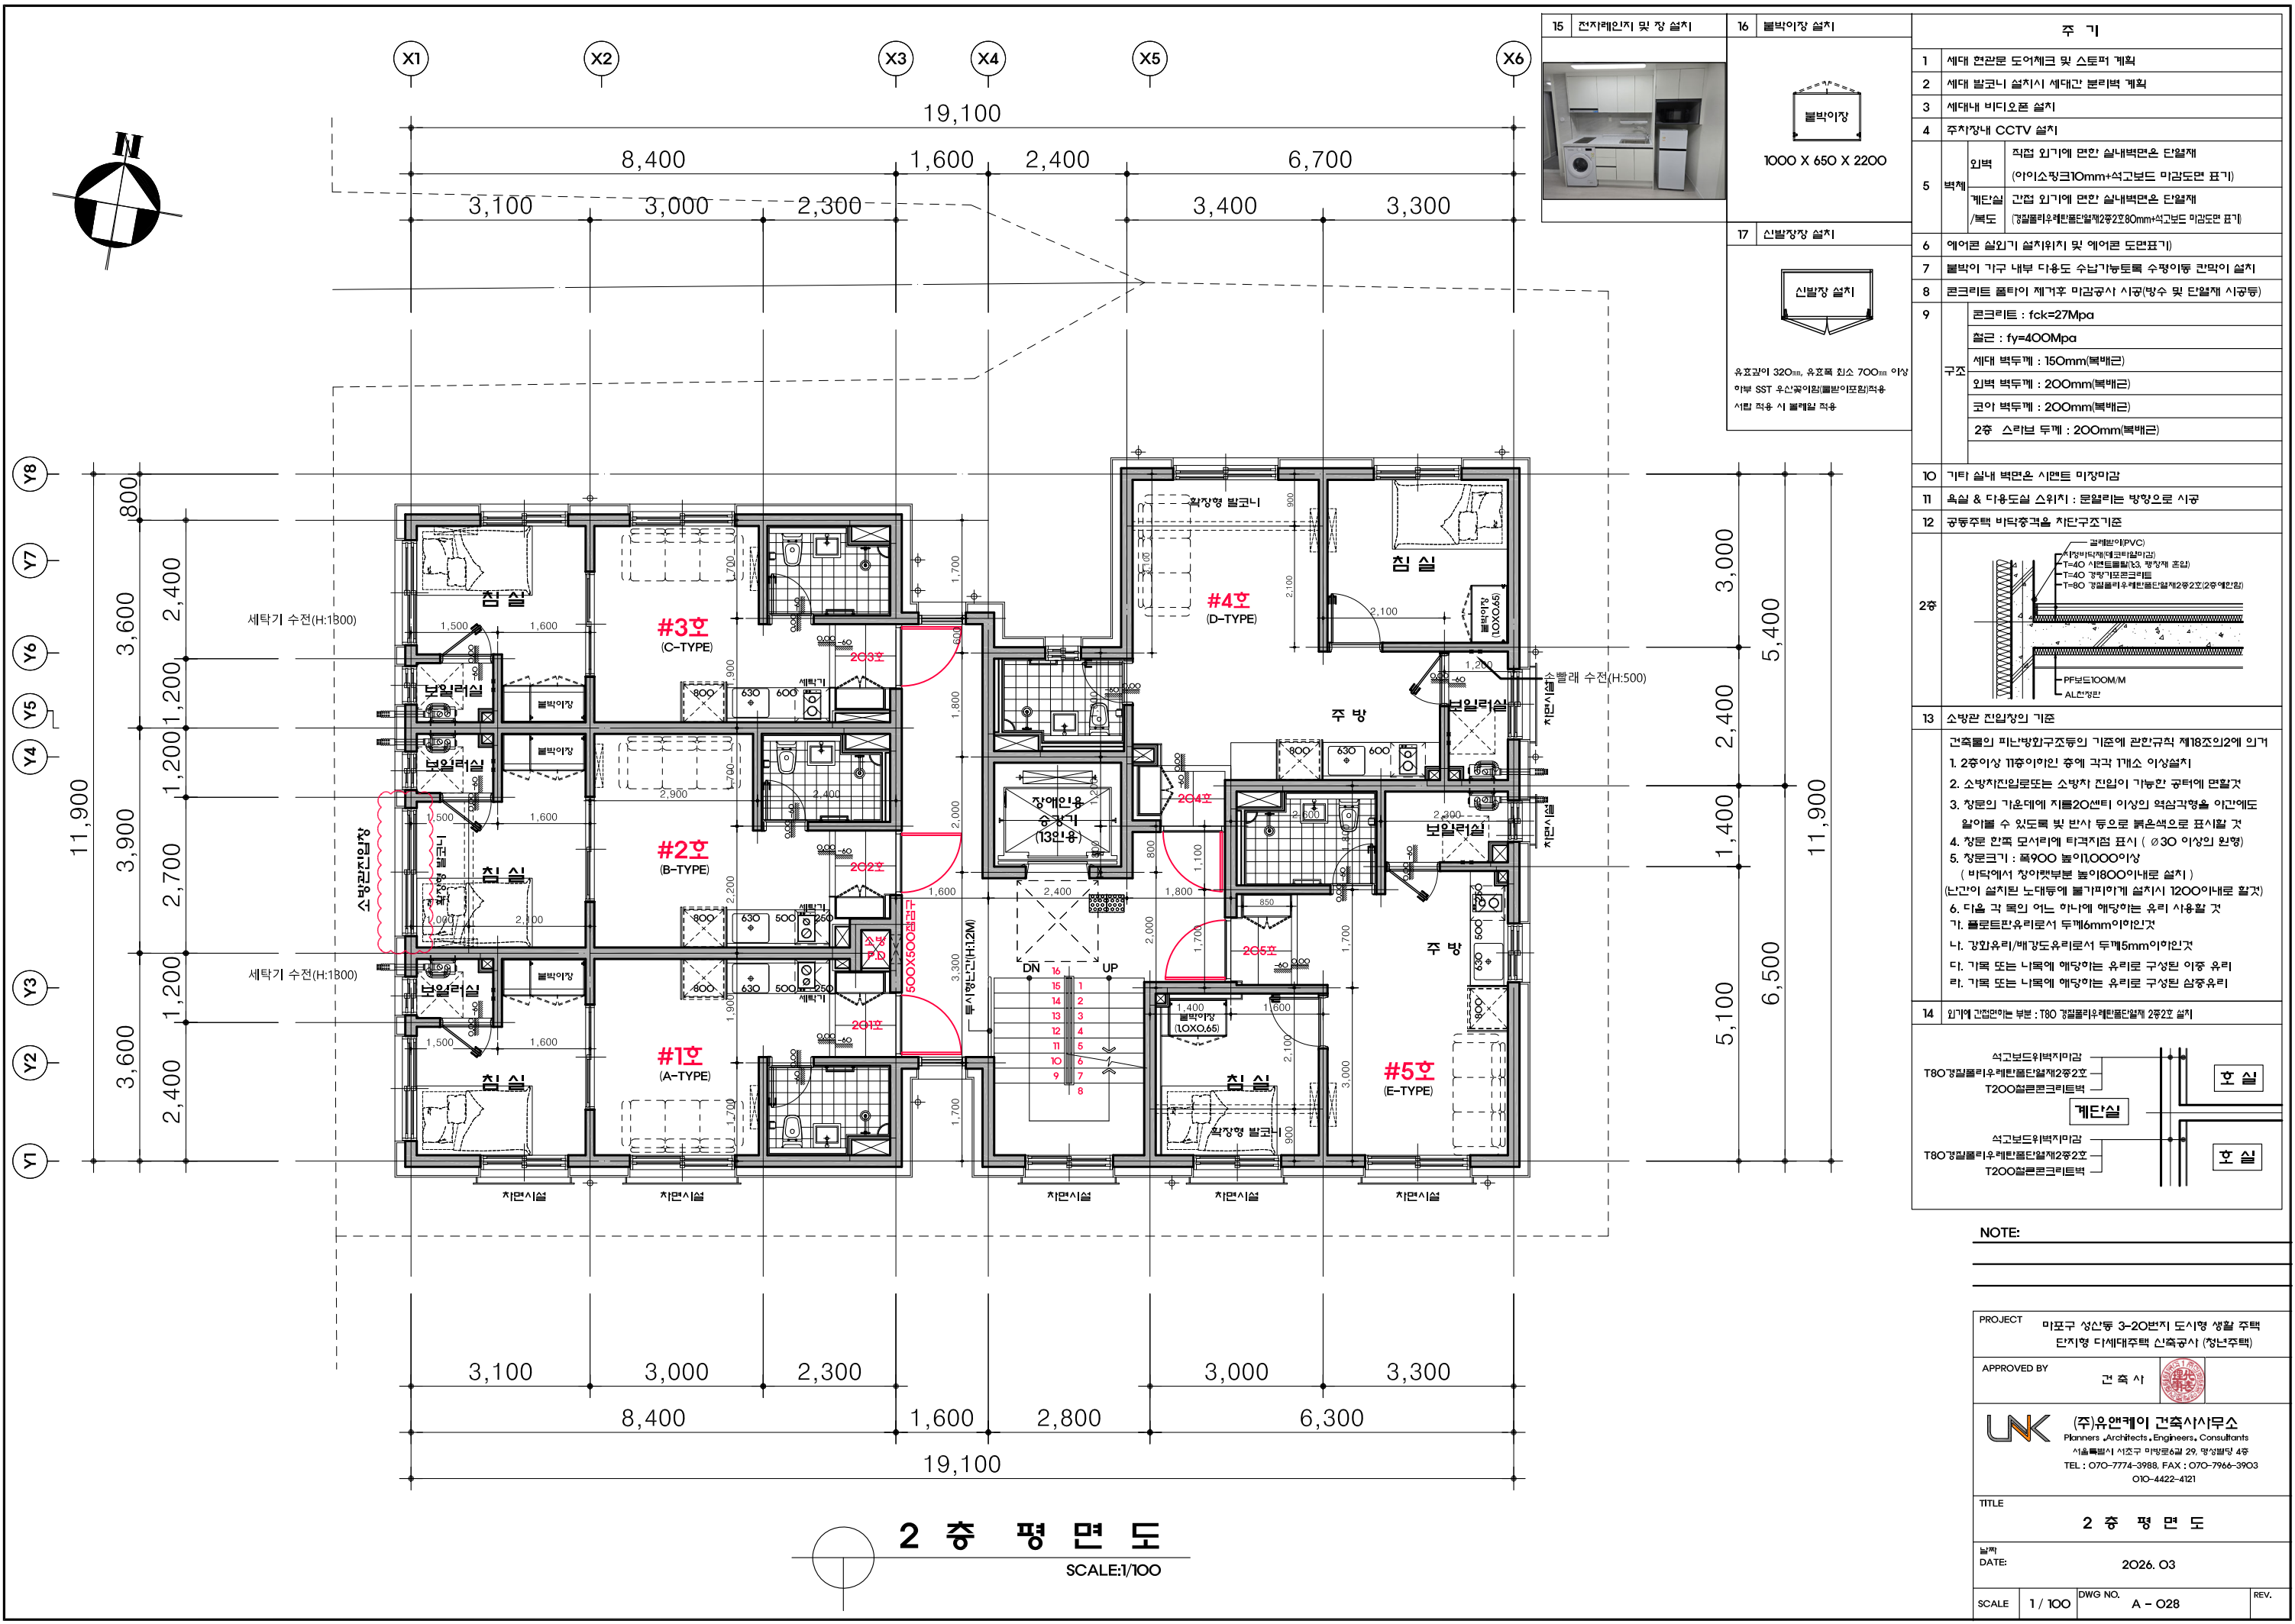

주 기		
1	세대 현관문 도어체크 및 스토퍼 계획	
2	세대 발코니 설치시 세대간 분리벽 계획	
3	세대내 바이오폰 설치	
4	주차장내 CCTV 설치	
5	벽체	직접 외기에 면한 실내벽면은 단열재 (아이소핑크10mm+석고보드 마감도면 표기)
		계단실 간접 외기에 면한 실내벽면은 단열재 (강질폴리우레탄폼단열재2중2호80mm+석고보드 마감도면 표기)
6	에어콘 설치위치 및 에어컨 도면표기)	
7	불박이 가구 내부 다용도 수납기능토록 수평이동 칸막이 설치	
8	콘크리트 골타이 제거후 미감공사 시공(방수 및 단열재 시공등)	
9	구조	콘크리트 : fck=27Mpa
		철근 : fy=400Mpa
		세대 벽두께 : 150mm(복배근)
		외벽 벽두께 : 200mm(복배근)
		코어 벽두께 : 200mm(복배근)
		2층 스리브 두께 : 200mm(복배근)
10	기타 실내 벽면은 시멘트 미장미감	
11	욕실 & 다용도실 스위치 : 문열리는 방향으로 시공	
12	공동주택 바닥충격음 차단구조기준	
2층		
13	소방관 진입장의 기준 건축물의 피난방화구조등의 기준에 관한규칙 제18조외2에 의거 1. 2층이상 11층이하인 층에 각각 1개소 이상설치 2. 소방차진입로또는 소방차 진입이 가능한 공터에 면할것 3. 층문의 가운데에 지름20센티 이상의 역삼각형을 아간에도 알아볼 수 있도록 빛 반사 등으로 붉은색으로 표시할 것 4. 층문 왼쪽 모서리에 타격지점 표시 (Ø30 이상의 원형) 5. 층문크기 : 폭900 높이1,000이상 (비탁에서 창아랫부분 높이800이내로 설치) (난간이 설치된 노대등에 불기러미가게 설치시 1200이내로 할것) 6. 다용 각 폭의 어느 하나에 해당하는 유리 사용할 것 가. 폴로트란유리로서 두께6mm이상이란것 나. 강화유리/배강도유리로서 두께5mm이상이란것 다. 기록 또는 기록에 해당하는 유리로 구성된 이중 유리 라. 기록 또는 기록에 해당하는 유리로 구성된 삼중유리	
14	입구에 간접연하는 부분 : T80 경질폴리우레탄폼단열재 2중2호 설치 	

NOTE:

PROJECT 미포구 성산동 3-20번지 도시형 생활 주택
단지형 다세대주택 신축공사 (정년주택)


APPROVED BY 건축사

LINK (주)유엔케이 건축사사무소
Planners, Architects, Engineers, Consultants
서울특별시 서초구 미포동6길 29, 영성빌딩 4층
TEL : 070-7774-3988, FAX : 070-7966-3903
010-4422-4121

TITLE 2층 평면도

날짜 DATE: 2026. 03

SCALE 1/100 DWG NO. A - 028 REV.

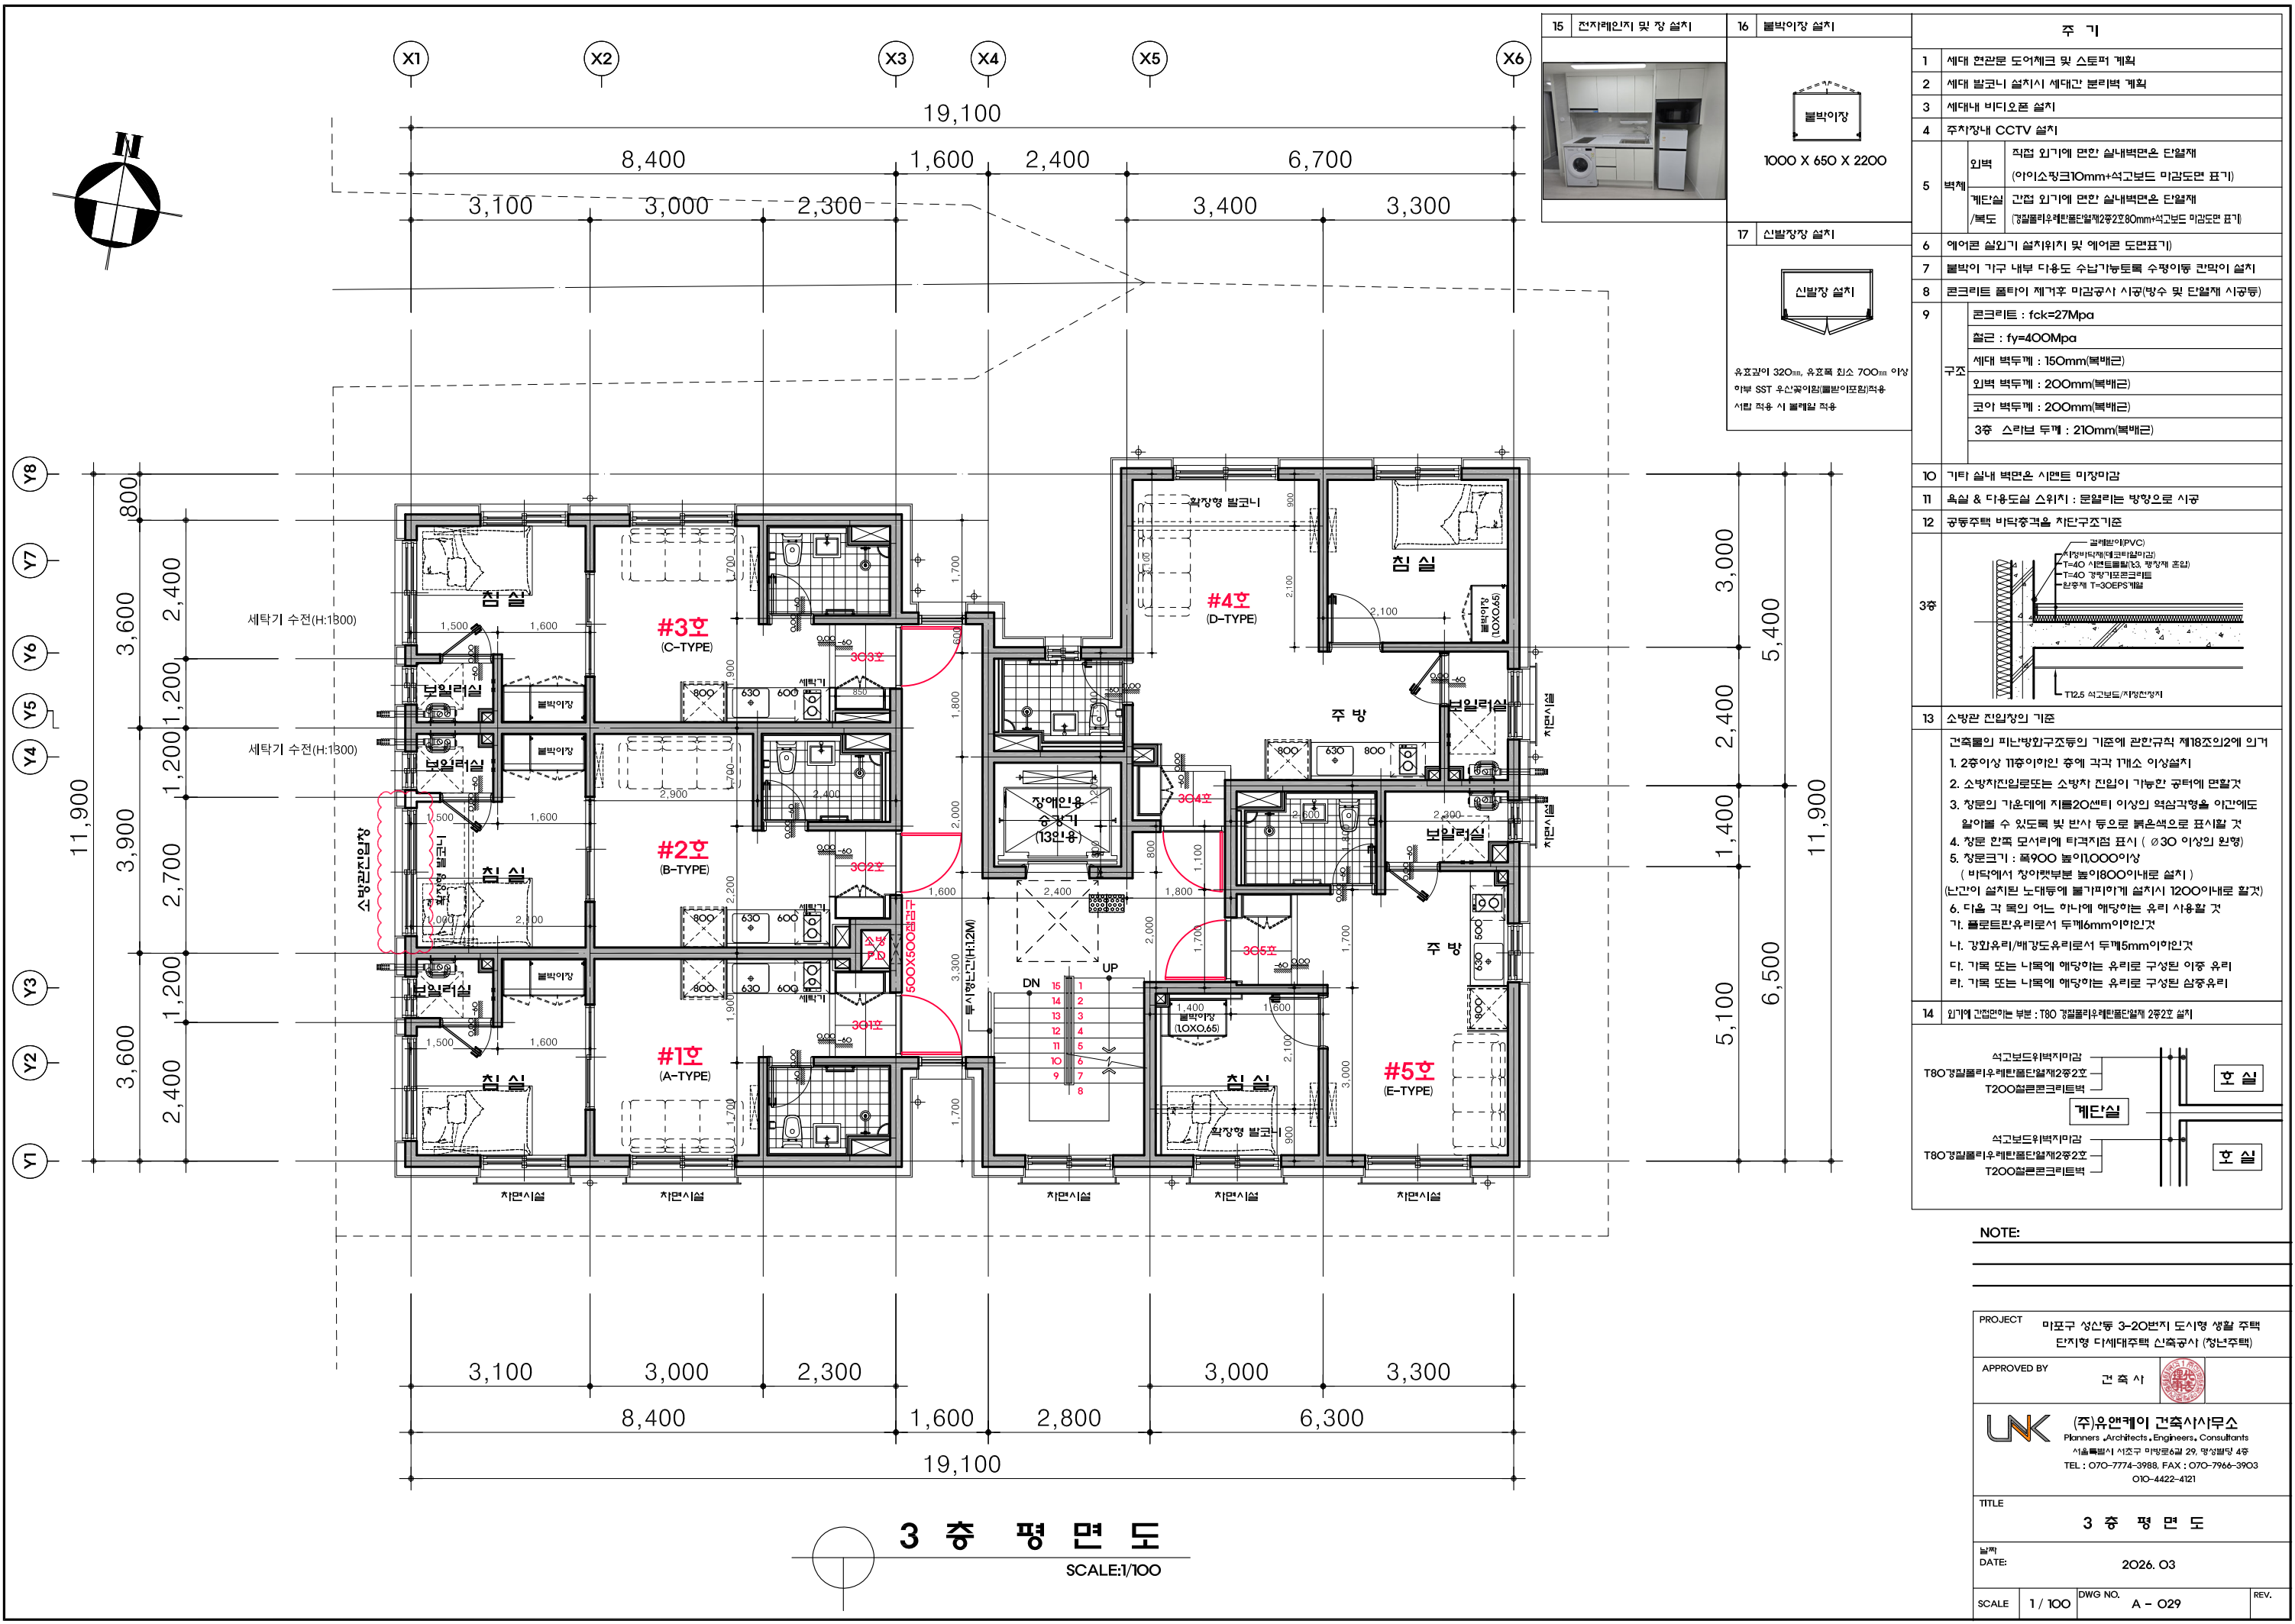


15	전자레인지 및 장 설치
16	불박이장 설치
17	신발장장 설치

주 기	
1	세대 현관문 도어체크 및 스토퍼 계획
2	세대 발코니 설치시 세대간 분리벽 계획
3	세대내 바이오폰 설치
4	주차장내 CCTV 설치
5	벽체
6	에어콘 실외기 설치위치 및 에어콘 도면표기
7	불박이 가구 내부 다용도 수납기능토록 수평이동 칸막이 설치
8	콘크리트 폴타이 제거후 미감공사 시공(방수 및 단열재 시공등)
9	콘크리트 : fck=27Mpa 철근 : fy=400Mpa 세대 벽두께 : 150mm(복배근) 외벽 벽두께 : 200mm(복배근) 코어 벽두께 : 200mm(복배근) 3층 스크린 두께 : 210mm(복배근)
10	기타 실내 벽면은 시멘트 미장미감
11	욕실 & 다용도실 스위치 : 문열리는 방향으로 시공
12	공동주택 바닥충격음 차단구조기준
13	소방관 진입장의 기준
14	입구에 근접한이는 부분 : T80 경질폴리우레탄단열재 2중2호 설치

NOTE:

PROJECT	미포구 성산동 3-20번지 도시형 생활 주택 단지형 다세대주택 신축공사 (정년주택)
APPROVED BY	건축사
LINK	(주)유엔케이 건축사사무소 Planners, Architects, Engineers, Consultants 서울특별시 서초구 미포동6길 29, 영성빌딩 4층 TEL : 070-7774-3988, FAX : 070-7966-3903 010-4422-4121
TITLE	3 층 평 면 도
날짜 DATE:	2026. 03
SCALE	1 / 100
DWG NO.	A - 029
REV.	

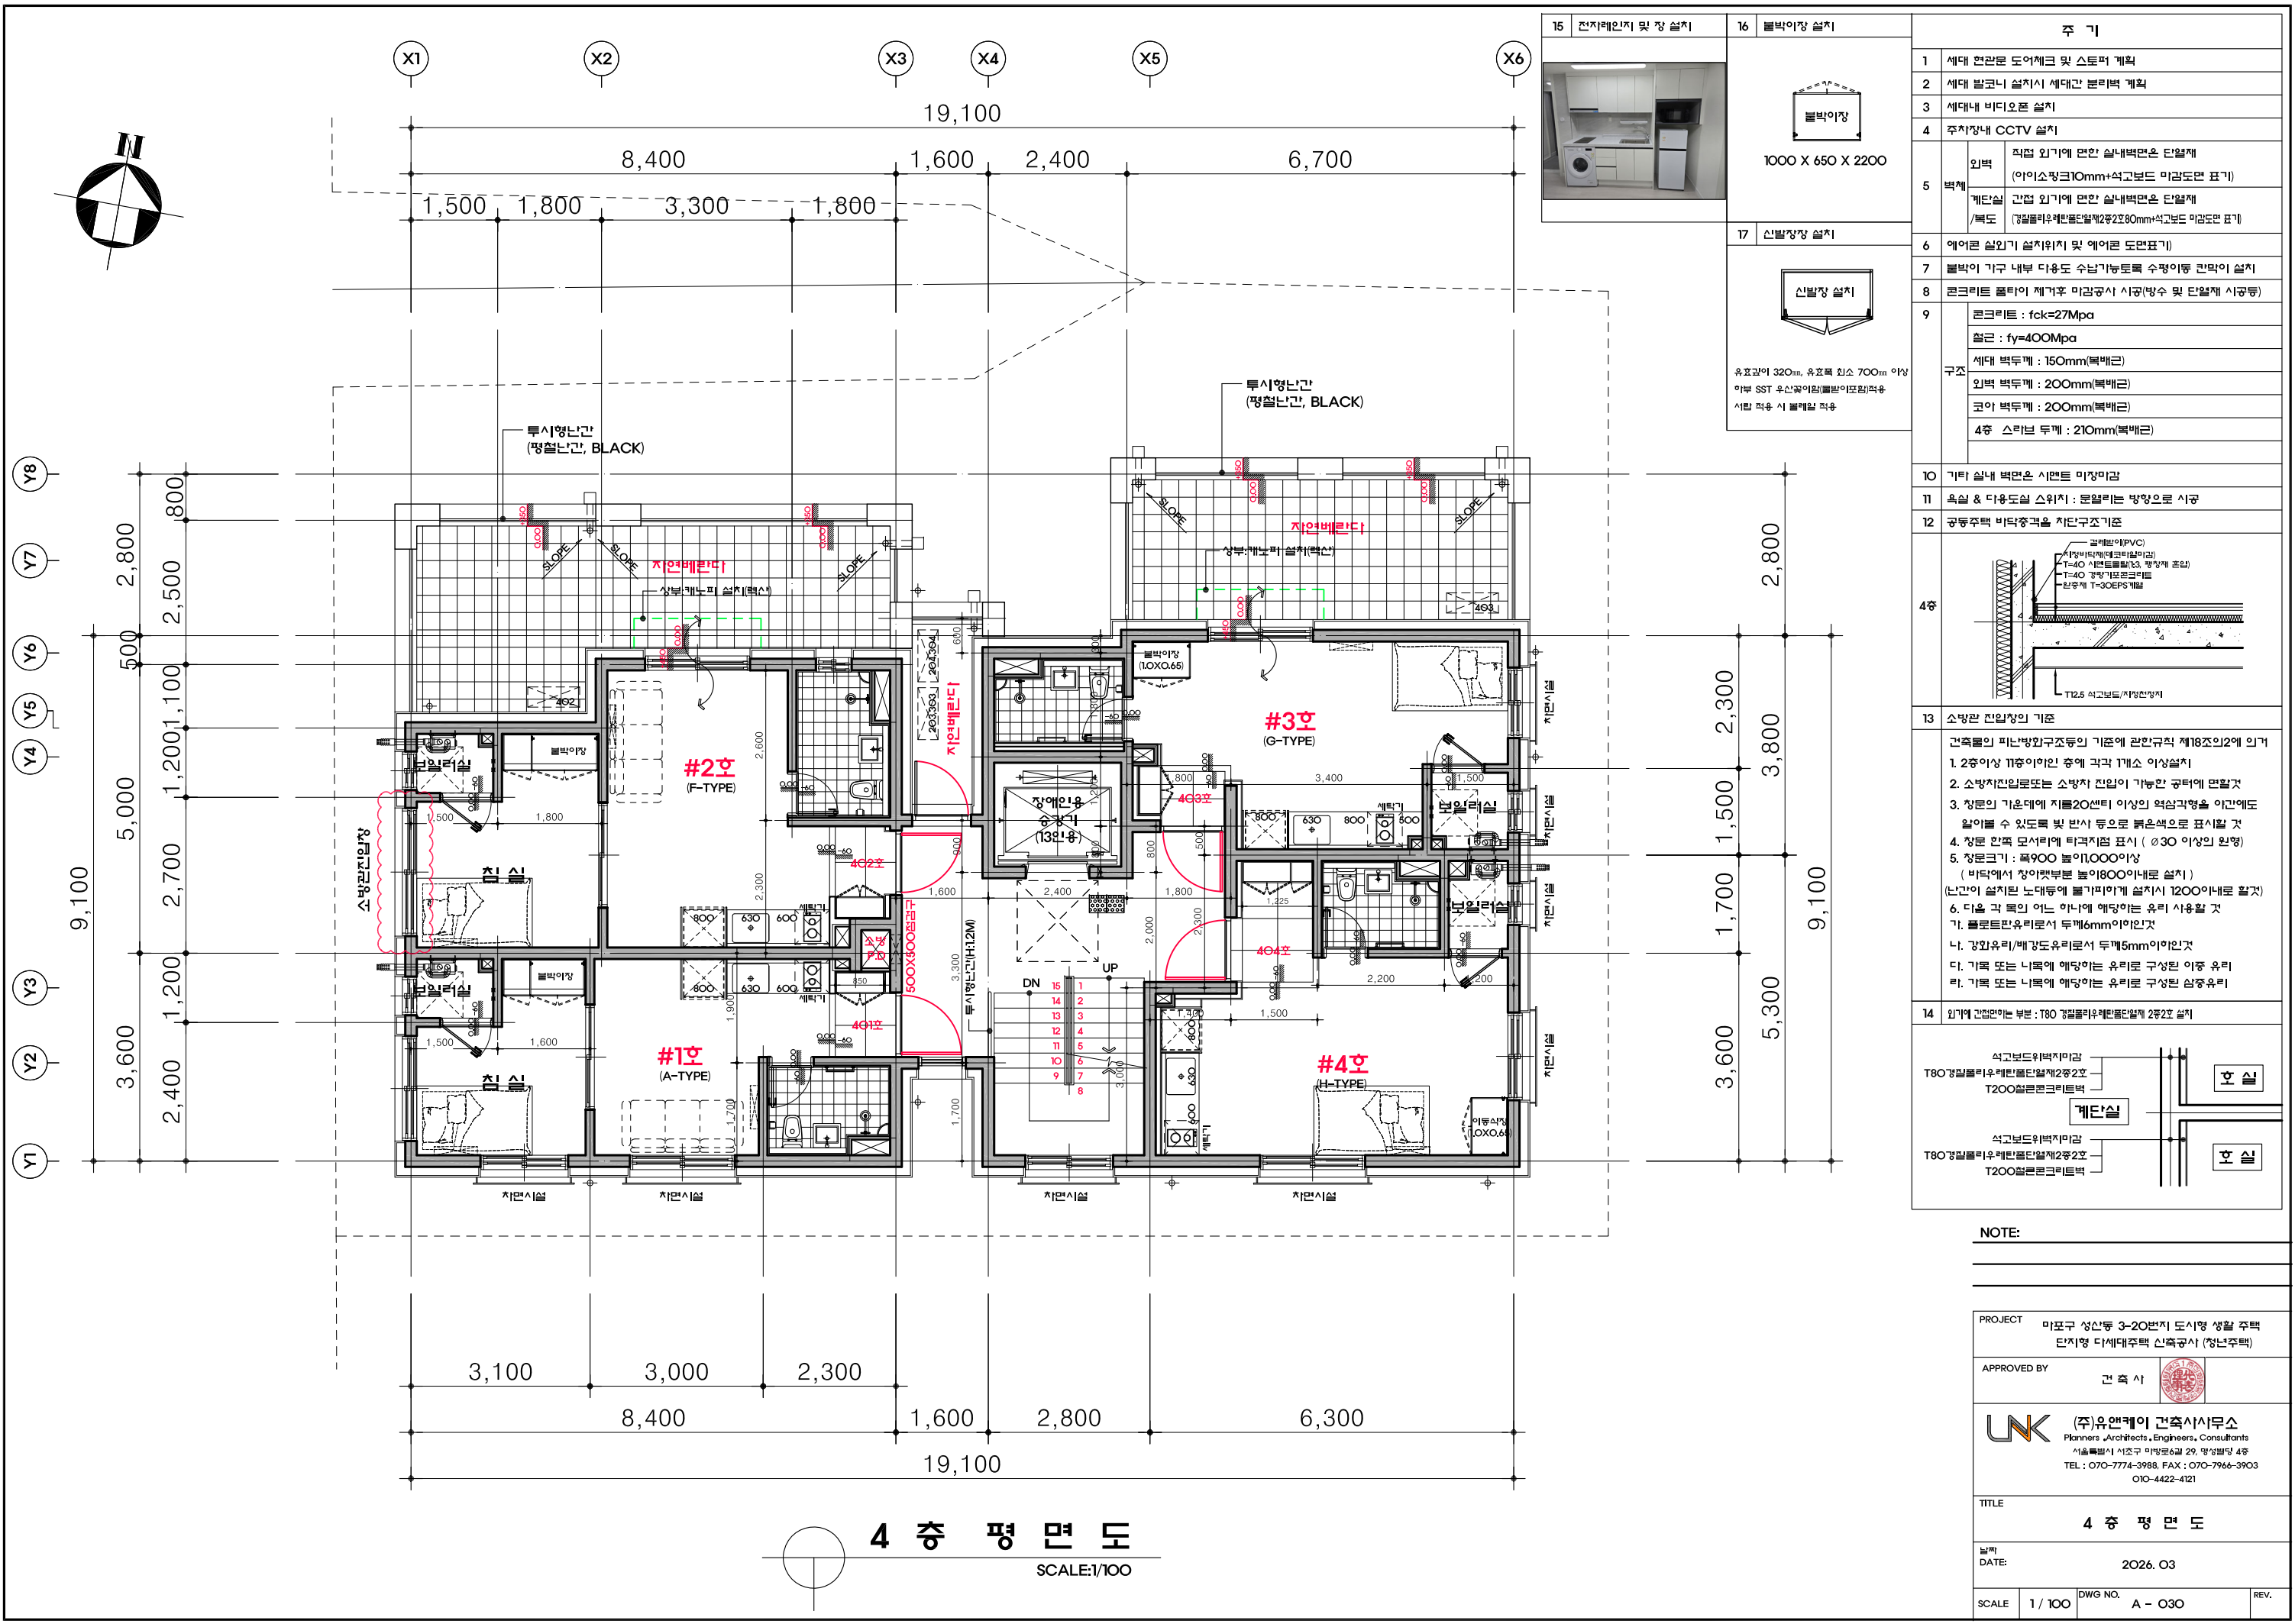

4 층 평 면 도

SCALE:1/100

주 기		
1	세대 현관문 도어체크 및 스토퍼 계획	
2	세대 발코니 설치시 세대간 분리벽 계획	
3	세대내 비디오폰 설치	
4	주차장내 CCTV 설치	
5	벽체	직접 외기에 면한 실내벽면은 단열재 (아이소핑크10mm+석고보드로 마감도면 표기)
		계단실 /복도 간접 외기에 면한 실내벽면은 단열재 (강질플리우레탄폼단열재2중2호80mm+석고보드로 마감도면 표기)
6	에어콘 실외기 설치위치 및 에어콘 도면표기)	
7	불박이 가구 내부 다용도 수납기능토록 수평이동 칸막이 설치	
8	콘크리트 폴터이 제거후 마감공사 시공(방수 및 단열재 시공등)	
9	구조	콘크리트 : fck=27Mpa
		철근 : fy=400Mpa
		세대 벽두께 : 150mm(복배근)
		외벽 벽두께 : 200mm(복배근)
		코어 벽두께 : 200mm(복배근)
		4층 스리브 두께 : 210mm(복배근)
10	기타 실내 벽면은 시멘트 미장미감	
11	욕실 & 다용도실 스위치 : 문열리는 방향으로 시공	
12	공동주택 바닥충격음 차단구조기준	
4층		
13	소방관 진입장의 기준	
	건축물의 피난방화구조등의 기준에 관한규칙 제18조외2에 의거	
	2. 2층이상 11층이하인 층에 각각 1개소 이상설치	
	2. 소방차진입로또는 소방차 진입이 가능한 공터에 면할것	
	3. 층문의 가운데에 지름20센티 이상의 역삼각형을 아간에도 알아볼 수 있도록 빛 반사 등으로 붉은색으로 표시할 것	
	4. 층문 한쪽 모서리에 타격지점 표시 (Ø30 이상의 원형)	
	5. 층문크기 : 폭900 높이1,000이상 (바닥에서 창아랫부분 높이800이내로 설치) (난간이 설치된 노대등에 불기리하게 설치시 1200이내로 할것)	
	6. 다용도실 또는 욕실에 해당하는 유리 사용할 것 가. 플로트관유리로서 두께6mm이상이란것 나. 강화유리/배강도유리로서 두께5mm이상이란것 다. 기록 또는 기록에 해당하는 유리로 구성된 이중 유리 라. 기록 또는 기록에 해당하는 유리로 구성된 삼중유리	
14	외기에 간접면하는 부분 : T80 강질플리우레탄폼단열재 2중2호 설치	

NOTE:

PROJECT 미포구 성산동 3-20번지 도시형 생활 주택
단지형 다세대주택 신축공사 (정년주택)


APPROVED BY 건축사

LINK (주)유엔케이 건축사사무소
Planners, Architects, Engineers, Consultants
서울특별시 서초구 미망로6길 29, 영성빌딩 4층
TEL : 070-7774-3988, FAX : 070-7966-3903
010-4422-4121

TITLE 4 층 평 면 도

날짜 DATE: 2026. 03

SCALE 1/100 DWG NO. A - 030 REV.


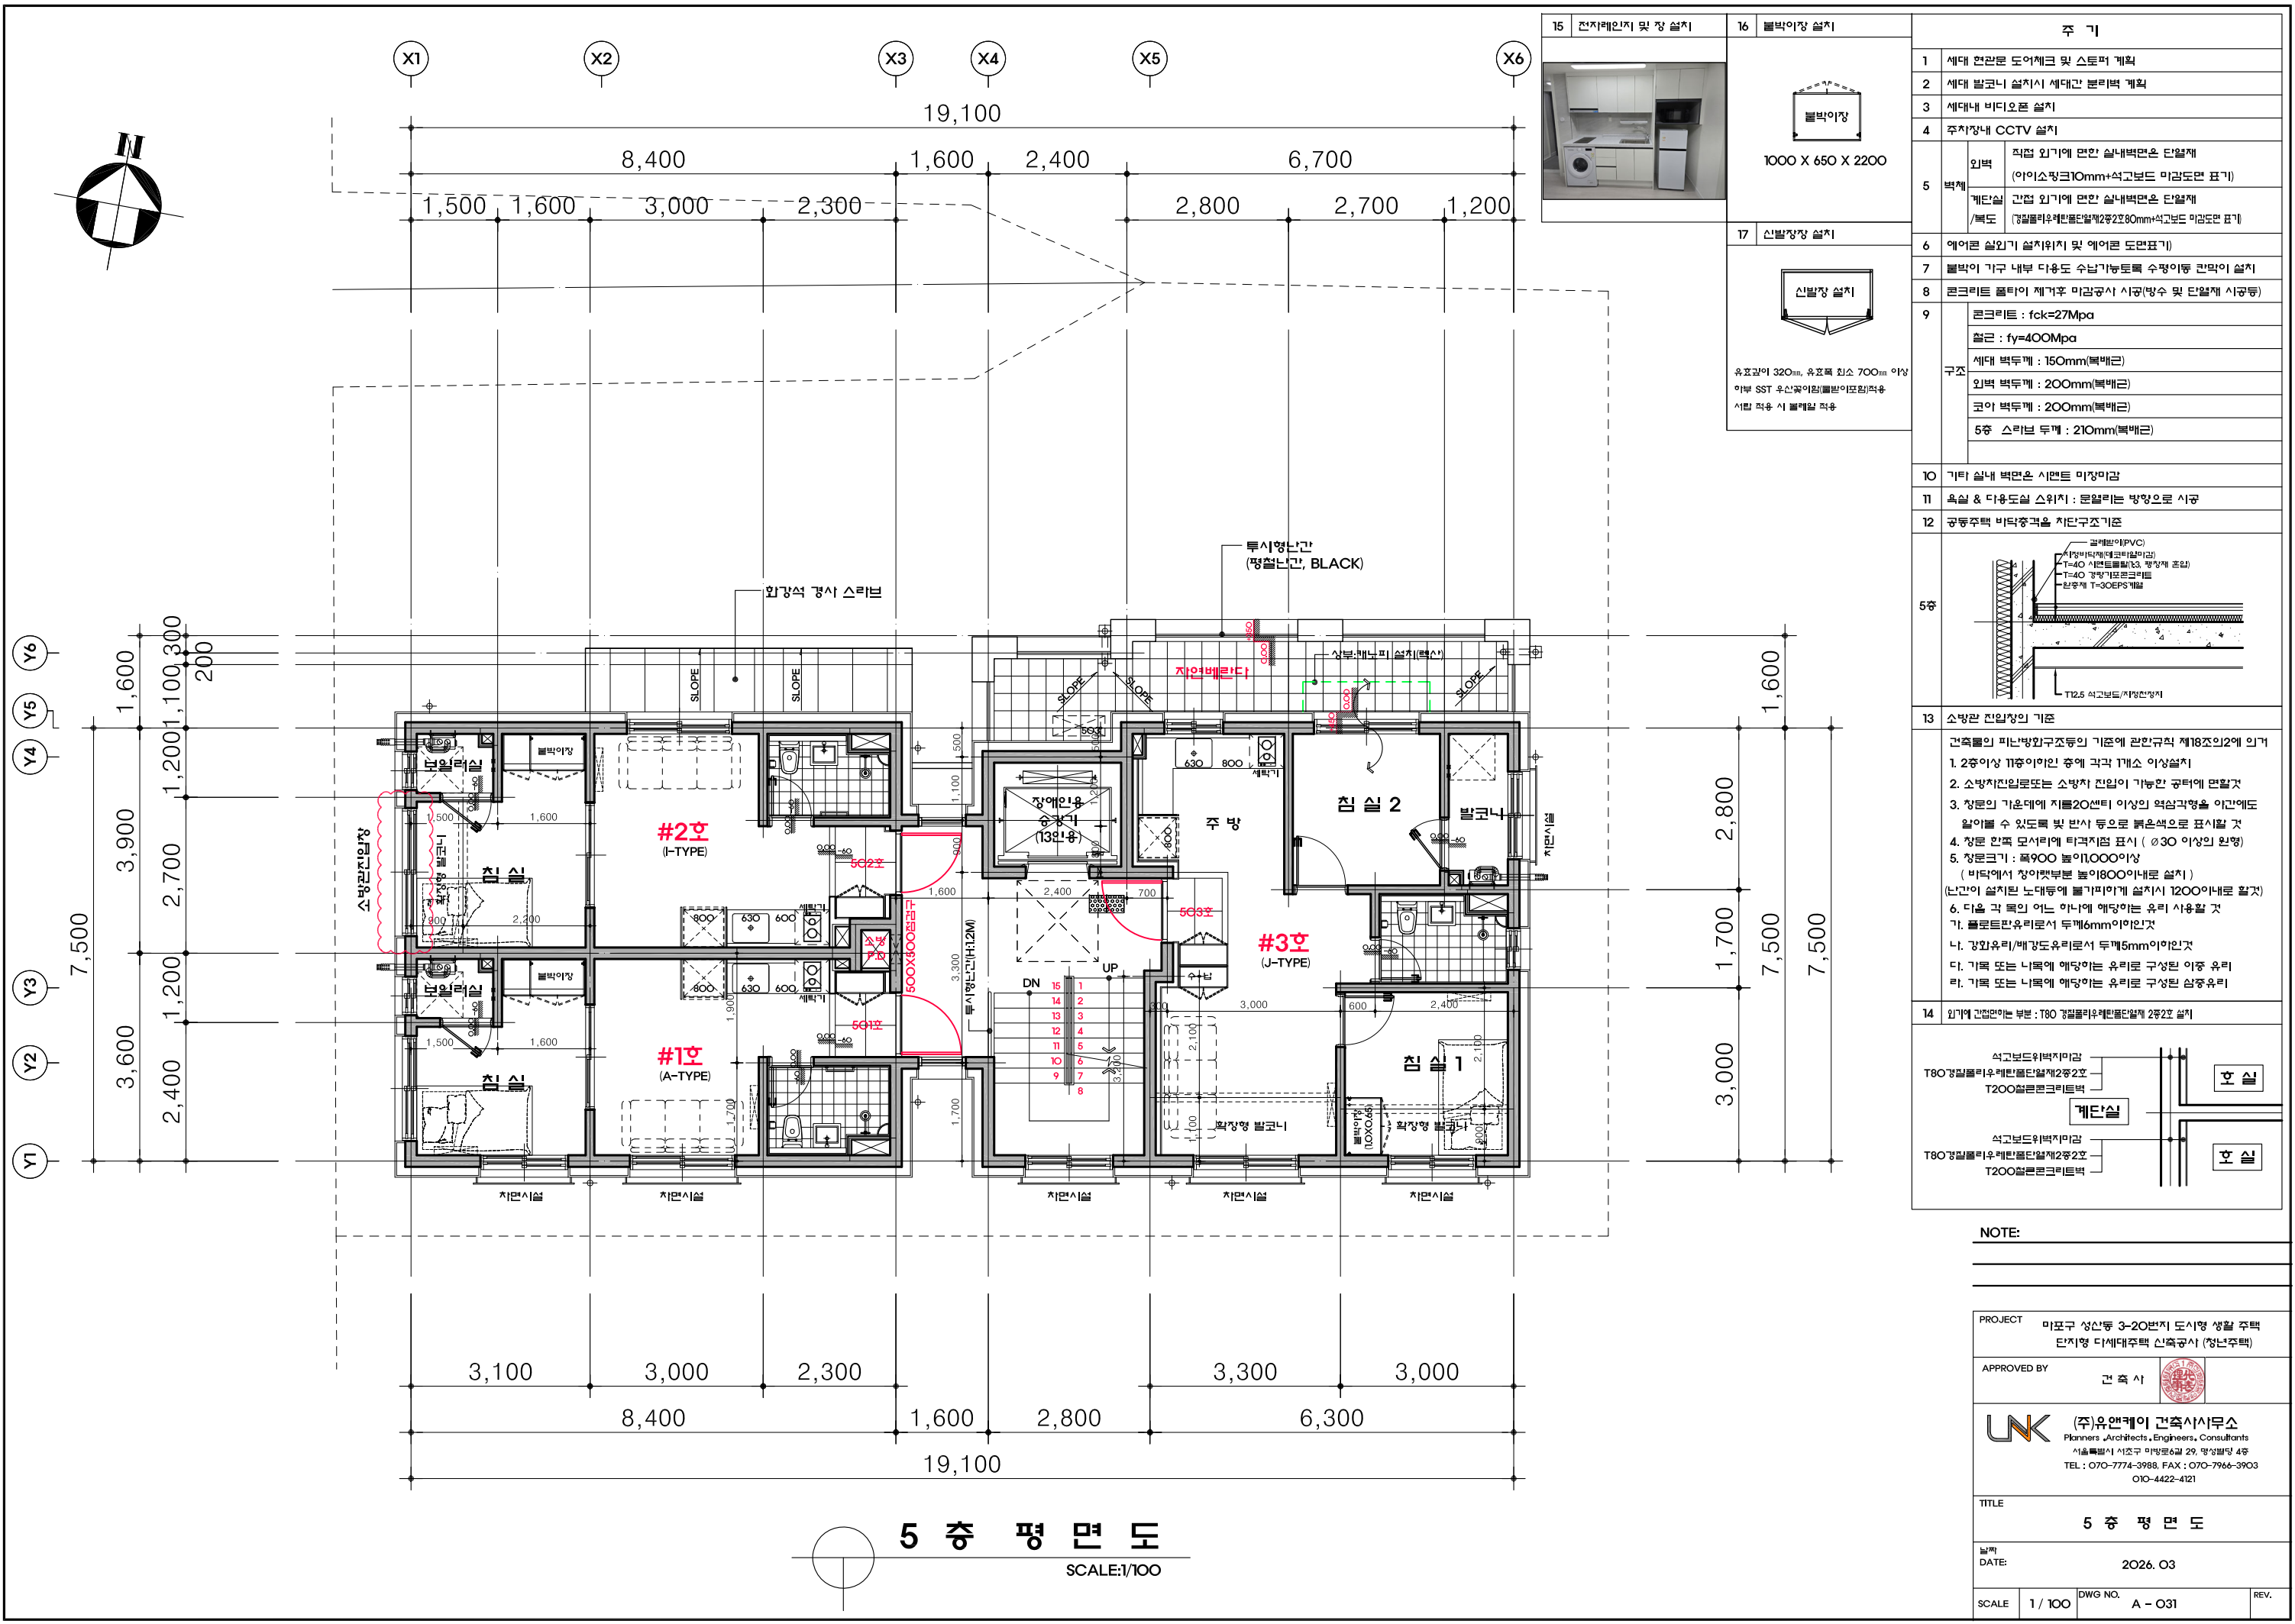


5 층 평 면 도
SCALE:1/100


주 기		
1	세대 현관문 도어체크 및 스토퍼 계획	
2	세대 발코니 설치시 세대간 분리벽 계획	
3	세대내 바이오온 설치	
4	주차장내 CCTV 설치	
5	벽체	직접 외기에 면한 실내벽면은 단열재 (아이소핑크10mm+석고보드로 마감도면 표기) 계단실 /복도 간접 외기에 면한 실내벽면은 단열재 (강질폴리우레탄폼단열재2종2호80mm+석고보드로 마감도면 표기)
6	에어콘 실외기 설치위치 및 에어콘 도면표기)	
7	불박이 가구 내부 다용도 수납기능토록 수평이동 칸막이 설치	
8	콘크리트 골타이 제거후 미감공사 시공(방수 및 단열재 시공등)	
9	구조	콘크리트 : fck=27Mpa 철근 : fy=400Mpa 세대 벽두께 : 150mm(복배근) 외벽 벽두께 : 200mm(복배근) 코어 벽두께 : 200mm(복배근) 5층 스크린 두께 : 210mm(복배근)
10		가터 실내 벽면은 시멘트 미장미감
11		욕실 & 다용도실 스위치 : 문열리는 방향으로 시공
12		공동주택 바닥충격음 차단구조기준
5층		골재층(아)PVC) 자장비드(대규비드(강) T=40mm 시멘트층(최소, 정장제 포함) T=40mm 강방수코팅콘크리트 인장층 T=30EPS 거름 T12.5 석고보드/방청장지
13	소방관 진입장의 기준	
건축물의 피난방화구조등의 기준에 관한규칙 제18조2에 의거		
1. 2층이상 11층이하인 층에 각각 1개소 이상설치		
2. 소방차진입로또는 소방차 진입이 가능한 공터에 면할것		
3. 창문의 가운데에 지름20센티 이상의 역삼각형을 아간에도 알아볼 수 있도록 빛 반사 등으로 붉은색으로 표시할 것		
4. 창문 왼쪽 모서리에 타격지점 표시 (Ø30 이상의 원형)		
5. 창문크기 : 폭900 높이1,000이상 (바닥에서 창아랫부분 높이800이내로 설치) (난간이 설치된 노대등에 불기리하게 설치시 1200이내로 할것)		
6. 다음 각 목의 어느 하나에 해당하는 유리 사용할 것 가. 폴로트랜유리로서 두께6mm이상이란것 나. 강화유리/배강도유리로서 두께5mm이상이란것 다. 기록 또는 기록에 해당하는 유리로 구성된 이중 유리 라. 기록 또는 기록에 해당하는 유리로 구성된 삼중유리		
14	입구에 간접연하는 부분 : T80 강질폴리우레탄폼단열재 2종2호 설치	

NOTE:

PROJECT		마포구 성산동 3-20번지 도시형 생활 주택 단지형 다세대주택 신축공사 (정년주택)	
APPROVED BY		건축사	
		(주)유엔케이 건축사사무소 Planners, Architects, Engineers, Consultants 서울특별시 서초구 역삼로6길 29, 영성빌딩 4층 TEL : 070-7774-3988, FAX : 070-7966-3903 010-4422-4121	
TITLE			
5 층 평 면 도			
날짜 DATE:		2026. 03	
SCALE	1 / 100	DWG NO.	A - 031
			REV.

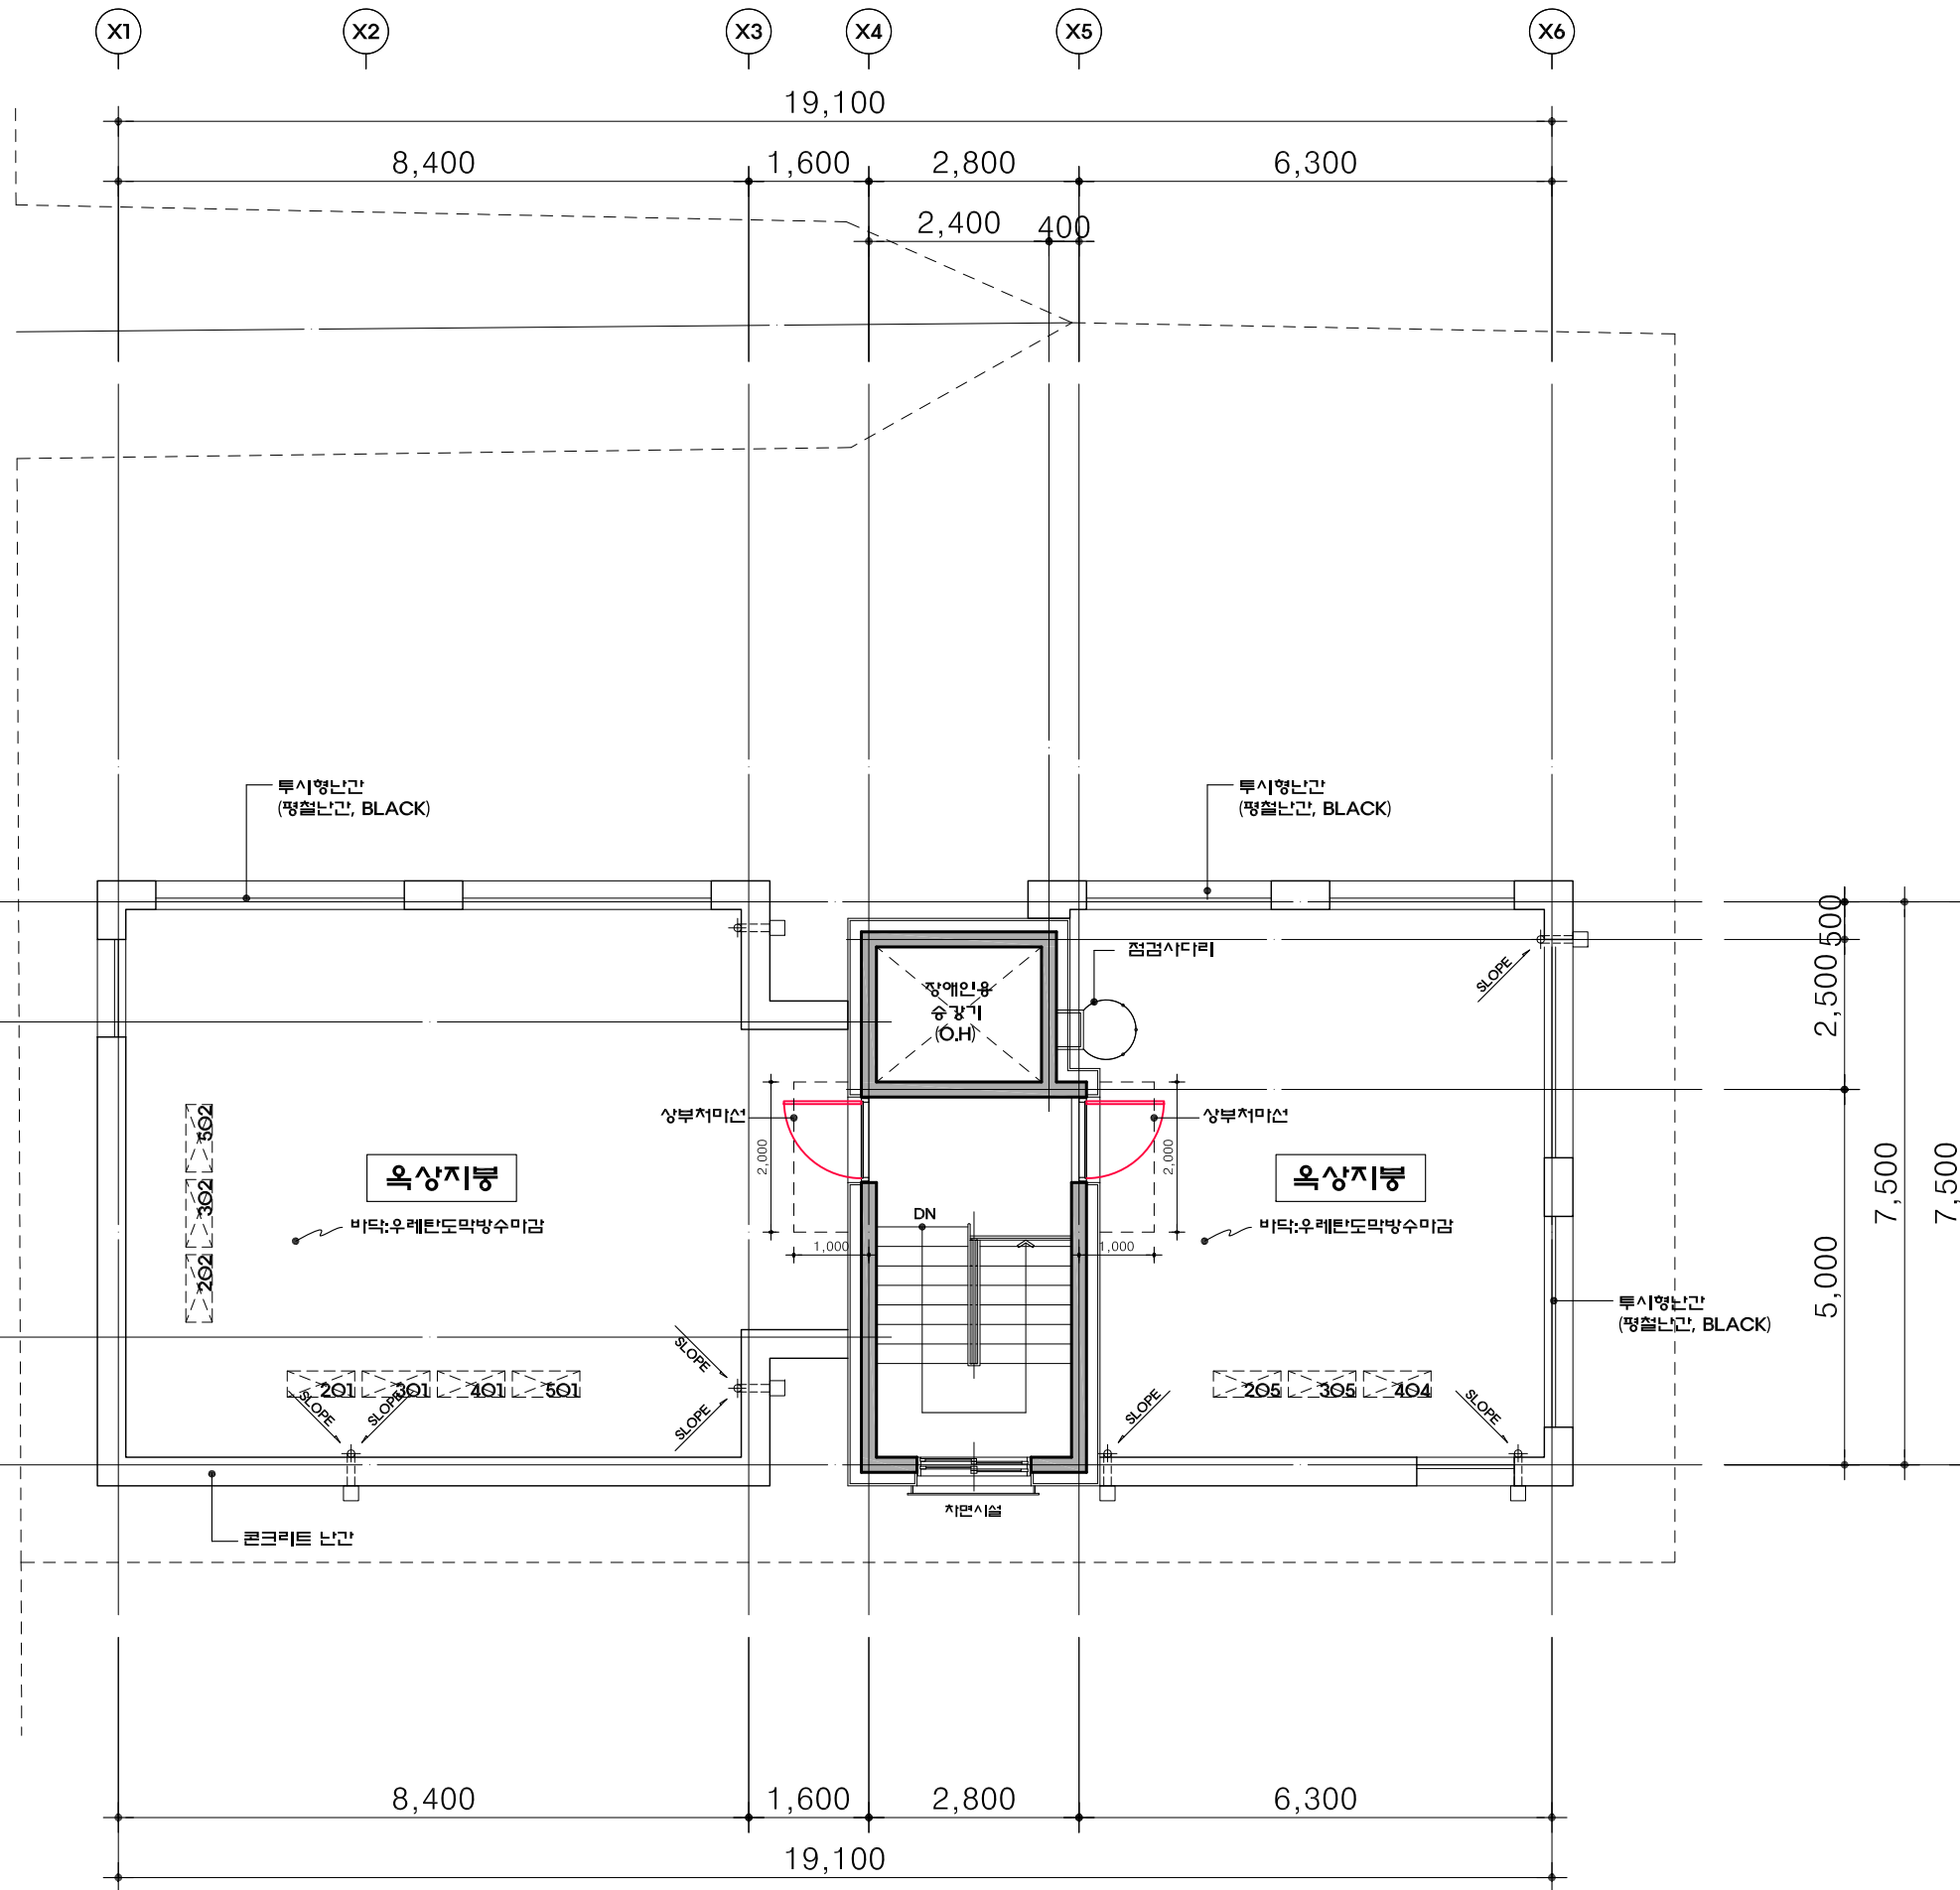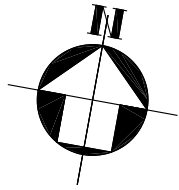

주 기	
1	콘크리트 : fck=27Mpa
	철근 : fy=400Mpa
구조	난간 벽두께 : 200mm(복배근)
	코아 벽두께 : 200mm(복배근)
	지붕 스키브 두께 : 180mm(복배근)

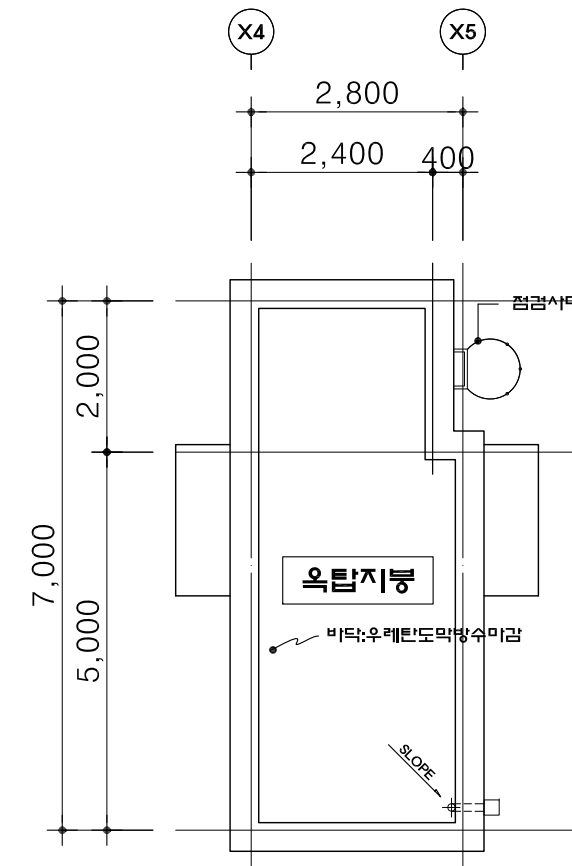

옥 탑 층 평면도

SCALE:1/100

옥탑 지붕층 평면도

SCALE:1/100

NOTE:

PROJECT 마포구 성산동 3-20번지 도시형 생활 주택
단지형 다세대주택 신축공사 (경년주택)

APPROVED BY 건축사

LINK (주)유엔케이 건축사무소
Planners, Architects, Engineers, Consultants
서울특별시 서초구 미림로6길 29, 영성빌딩 4층
TEL : 070-7774-3988, FAX : 070-7966-3903
010-4422-4121


TITLE 옥 탑 층 평 면 도
옥탑 지붕층 평면도

날짜 DATE: 2026. 03

SCALE 1 / 100 DWG NO. A - 032 REV.



정 면 도
SCALE:1/100

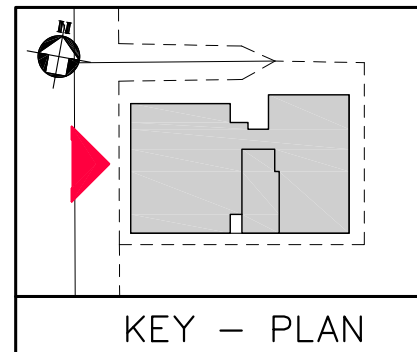

NOTE:

PROJECT 미포구 성산동 3-20번지 도시형 생활 주택
단지형 다세대주택 신축공사 (정년주택)


APPROVED BY 건축사

UNK (주)유엔케이 건축사무소
Planners, Architects, Engineers, Consultants
서울특별시 서초구 미포로6길 29, 영성빌딩 4층
TEL : 070-7774-3988, FAX : 070-7966-3903
010-4422-4121

TITLE 정 면 도

날짜 DATE: 2026. 03

SCALE 1 / 100 DWG NO. A - 043 REV.

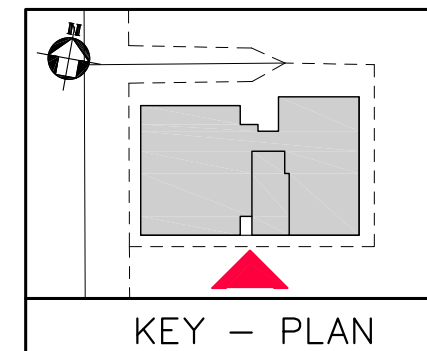

NOTE:

PROJECT 미포구 성산동 3-20번지 도시형 생활 주택
단지형 다세대주택 신축공사 (청년주택)


APPROVED BY 건축사

UNK (주)유엔케이 건축사무소
Planners, Architects, Engineers, Consultants
서울특별시 서초구 미포동6길 29, 영성빌딩 4층
TEL : 070-7774-3988, FAX : 070-7966-3903
010-4422-4121

TITLE 우 측 면 도

날짜 DATE: 2026. 03

SCALE 1 / 100 DWG NO. A -044 REV.

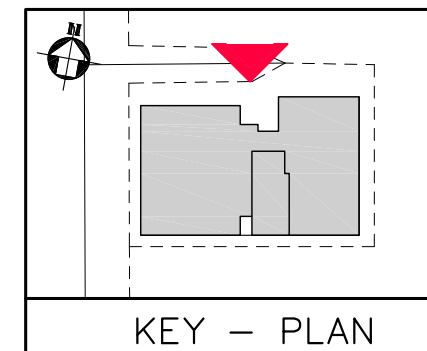

좌 측 면 도
SCALE:1/100

NOTE:

PROJECT 미포구 성산동 3-20번지 도시형 생활 주택
단지형 다세대주택 신축공사 (청년주택)


APPROVED BY 건축사

LINK (주)유엔케이 건축사무소
Planners, Architects, Engineers, Consultants
서울특별시 서초구 미포로6길 29, 영성빌딩 4층
TEL : 070-7774-3988, FAX : 070-7966-3903
010-4422-4121


TITLE 좌 측 면 도

날짜 DATE: 2026. 03

SCALE 1 / 100 DWG NO. A -045 REV.

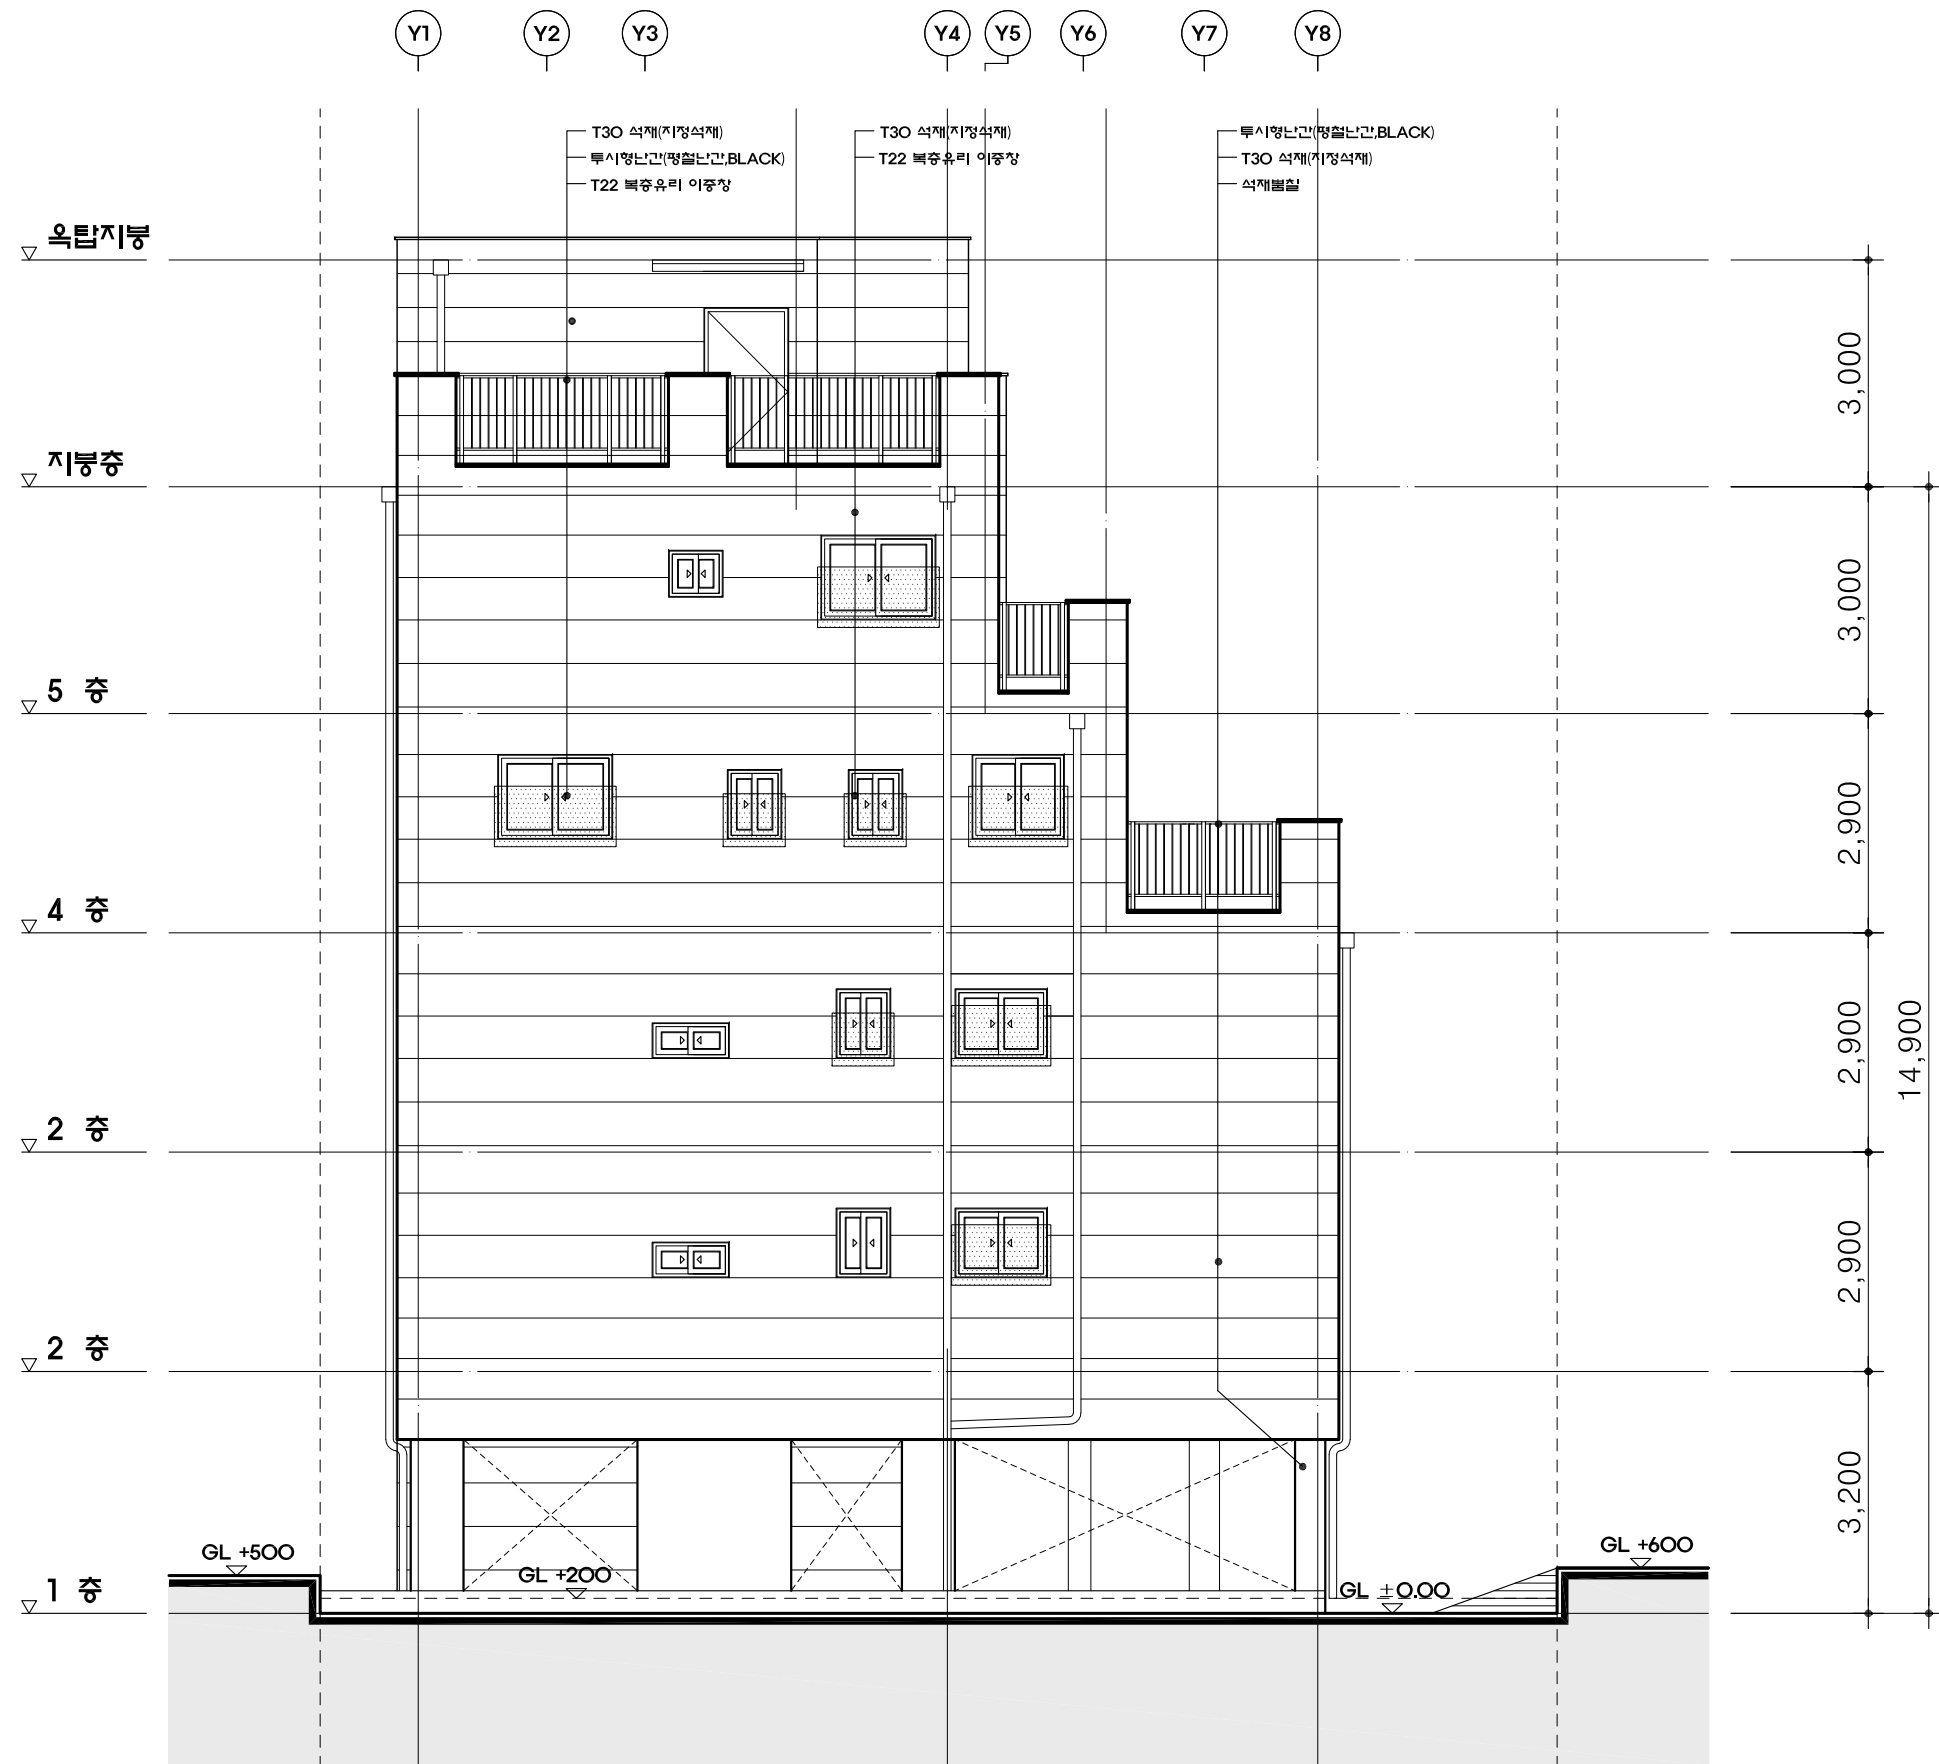

배 면 도
SCALE:1/100

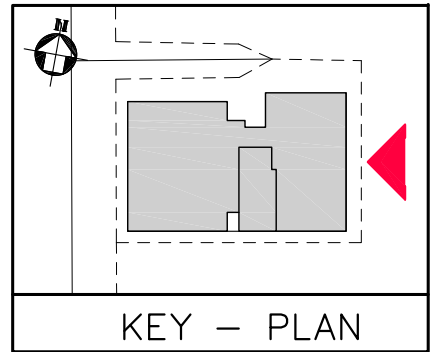

NOTE:

PROJECT 미포구 성산동 3-20번지 도시형 생활 주택
단지형 다세대주택 신축공사 (청년주택)



APPROVED BY 건축사

UNK (주)유엔케이 건축사무소
Planners, Architects, Engineers, Consultants
서울특별시 서초구 미포로6길 29, 영성빌딩 4층
TEL : 070-7774-3988, FAX : 070-7966-3903
010-4422-4121

TITLE 배 면 도

날짜 DATE: 2026. 03

SCALE	1 / 100	DWG NO.	A -046	REV.
-------	---------	---------	--------	------

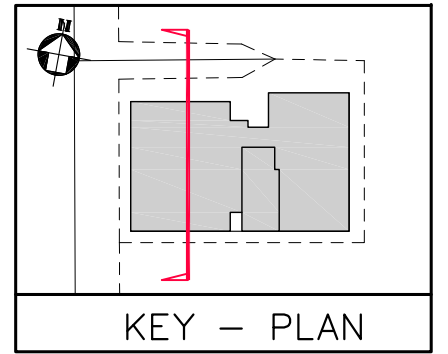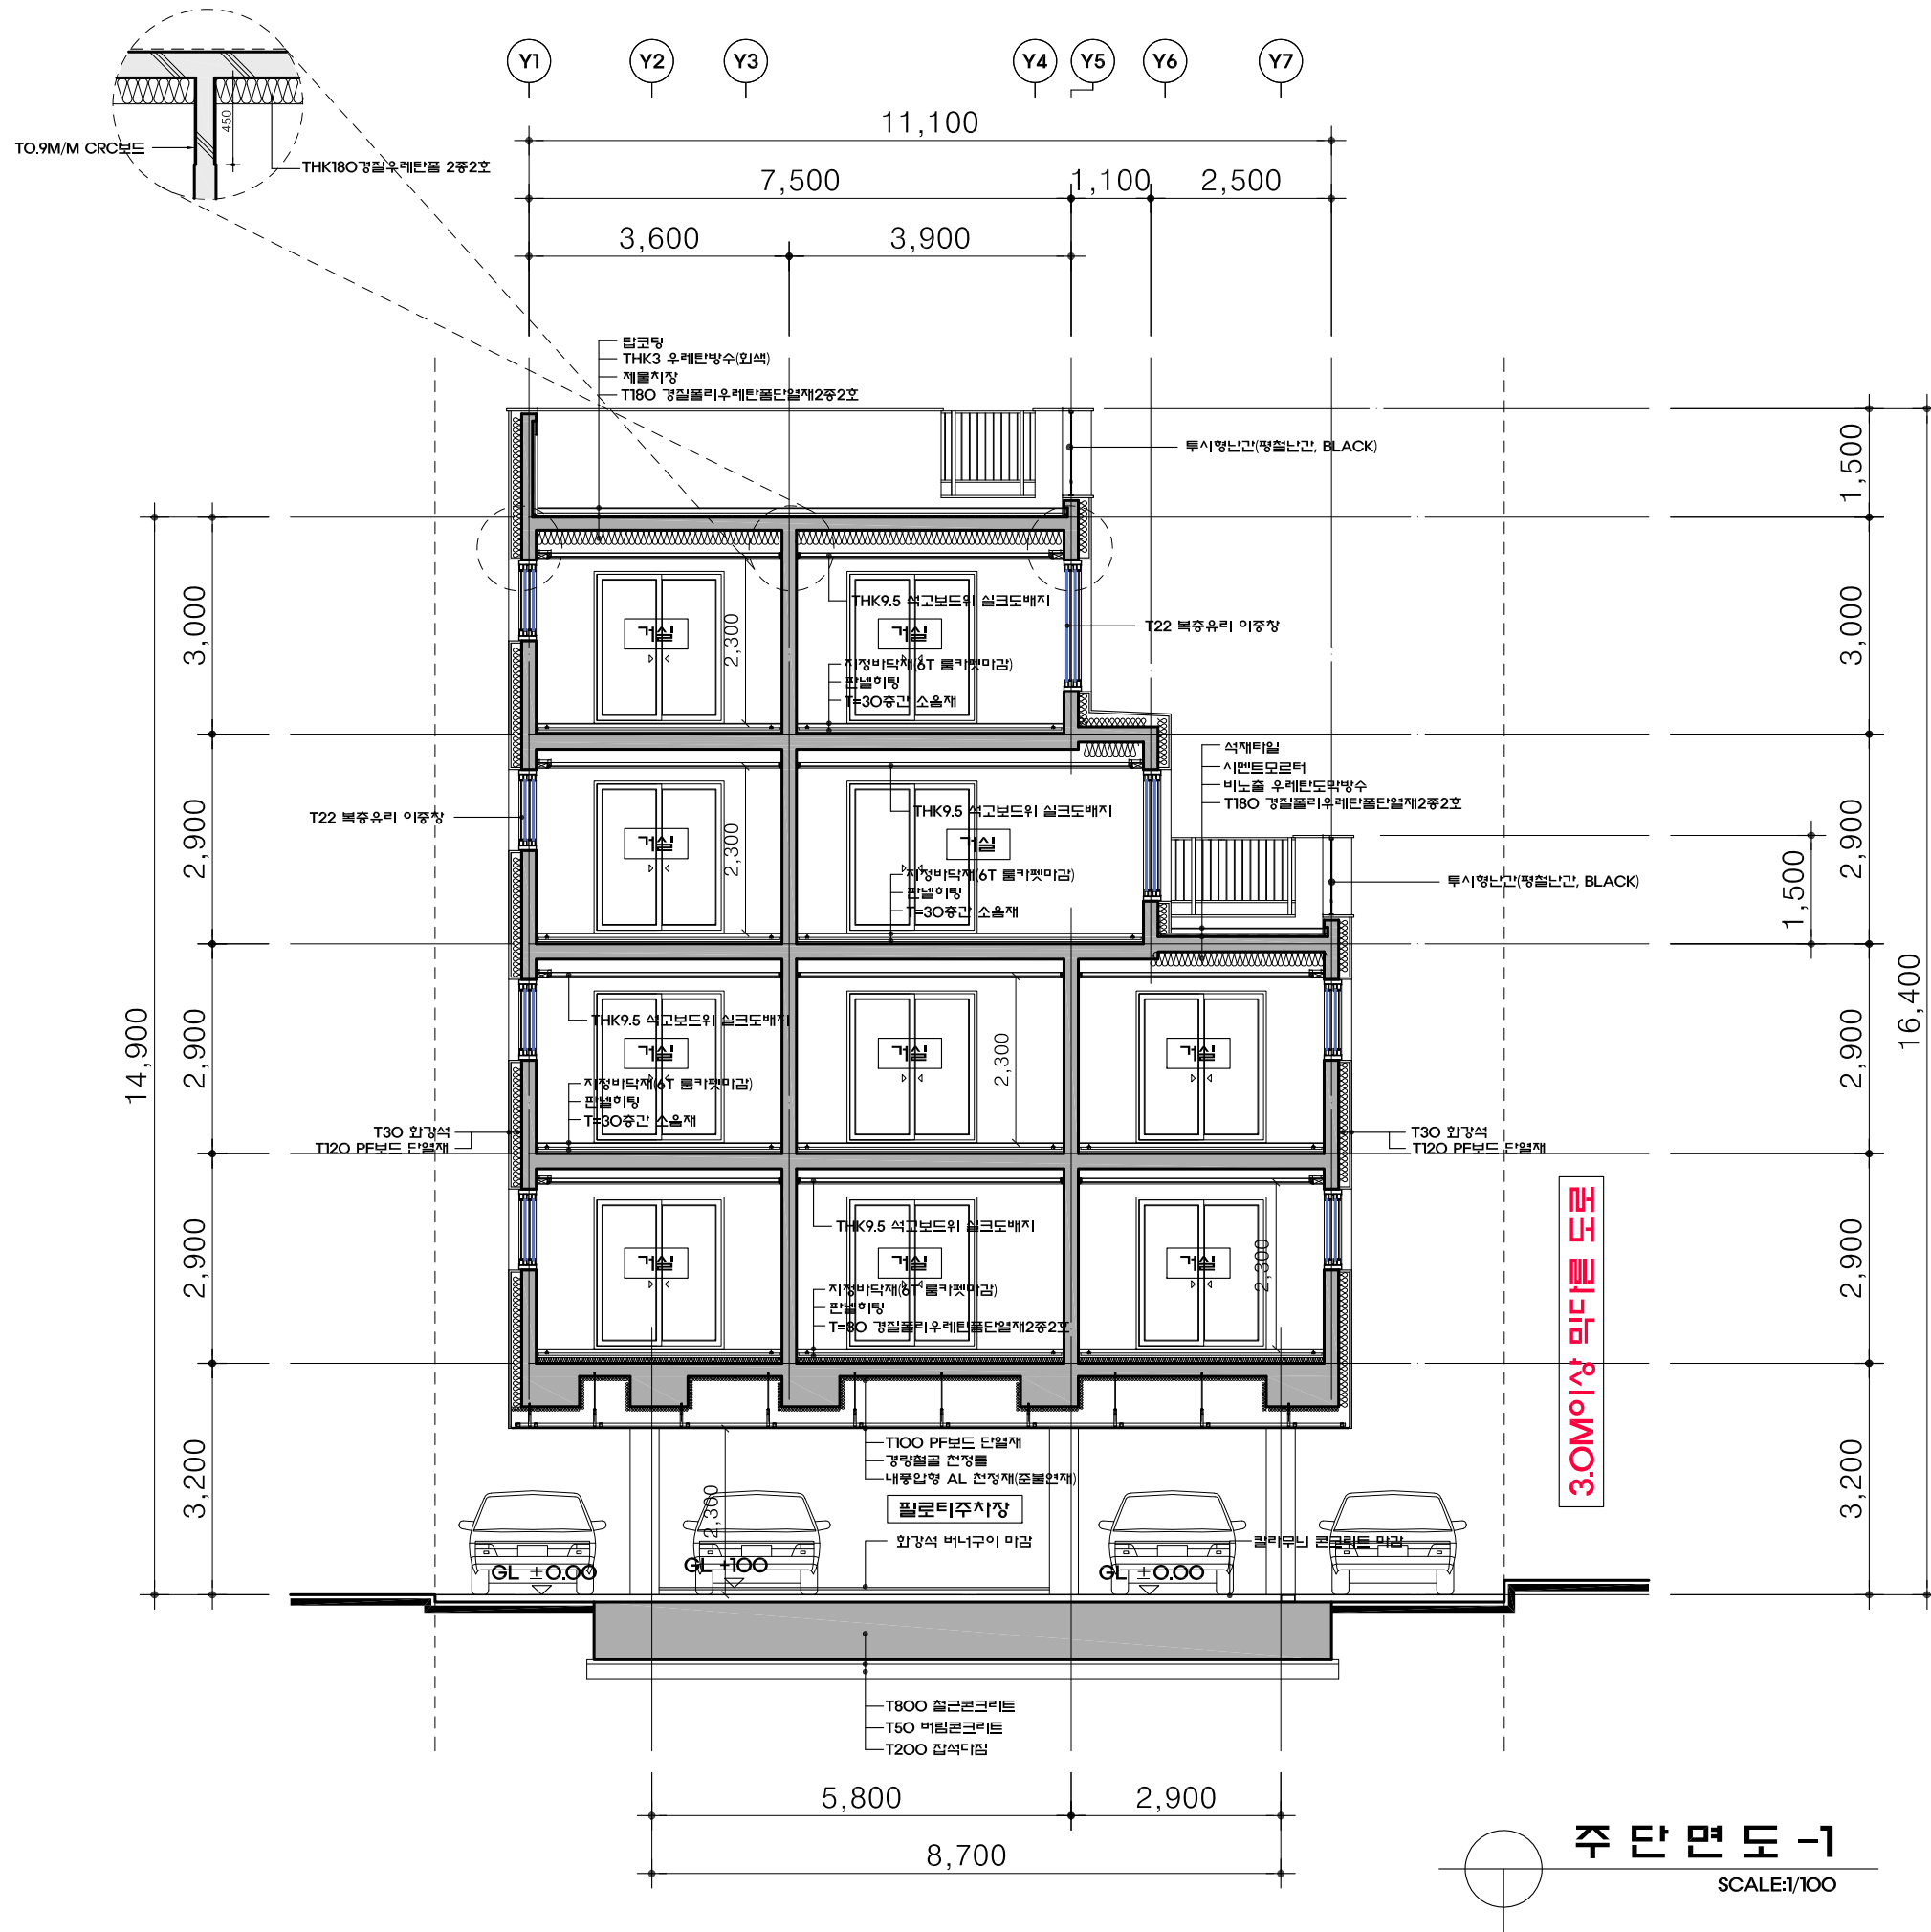

NOTE:

PROJECT 미포구 성산동 3-20번지 도시형 생활 주택
단지형 다세대주택 신축공사 (정년주택)



APPROVED BY 건축사

LINK (주)유엔케이 건축사사무소
Planners, Architects, Engineers, Consultants
서울특별시 서초구 미포로6길 29, 영성빌딩 4층
TEL : 070-7774-3988, FAX : 070-7966-3903
010-4422-4121

TITLE 주 단 면 도 -1

날짜 DATE: 2026. 03

SCALE 1 / 100 DWG NO. A -047 REV.

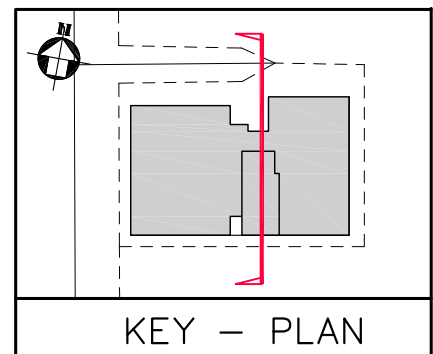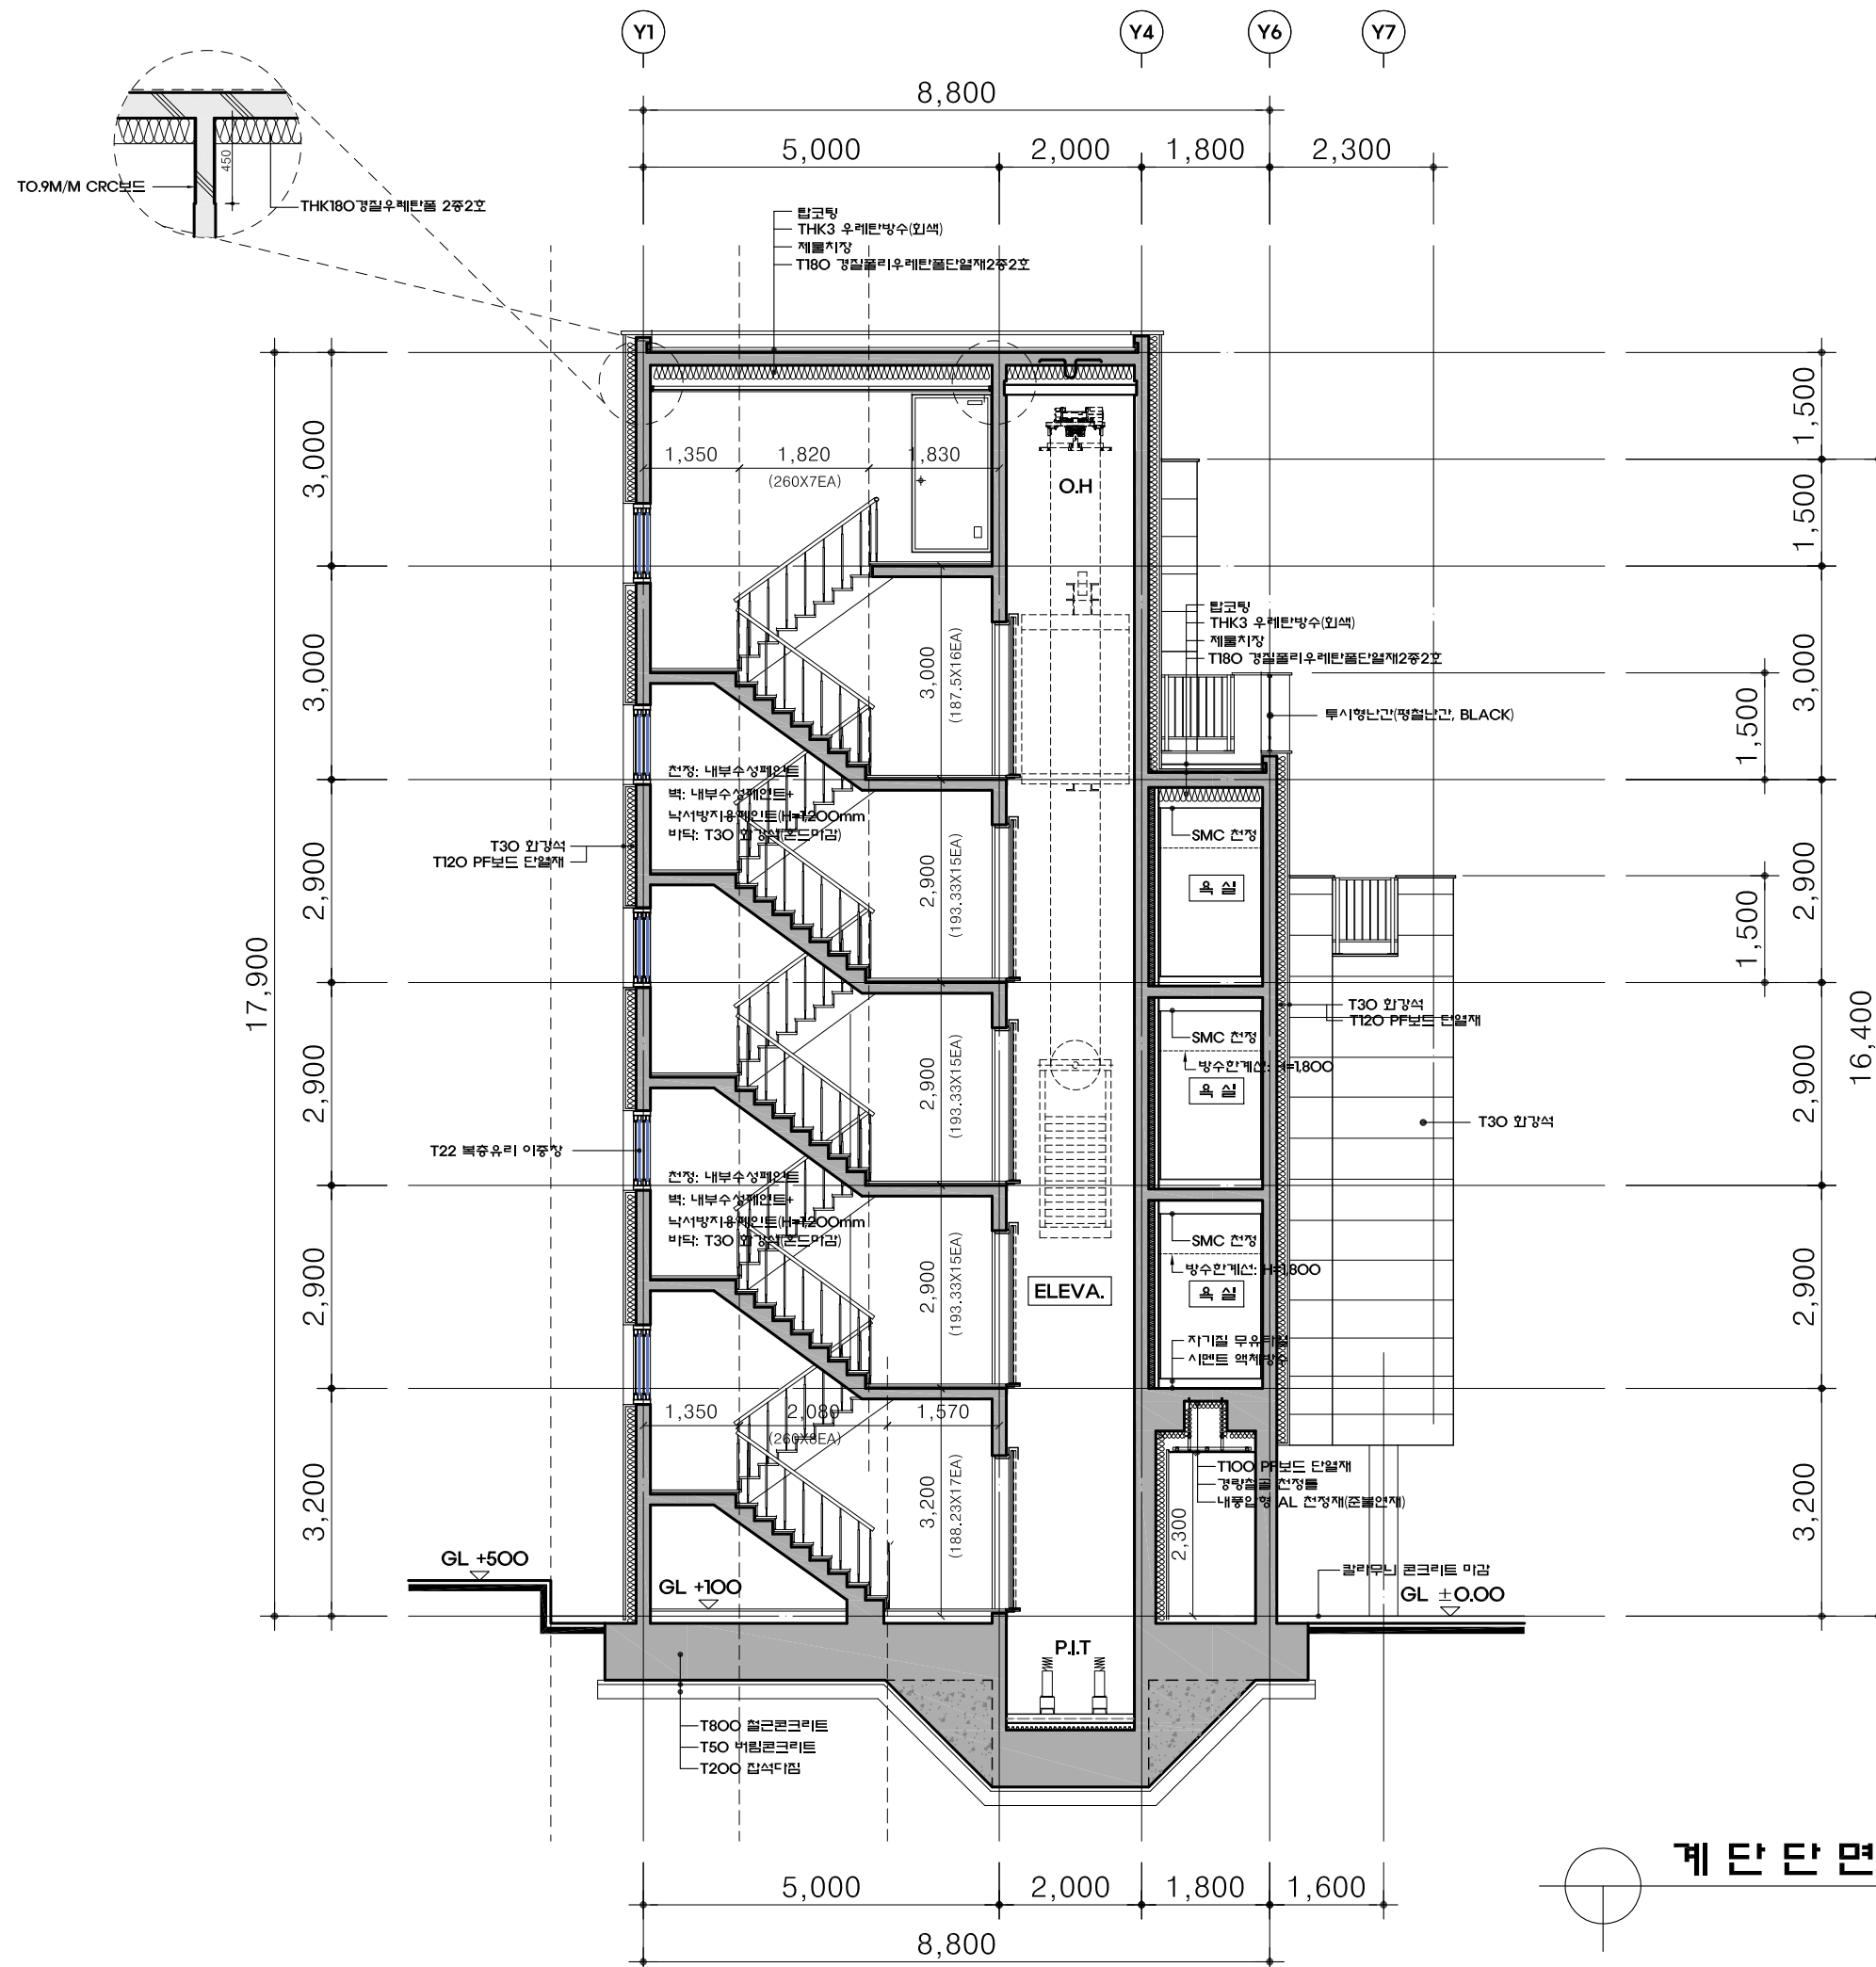

NOTE:

PROJECT 미포구 성산동 3-20번지 도시형 생활 주택
단지형 다세대주택 신축공사 (정년주택)

APPROVED BY 건축사

LINK (주)유엔케이 건축사무소
Planners, Architects, Engineers, Consultants
서울특별시 서초구 미포로6길 29, 영성빌딩 4층
TEL : 070-7774-3988, FAX : 070-7966-3903
010-4422-4121

TITLE 계 단 단 면 도 - 1

날짜 DATE: 2026. 03

SCALE 1 / 100 DWG NO. A - 048 REV.