



1. 접근로의 유효폭 1.2미터 이상 확보
2. 접근로의 기울기는 1/18 이하로 설치
3. 대지 내를 연결하는 주접근로에 단차가 있을 경우
그 높이차는 2cm 이하가 되도록 설치
4. 접근로는 차도와 색상과 재질을 달리하여 반드시
보차분리를 명확히 해주어야 함
5. 접근로의 바닥표면은 잘미끄러지지 않는 재질로 평탄하게 마감하여야 함
6. 블록 등으로 접근로를 포장하는 경우에는 이음새의 틈이
벌어지지 아니하도록 하여 면이 평탄하게 시공하여야 함
7. 뒀개를 설치할 경우 뒀개에 격자구멍 또는 틈새의 양방향 간격이
2cm 이하가 되도록 설치
8. 점형블록은 매립형으로 설치함(황색K.S제품)

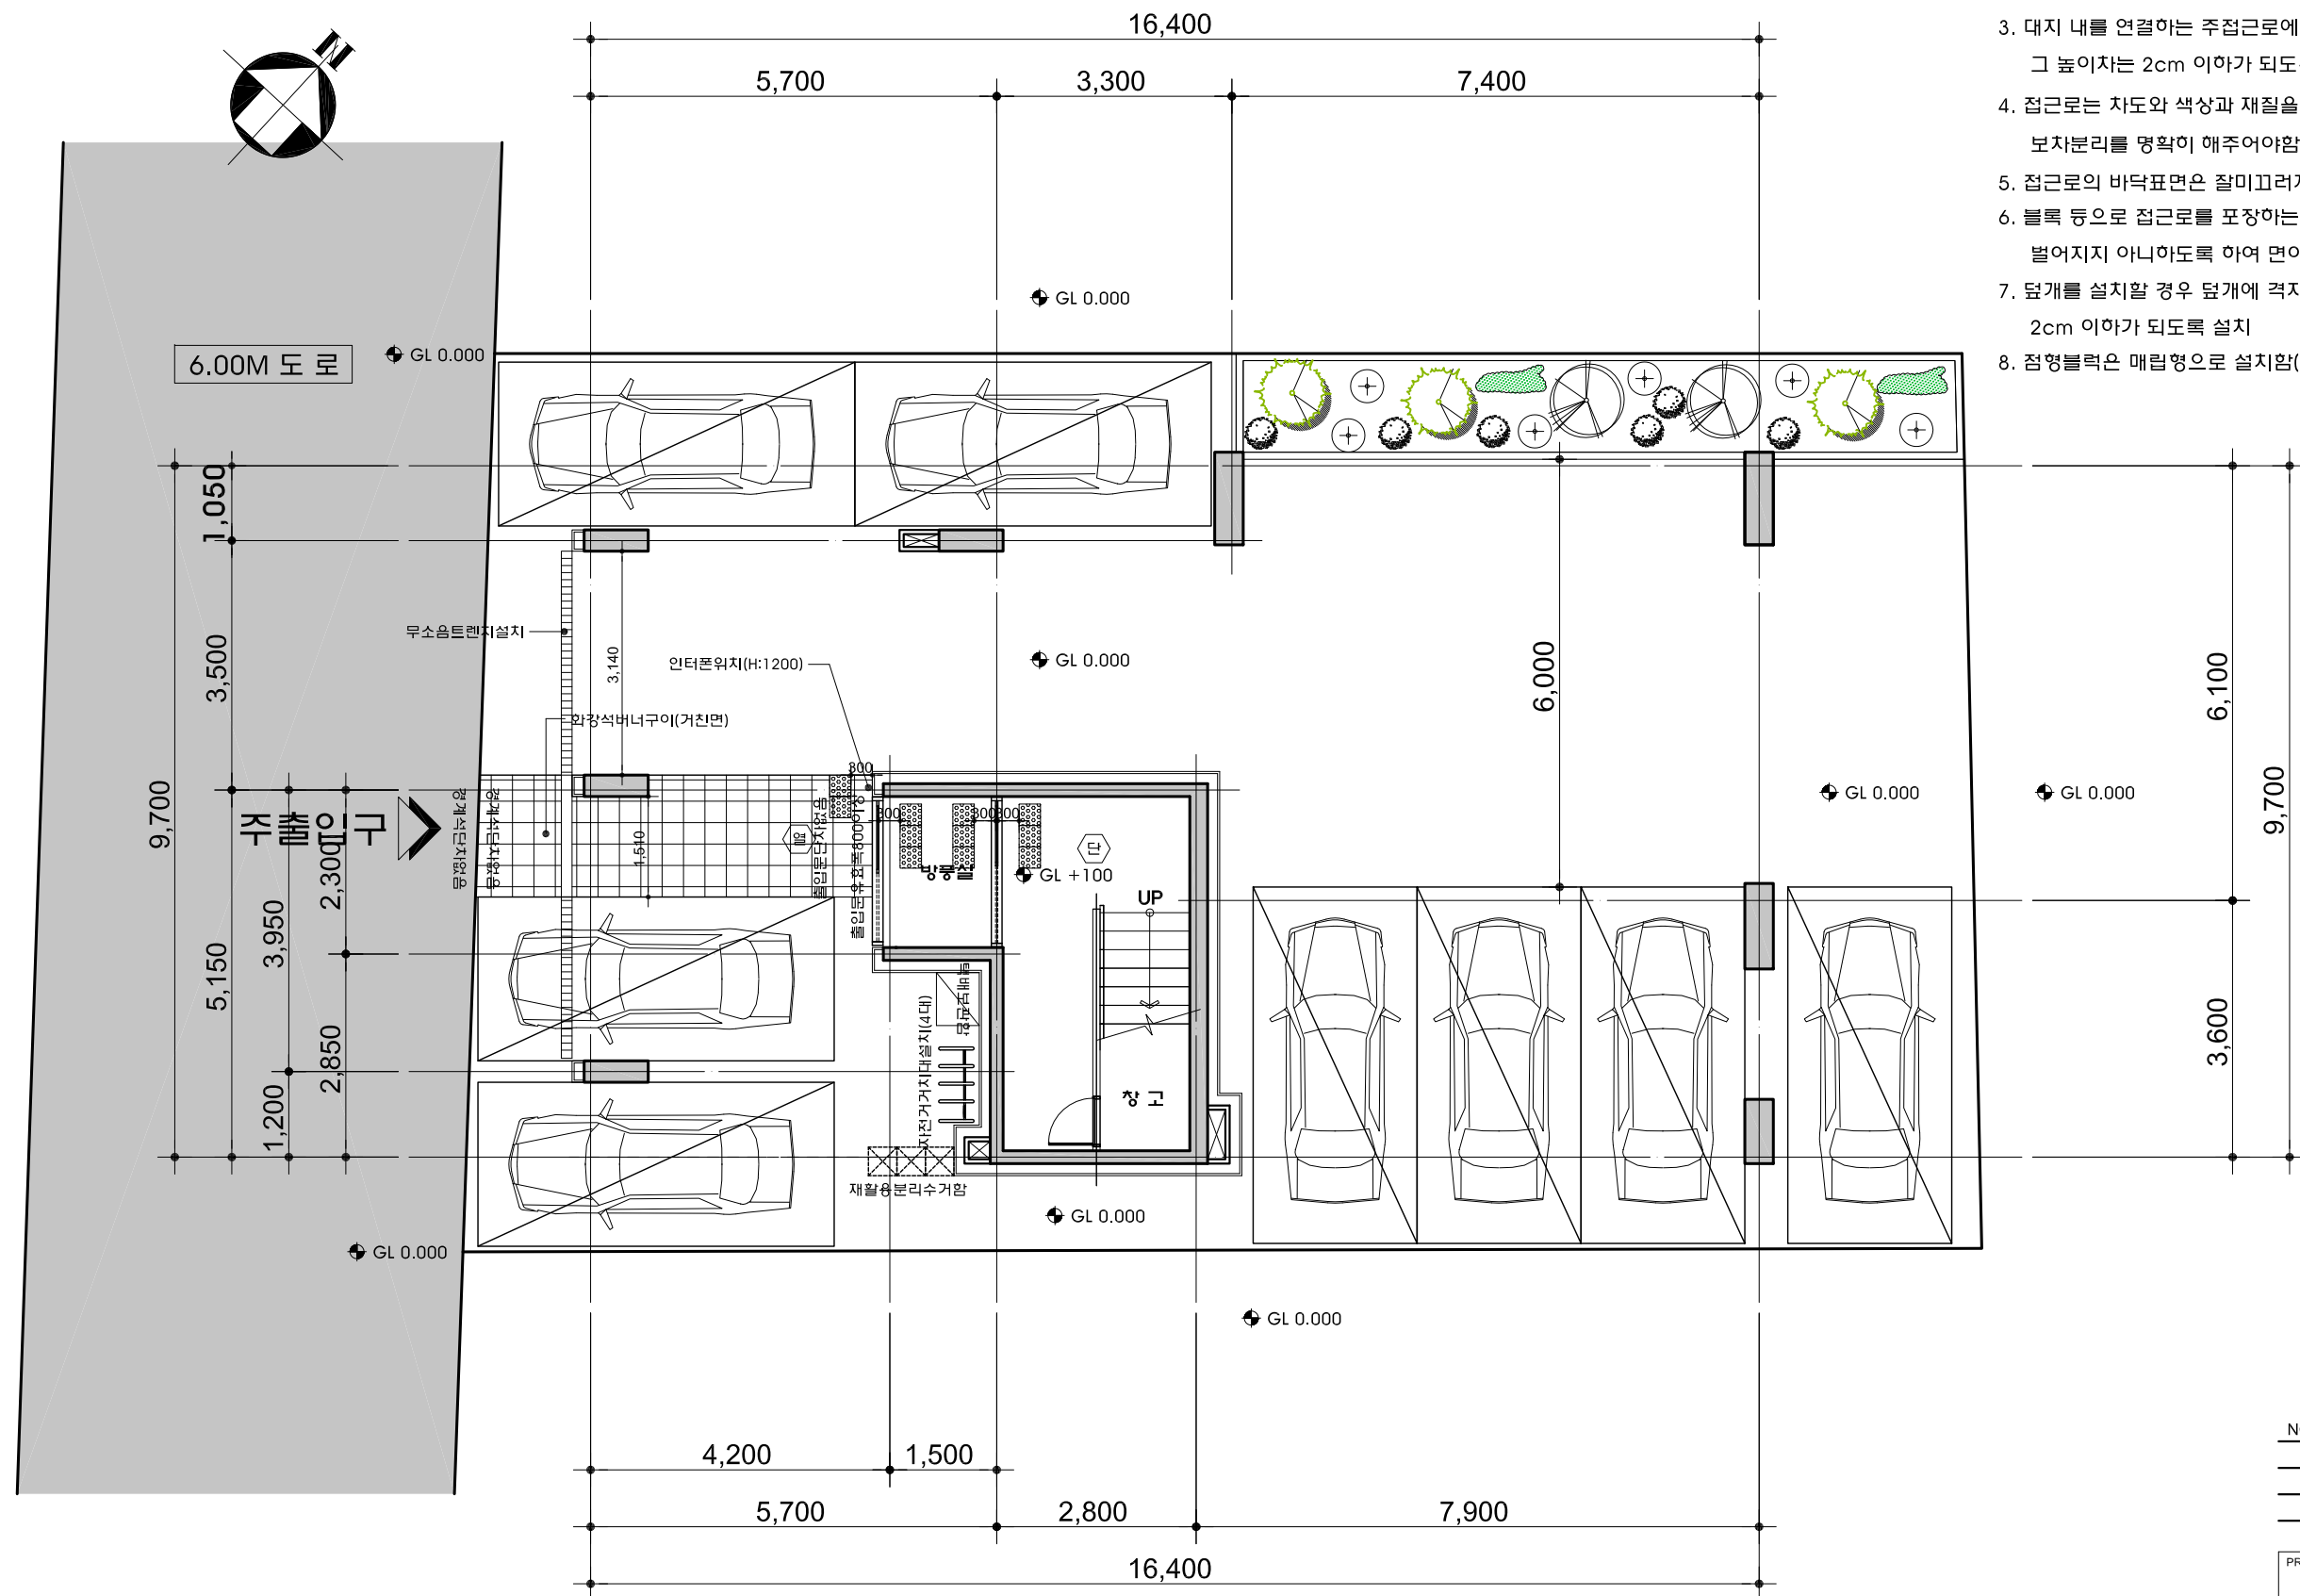

NOTE:

PROJECT		서대문구 홍제동 360-40,41번지 다세대주택 건축공사	
APPROVED BY			
		건축사사무소 유원엔지니어링 SEOUL, KOREA TEL:540-1546, FAX:540-1576	
TITLE			
1 층 평 면 도			
개량 DATE:		2017. 07	
SCALE	1/100	DWG NO.	REV.

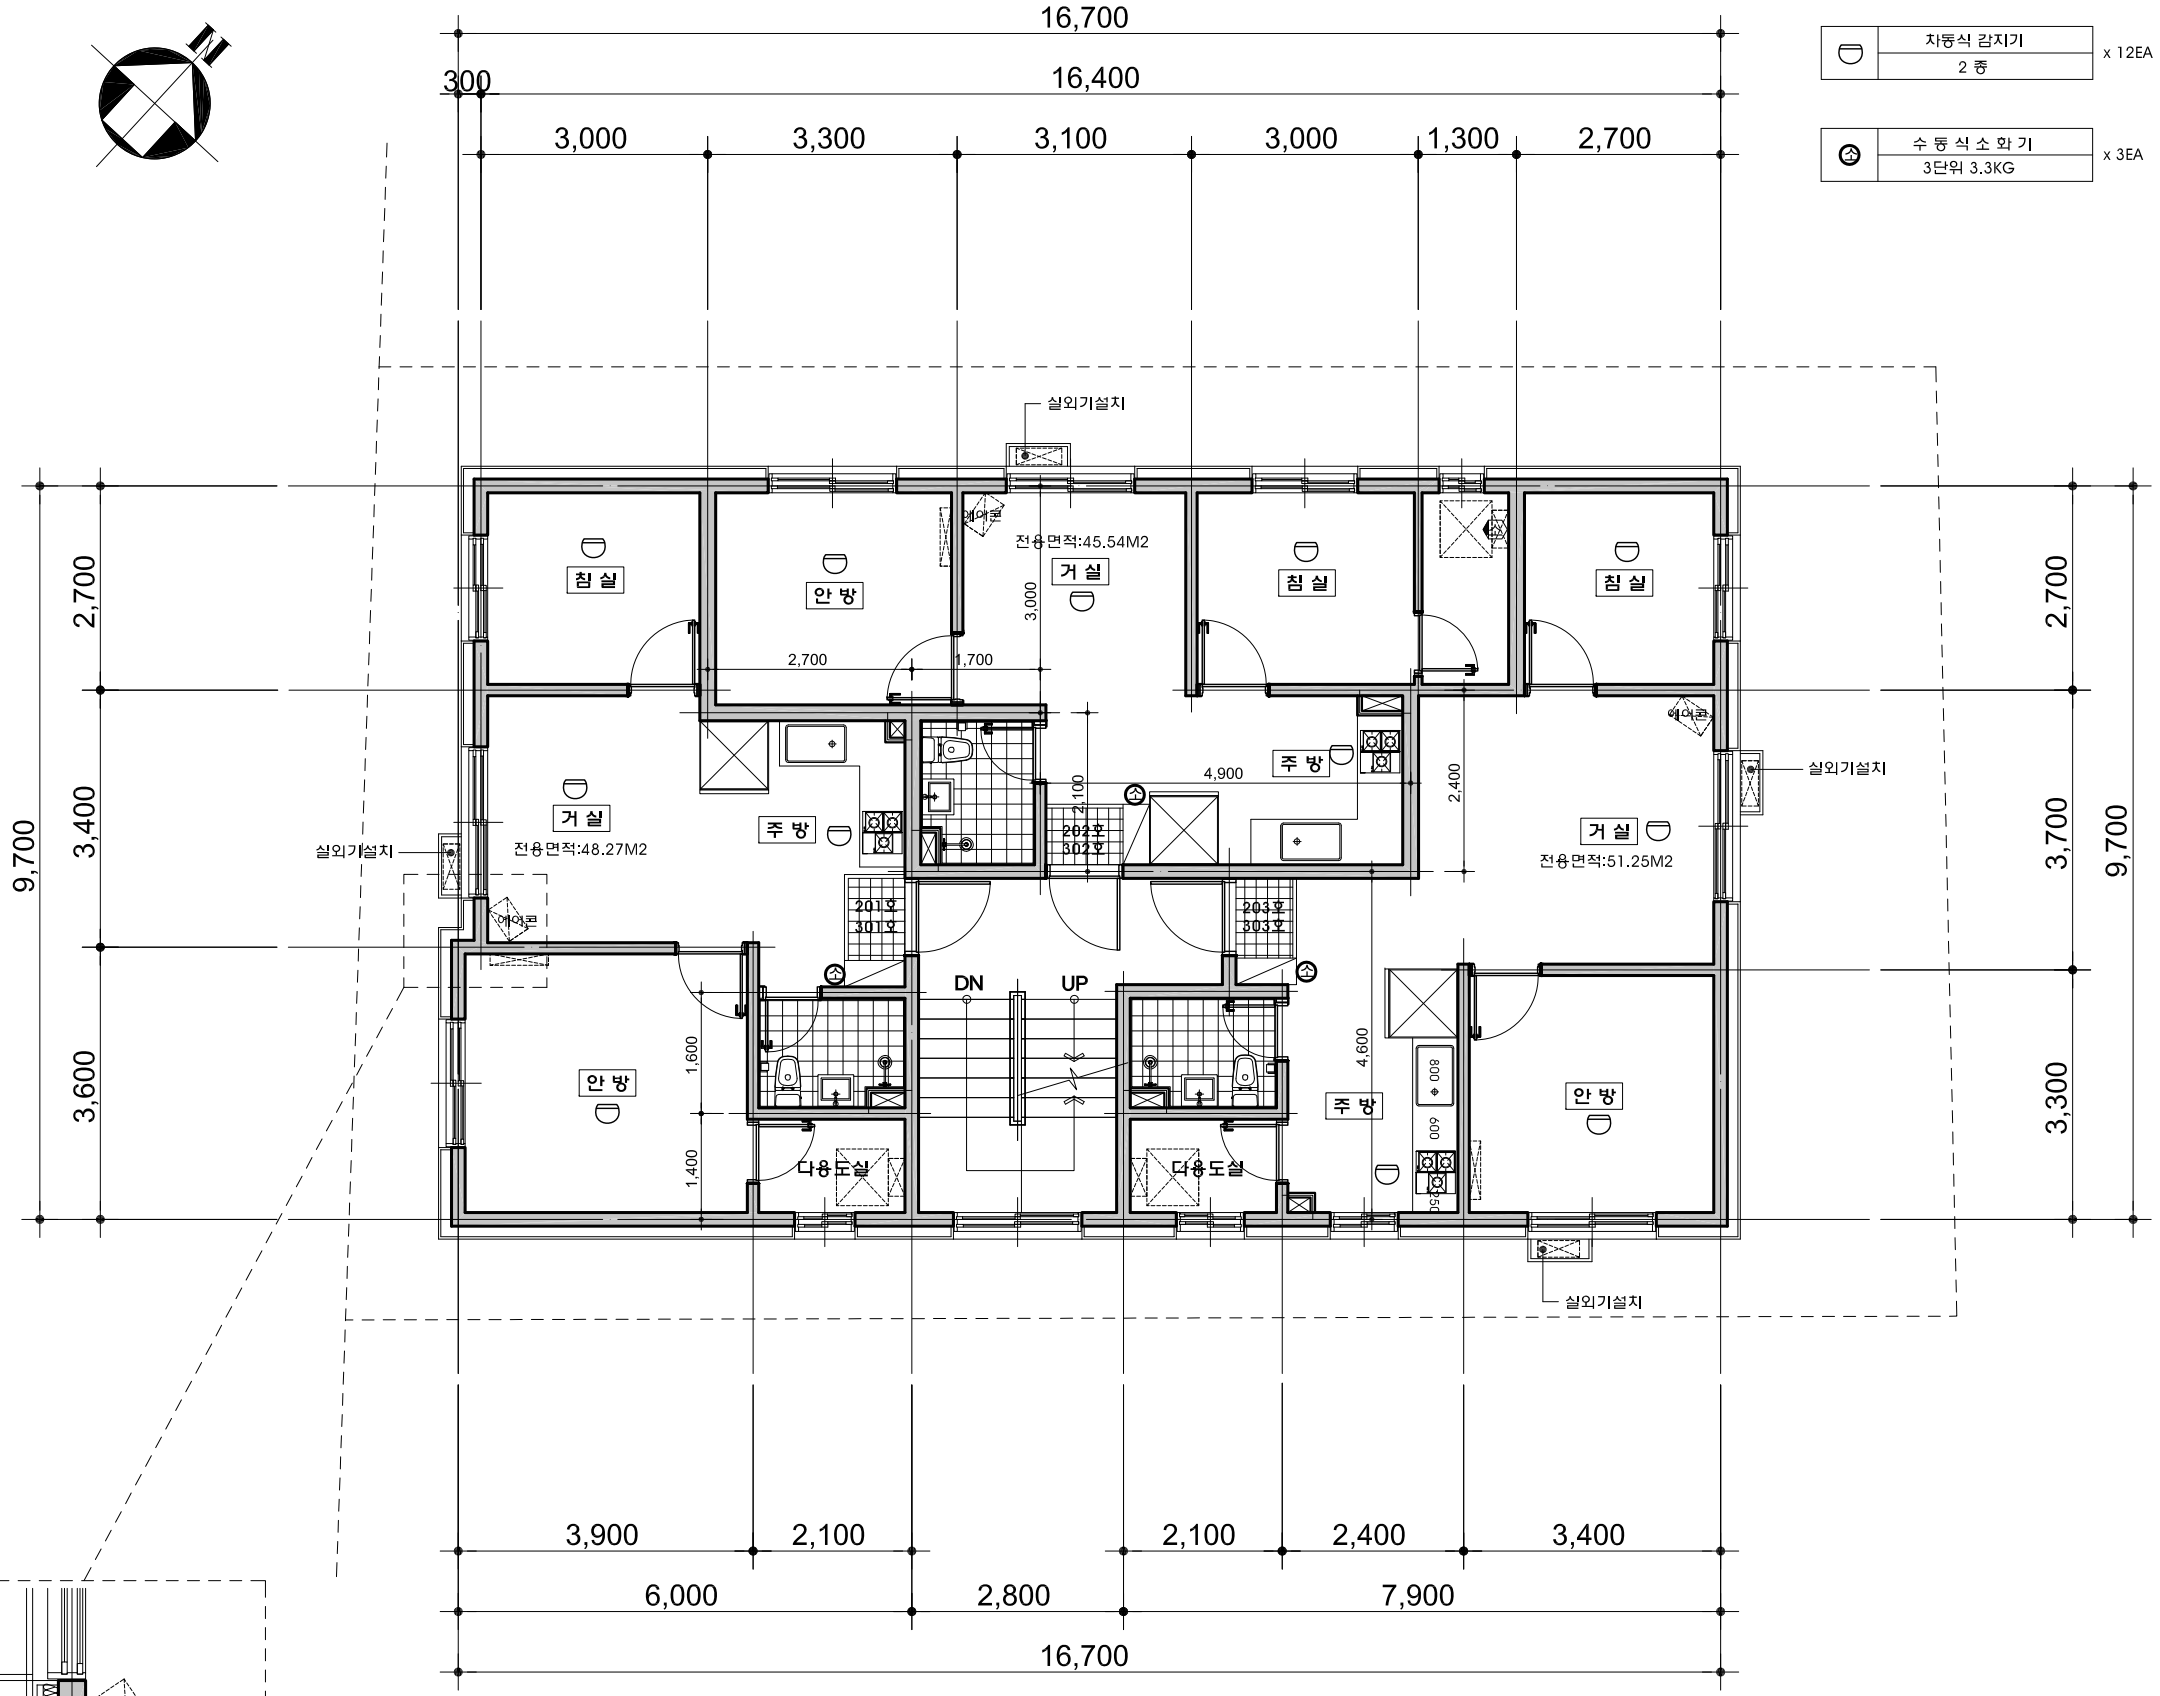


- | | | |
|--|----------------------|--------|
| | 차동식 감지기
2종 | x 12EA |
| | 수동식 소화기
3단위 3.3KG | x 3EA |

2~3 층 평 면 도
SCALE:1/100

주 기		
1	세대 현관문 도어체크 및 스토퍼 계획	
2	세대 발코니 설치시 세대간 분리벽 계획	
3	세대 발코니 설치시 세대간 분리벽 계획	
4	세대내 비디오폰 설치	
5	주차장내 CCTV 설치	
6	외벽	직접 외기에 면한 실내벽면은 단열재 (아이소핑크10mm+석고보드 마감도면 표기)
	계단실 /복도	간접 외기에 면한 실내벽면은 단열재 (아이소핑크20mm+석고보드 마감도면 표기)
7	에어콘 설치위치 및 에어콘 콘센트 및 냉매 및 배수관 위치 도면표기(배수관 수직으로 매립) - (에어콘 콘센트 표기)	
8	불박이 가구 내부 다용도 수납가능도록 수평이동 칸막이 설치	
9	콘크리트 폴타이 제거후 마감공사 시공(방수 및 단열재 시공등)	
10	콘크리트 : fck=24Mpa 철근 : fy=400Mpa 구조 세대 벽두께 : 150mm(복배근) 외벽 벽두께 : 180mm(복배근) 교아 벽두께 : 180mm(복배근) 스라브 두께 : 210mm(복배근)	
11	기타 실내 벽면은 시멘트 미장마감	
12	욕실 & 다용도실 스위치 : 문열리는 방향으로 시공	
13	공동주택 바닥충격음 차단구조기준 플레트받이(MDF) 장판지마감(2.2T이상) T=40 시멘트블록(1:3) T=40 경량기포콘크리트 T=0.06 PE필름1겹 T=30 압중재(EVA계열) T=210 콘크리트슬래브	

NOTE:			
PROJECT			
서대문구 홍제동 360-40,41번지 다세대주택 신축공사			
APPROVED BY			
PROJECT			
건축사사무소 유일엔지니어링 SEOUL, KOREA TEL:540-1546, FAX:540-1576			
TITLE			
2~3 층 평 면 도			
DATE			
2017. 07			
SCALE	1/100	DWG NO.	REV.

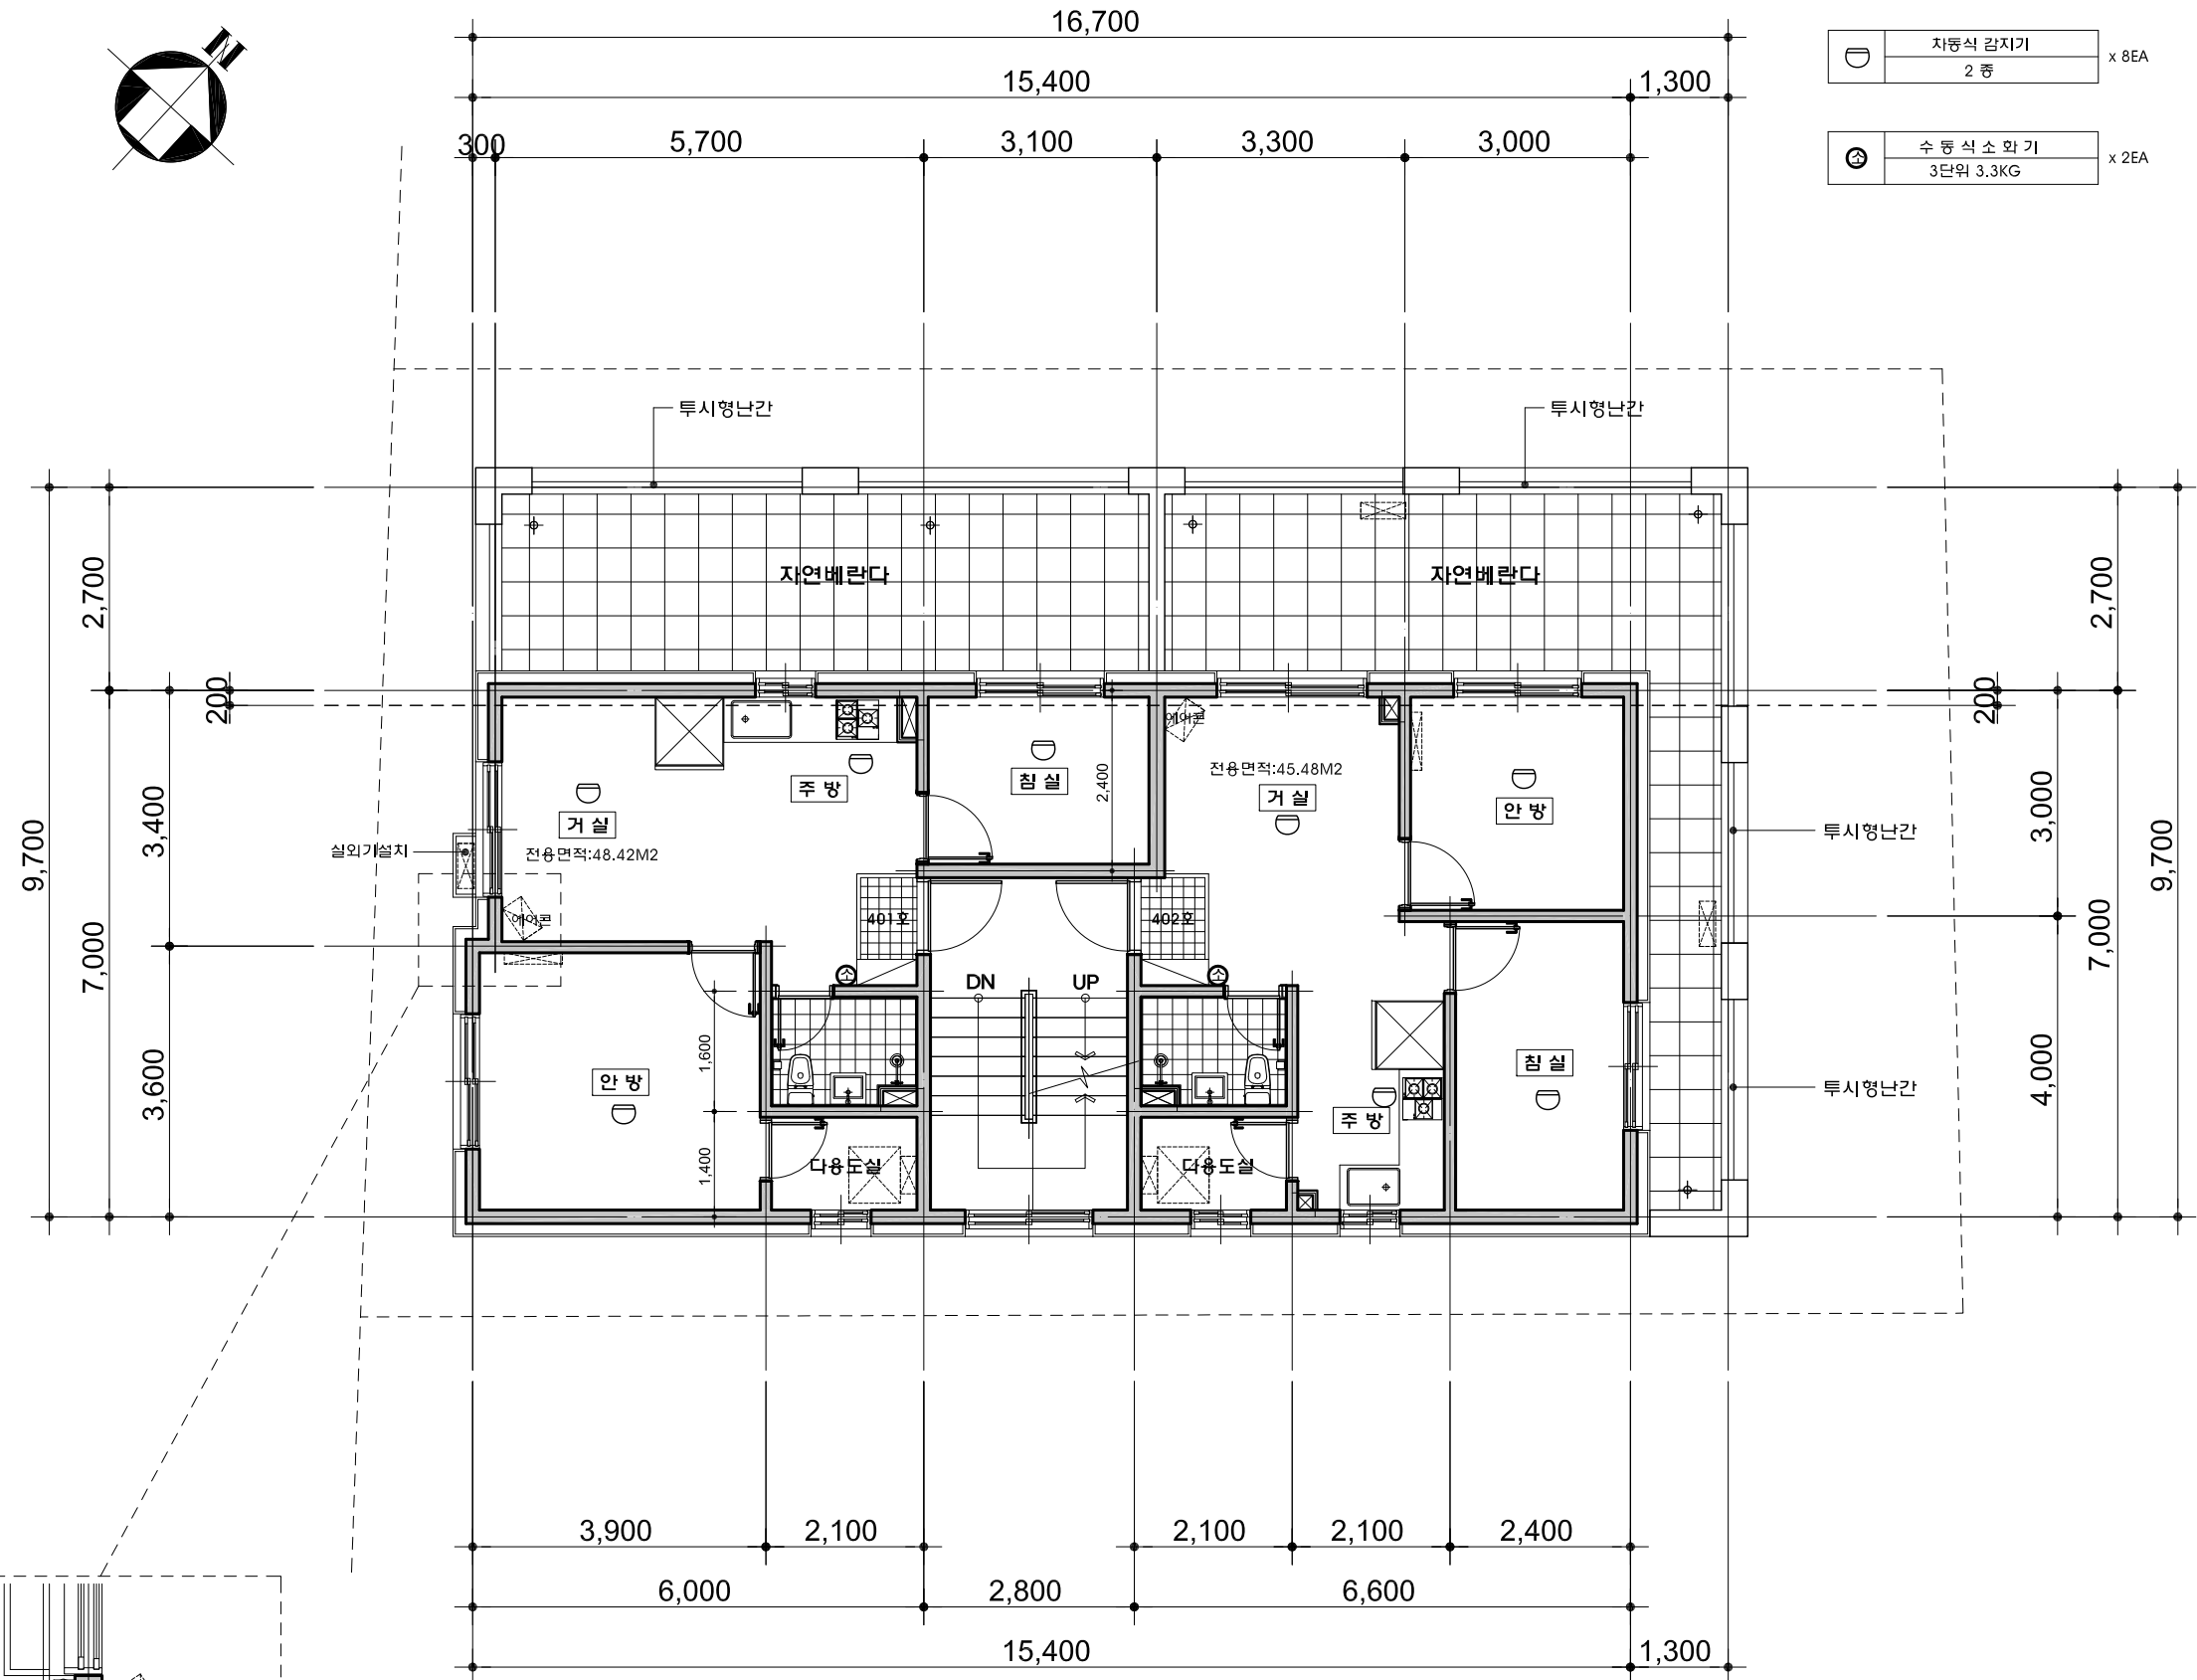

4 층 평 면 도
SCALE:1/100


차동식 감지기 2 종	x 8EA
수 동 식 소 화 기 3단위 3.3KG	x 2EA

주 기		
1	세대 현관문 도어체크 및 스토퍼 계획	
2	세대 발코니 설치시 세대간 분리벽 계획	
3	세대 발코니 설치시 세대간 분리벽 계획	
4	세대내 비디오폰 설치	
5	주차장내 CCTV 설치	
6	벽체	직접 외기에 면한 실내벽면은 단열재 (아이소핑크10mm+ 석고보드 마감도면 표기) 계단실 간접 외기에 면한 실내벽면은 단열재 (아이소핑크20mm+ 석고보드 마감도면 표기)
7	에어콘 실외기 설치위치 및 에어컨 콘센트 및 냉매 및 배수관 위치 도면표기(배수관 수직으로 매립)	● - (에어콘 콘센트 표기)
8	불박이 가구 내부 다용도 수납가능도록 수평이동 칸막이 설치	
9	콘크리트 폴타이 제거후 마감공사 시공(방수 및 단열재 시공등)	
10	구조	콘크리트 : fck=24Mpa 철근 : fy=400Mpa 세대 벽두께 : 150mm(복배근) 외벽 벽두께 : 180mm(복배근) 교야 벽두께 : 180mm(복배근) 스라브 두께 : 210mm(복배근)
11	기타 실내 벽면은 시멘트 미장마감	
12	욕실 & 다용도실 스위치 : 문열리는 방향으로 시공	
13	공동주택 바닥충격음 차단구조기준	플레임이(MDF) 장판지마감(2.2T이상) T=40 시멘트블록(1:3) T=40 경량기모콘크리트 T=0.06 PE필름1겹 T=30 완충재(EVA계열) T=210 콘크리트슬래브

NOTE:			
PROJECT			
서대문구 홍제동 360-40,41번지 다세대주택 신축공사			
APPROVED BY			
건축사사무소 유일엔지니어링 SEOUL, KOREA TEL:540-1546, FAX:540-1576			
TITLE			
4 층 평 면 도			
DATE			
2017. 07			
SCALE	1/100	DWG NO.	REV.



	차동식 감지기 2 종	x 6EA
	수 동 식 소 화 기 3단위 3.3KG	x 2EA

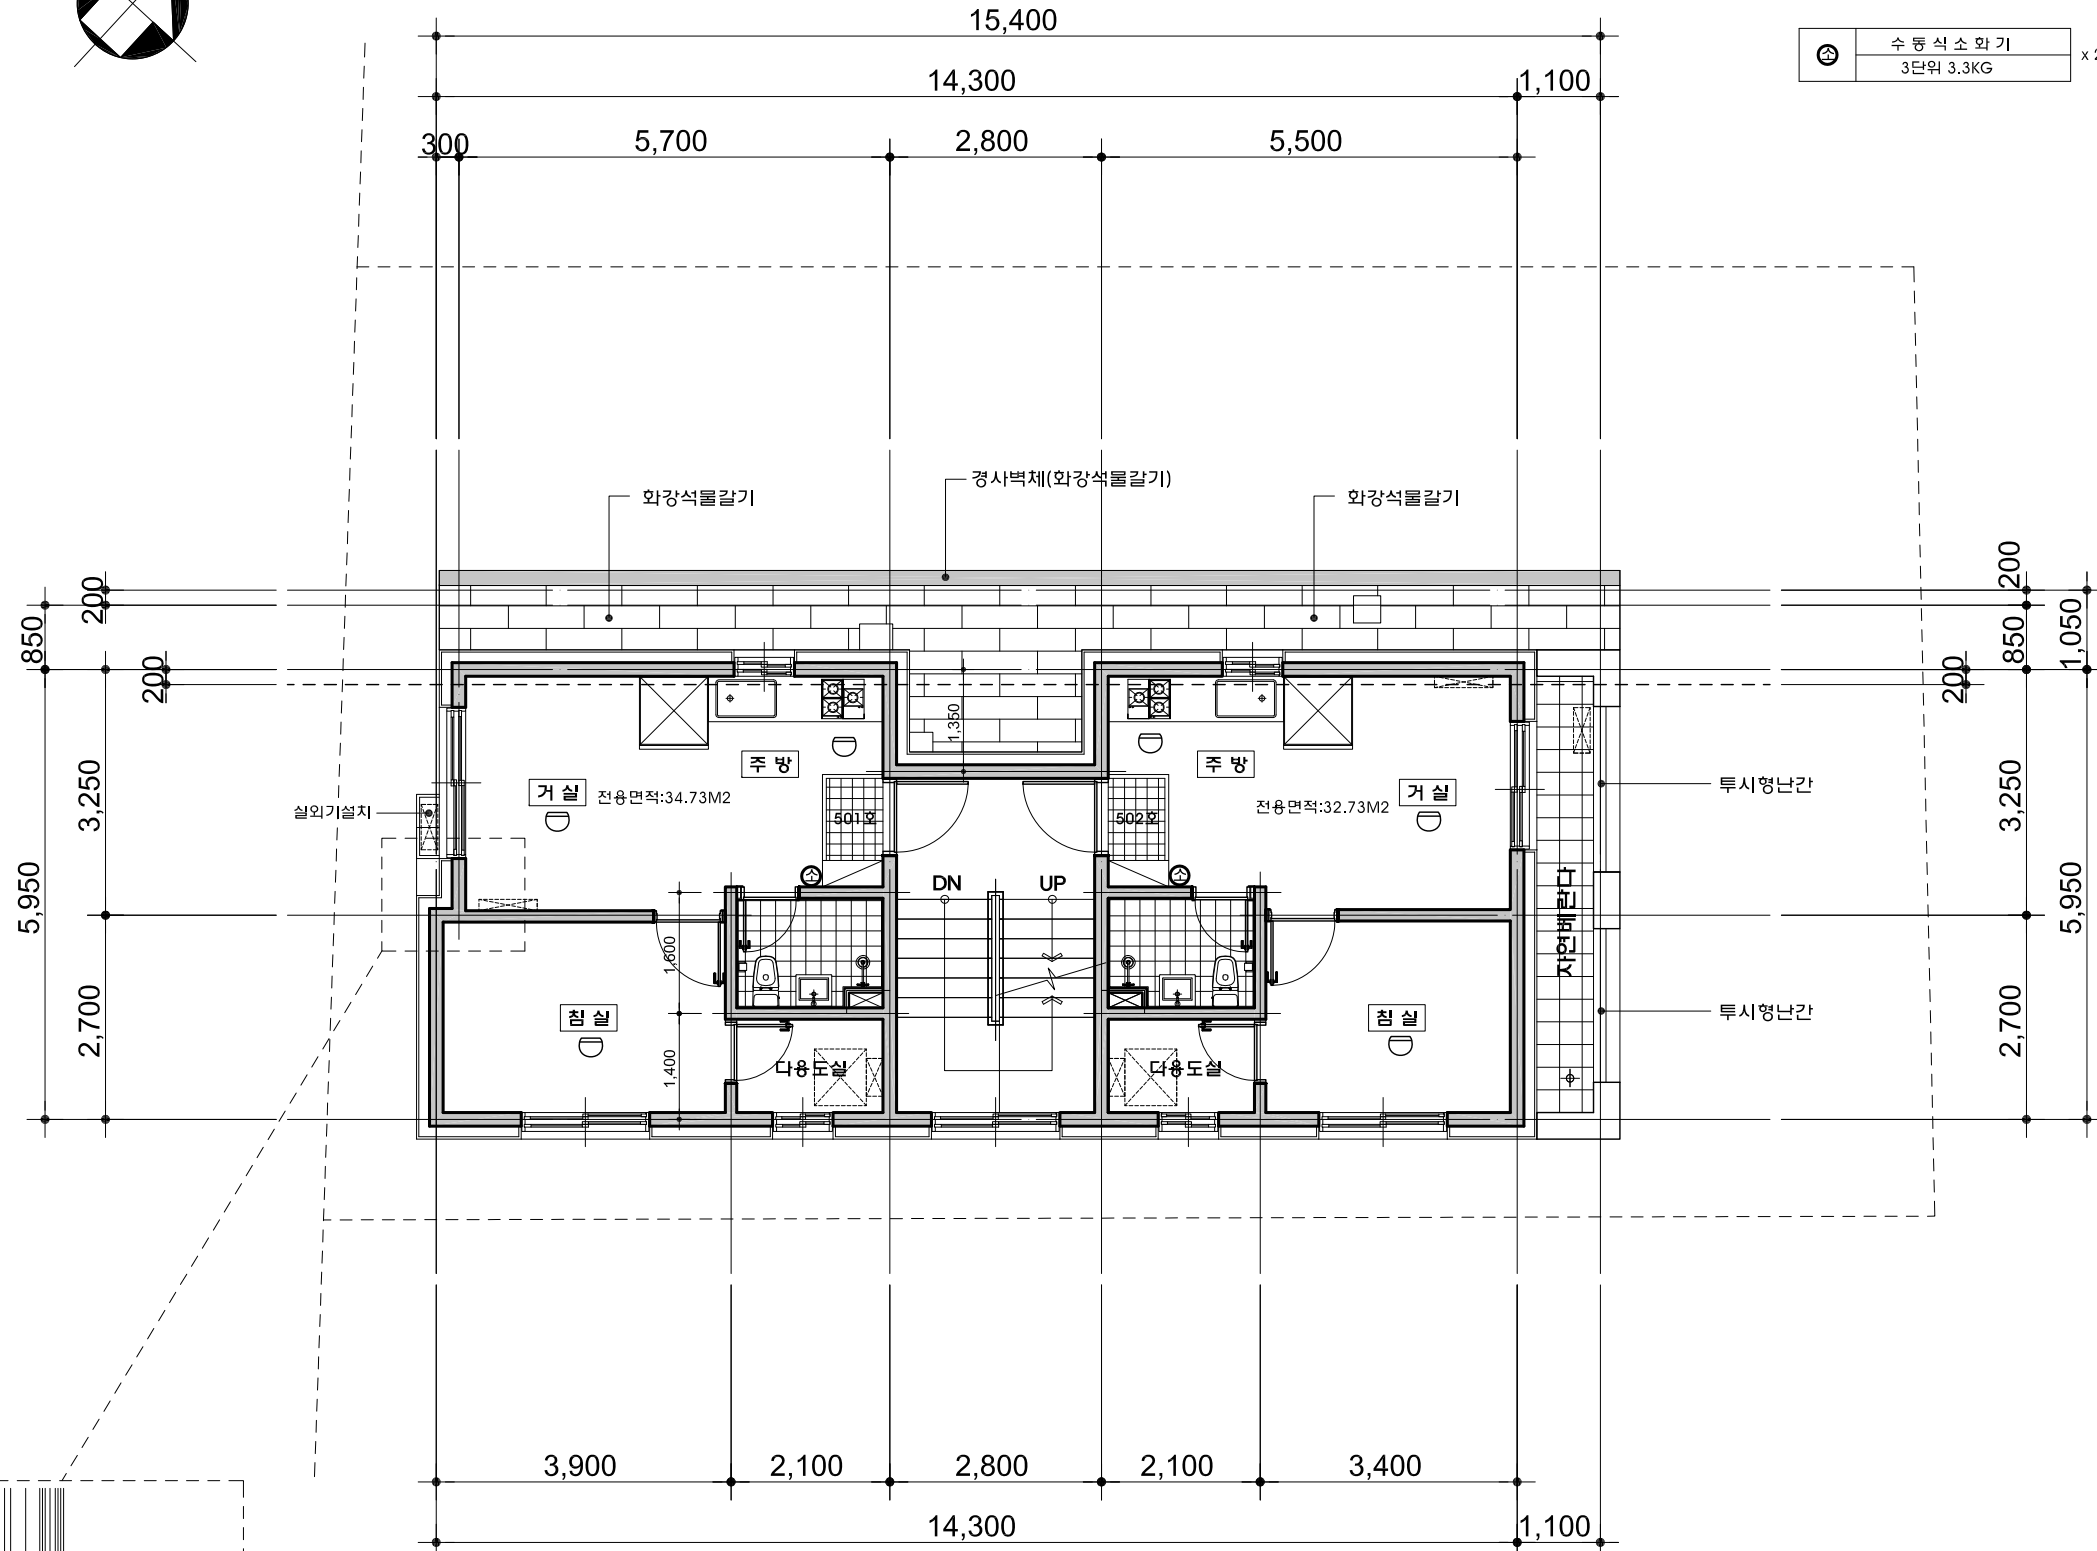


5 층 평 면 도

SCALE:1/100

주 기

- 세대 현관문 도어체크 및 스토퍼 계획
- 세대 발코니 설치시 세대간 분리벽 계획
- 세대 발코니 설치시 세대간 분리벽 계획
- 세대내 비디오폰 설치
- 주차장내 CCTV 설치
- | | |
|---------|--|
| 외벽 | 직접 외기에 면한 실내벽면은 단열재 (아이소핑크10mm+석고보드 마감도면 표기) |
| 계단실 /복도 | 간접 외기에 면한 실내벽면은 단열재 (아이소핑크20mm+석고보드 마감도면 표기) |
- 에어콘 실외기 설치위치 및 에어컨 콘센트 및 냉매 및 배수관 위치 도면표기(배수관 수직으로 매립)
 - (에어콘 콘센트 표기)
- 불박이 가구 내부 다용도 수납가능도록 수평이동 칸막이 설치
- 콘크리트 폴타이 제거후 마감공사 시공(방수 및 단열재 시공등)

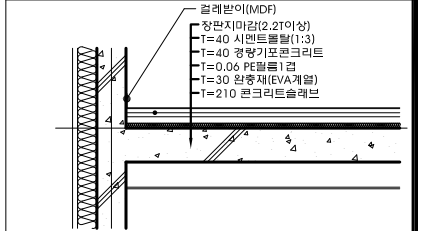

NOTE:

PROJECT 서대문구 홍제동 360-40,41번지
다세대주택 신축공사

APPROVED BY




건축사사무소 유일엔지니어링
SEOUL, KOREA
TEL:540-1546, FAX:540-1576


TITLE 1 층 평 면 도

DATE: 2017. 07

SCALE	1/100	DWG NO.	REV.
-------	-------	---------	------

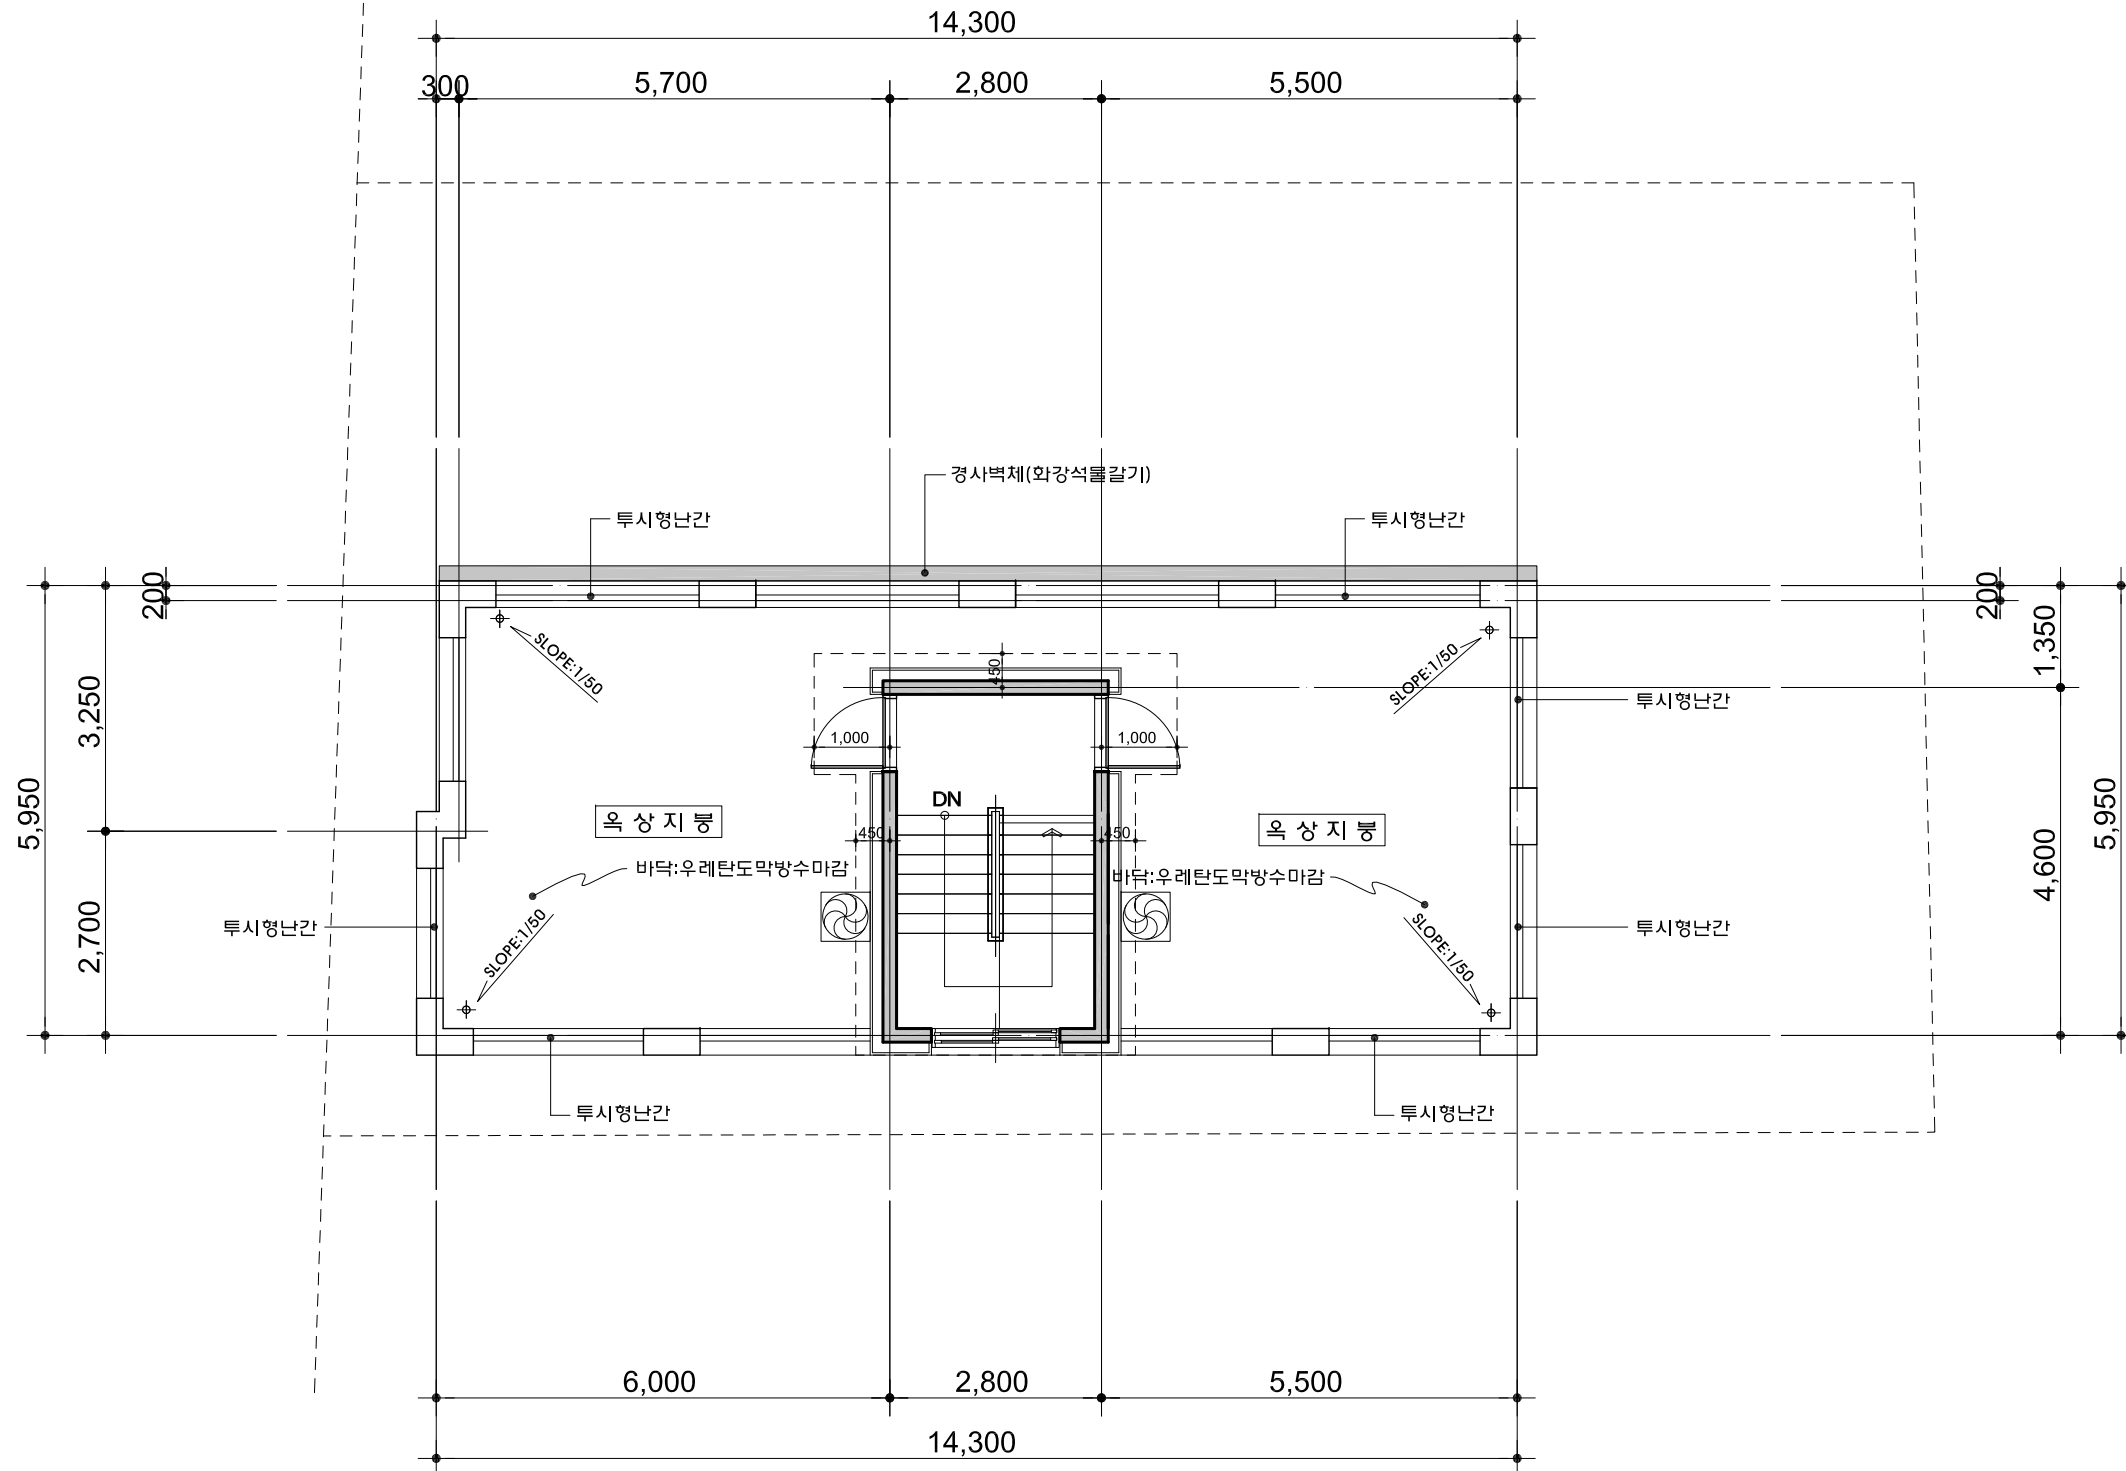


NOTE:			
PROJECT 서대문구 홍재동 360-40, 41번지 다세대주택 신축공사			
APPROVED BY			
 건축사사무소 유일엔지니어링 SEOUL, KOREA TEL:540-1546, FAX:540-1576			
TITLE 옥 5층 평면도			
DATE: 2017. 07			
SCALE	1/100	DWG NO.	REV.

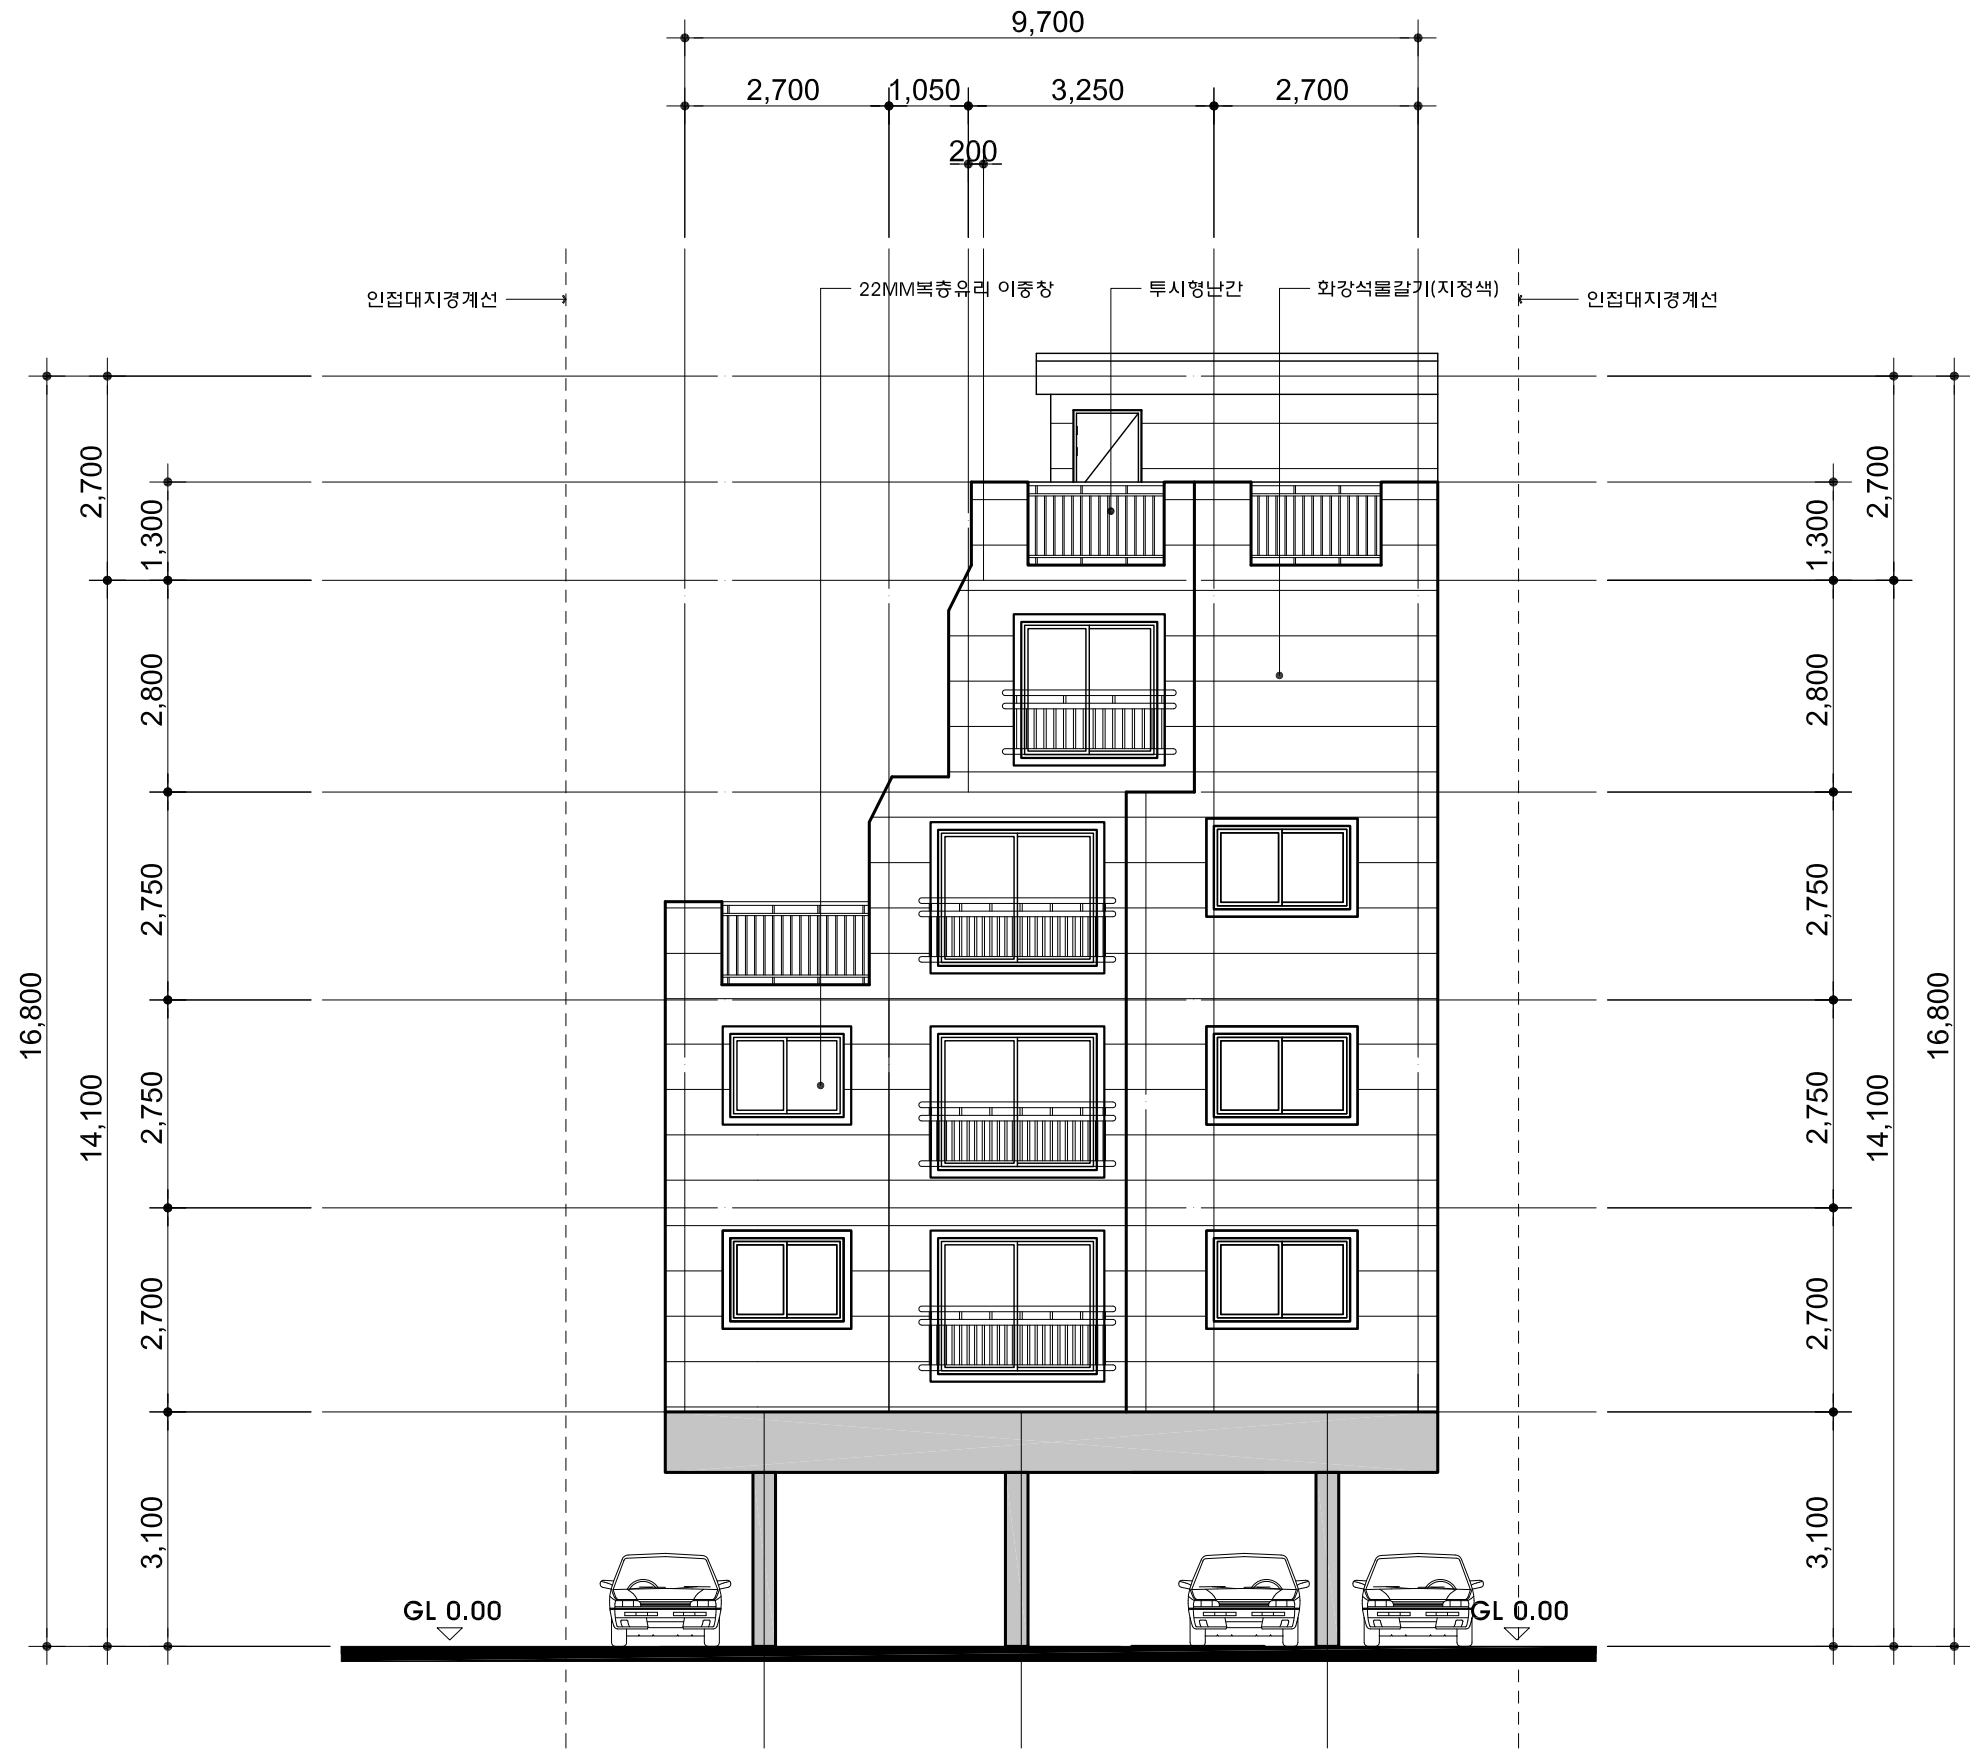


정 면 도 (동 측 면 도)
SCALE:1/100

NOTE:			
PROJECT 서대문구 홍제동 360-40,41번지 다세대주택 신축공사			
APPROVED BY			
 건축사사무소 유알엔지니어링 SEOUL, KOREA TEL:540-1546, FAX:540-1576			
TITLE 정 면 도 (동 측 면 도)			
DATE: 2016. 10.			
SCALE	1/100	DWG NO.	REV.

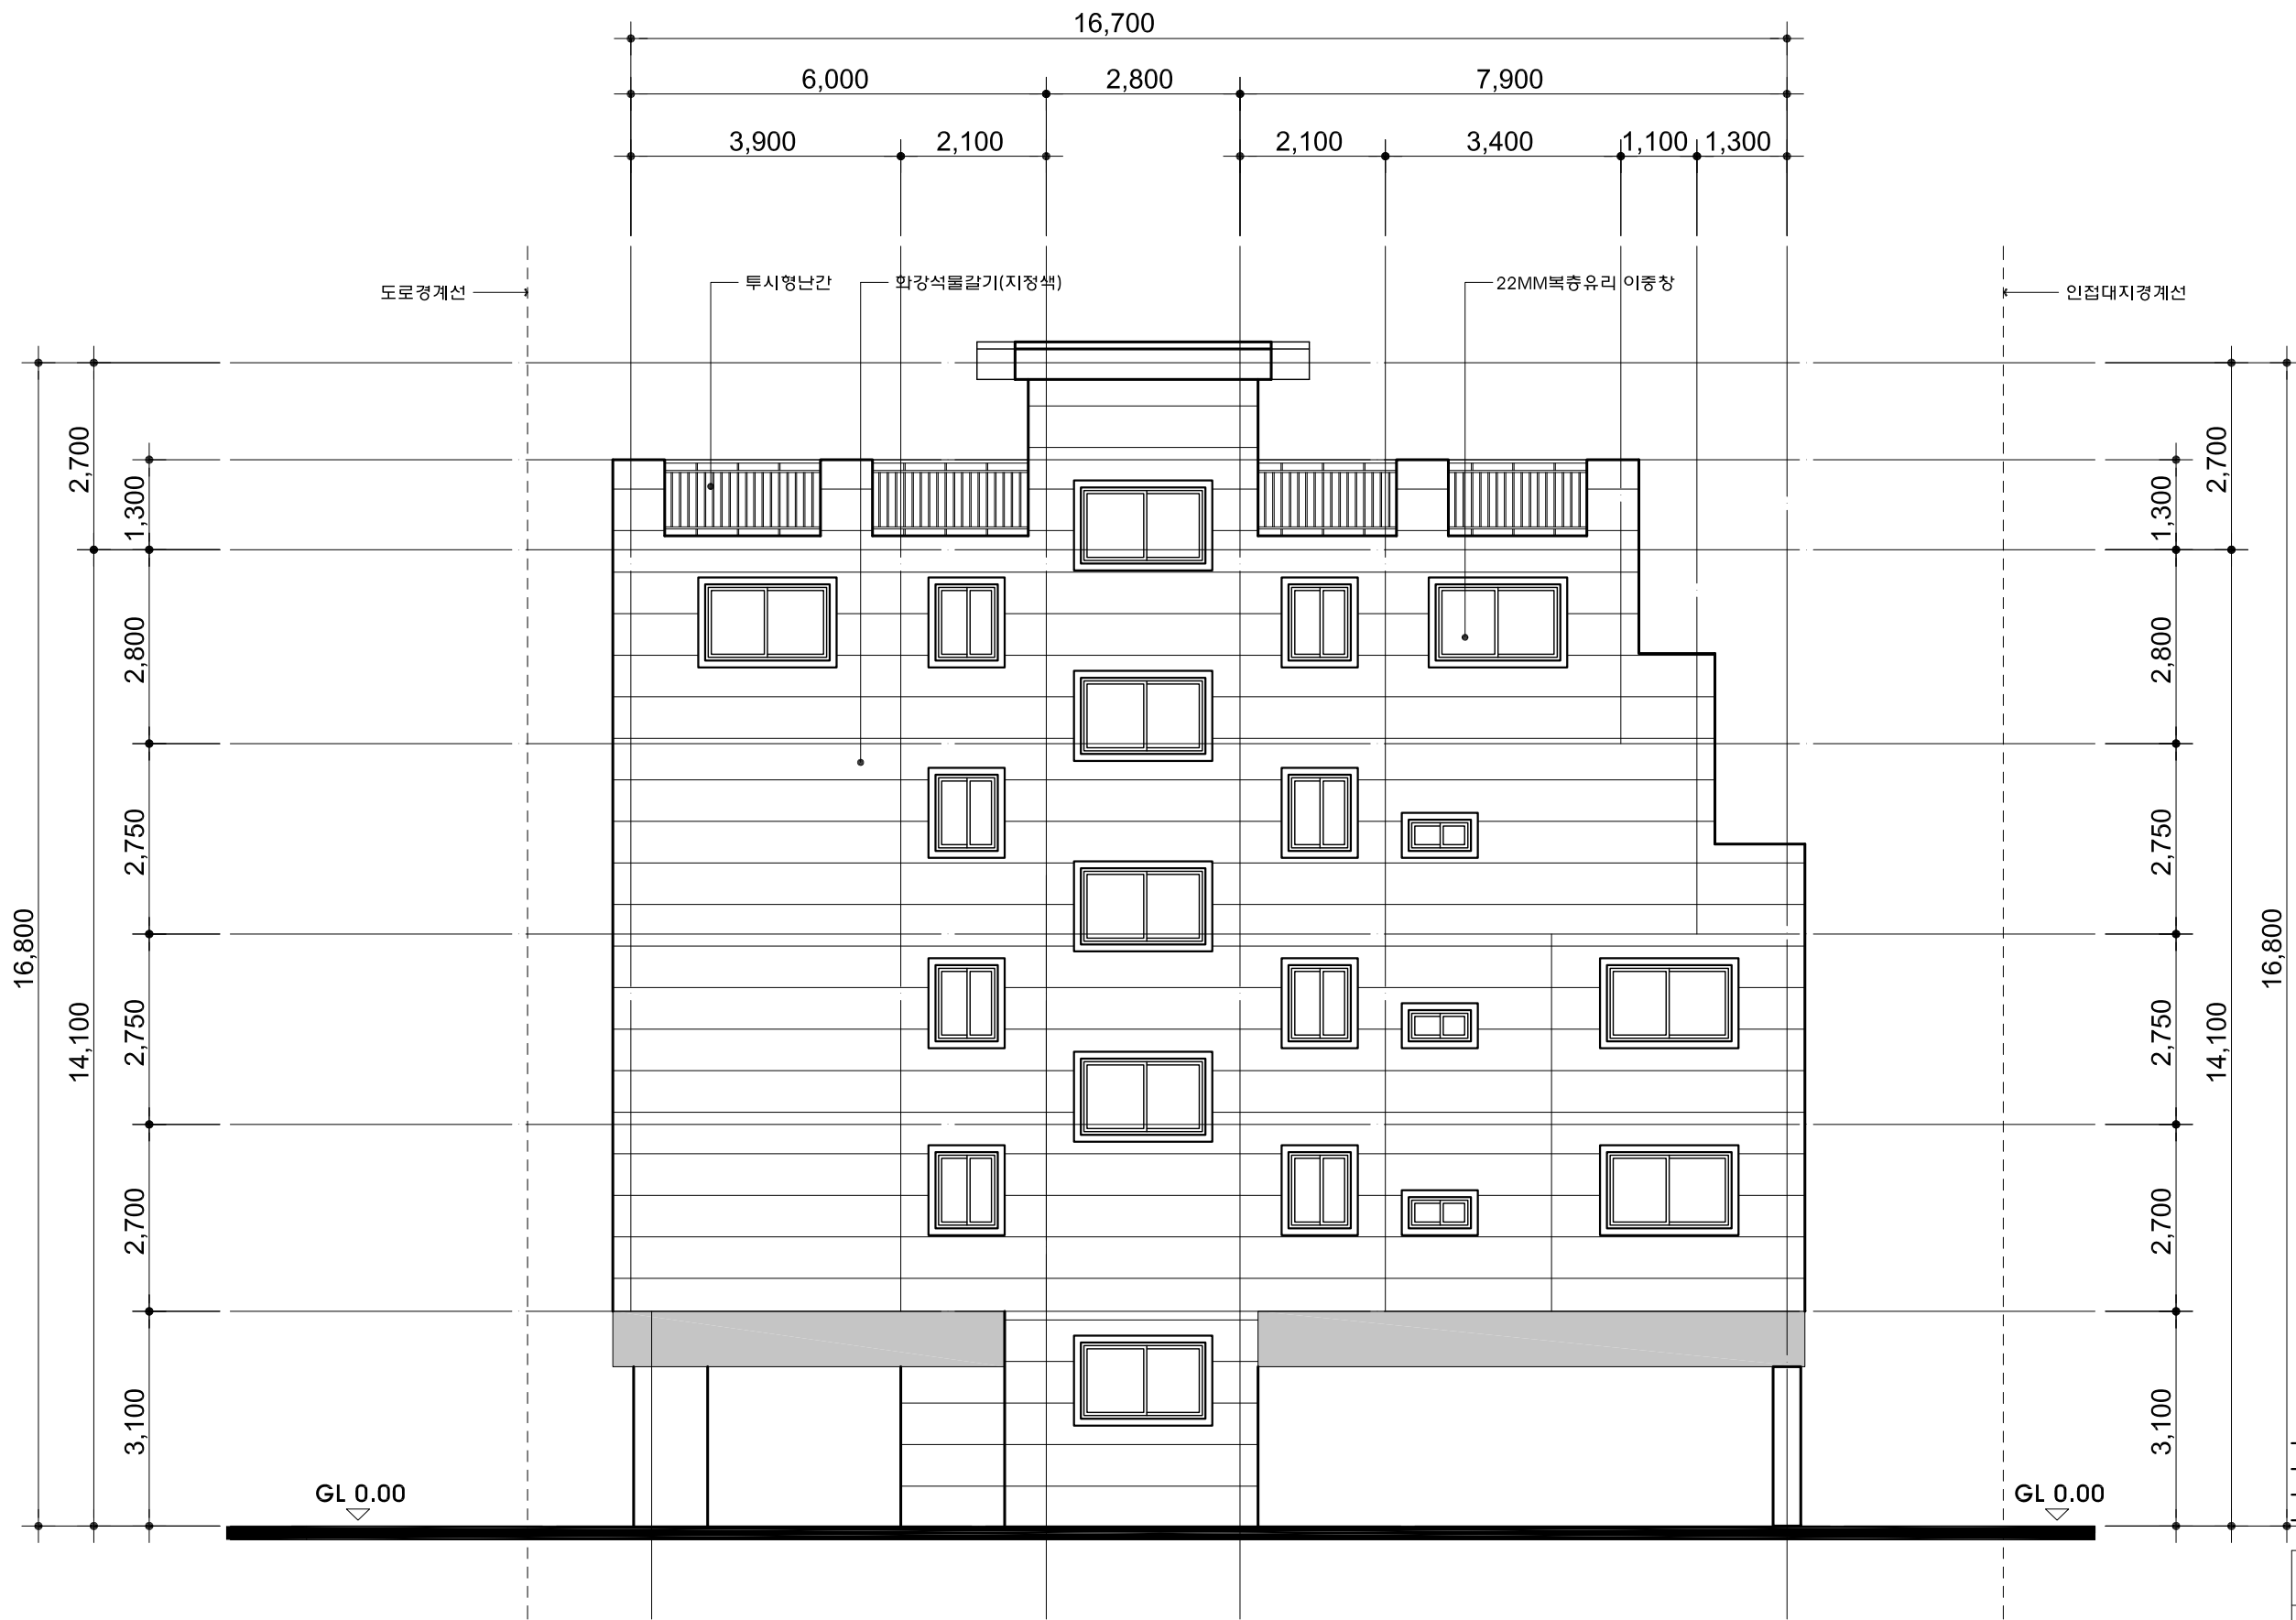

우 측 면 도 (북 측 면 도)
SCALE:1/100


NOTE:			
PROJECT	서대문구 홍제동 360-40,41번지 다세대주택 신축공사		
APPROVED BY			
	 건축사사무소 유알엔지니어링 SEOUL, KOREA TEL:540-1546, FAX:540-1576		
TITLE	우 측 면 도 (북 측 면 도)		
DATE:	2016. 10.		
SCALE	1/100	DWG NO.	REV.

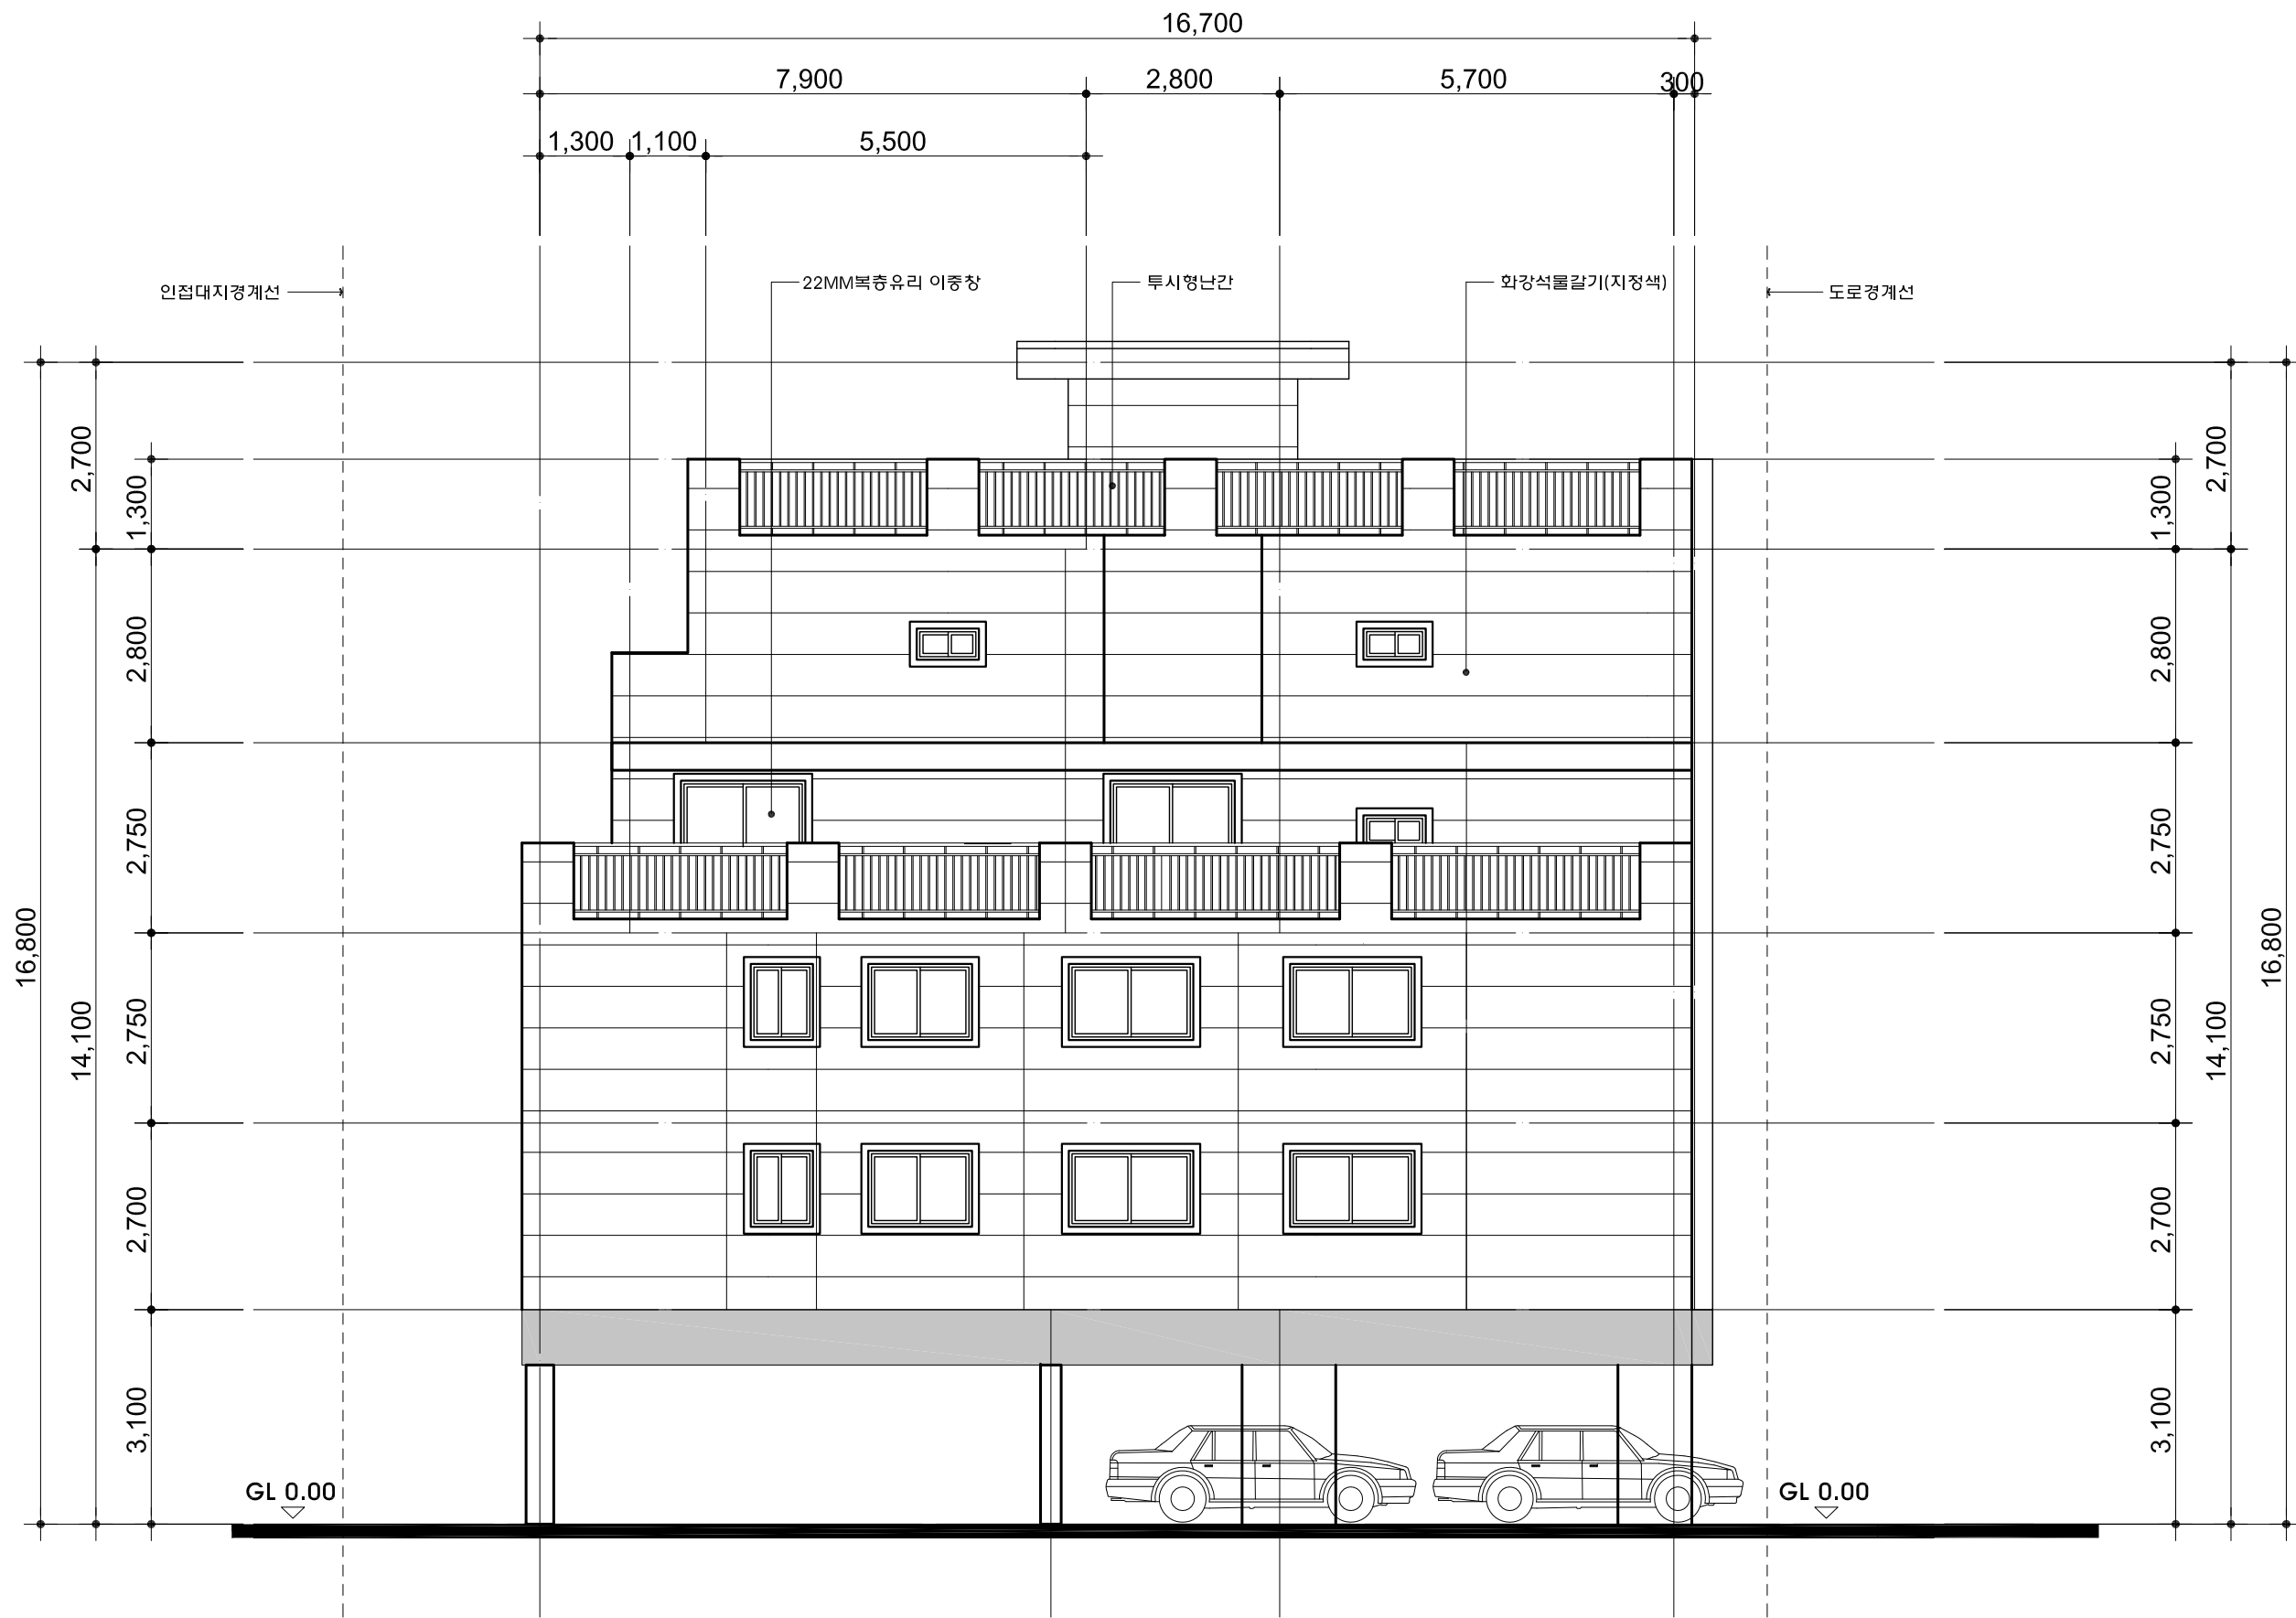

좌 측 면 도 (서 측 면 도)

SCALE:1/100

NOTE:			
PROJECT 서대문구 홍재동 360-40,41번지 다세대주택 신축공사			
APPROVED BY			
건축사사무소 유알엔지니어링 SEOUL, KOREA TEL:540-1546, FAX:540-1576			
TITLE 좌 측 면 도 (서 측 면 도)			
DATE: 2016. 10.			
SCALE	1/100	DWG NO.	REV.

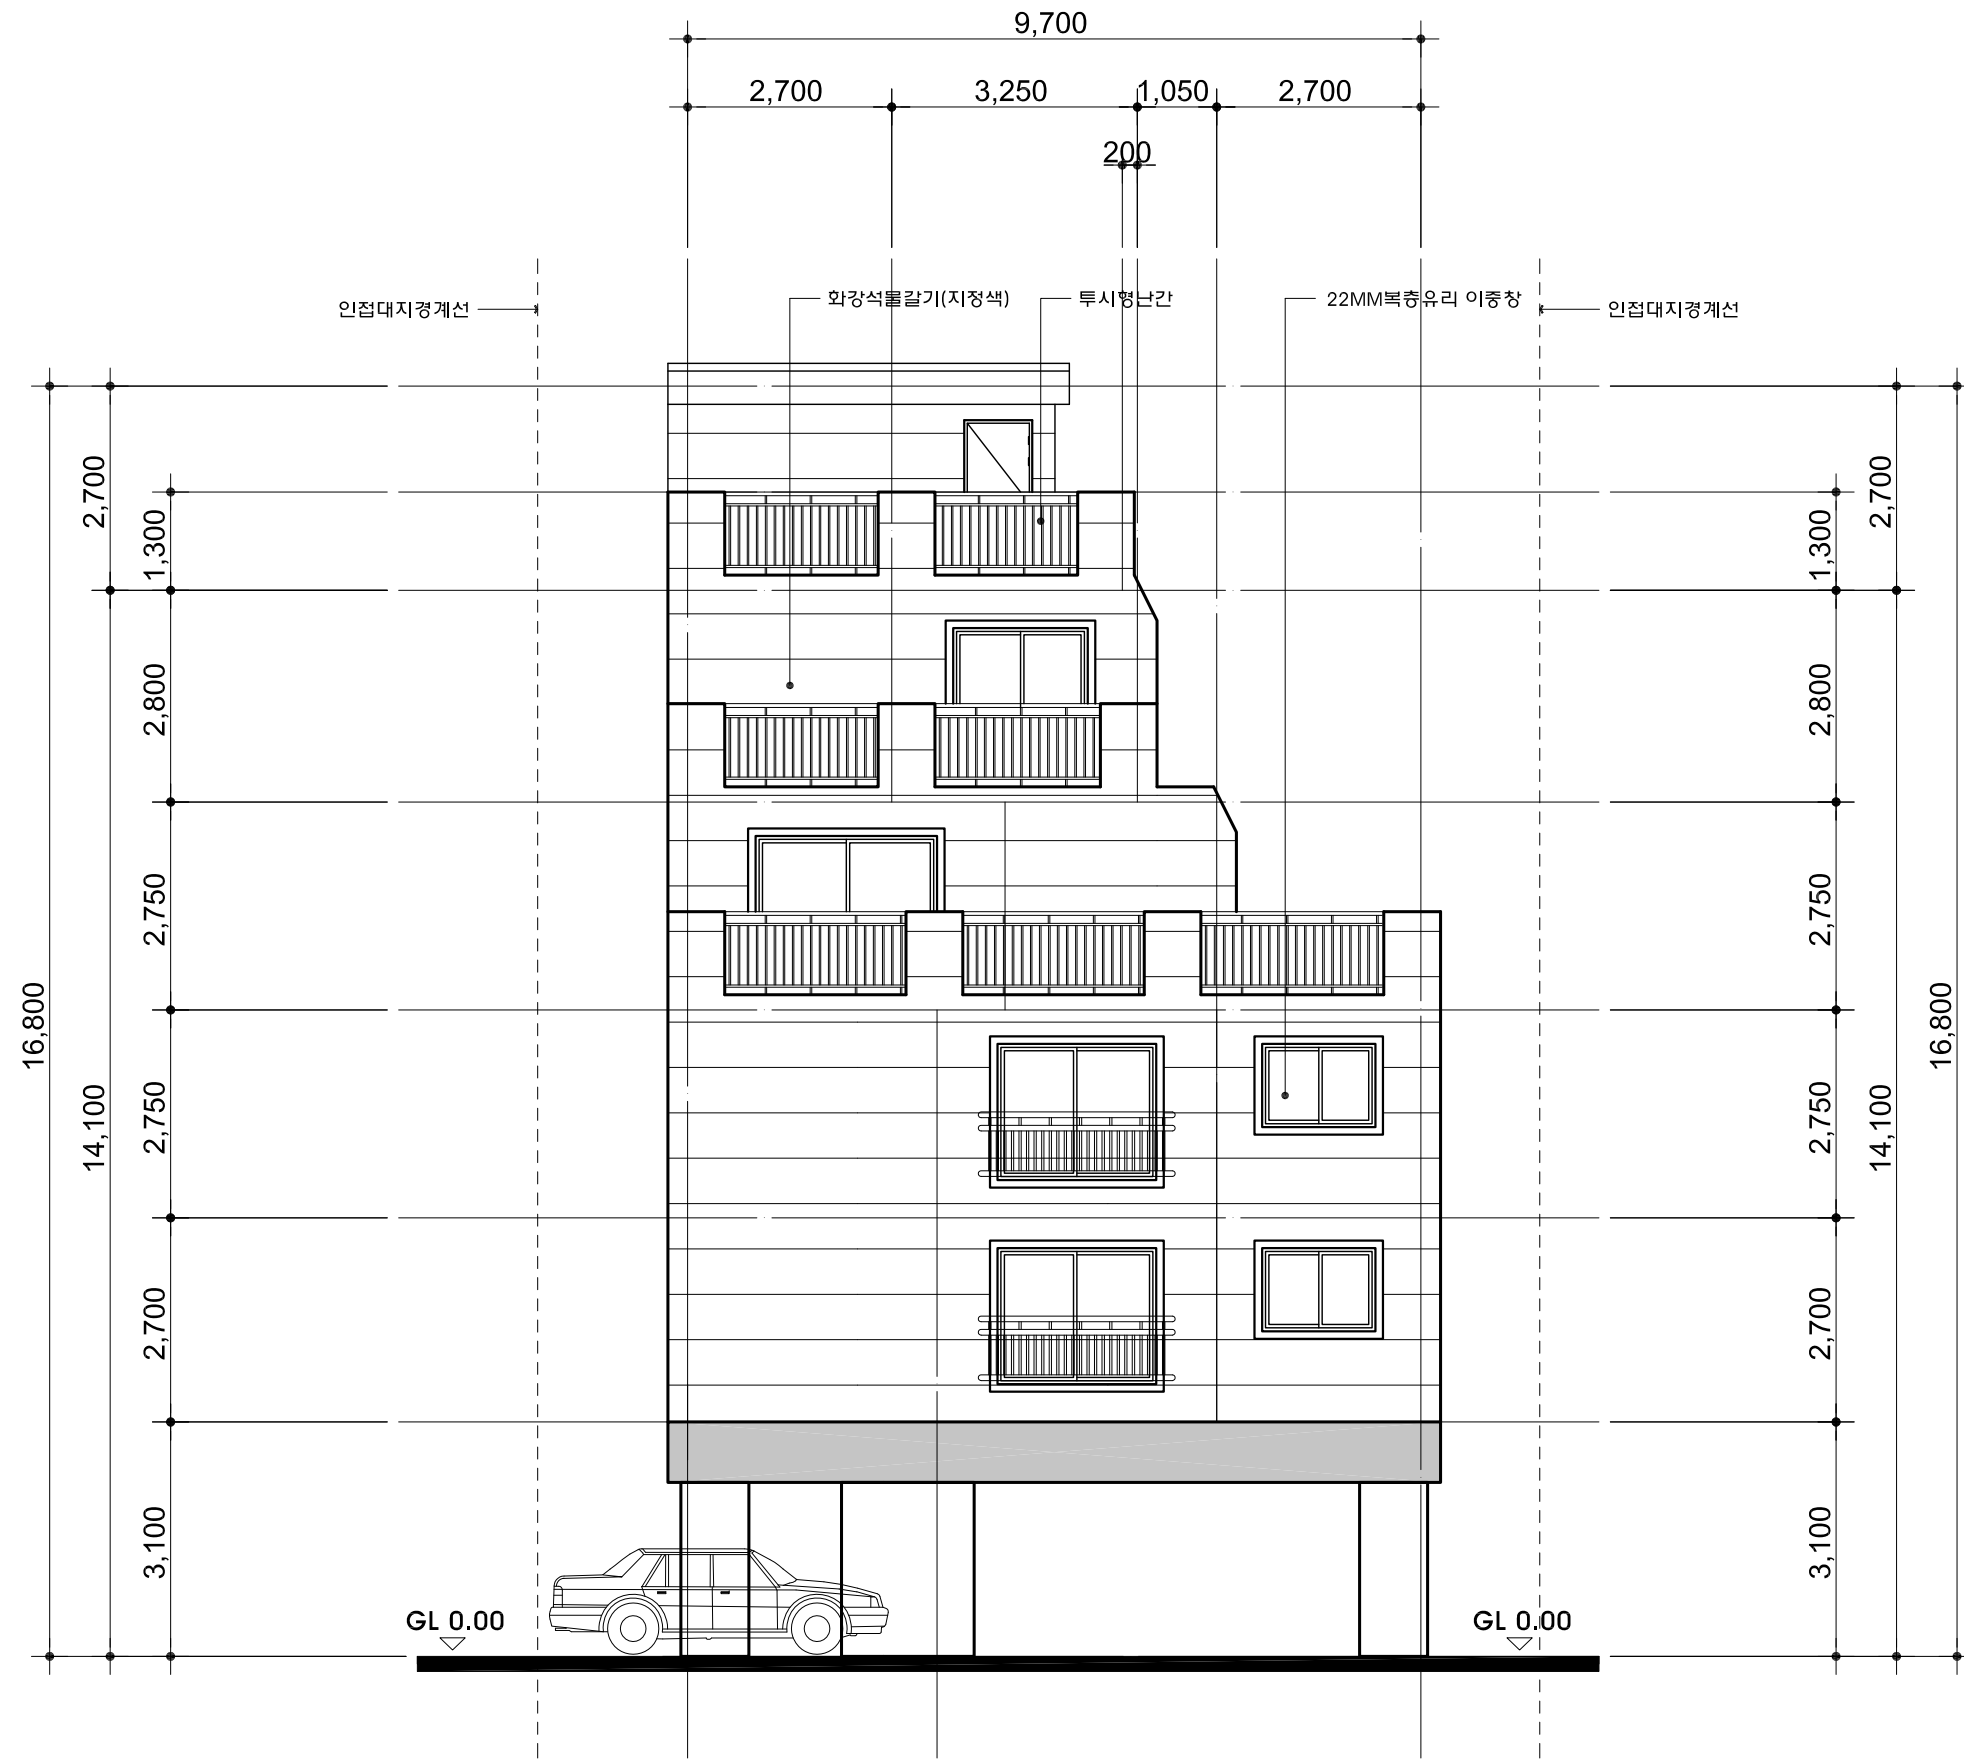

배 면 도 (서 측 면 도)
SCALE:1/100

NOTE:			
PROJECT			
서대문구 홍제동 360-40,41번지			
다세대주택 신축공사			
APPROVED BY			
TITLE			
배 면 도 (서 측 면 도)			
DATE:			
2016. 10.			
SCALE	1/100	DWG NO.	REV.