










주 차 대 수		9세대 X 0.5대 = 4.5대 $\left\{ \begin{array}{l} 9 \\ 6 \end{array} \right\} \rightarrow 6.9\text{대 (7대 계획)}$ 6세대 X 0.4대 = 2.4대 *서울시 공공주택건설 및 공급등에 관한 조례 제2조 1호, 마목 및 제11조의2 에의거 주차산정함. 세대당 0.5대(전용면적이 30㎡ 미만인경우 세대당 0.4대)
	계 획	7대 설치



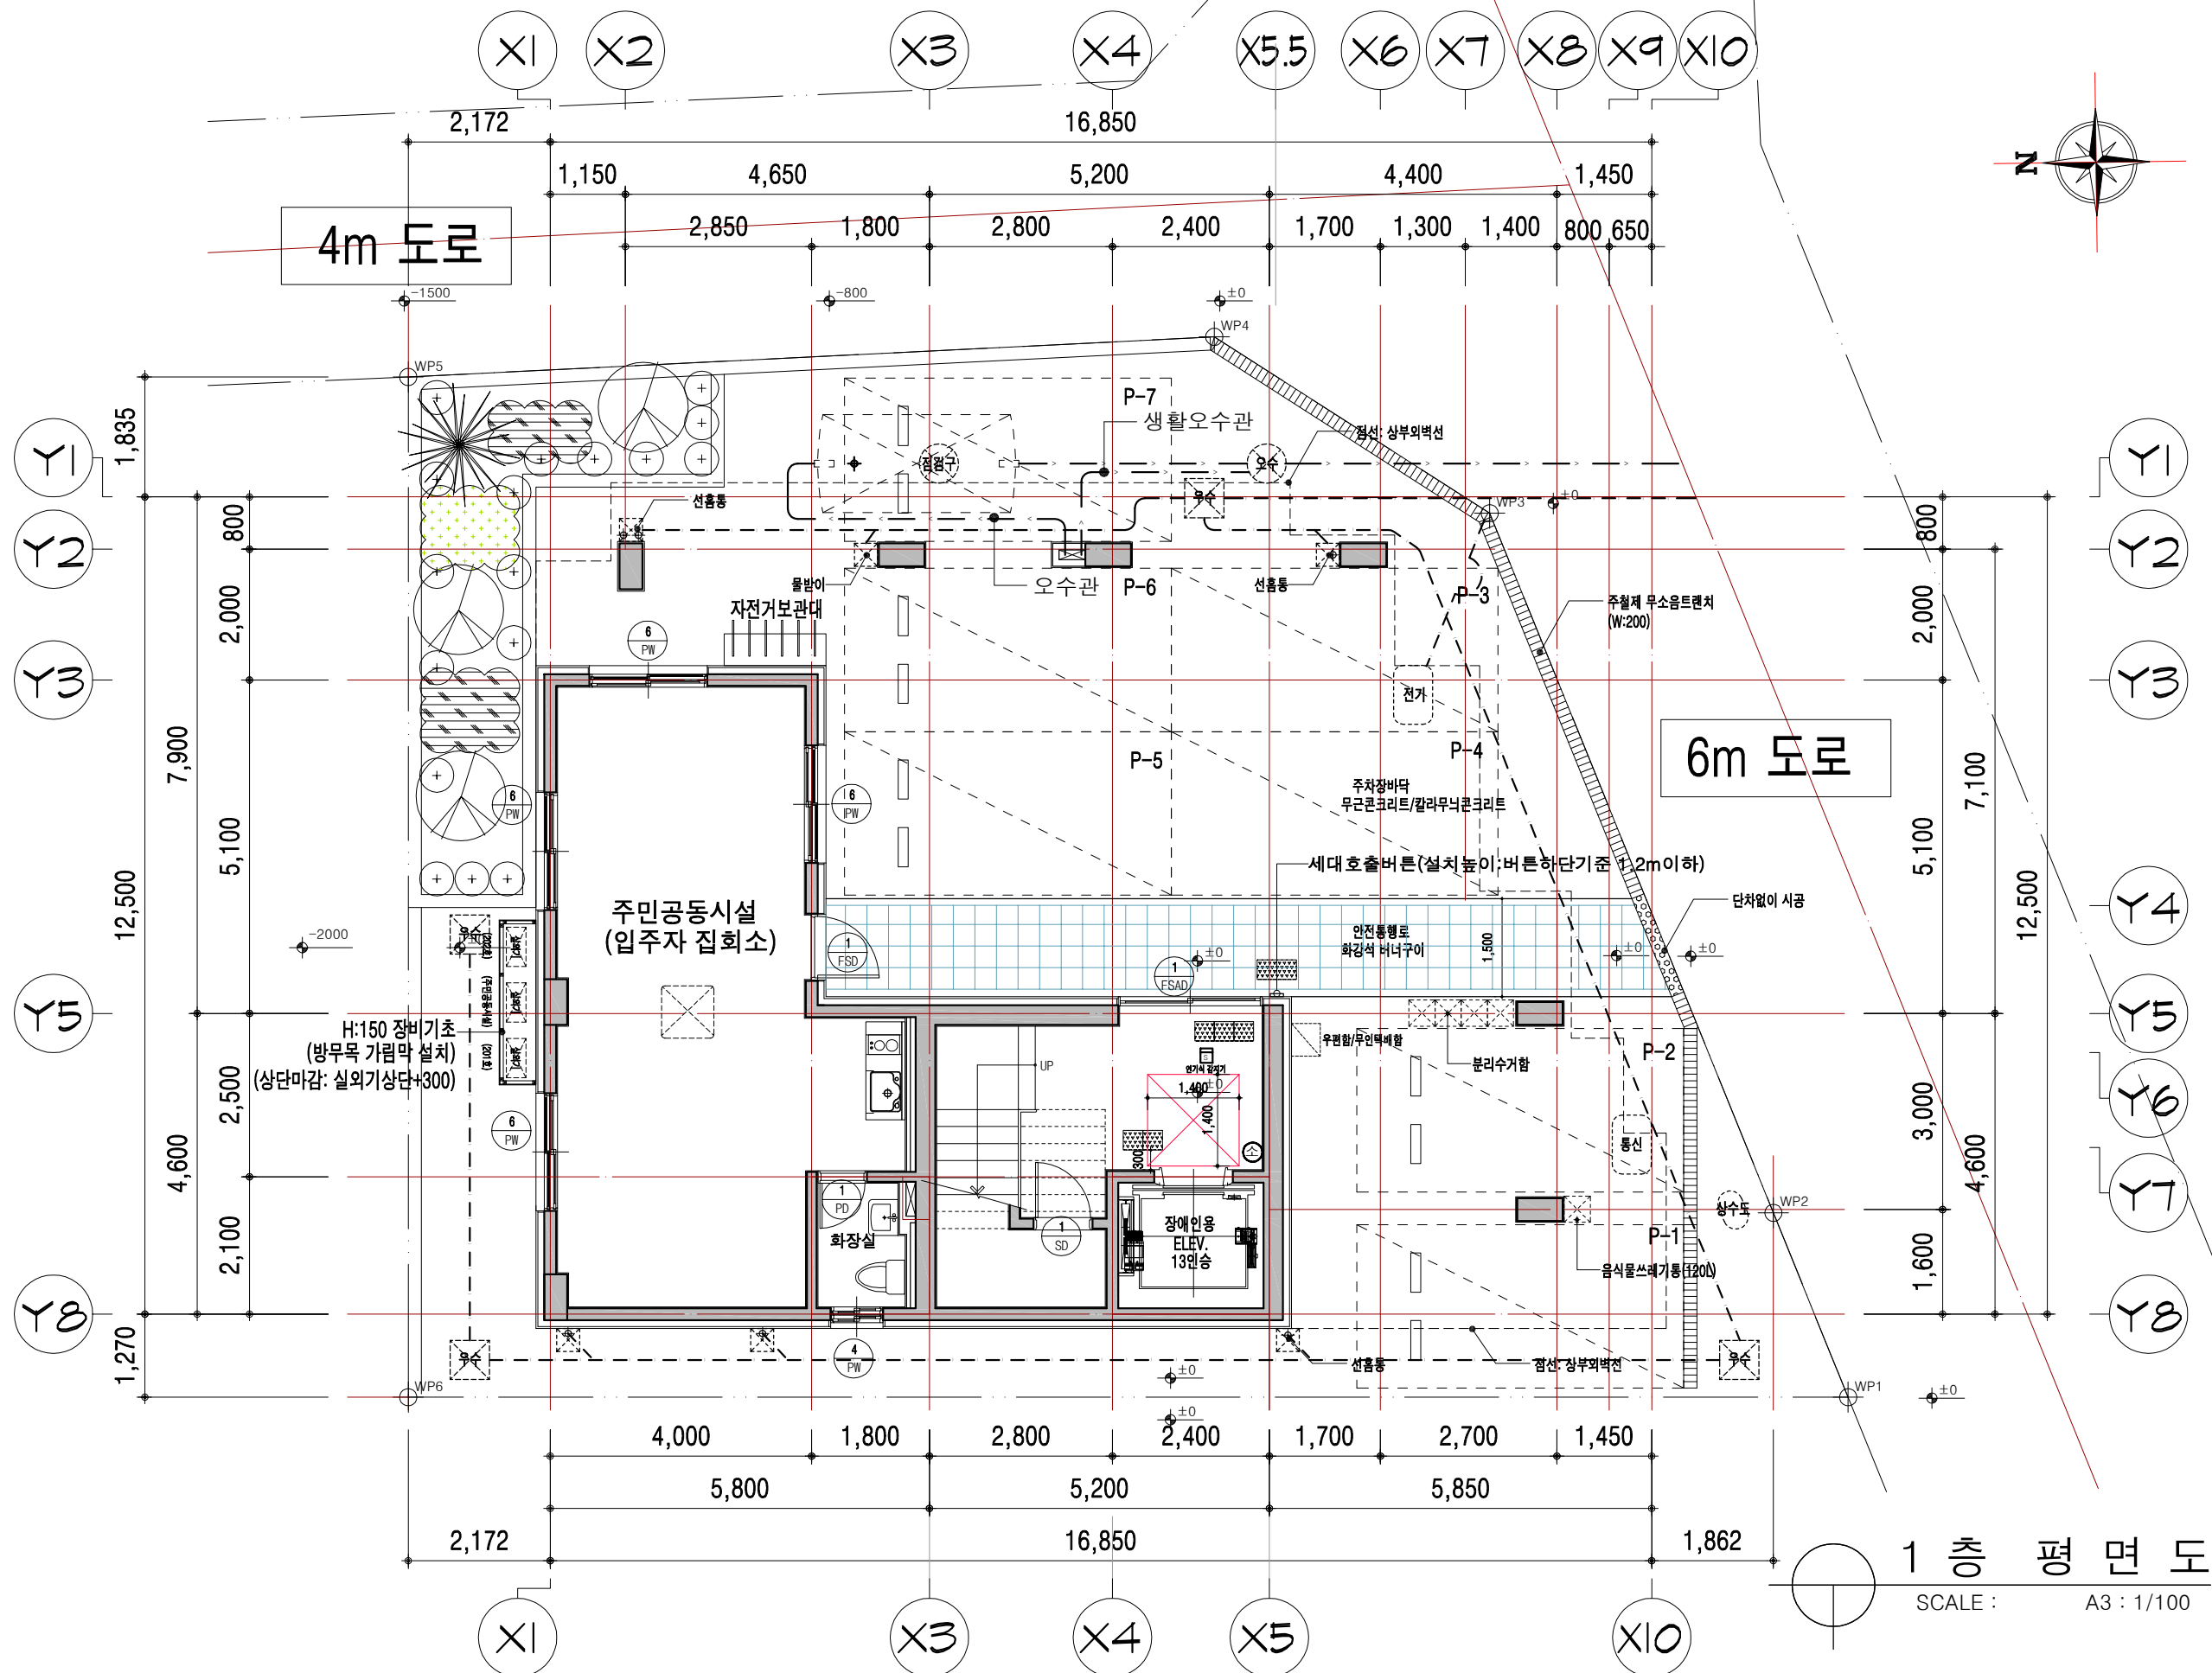


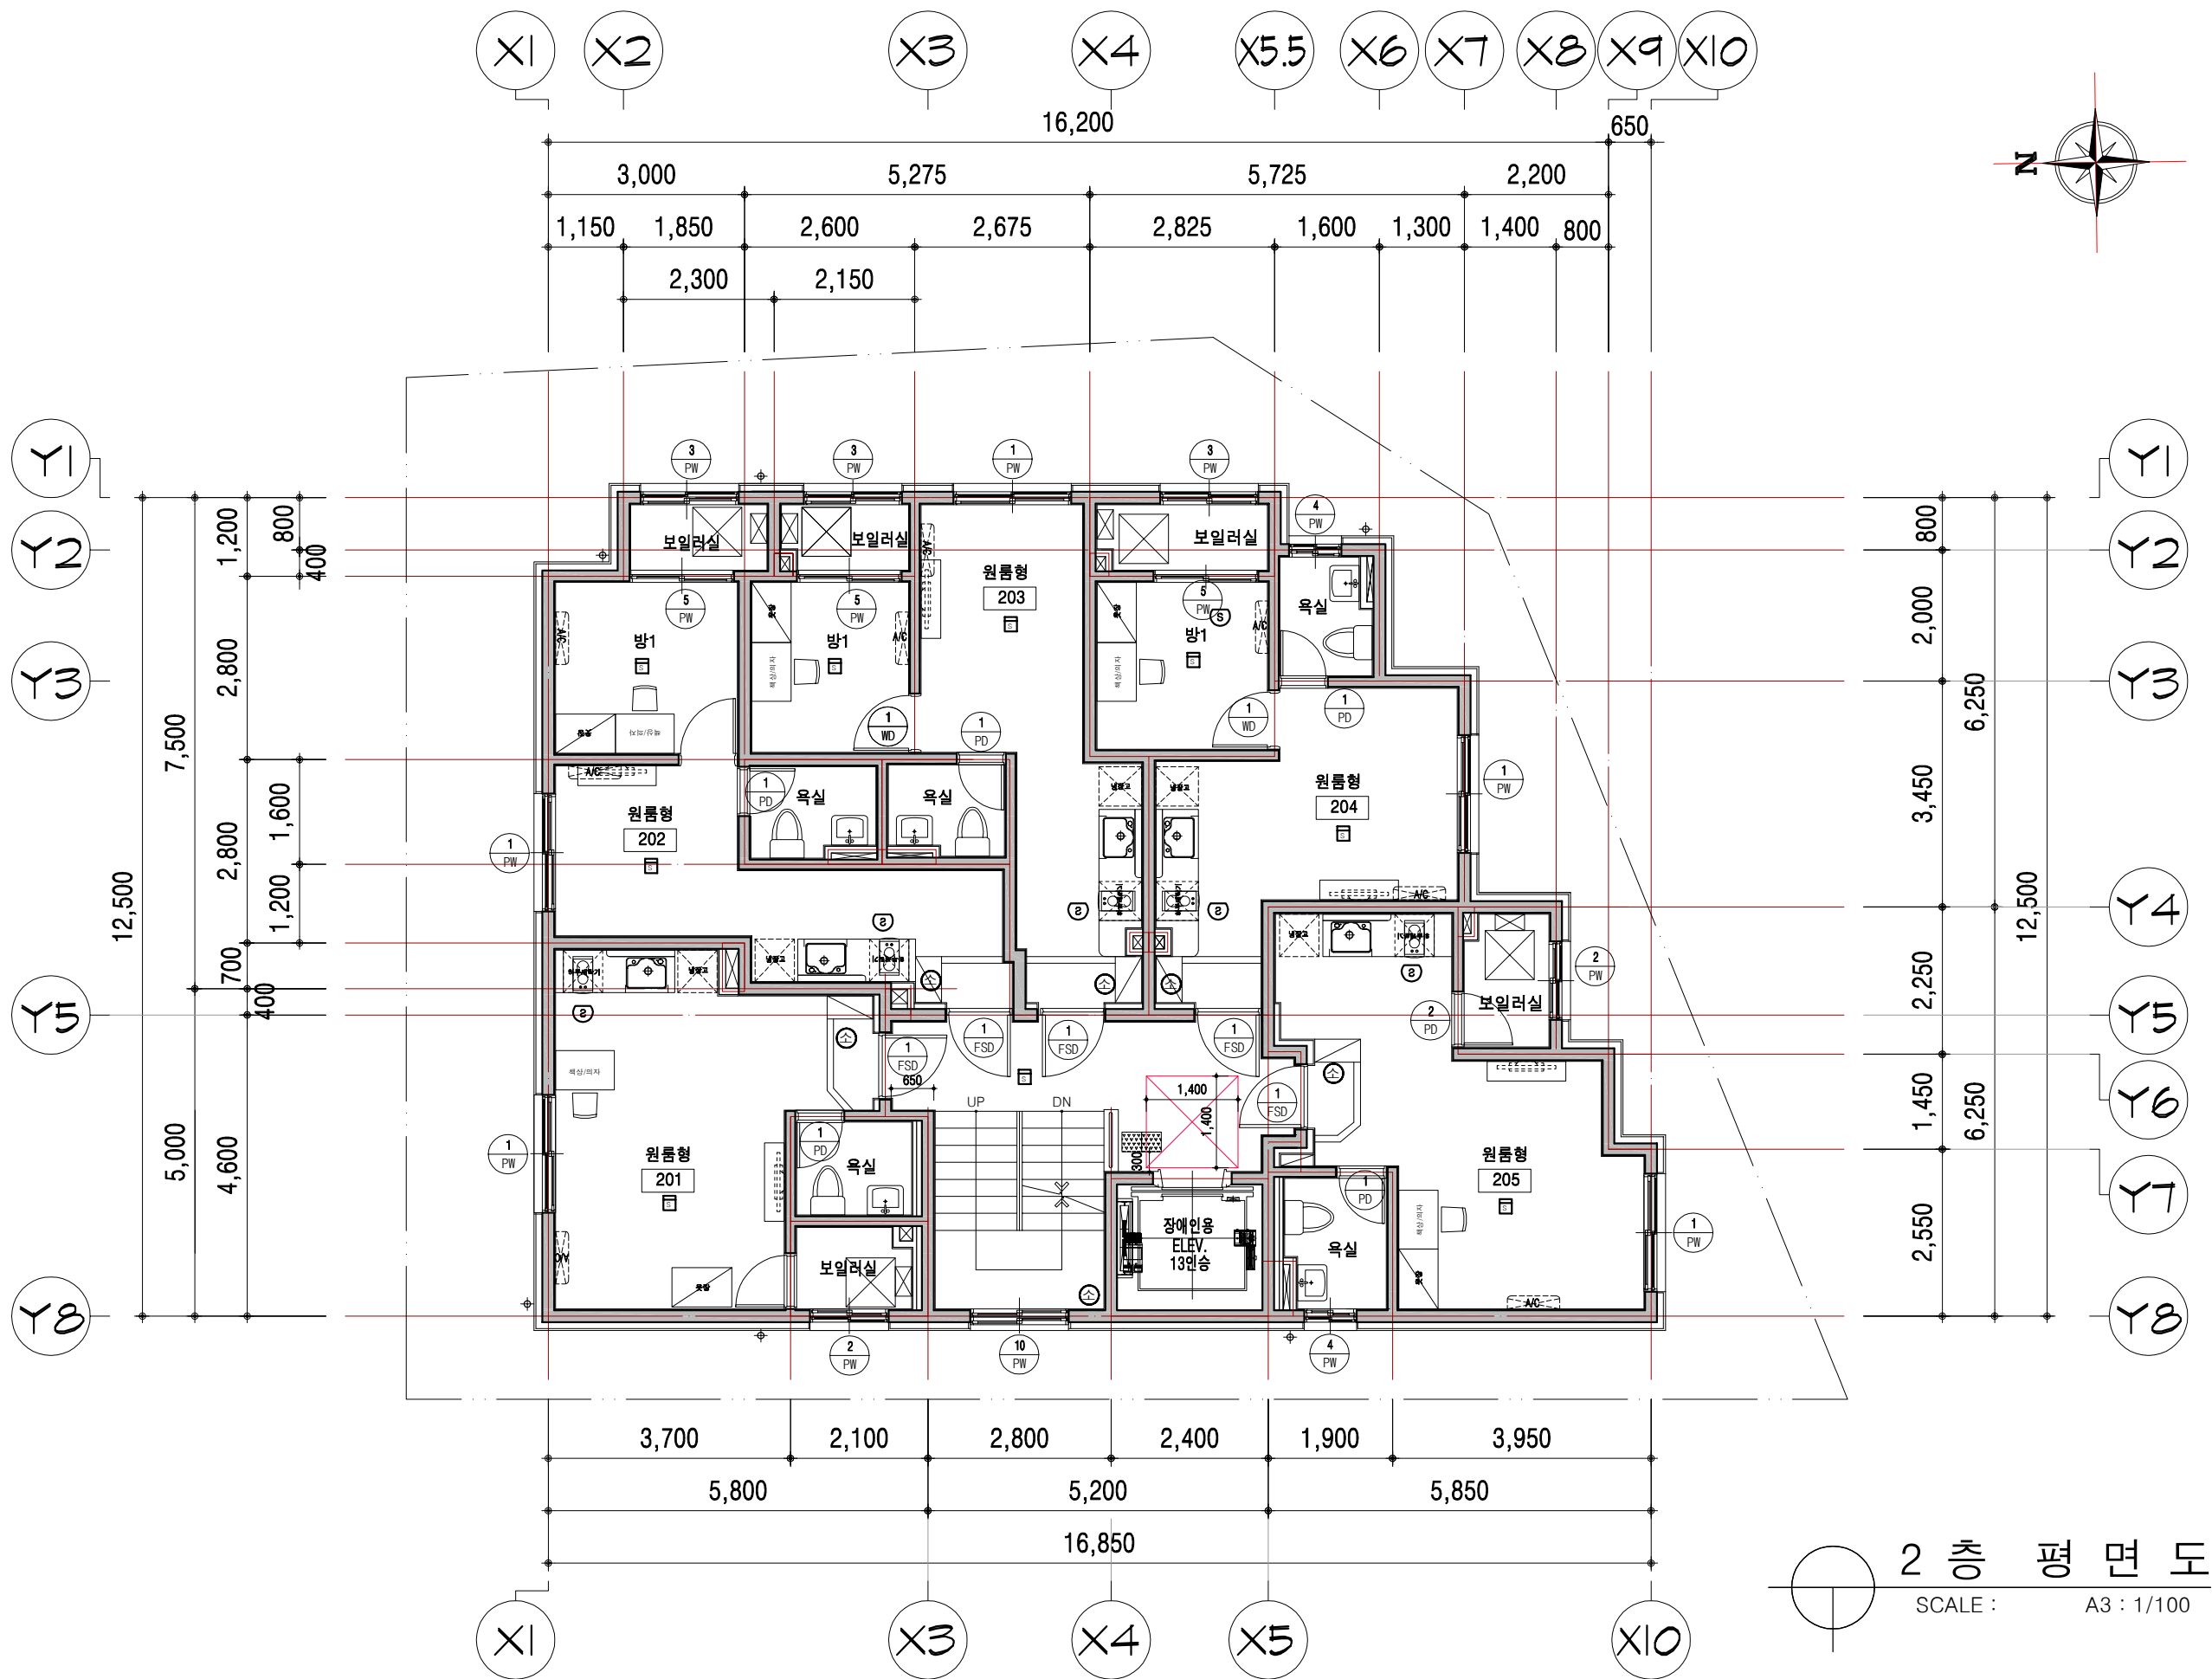


2층 평면도
SCALE : A3 : 1/100

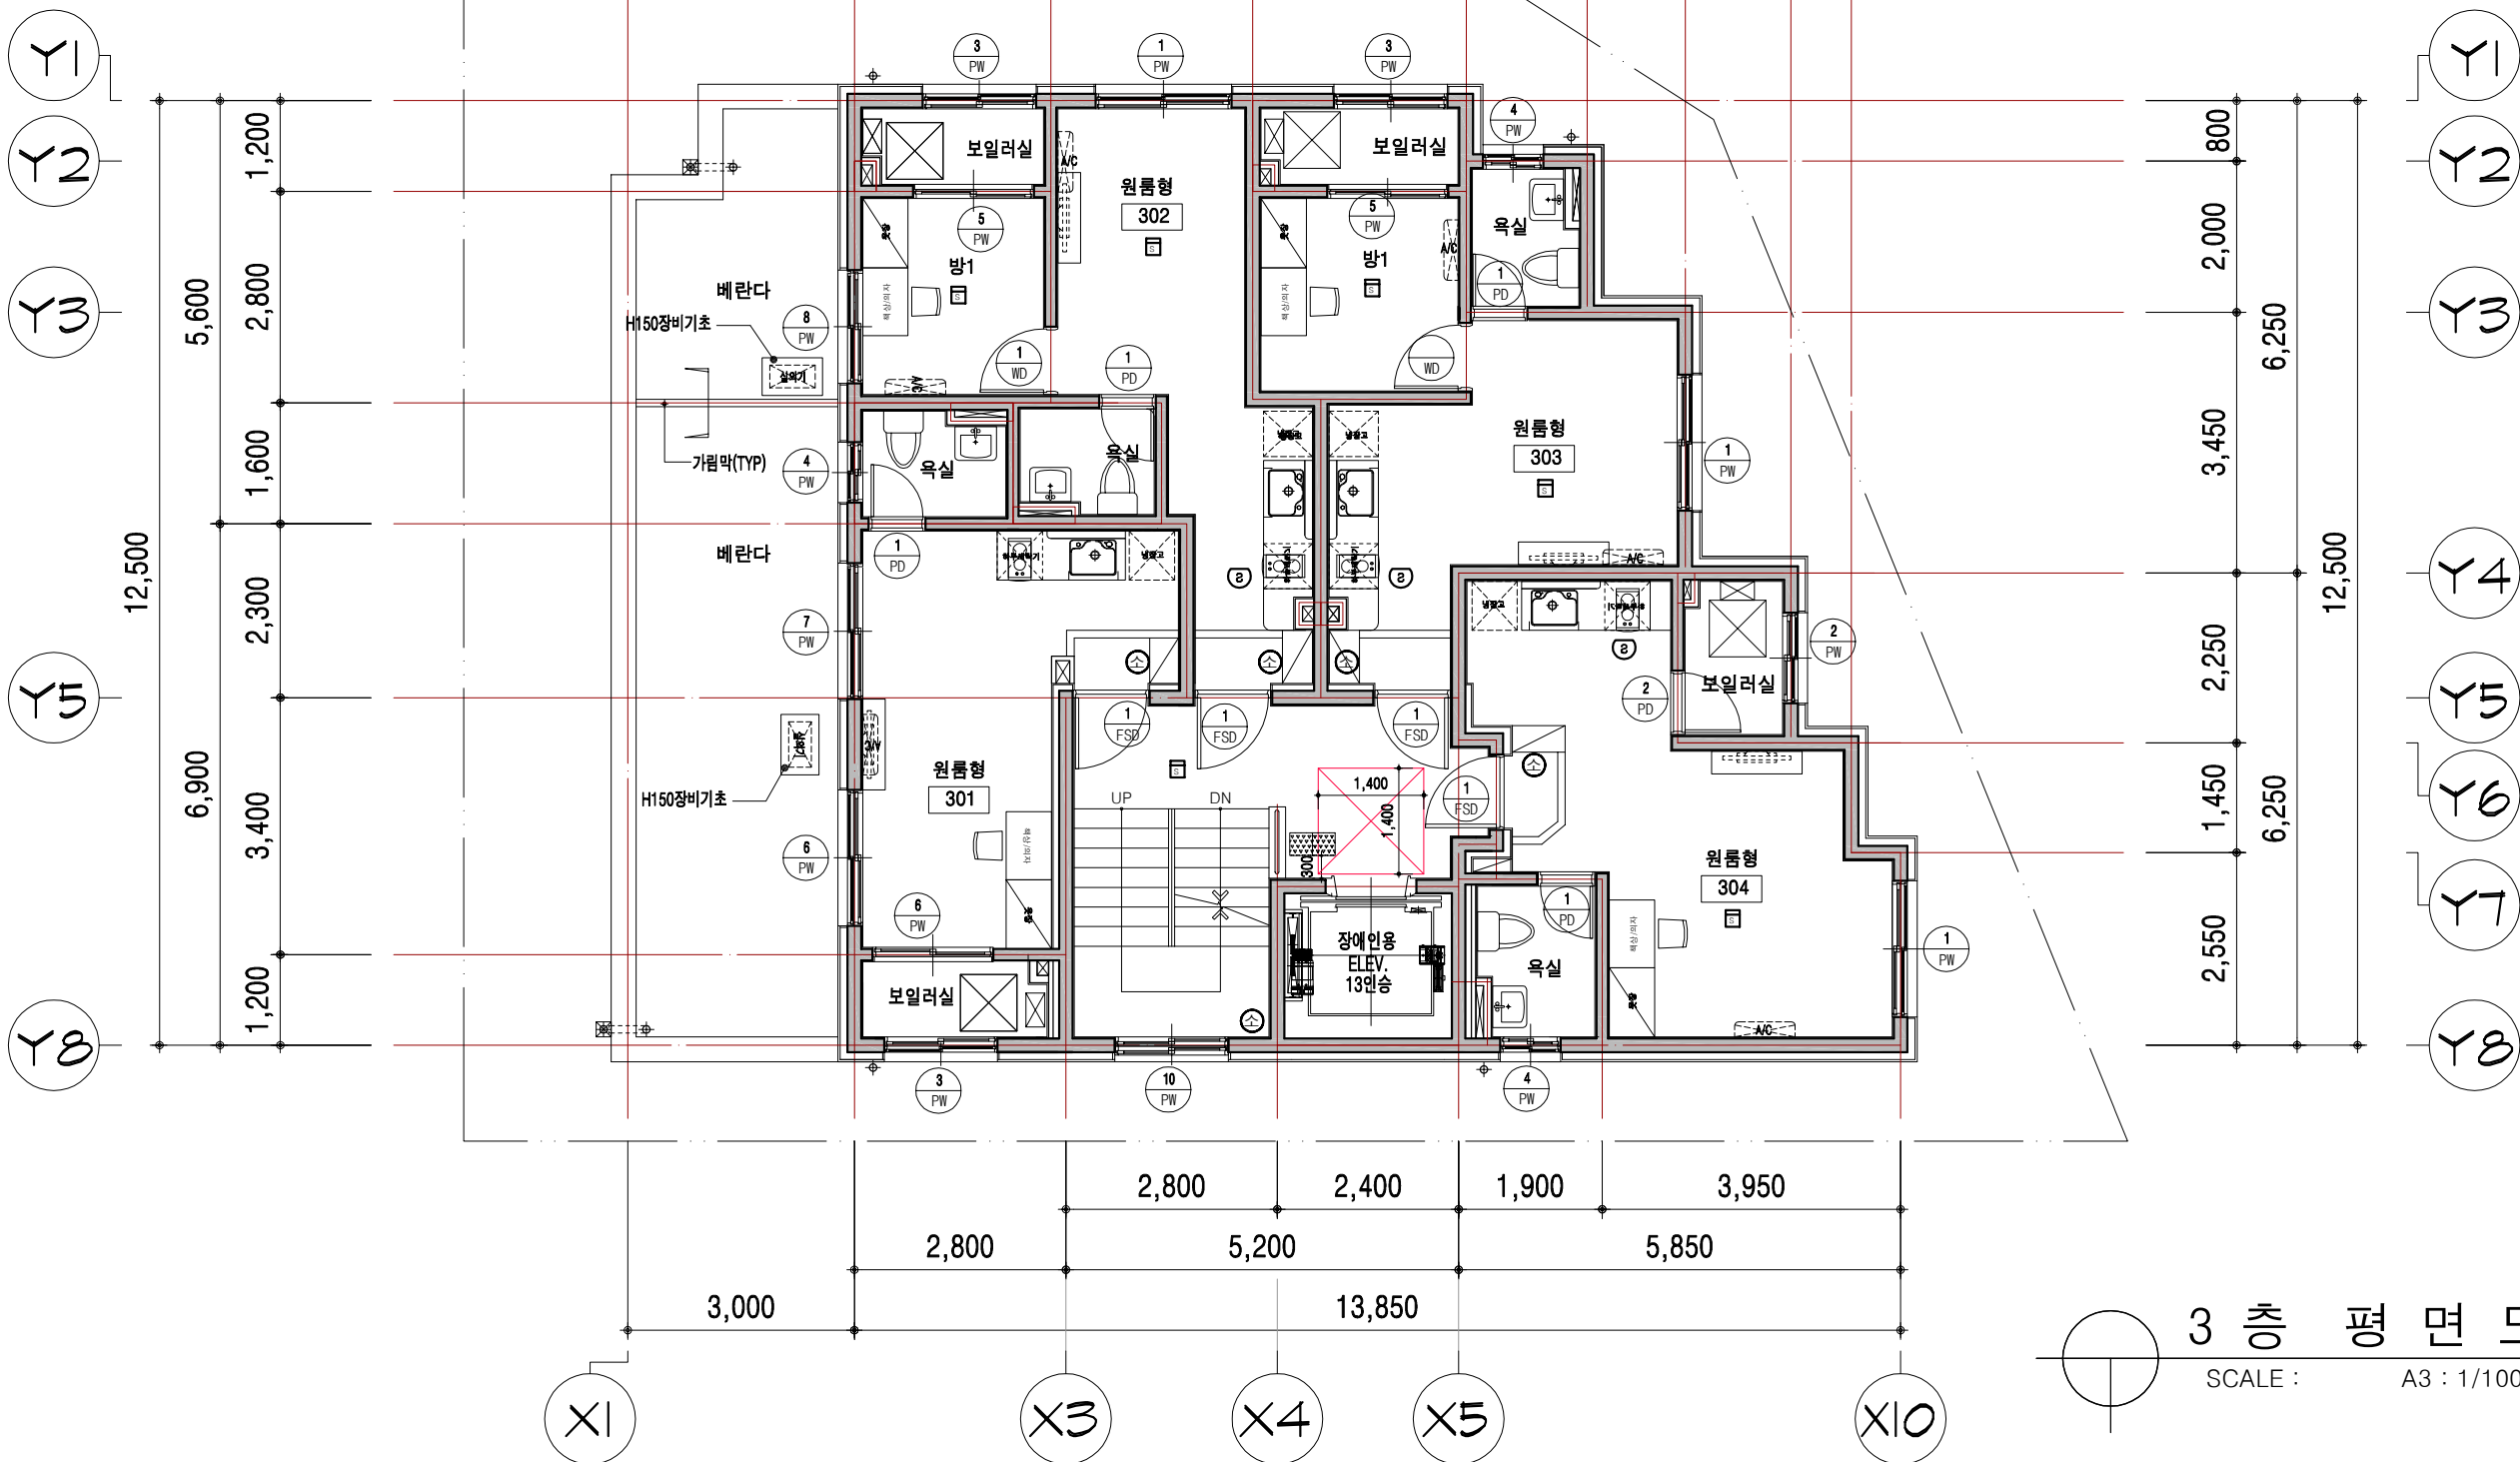
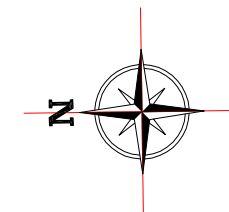
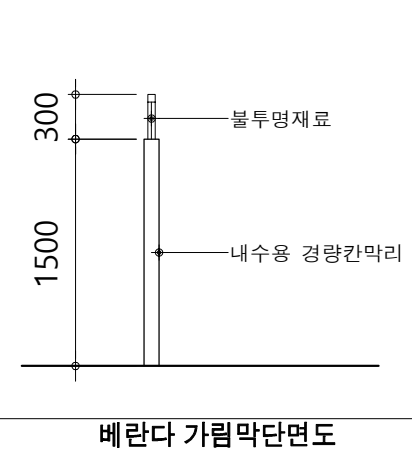


3 층 평면도
SCALE : A3 : 1/100

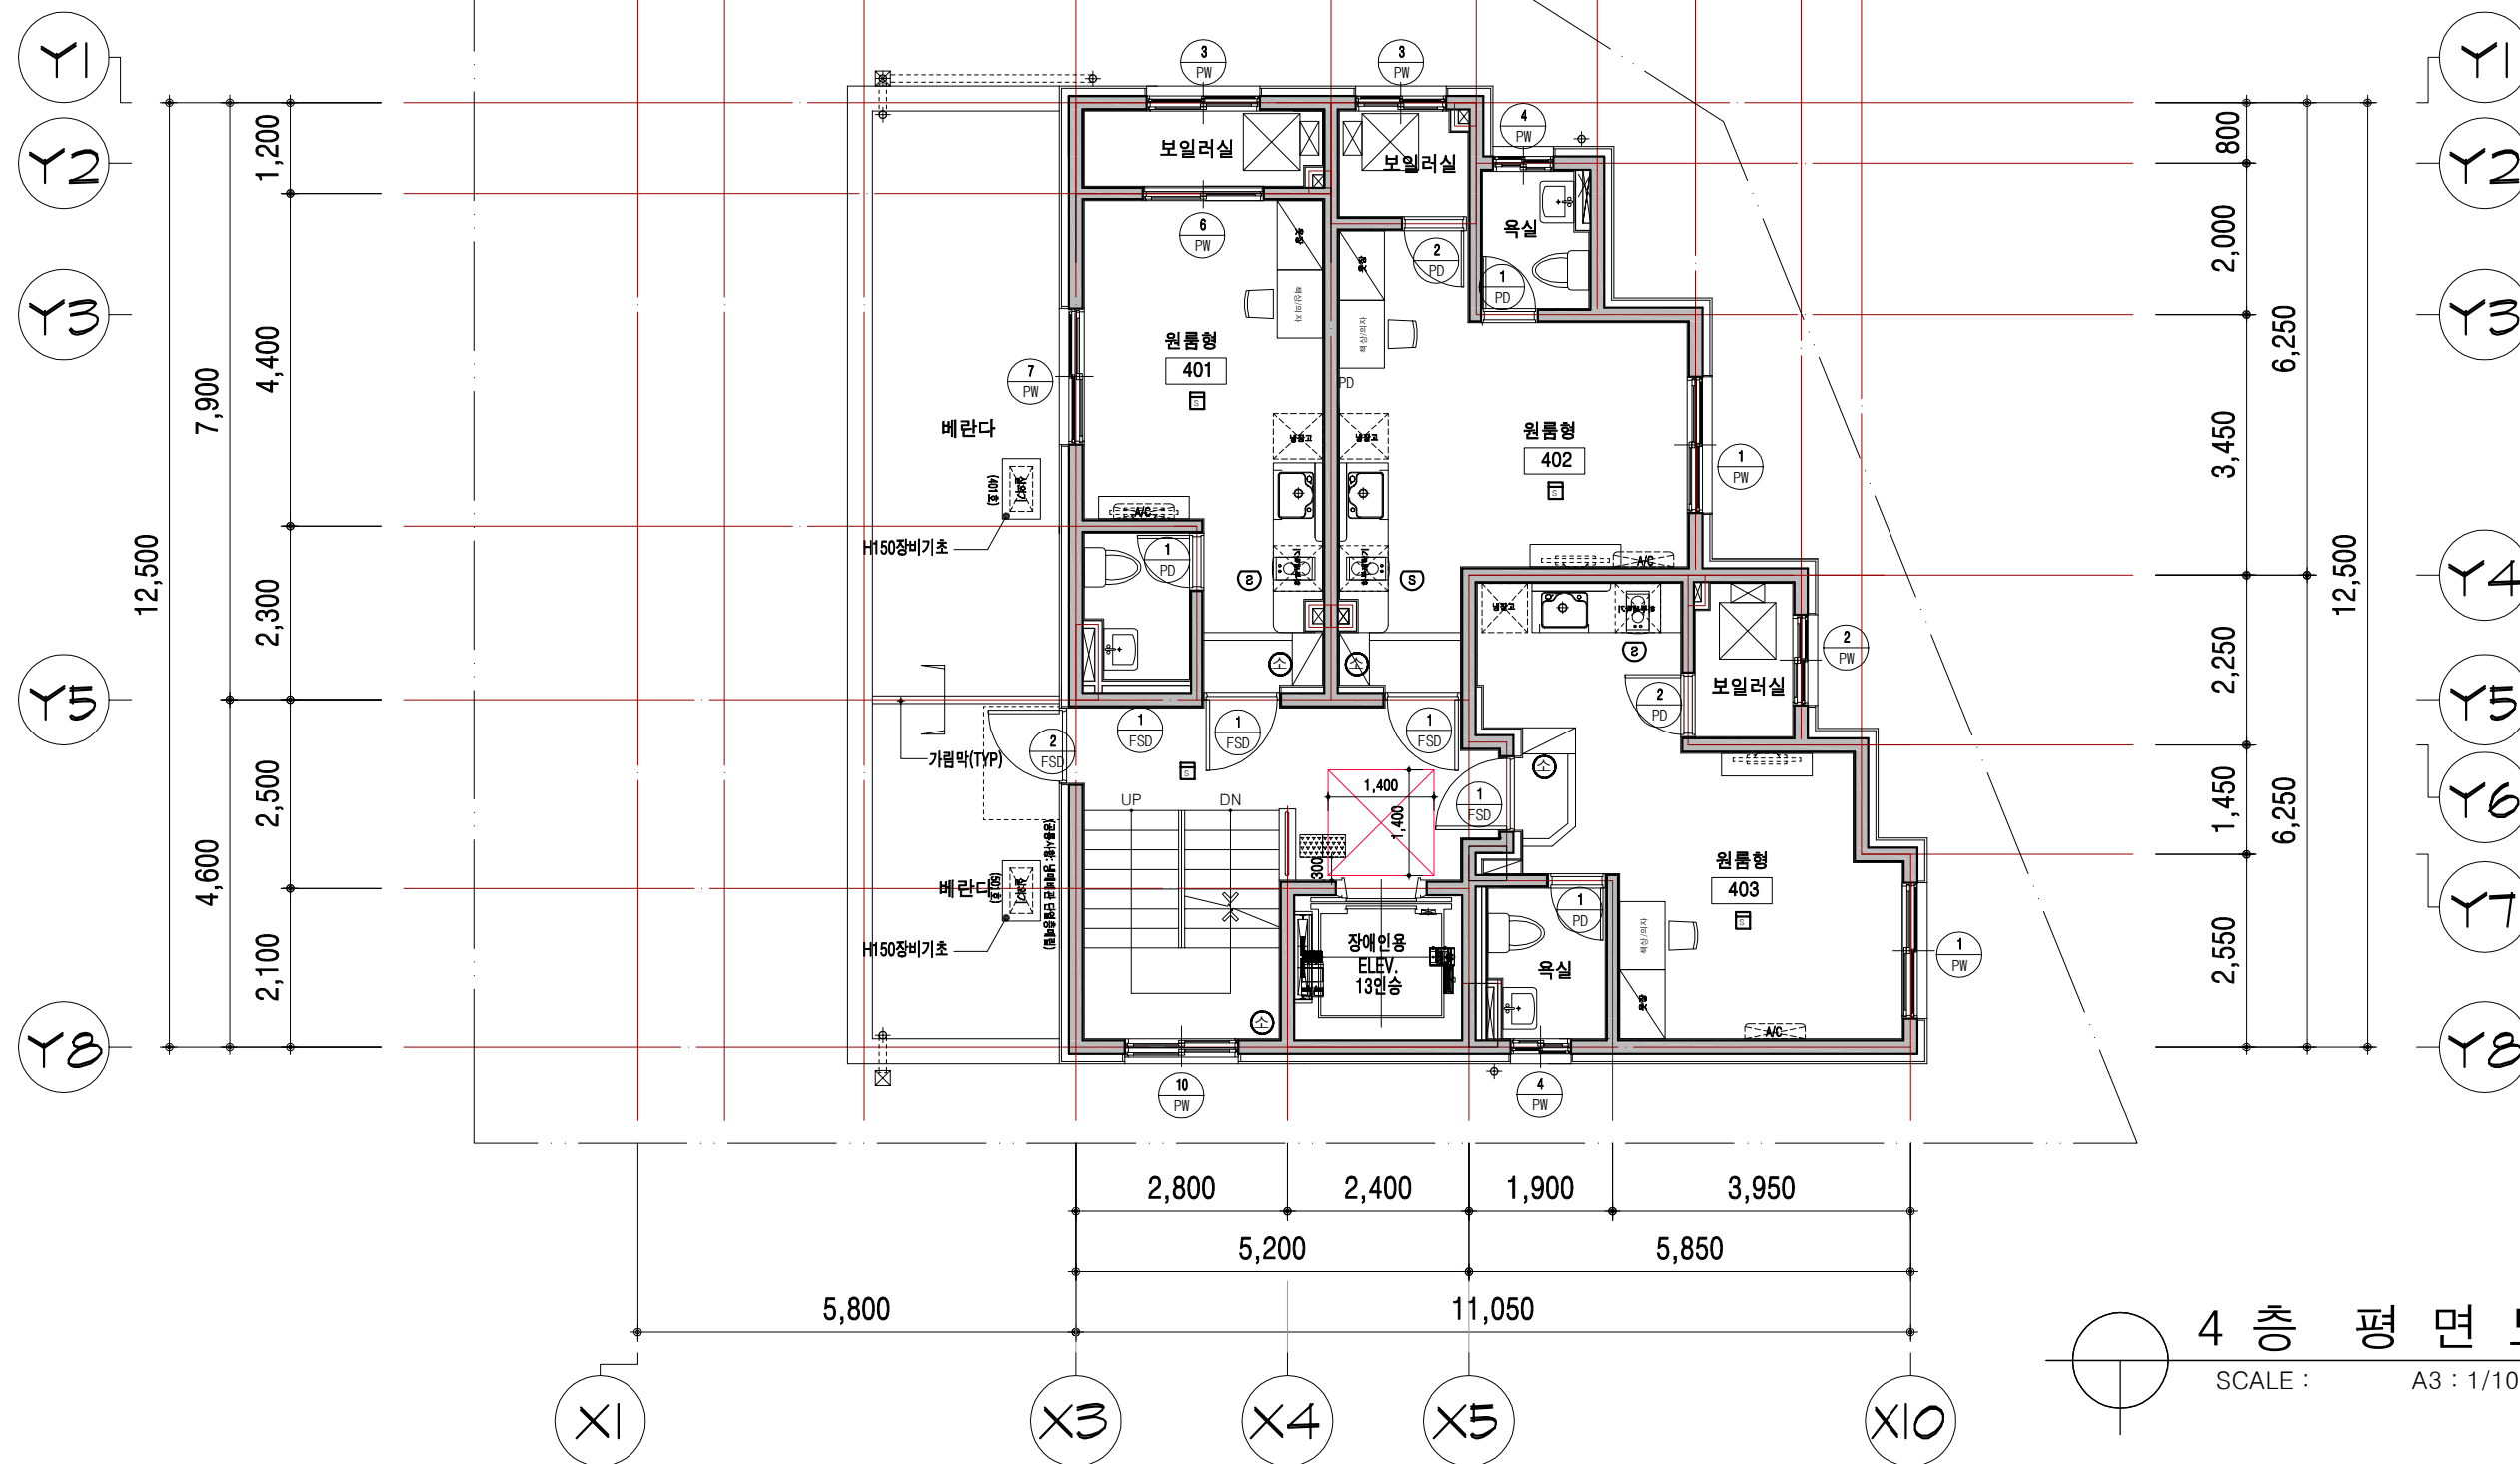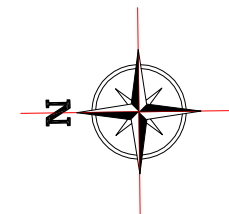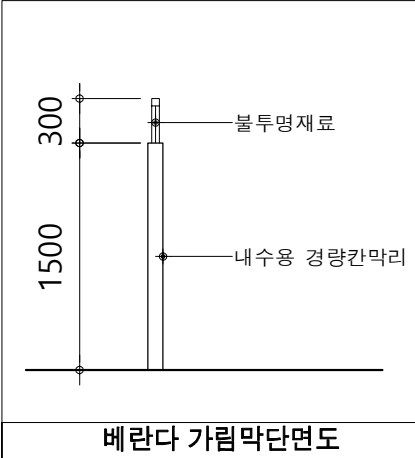

4 층 평 면 도
SCALE : A3 : 1/100

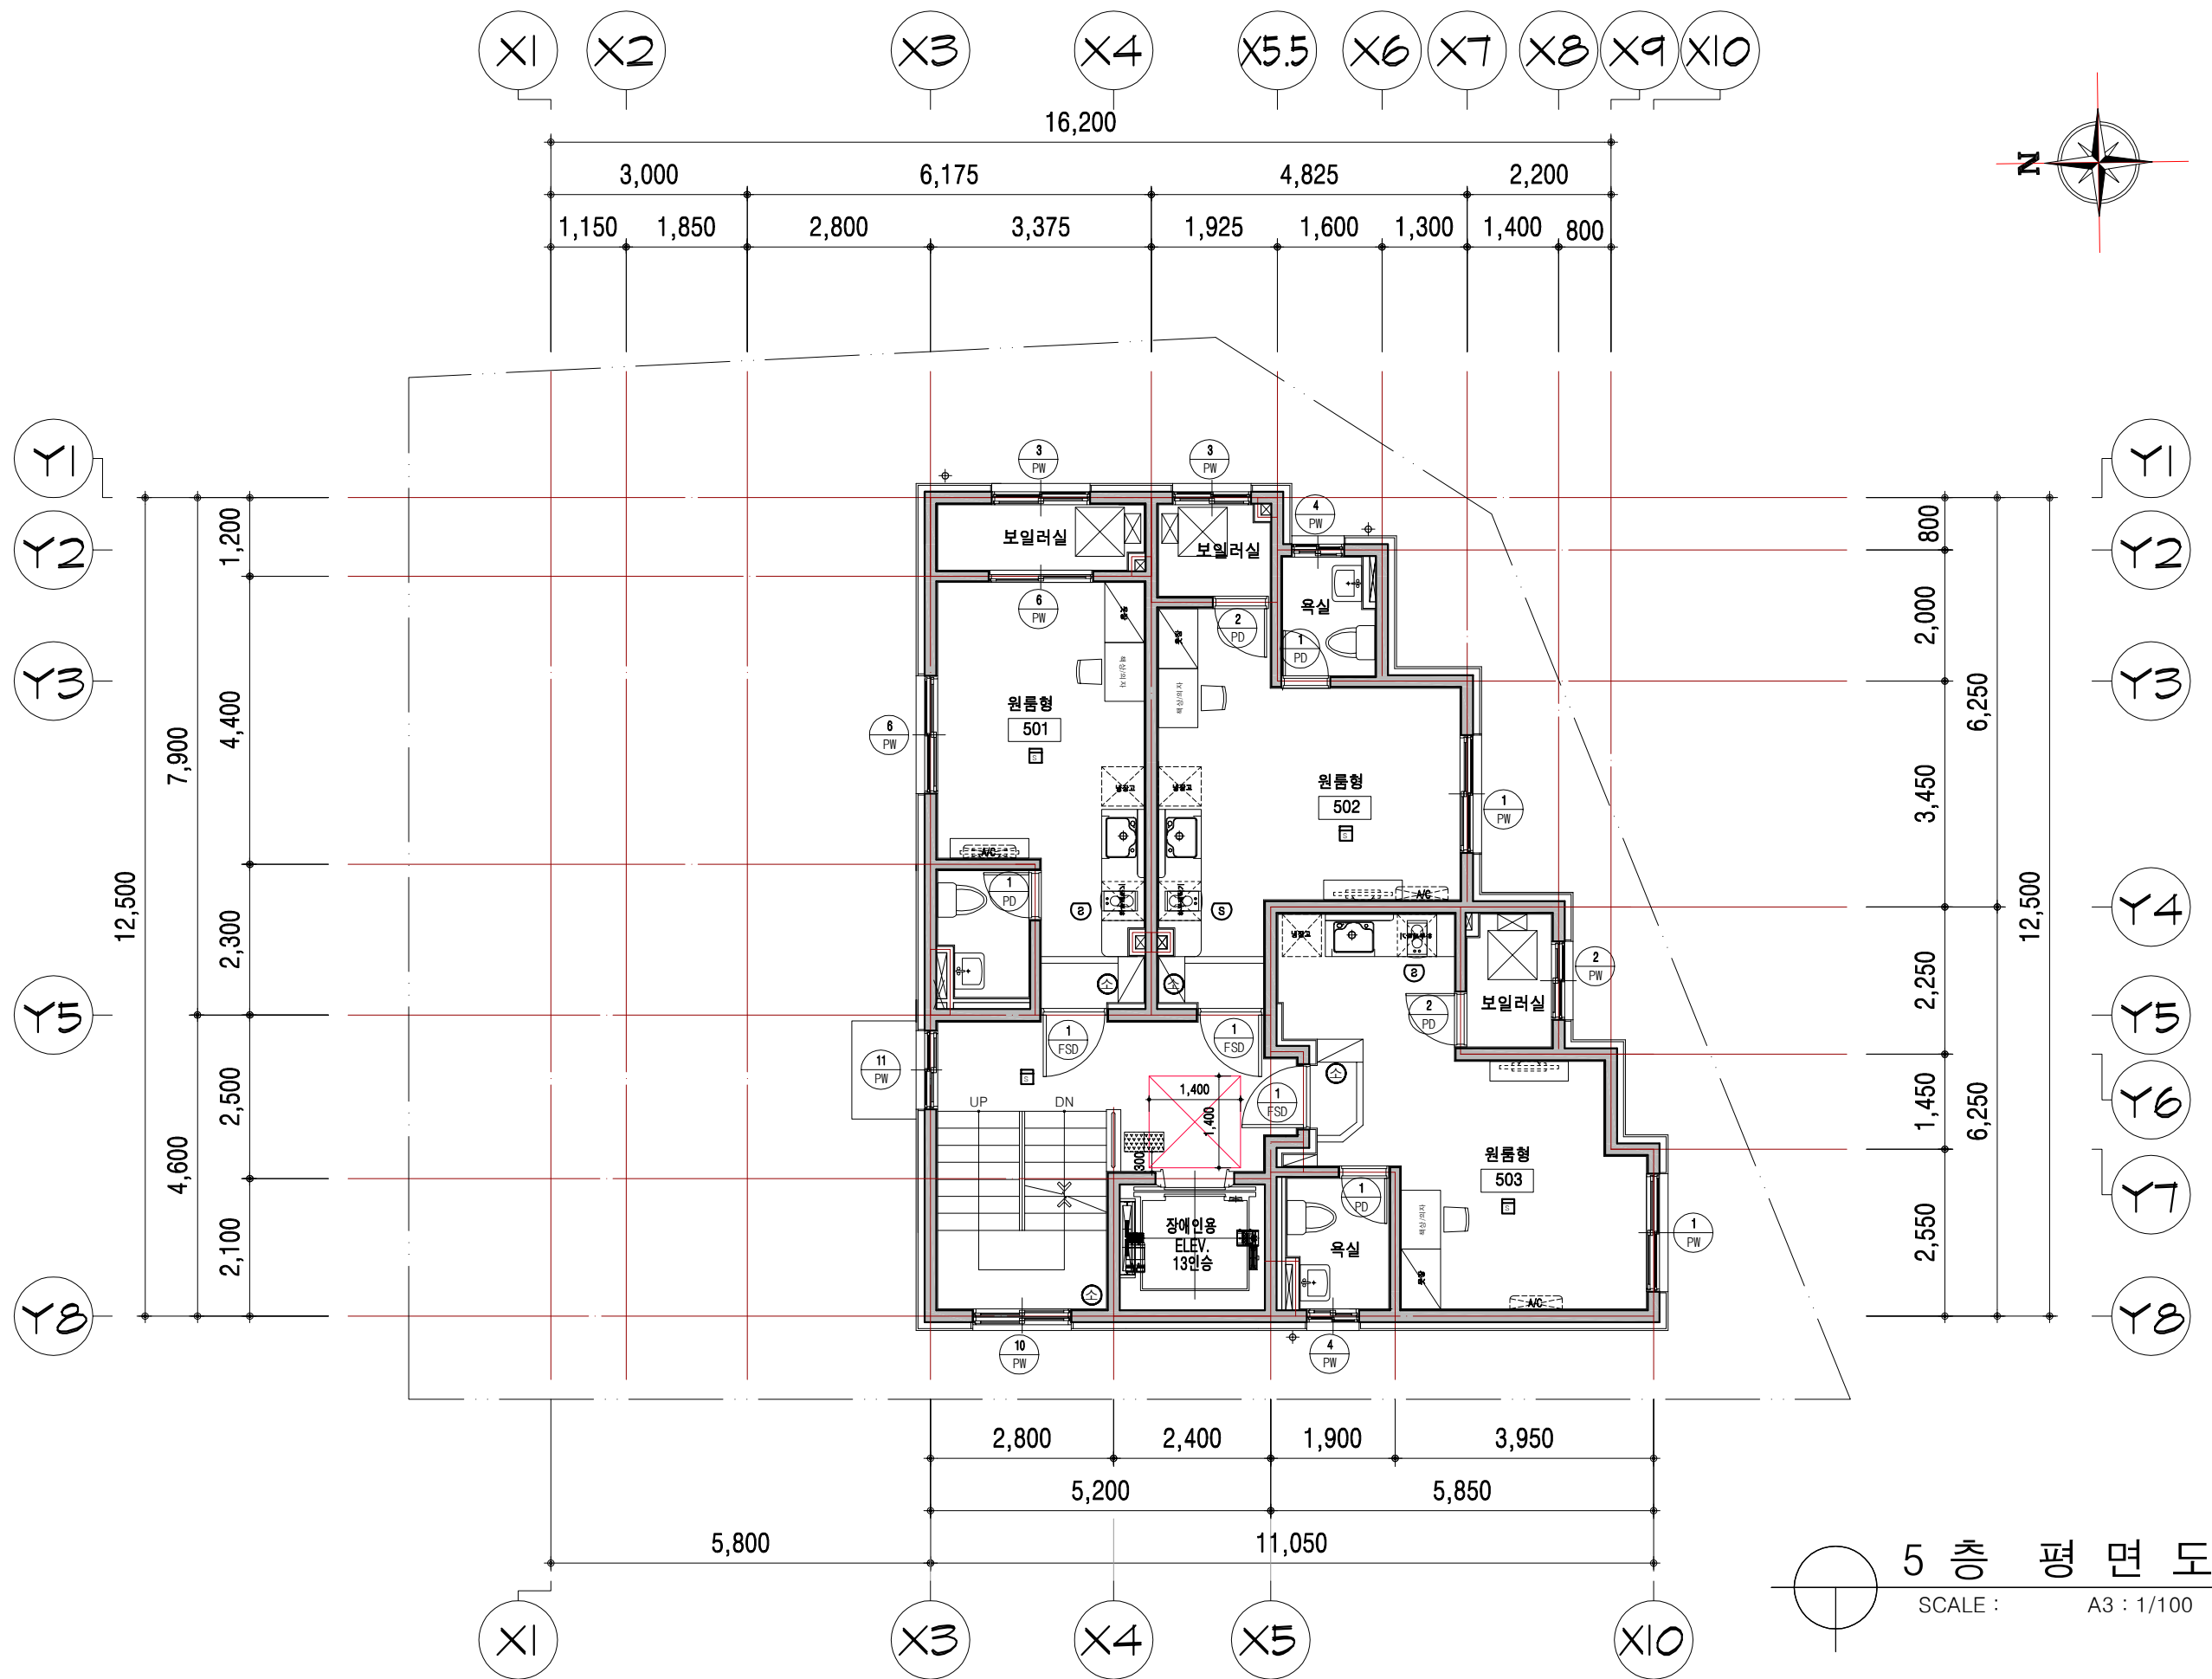


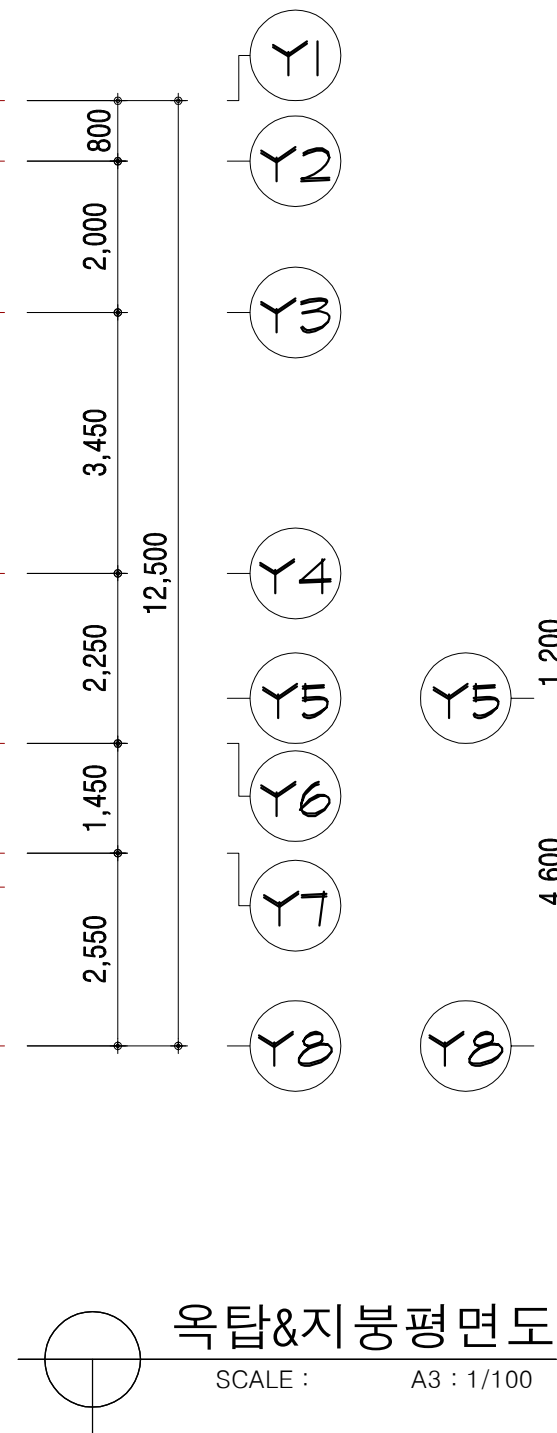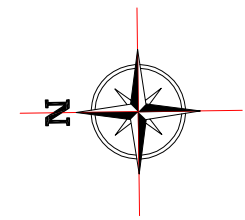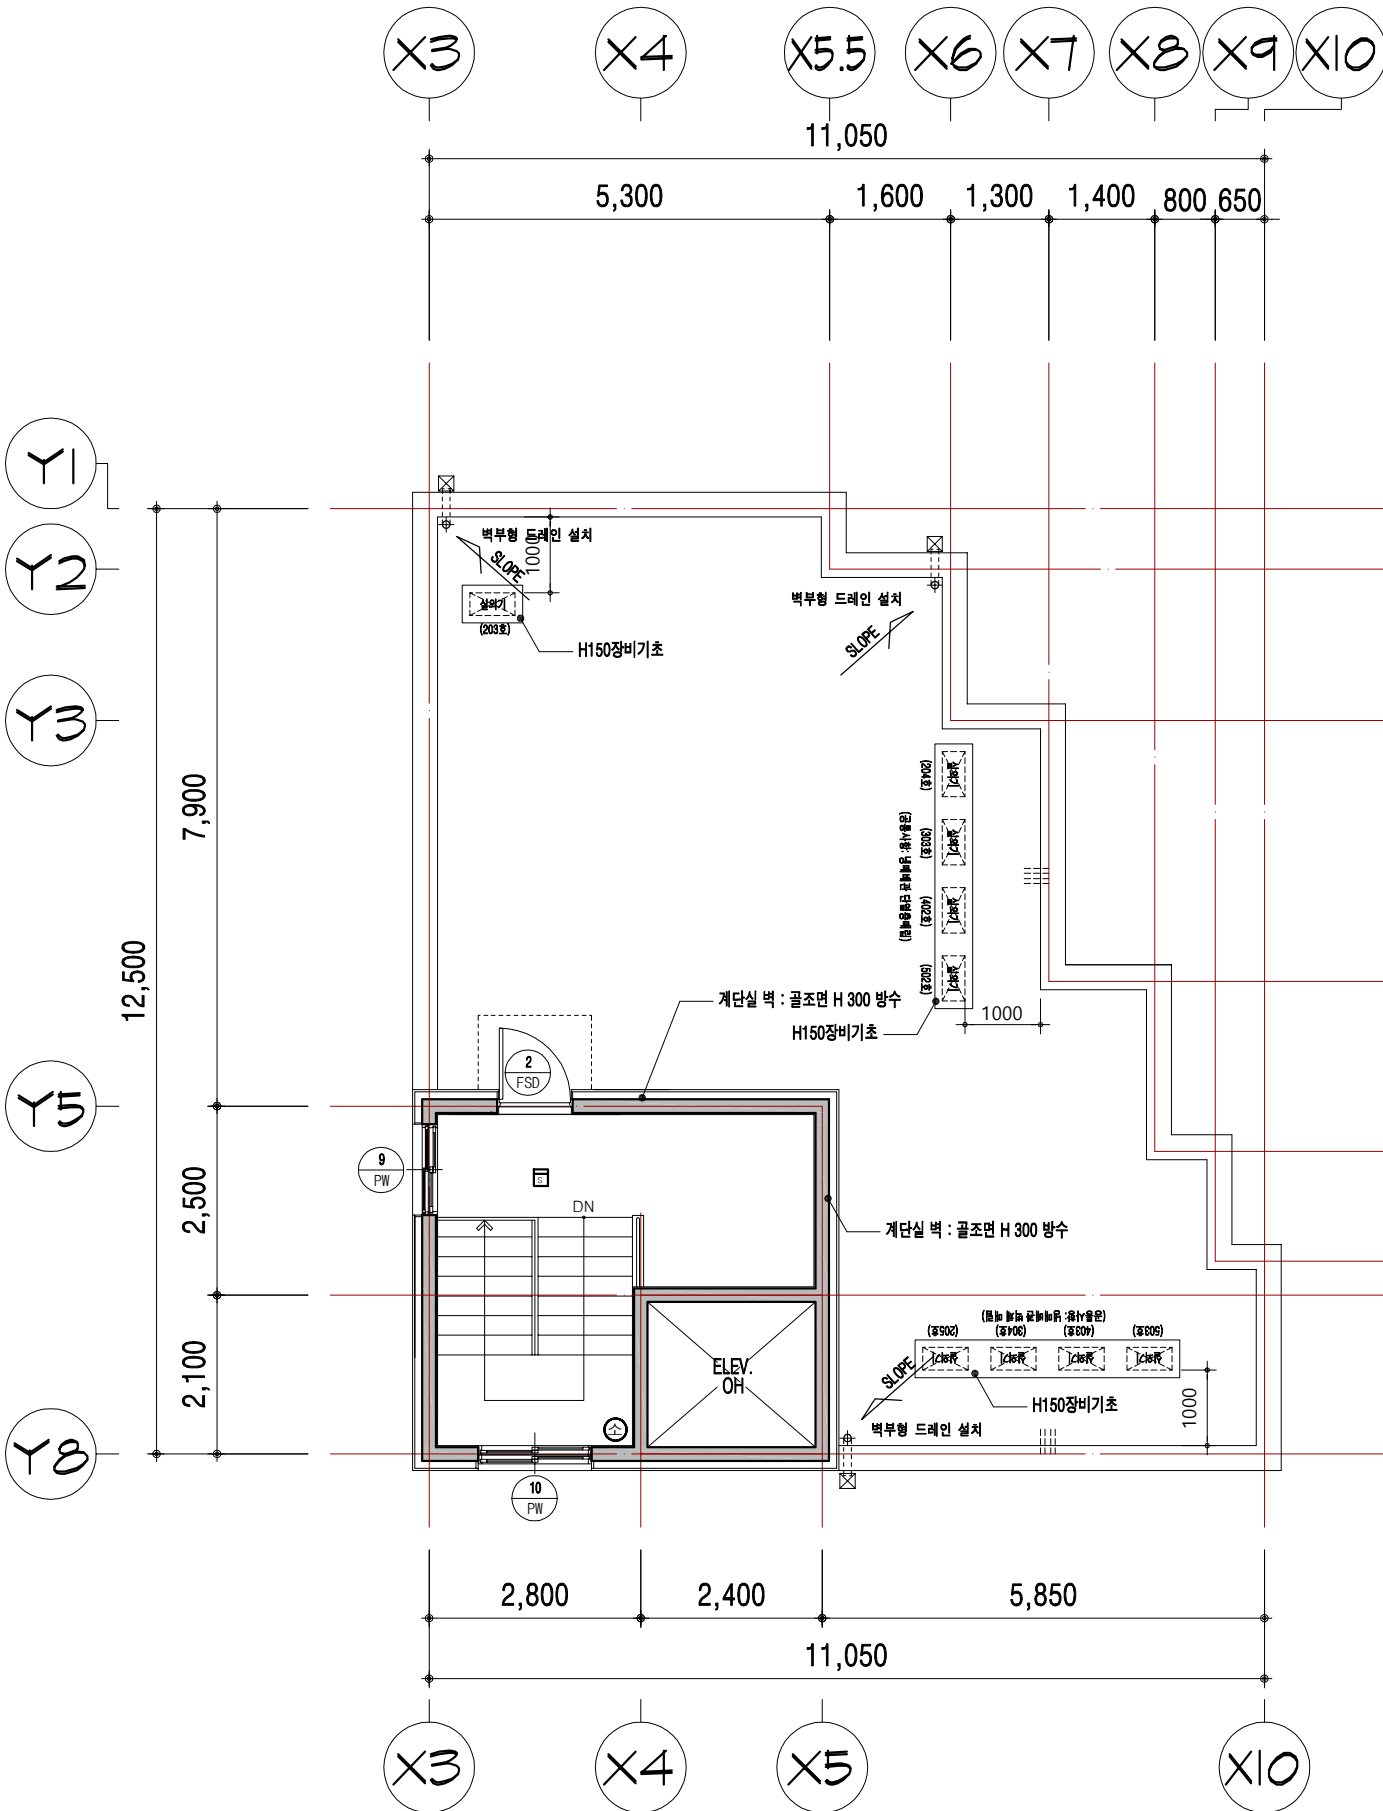

옥탑&지붕평면도

SCALE : A3 : 1/100



* 외부면 노출 창호프레임 칼라
색상번호 : H-80300 동등 칼라 (도료용 표준색 견본)

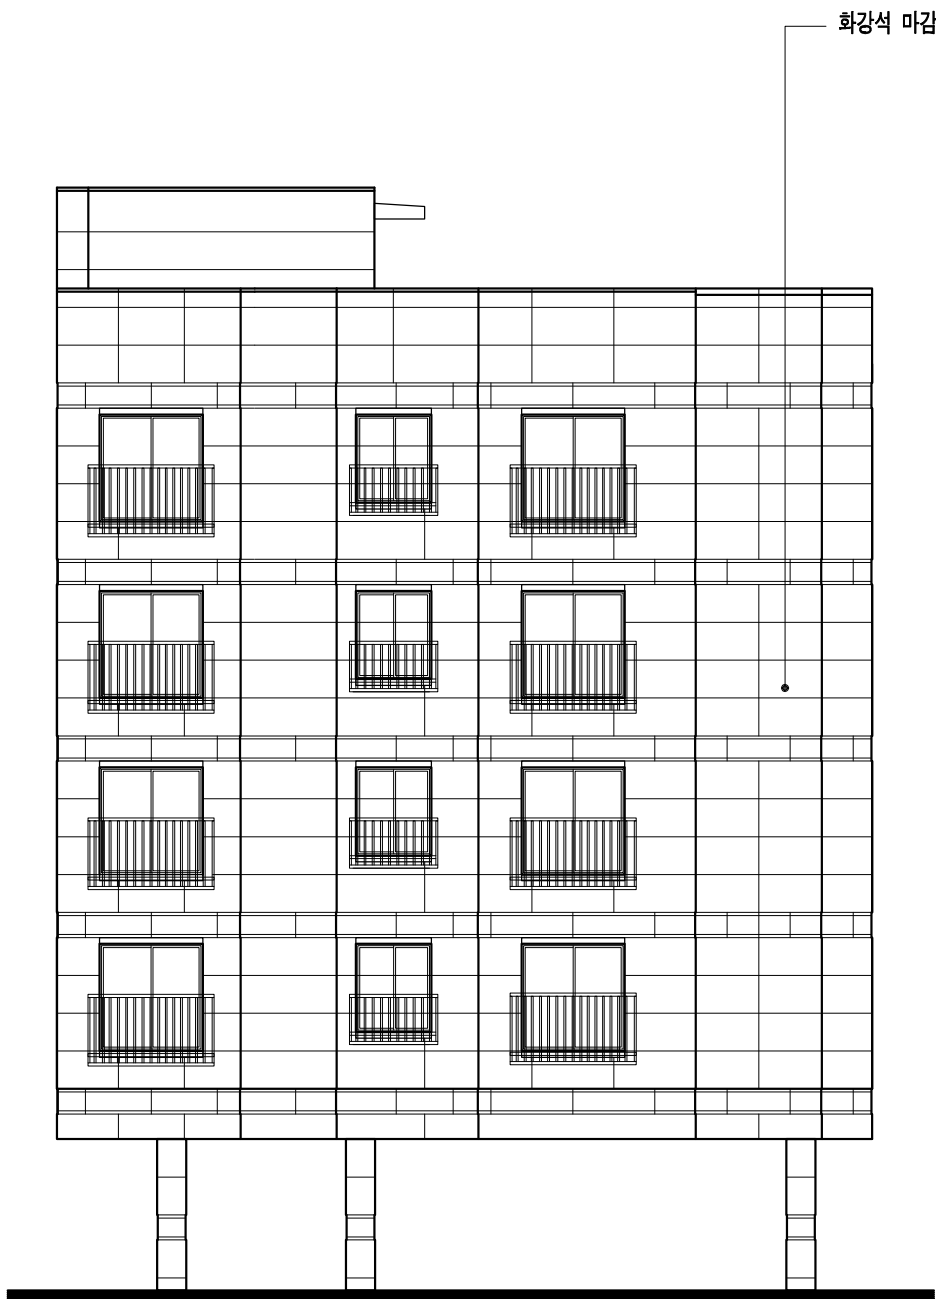

▽ 옥상지붕 바닥
▽ 5층 바닥
▽ 4층 바닥
▽ 3층 바닥
▽ 2층 바닥
▽ 1층 바닥




정 면 도
SCALE : A3 : 1/120

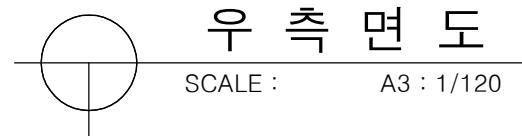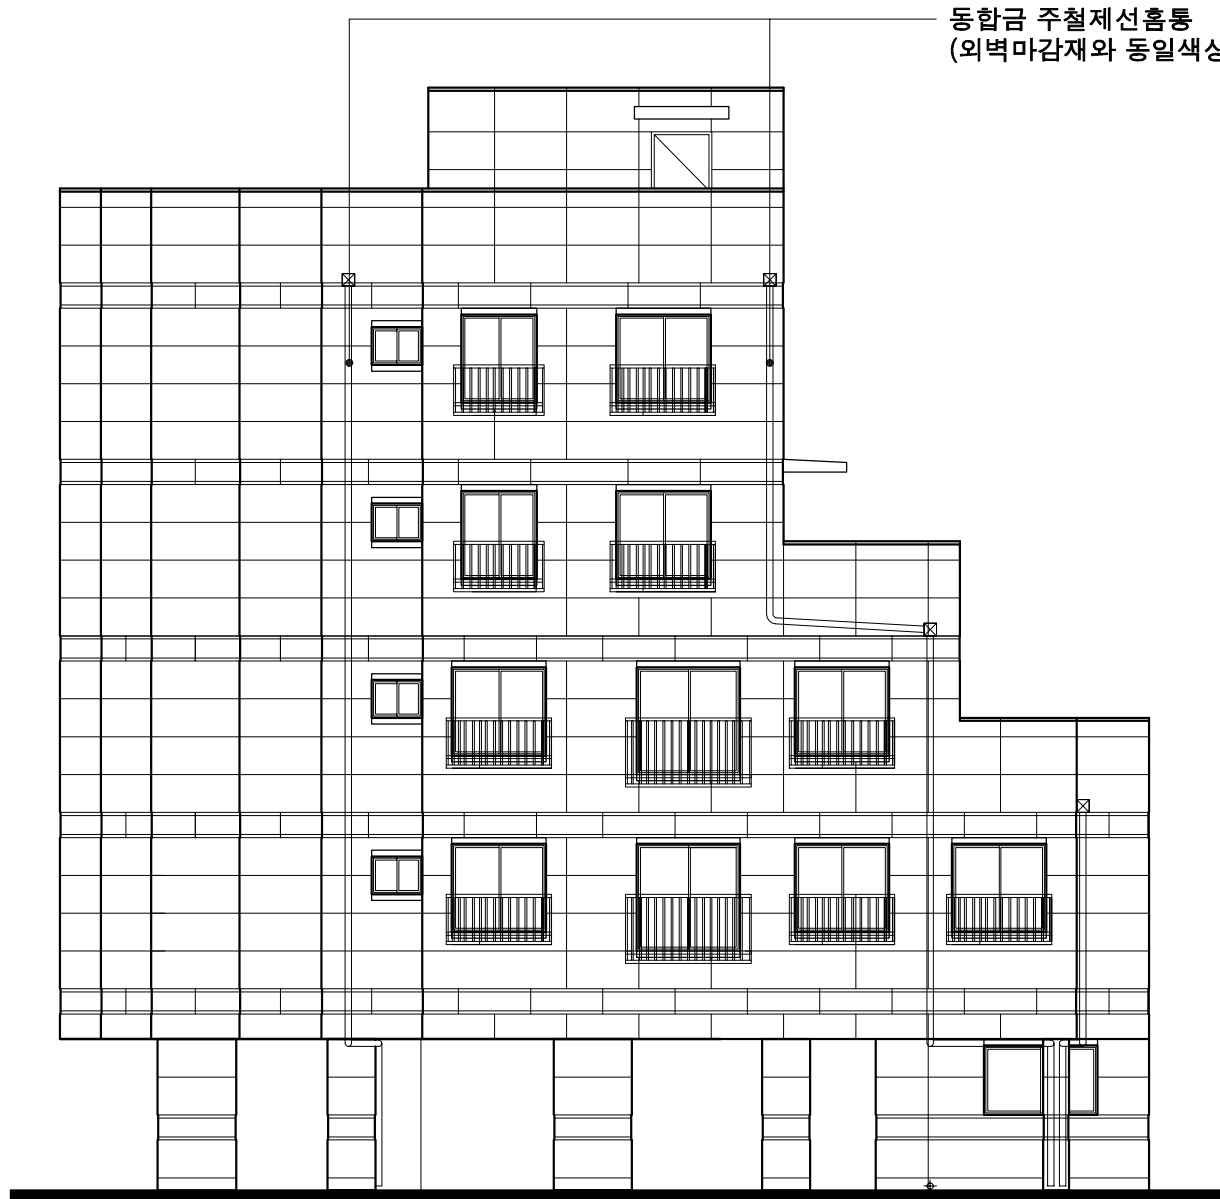

우 측 면 도
SCALE : A3 : 1/120

* 외부면 노출 창호프레임 칼라
색상번호 : H-80300 동등 칼라 (도료용 표준색 견본)

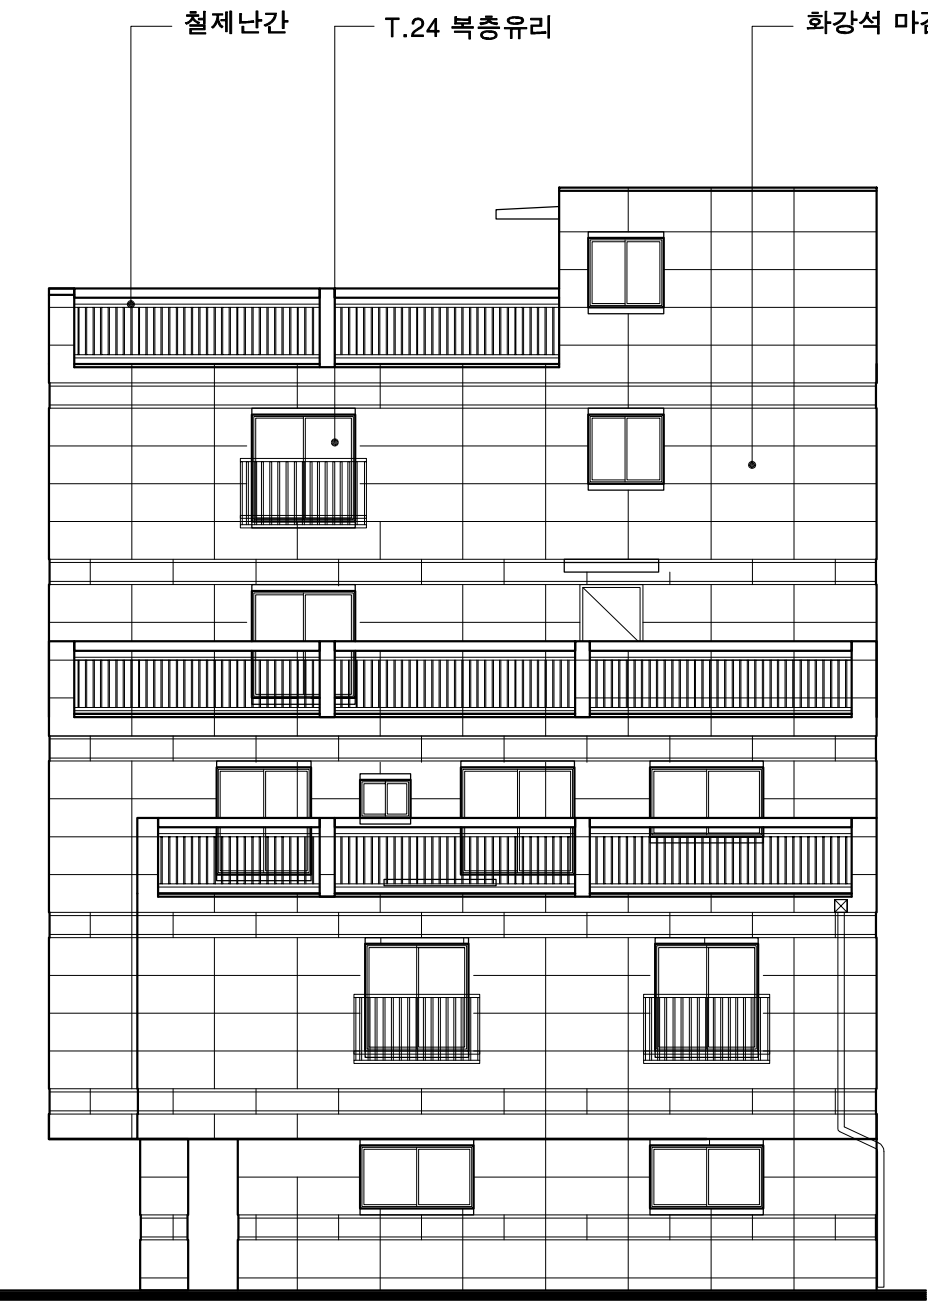

▽ 옥상지붕 바닥

▽ 5층 바닥

▽ 4층 바닥

▽ 3층 바닥


▽ 2층 바닥

▽ 1층 바닥



배 면 도

SCALE : A3 : 1/120

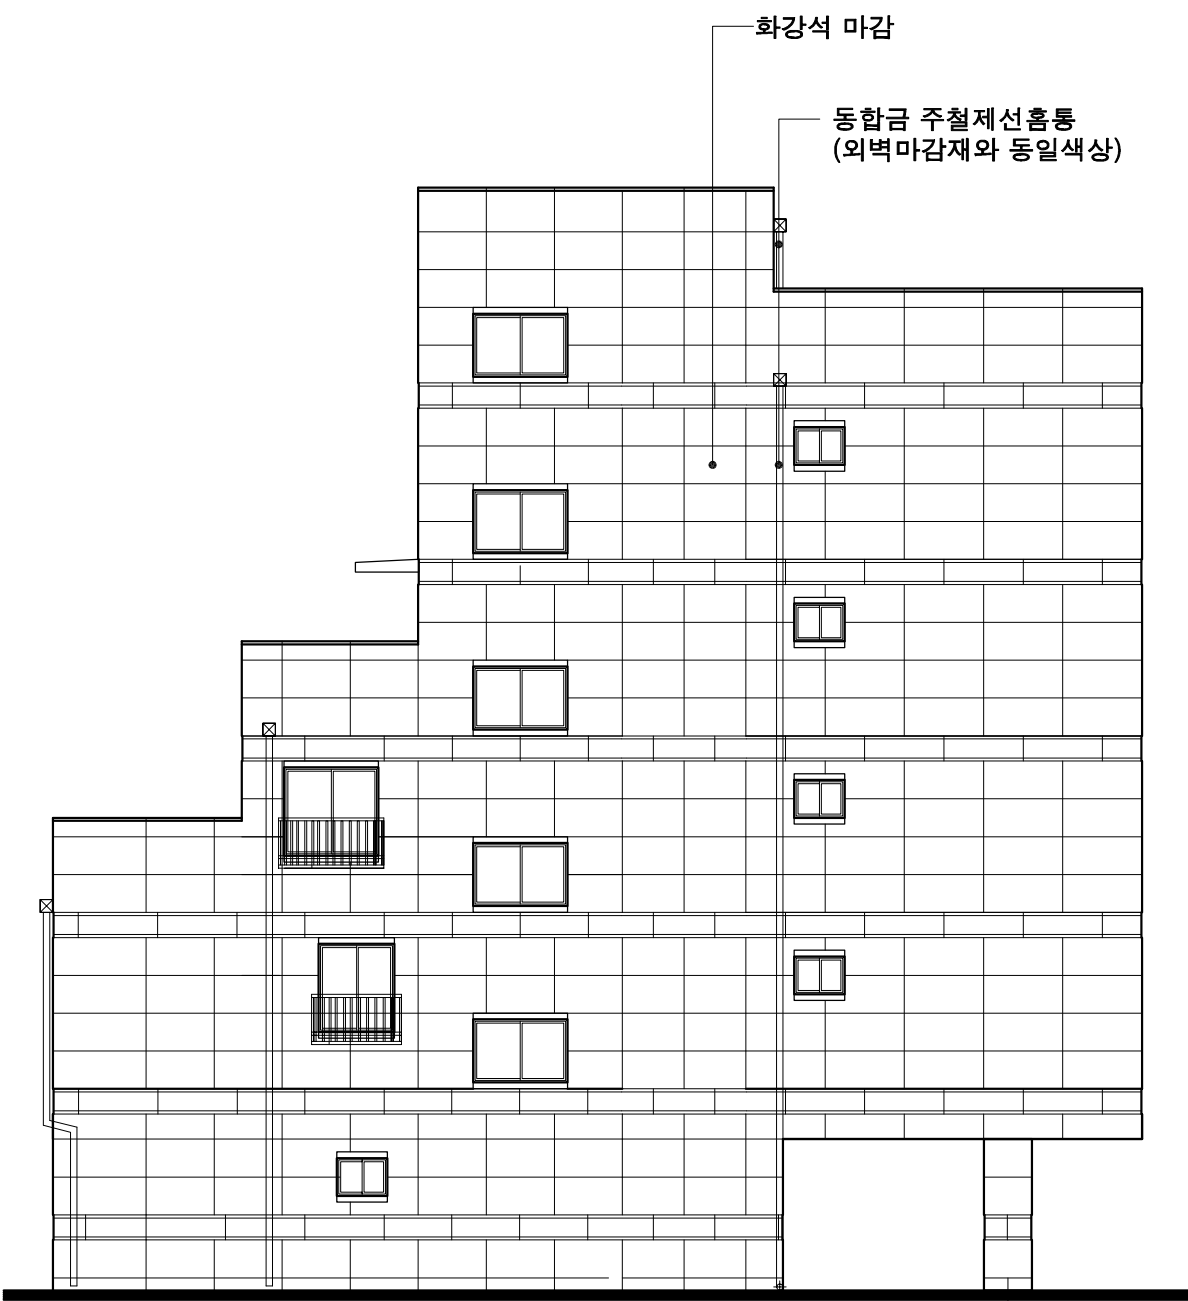

좌 측 면 도

SCALE : A3 : 1/120