


NOTE




	DATE 일자	REV DESCRIPTION 변경 내용	DRW 담당	CHE 검토	APP 승인				
APPROVED BY 승인									
CHECKED BY 검토									
DRAWN BY 제도									
DATE 일자		2020.02.							
PROJECT NAME 사업명									
반포동 726-40번지 도시형생활주택(원룸형) 신축공사									
DRAWING TITLE 도면명									
1층 평면도									
SCALE 축척									
1 / 100									
DRAWING NO. 도면번호									
A-									

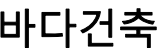



BADA ARCHITECTS & ENGINEERS
TEL:031)523-3383 FAX:031)571-3348

NOTE

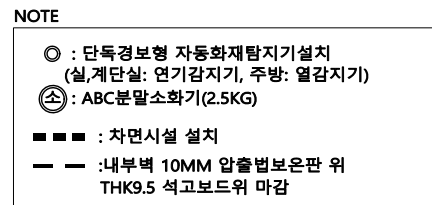

1 2층,3층 평면도
SCALE : 1/100

	DATE 일자	REV DESCRIPTION 변경 내용	DRW 담당	CHE 검토	APP 승인		
APPROVED BY 승인							
CHECKED BY 검토							
DRAWN BY 제도							
DATE 일자		2020.02.					
PROJECT NAME 사업명							
반포동 726-40번지 도시형생활주택(원룸형) 신축공사							
DRAWING TITLE 도면명							
2층,3층 평면도							
SCALE 축척							
1 / 100							
DRAWING NO. 도면번호							
A-							

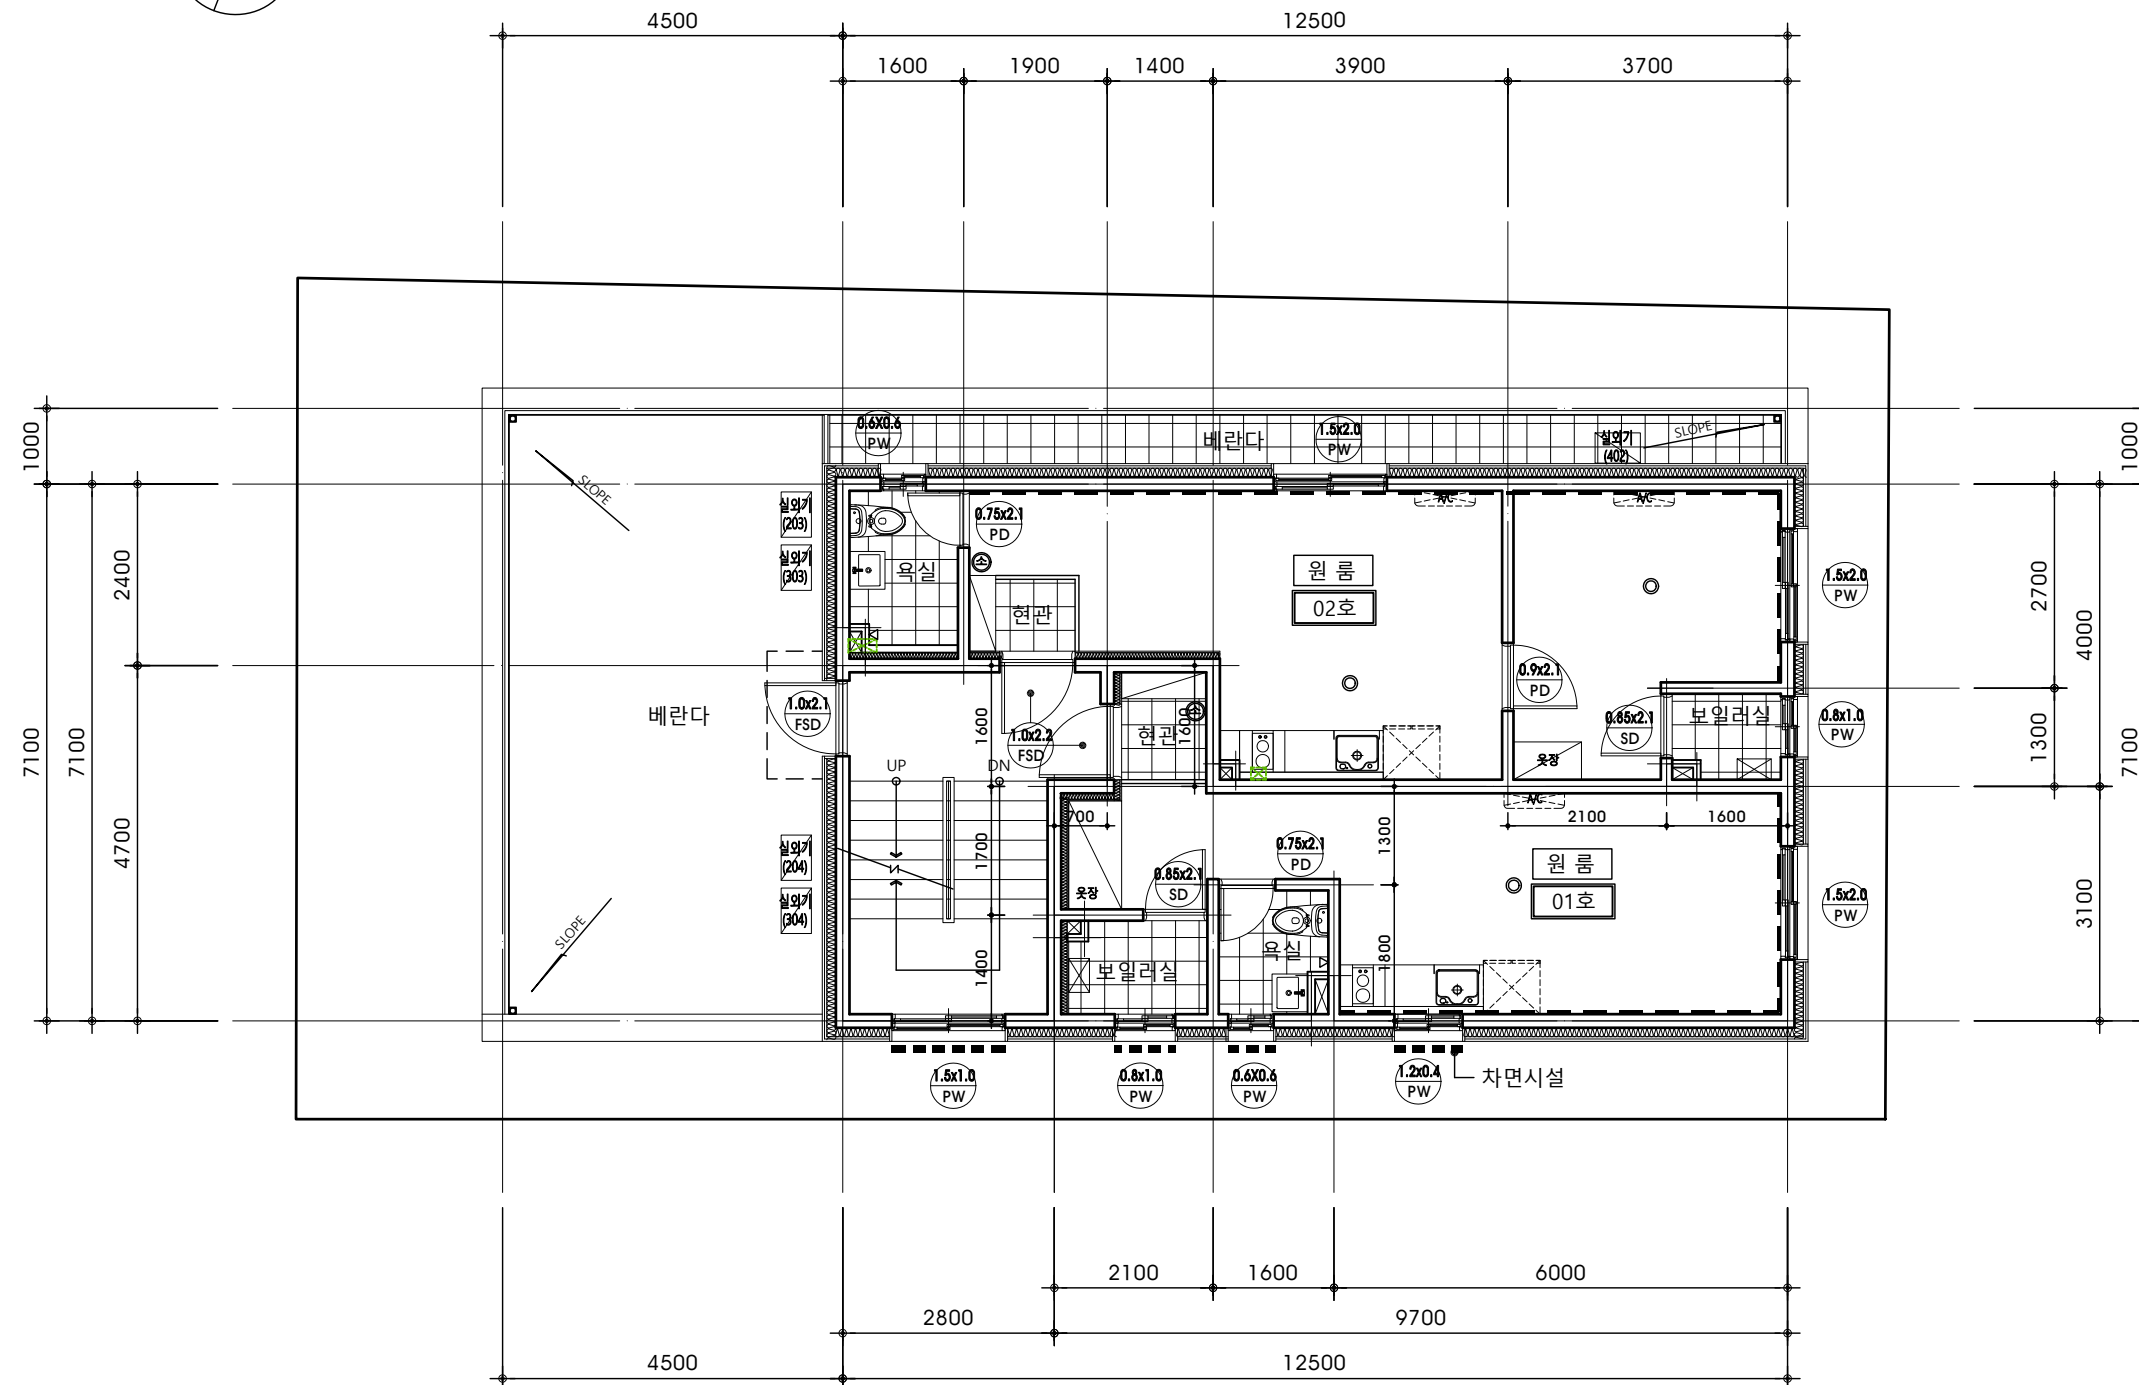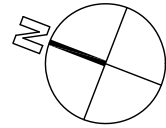

NOTE

- : 단독경보형 자동화재탐지기설치
(실,계단실: 연기감지기, 주방: 열감지기)
- ⊕ : ABC분말소화기(2.5KG)
- ■ ■ : 차면시설 설치
- : 내부벽 10MM 압출법보온판 위
THK9.5 석고보드위 마감

1

4층 평면도

SCALE : 1/100



바다건축

BADA ARCHITECTS & ENGINEERS
TEL:031)523-3383 FAX:031)571-3348

NOTE

DATE	REV	DESCRIPTION	DRW	CHE	APP
일자	변경	내용	담당	검토	승인

APPROVED BY
승인

CHECKED BY
검토

DRAWN BY
제도


DATE
일자 2020.02.

PROJECT NAME
사업명
반포동 726-40번지
도시형생활주택(원룸형) 신축공사

DRAWING TITLE
도면명
4층 평면도


SCALE
축척
1 / 100

DRAWING NO.
도면번호
A-

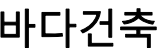

BADA ARCHITECTS & ENGINEERS
TEL:031)523-3383 FAX:031)571-3348

NOTE

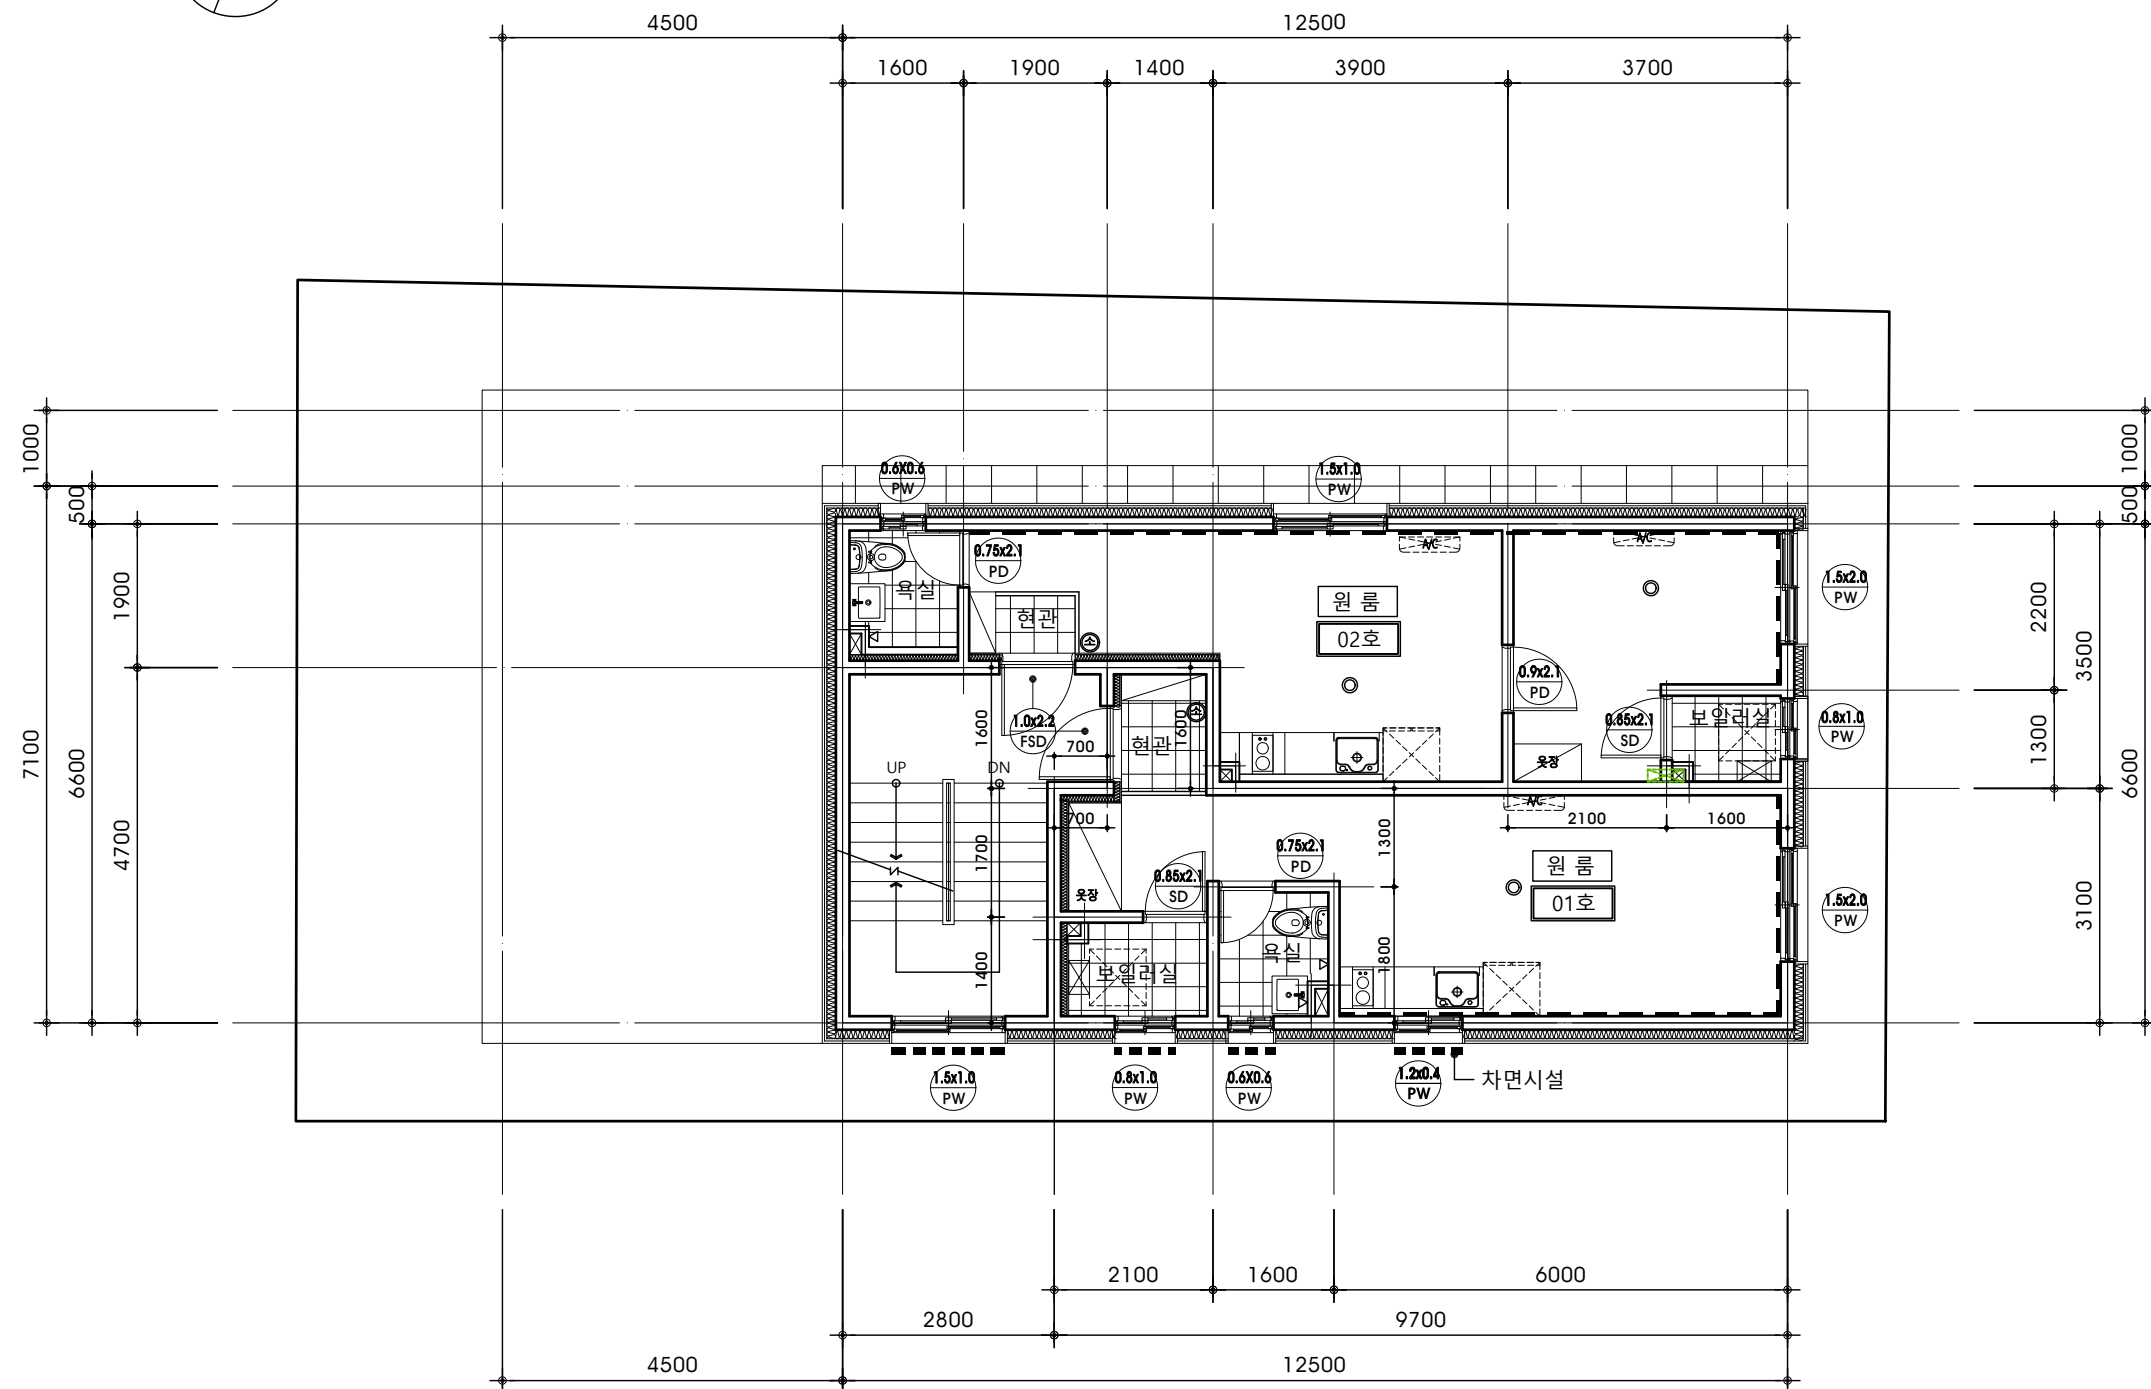

5층 평면도

SCALE : 1/100

1




1 / 100

DRAWING NO.


A-

NOTE


- : 단독경보형 자동화재탐지장치설치
(실,계단실: 연기감지기, 주방: 열감지기)
- ③ : ABC분말소화기(2.5KG)
- ■ ■ : 차면시설 설치
- — : 내부벽 10MM 압출법보온판 위
THK9.5 석고보드위 마감

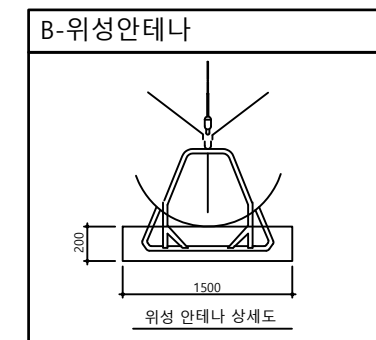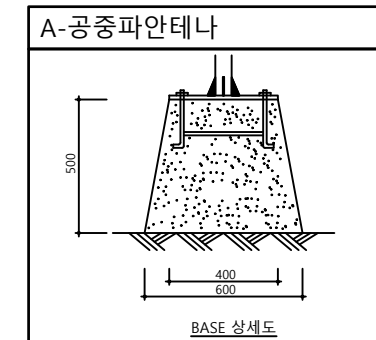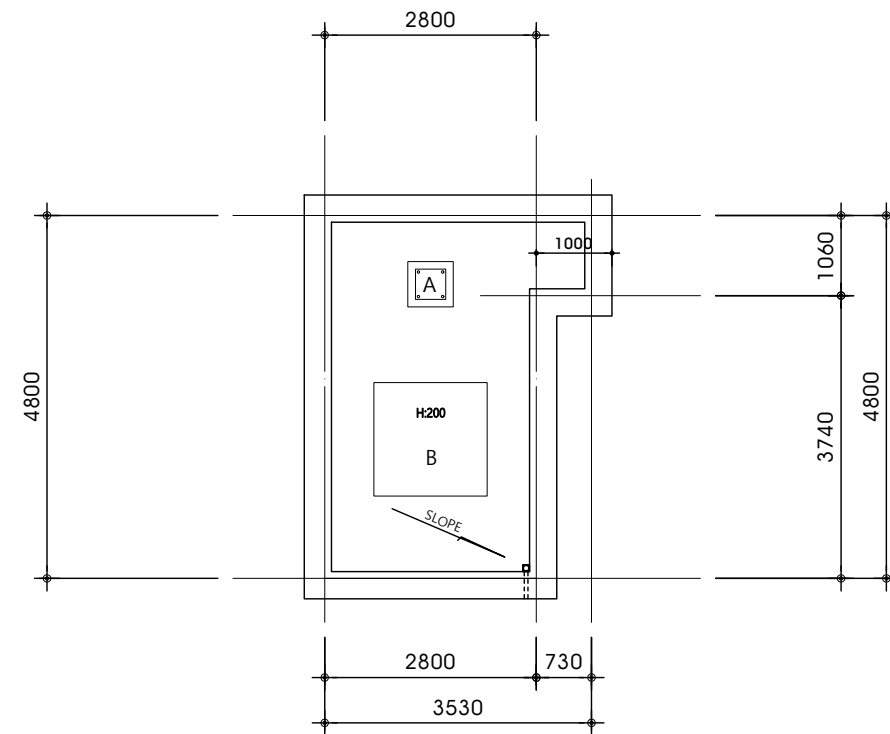

2 옥탑지붕 평면도
SCALE : 1/100

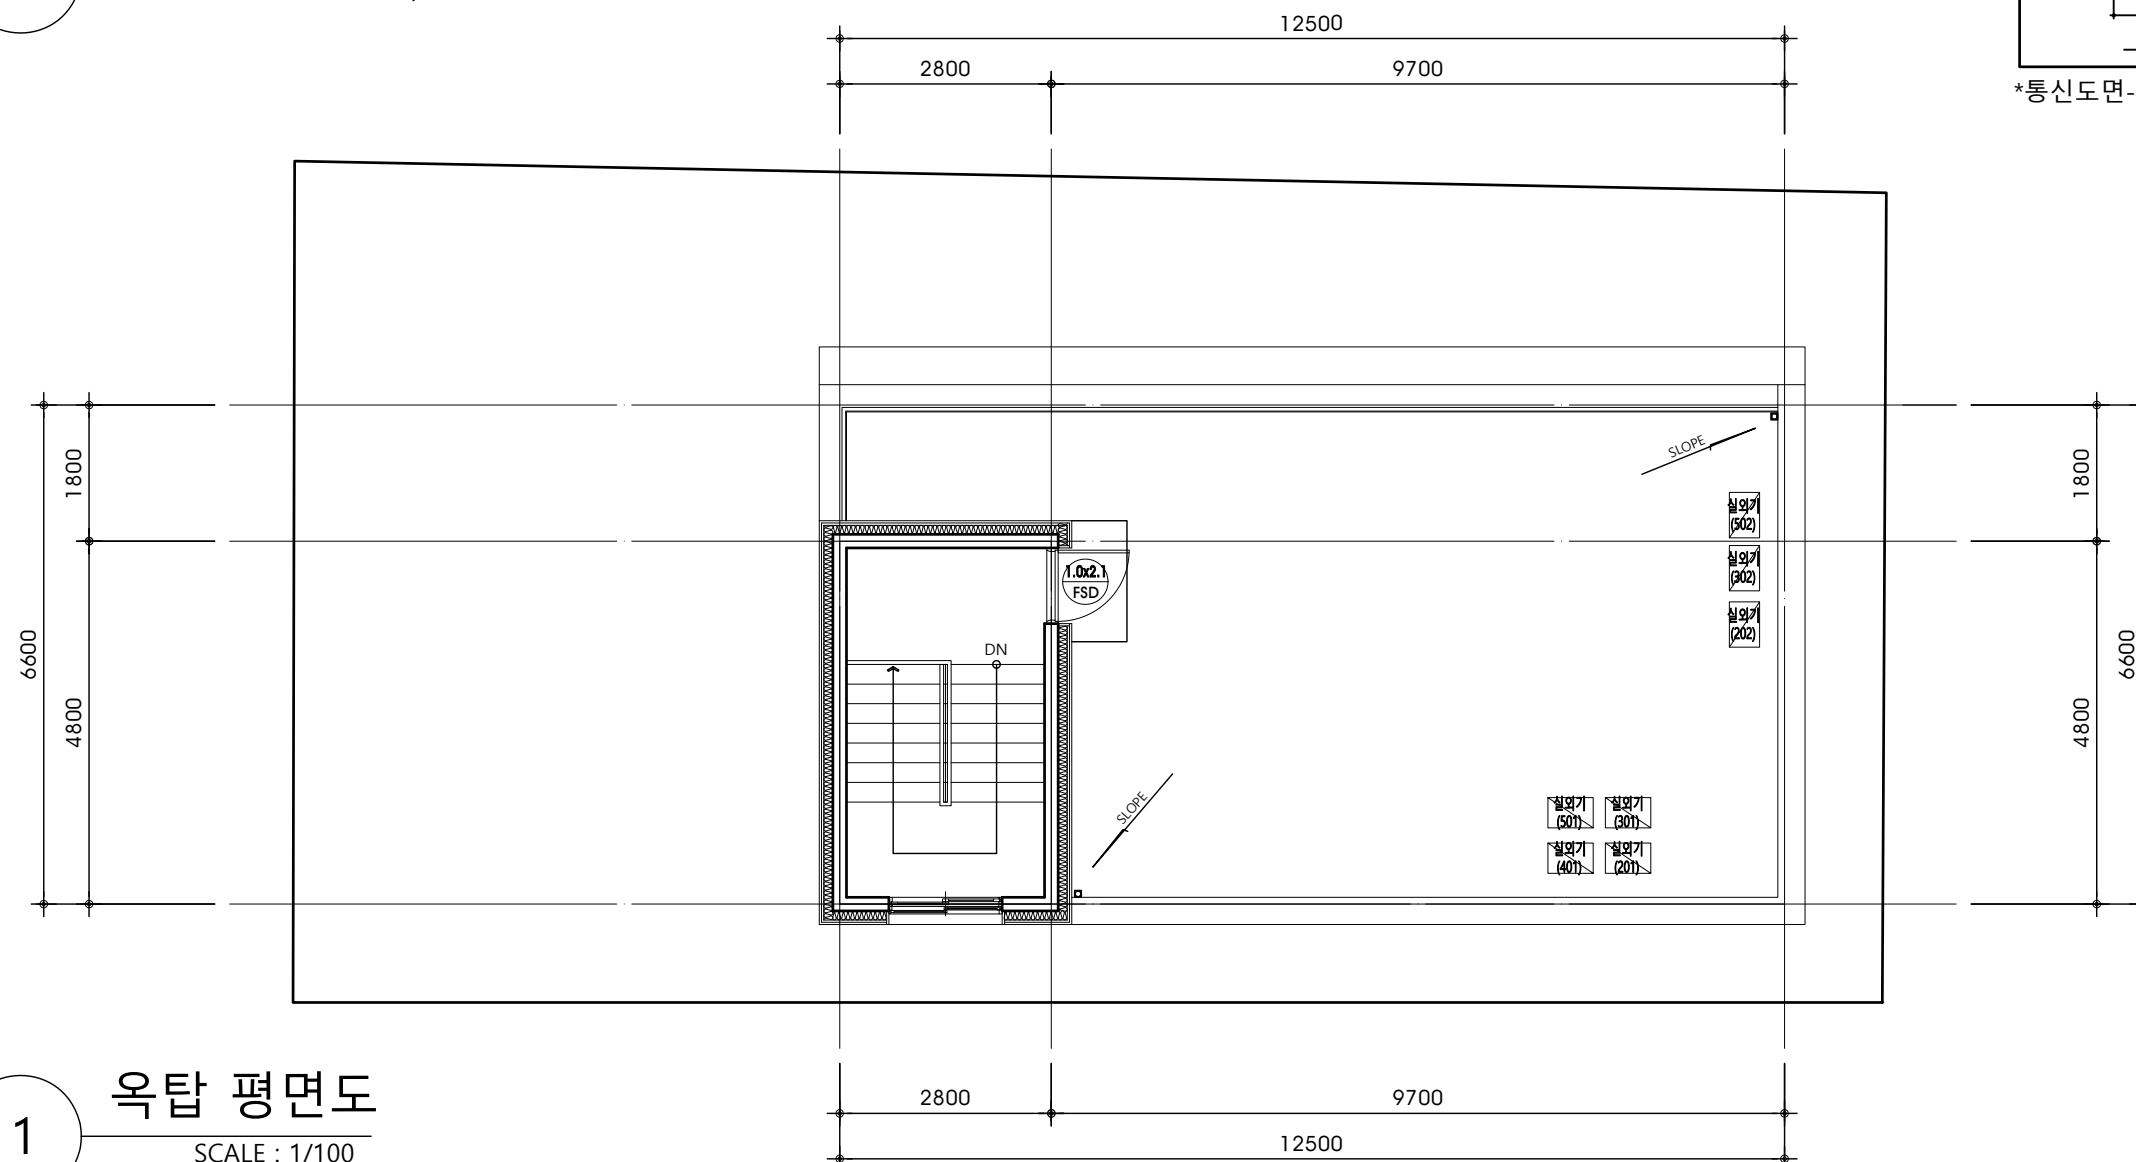

1 옥탑 평면도
SCALE : 1/100

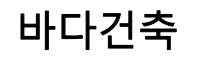

NOTE

	DATE 일자	REV DESCRIPTION 변경내용	DRW 담당	CHE 검토	APP 승인				
APPROVED BY 승인									
CHECKED BY 검토									
DRAWN BY 제도									
DATE 일자		2020.02.							
PROJECT NAME 사업명 반포동 726-40번지 도시형생활주택(원룸형) 신축공사									
DRAWING TITLE 도면명 옥탑 평면도 옥탑지붕 평면도									
SCALE 축척		1 / 100							
DRAWING NO. 도면번호 A-									




NOTE



	DATE 일자	REV DESCRIPTION 변경내용	DRW 담당	CHE 검토	APP 승인			
APPROVED BY 승인								
CHECKED BY 검토								
DRAWN BY 제도								
DATE 일자		2020.02.						
PROJECT NAME 사업명 반포동 726번지 도시형생활주택(원룸형) 신축공사								
DRAWING TITLE 도면명 정면도, 우측면도								
SCALE 축척 1/150								
DRAWING NO. 도면번호 A-								



NOTE

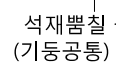

석재뿔칠
(기둥공통)

1 좌 측 면 도
SCALE : 1/150

△ ACK	DATE 일자	REV DESCRIPTION 변경 내용	DRW 담당	CHE 검토	APP 승인
APPROVED BY 승 인					
CHECKED BY 검 토					
DRAWN BY 제 도					
DATE 일 자		2020.02.			
PROJECT NAME 사 업 명 반포동 726-40번지 도시형생활주택(원룸형) 신축공사					
DRAWING TITLE 도 면 명 배면도, 좌측면도					
SCALE 축 적		1/150			
DRAWING NO. 도 면 번 호 A-					