


1. 조감도




2. 건축개요 및 현황도

대 지 위 치	서울특별시 서초구 반포동 716-5호	
대 지 면 적	215.00 ^{M2} - 2.00 (도로후퇴면적) ^{M2} = 실사용면적 : 213.00 ^{M2}	
지 역 , 지 구	제2종 일반주거지역	
용 적 륜	법 정	200.00 %
	계 획	199.99 %
건 폐 율	법 정	60.00 %
	계 획	59.90 %
건 축 면 적	127.59 M2	
용적률산정연면적	425.98 M2	
연 면 적	425.98 M2	
최 고 높 이	15.85 M	
건 축 규 모	지상 5층	
용 도	다세대주택-도시형생활주택(소형주택)-12세대	
조 경 면 적	법 정	213.00m' x 5.0% = 10.65m'
	계 획	10.74m' (5.04 %)
정 화 조	법 정	(2세대 X 2.7인) + (10세대 X 2.0인) = 25.4인
	계 획	부패탱크식 30인조
주 차 대 수	법 정	(10세대 X 0.4대) + (2세대 X 0.5대) = 5.0대 *서울시 공공건설 및 공공물에 관한 조례 제2조 및 제11조의 2 에의거 주차산정할 세대당 0.5대 (전용면적이 30㎡ 미만인경우 세대당 0.4대)
	계 획	5대 설치
비 고		

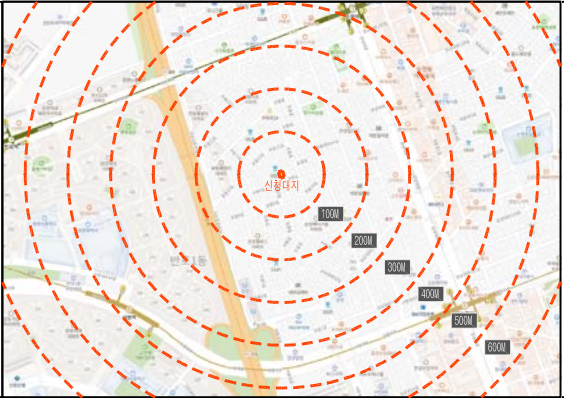


□ 위치도

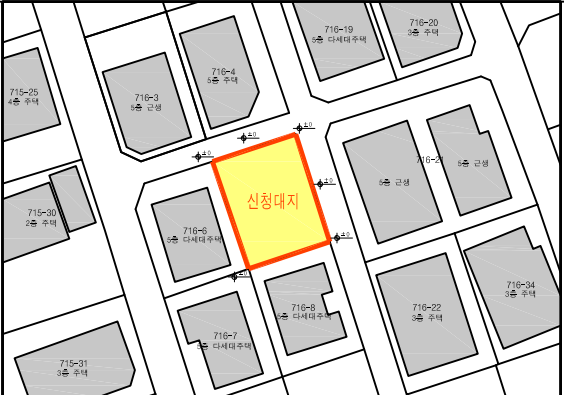

□ 주변현황도

3. 입면도

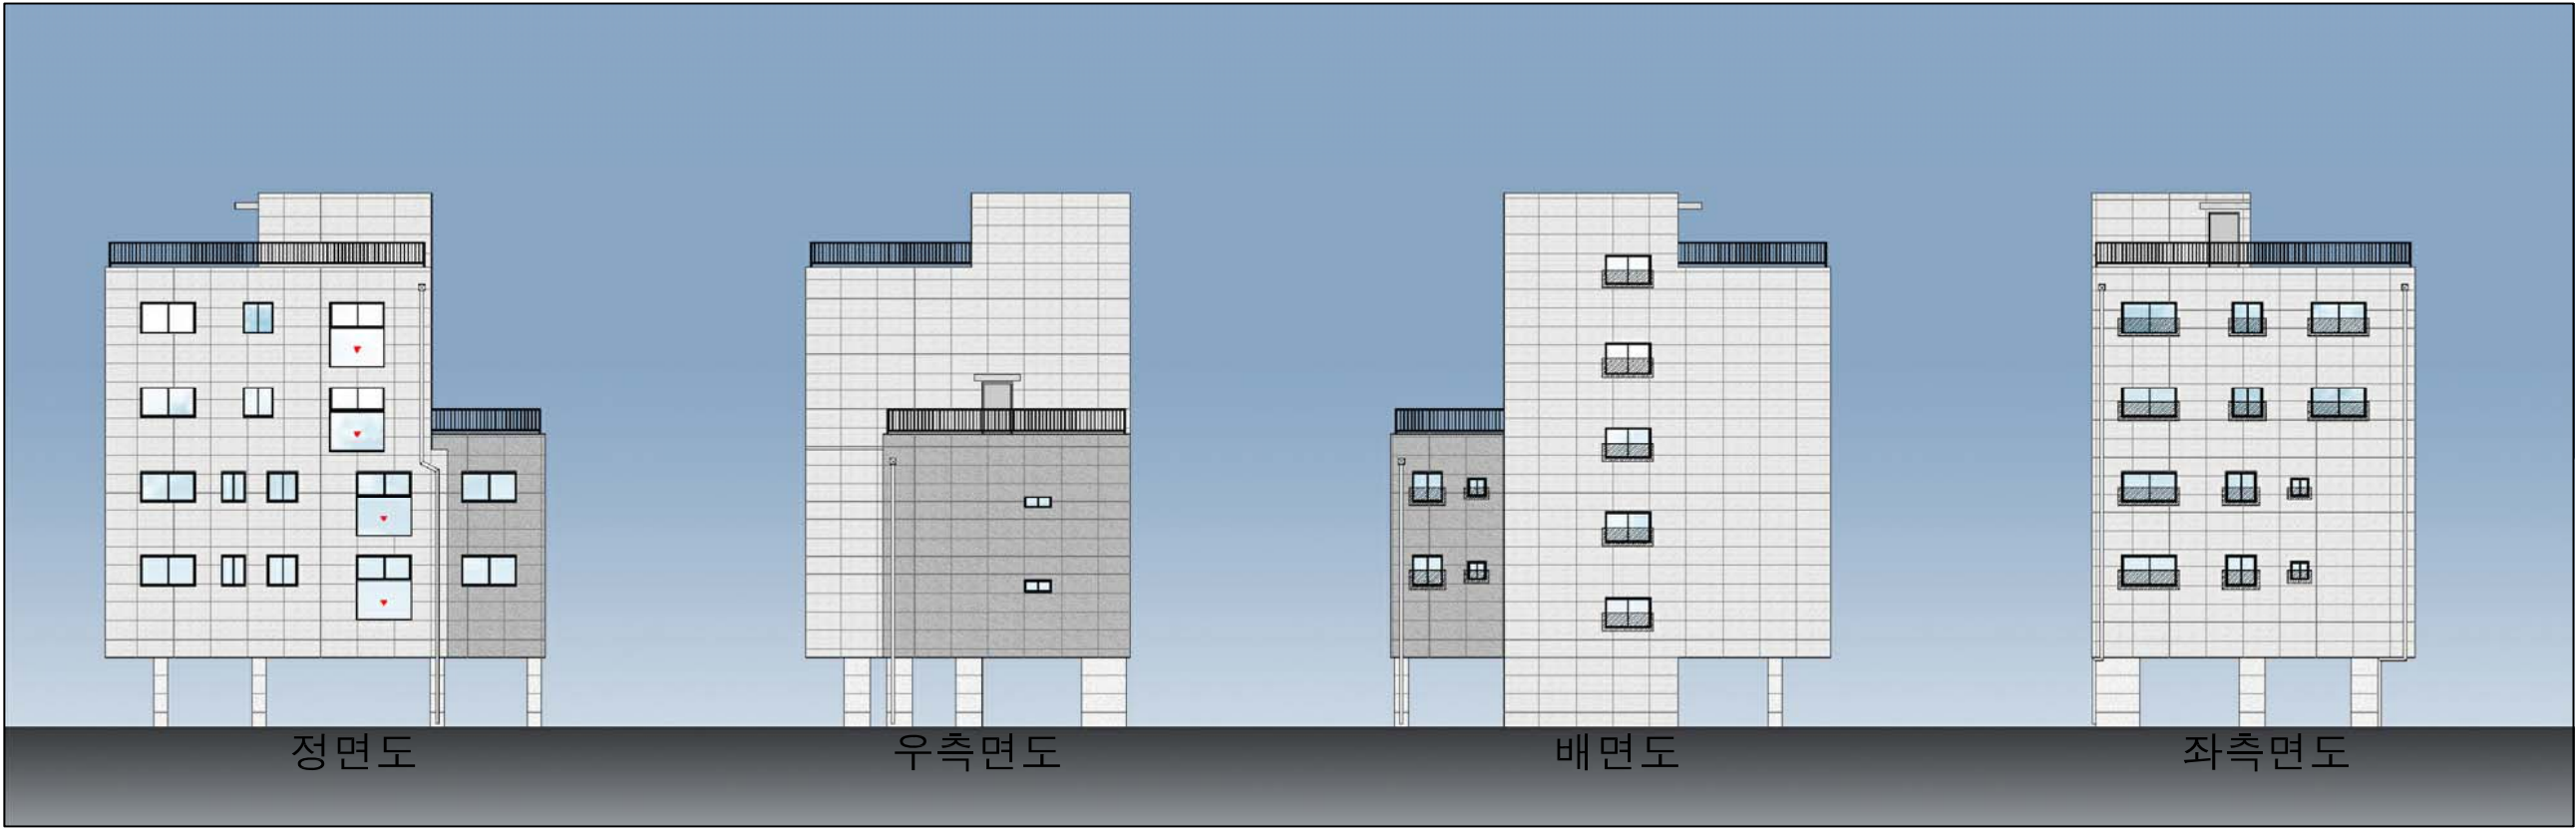

정면도

우측면도

배면도


좌측면도

PROJECT TITLE 사 업 명 칭		
서초구 반포동 716-5호 도시형생활주택(소형주택) 신축공사		
NAME OF DRAWING 도 면 명		
투 시 도		
NOTE 주 기		
NO. ▲ REVISIONS ▲ DATE 번호 수 정 일자		
DESIGNED BY 설 계		
CHECKED BY 심 사		
APPROVED BY 승 인		
CONSULTANTS 업 통 설 계		
SCALE 축 척		
DATE 일 자 2022. 08.		
DWG NO. 도면 번호 A-02		
SHEET NO. 일련 번호 □-□□□		
 daumoo 건축사사무소 다움건축		
THE ARCHITECTS DESIGN GROUP TEL. 02.414.6061 (代) FAX. 02.414.6062		

4. 설계자 의도

■ 디자인 의도

- 보행자, 차량 출입의 원활한 계획
- 도로측에 순응한 주동 배치
- 정면성을 강조하는 디자인 계획

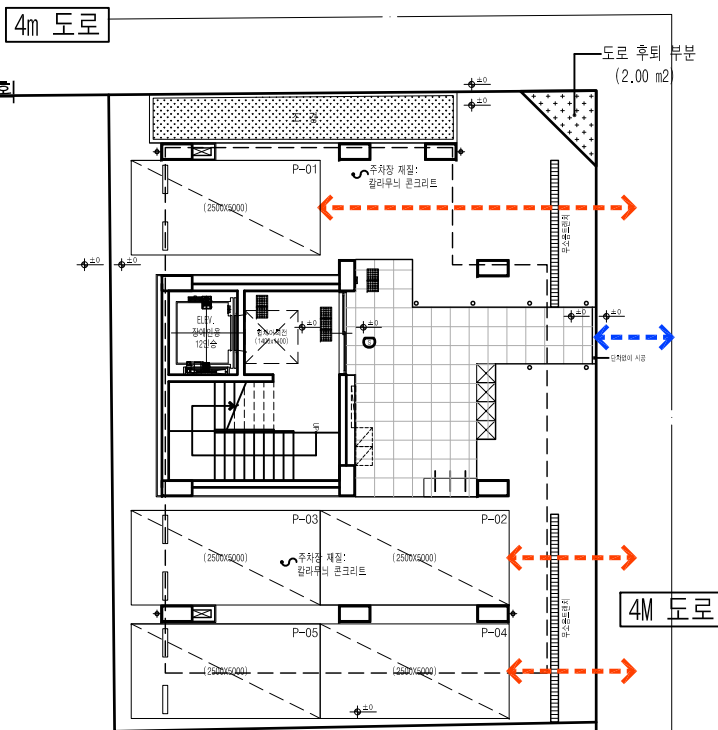

■ 입면 디자인 계획 (정면성 강조)

- 창호크기 및 열을 맞추어 입면에 정돈된 이미지를 부여함.


밝은 색 돌마감으로 단정한 입면 계획.

어두운 색 돌마감으로 면분할하여 단조롭고 심심한 입면 탈피.



5. 재료계획

1. 외벽 마감재

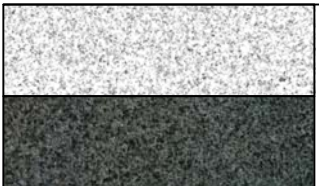


화강석

2. 주차장 바닥재



칼라 콘크리트

3. 옥외 난간재

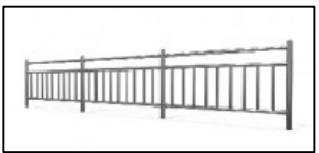

철제 난간

□ 외장재

구분

실명

재료명

1층

필로티 주차장

바닥 : 칼라 콘크리트
천정 : AL 천정판

2~5층

현관

바닥 : 화강석 마감

방

바닥 : 비닐쉬트 마감
천정 : 천정지

거실

바닥 : 데코타일or비닐쉬트 마감
천정 : 천정지

베란다

바닥 : 석재타일
천정 : 무기질계 도막방수

□ 내장재

6. 색채계획

- ☐ 자연스러운 색상과 주변과의 조화
- ☐ 무채색 위주의 색상 활용으로 주변과 어울리는 건물계획
- ☐ 가로경관 미관성 및 친근성



거창석 계열:화강석

고흥석 계열:화강석

PROJECT TITLE
사업명칭

서초구 반포동 716-5호
도시형생활주택(소형주택)
신축공사

NAME OF DRAWING
도면명

디자인 의도, 재료계획, 색채 계획도

NOTE
주 기

NO. ▲ REVISIONS ▲ DATE
번호 수정 일자

DESIGNED BY
설 계

CHECKED BY
심 사

APPROVED BY
승 인

CONSULTANTS
업 종 설 계

SCALE
축 척



DATE
일 자 2022. 08.

DWG NO.
도면 번호 A-03

SHEET NO.
일련 번호 □-□□□



BAWOOO
dawoom
건축사사무소 다움건축

THE ARCHITECTS DESIGN GROUP
TEL. 02.414.6061 (代)
FAX. 02.414.6062

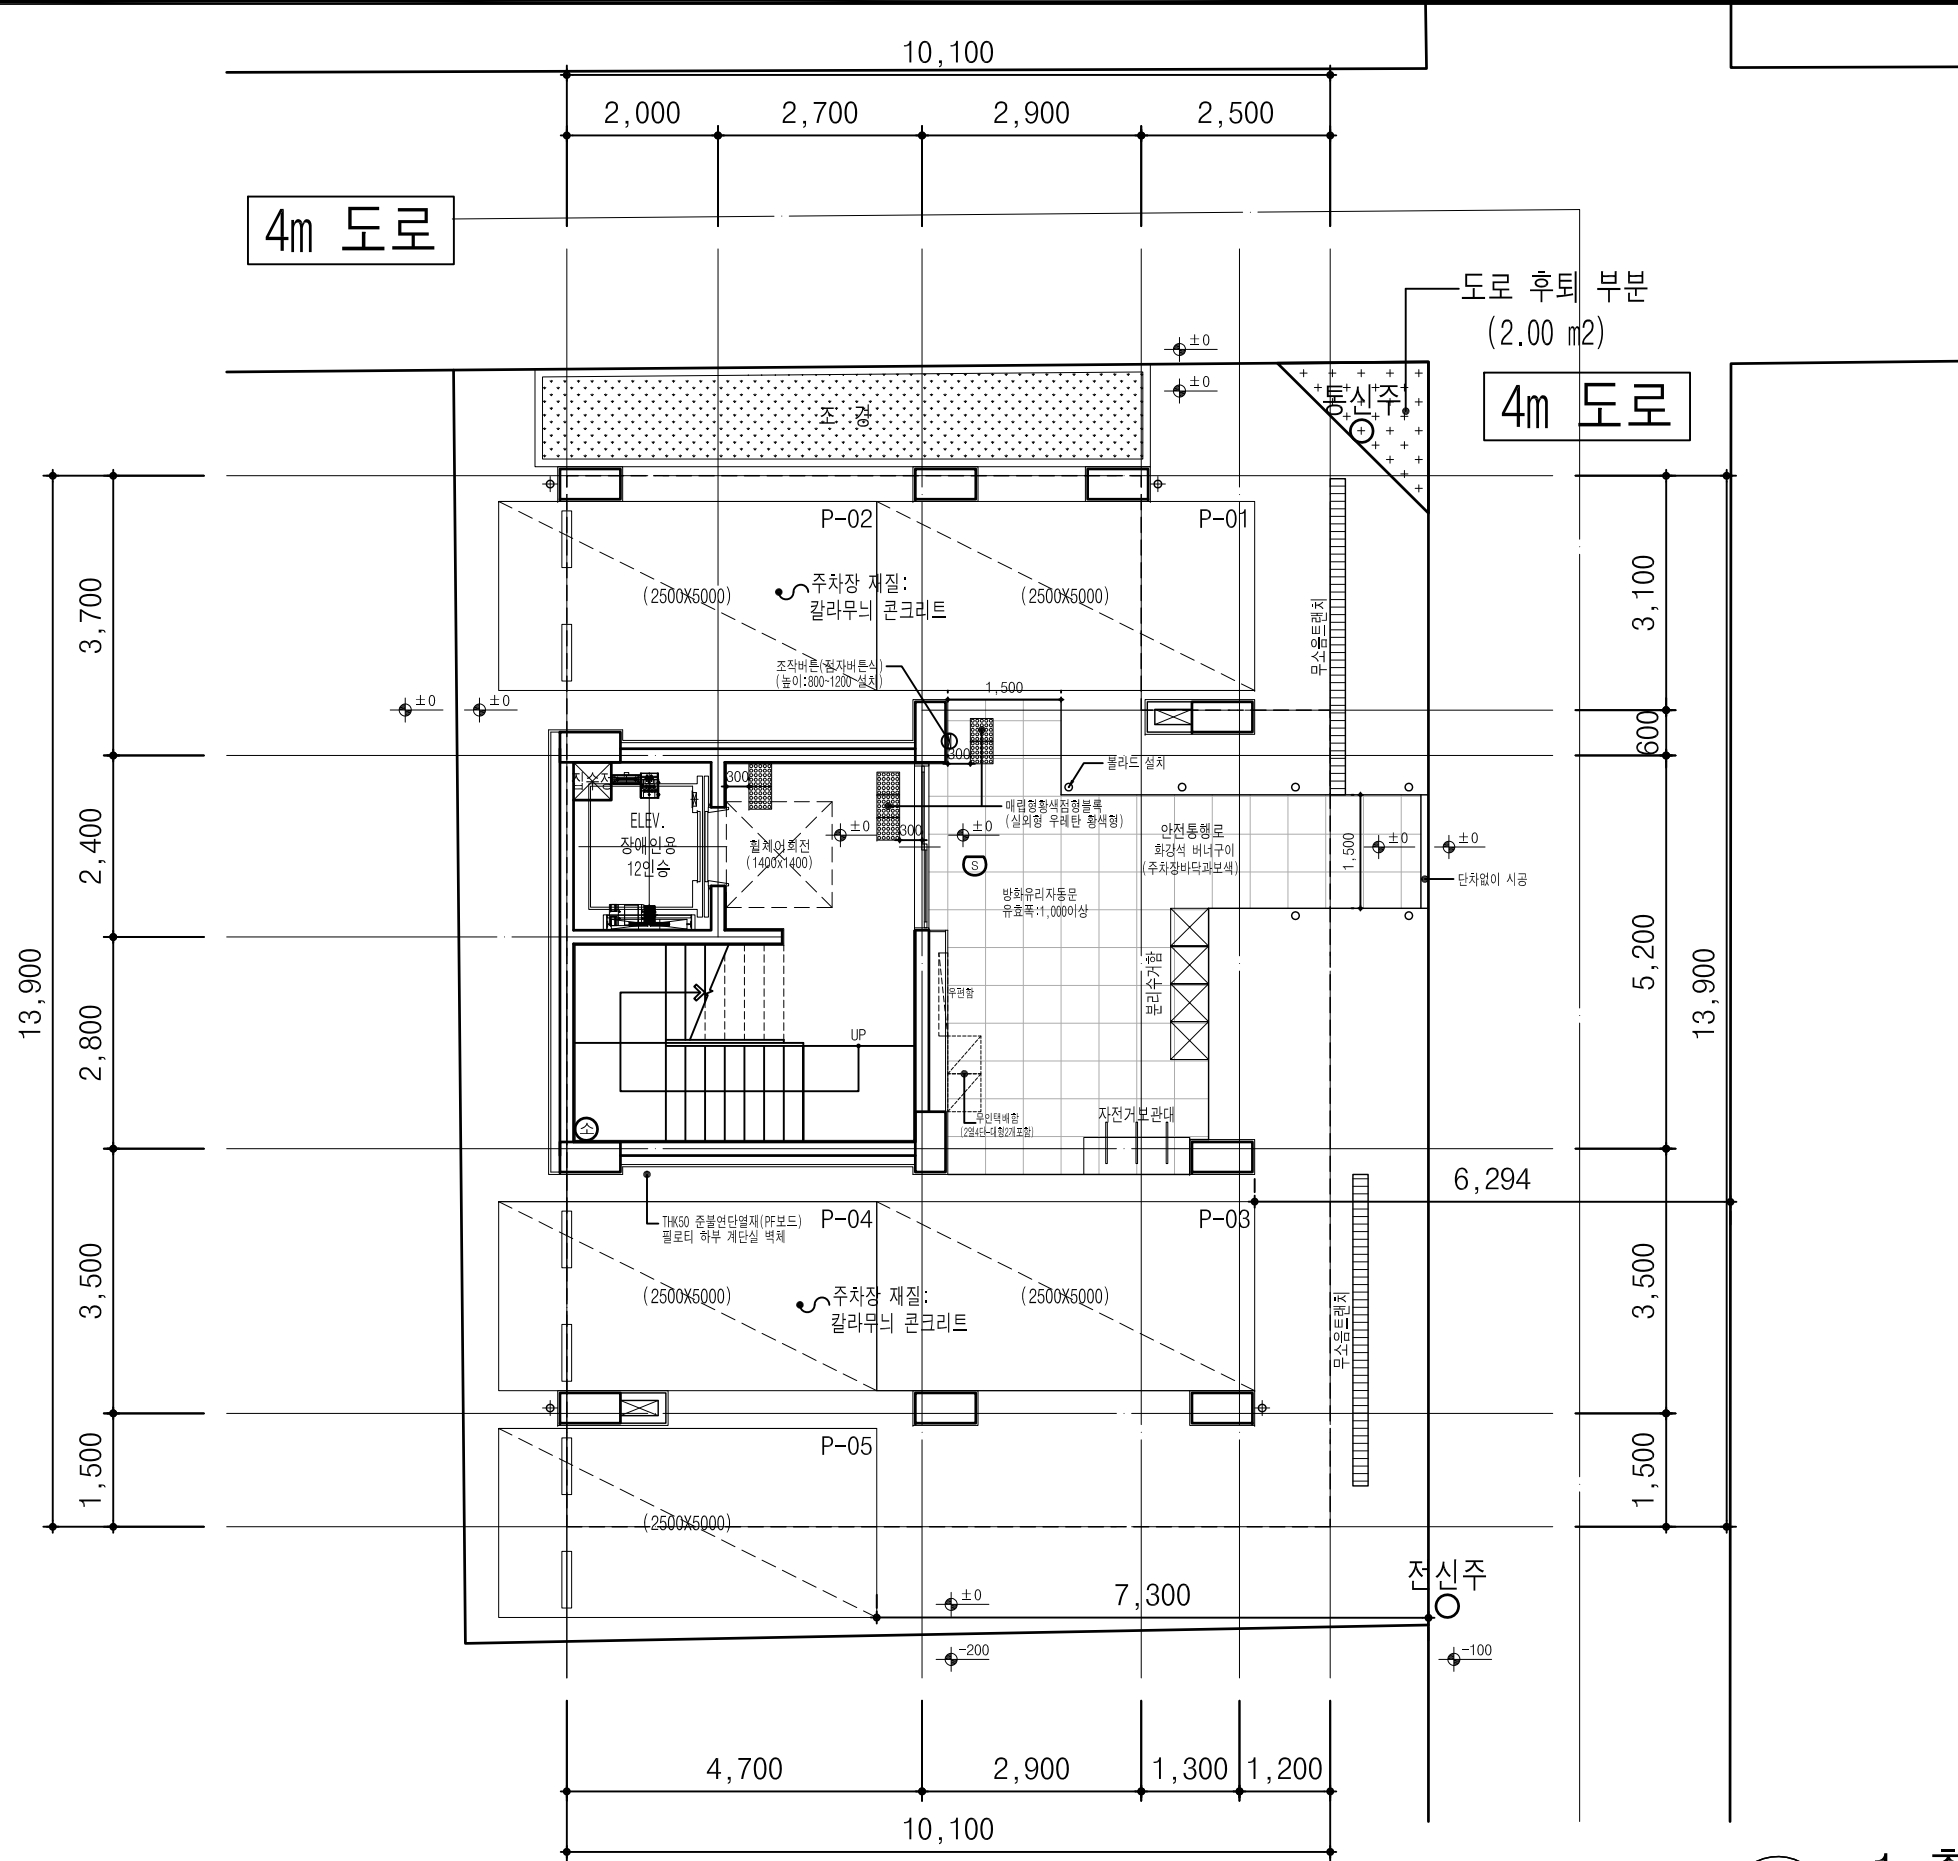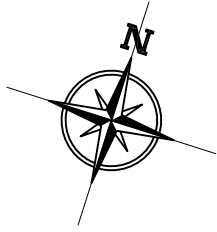

1층 평면도
SCALE : A3 : 1/100

PROJECT TITLE 사업명명		
서초구 반포동 716-5호 도시형생활주택(소형주택) 신축공사		
NAME OF DRAWING 도면명		
1층 평면도		
NOTE 주기		
단독경보감지기(연기식)		
단독경보감지기(열감지)		
ABC분말소화기(2.5KG)		
가스누설경보기		
일산화탄소경보기		
차면시설		
보일러		
에어컨 실외기		
NO. REVISIONS DATE 번호 수정 일자		
DESIGNED BY 설계		
CHECKED BY 심사		
APPROVED BY 승인		
CONSULTANTS 업종설계		
SCALE 축척 1/100		
DATE 일자 2022. 08.		
DWG NO. 도면번호 A-21		
SHEET NO. 일련번호 □-□□□		
 건축사사무소 다움건축 THE ARCHITECTS DESIGN GROUP TEL. 02.414.6061 (대) FAX. 02.414.6062		

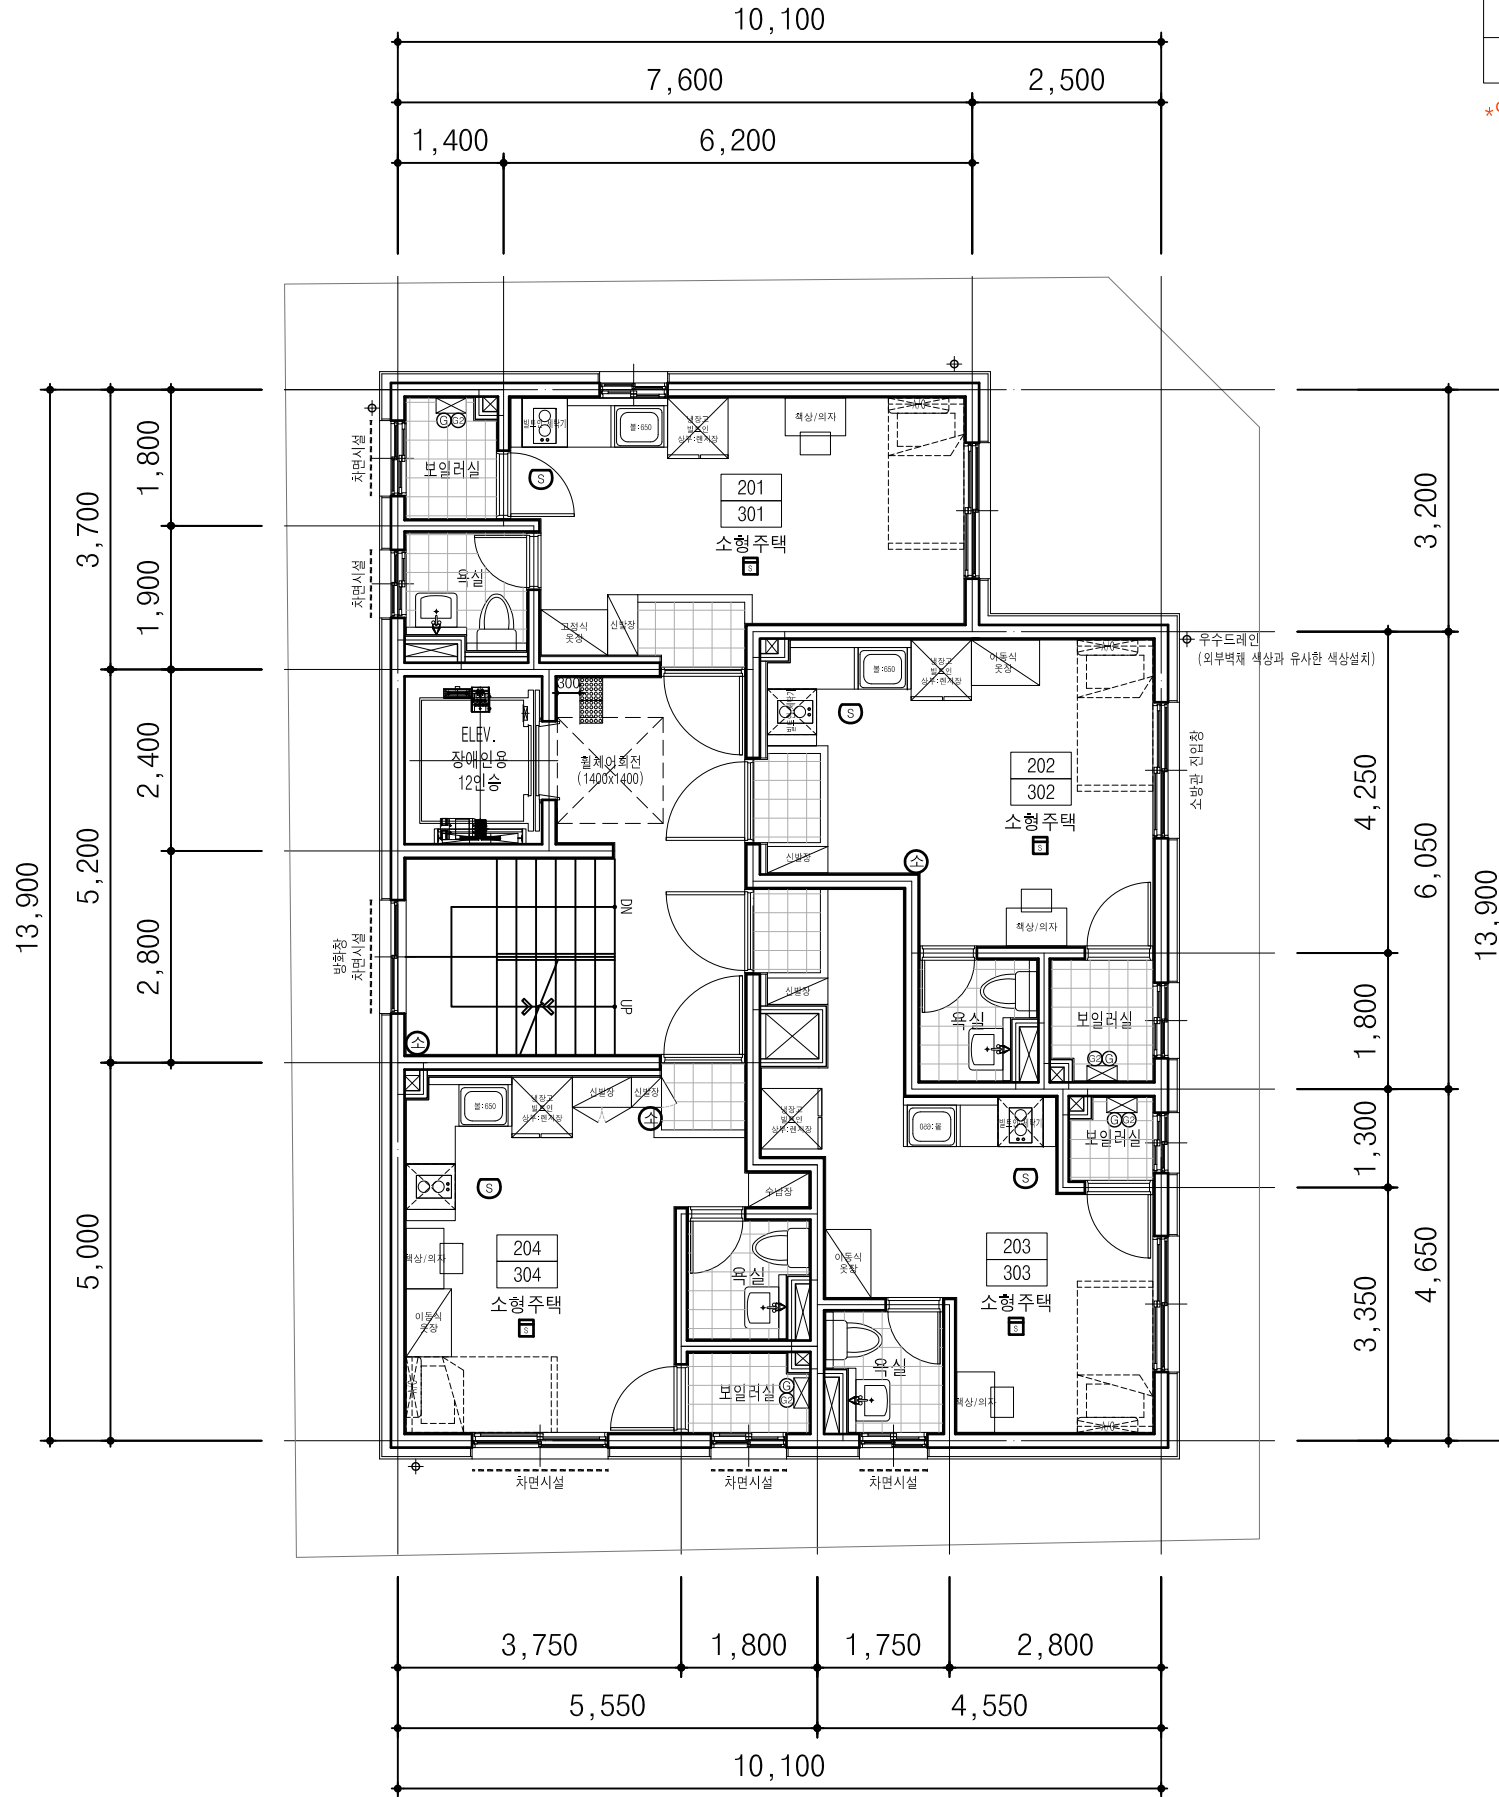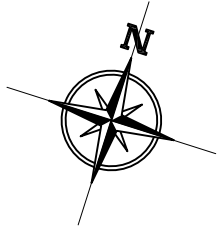

*빌트인 필수 품목

구분	냉장고	벽걸이 에어컨	세탁기	책상	의자	이동식옷장
에너지 효율	최상위	최상위	최상위	-	-	-

*엘리베이터 인접세대 벽체에 차음시트(3T) 부착

PROJECT TITLE 사업명칭	서초구 반포동 716-5호 도시형생활주택(소형주택) 신축공사
-----------------------	---

NAME OF DRAWING 도면명	2~3 층 평면도
------------------------	-----------

2~3 층 평면도

NOTE
주 기

- 단독경보감지기(연기식)
- 단독경보감지기(열감지)
- ABC분말소화기(2.5KG)
- 가스누설경보기
- 일산화탄소경보기
- 차면시설
- 보일러
- 에어컨 실외기

NO.	REVISIONS	DATE
번호	수정	일자

DESIGNED BY
설계

CHECKED BY
심사

APPROVED BY
승인

CONSULTANTS
합동설계

SCALE
축척 1/100



DATE
일자 2022. 08.

DWG NO.
도면번호 A-22

SHEET NO.
일련번호

DAWOOM
다움건축
건축사사무소 다움건축
THE ARCHITECTS DESIGN GROUP
TEL. 02.414.6061 (代)
FAX. 02.414.6062

2~3 층 평면도
SCALE : A3 : 1/100

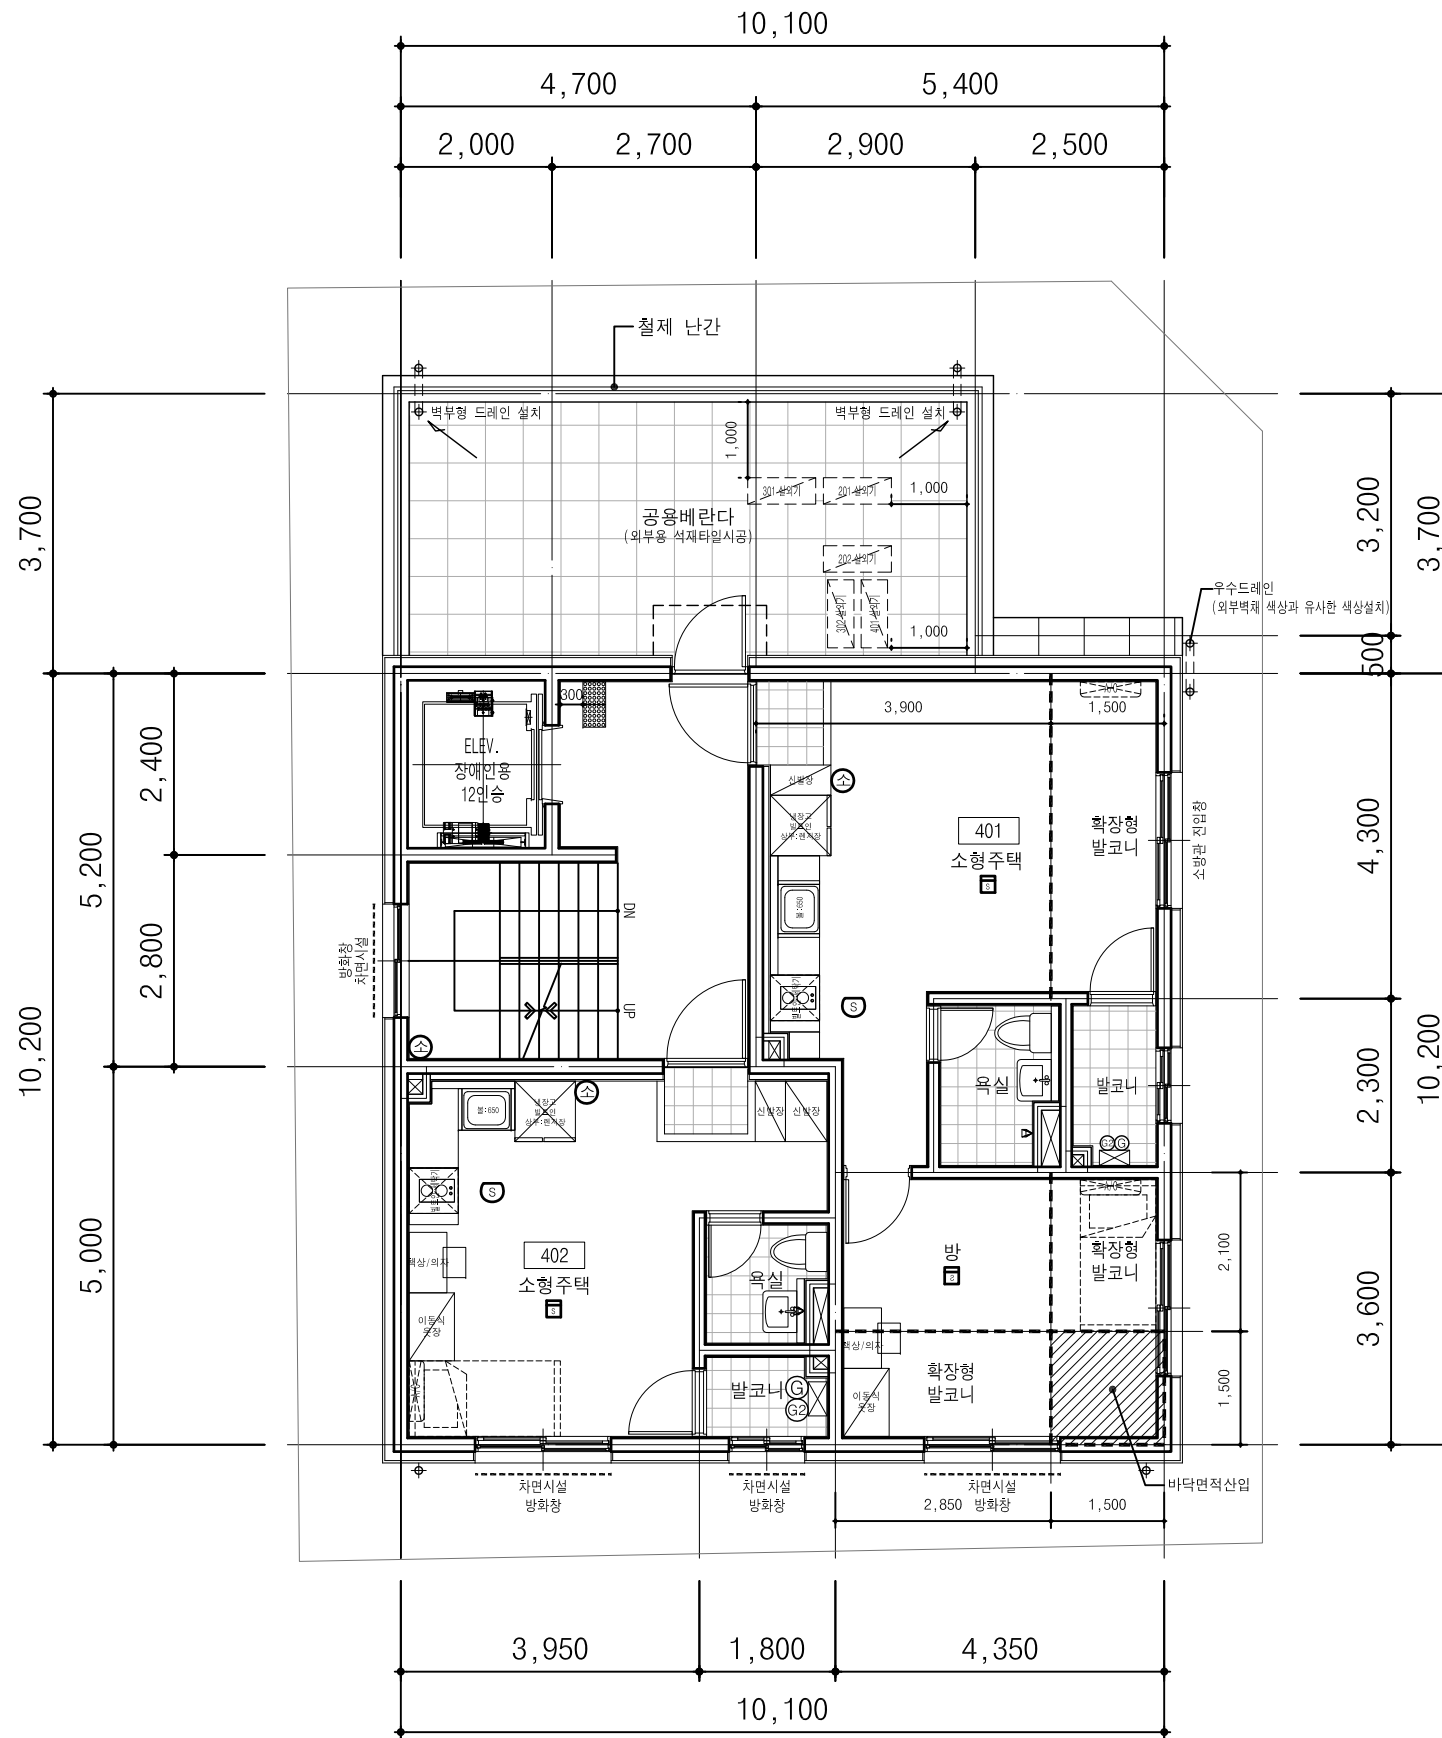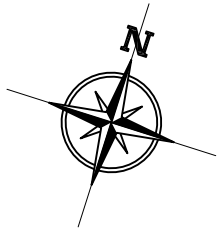

*빌트인 필수 품목

구분	냉장고	벽걸이 에어컨	세탁기	책상	의자	이동식옷장
에너지 효율	최상위	최상위	최상위	-	-	-

*엘리베이터 인접세대 벽체에 차음시트(3T) 부착

4 층 평 면 도
SCALE : A3 : 1/100

PROJECT TITLE
사업명칭
서초구 반포동 716-5호
도시형생활주택(소형주택)
신축공사

NAME OF DRAWING
도면명
4 층 평 면 도

- NOTE
주 기
- 단독경보감지기(연기식)
 - 단독경보감지기(열감지)
 - ABC분말소화기(2.5KG)
 - 가스누설경보기
 - 일산화탄소경보기
 - 차면시설
 - 보일러
 - 에어컨 실외기

NO. ▲ REVISIONS ▲ DATE
번호 수정 일자

DESIGNED BY
설 계

CHECKED BY
심 사

APPROVED BY
승 인

CONSULTANTS
업 종 설 계



SCALE
축 척 1/100

DATE
일 자 2022. 08.

DWG NO.
도면 번호 A-23

SHEET NO.
일련 번호 □-□□□

다원도원
dawoon
건축사사무소 다원건축
THE ARCHITECTS DESIGN GROUP
TEL. 02.414.6061 (代)
FAX. 02.414.6062

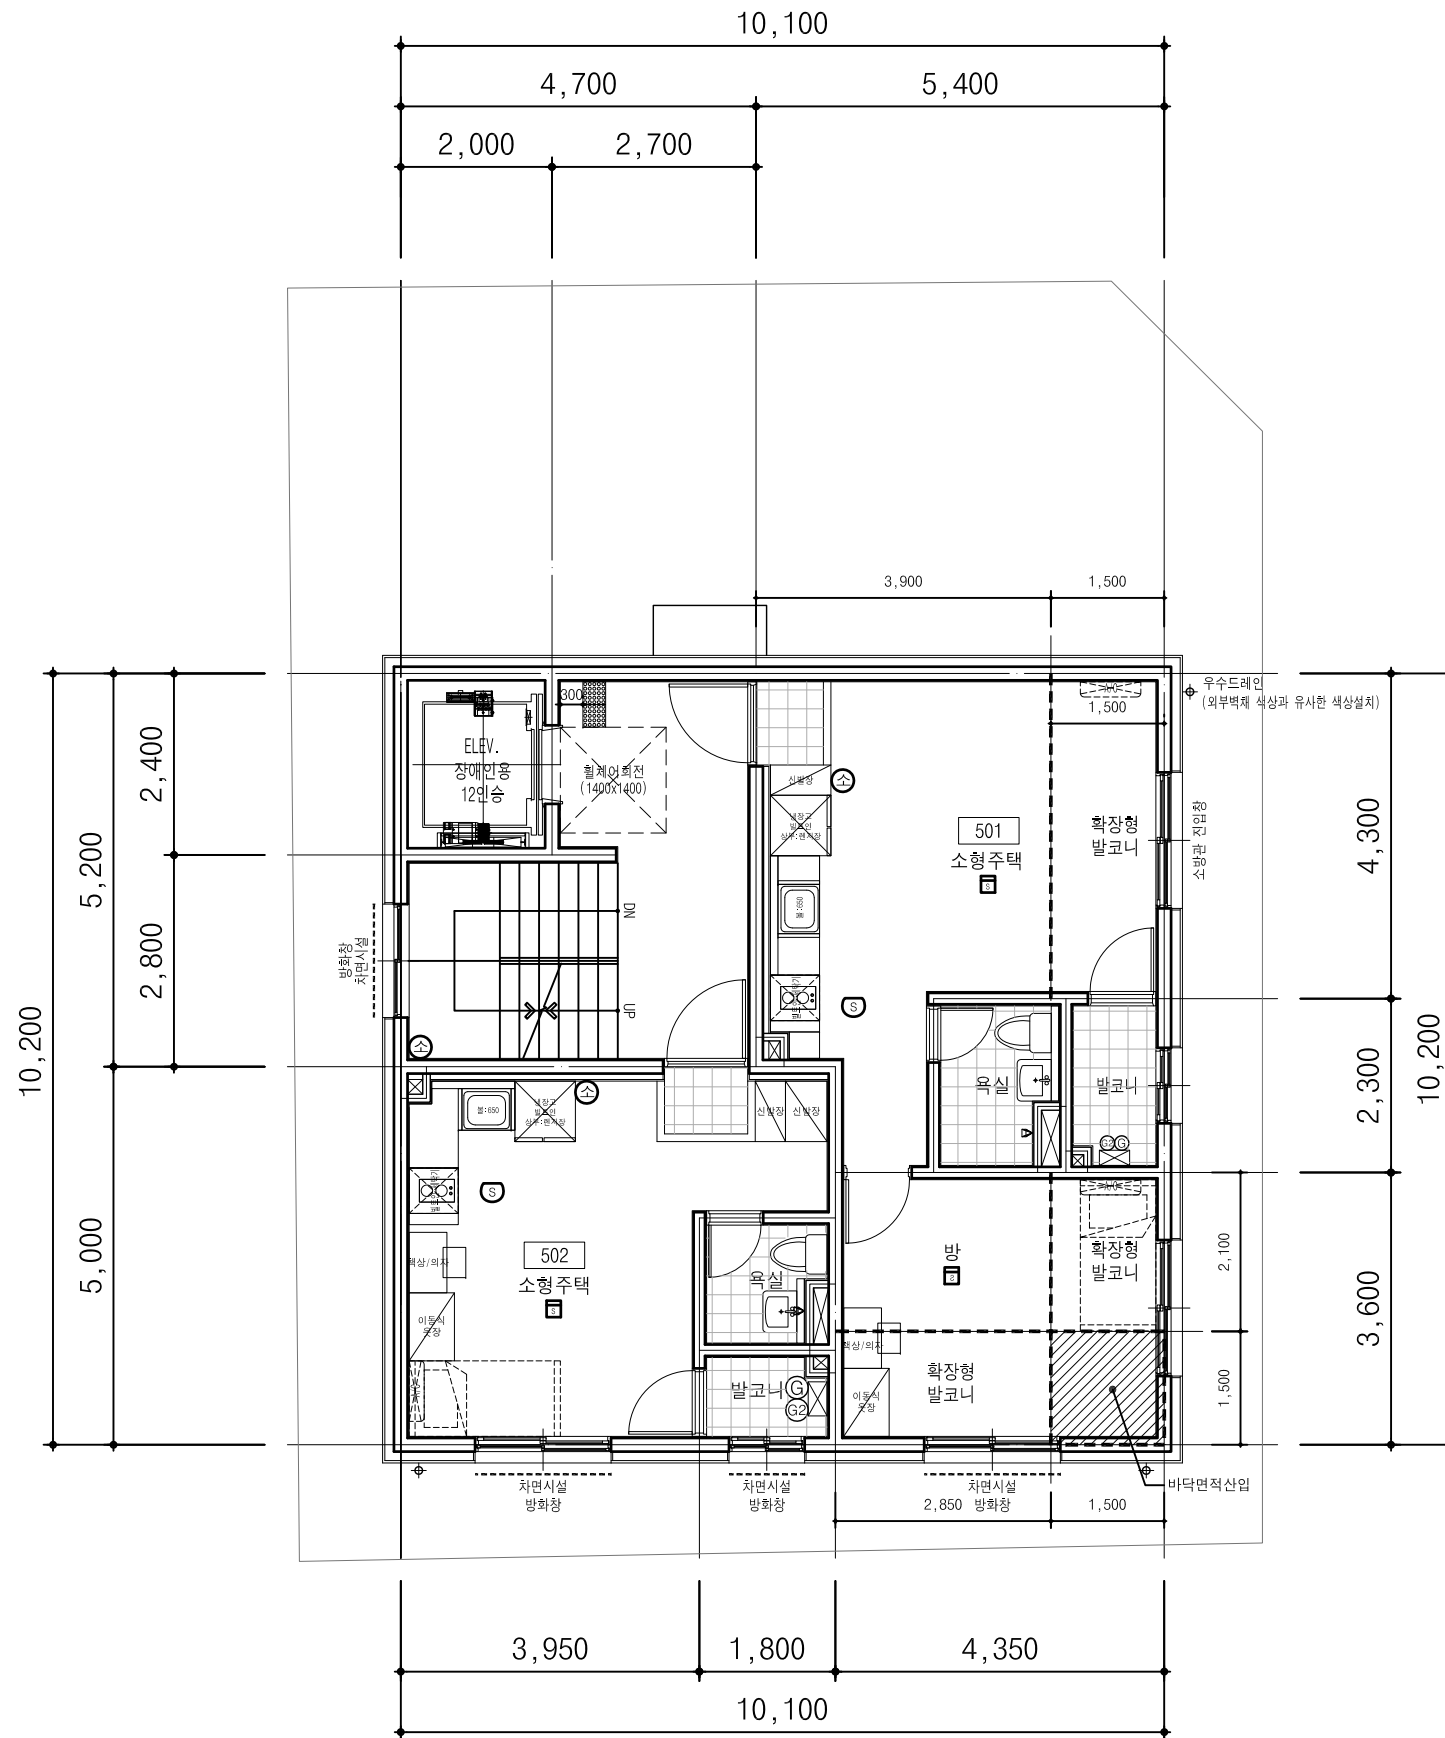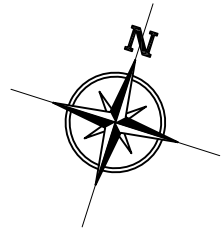

*빌트인 필수 품목

구분	냉장고	벽걸이 에어컨	세탁기	책상	의자	이동식옷장
에너지 효율	최상위	최상위	최상위	-	-	-

*엘리베이터 인접세대 벽체에 차음시트(3T) 부착

5 층 평 면 도
SCALE : A3 : 1/100

PROJECT TITLE
사업명칭
서초구 반포동 716-5호
도시형생활주택(소형주택)
신축공사

NAME OF DRAWING
도면명
5 층 평 면 도

- NOTE
주 기
- 단독경보감지기(연기식)
 - 단독경보감지기(열감지)
 - ABC분말소화기(2.5KG)
 - 가스누설경보기
 - 일산화탄소경보기
 - 차면시설
 - 보일러
 - 에어컨 실외기

NO. ▲ REVISIONS ▲ DATE
번호 수 명 일자

DESIGNED BY
설 계

CHECKED BY
심 사

APPROVED BY
승 인

CONSULTANTS
업 종 설 계



SCALE
축 척 1/100

DATE
일 자 2022. 08.

DWG NO.
도면 번호 A-24

SHEET NO.
일련 번호 □-□□□


daumoom
건축사사무소 다움건축
THE ARCHITECTS DESIGN GROUP
TEL. 02.414.6061 (代)
FAX. 02.414.6062

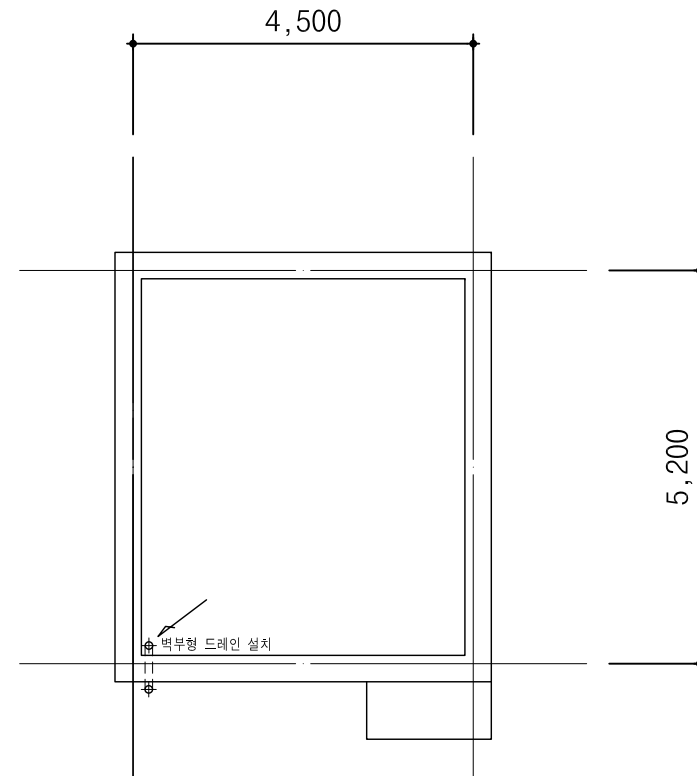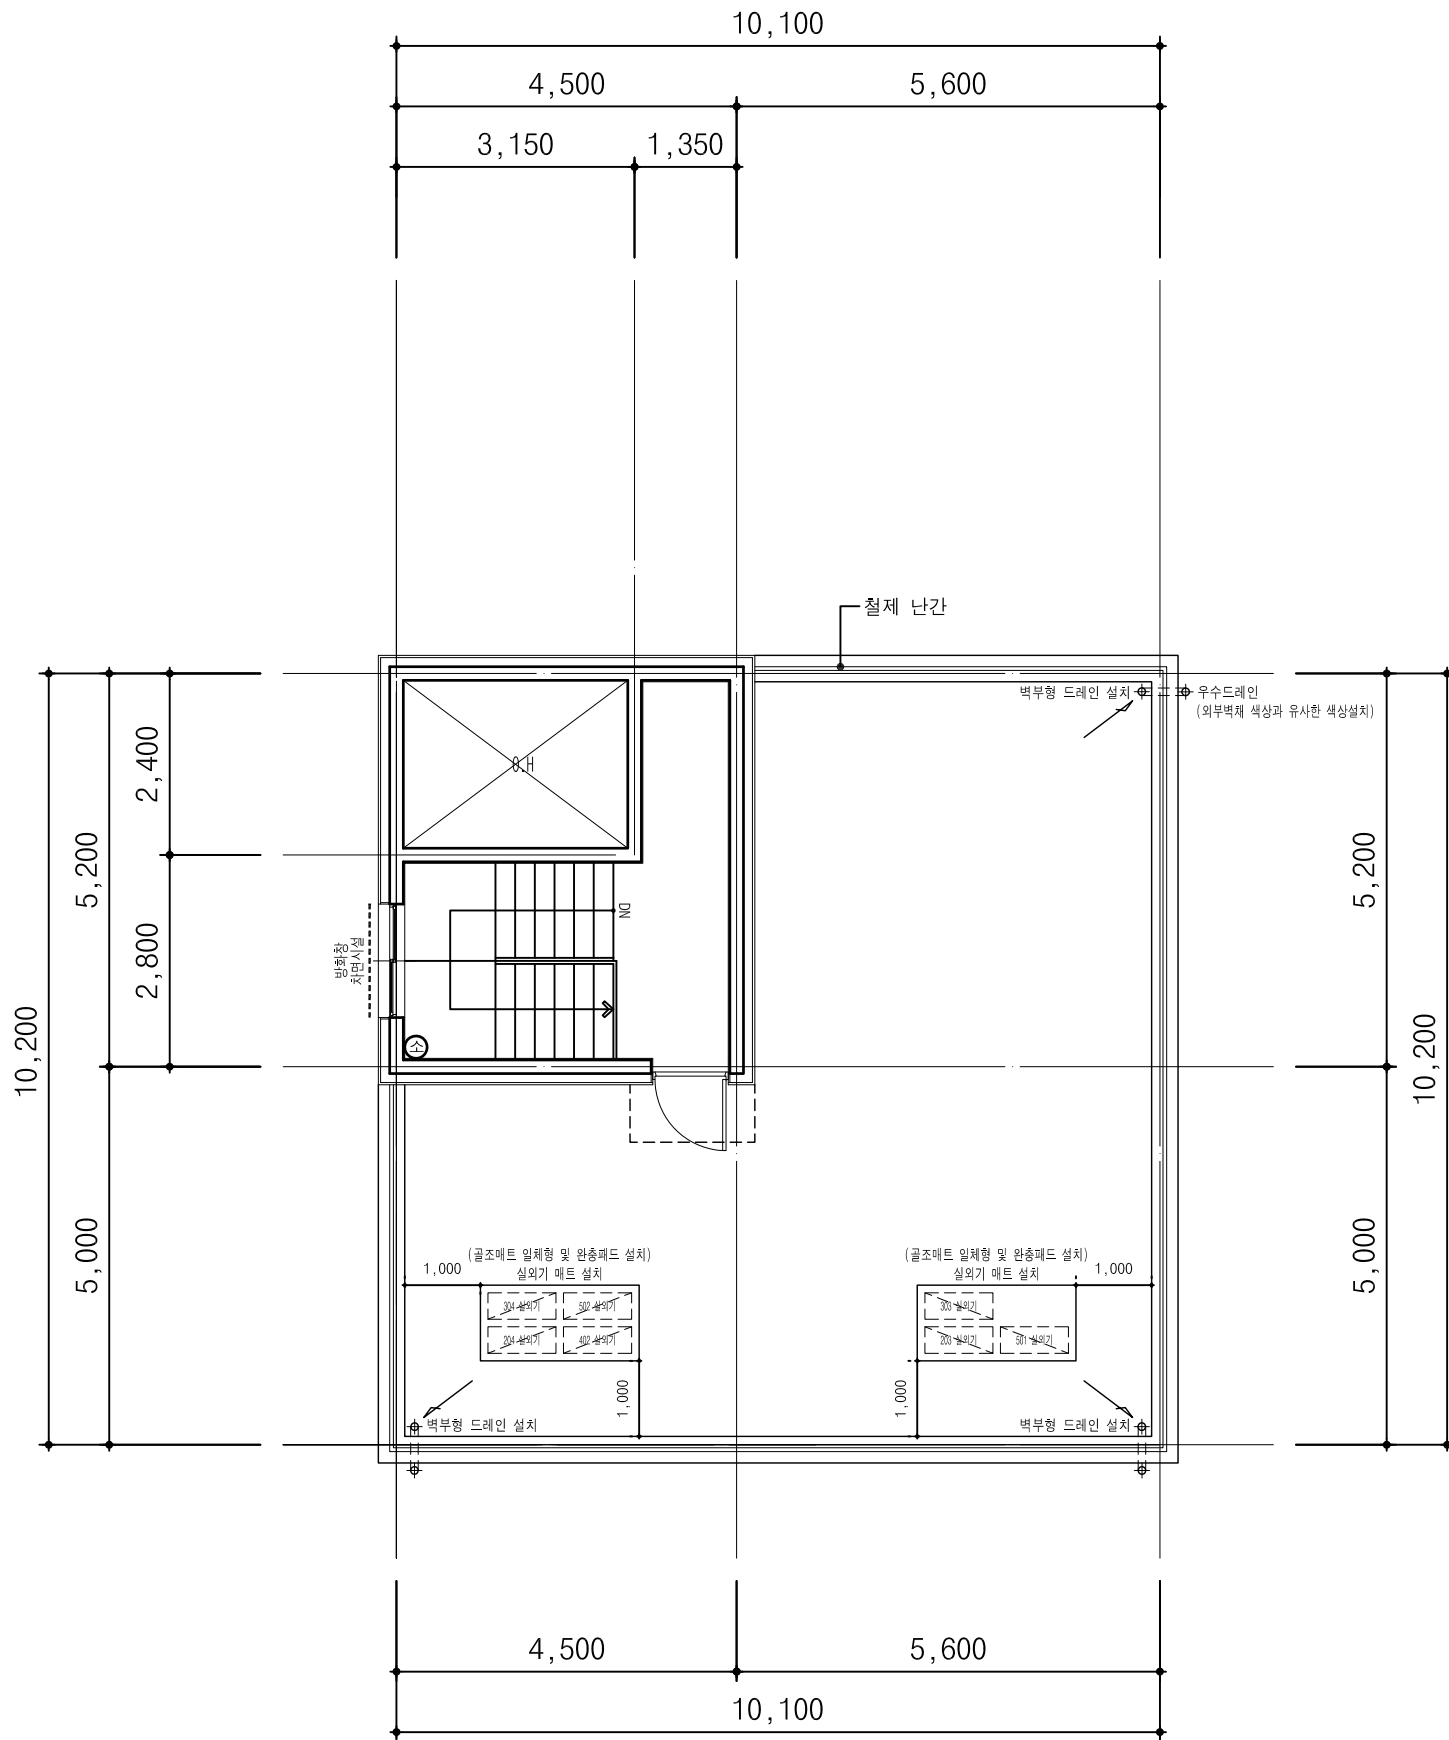

지붕및옥탑평면도
SCALE : A3 : 1/100

PROJECT TITLE
사업명칭

서초구 반포동 716-5호
도시형생활주택(소형주택)
신축공사

NAME OF DRAWING
도면명

지붕및옥탑평면도

- NOTE
주 기
- 단독경보감지기(연기식)
 - 단독경보감지기(열감지)
 - ABC분말소화기(2.5KG)
 - 가스누설경보기
 - 일산화탄소경보기
 - 차면시설
 - 보일러
 - 에어컨 실외기

NO. REVISIONS DATE
번호 수정 일자

DESIGNED BY
설계

CHECKED BY
심사

APPROVED BY
승인

CONSULTANTS
담당설계



SCALE
축척 1/100

DATE
일자 2022. 08.

DWG NO.
도면번호 A-25

SHEET NO.
일련번호 □—□□□


dawoon
건축사사무소 다움건축
THE ARCHITECTS DESIGN GROUP
TEL. 02.414.6061 (代)
FAX. 02.414.6062

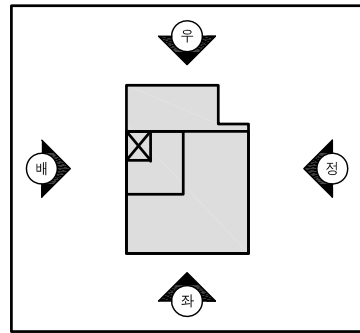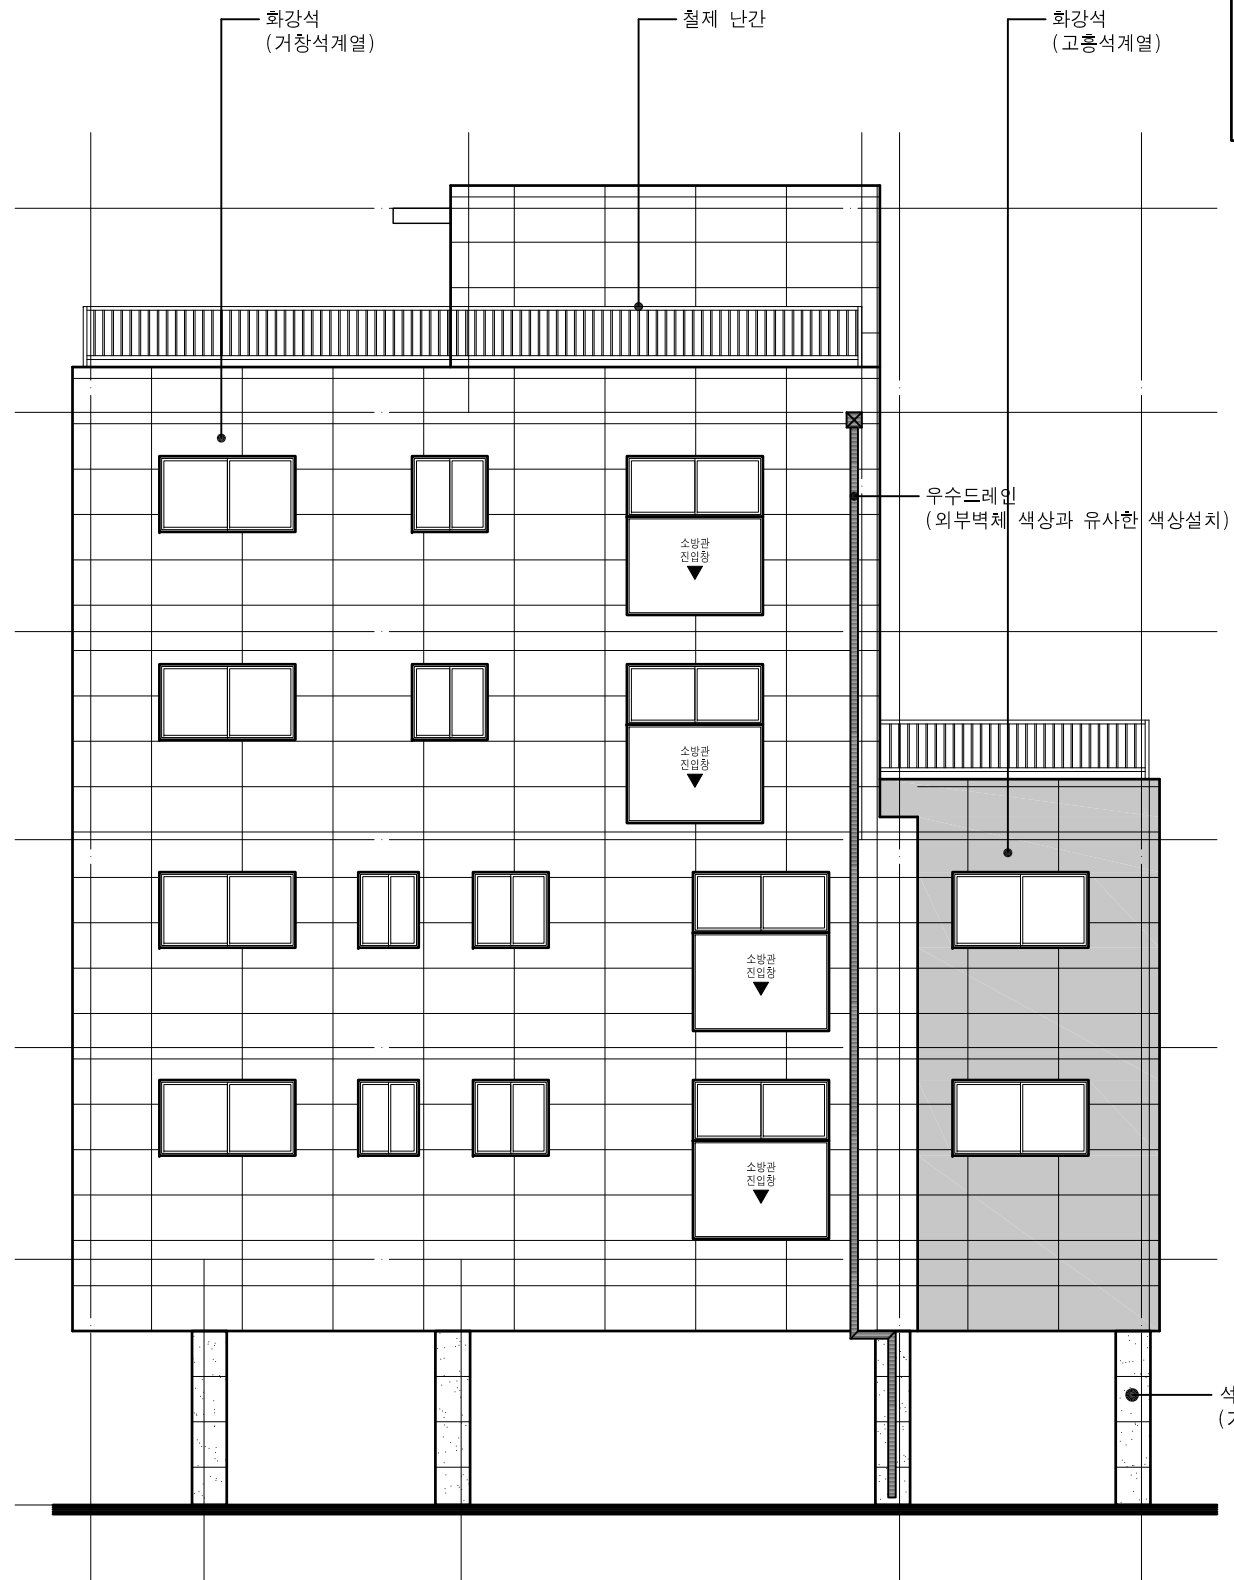

▽지붕층 바닥

▽5층 바닥

▽4층 바닥


우수드레인
(외부벽체 색상과 유사한 색상설치)

▽3층 바닥

▽2층 바닥

▽1층 바닥

정면도
SCALE : A3 : 1/100

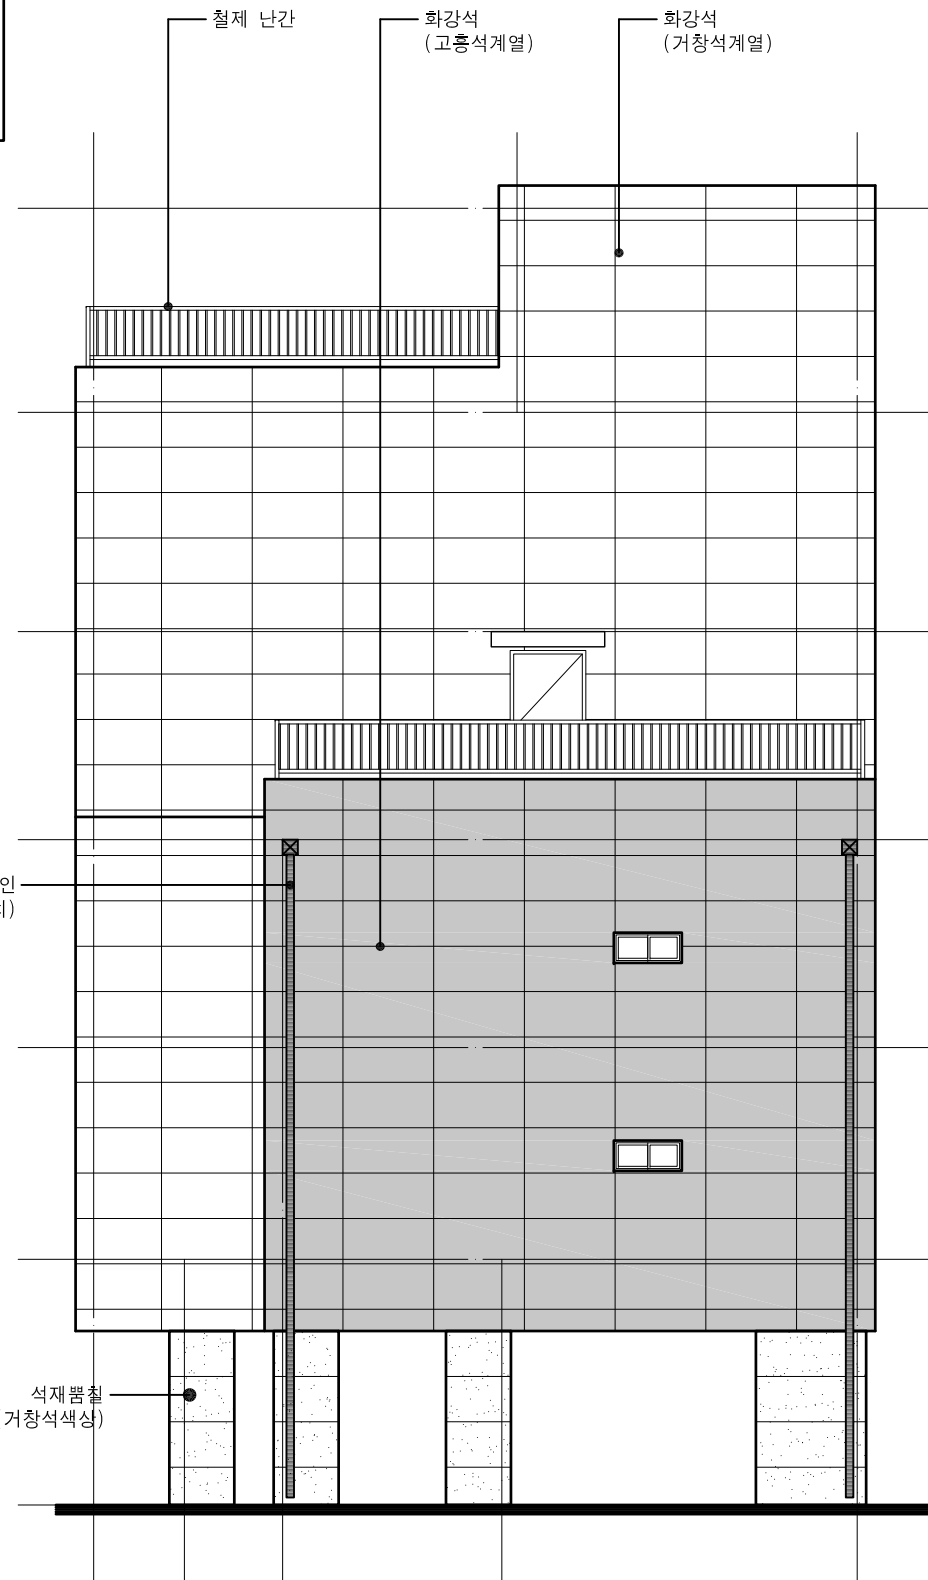

석재뿔칠
(거창석색상)

우측면도
SCALE : A3 : 1/100

PROJECT TITLE
사업명칭

서초구 반포동 716-5호
도시형생활주택(소형주택)
신축공사

NAME OF DRAWING
도면명

입면도-1

NOTE
주
기

창호 PVC 블랙
소방관진입창 - 스티커부착

NO. ▲ REVISIONS ▲ DATE
번호 수정 일자

DESIGNED BY
설계

CHECKED BY
심사

APPROVED BY
승인

CONSULTANTS
담당설계


SCALE
축척 1/100

DATE
일자 2022. 08.


DWG NO.
도면번호 A-31

SHEET NO.
일련번호 □-□□□


dawoom
건축사사무소 다움건축
THE ARCHITECTS DESIGN GROUP
TEL. 02.414.6061 (代)
FAX. 02.414.6062

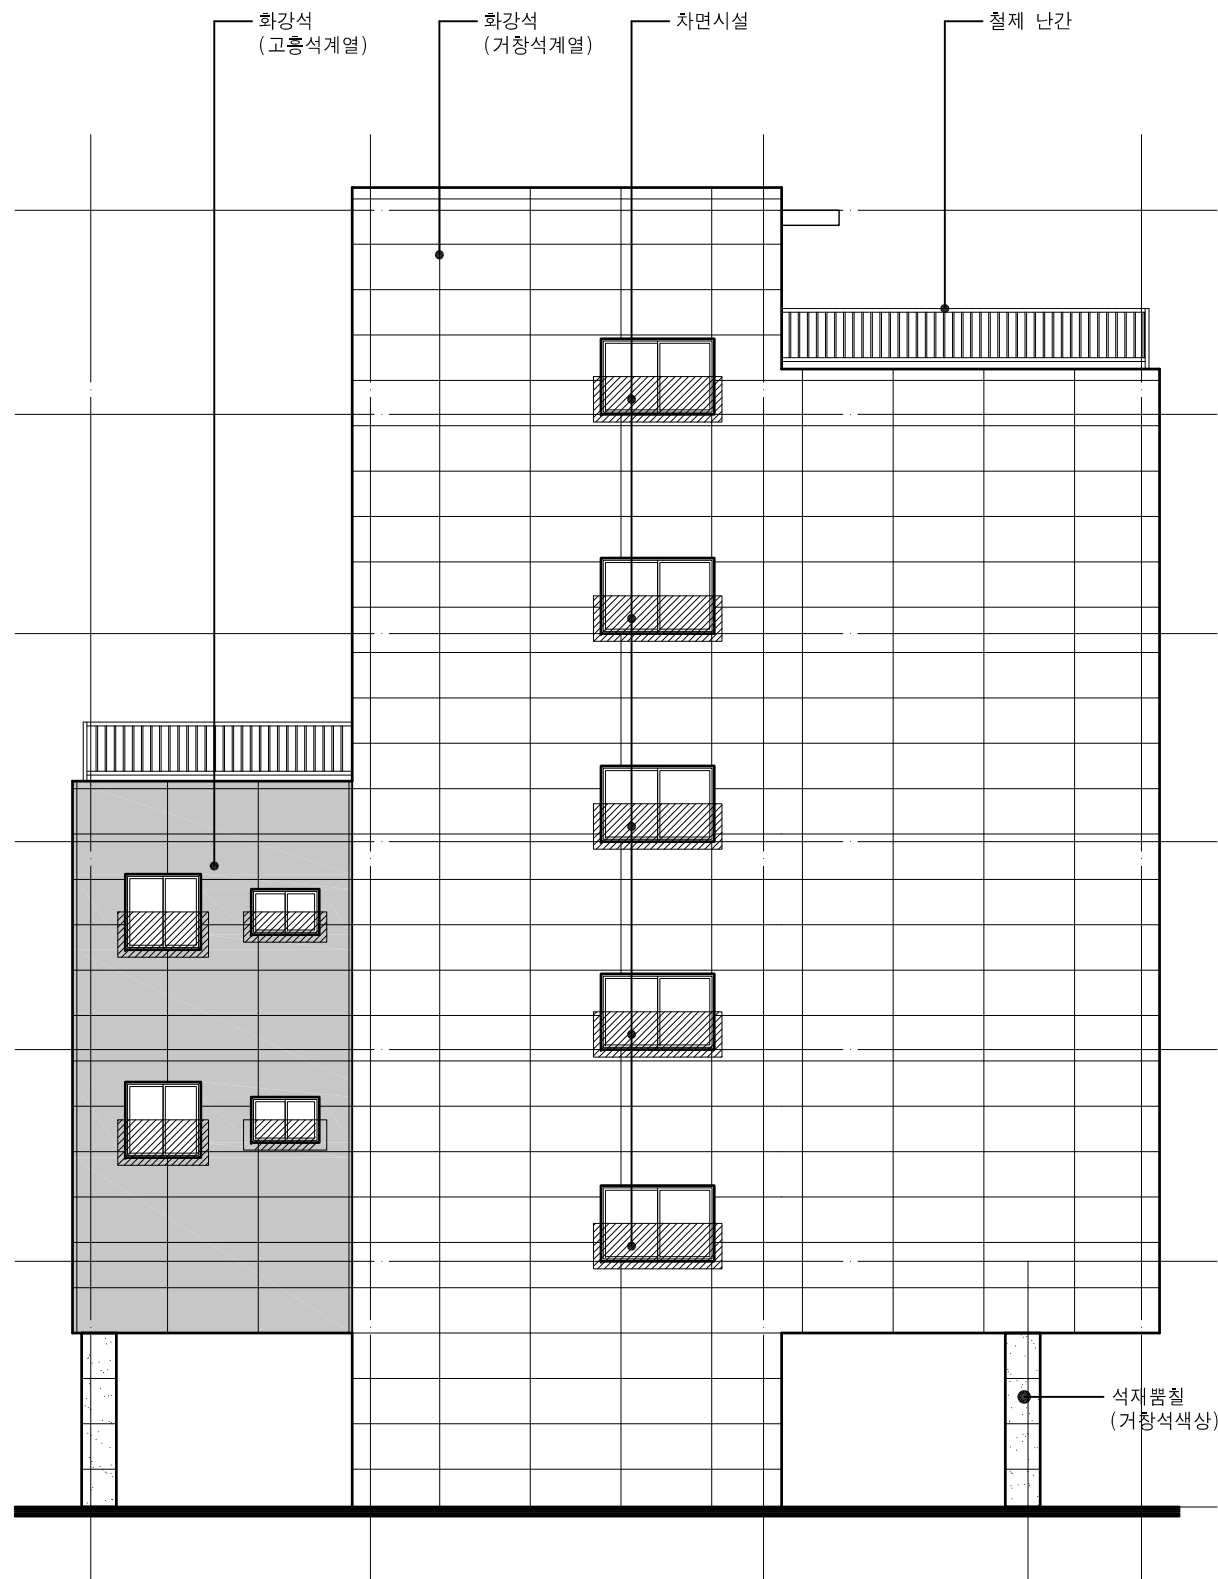

배 면 도
SCALE : A3 : 1/100

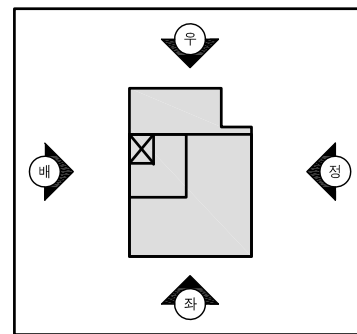

▽ 지붕층 바닥


▽ 5층 바닥

▽ 4층 바닥

▽ 3층 바닥

▽ 2층 바닥

▽ 1층 바닥

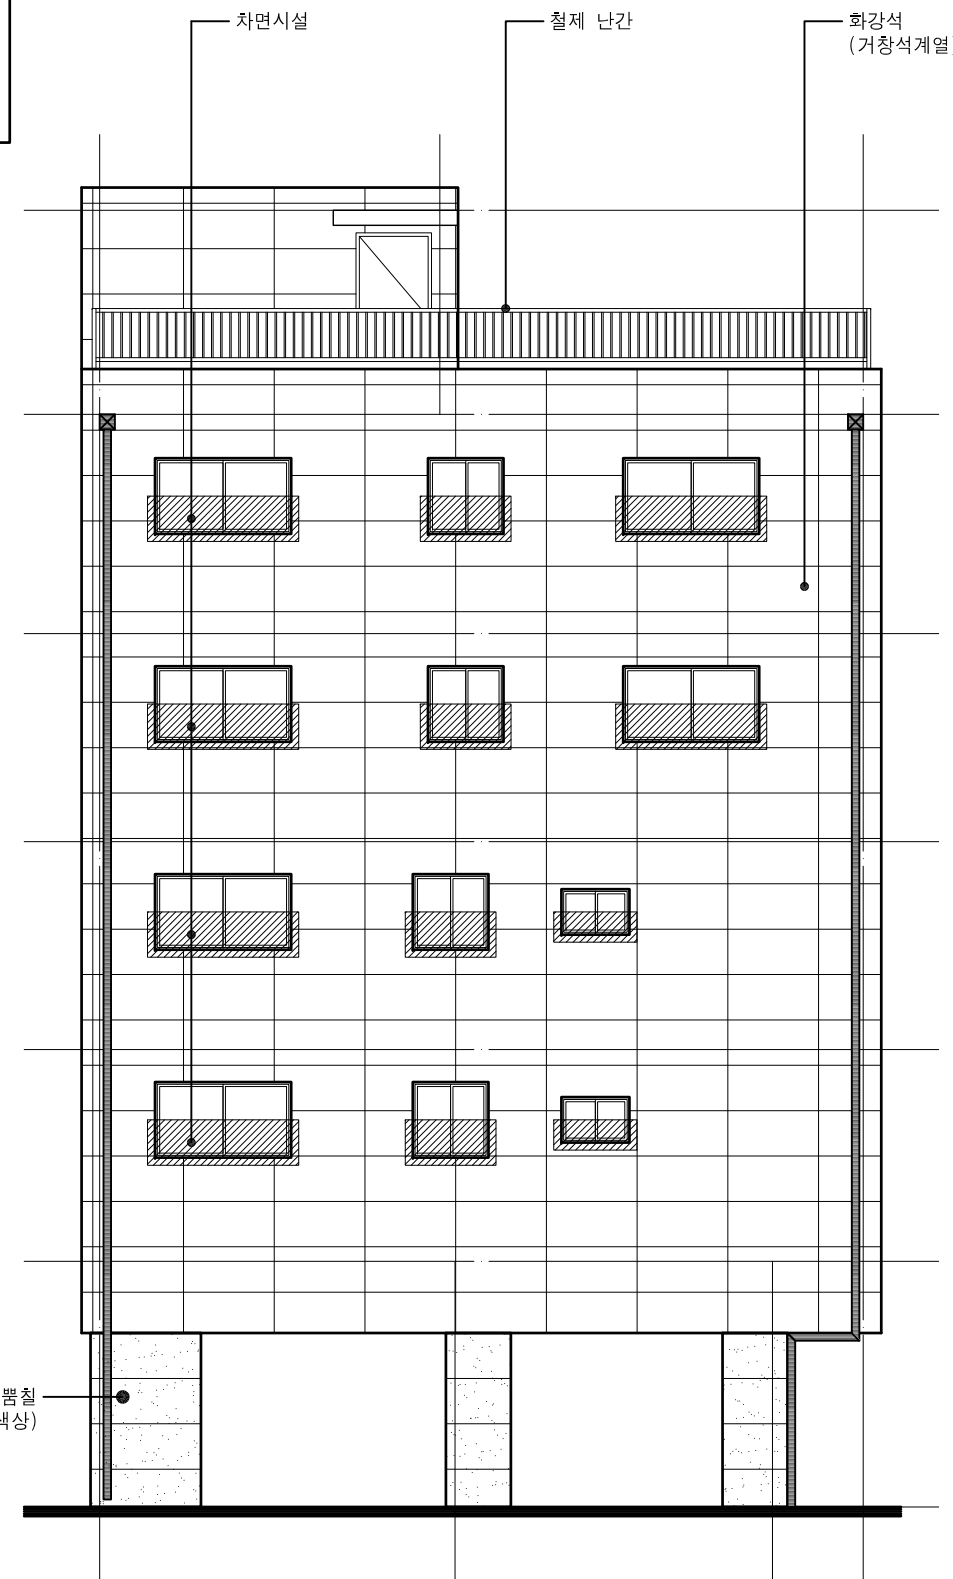

좌 측 면 도
SCALE : A3 : 1/100

PROJECT TITLE
사업명칭

서초구 반포동 716-5호
도시형생활주택(소형주택)
신축공사

NAME OF DRAWING
도면명

입면도-2

NOTE
주 기

창호 PVC 블랙

NO. ▲ REVISIONS ▲ DATE
번호 수 명 일자

DESIGNED BY
설 계

CHECKED BY
심 사

APPROVED BY
승 인

CONSULTANTS
업 종 설 계

SCALE
축 척 1/100

DATE
일자 2022. 08.

DWG NO.
도면 번호 A-32

SHEET NO.
일련 번호 □-□□□

다움
dawoom
건축사사무소 다움건축
THE ARCHITECTS DESIGN GROUP
TEL. 02.414.6061 (代)
FAX. 02.414.6062