


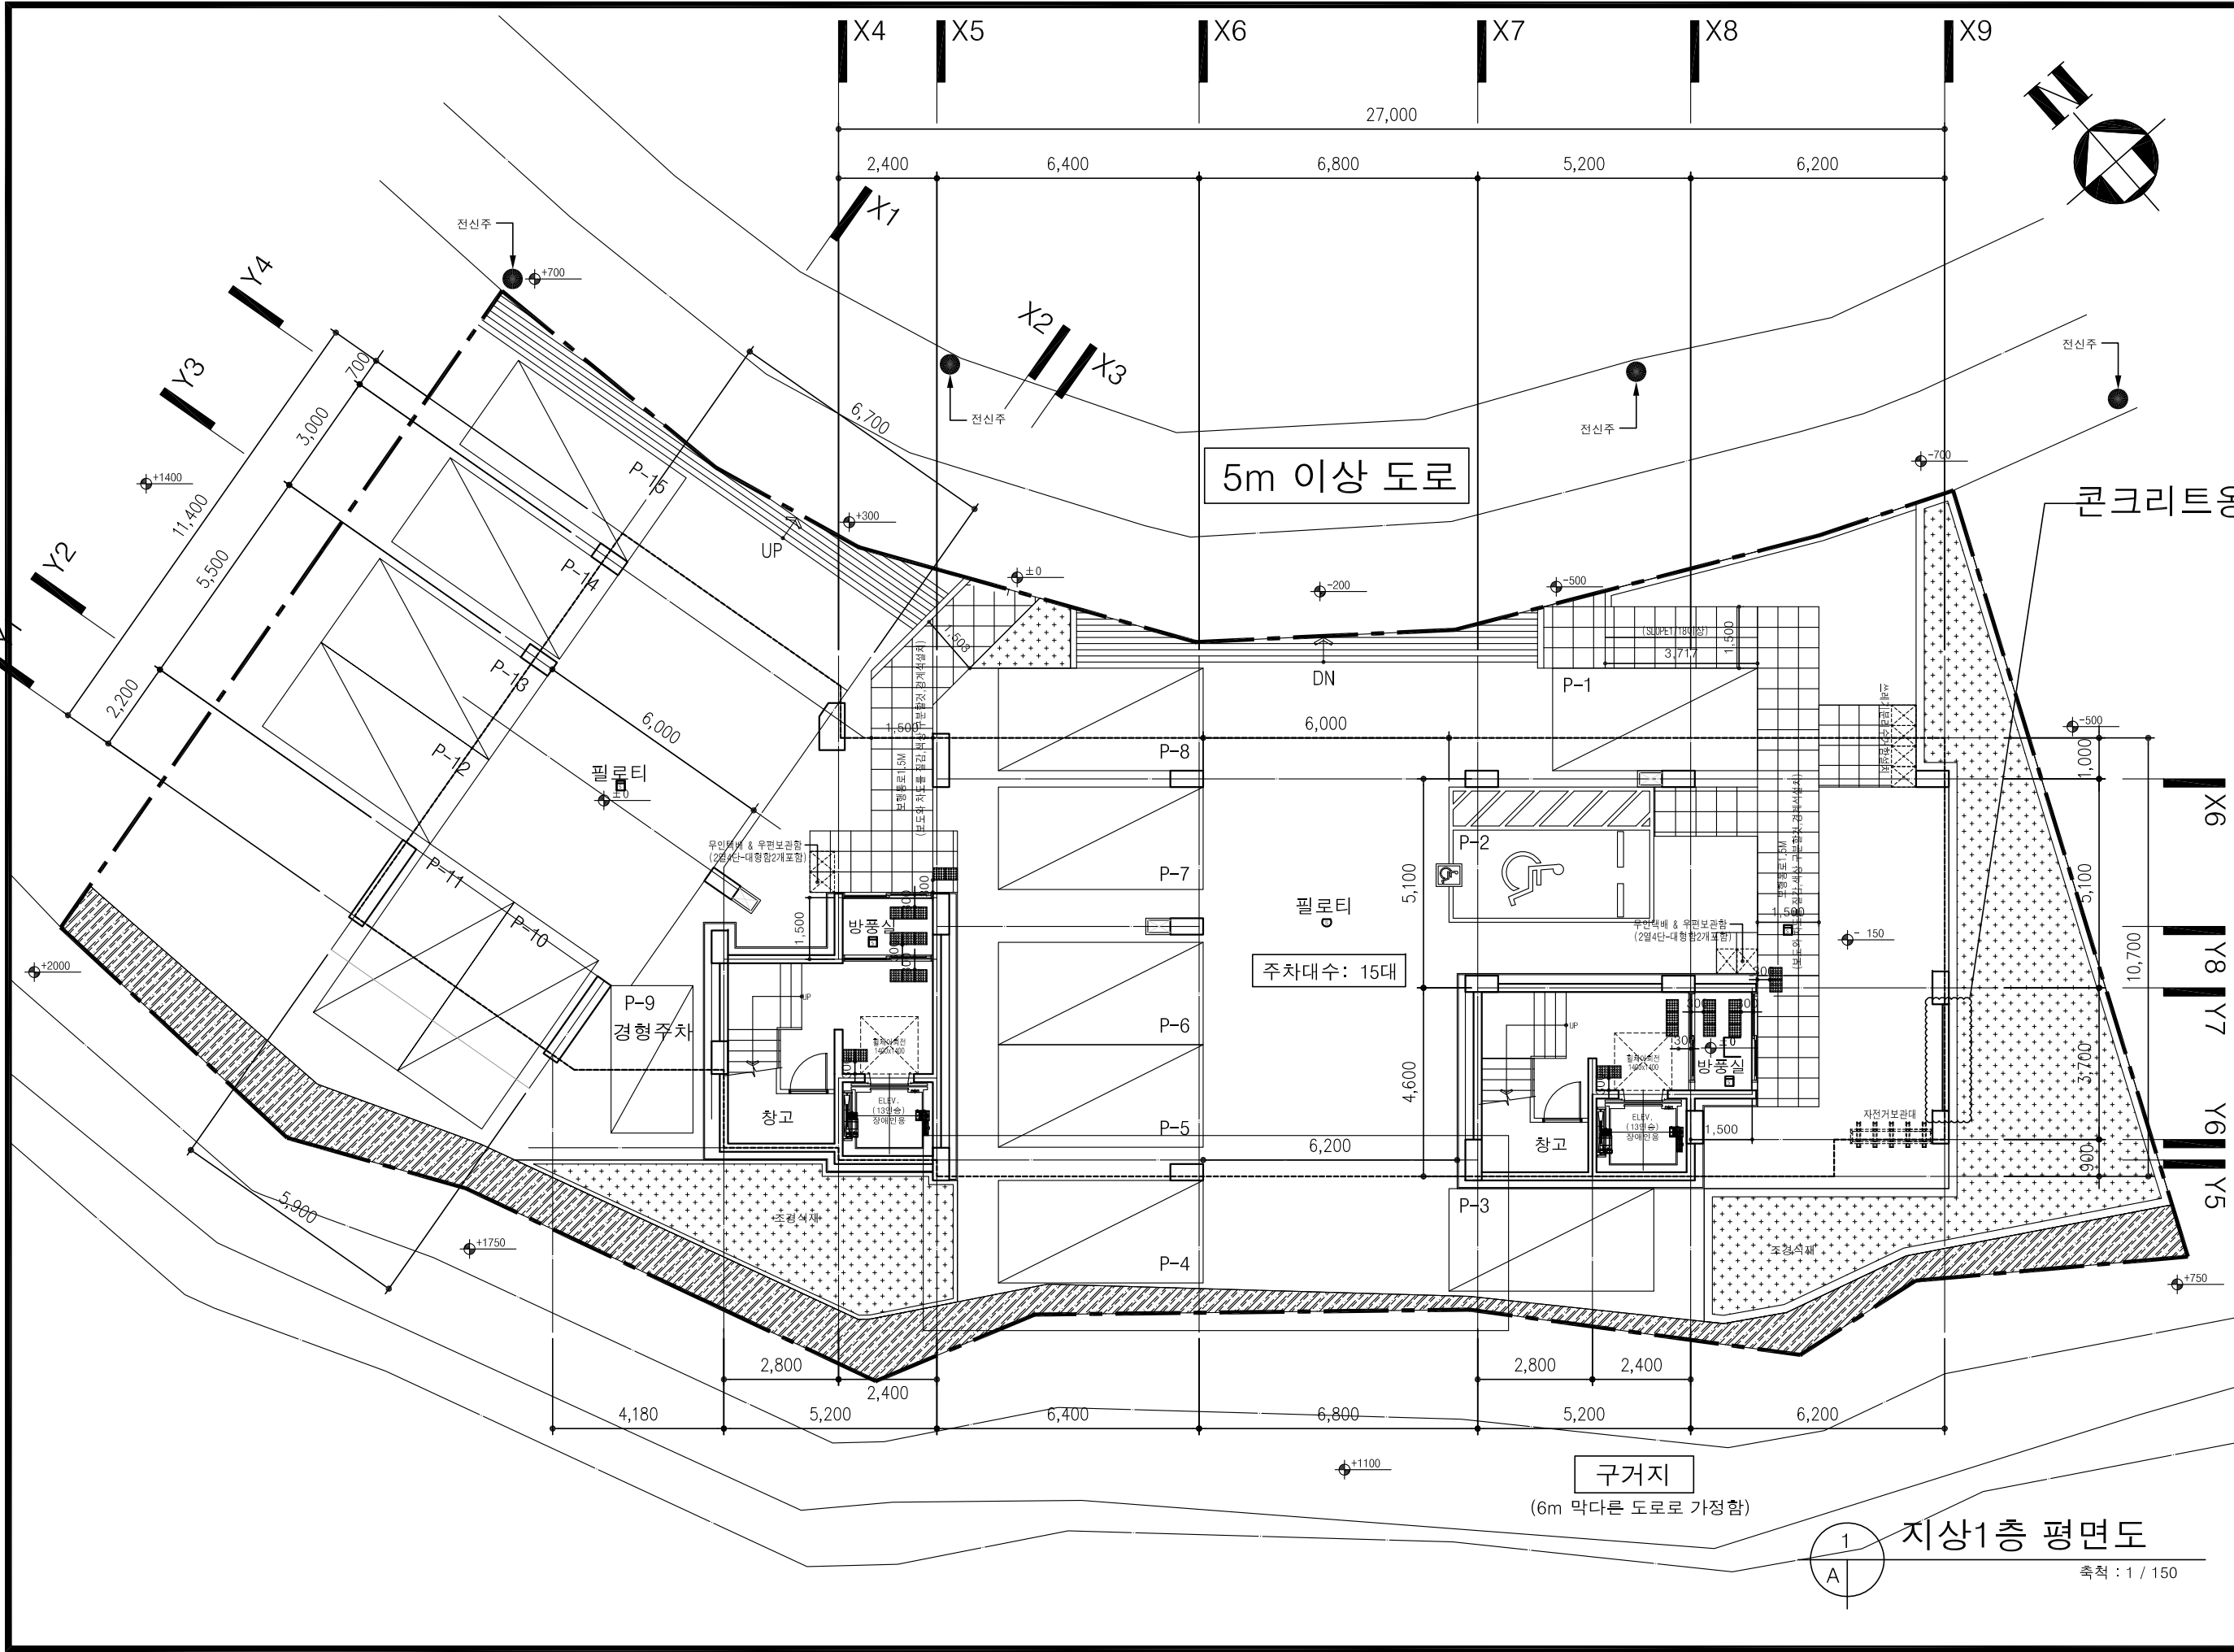

PROJECT TITLE
사업명칭

성북구 정릉동
692-12호외3필지
연립주택 신축공사

NAME OF DRAWING
도면명

지상1층 평면도

NOTE
주 기

단독경보감지기(연가식)

단독경보감지기(열감지)

ABC분말소화기(2.5KG)

가속설검지기

차면시설

보일러

에어컨 설비기

NO. 1
번호

REVISIONS
수정

DATE
일 자

DESIGNED BY
설 계

CHECKED BY
심 사

APPROVED BY
승 인

CONSULTANTS
합 동 설 계

SCALE
축척

A3 : 1 / 150

DATE
일 자

2023.07.

SHEET NO.
시트 번호

DWG NO.
도면 번호

A-011

sig.A


(주)건축사사무소 시그에이

THE ARCHITECTS GROUP

TEL. 02.541.5516

FAX. 02.512.2882

1
A 지상1층 평면도
축척 : 1 / 150

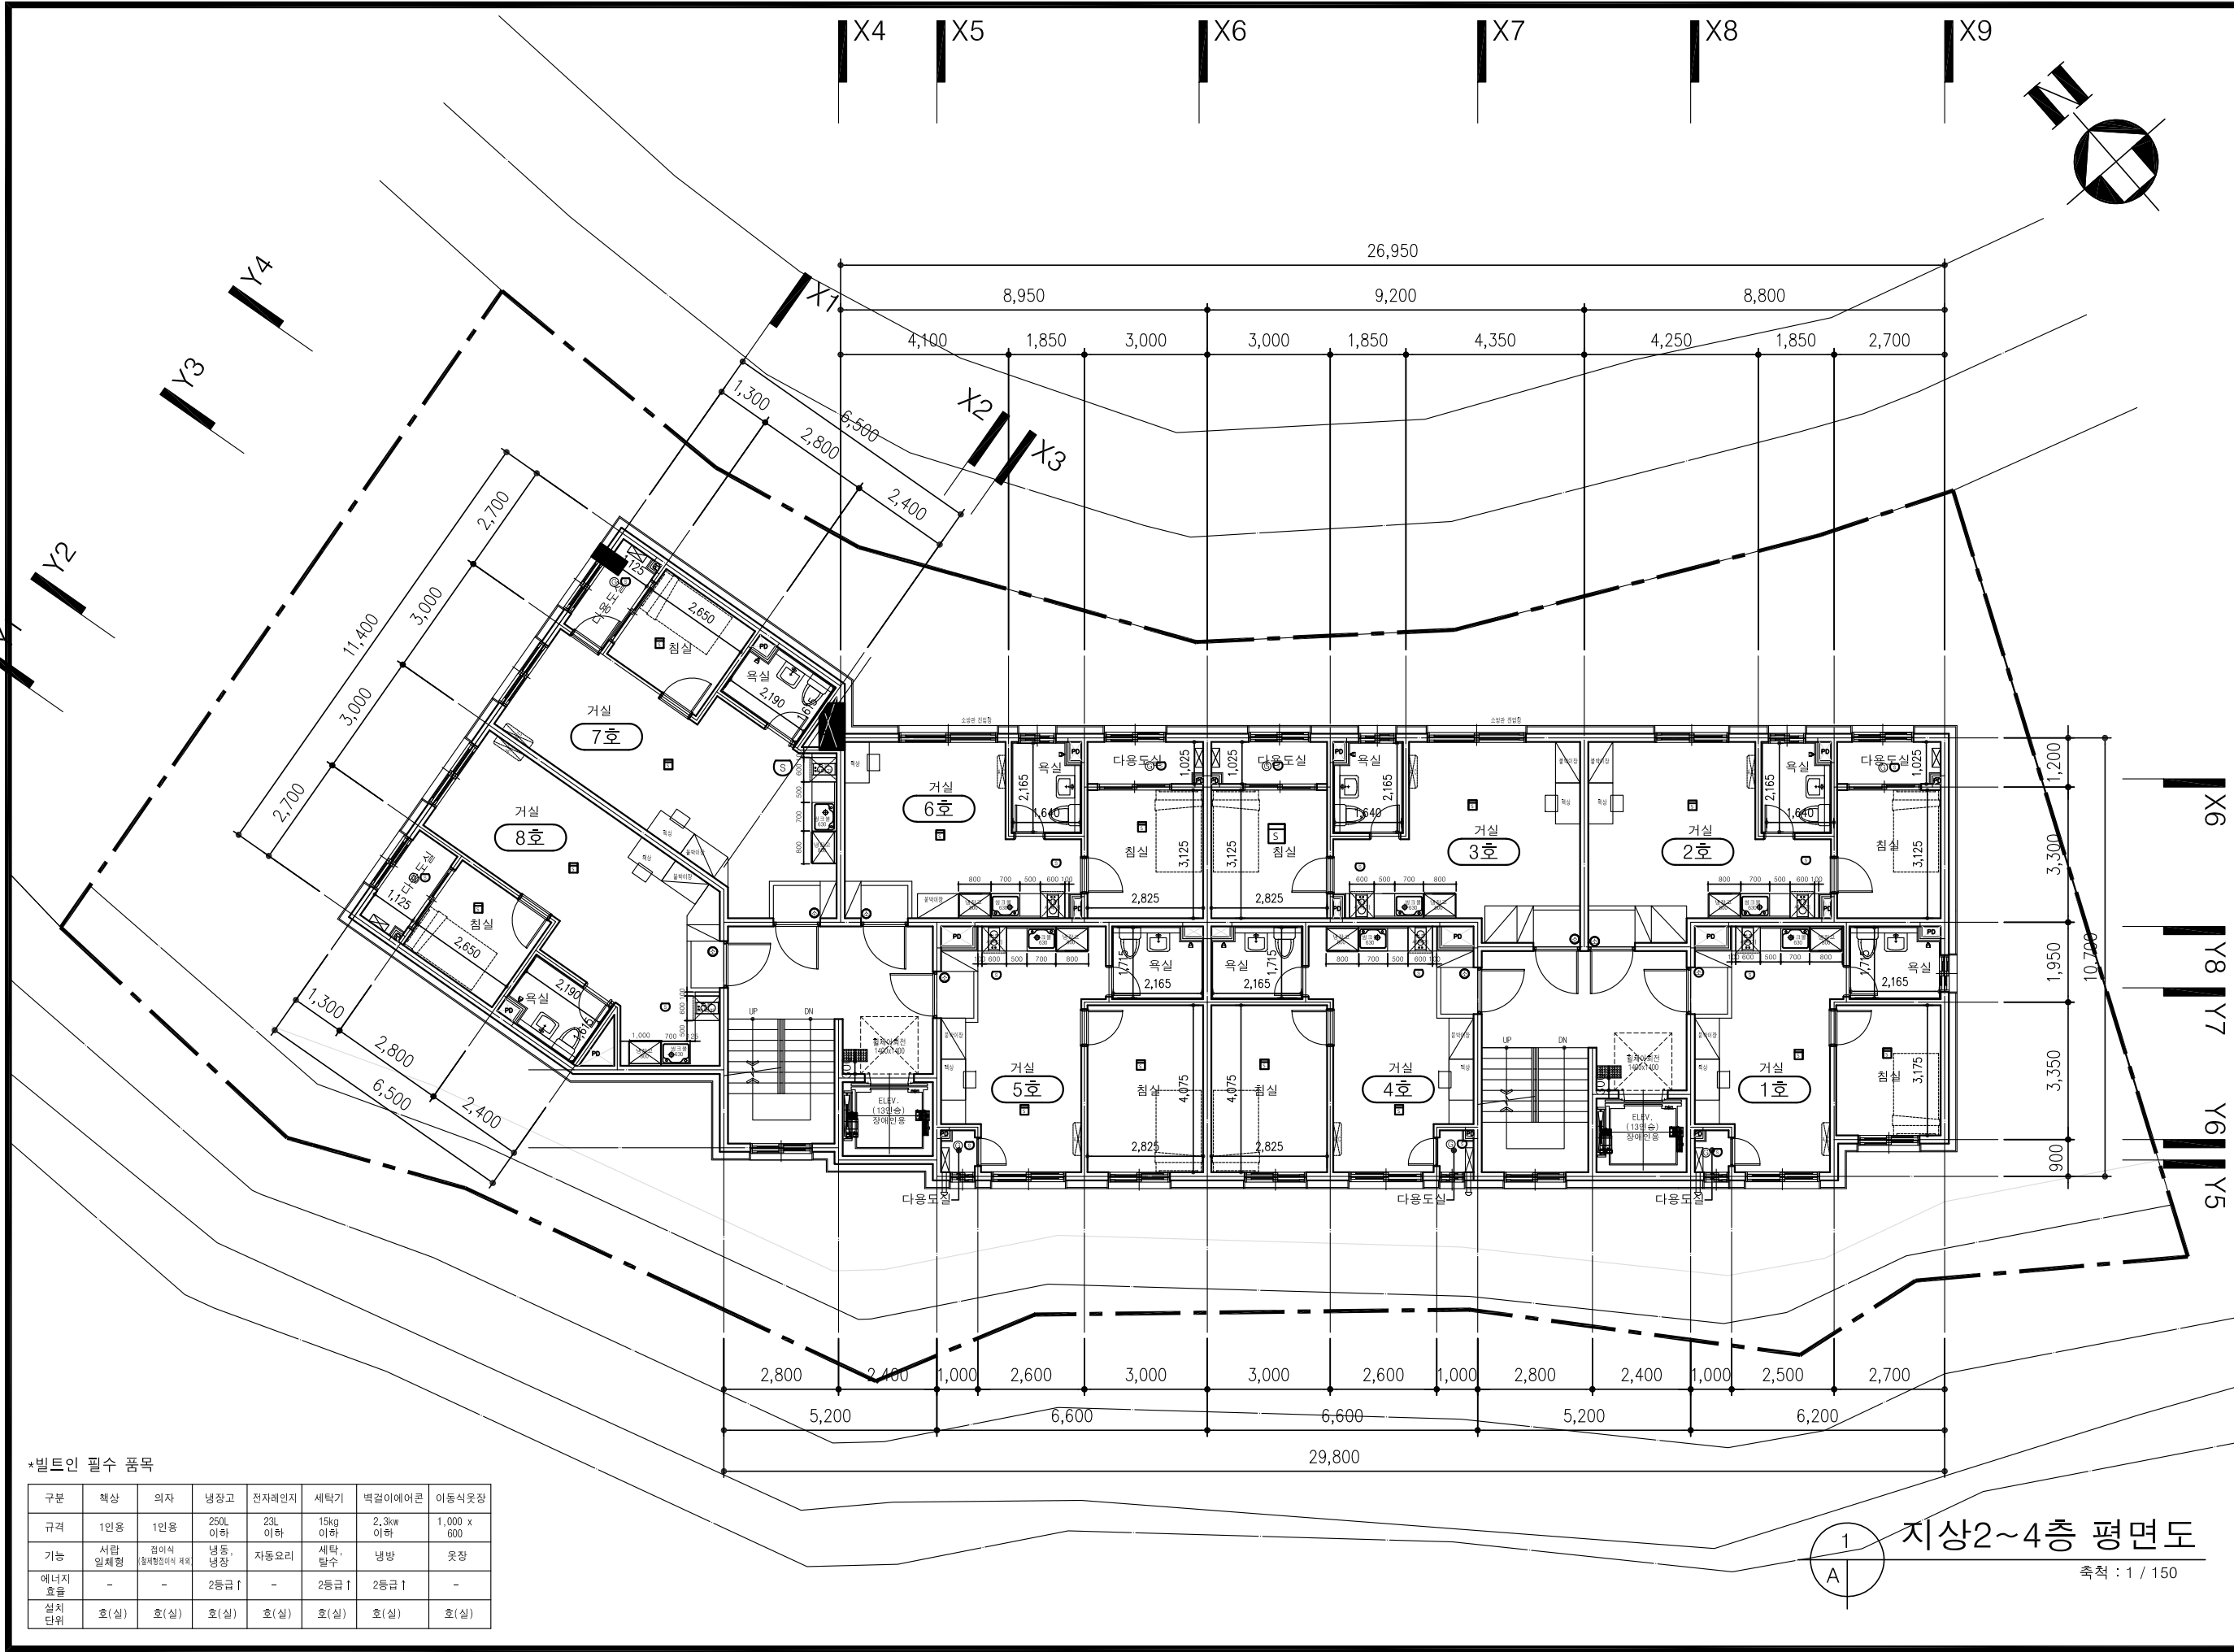

*빌트인 필수 품목

구분	책상	의자	냉장고	전자레인지	세탁기	벽걸이에어콘	이동식옷장
규격	1인용	1인용	250L 이하	23L 이하	15kg 이하	2.3kW 이하	1,000 x 600
기능	서랍	접이식	냉동, 냉장	자동요리	세탁, 탈수	냉방	옷장
에너지효율	-	-	2등급 I	-	2등급 I	2등급 I	-
설치단위	호(실)	호(실)	호(실)	호(실)	호(실)	호(실)	호(실)

PROJECT TITLE
사업명칭

성북구 정릉동
692-12호외3필지
연립주택 신축공사

NAME OF DRAWING
도면명

지상2~4층 평면도

NOTE
주 기

단독경보감지기(연가식)
단독경보감지기(열감지)
ABC분말소화기(2.5KG)
가스누설경보기
차면시설
보일러
에어컨 설비기

NO. REVISIONS DATE
번호 ▲ 수 정 ▲ 일 자

DESIGNED BY
설 계

CHECKED BY
심 사

APPROVED BY
승 인

CONSULTANTS
합 동 설 계

SCALE
축척 A3 : 1 / 150

DATE
일 자 2023.07.

SHEET NO.
일련 번호

DWG NO.
도면 번호
A-012

1
A


지상2~4층 평면도

축척 : 1 / 150

sig.A

(주)건축사사무소 시그에이

THE ARCHITECTS GROUP
TEL. 02.541.5516
FAX. 02.512.2882

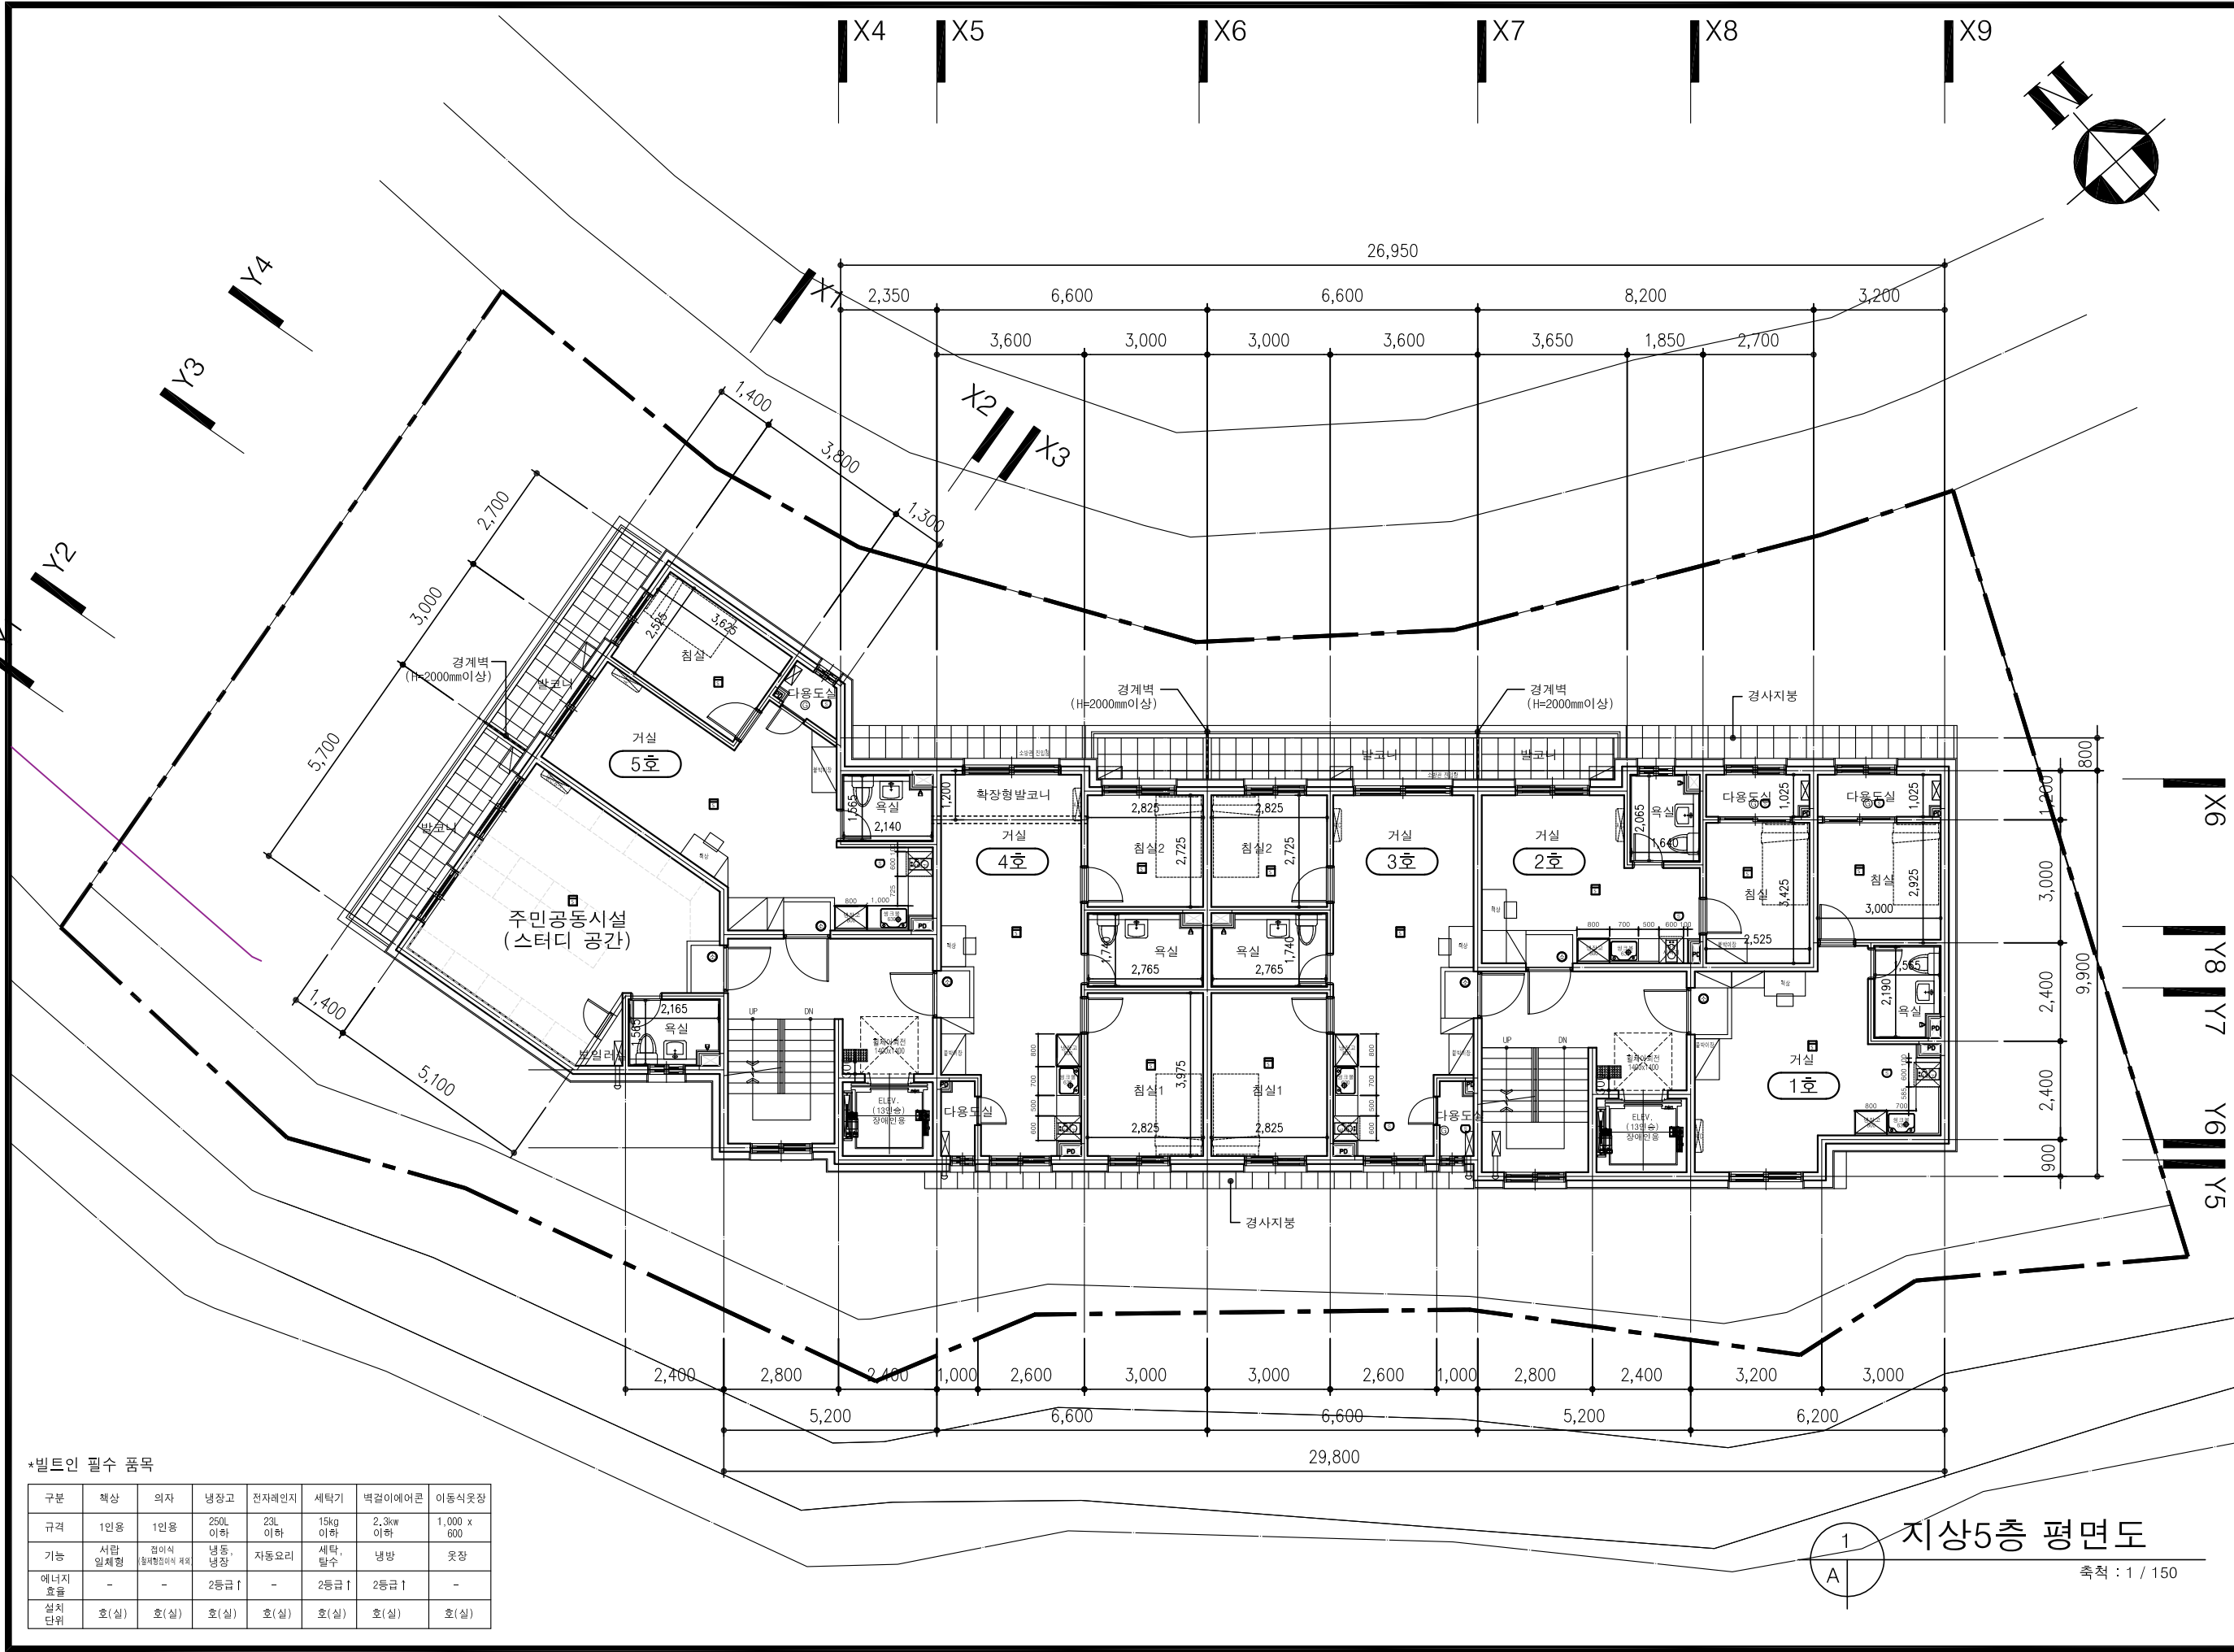

*빌트인 필수 품목

구분	책상	의자	냉장고	전자레인지	세탁기	벽걸이에어콘	이동식옷장
규격	1인용	1인용	250L 이하	23L 이하	15kg 이하	2.3kW 이하	1,000 x 600
기능 일체형	서랍 일체형	접이식 올래형임이체 제로	냉동, 냉장	자동요리	세탁, 탈수	냉방	옷장
에너지 효율	-	-	2등급 I	-	2등급 I	2등급 I	-
설치 단위	호(실)	호(실)	호(실)	호(실)	호(실)	호(실)	호(실)

PROJECT TITLE
사업명칭

성북구 정릉동
692-12호외3필지
연립주택 신축공사

NAME OF DRAWING
도면명

지상5층 평면도

NOTE
주 기

단독경보감지기(연가식)

단독경보감지기(열감지)

ABC분말소화기(2.5KG)

가스누설경보기

차면시설

보일러

에어컨 설외기

NO. 1
번호

REVISIONS
수정

DATE
일 자

DESIGNED BY
설 계

CHECKED BY
심 사

APPROVED BY
승 인

CONSULTANTS
합 동 설 계

SCALE
축척

A3 : 1 / 150

DATE
일 자

2023.07.

SHEET NO.
시트 번호

013

DWG NO.
도면 번호

1-013

1
A

지상5층 평면도

축척 : 1 / 150


sig.A

(주)건축사사무소 시그에이

THE ARCHITECTS GROUP

TEL. 02.541.5516

FAX. 02.512.2882

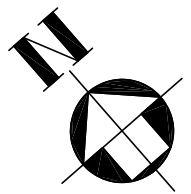

PROJECT TITLE
사업명칭

성북구 정릉동
692-12호외3필지
연립주택 신축공사

NAME OF DRAWING
도면명

옥탑 지붕 평면도

- NOTE
주 기
- ▼ ▼
- 단독경보감지기(연가식)
 - 단독경보감지기(열감지)
 - ABC분말소화기(2.5KG)
 - 가스누설경보기
 - 차면시설
 - 보일러
 - 에어컨 실외기

NO. ▲ REVISIONS ▲ DATE
번호 수정 일자

DESIGNED BY
설 계

CHECKED BY
심 사

APPROVED BY
승 인

CONSULTANTS
합 동 설 계

SCALE
축 척 A3 : 1 / 150

DATE
일 자 2023.07.



SHEET NO.
일련 번호

DWG NO.
도면 번호 A-015

 sig.A


(주)건축사사무소 시그에이

THE ARCHITECTS GROUP
TEL. 02.541.5516
FAX. 02.512.2882

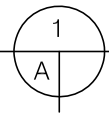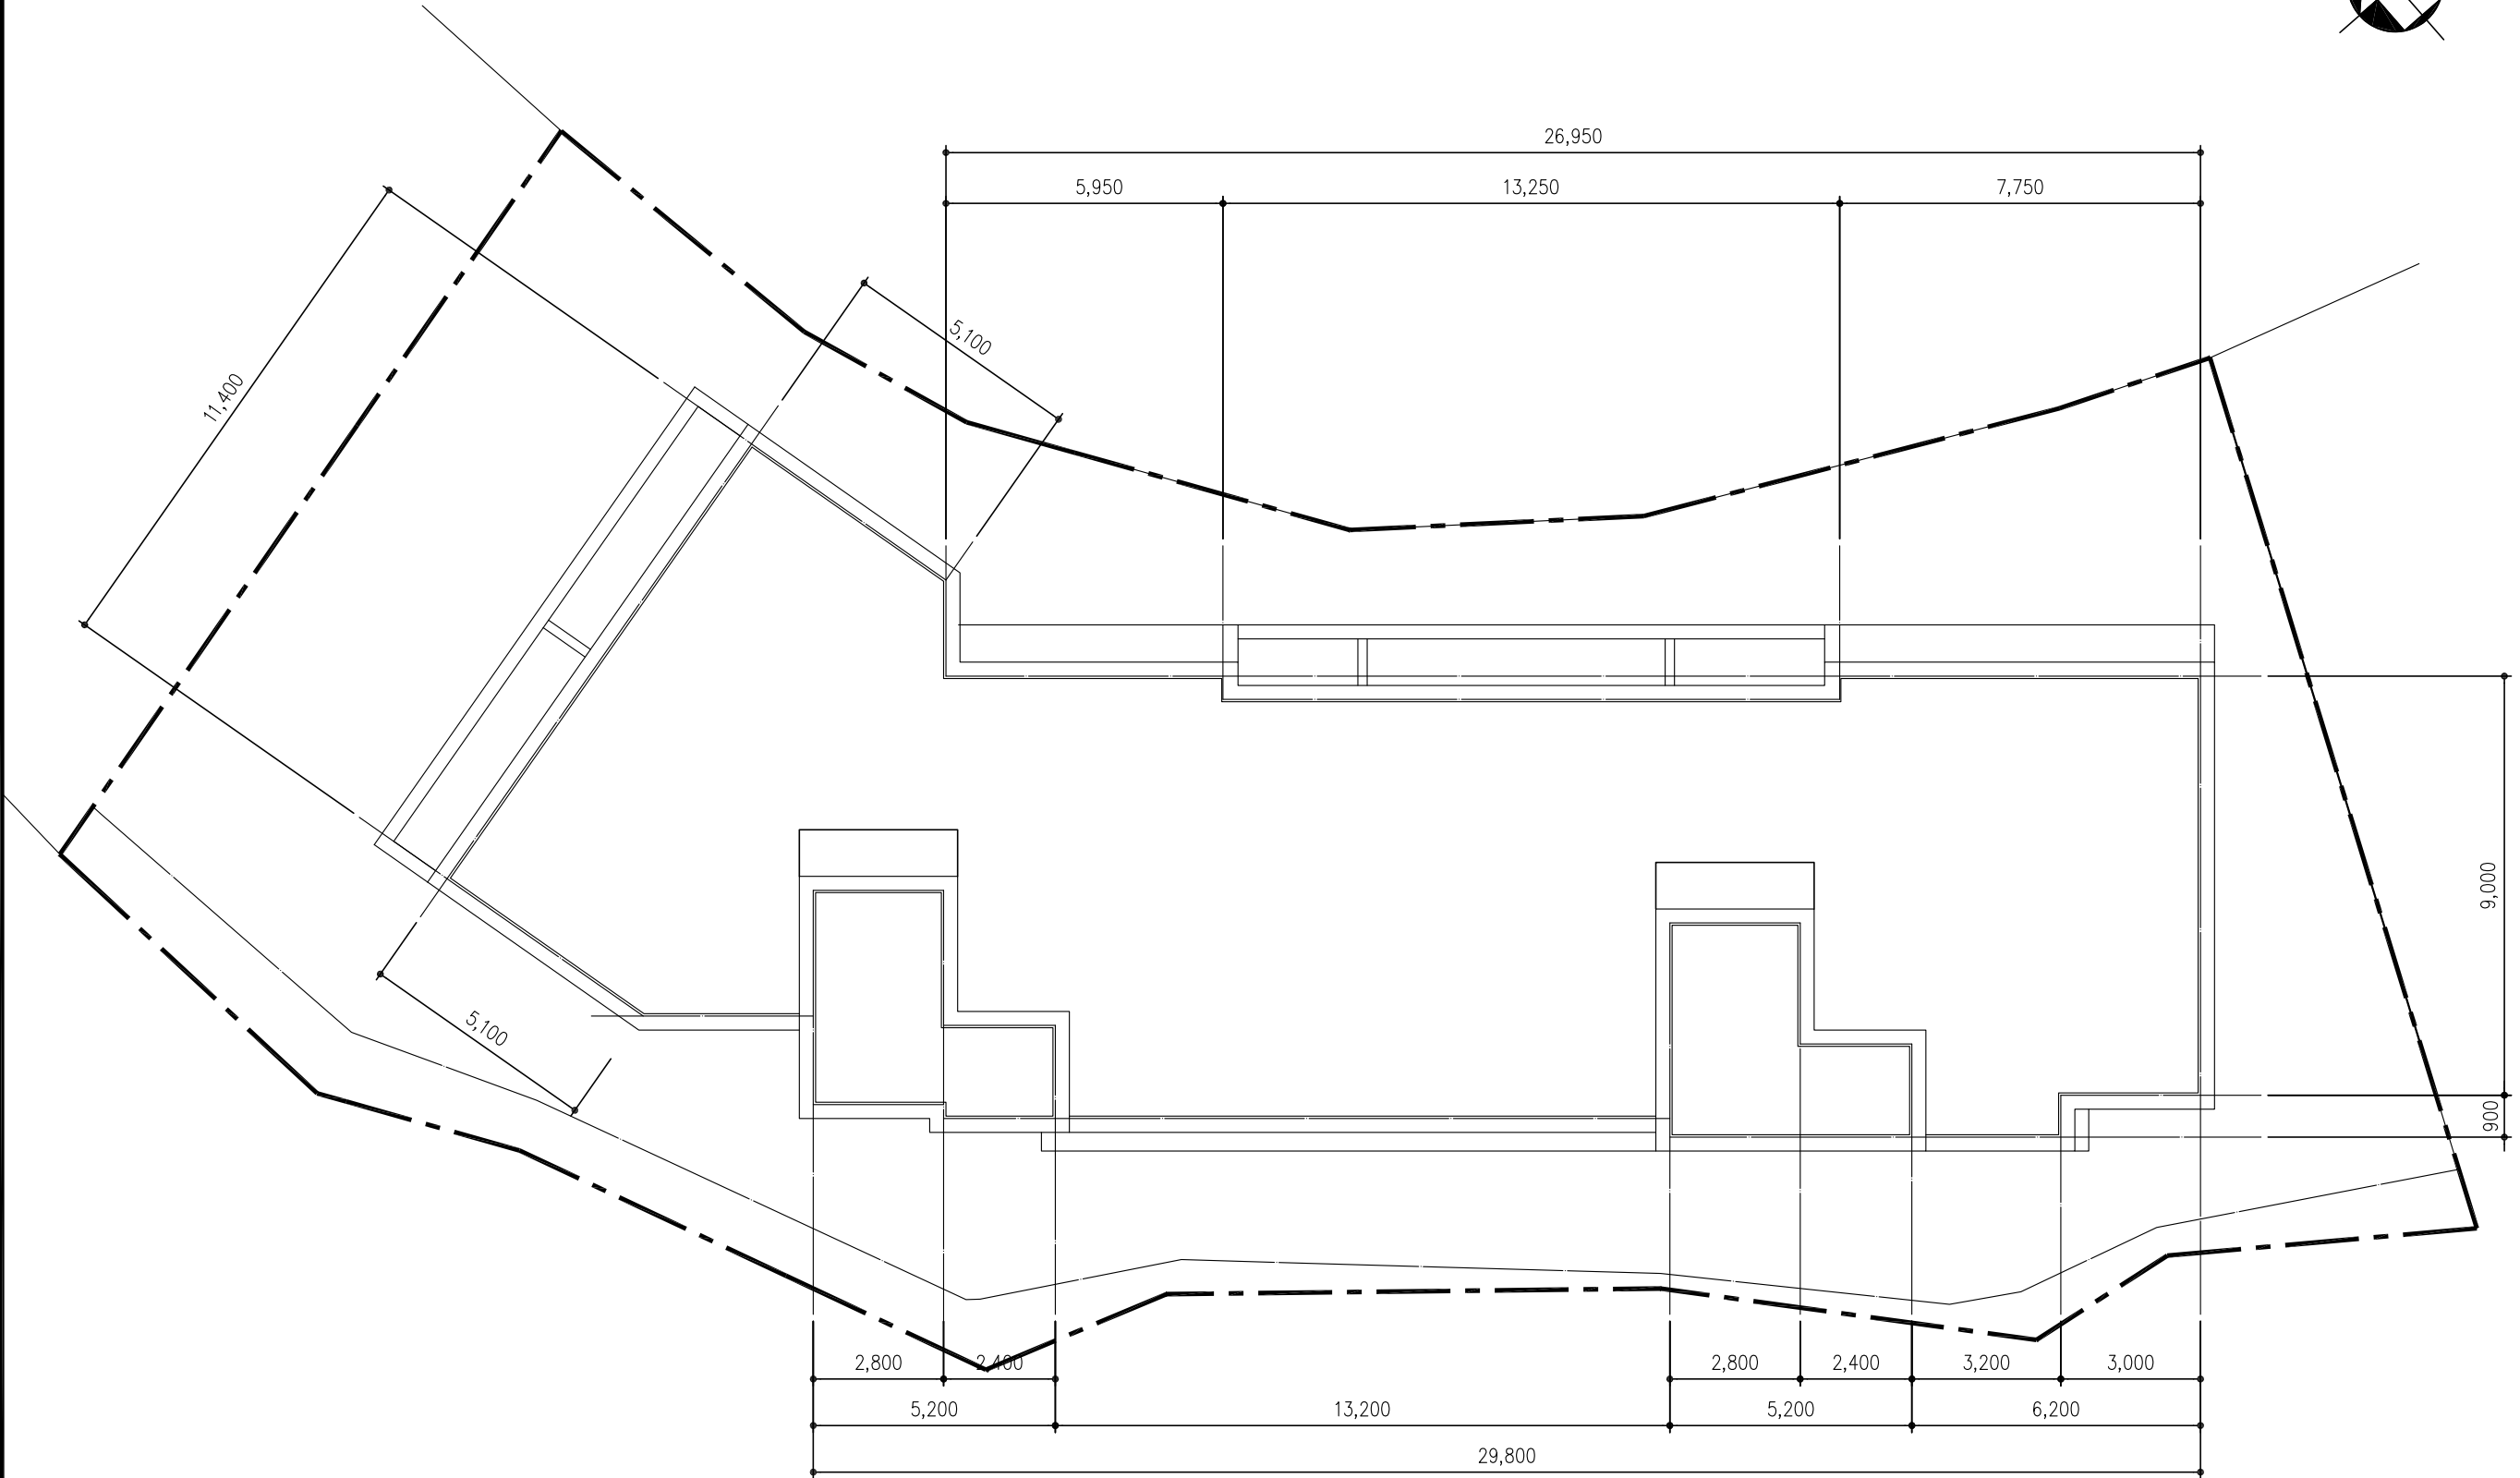

옥탑 지붕 평면도

축척 : 1 / 150

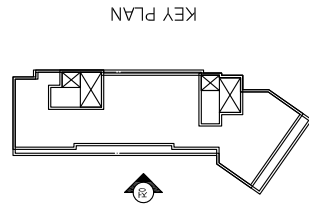

1
A 정 면 도
축척 : 1 / 150

PROJECT TITLE
사업명칭

성북구 정릉동
692-12호외3필지
연립주택 신축공사

NAME OF DRAWING
도면명

정면도

NOTE
주 기

NO. ▲ REVISIONS ▲ DATE
번호 수정 일자

DESIGNED BY
설 계

CHECKED BY
심 사

APPROVED BY
승 인

CONSULTANTS
합 동 설 계

SCALE
축척 A3 : 1 /

DATE
일 자 2023.07.


SHEET NO.
일련 번호

DWG NO.
도면 번호

A-016



(주)건축사사무소 시그에이
THE ARCHITECTS GROUP
TEL. 02.541.5516
FAX. 02.512.2882

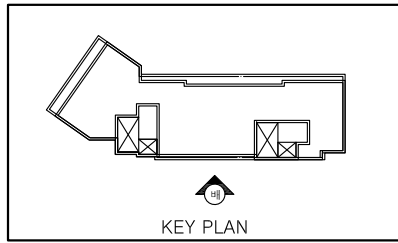

1
A
배 면 도
축척 : 1 / 150

PROJECT TITLE
사업명칭

성북구 정릉동
692-12호외3필지
연립주택 신축공사

NAME OF DRAWING
도면명

배 면 도

NOTE
주 기

▼ ▼

NO. ▲ REVISIONS ▲ DATE
번호 수정 일자

DESIGNED BY
설 계

CHECKED BY
심 사

APPROVED BY
승 인

CONSULTANTS
합 동 설 계

SCALE 축척 A3 : 1 / 150

DATE 일자 2023.07.


SHEET NO.
일련 번호

ORIG. NO.
도면 번호


A-017

sig.A

(주)건축사사무소 시그에이
THE ARCHITECTS GROUP
TEL. 02.541.5516
FAX. 02.512.2882

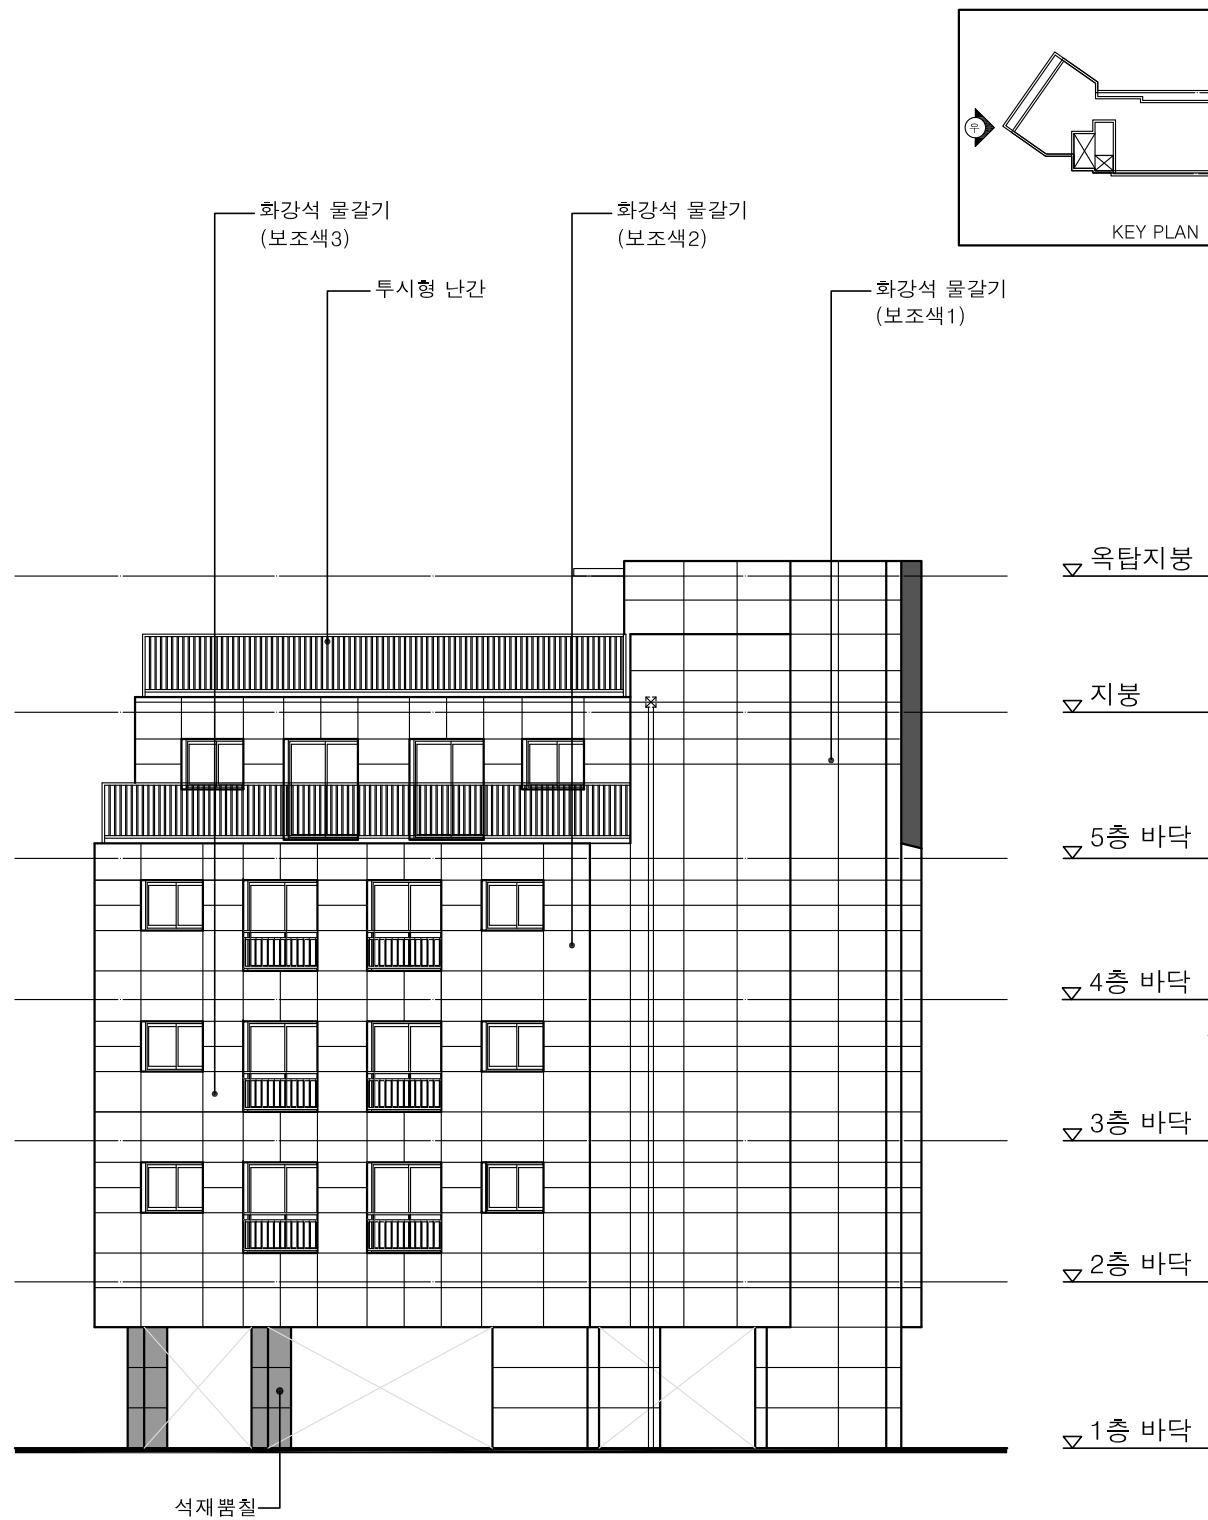

1 우 측 면 도
축척 : 1 / 150

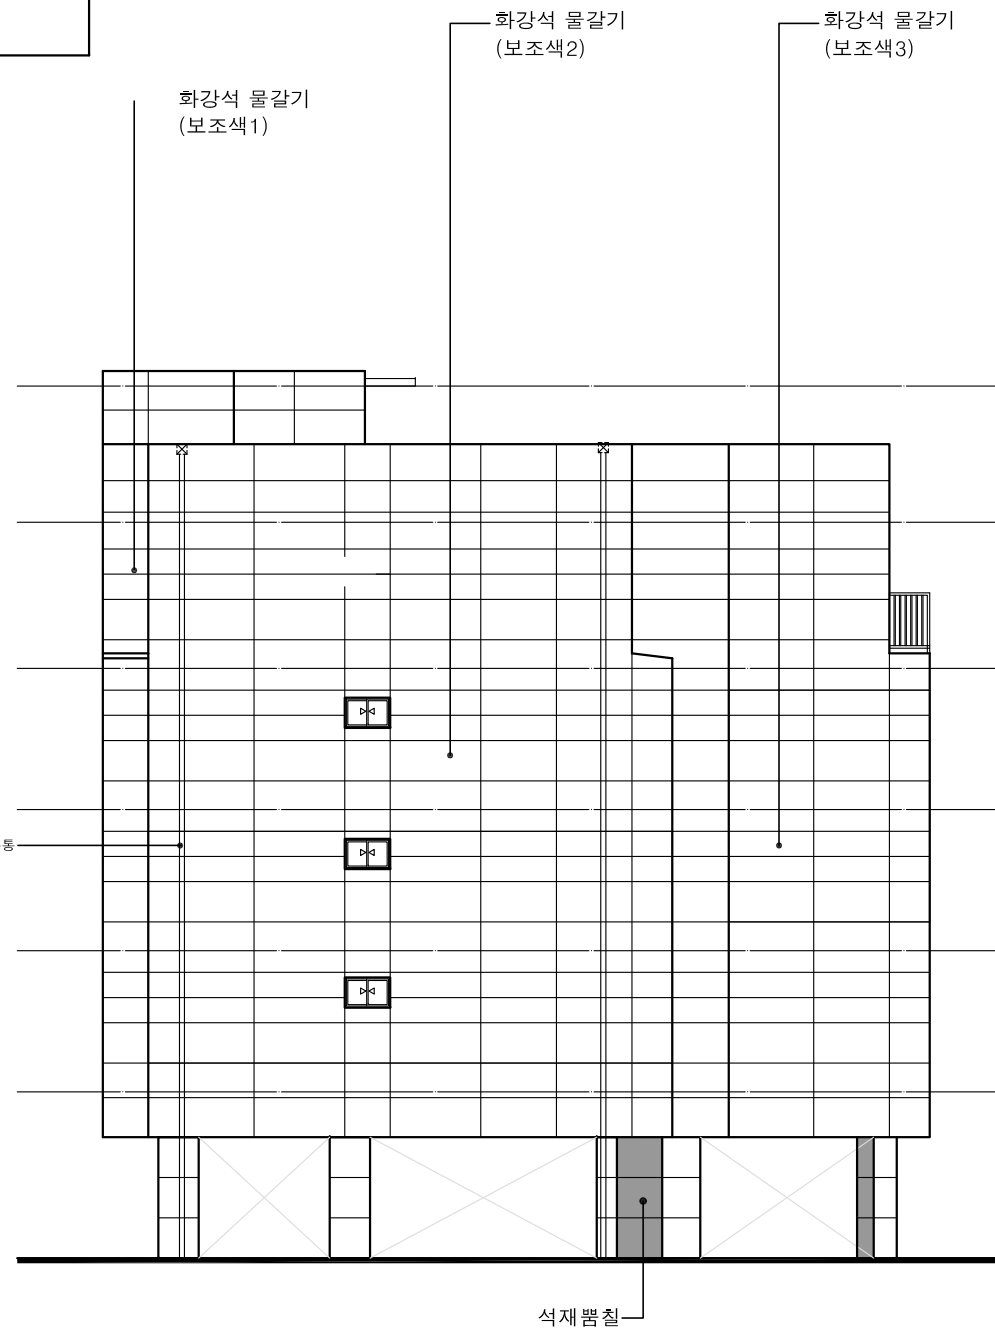

2 좌 측 면 도
축척 : 1 / 150

PROJECT TITLE
사 업 명 칭

성북구 정릉동
692-12호외3필지
연립주택 신축공사

NAME OF DRAWING
도 면 명

우측 면도, 좌측 면도

NOTE
주 기

▼ ▼

NO. ▲ REVISIONS ▲ DATE
번호 수정 일자

DESIGNED BY
설 계

CHECKED BY
심 사

APPROVED BY
승 인

CONSULTANTS
합 동 설 계

SCALE 축척 A3 : 1 / 150

DATE 일자 2023.07.

SHEET NO.
일련 번호

DWG NO.
도면 번호 A-018

sig.A

(주)건축사사무소 시그에이
THE ARCHITECTS GROUP
TEL. 02.541.5516
FAX. 02.512.2882