


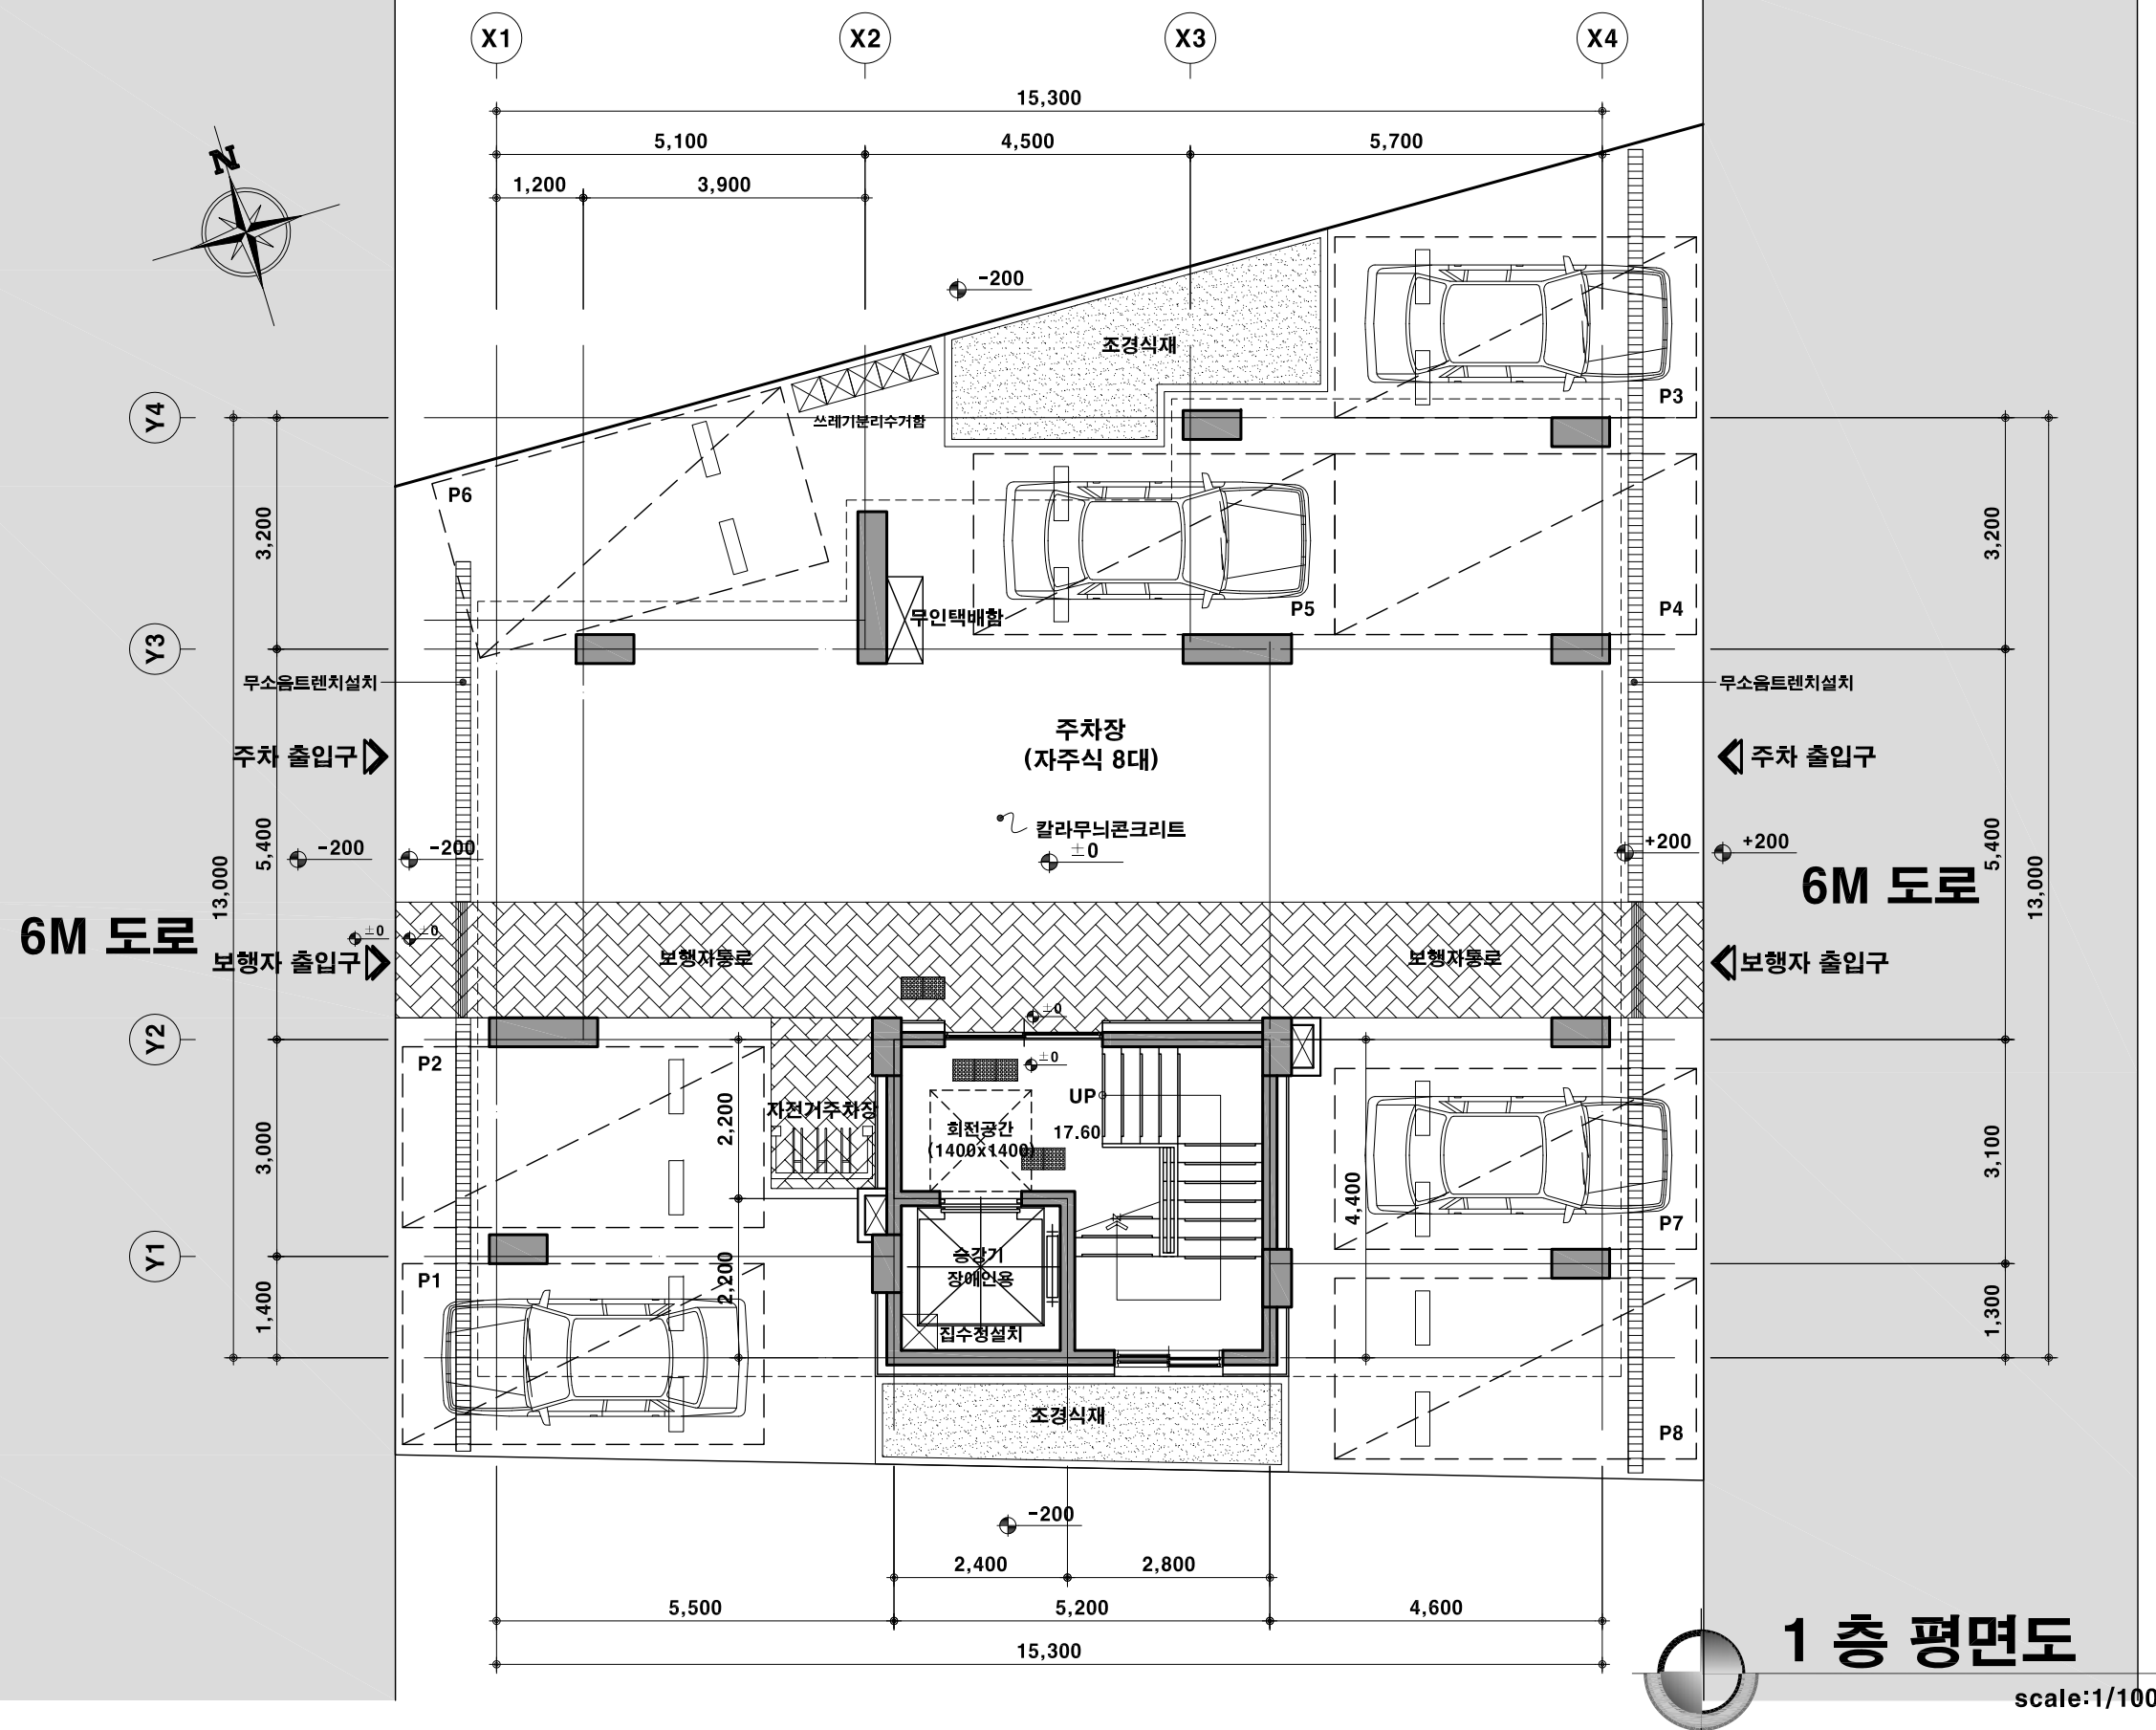

(주)다림 건축사사무소
Architects & Engineers Darim
Tel: (02) 2066-5599, Fax: (02) 2066-5598




NO	DATE	REVISION DESCRIPTION	DRWN	CHK'D	APPD
01		사용승인			

PROJECT TITLE
공사명 송파구 오금동 119-18번지
도시형생활주택(소형주택)
신축공사

CHK'D BY	SCALE 1 / 100
	DATE 2026.01
	DRWN BY

DRAWING TITLE
도면명 1층 평면도

B.C.C NO	JOB NO	APPROVE D BY
DRWG NO	A - 015	DESIGNED BY

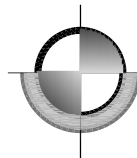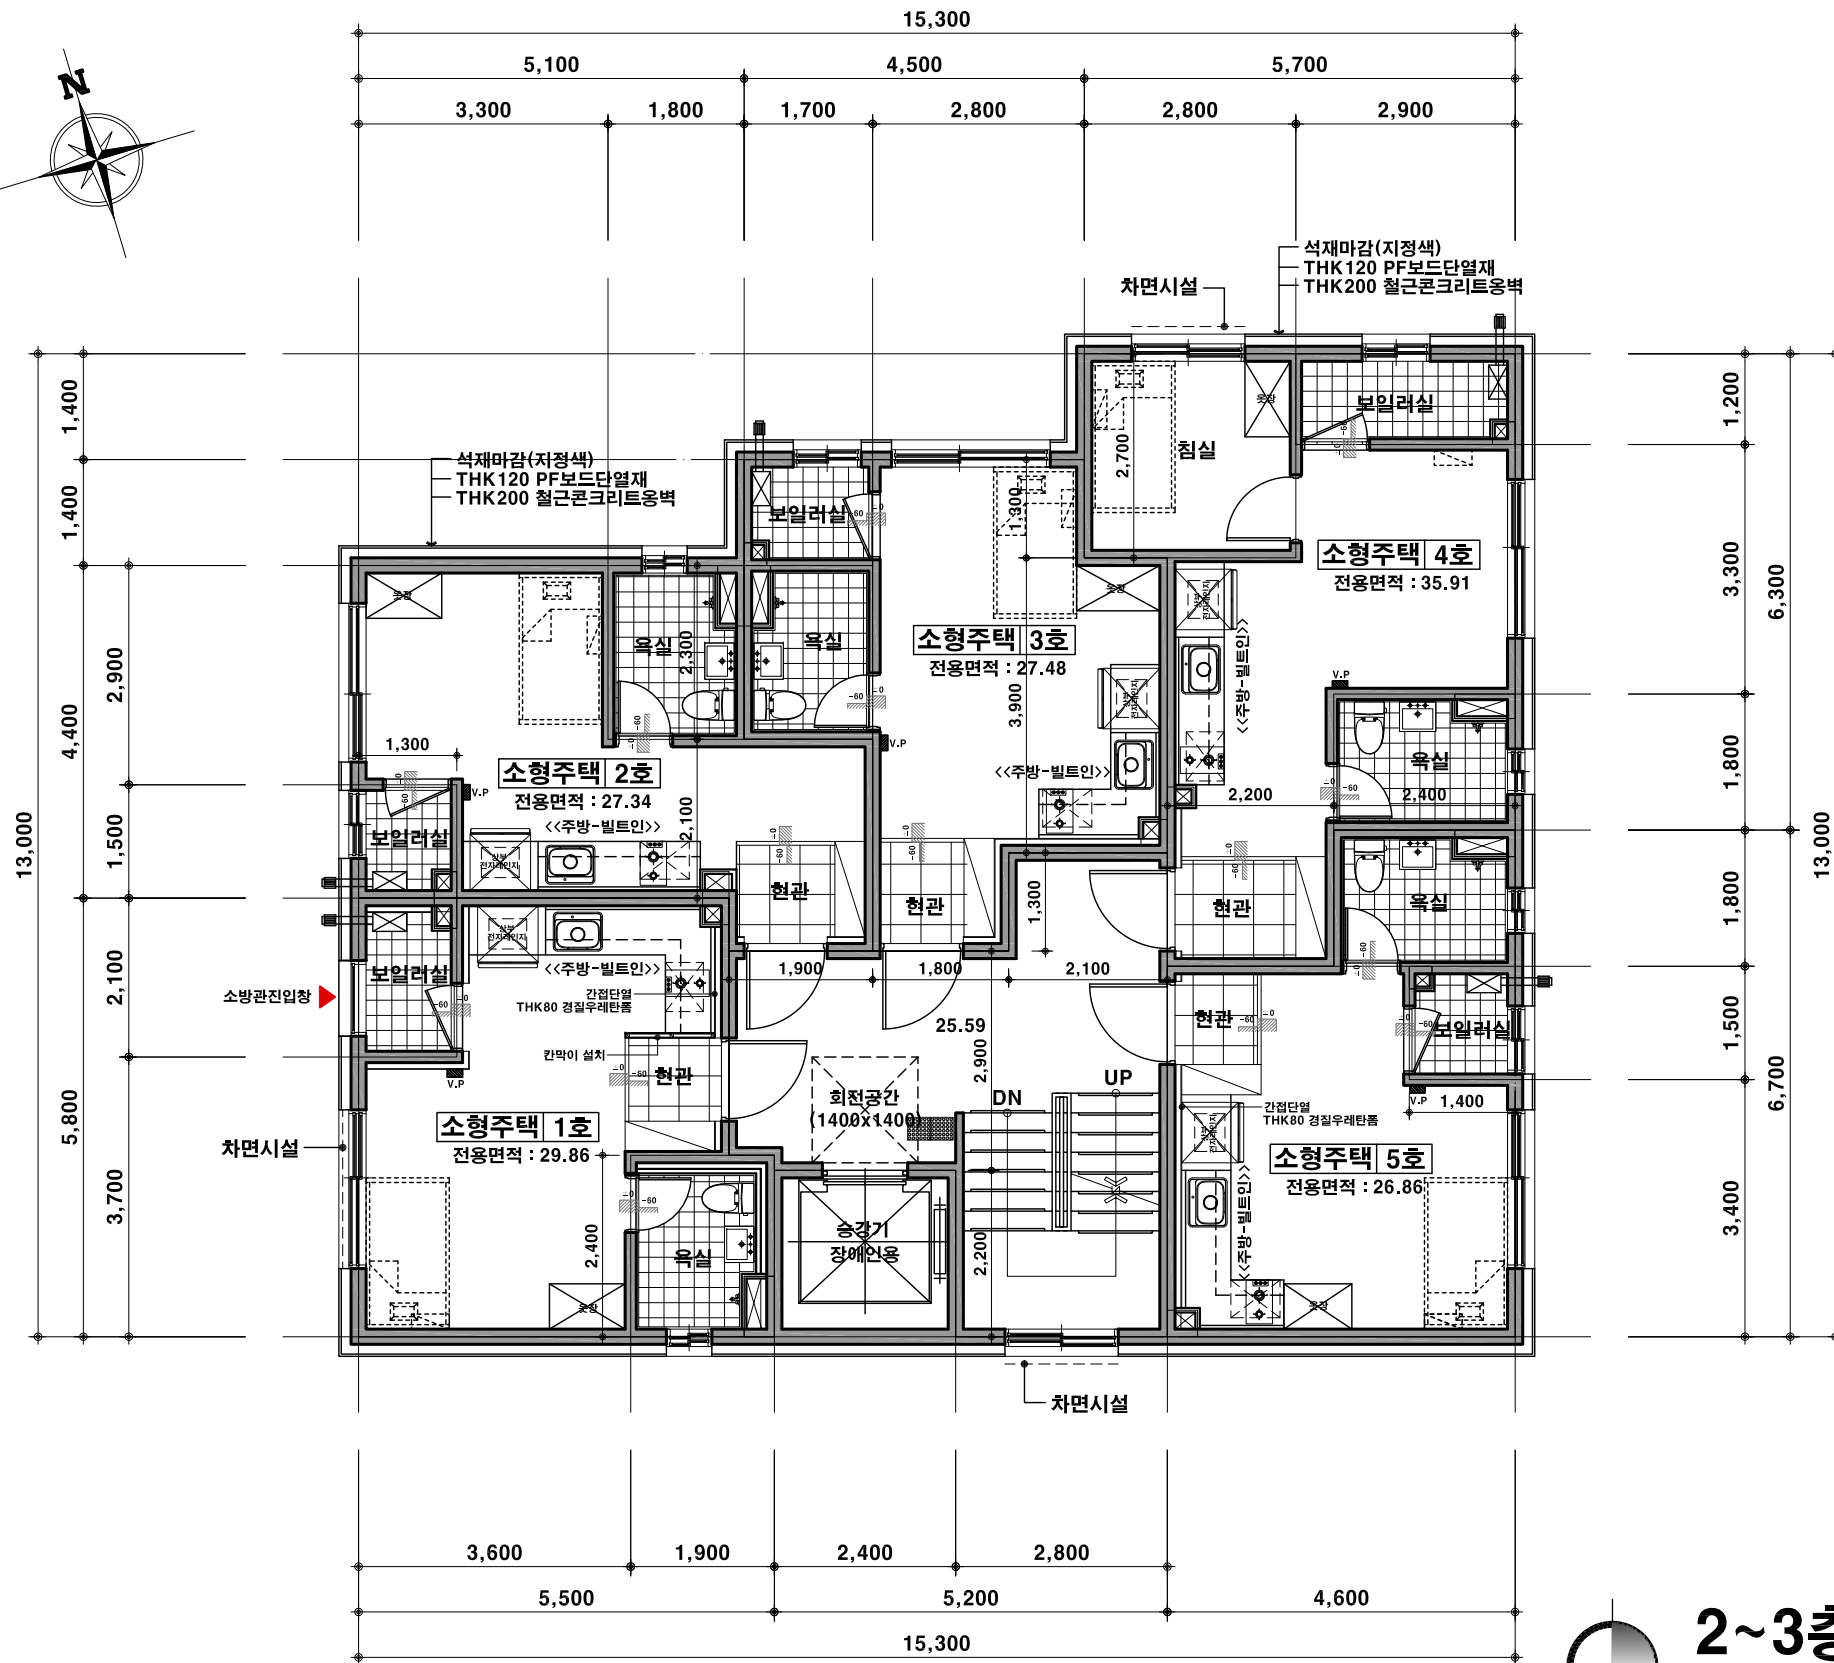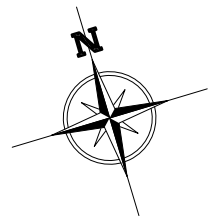

2~3층 평면도

scale:1/100

주 기			
건 축	1 (외부)	주차장내 CCTV,쓰레기분리수거,자전거보관대 설치	
		우편함 설치 (세대전용, 공용, 반송용, 폐건전지함 구분 설치)	
		테라스 창호 PL이중창 설치	
		세대 테라스 설치시 세대간 분리벽 계획	
		세대 발코니 설치시 차양시설 설치	
	2 (계단실)	세대 현관문 도어체크 설치 계단실의 현관과 계단 이격거리 (최소600mm이상)	
	3 (내부)	세대내 욕실, 휴지걸이 매립형 설치	
	4 (시공)	콘크리트 폼타이 제거 후 마감공사 시공 (방수, 단열재 시공 등)	
		욕실 & 다용도실 스위치 : 문 열리는 방향으로 시공	
		주차장 차량 진출입구간 무소음트렌치 시공	
5 (마감)	-직접외기(외벽)에 면한 실내벽면 단열재 [아이소핑크(10mm) + 석고보드 마감도면 표기]		
	-간접외기(계단실,복도)에 면한 실내벽면 단열재 일반내부 : [경질우레탄폼(80mm) + 석고보드 마감도면 표기] 욕실,다용도실 : [단열재판넬(80mm) 시공]		
	*기타 실내 벽면 시멘트 미장 마감		
구 조	1	철근 : fy=400MPa(HD16이하) , 500MPa(SHD190이상) 콘크리트 : fck=24Mpa	
		스라브두께 : 210mm (복배근)	
	2	외벽두께 : 200mm (복배근)	
		코아벽두께 : 200mm (복배근)	
		세대간벽두께 : 200mm (복배근)	
		내벽두께 : 150mm (복배근)	
전 기	1	-콘센트 설치 (바닥 마감선 기준)	
		[거실] 스탠드형 에어컨 : 350	
		[안방] 벽걸이형 에어컨 : 1900	
		[화장실] 양변기 옆 : 900	
		[주방] 조리대 : 중앙 / 냉장고 : 350 / 후드 : 2100	
	2	-비디오폰(VP),보일러온도조절기(B), 스위치(S), 전열교환기스위치(E) (거실 아트홀 위치)	
		VP S E B	
	3	에어컨 실외기	
		냉매, 배수관 (배수관수직매립)	
비 고	세대현관문 ## 규격"틀"포함 : 1100X2200 * 반드시 가열대뒤에도 선반 설치할 것. * 빌트인계획반영(냉장고,에어컨,세탁기,신발장,싱크대) * 공용공간 CCTV 설치 (모니터장비 포함) : 출입문, 계단실, 승강기 * 냉장고 - 개수대와 냉장고가 입접한경우 물막이턱 설치 * 샤워칸막이 - 안전강화유리 8T(협의후 변경가능)		



(주)다림 건축사사무소
Architects & Engineers Darim
Tel:(02) 2066-5599,Fax:(02) 2066-5598




NO	DATE	REVISION DESCRIPTION	DRWN	CHK'D	APPD
01		사용승인			

PROJECT TITLE
공 사 명 송파구 오금동 119-18번지
도시형생활주택(소형주택)
신축공사

CHK'D BY	SCALE 1 / 100
	DATE 2026.01
	DRWN BY

DRAWING TITLE
도 면 명 2~3층 평면도

B.C.C NO	JOB NO	APPROVE D BY
DRWG NO	A - 016	DESIGNED BY

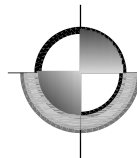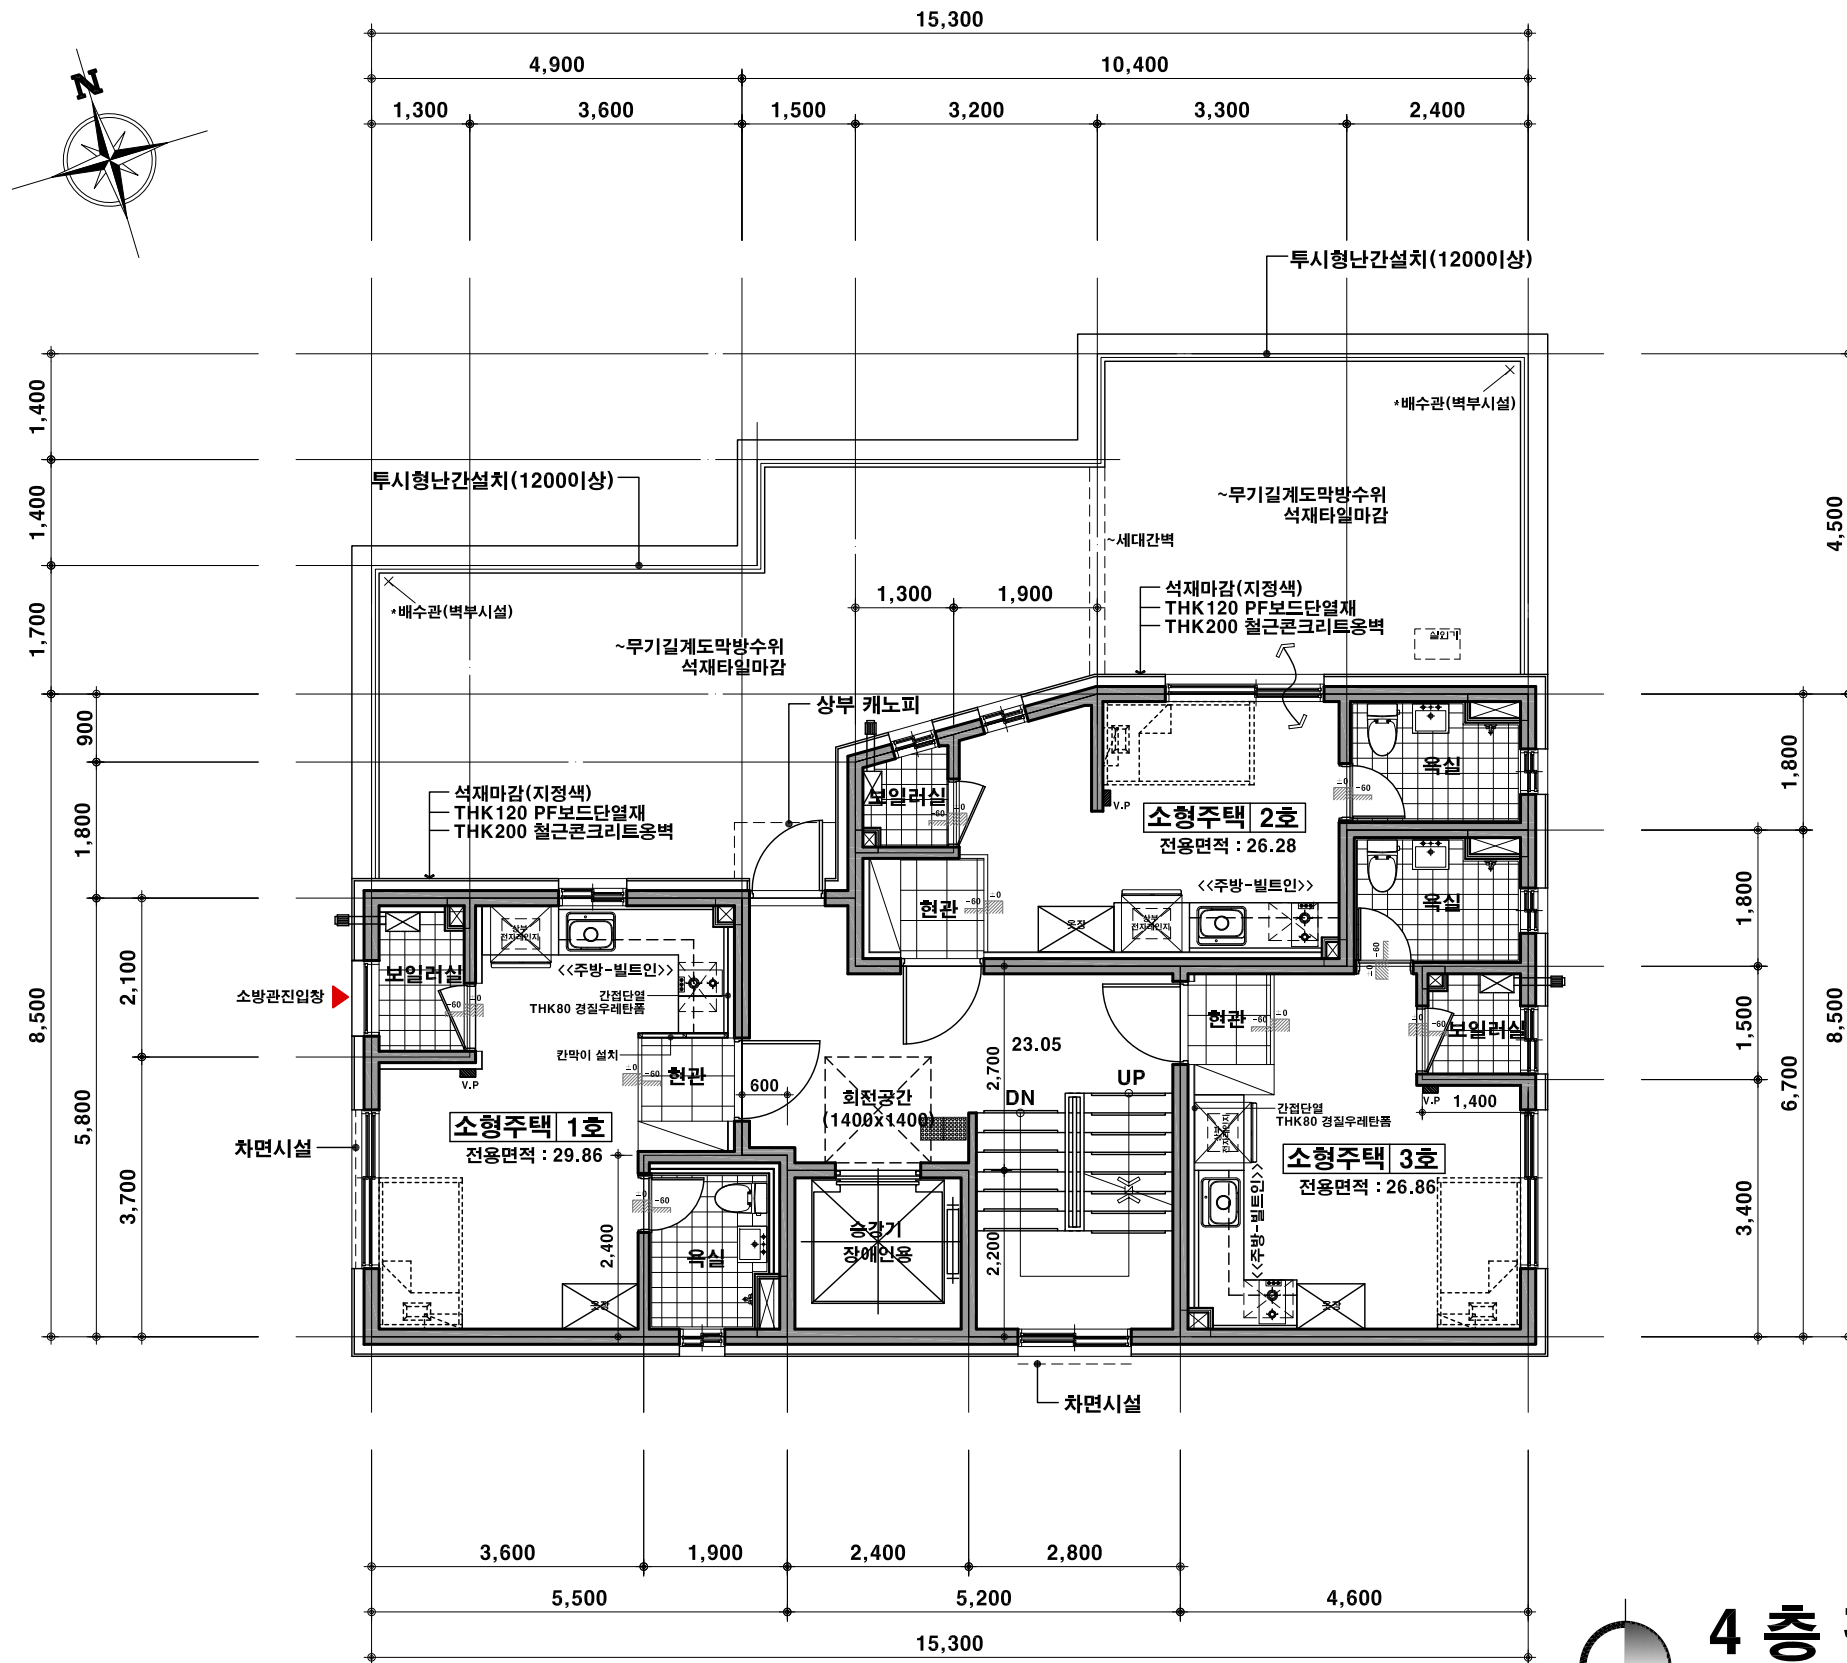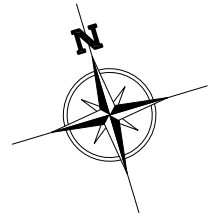

4 층 평면도

scale:1/100

주 기			
건 축	1 (외부)	주차장내 CCTV,쓰레기분리수거,자전거보관대 설치	
		우편함 설치 (세대전용, 공용, 반송용, 폐전지함 구분 설치)	
		테라스 창호 PL이중창 설치	
		세대 테라스 설치시 세대간 분리벽 계획	
		세대 발코니 설치시 차양시설 설치	
	2 (계단실)	세대 현관문 도어체크 설치	
	계단참의 현관과 계단 이격거리 (최소600mm이상)		
	3 (내부)	세대내 욕실, 휴지걸이 매립형 설치	
	4 (시공)	콘크리트 폼타이 제거 후 마감공사 시공 (방수, 단열재 시공 등)	
		욕실 & 다용도실 스위치 : 문 열리는 방향으로 시공	
		주차장 차량 진출입구간 무소음트렌치 시공	
		5 (마감)	-직접외기(외벽)에 면한 실내벽면 단열재
			[아이소핑크(10mm) + 석고보드 마감도면 표기]
	-간접외기(계단실,복도)에 면한 실내벽면 단열재		
	일반내부 : [경질우레탄폼(80mm) + 석고보드 마감도면 표기]		
구 조	1	철근 : fy=400MPa(HD16이하) , 500MPa(SHD190이상)	
		콘크리트 : fck=24Mpa	
	2	스라브두께 : 210mm (복배근)	
		외벽두께 : 200mm (복배근)	
		코아벽두께 : 200mm (복배근)	
		세대간벽두께 : 200mm (복배근)	
		내벽두께 : 150mm (복배근)	
	전 기	1	-콘센트 설치 (바닥 마감선 기준)
			[거실] 스탠드형 에어컨 : 350
			[안방] 벽걸이형 에어컨 : 1900
[화장실] 양변기 옆 : 900			
[주방] 조리대 : 중앙 / 냉장고 : 350 / 후드 : 2100			
2		-비디오폰(VP),보일러온도조절기(B), 스위치(S), 전열교환기스위치(E) (거실 아트홀 위치)	
3		에어컨 실외기	
	냉매, 배수관 (배수관수직매립)		
비 고	세대현관문		
	## 규격"를"포함 : 1100X2200		
	* 반드시 가열대뒤에도 선반 설치할 것.		
	* 빌트인계획반영(냉장고,에어컨,세탁기,신발장,싱크대)		
	* 공용공간 CCTV 설치 (모니터장비 포함)		
	: 출입문, 계단실, 승강기		
	* 냉장고 - 개수대와 냉장고가 입접한경우 물막이턱 설치		
* 샤워칸막이 - 안전강화유리 8T(협의후 변경가능)			



(주)다림 건축사사무소
Architects & Engineers Darim
Tel: (02) 2066-5599, Fax: (02) 2066-5598




NO	DATE	REVISION DESCRIPTION	DRWN	CHK'D	APPD
01		사용승인			

PROJECT TITLE
공 사 명 송파구 오금동 119-18번지
도시형생활주택(소형주택)
신축공사

CHK'D BY	SCALE 1 / 100
	DATE 2026.01
	DRWN BY

DRAWING TITLE
도 면 명 4 층 평면도

B.C.C NO	JOB NO	APPROVE D BY
DRWG NO	A - 017	DESIGNED BY

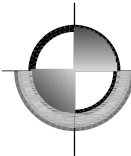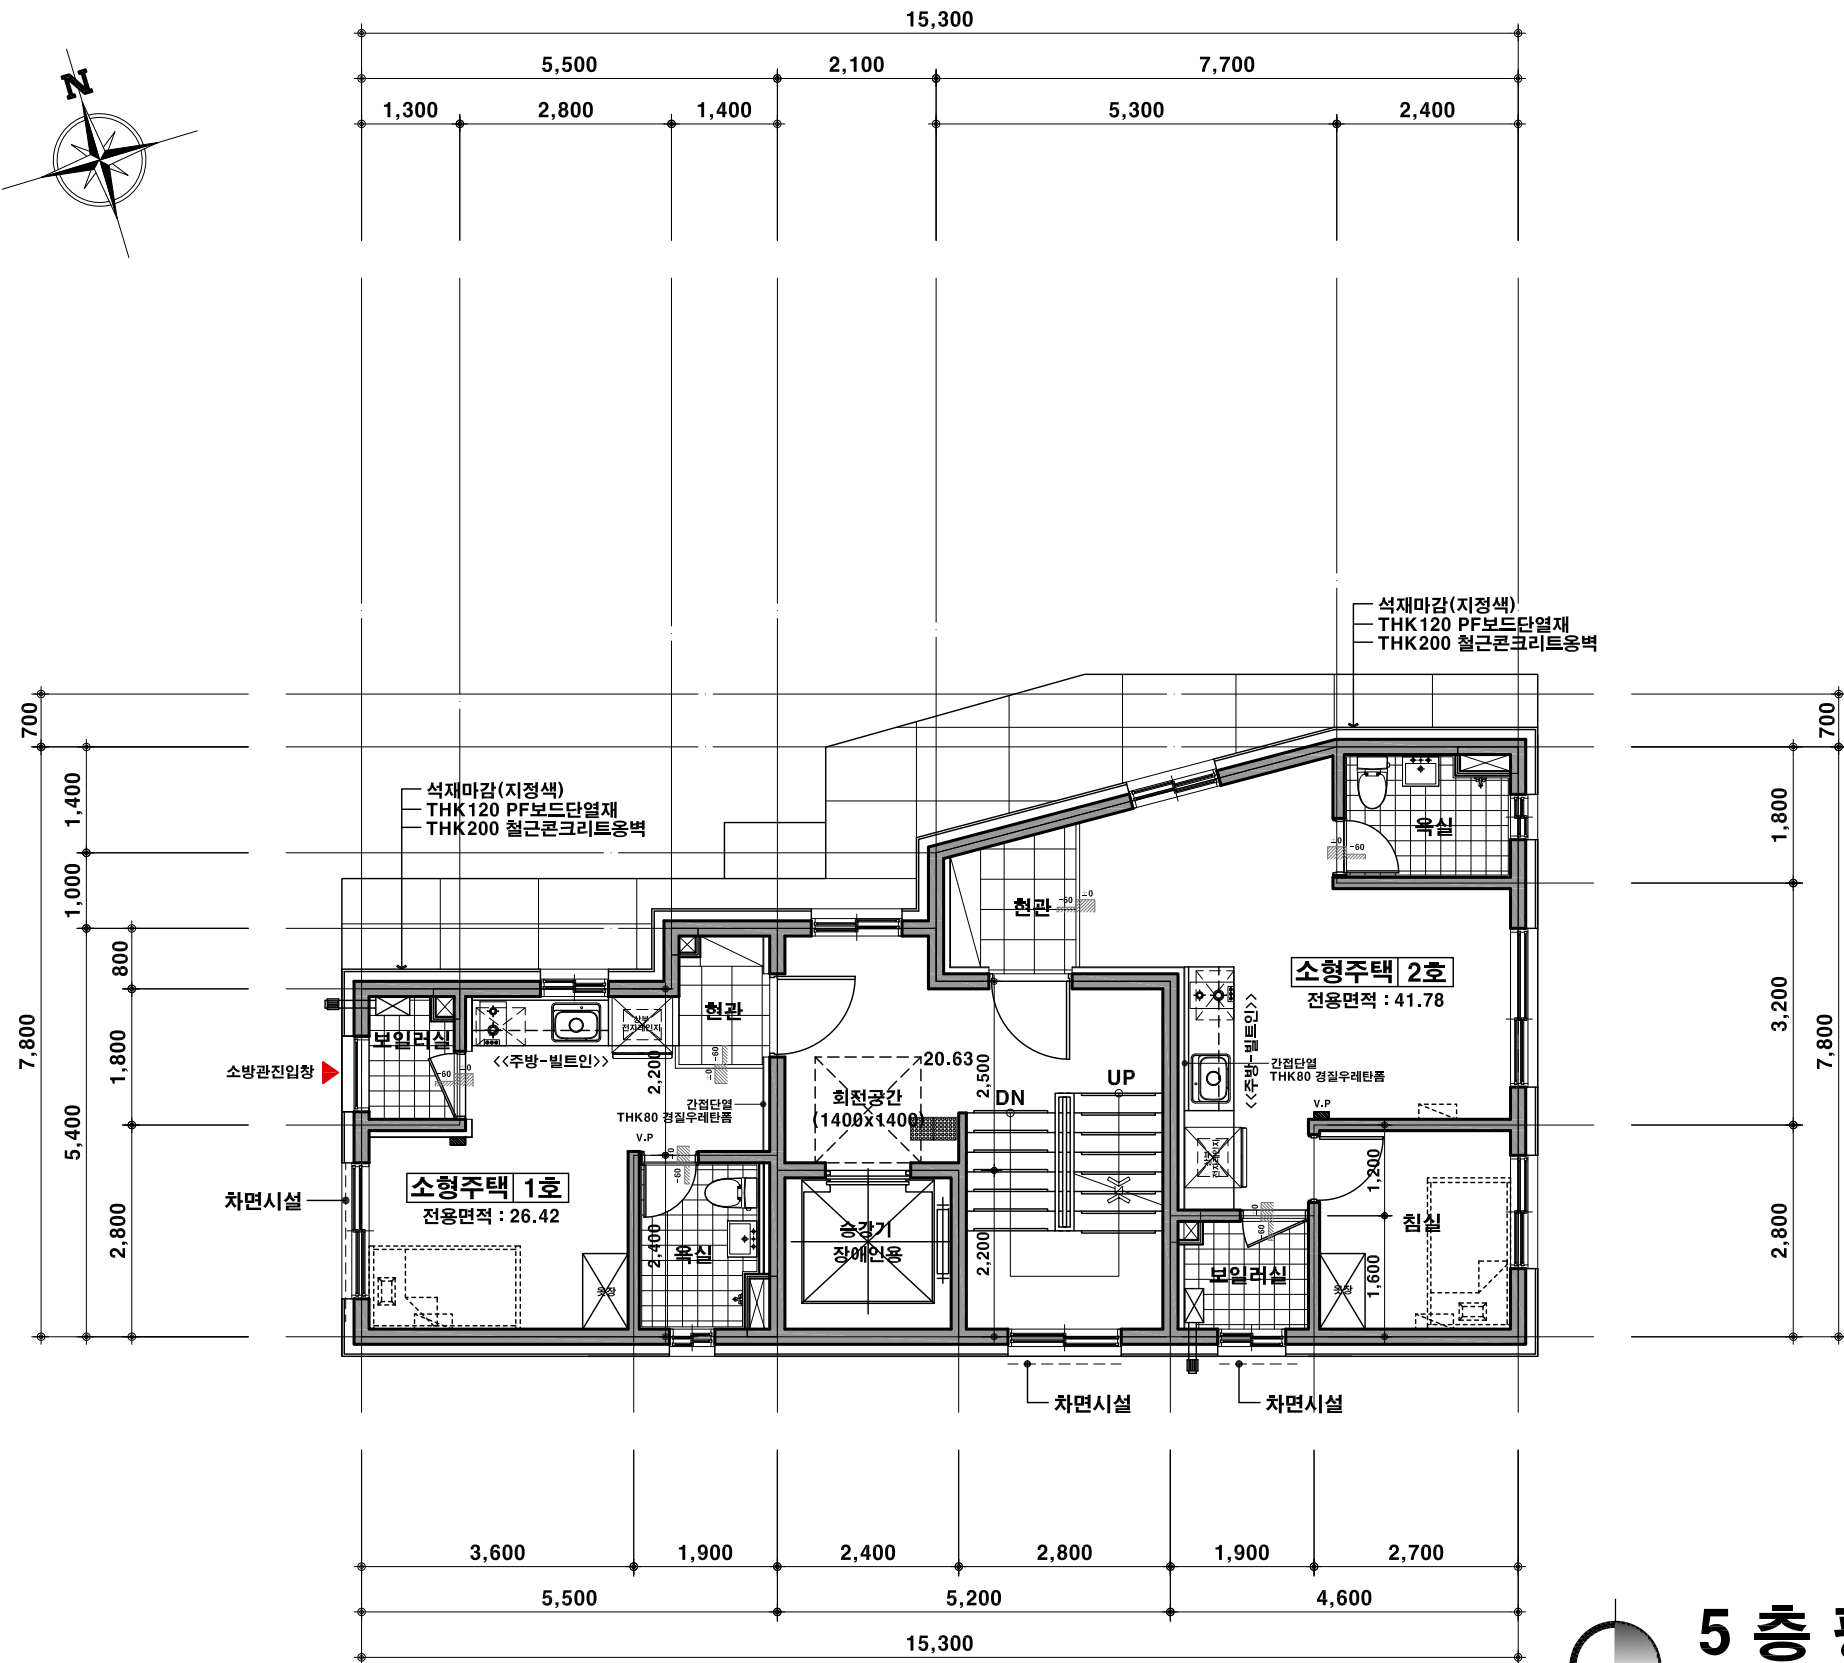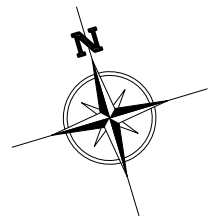

5 층 평면도

scale:1/100

주 기									
건 축	1 (외부)	주차장내 CCTV,쓰레기분리수거,자전거보관대 설치							
		우편함 설치 (세대전용, 공용, 반송용, 폐건전지함 구분 설치)							
		테라스 창호 PL이중창 설치							
		세대 테라스 설치시 세대간 분리벽 계획							
		세대 발코니 설치시 차양시설 설치							
	2 (계단실)	세대 현관문 도어체크 설치							
	(계단실) 계단참의 현관과 계단 이격거리 (최소600mm이상)								
	3 (내부)	세대내 욕실, 휴지걸이 매립형 설치							
	4 (시공)	콘크리트 폼타이 제거 후 마감공사 시공 (방수, 단열재 시공 등)							
		욕실 & 다용도실 스위치 : 문 열리는 방향으로 시공							
		주차장 차량 진출입구간 무소음트렌치 시공							
5 (마감)	-직접외기(외벽)에 면한 실내벽면 단열재								
	[아이소핑크(10mm) + 석고보드 마감도면 표기]								
	-간접외기(계단실,복도)에 면한 실내벽면 단열재								
	일반내부 : [경질우레탄폼(80mm) + 석고보드 마감도면 표기]								
	욕실,다용도실 : [단열재판넬(80mm) 시공]								
*기타 실내 벽면 시멘트 미장 마감									
구 조	1	철근 : $f_y=400\text{MPa}$ (HD16이하) , 500MPa (SHD190이상)							
	2	콘크리트 : $f_{ck}=24\text{Mpa}$							
		스라브두께 : 210mm (복배근)							
		외벽두께 : 200mm (복배근)							
		코아벽두께 : 200mm (복배근)							
		세대간벽두께 : 200mm (복배근)							
내벽두께 : 150mm (복배근)									
전 기	1	-콘센트 설치 (바닥 마감선 기준)							
		[거실] 스탠드형 에어컨 : 350							
		[안방] 벽걸이형 에어컨 : 1900							
		[화장실] 양변기 옆 : 900							
		[주방] 조리대 : 중앙 / 냉장고 : 350 / 후드 : 2100							
	2	-비디오폰(VP),보일러온도조절기(B), 스위치(S), 전열교환기스위치(E) (거실 아트홀 위치)	<table><tr><td colspan="3">VP</td></tr><tr><td>S</td><td>E</td><td>B</td></tr></table>	VP			S	E	B
	VP								
S	E	B							
3	에어컨 실외기								
	냉매, 배수관 (배수관수직매립)								
비 고	세대현관문 ## 규격"를"포함 : 1100X2200 * 반드시 가열대뒤에도 선반 설치할 것. * 빌트인계획반영(냉장고,에어컨,세탁기,신발장,싱크대) * 공용공간 CCTV 설치 (모니터장비 포함) : 출입문, 계단실, 승강기 * 냉장고 - 개수대와 냉장고가 입접한경우 물막이턱 설치 * 샤워칸막이 - 안전강화유리 8T(협의후 변경가능)								



(주)다림 건축사사무소
Architects & Engineers Darim
Tel: (02) 2066-5599, Fax: (02) 2066-5598




NO	DATE	REVISION DESCRIPTION	DRWN	CHK'D	APPD
01		사용승인			

PROJECT TITLE
공 사 명 송파구 오금동 119-18번지
도시형생활주택(소형주택)
신축공사

CHK'D BY	SCALE 1 / 100
	DATE 2026.01
	DRWN BY

DRAWING TITLE
도 면 명 5 층 평면도

B.C.C NO	JOB NO	APPROVE D BY
DRWG NO	A - 018	DESIGNED BY

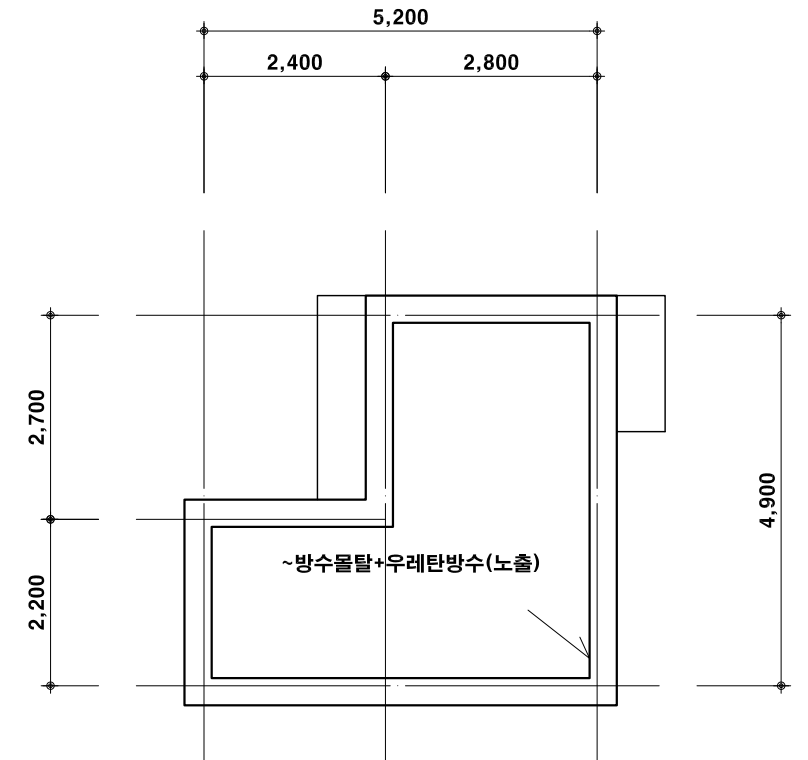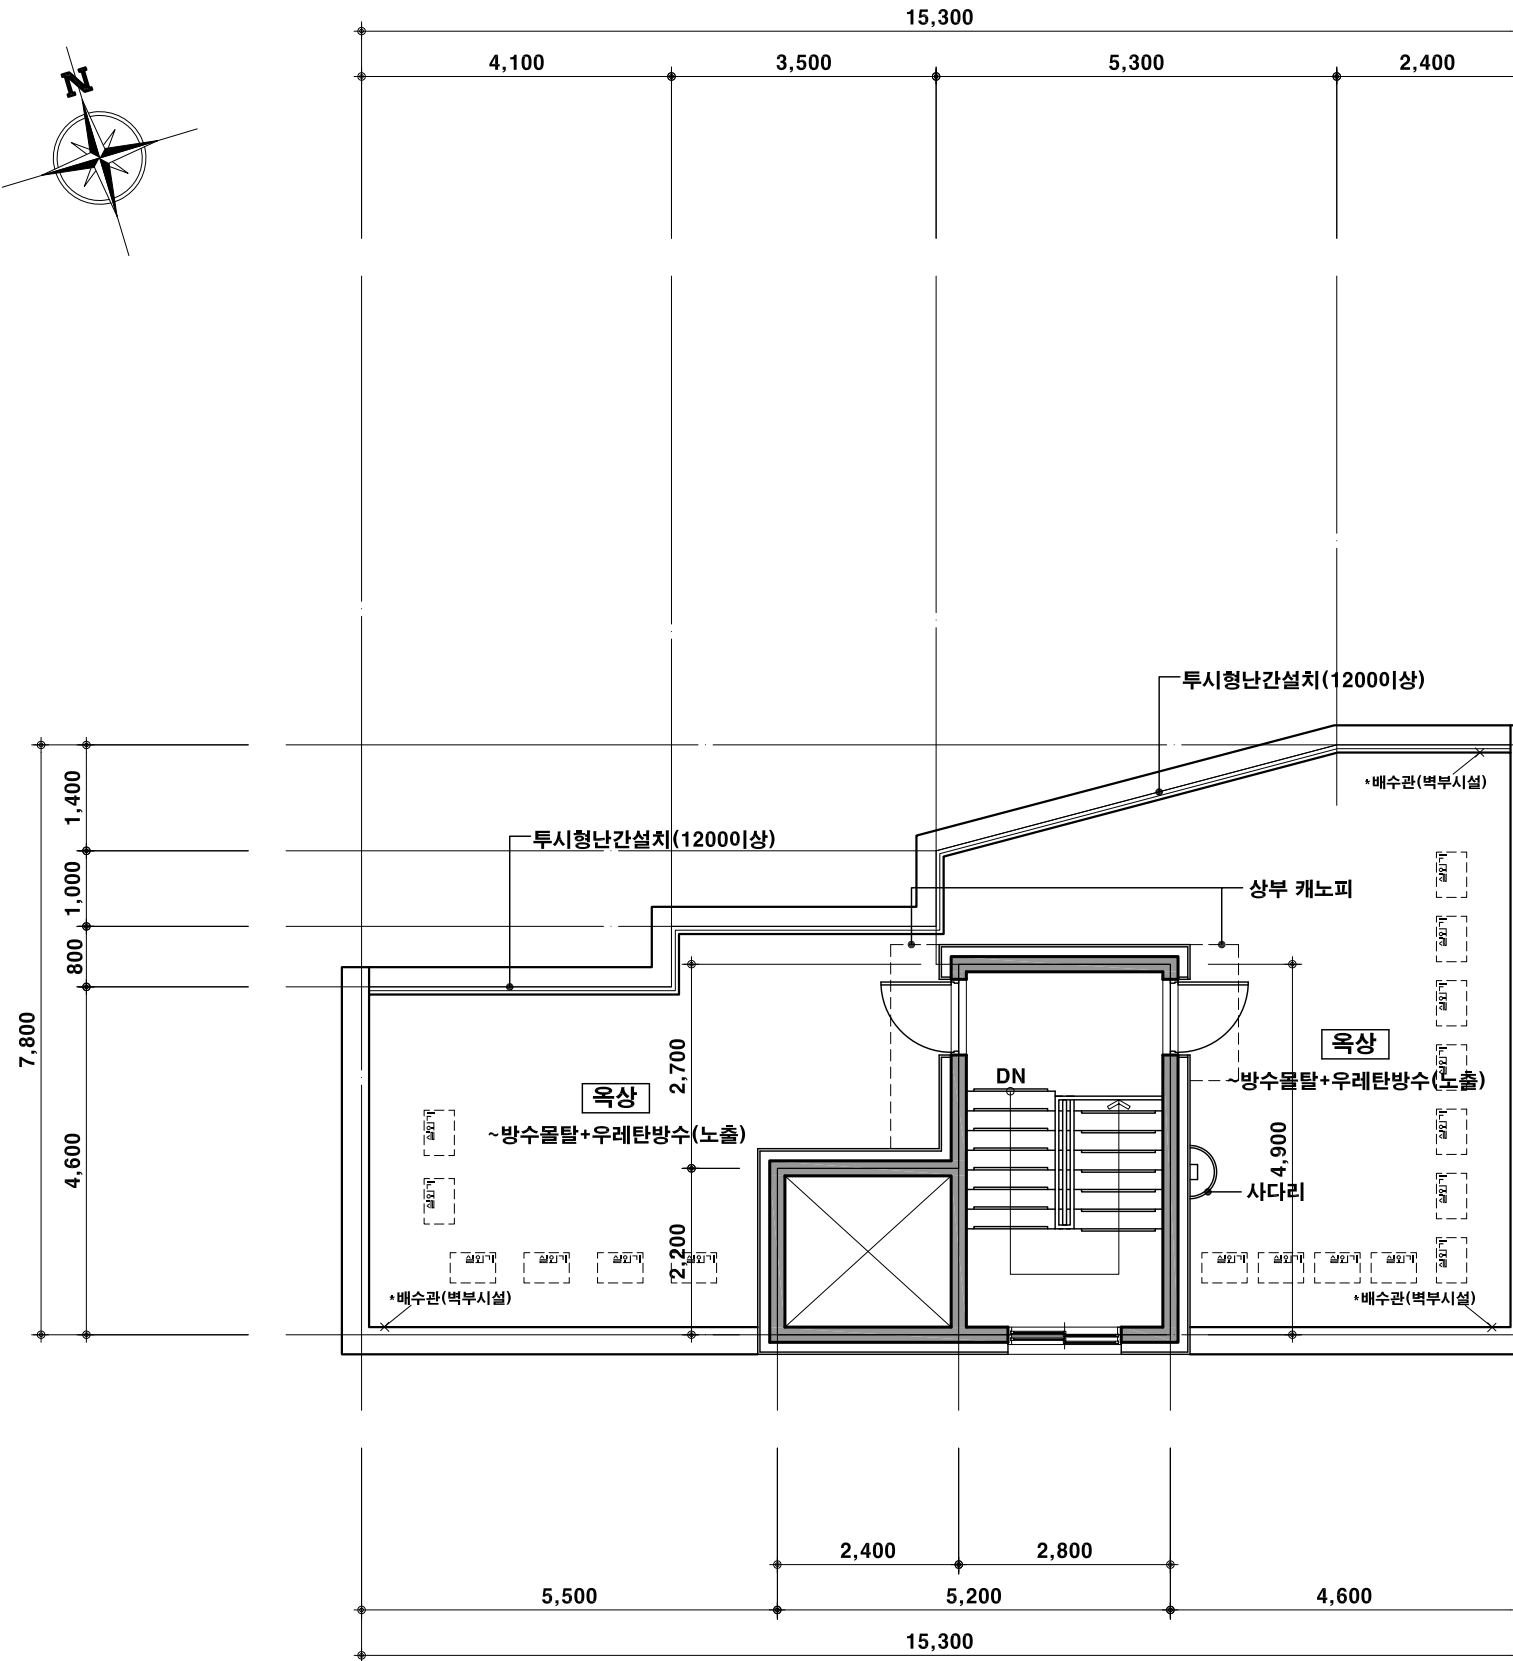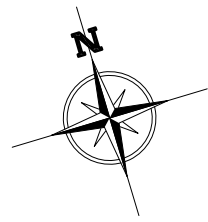

옥탑지붕 평면도

scale:1/100





지붕 평면도

scale:1/100



(주)다림 건축사사무소
Architects & Engineers Darim
Tel: (02) 2066-5599, Fax: (02) 2066-5598

NO	DATE	REVISION DESCRIPTION	DRWN	CHK'D	APPD	PROJECT TITLE	CHK'D BY	SCALE	DRAWING TITLE	B.C.C NO	JOB NO	APPROVE D BY
01		사용승인				공사명 송파구 오금동 119-18번지 도시형생활주택(소형주택) 신축공사		1 / 100	도면명 지붕 평면도			
								DATE 2026.01		DRWG NO	A - 019	DESIGNED BY
								DRWN BY				

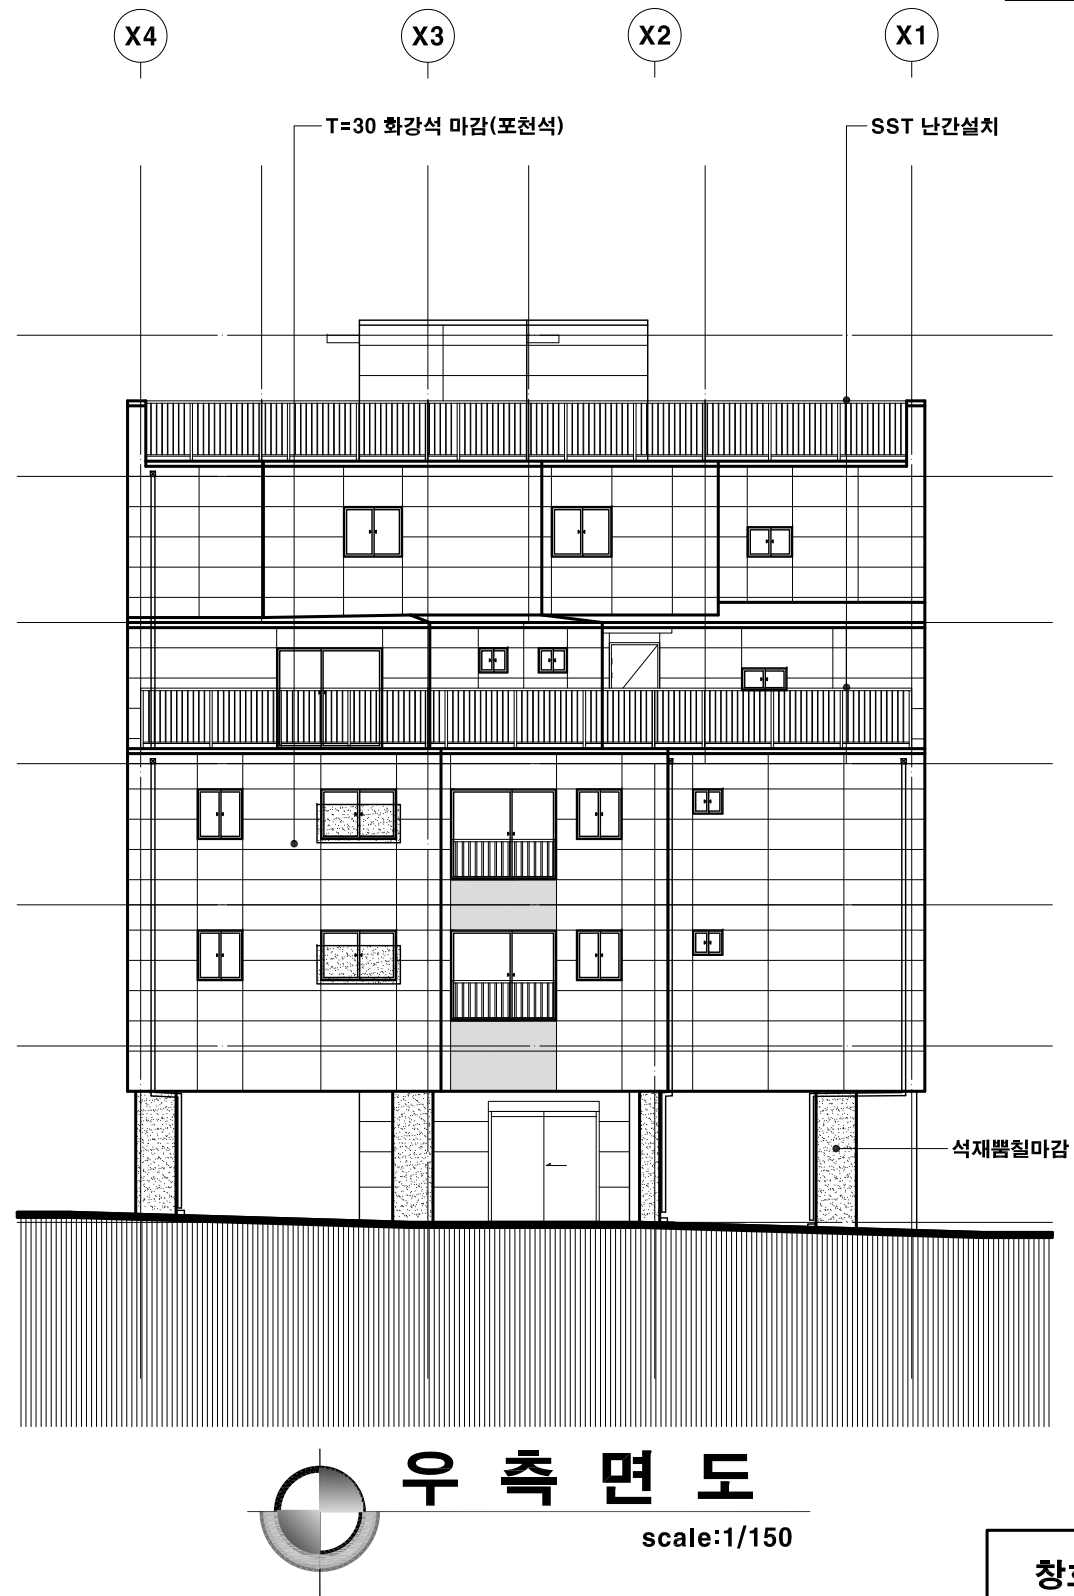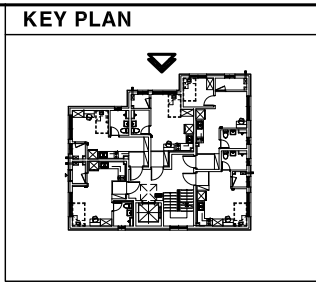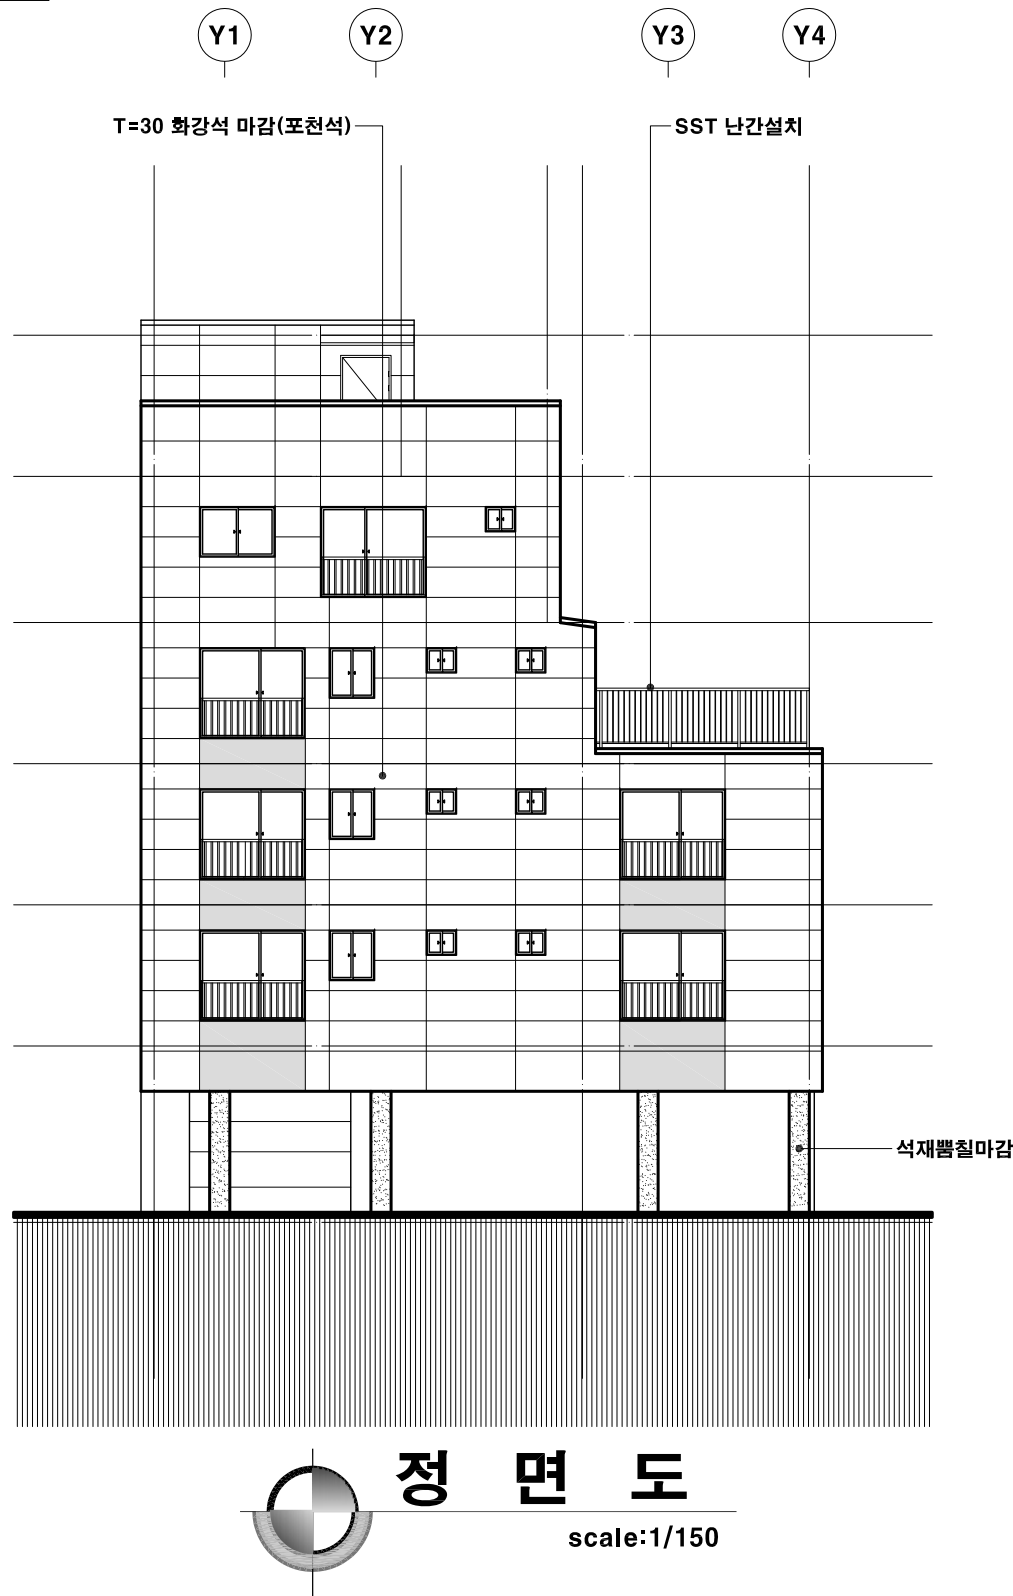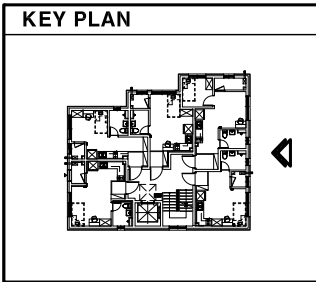

창호 색상 - 검정



(주)다림 건축사사무소
Architects & Engineers Darim
Tel: (02) 2066-5599, Fax: (02) 2066-5598

NO	DATE	REVISION DESCRIPTION	DRWN	CHK'D	APPD
01		사용승인			





PROJECT TITLE
공사명 송파구 오금동 119-18번지
도시형생활주택(소형주택)
신축공사

CHK'D BY	SCALE 1 / 150
	DATE 2026.01
	DRWN BY

DRAWING TITLE
도면명 정면도, 우측면도

B.C.C NO	JOB NO
DRWG NO	A - 020

APPROVE D BY
DESIGNED BY

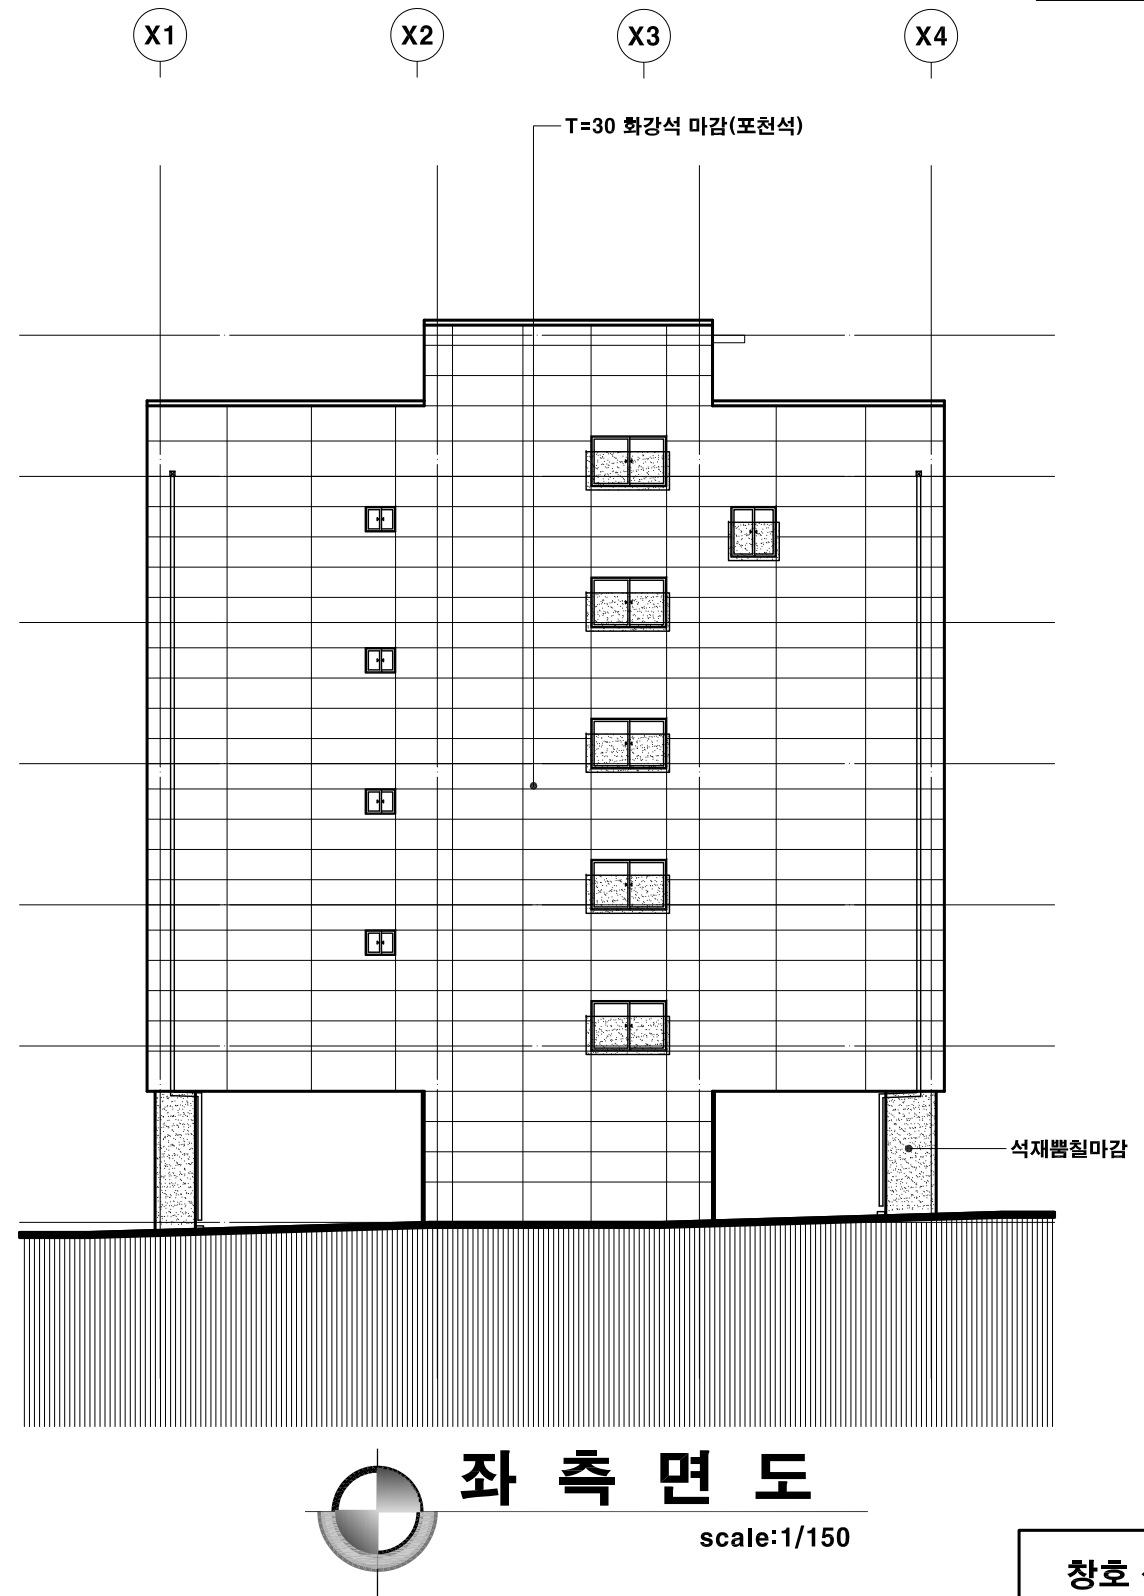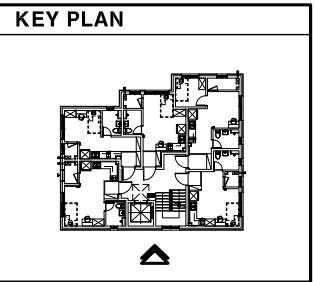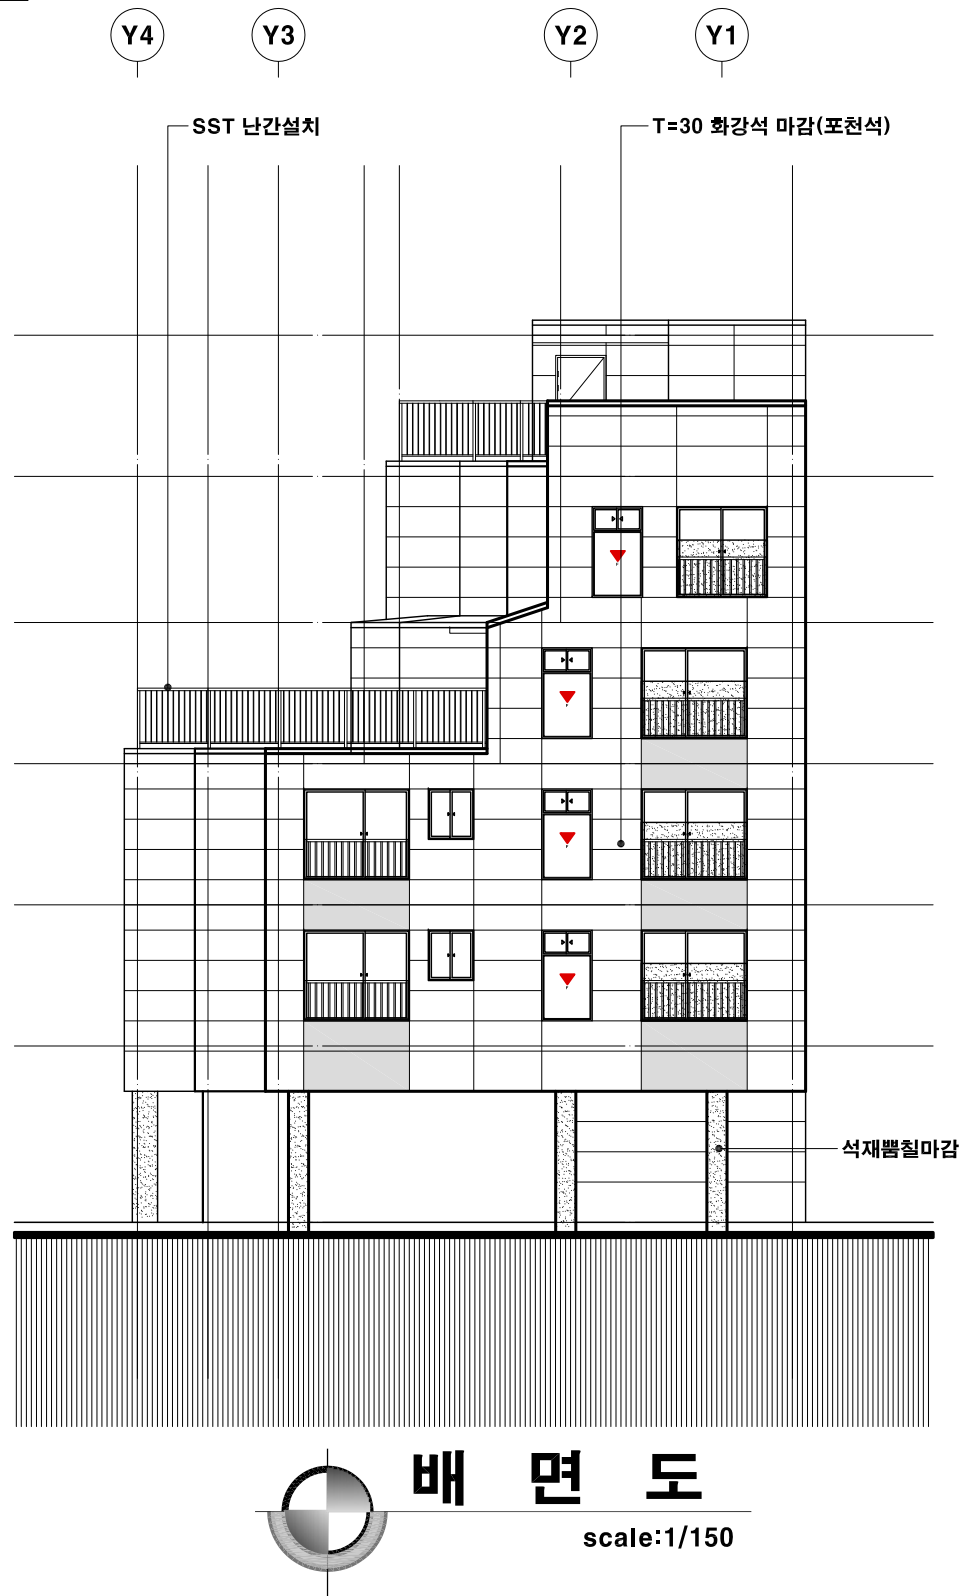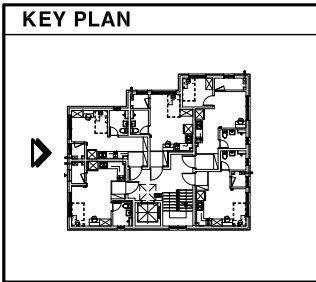

창호 색상 - 검정



(주)다림 건축사사무소
Architects & Engineers Darim
Tel: (02) 2066-5599, Fax: (02) 2066-5598

NO	DATE	REVISION DESCRIPTION	DRWN	CHK'D	APPD
01		사용승인			

PROJECT TITLE
공 사 명 송파구 오금동 119-18번지
도시형생활주택(소형주택)
신축공사

CHK'D BY	SCALE 1 / 150
	DATE 2026.01
	DRWN BY

DRAWING TITLE
도 면 명 배 면도, 좌 측면도

B.C.C NO	JOB NO	APPROVE D BY
DRWG NO	A - 021	DESIGNED BY

*방수시도접기시공
(욕실/다용도실/발코니~~)

실내

실내

물받이자리
방수처리


알루미늄크리플스리프

석고보드

방수층

실내

단열재 범위			
위치		두께	재질
주차장 (천정)	난방	60	PF보드단열재 (준불연단열재)
	비난방	150	
2층 바닥		80	경질우레탄폼
지붕층		190	경질우레탄폼
외벽	직접	120	PF보드단열재 (준불연단열재)
	간접	80	경질우레탄폼

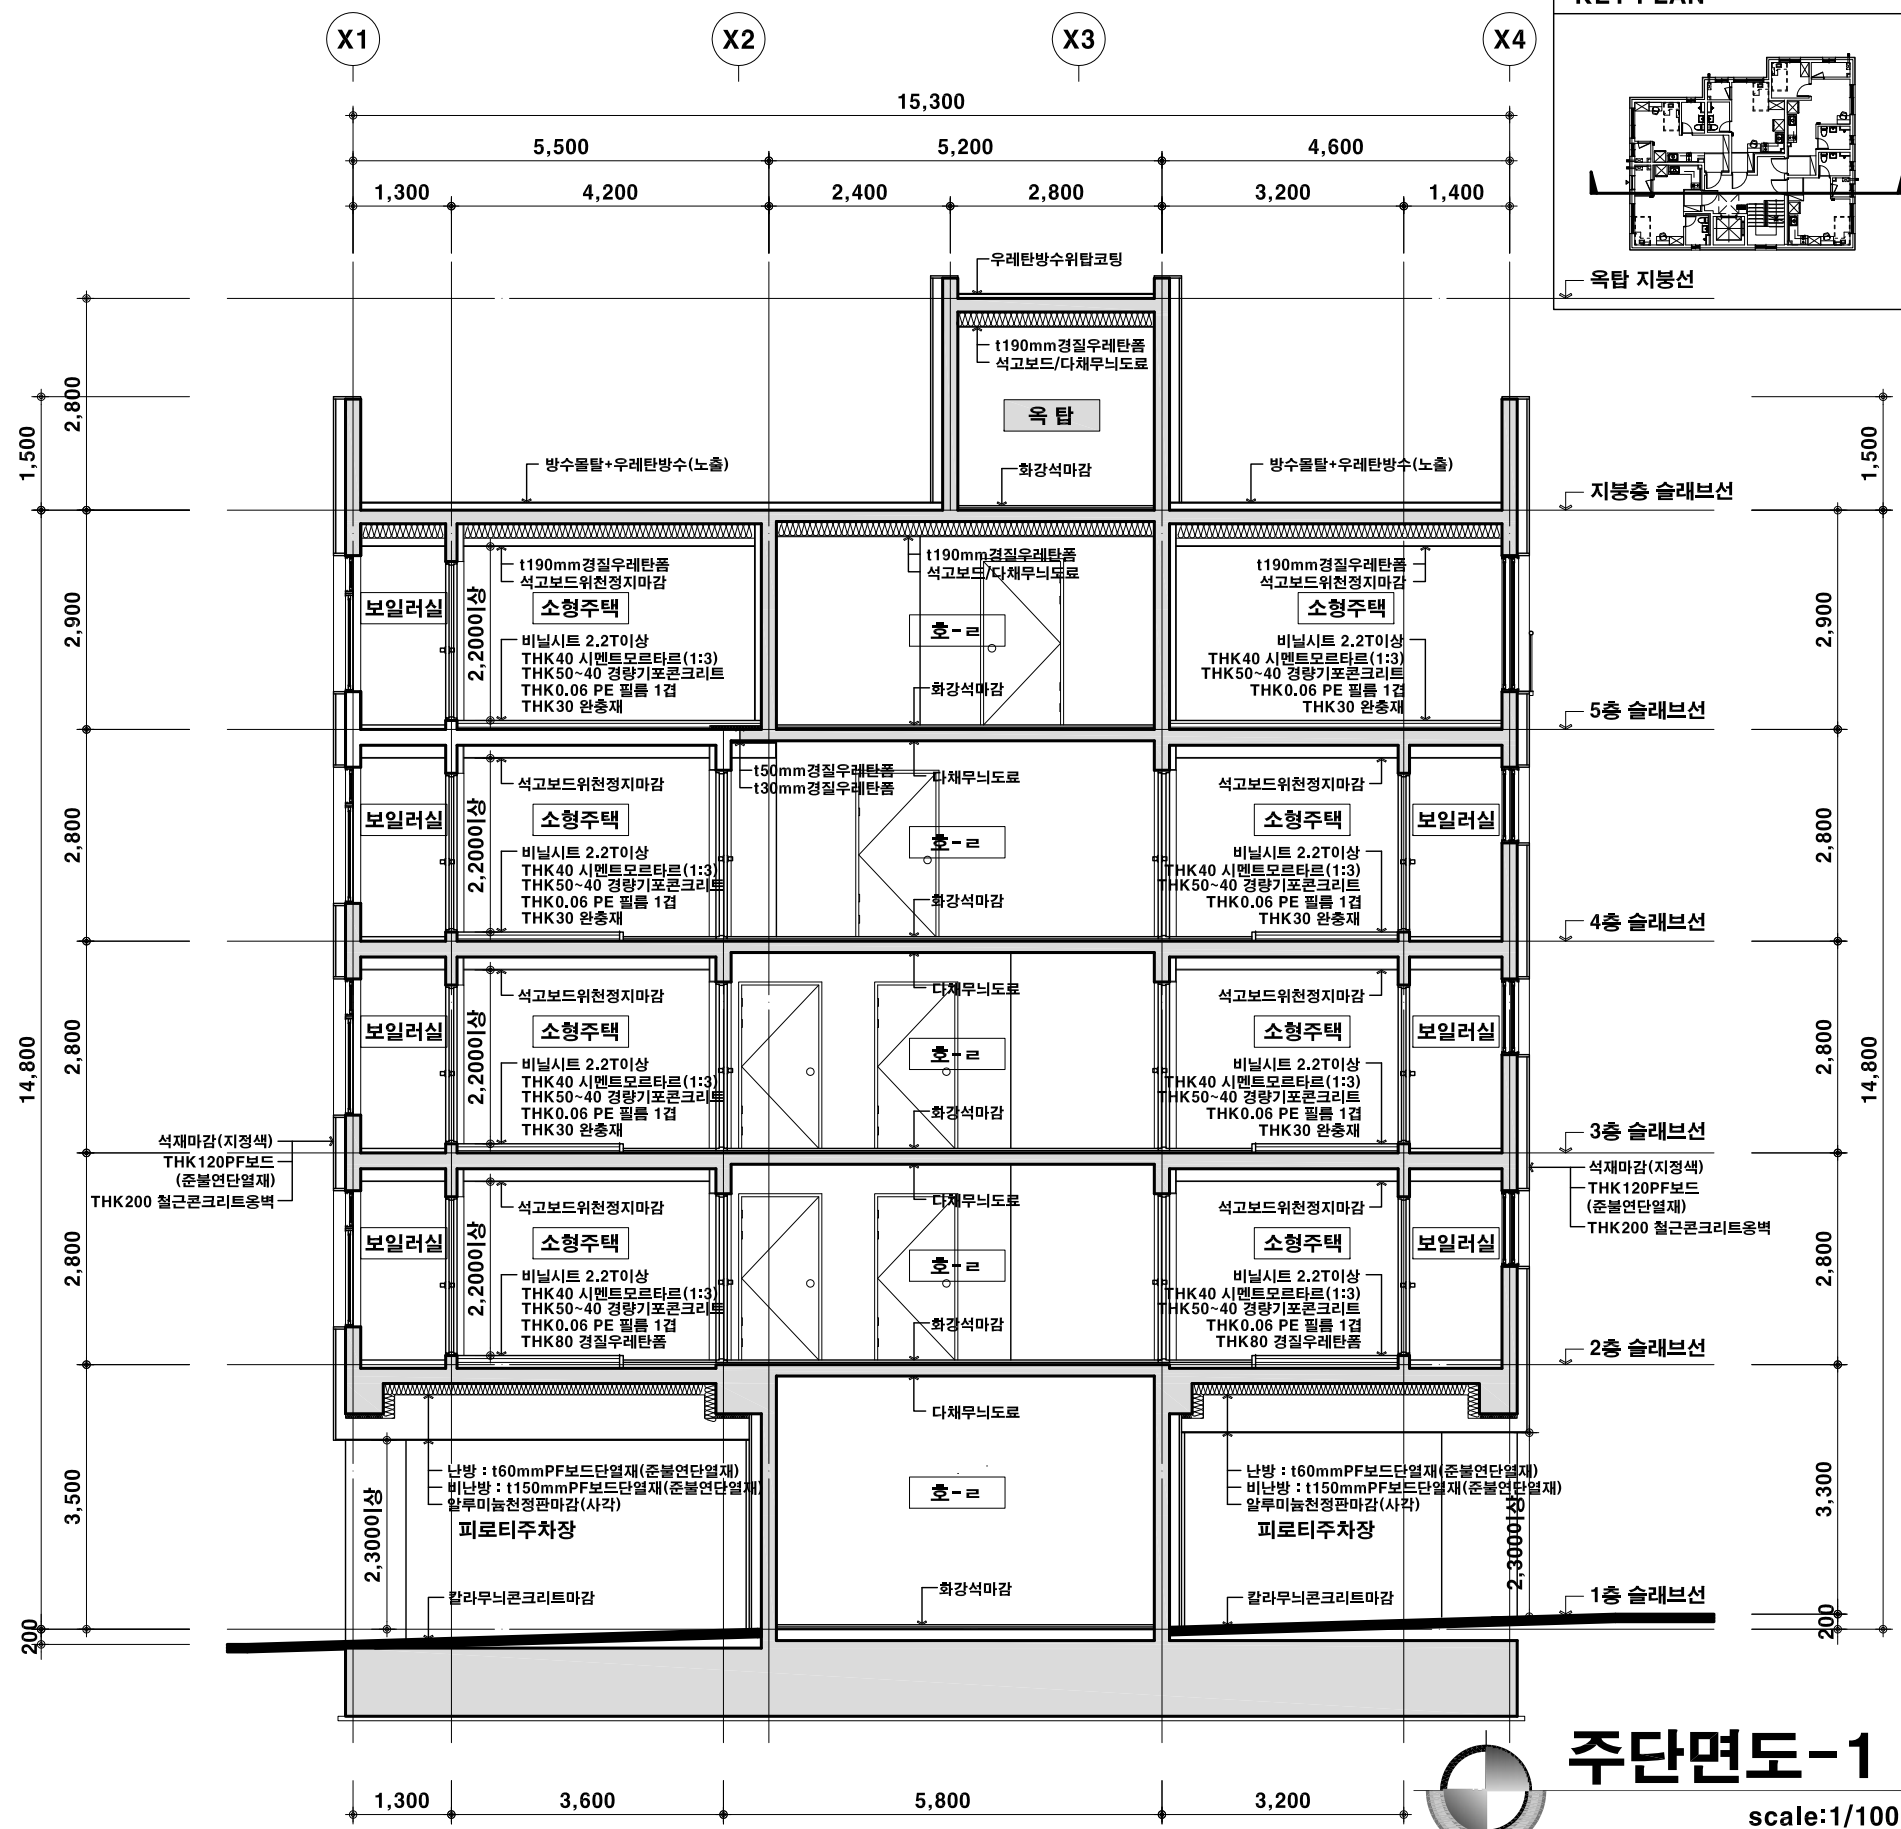

옥상지붕 바닥

- t180mm스라브
- t190mm경질우레탄폼
- t9.5mm석고보드
- 천정지마감
- t10mm아이소핑크
- 타설시 부착

*방수시모접기시공
(테라스/옥상~~)

우레탄방수위탁코팅

철근콘크리트스ラブ

슬라브

단열재

t9.5mm 석고보드

천정지마감

실외

실내

t10mm 아이소폼크
타설시 부착

비닐시트 2.2T이상
 마감모르타르 40mm이상
 경량거포콘크리트 40mm이상
 완충재 30mm이상
 콘크리트슬래브 210mm이상

시멘트물탈취 석재마감
 ~걸레받이

60, 40, 40, 30

<< 완충재 성능 기준참조 >>

[illegible]

방수시모접기시공
(육실/다용도실/발코니~~)

실내

실내

물탈위자기질타일마감


방수처리

실외크리올스라브

석고보드워천정지마감

실내

단열재 범위			
위치		두께	재질
주차장 (천정)	난방	60	PF보드단열재 (준불연단열재)
	비난방	150	
2층 바닥		80	경질우레탄폼
지붕층		190	경질우레탄폼
외벽	직접	120	PF보드단열재 (준불연단열재)
	간접	80	경질우레탄폼

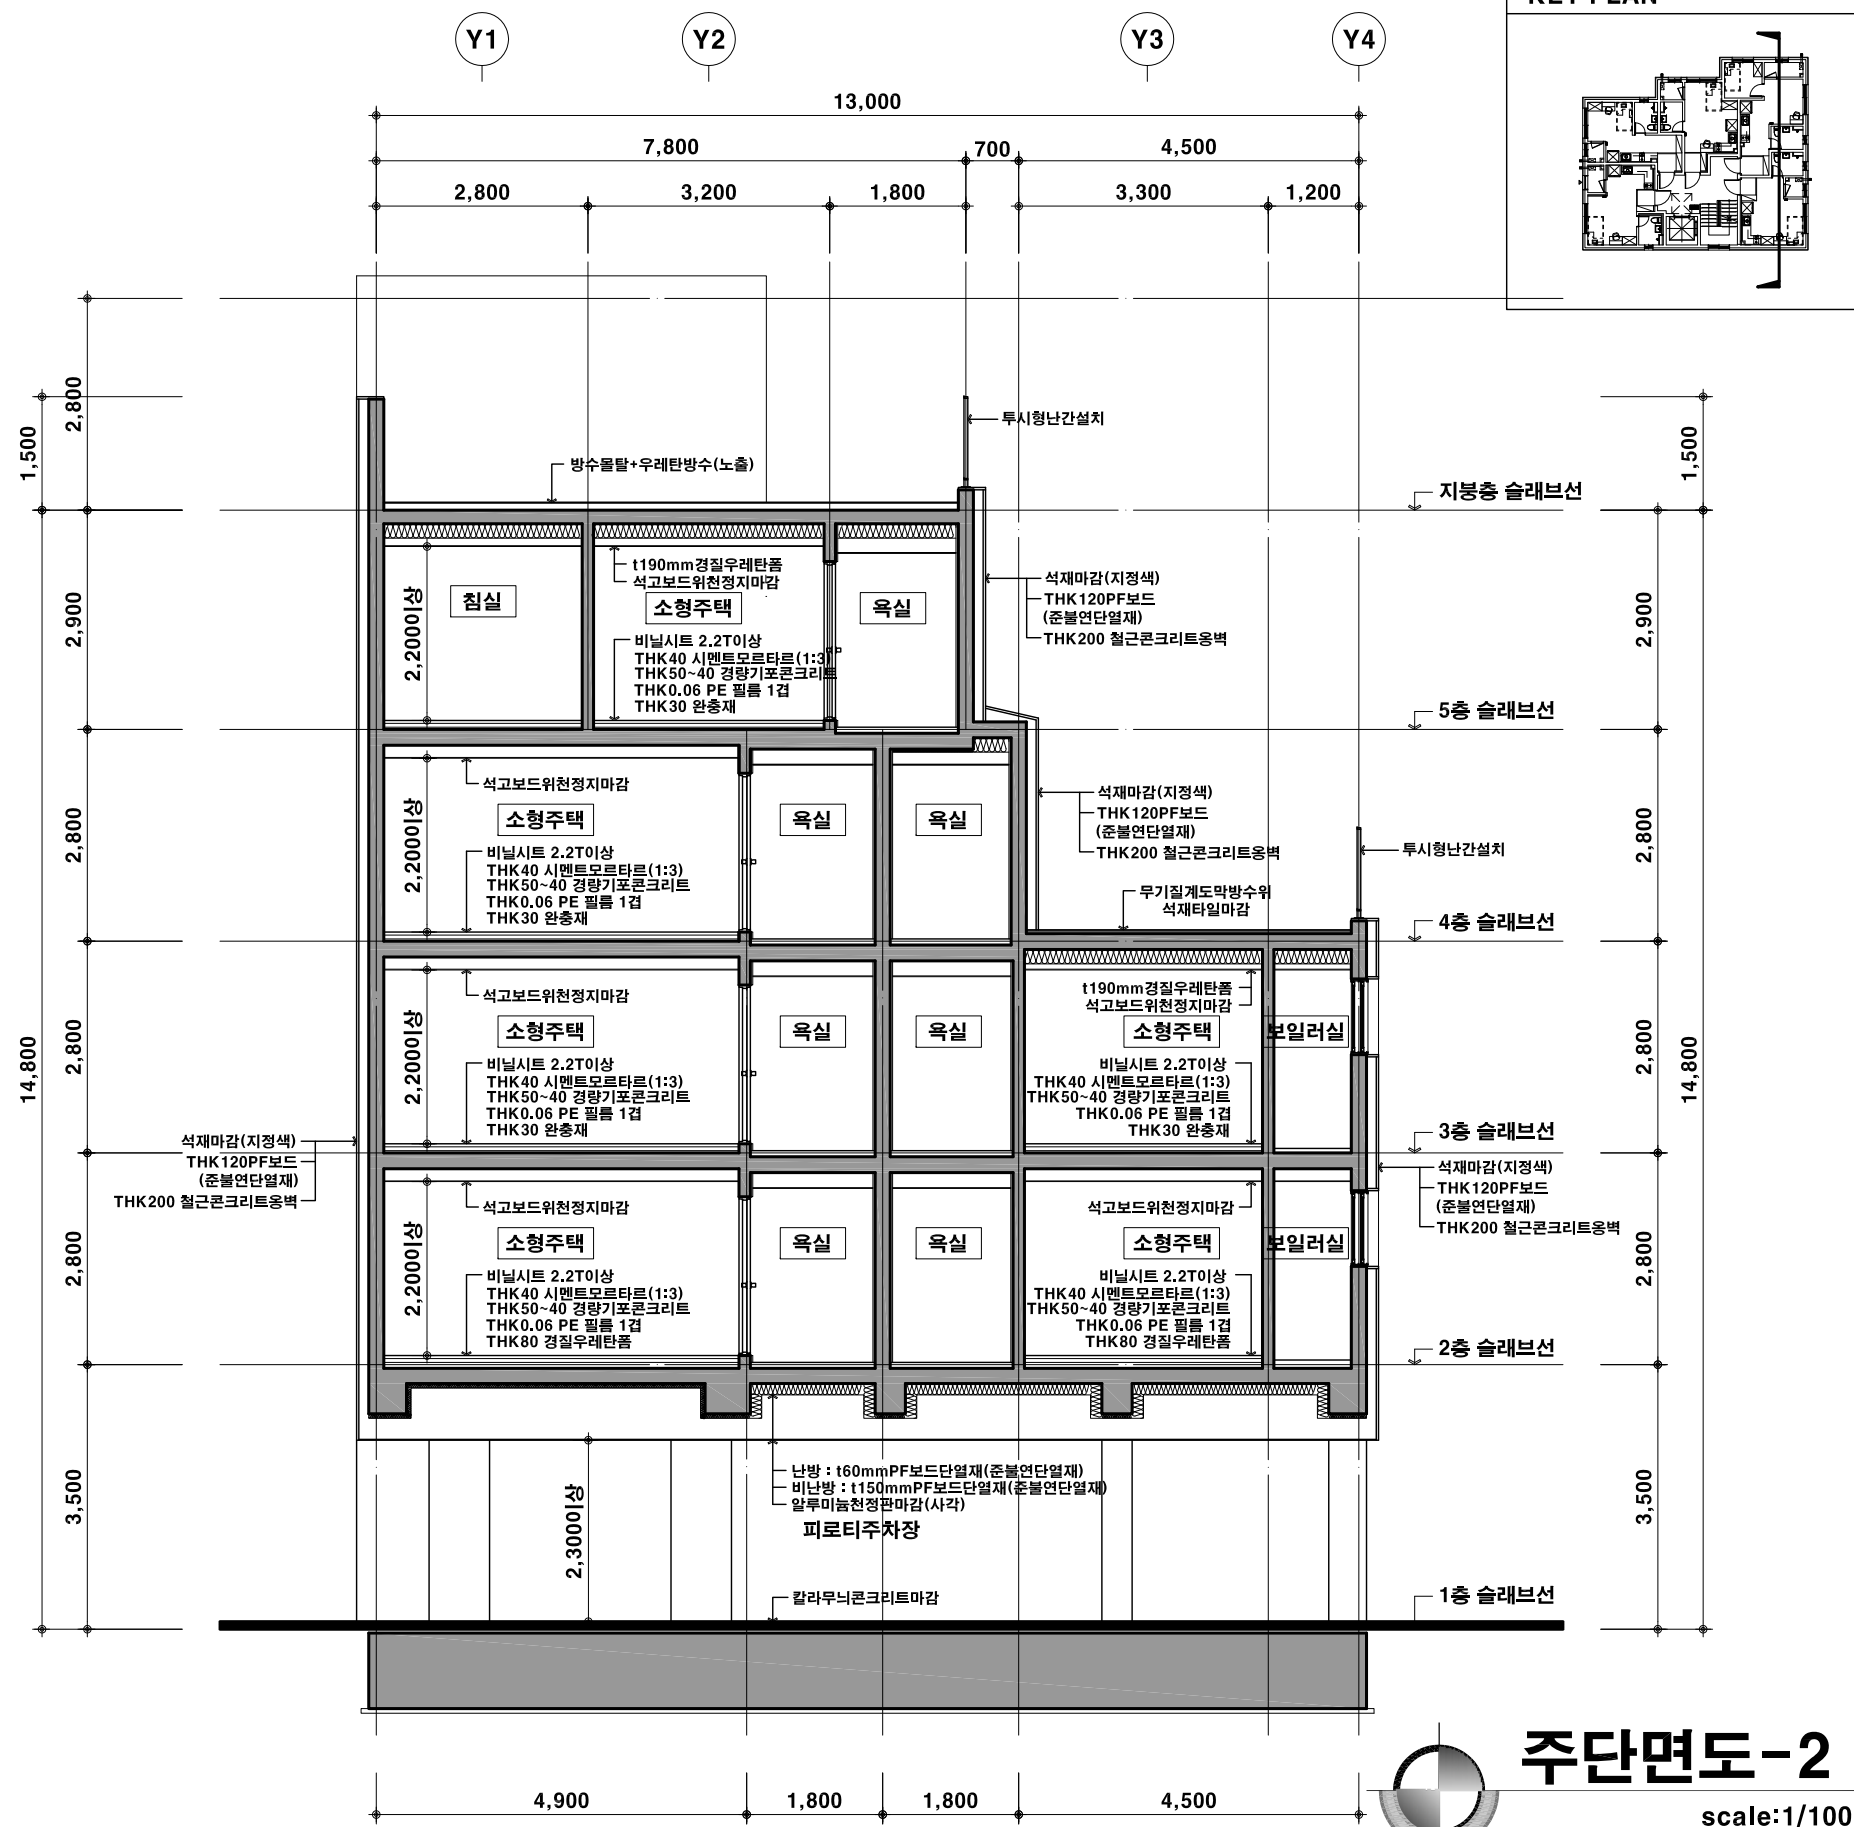

욕상지붕 바닥

- t180mm스라브
- t190mm경질우레탄폼
- t9.5mm석고보드
- 천정지마감
- t10mm아이소핑크
- 타설시 부착

*방수시모접기시공
(테라스/옥상~~)

우레탄방수위탁코팅

참금콘크리트스LAB

실외

실내

슬라브
단열재
t9.5mm 석고보드
천정지마감

t110mm 아이소핑크
타설시 부착

Diagram illustrating the cross-section of a wall and floor assembly, showing the materials and dimensions:

- 비닐시트 2.2T이상
- 마감도마트르40mm이상
- 경량자포콘크리트40mm이상
- 완충재30mm이상
- 콘크리트슬래브210mm이상
- ~걸레받이
- 시멘트몰탈위 석재마감
- 60
- 40
- 40
- 30

<< 완충재 성능 기준참조 >>

NO	DATE	REVISION DESCRIPTION	DRWN	CHK'D	APPD	PROJECT TITLE	CHK'D BY	SCALE	DRAWING TITLE	B.C.C NO	JOB NO	APPROVE D BY
01		사용승인				공 사 명 송파구 오금동 119-18번지 도시형생활주택(소형주택) 신축공사		1 / 100	도 면 명			
								2026.01	주단면도-2	DRWG NO		DESIGNED BY
								DRWN BY			A - 023	

*방수시도접기시공
(욕실/다용도실/발코니~~)

실내

실내

물받이자리
방수처리


알루미늄크리드

석고보드

방수층

실내

단열재 범위			
위치		두께	재질
주차장 (천정)	난방	60	PF보드단열재 (준불연단열재)
	비난방	150	
2층 바닥		80	경질우레탄폼
지붕층		190	경질우레탄폼
외벽	직접	120	PF보드단열재 (준불연단열재)
	간접	80	경질우레탄폼

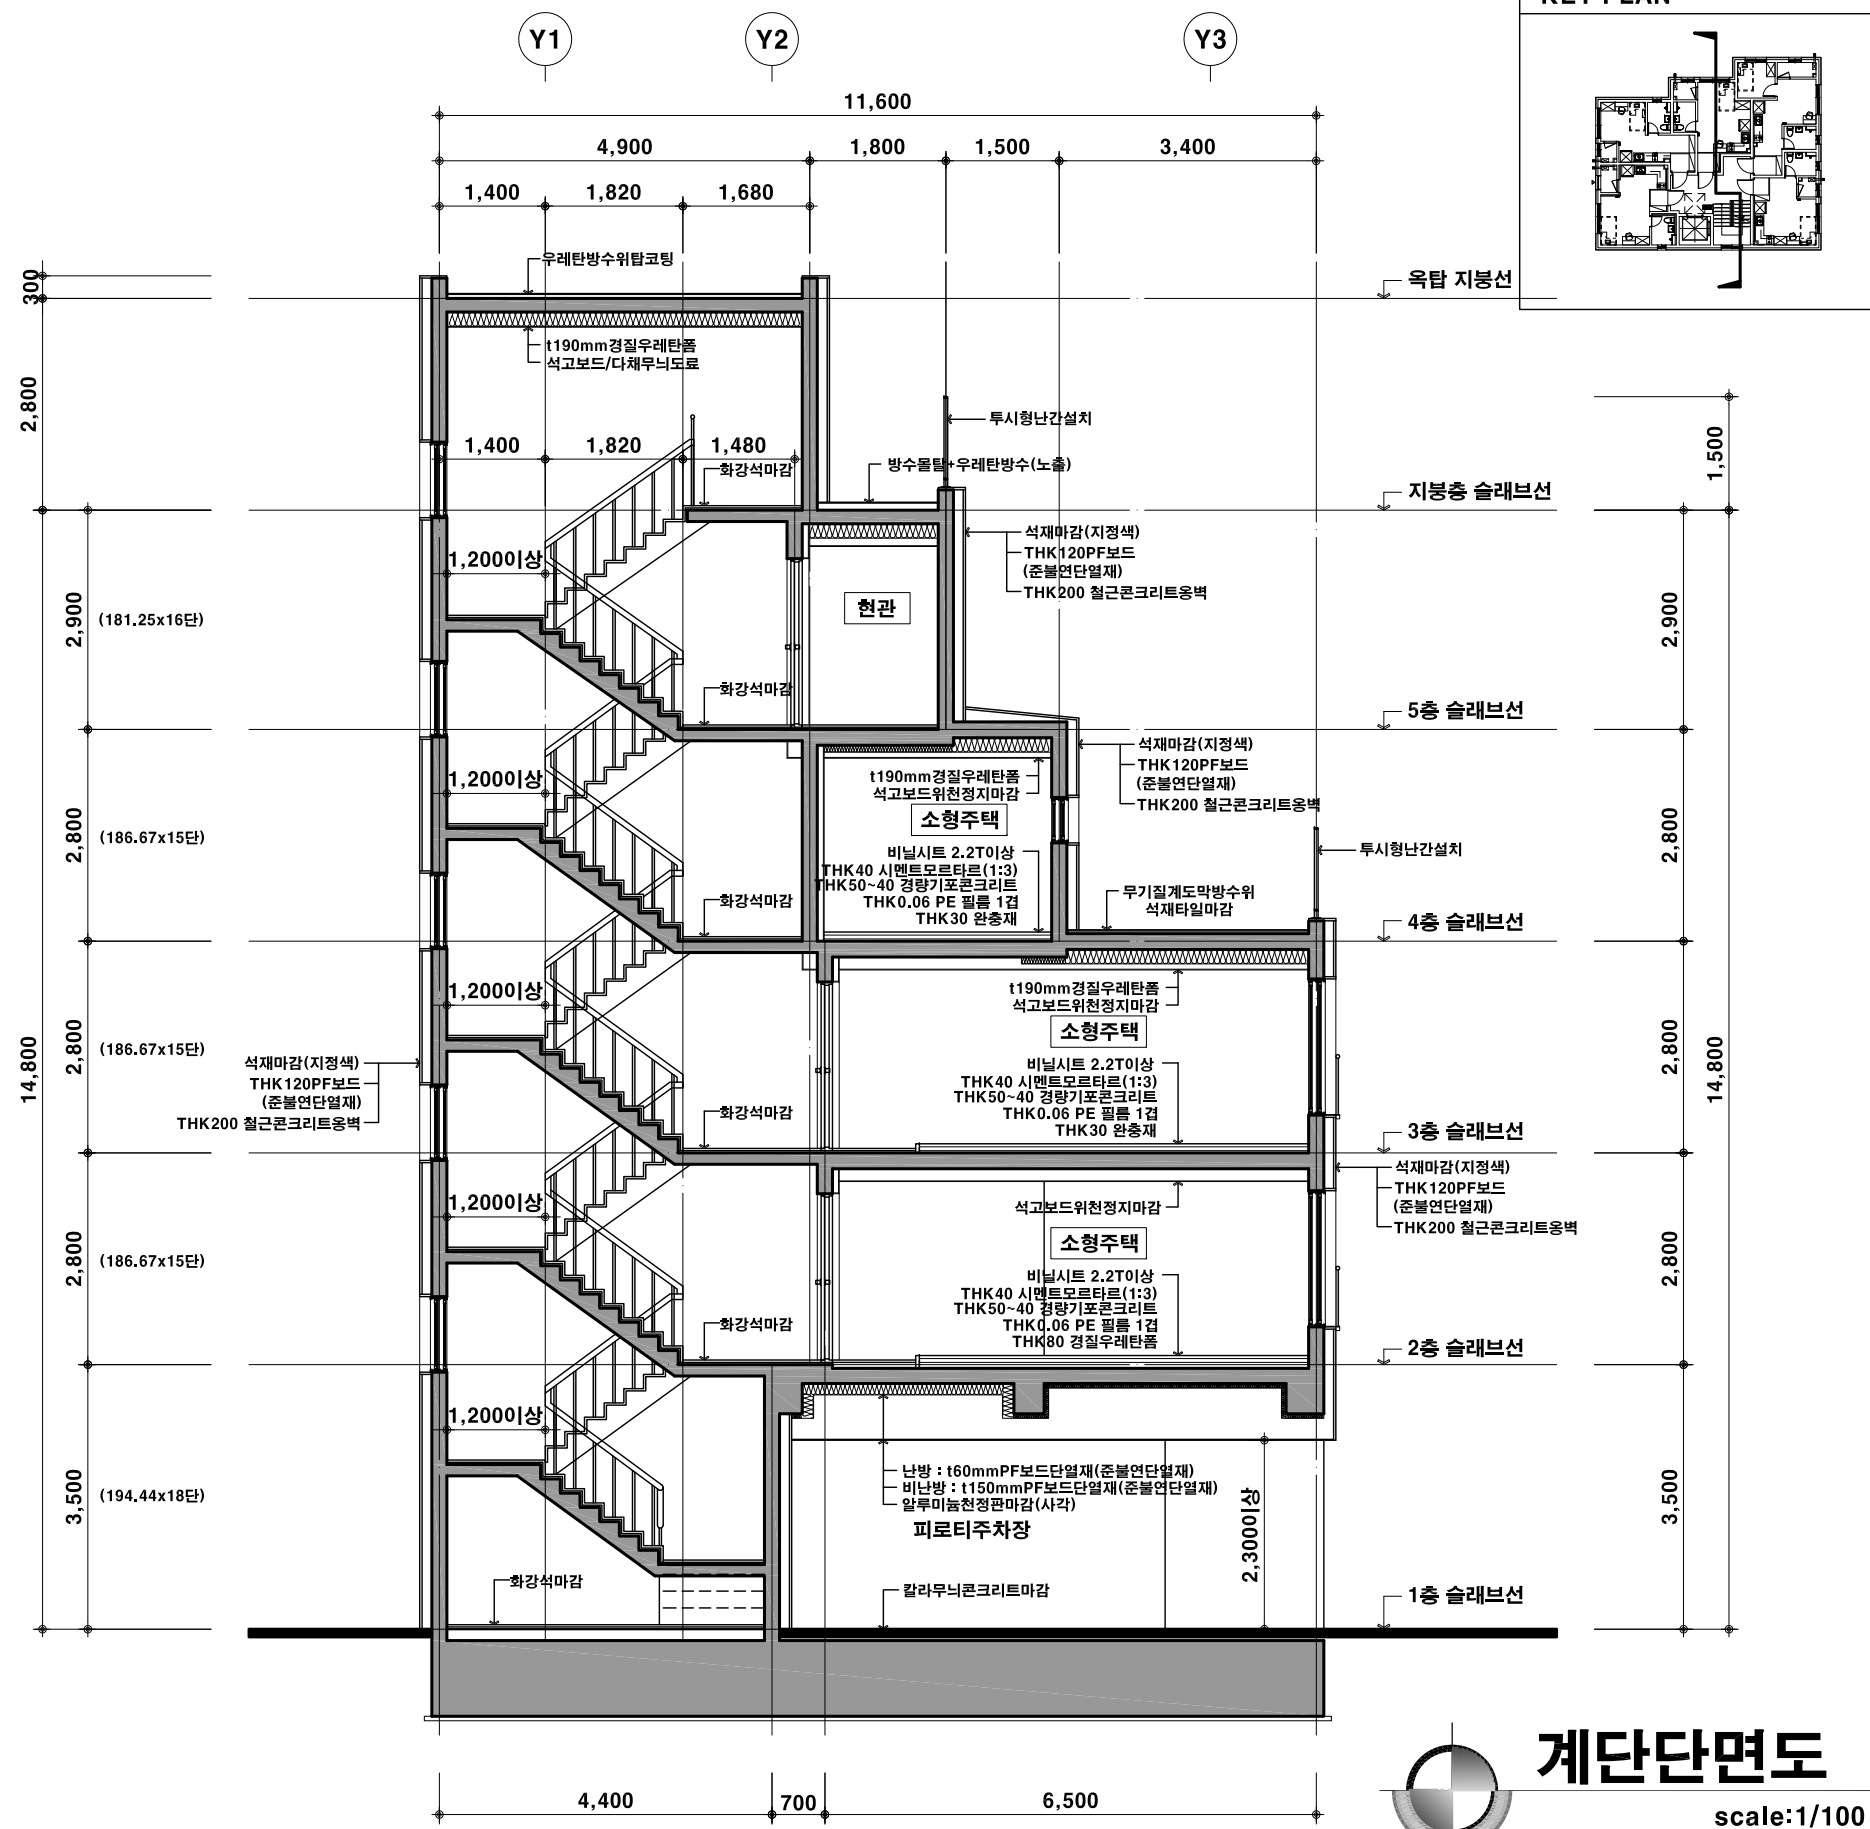

욕상지붕 바닥

- t180mm슬라브
- t190mm경질우레탄폼
- t9.5mm석고보드
- 천정지마감
- t10mm아이스핑크
- 타설시 부착

*방수시모접기시공
(테라스/옥상~~)

우레탄방수위탁코팅

철근콘크리트슬라브

실외

실내

슬라브
단열재
t9.5mm 석고보드
천정지마감

t10mm 아이소폼크
타설시 부착

비닐시트 2.2T이상
 마감모르타르 40mm이상
 경량가포콘크리트 40mm이상
 완충재 30mm이상
 콘크리트슬래브 210mm이상

~겉레받이

시멘트몰탈위 석재마감

40
 40
 30

60

<< 완충재 성능 기준참조 >>

NO	DATE	REVISION DESCRIPTION	DRWN	CHK'D	APPD	PROJECT TITLE	CHK'D BY	SCALE	DRAWING TITLE	B.C.C NO	JOB NO	APPROVE D BY
01		사용승인				공 사 명 송파구 오금동 119-18번지 도시형생활주택(소형주택) 신축공사		1 / 100	도 면 명			
								2026.01	계단단면도	DRWG NO		DESIGNED BY
								DRWN BY			A - 024	