


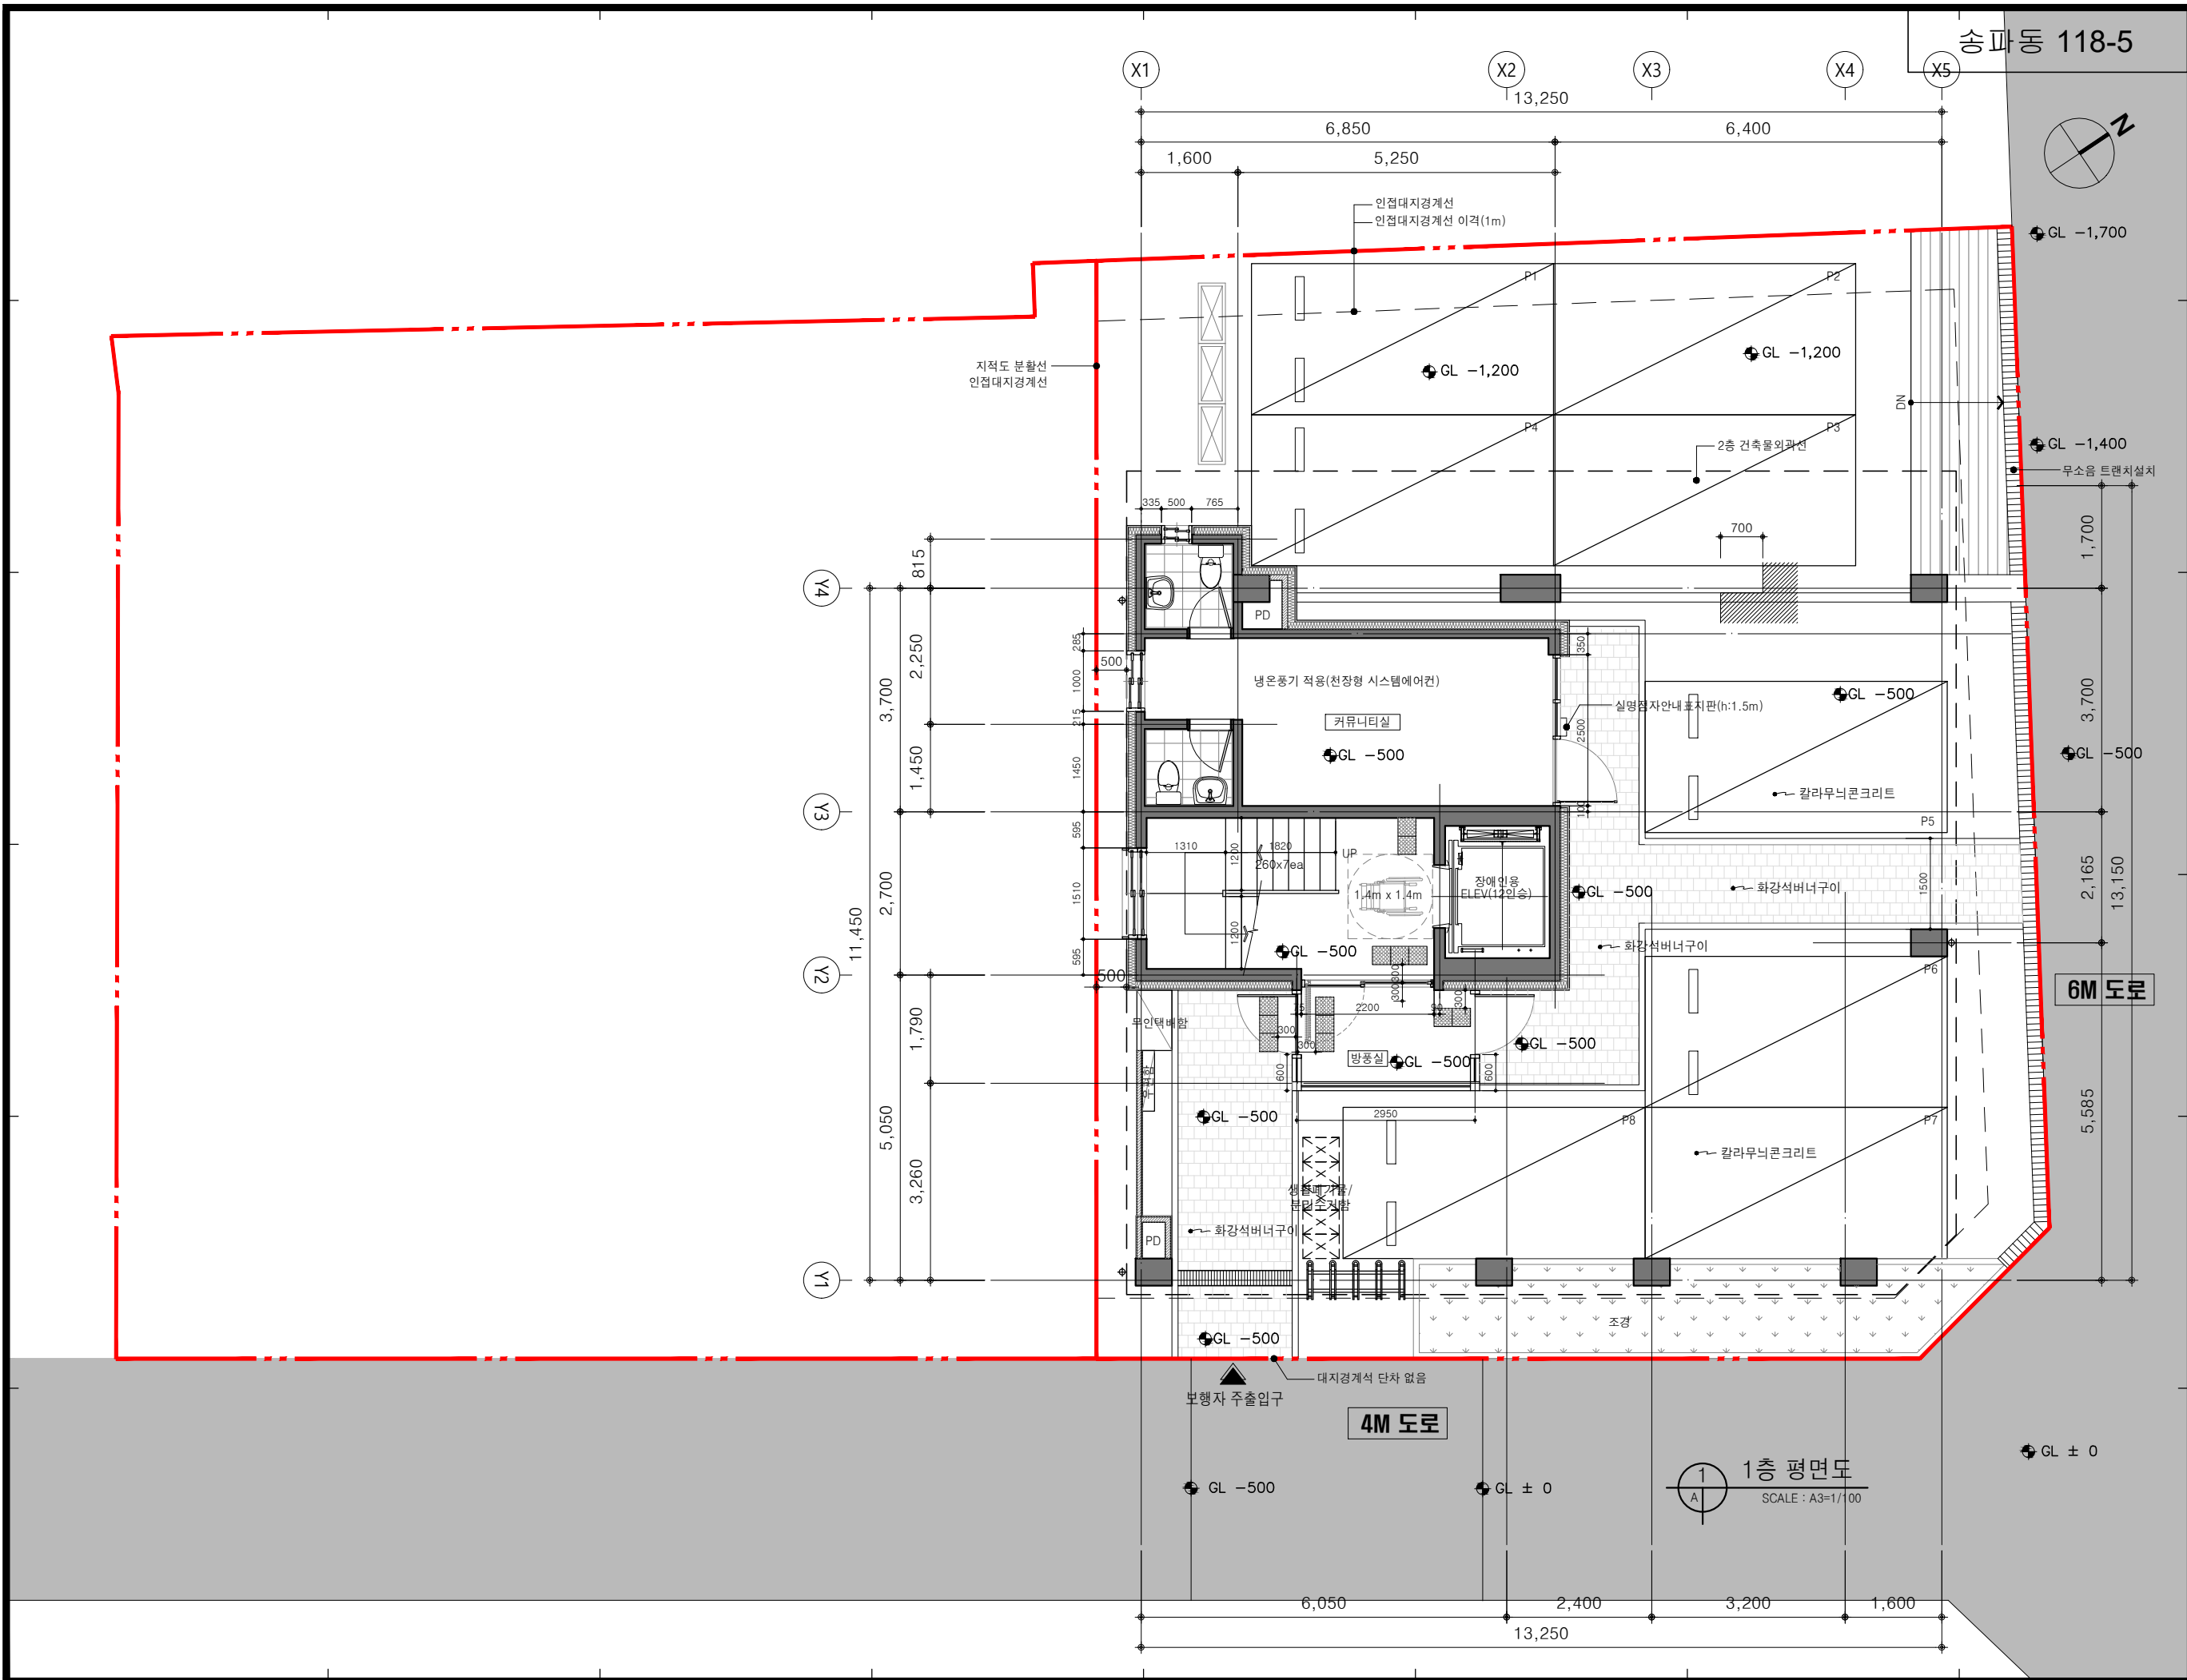

승파동 118-5



(주) 동심원건축사사무소

TEL : 02)3452-0597

FAX : 02)3452-0598

설계명 PROJECT TITLE

송파구 송파동

도시형생활주택 신축공사

주 기 NOTE

NO.	DATE	REVISION	DRAWN	APP.
1				
2				
3				

설 계	DRAWN	검 토	CHECK
심 사	SUBMIT	승 인	APPROVE

축 척	SCALE
A1	1 / 50
A3	1 / 100


일 자	DATE

설계번호	PROJECT NO.


도면파일명	DWG. FILE NAME

도면번호	SHEET NO.
A	- 101

도면명	SUBJECT TITLE
	1층 평면도

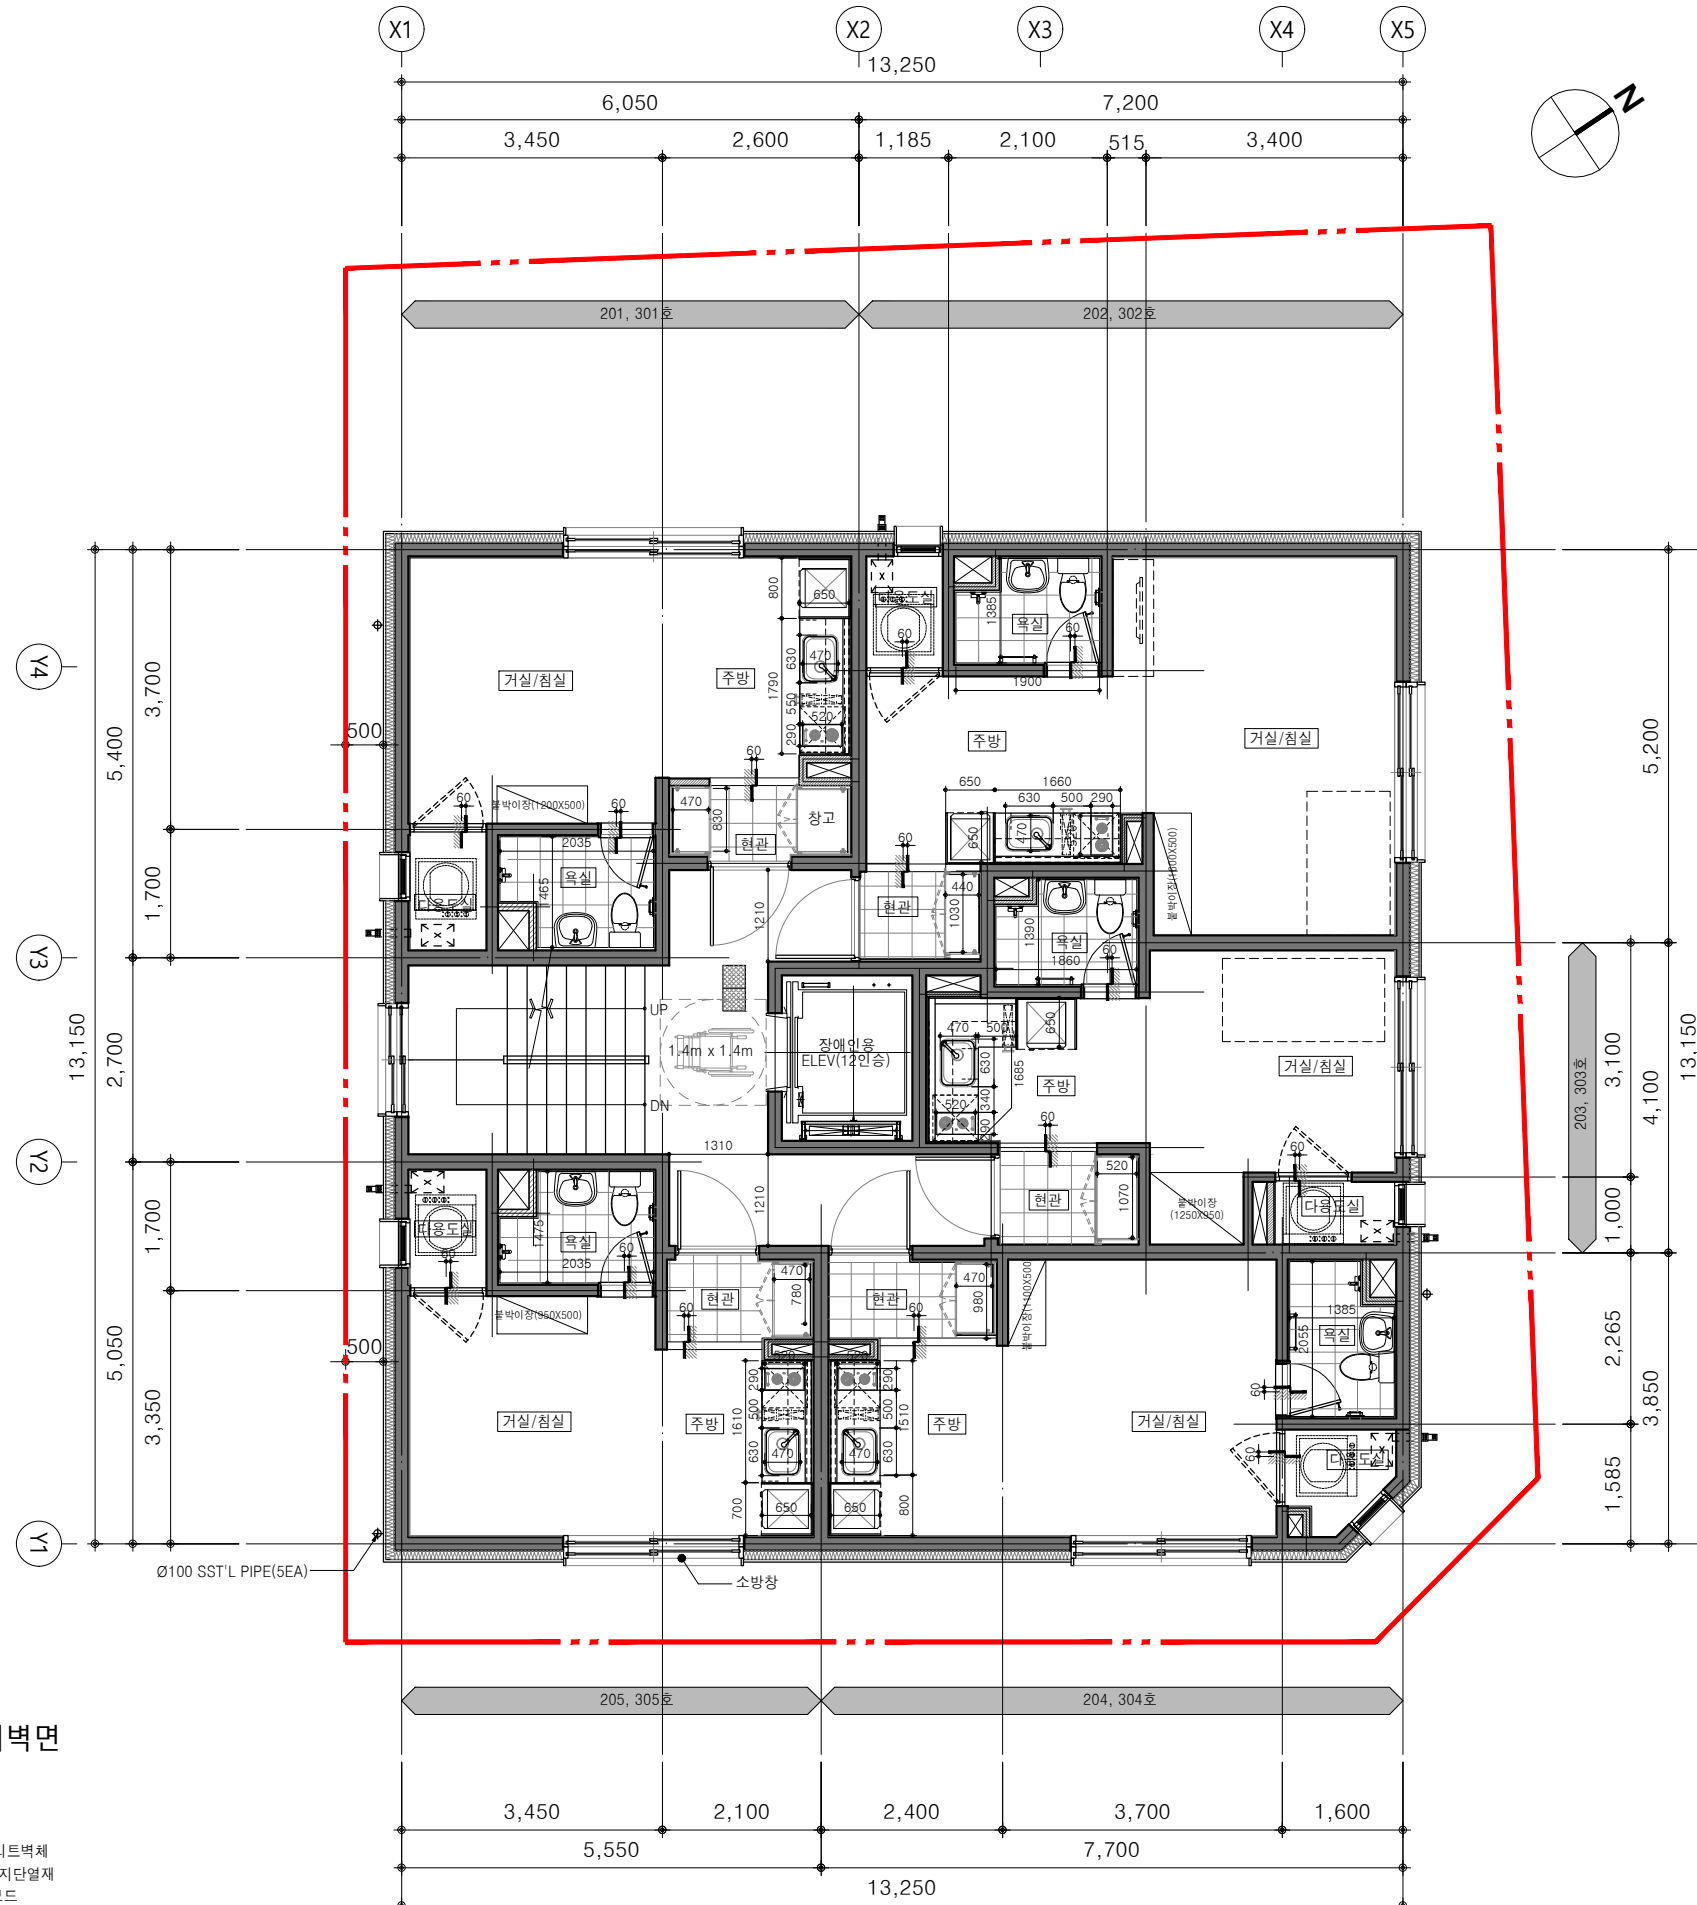

■ 간접외기에 면한 실내벽면

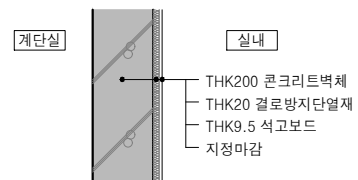

■ 빌트인설치 내역


구분	세탁기	냉장고	에어컨 (벽걸이)	전자 레인지
설치 유무	○	○	○	○

* 냉장고 상부 전자레인지 / 쿡탑 하부 세탁기 설치


2~3층 평면도

SCALE : A3=1/100

NO.	DATE	REVISION	DRAWN	APP.
1				
2				
3				
설 계	DRAWN	검 토	CHECK	
심 사	SUBMIT	승 인	APPROVE	
축 척	SCALE			
A1	1 / 50			
A3	1 / 100			
일 자	DATE			
설계번호	PROJECT NO.			
도면파일명	DWG. FILE NAME			
도면번호	SHEET NO.			
	A - 102			
도면명	SUBJECT TITLE			
	2~3층 평면도			

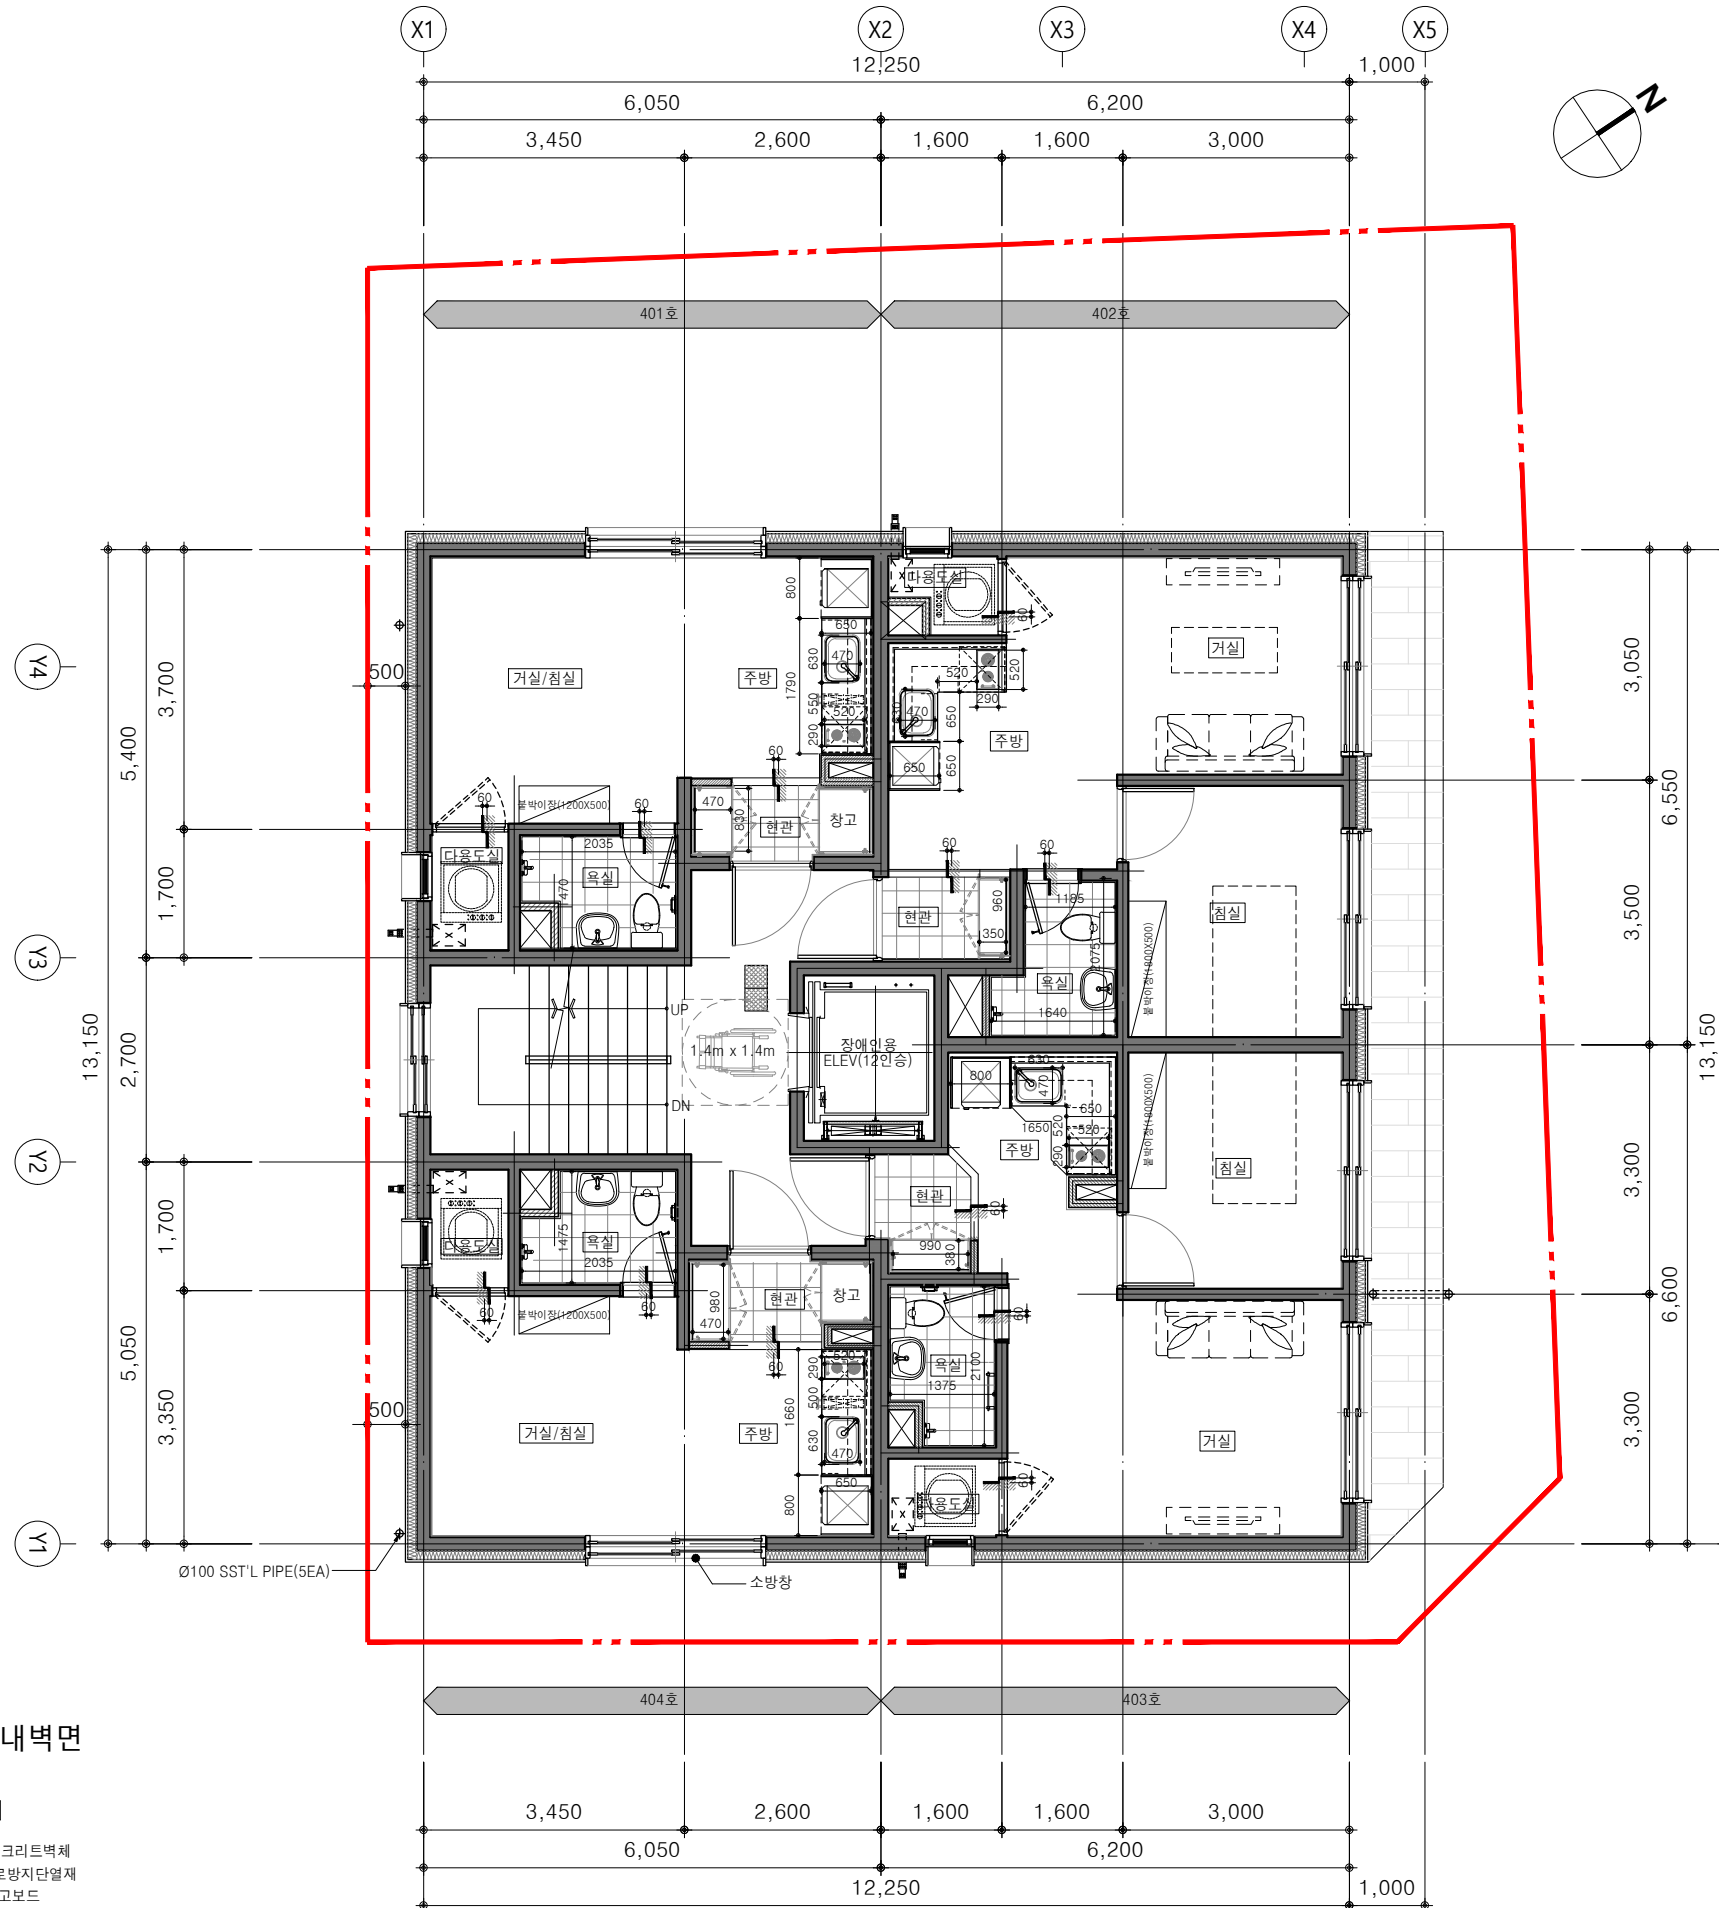

■ 간접외기에 면한 실내벽면

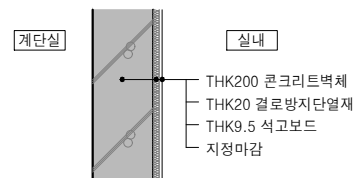

■ 빌트인설치 내역

구분	세탁기	냉장고	에어컨 (벽걸이)	전자 레인지
설치 유무	○	○	○	○

* 냉장고 상부 전자레인지 / 쿡탑 하부 세탁기 설치

4층 평면도
SCALE : A3=1/100

NO. DATE REVISION DRAWN APP.

1				
2				
3				

설 계 DRAWN 검토 CHECK

심 사 SUBMIT 승인 APPROVE

축 척 SCALE

A1	1 / 50
A3	1 / 100

일 자 DATE

설계번호 PROJECT NO.


도면파일명 DWG. FILE NAME

도면번호 SHEET NO.


A - 103

도면명 SUBJECT TITLE

4층 평면도

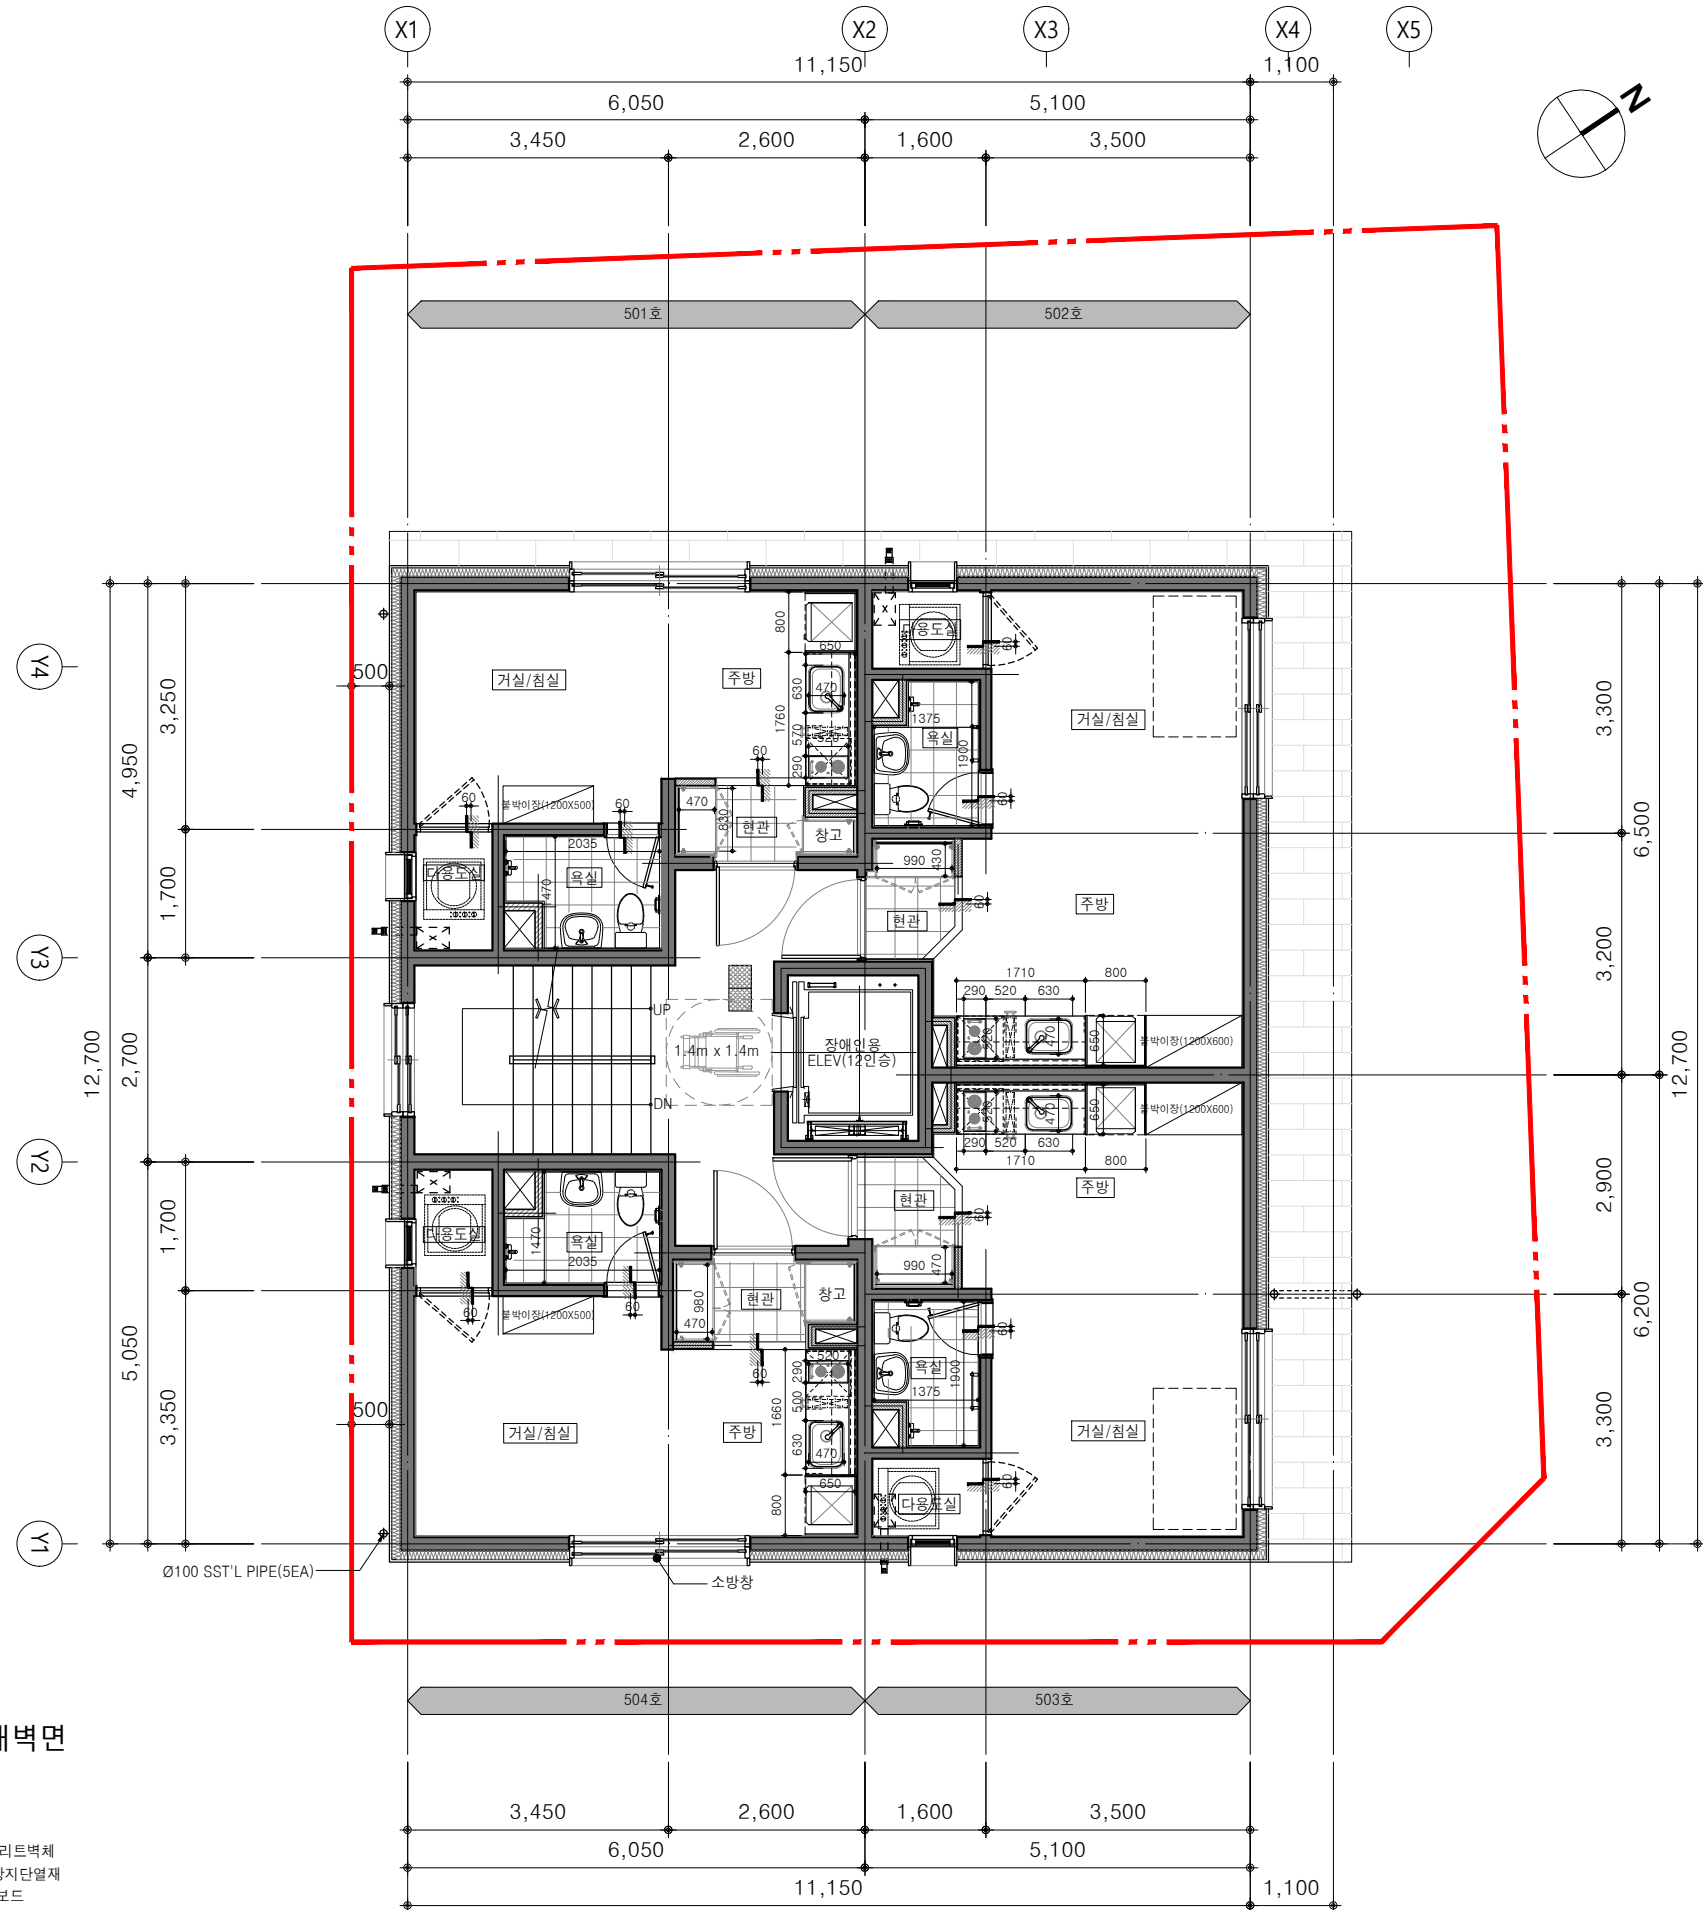

■ 간접외기에 면한 실내벽면

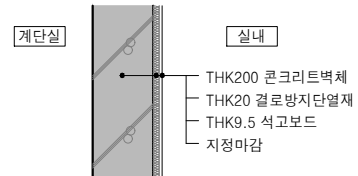

■ 빌트인설치 내역

구분	세탁기	냉장고	에어컨 (벽걸이)	전자 레인지
설치 유무	○	○	○	○

* 냉장고 상부 전자레인지 / 쿡탑 하부 세탁기 설치

1 5층 평면도
SCALE : A3=1/100

NO. DATE REVISION DRAWN APP.

1				
2				
3				

설 계 DRAWN 검토 CHECK

심 사 SUBMIT 승인 APPROVE

축 척 SCALE

A1	1 / 50
A3	1 / 100

일 자 DATE

설계번호 PROJECT NO.


도면파일명 DWG. FILE NAME

도면번호 SHEET NO.

A - 104


도면명 SUBJECT TITLE

5층 평면도

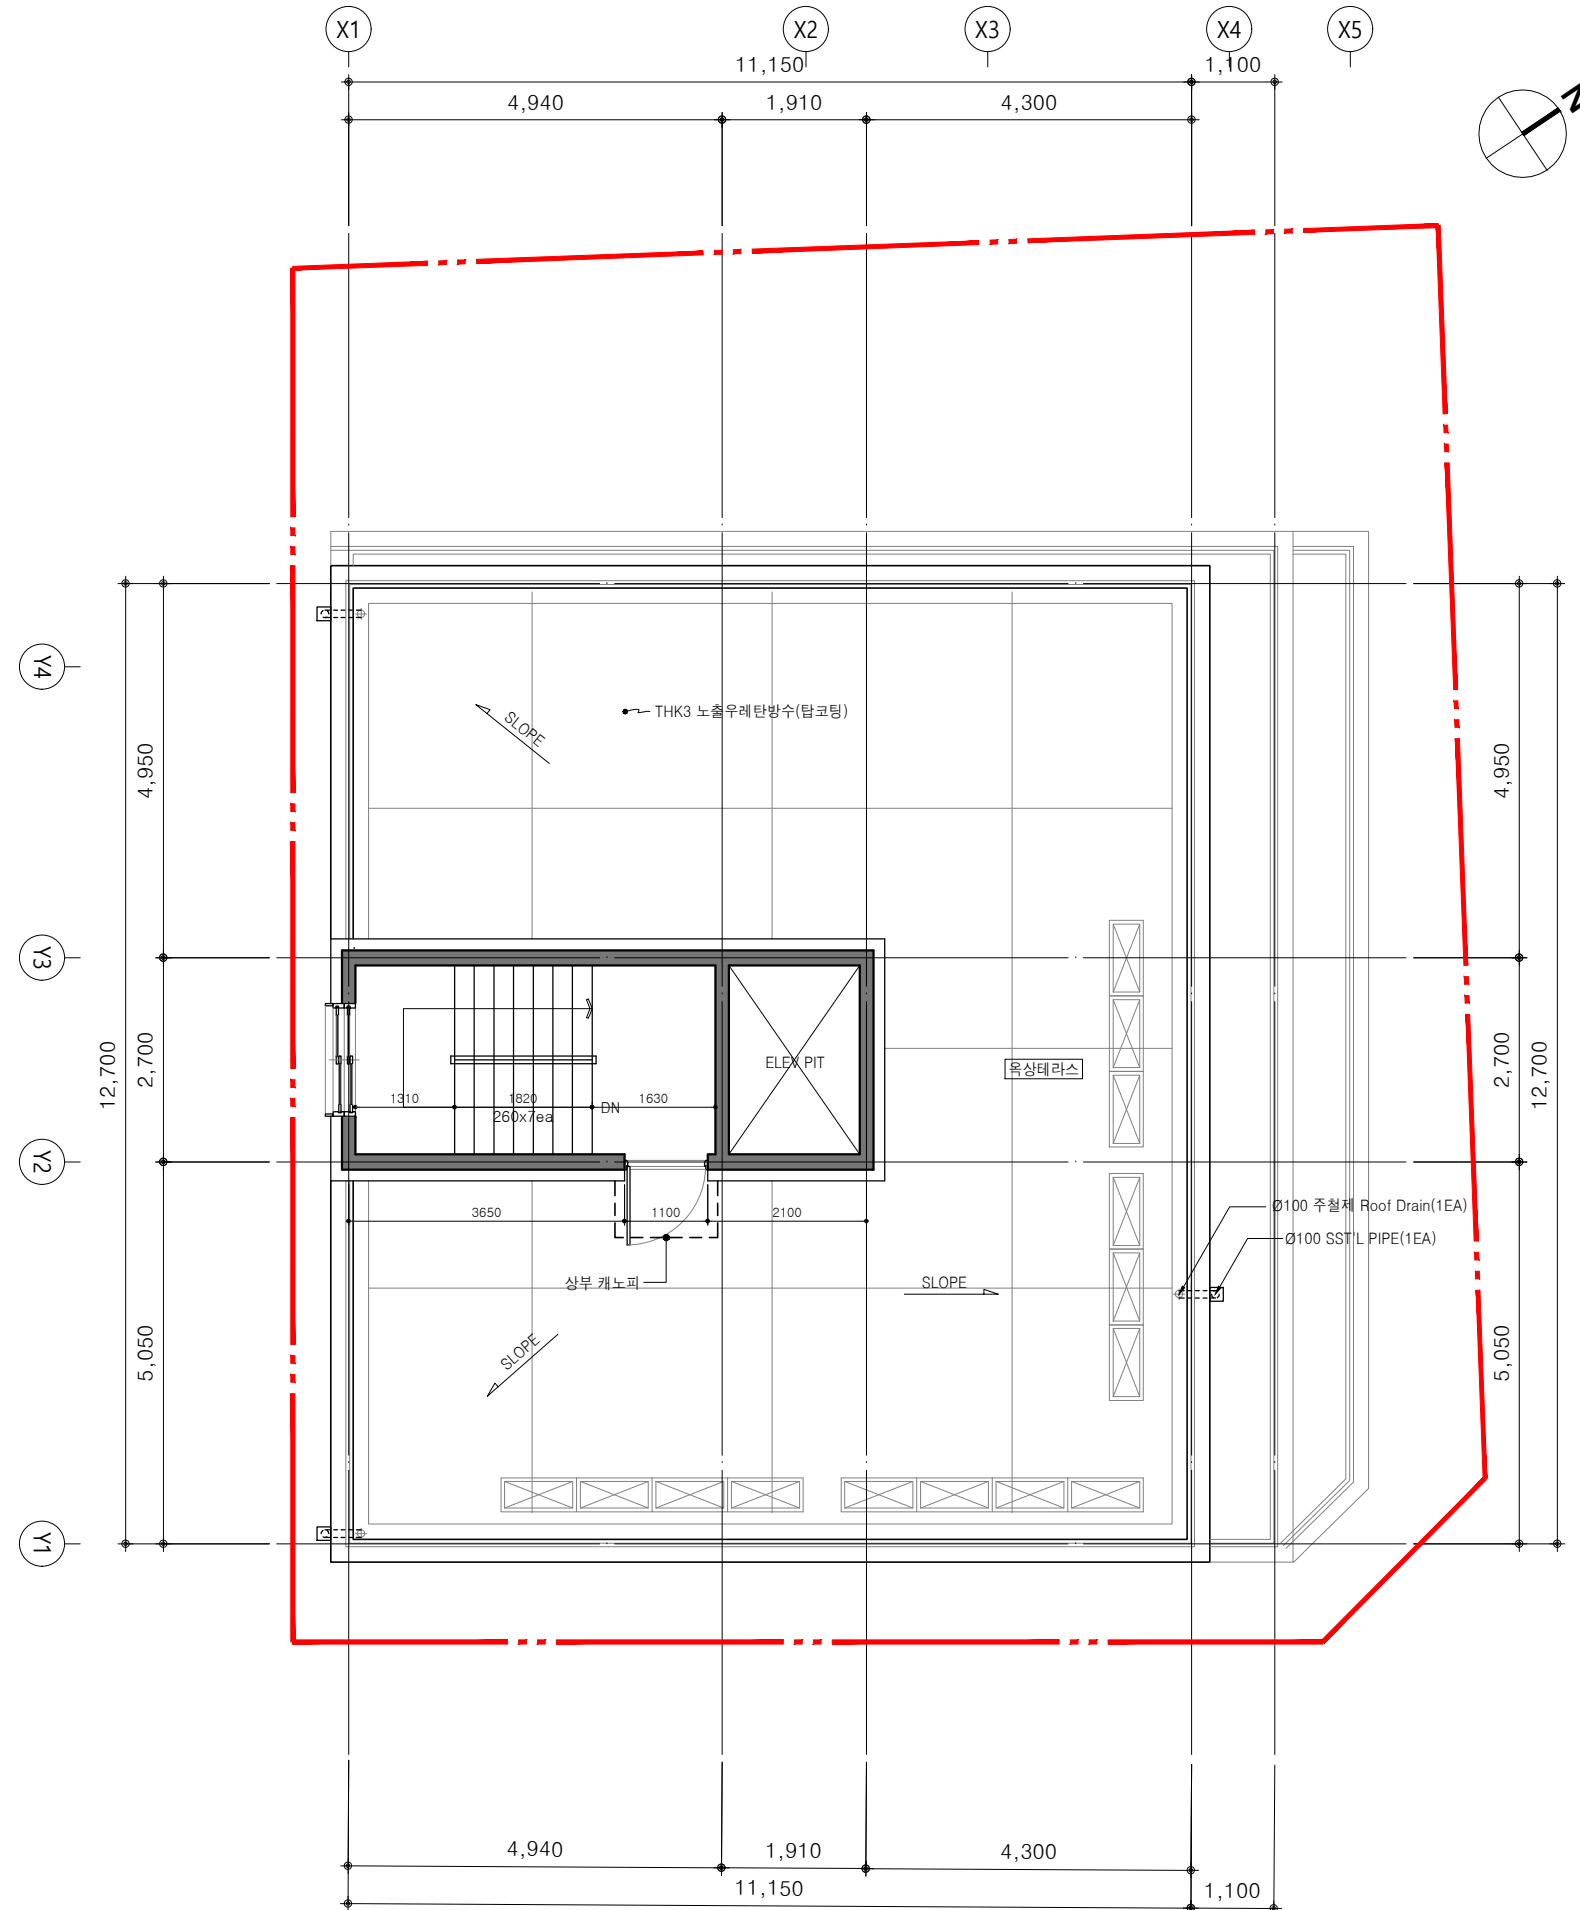

■ 파라펫 입면도

매립박스 설치 파라펫

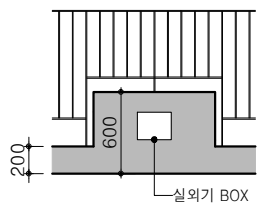

1 지붕층 평면도
SCALE : A3=1/100

NO. DATE REVISION DRAWN APP.

1				
2				
3				

설 계 DRAWN 검 토 CHECK

심 사 SUBMIT 승 인 APPROVE

축 척 SCALE

A1	1 / 50
A3	1 / 100

일 자 DATE

설계번호 PROJECT NO.

도면파일명 DWG. FILE NAME

도면번호 SHEET NO.

A - 105

도면명 SUBJECT TITLE

지붕층 평면도




(주) 동심원건축사사무소

TEL : 02)3452-0597
FAX : 02)3452-0598

설계명 PROJECT TITLE

송파구 송파동
도시형생활주택 신축공사

주 기 NOTE

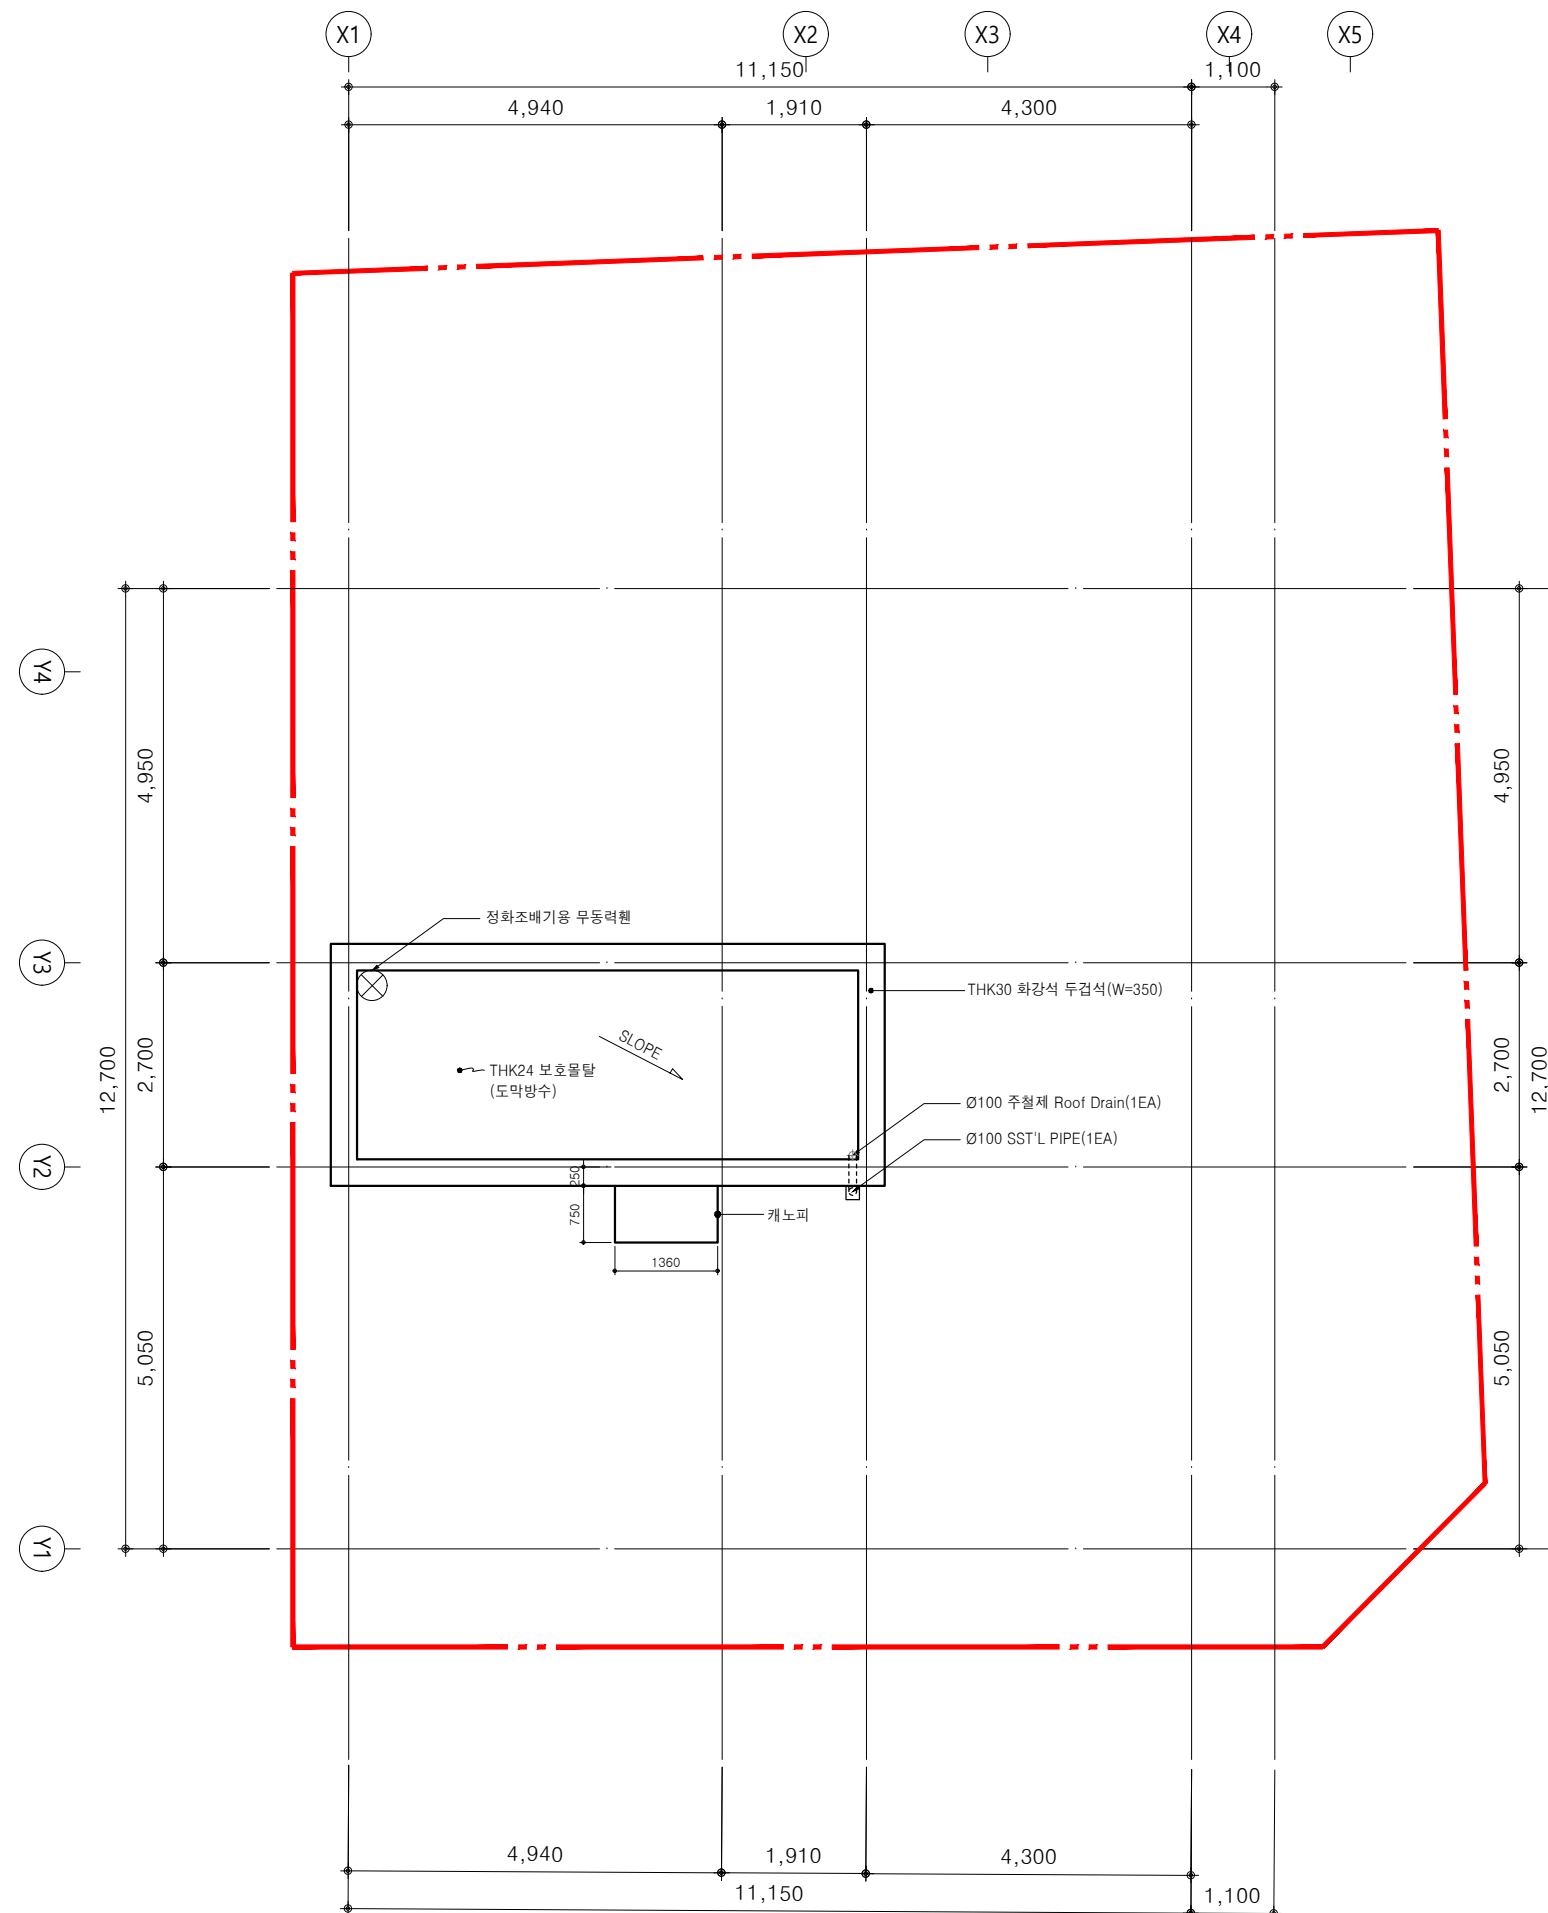

옥탑 평면도

SCALE : A3=1/100

NO. DATE REVISION DRAWN APP.

1				
2				
3				

설 계 DRAWN

검 토 CHECK

심 사 SUBMIT

승 인 APPROVE

축 척 SCALE

A1	1 / 50
A3	1 / 100

일 자 DATE

설계번호 PROJECT NO.

도면파일명 DWG. FILE NAME


도면번호 SHEET NO.

A - 106

도면명 SUBJECT TITLE


옥탑 평면도

■ Key plan

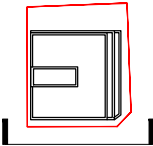

정면도
SCALE : A3=1/150

■ Key plan

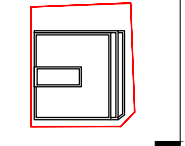

우측면도
SCALE : A3=1/150

NO. DATE REVISION DRAWN APP.

1				
2				
3				

설 계 DRAWN 검토 CHECK

심 사 SUBMIT 승인 APPROVE

축 척 SCALE

A1 1 /

A3 1 / 150

일 자 DATE

설계번호 PROJECT NO.

도면파일명 DWG. FILE NAME


도면번호 SHEET NO.

A - 301


도면명 SUBJECT TITLE

입면도-1


■ Key plan

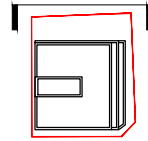

■ Key plan

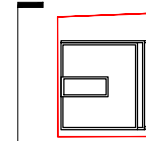

1
A 배면도
SCALE : A3=1/150

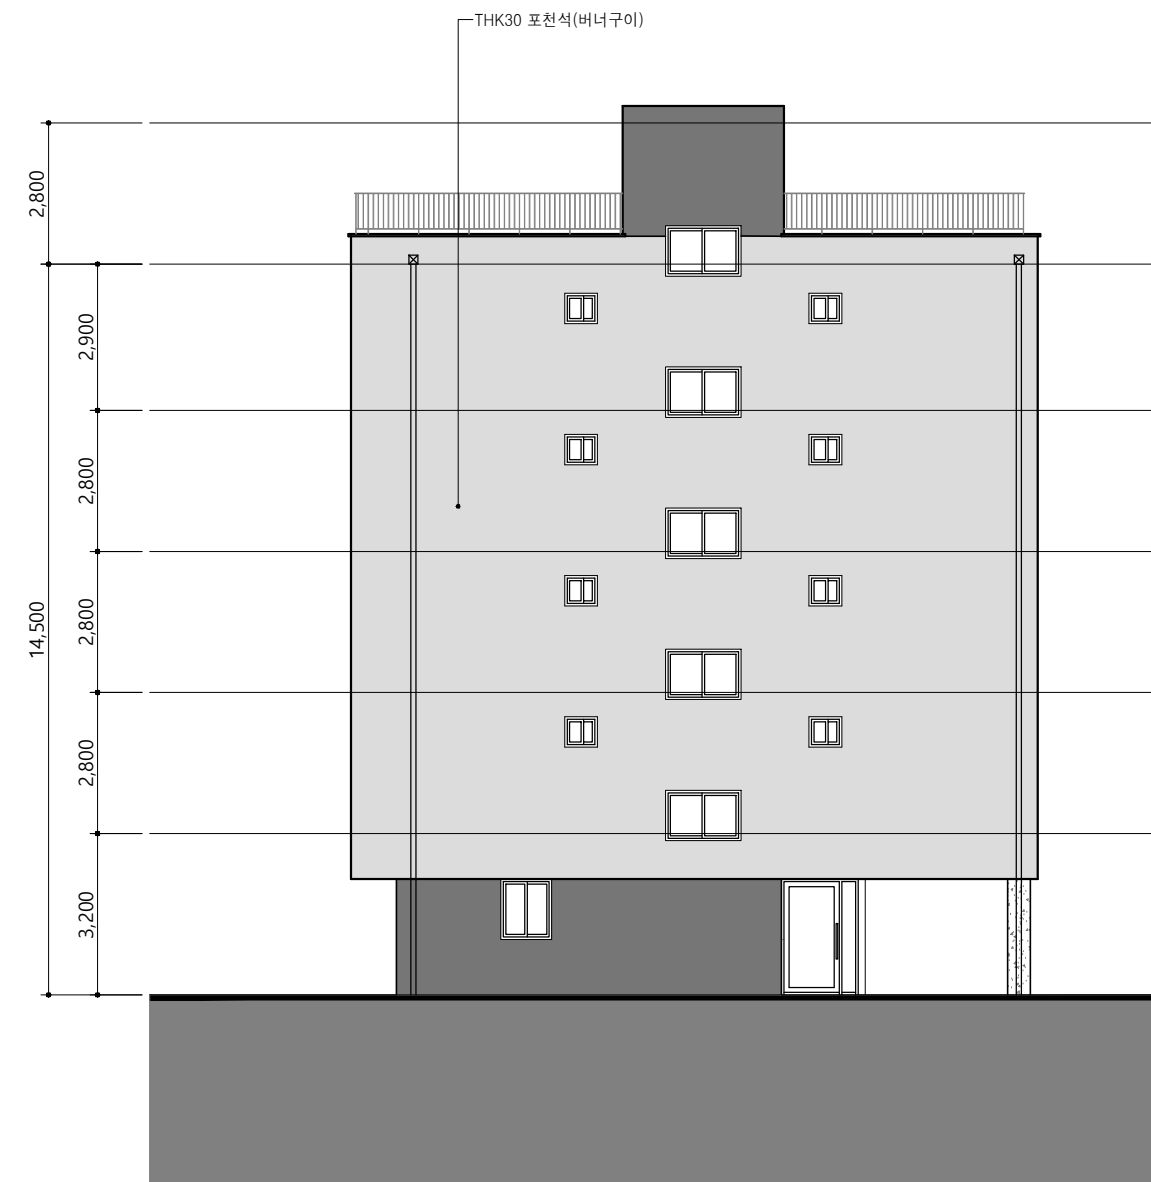

1
A 좌측면도
SCALE : A3=1/150

NO. DATE REVISION DRAWN APP.

1				
2				
3				

설 계 DRAWN 검토 CHECK

심 사 SUBMIT 승인 APPROVE

축 척 SCALE

A1 1 /

A3 1 / 150

일 자 DATE

설계번호 PROJECT NO.

도면파일명 DWG. FILE NAME



도면번호 SHEET NO.

A - 302

도면명 SUBJECT TITLE

입면도-2

Key plan

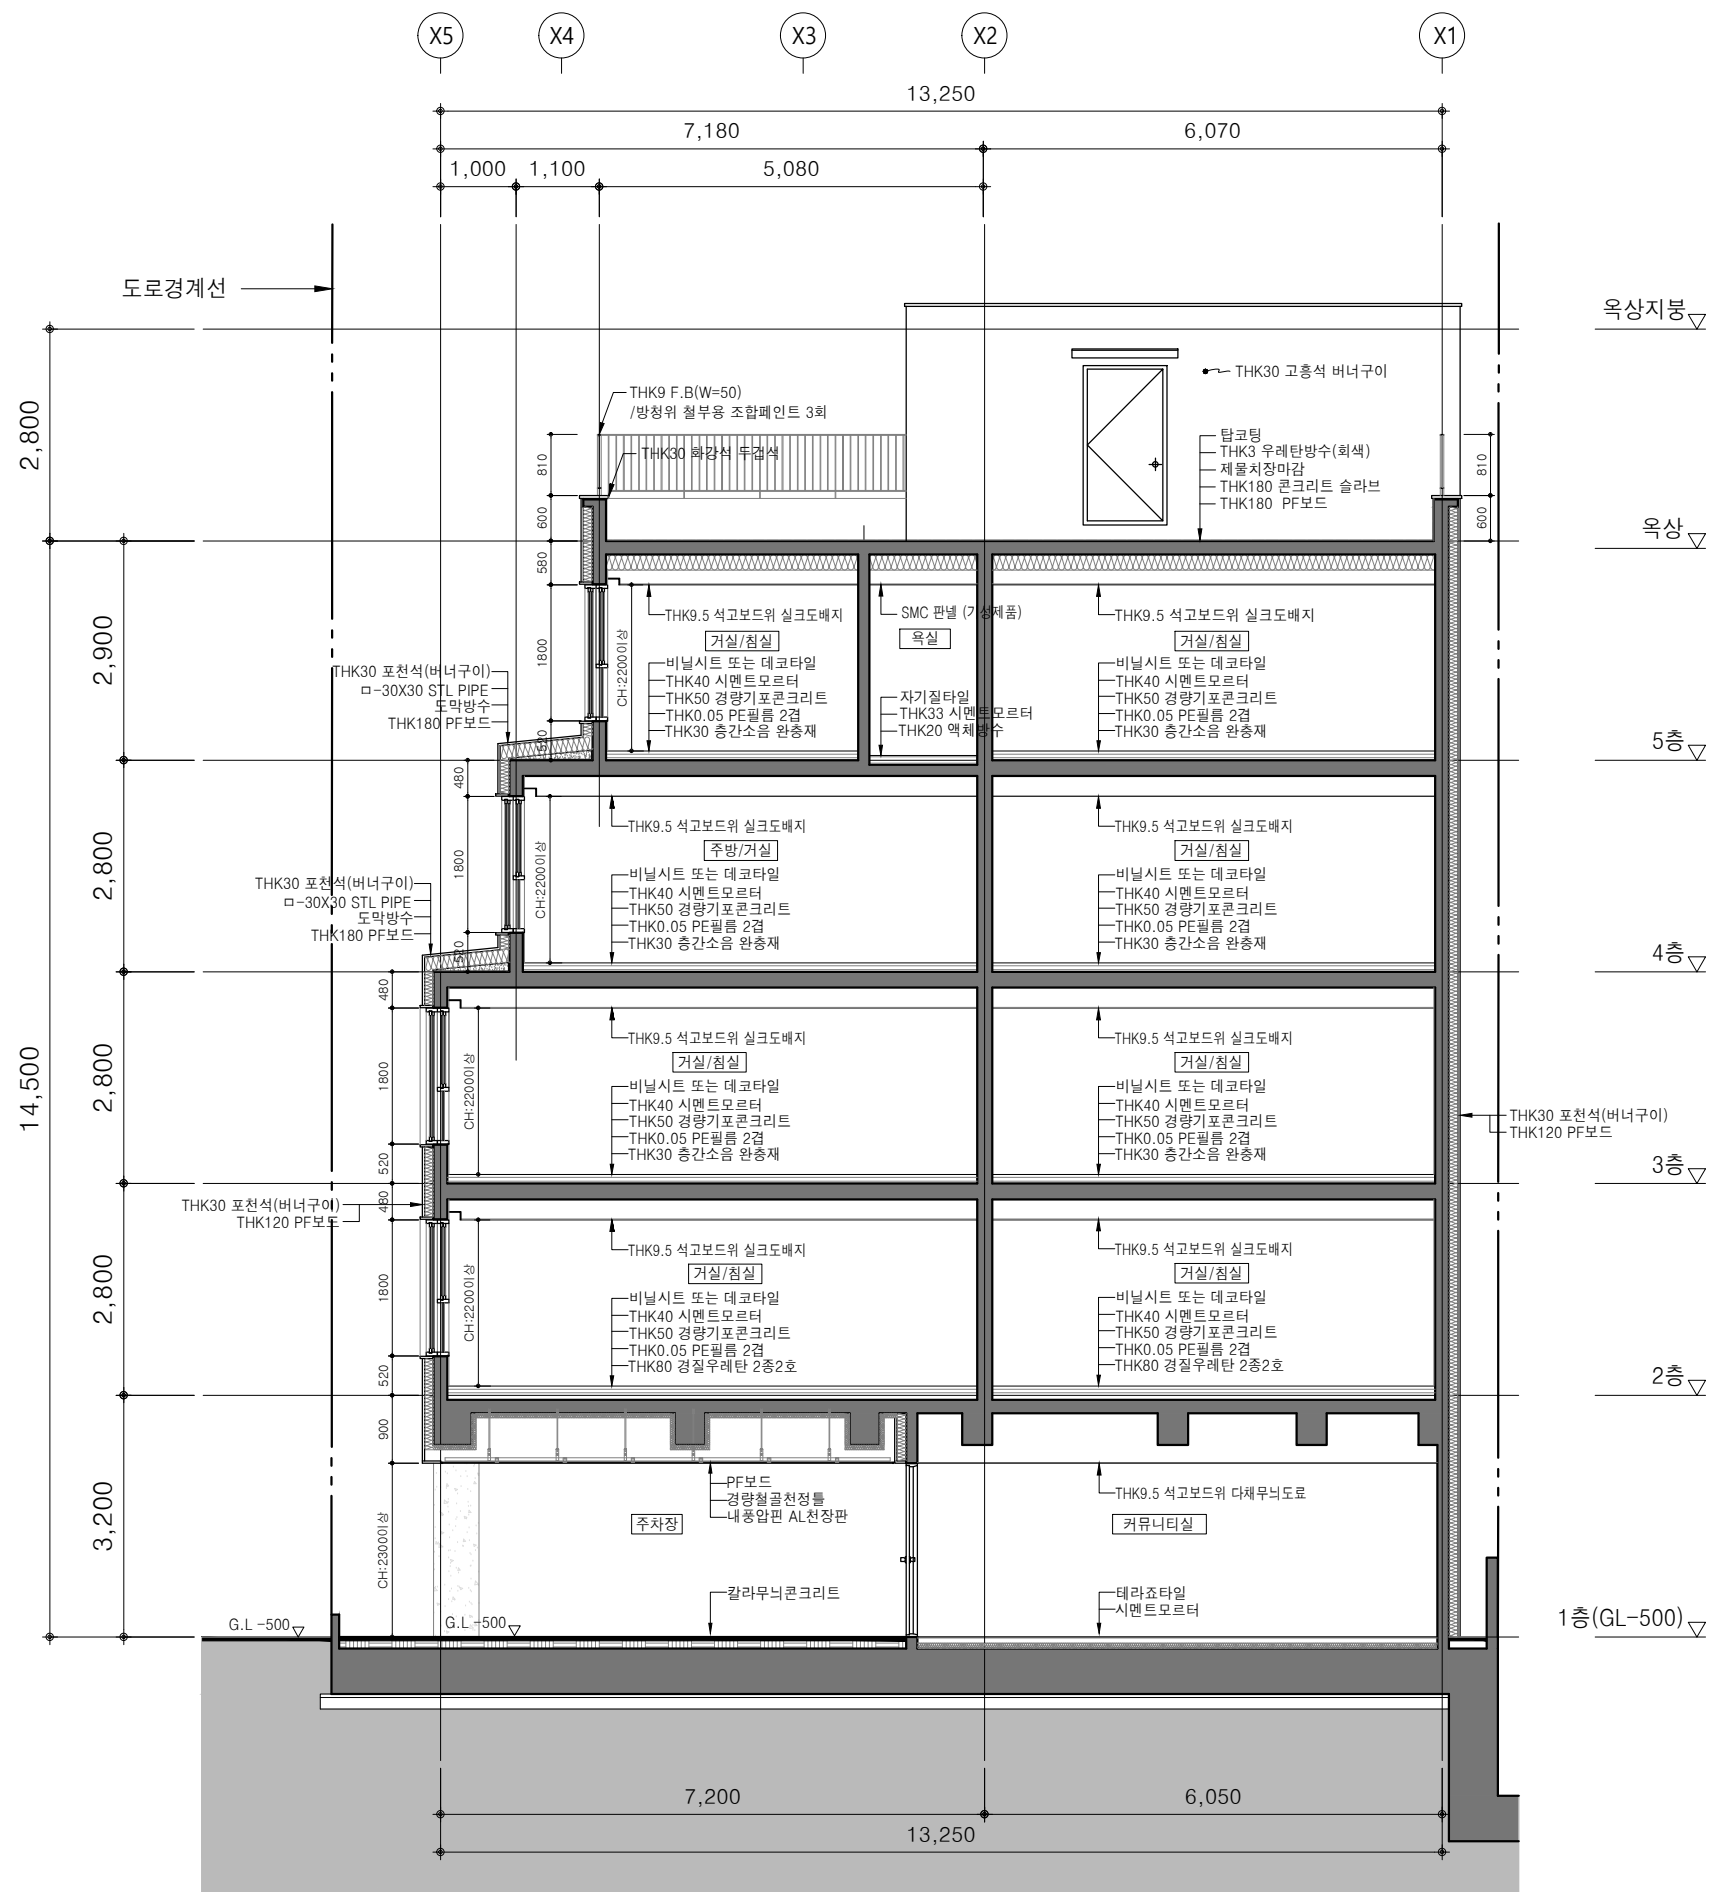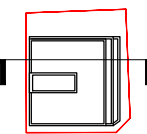

1
A
주단면도-1
SCALE : A3=1/100

NO. DATE REVISION DRAWN APP.

1				
2				
3				

설 계 DRAWN 검토 CHECK

심 사 SUBMIT 승인 APPROVE

축 척 SCALE

A1 1 /

A3 1 / 100

일 자 DATE

설계번호 PROJECT NO.

도면파일명 DWG. FILE NAME

도면번호 SHEET NO.

A - 401

도면명 SUBJECT TITLE

주단면도-1





(주) 동심원건축사사무소

TEL : 02)3452-0597
FAX : 02)3452-0598

설계명 PROJECT TITLE
송파구 송파동
도시형생활주택 신축공사

주 기 NOTE

■ Key plan

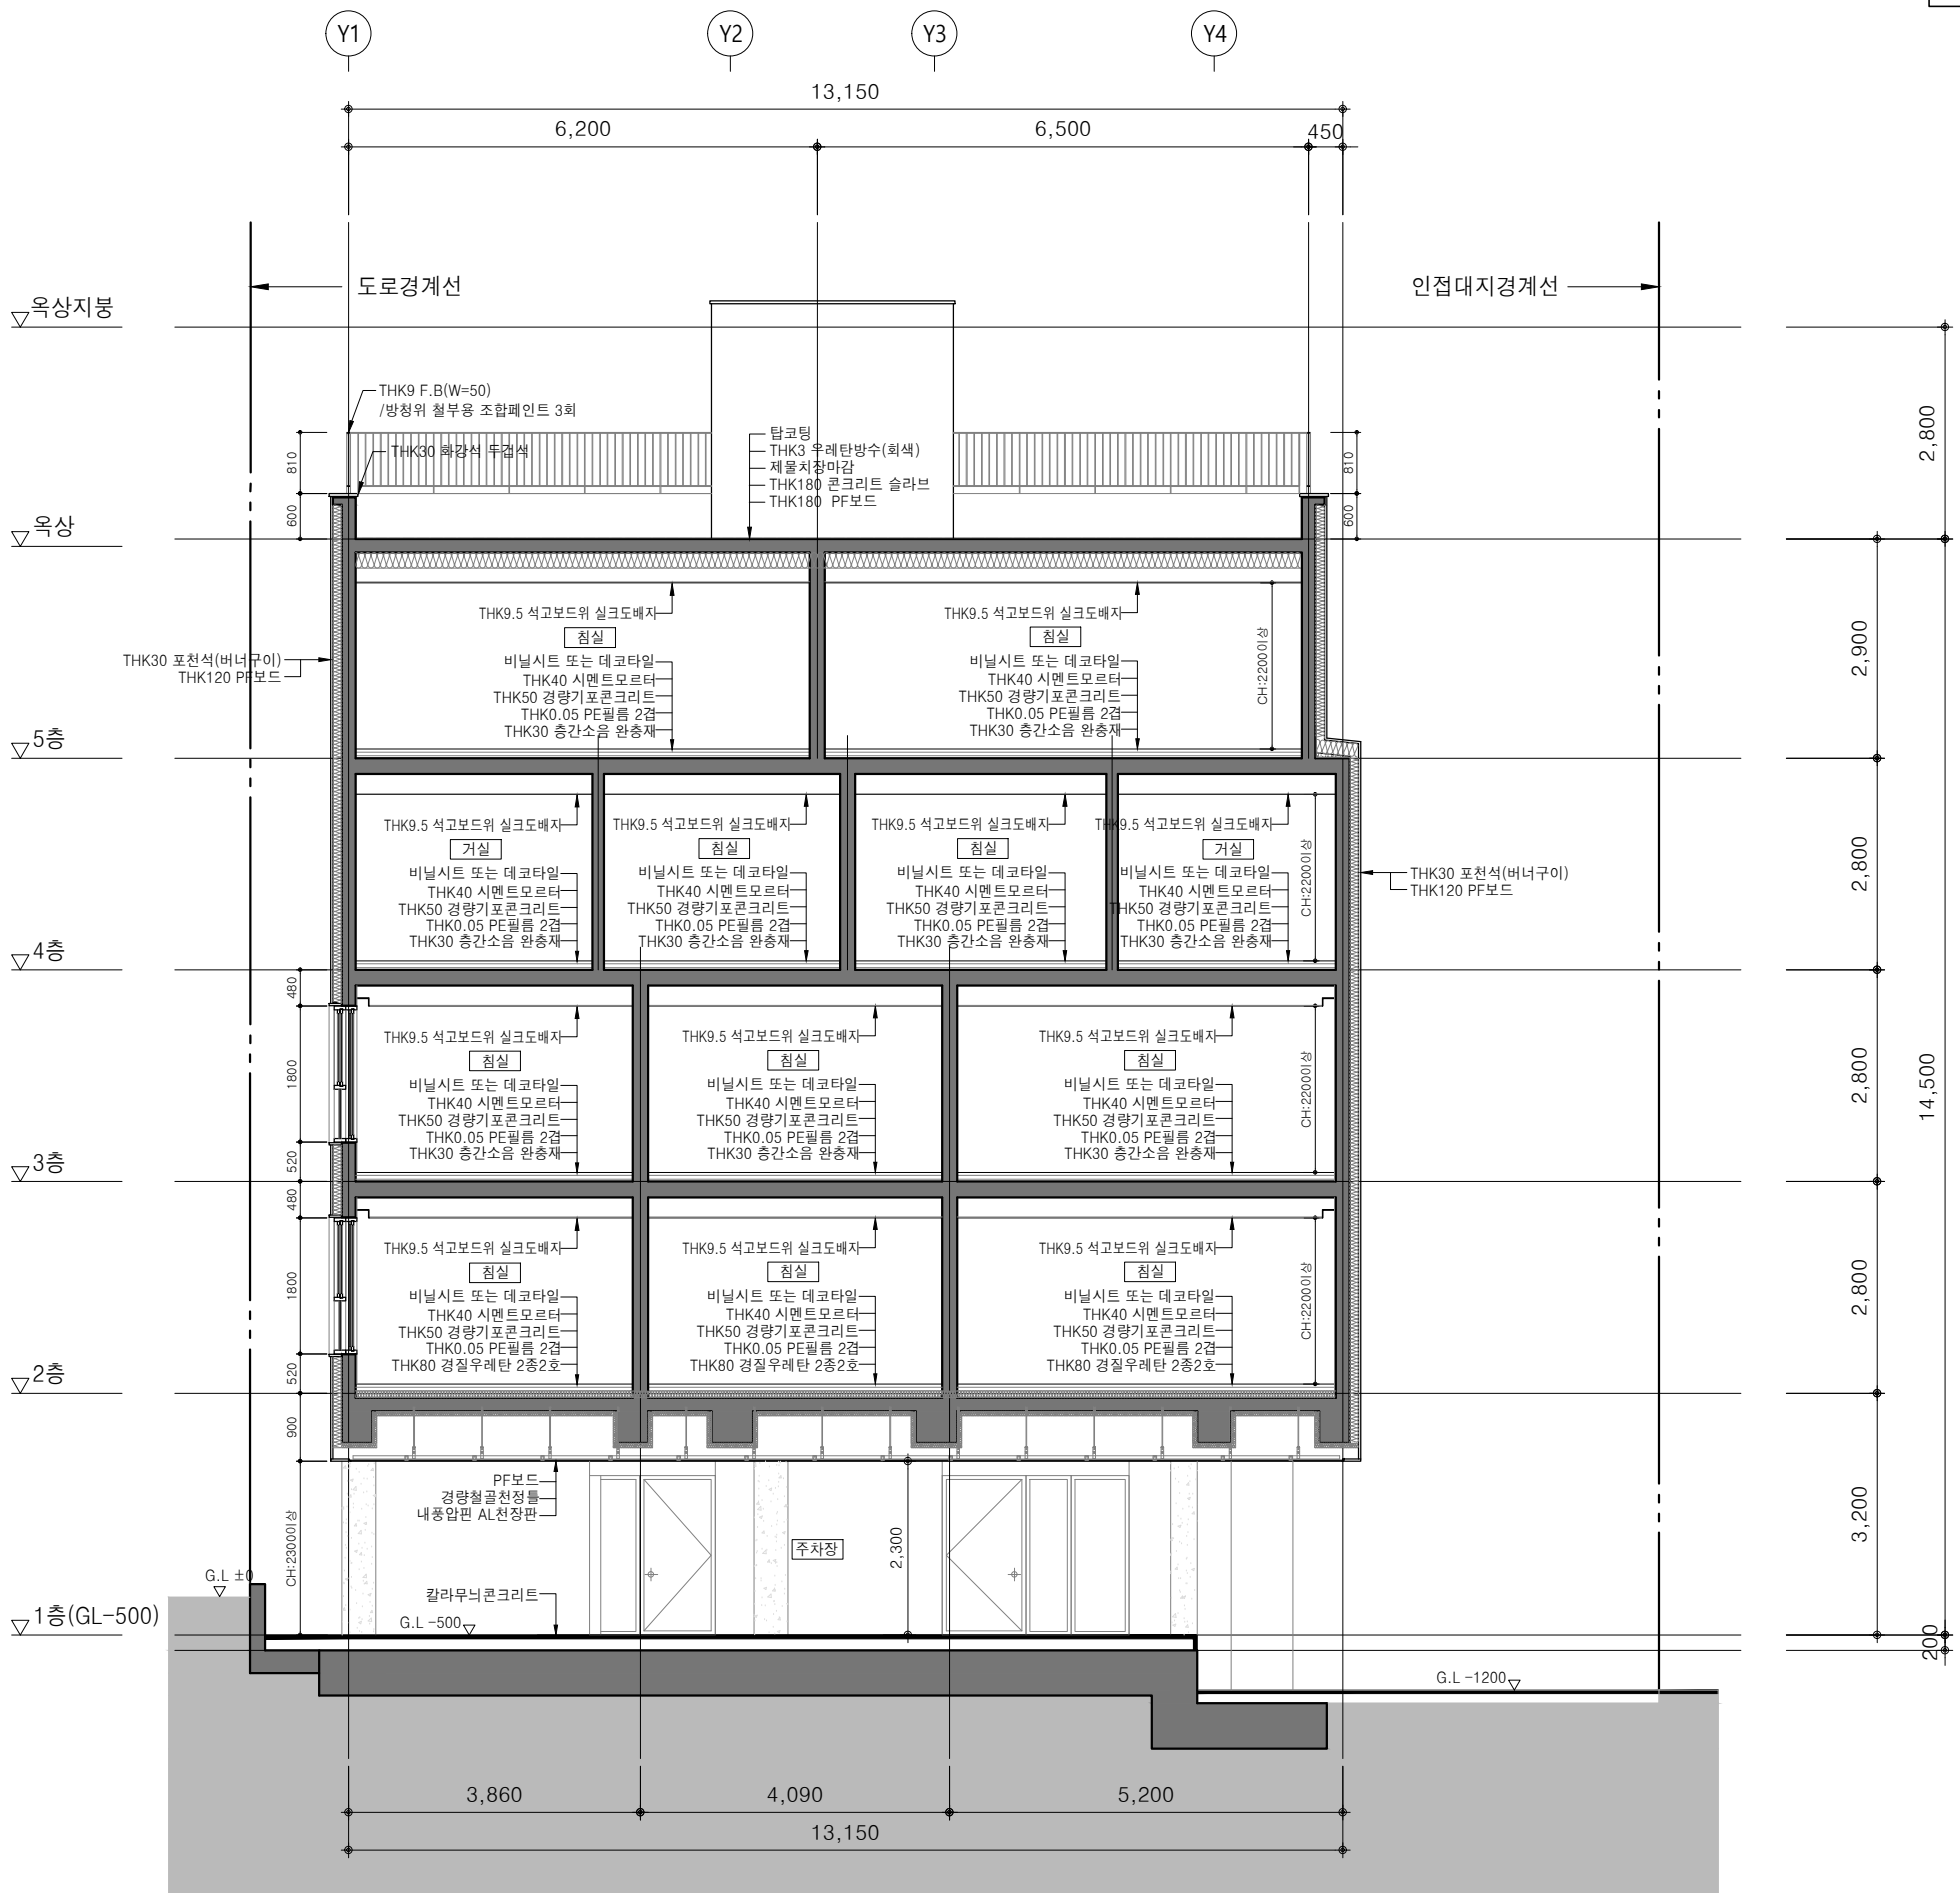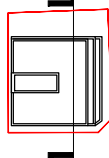

1
A
주단면도-2
SCALE : A3=1/100

NO.		DATE	REVISION	DRAWN	APP.
1					
2					
3					
설 계		DRAWN	검 토	CHECK	
심 사		SUBMIT	승 인	APPROVE	
축 척		SCALE			
A1		1 /			
A3		1 / 100			
일 자		DATE			
설계번호		PROJECT NO.			
도면파일명		DWG. FILE NAME			
도면번호		SHEET NO.			
		A - 402			
도면명		SUBJECT TITLE			
		주단면도-2			