


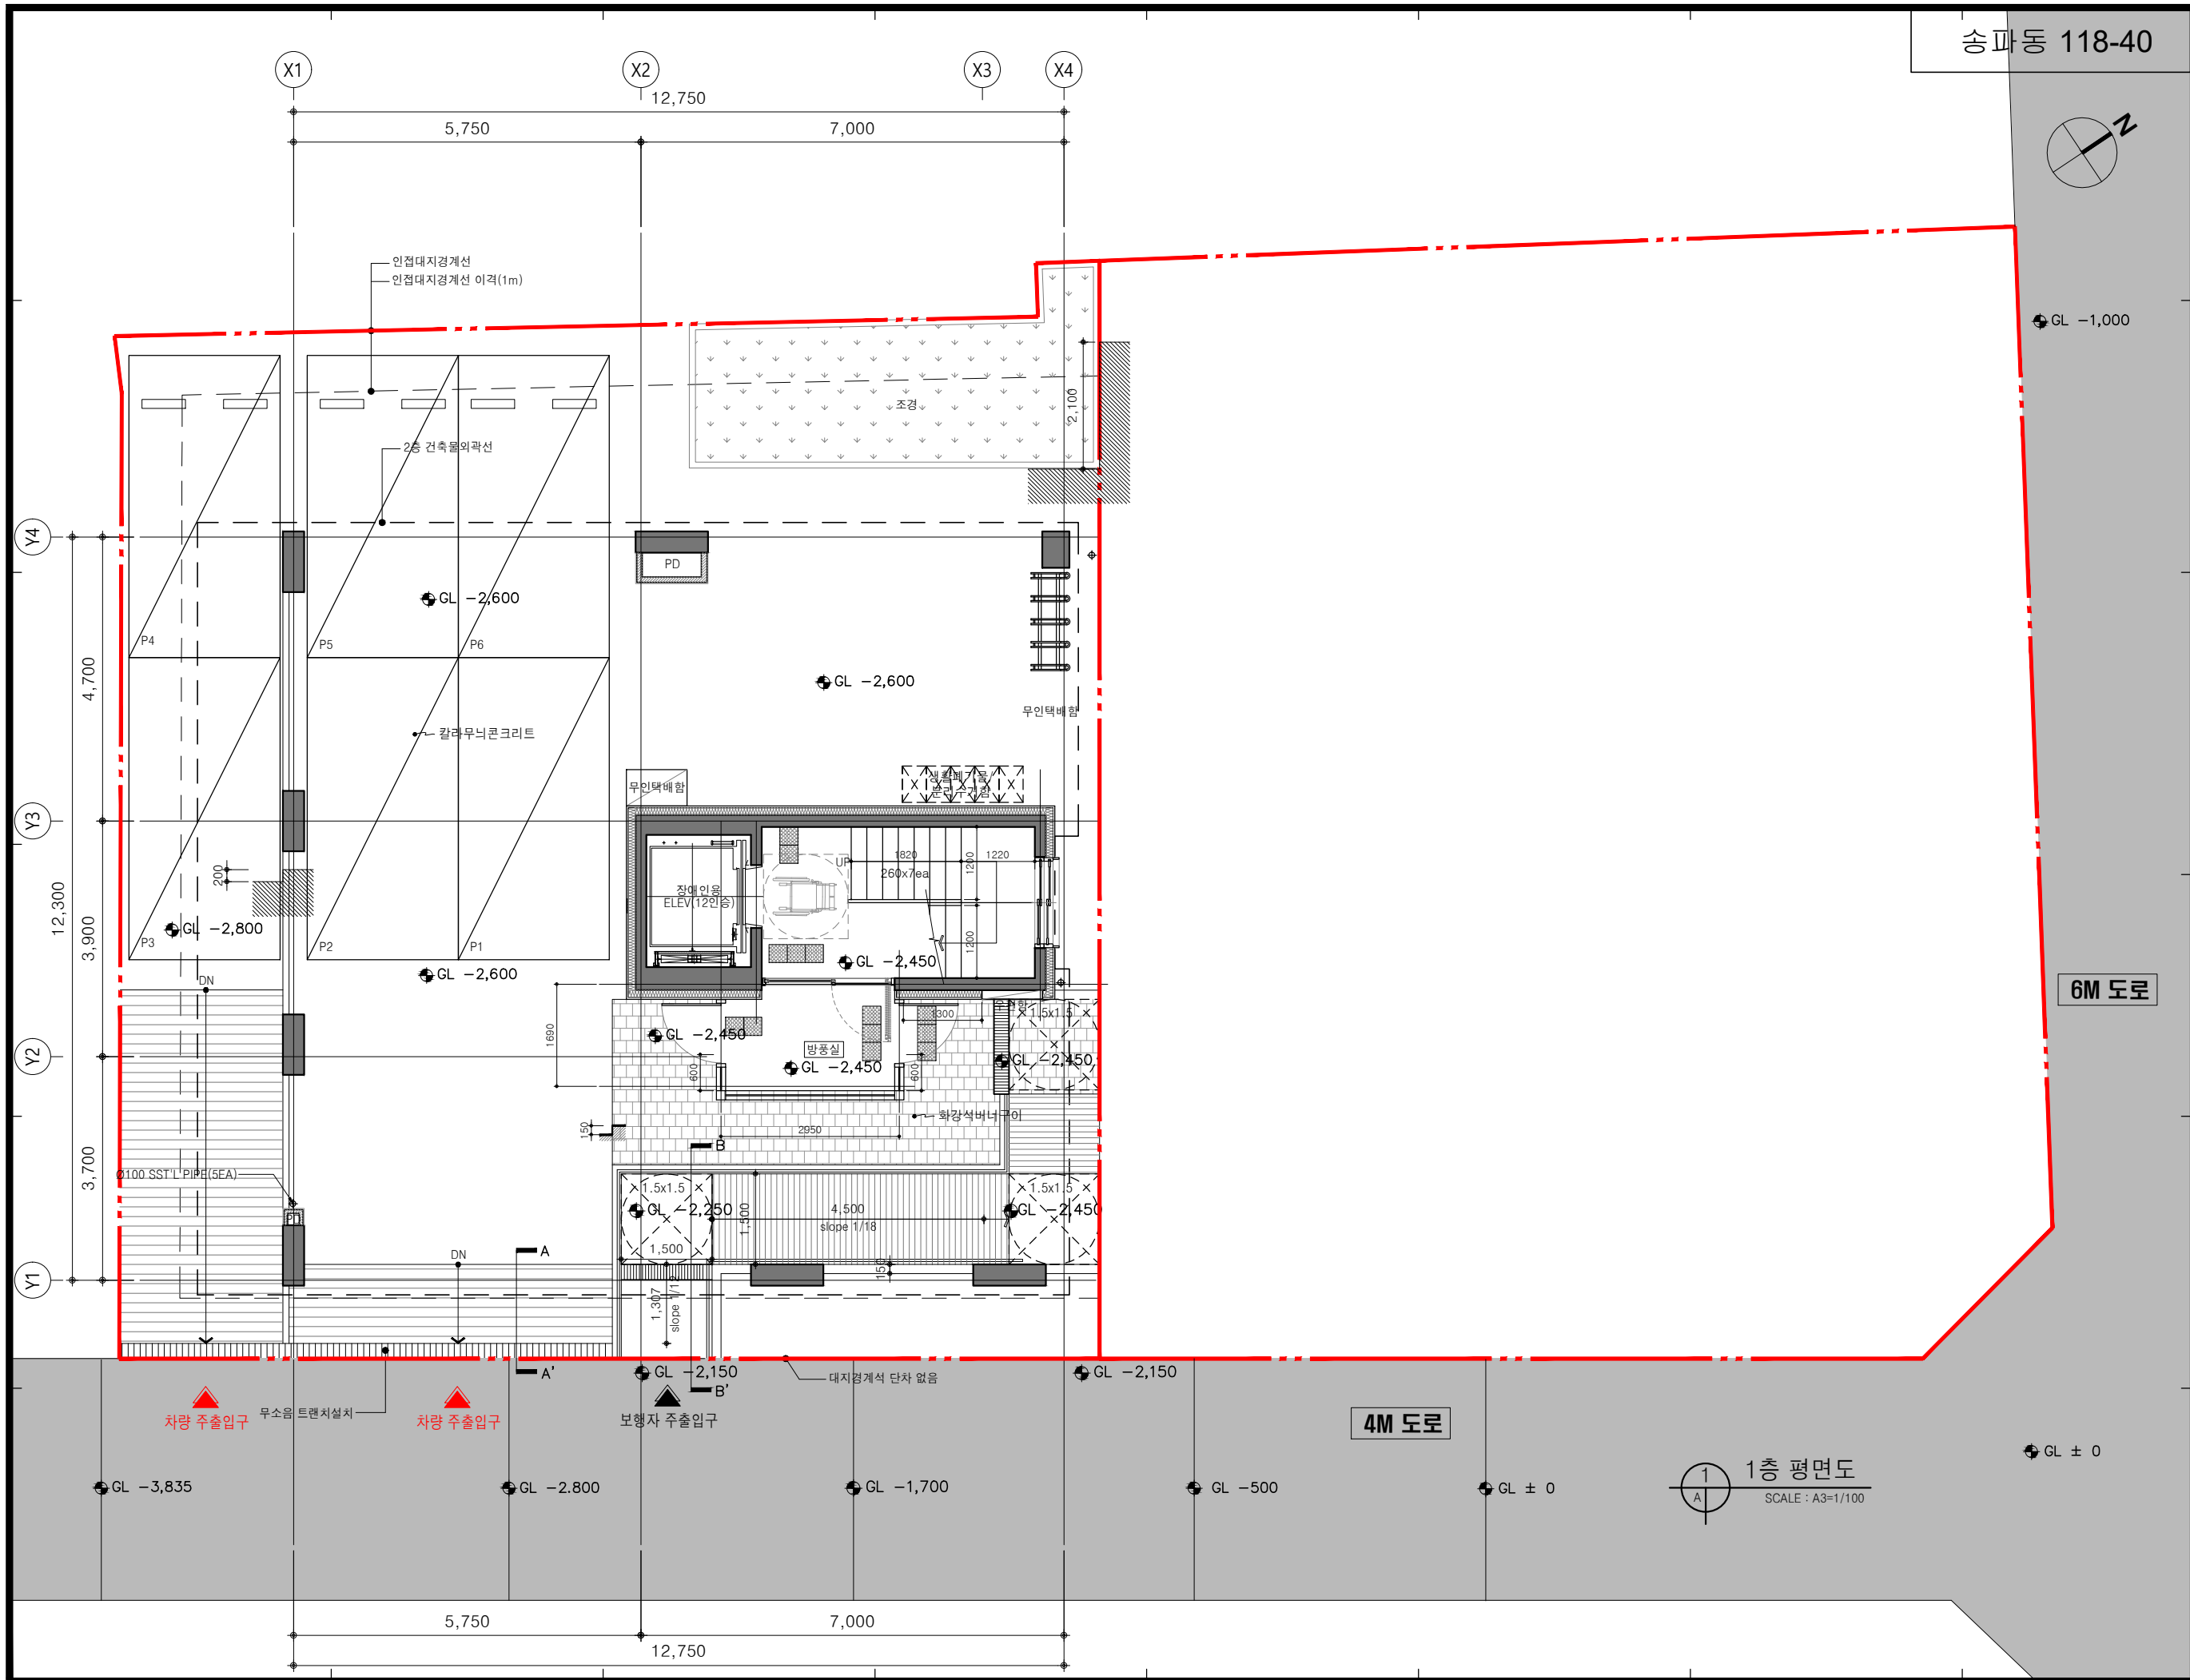

송파동 118-40



(주) 동심원건축사사무소

TEL : 02)3452-0597
FAX : 02)3452-0598

설계명 PROJECT TITLE

송파구 송파동
도시형생활주택 신축공사

주 기 NOTE

GL -1,000

6M 도로

4M 도로

GL ± 0

1층 평면도
SCALE: A3=1/100

NO. DATE REVISION DRAWN APP.

1				
2				
3				

설 계 DRAWN 검토 CHECK

심 사 SUBMIT 승인 APPROVE

축척 SCALE

A1	1 / 50
A3	1 / 100

일 자 DATE

설계번호 PROJECT NO.



도면파일명 DWG. FILE NAME

도면번호 SHEET NO.


A - 101

도면명 SUBJECT TITLE

1층 평면도

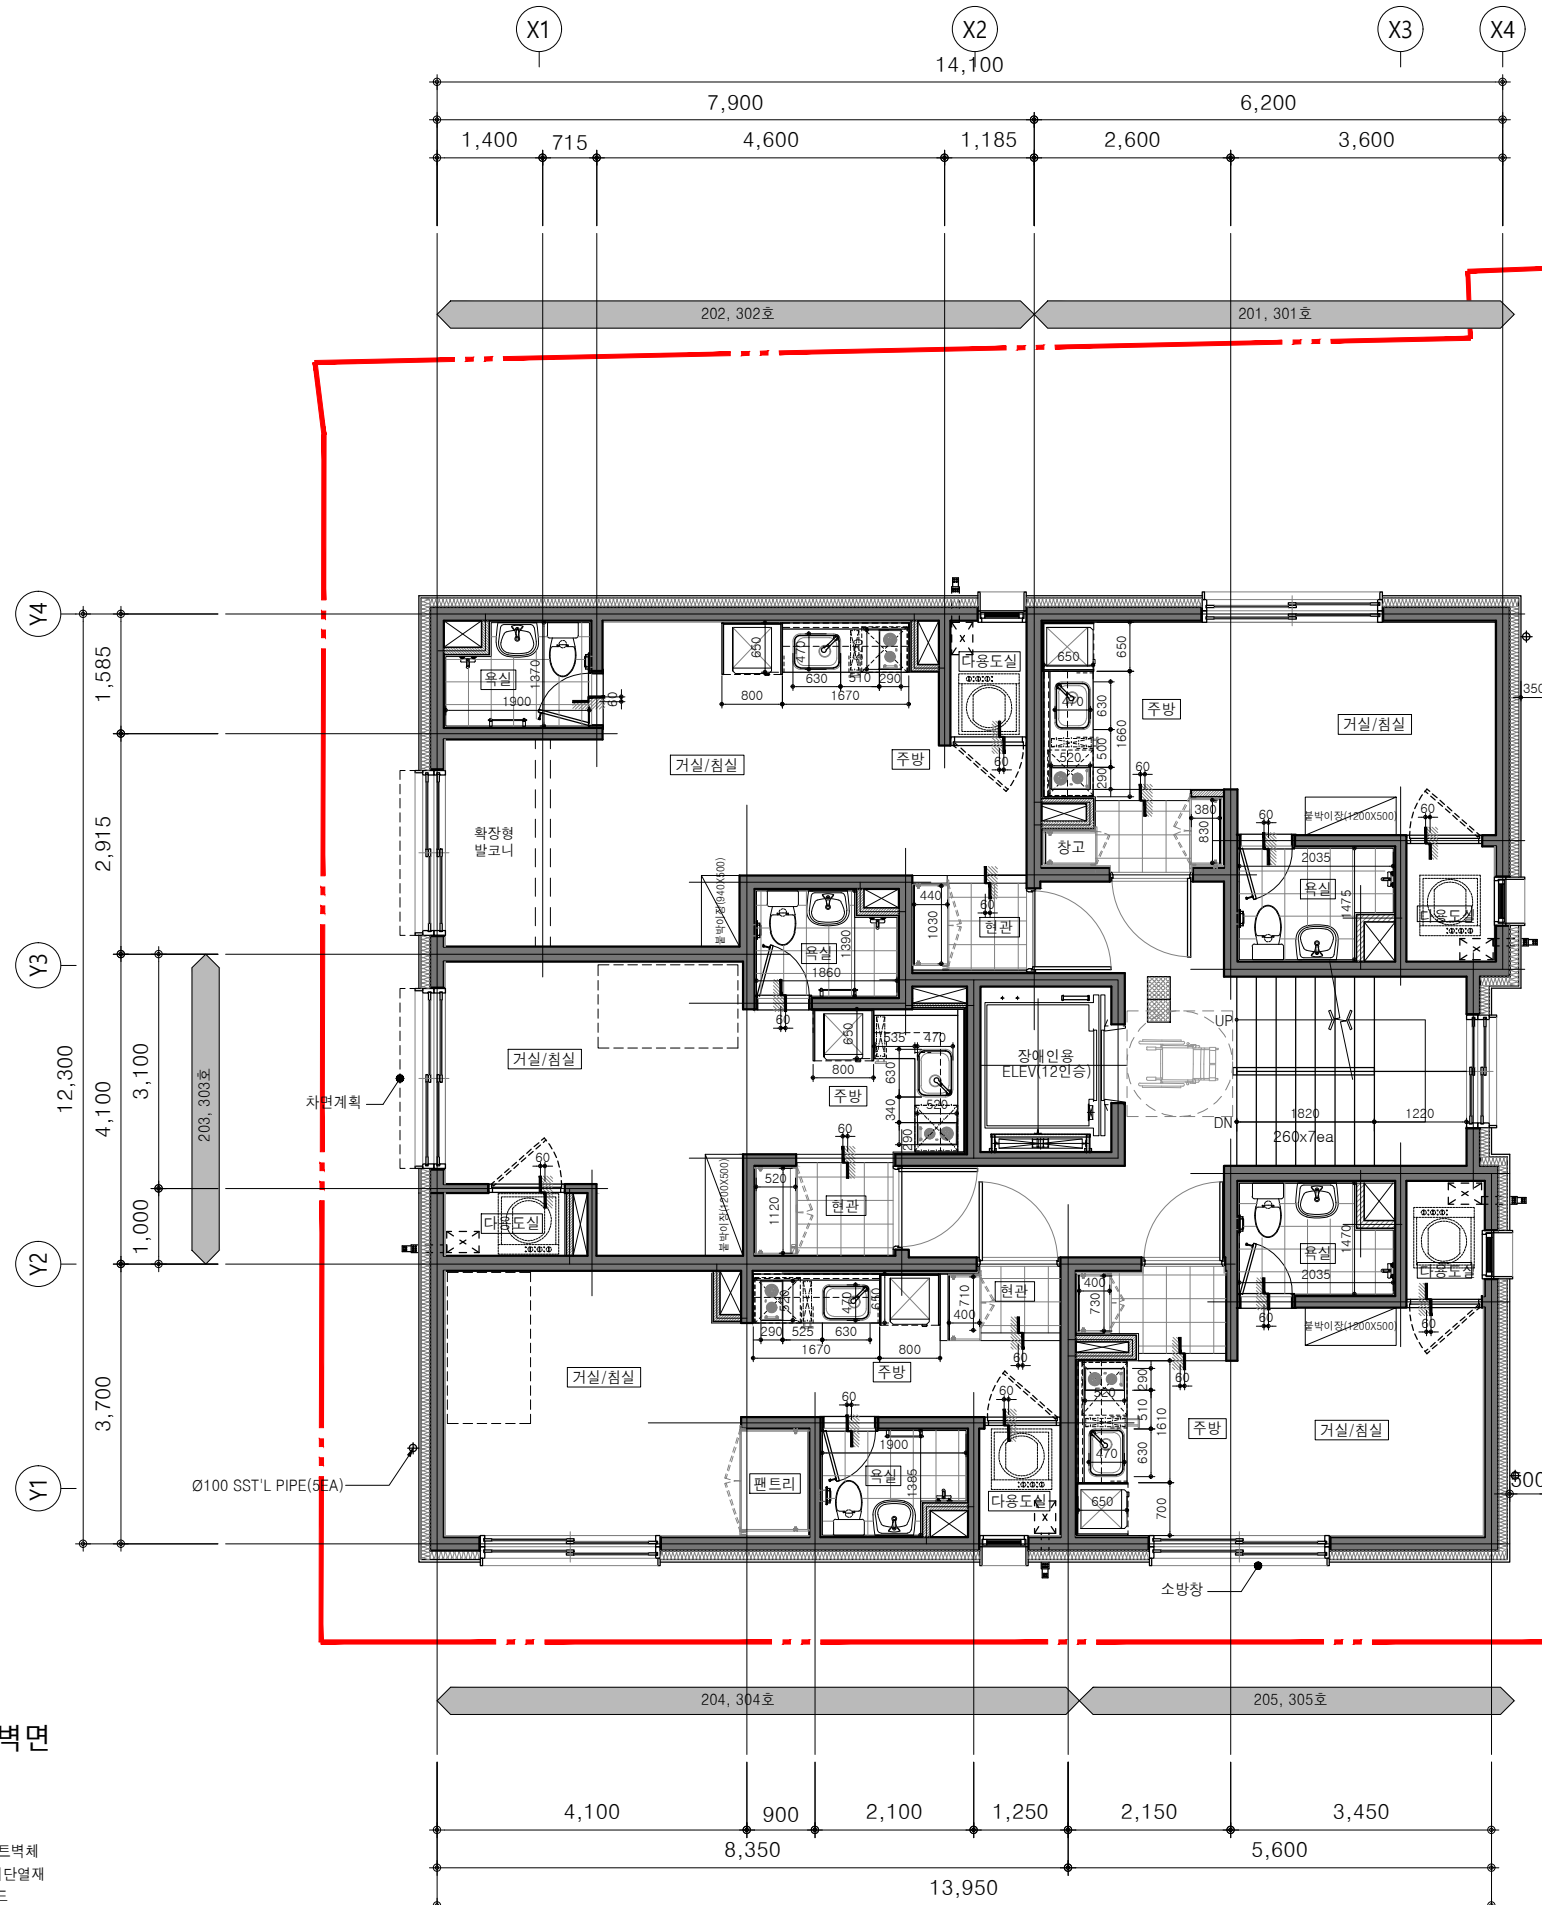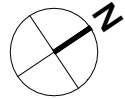

■ 간접외기에 면한 실내벽면

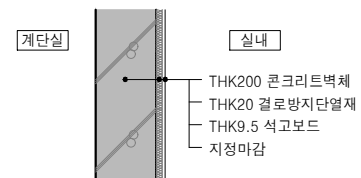

■ 빌트인설치 내역

구분	세탁기	냉장고	에어컨 (벽걸이)	전자 레인지
설치 유무	○	○	○	○

* 냉장고 상부 전자레인지 / 쿡탑 하부 세탁기 설치

NO. DATE REVISION DRAWN APP.

1				
2				
3				

설 계 DRAWN 검토 CHECK

심 사 SUBMIT 승인 APPROVE

축 척 SCALE

A1	1 / 50
A3	1 / 100

일 자 DATE

설계번호 PROJECT NO.

도면파일명 DWG. FILE NAME



도면번호 SHEET NO.

A - 102


도면명 SUBJECT TITLE

2~3층 평면도

2~3층 평면도
SCALE : A3=1/100

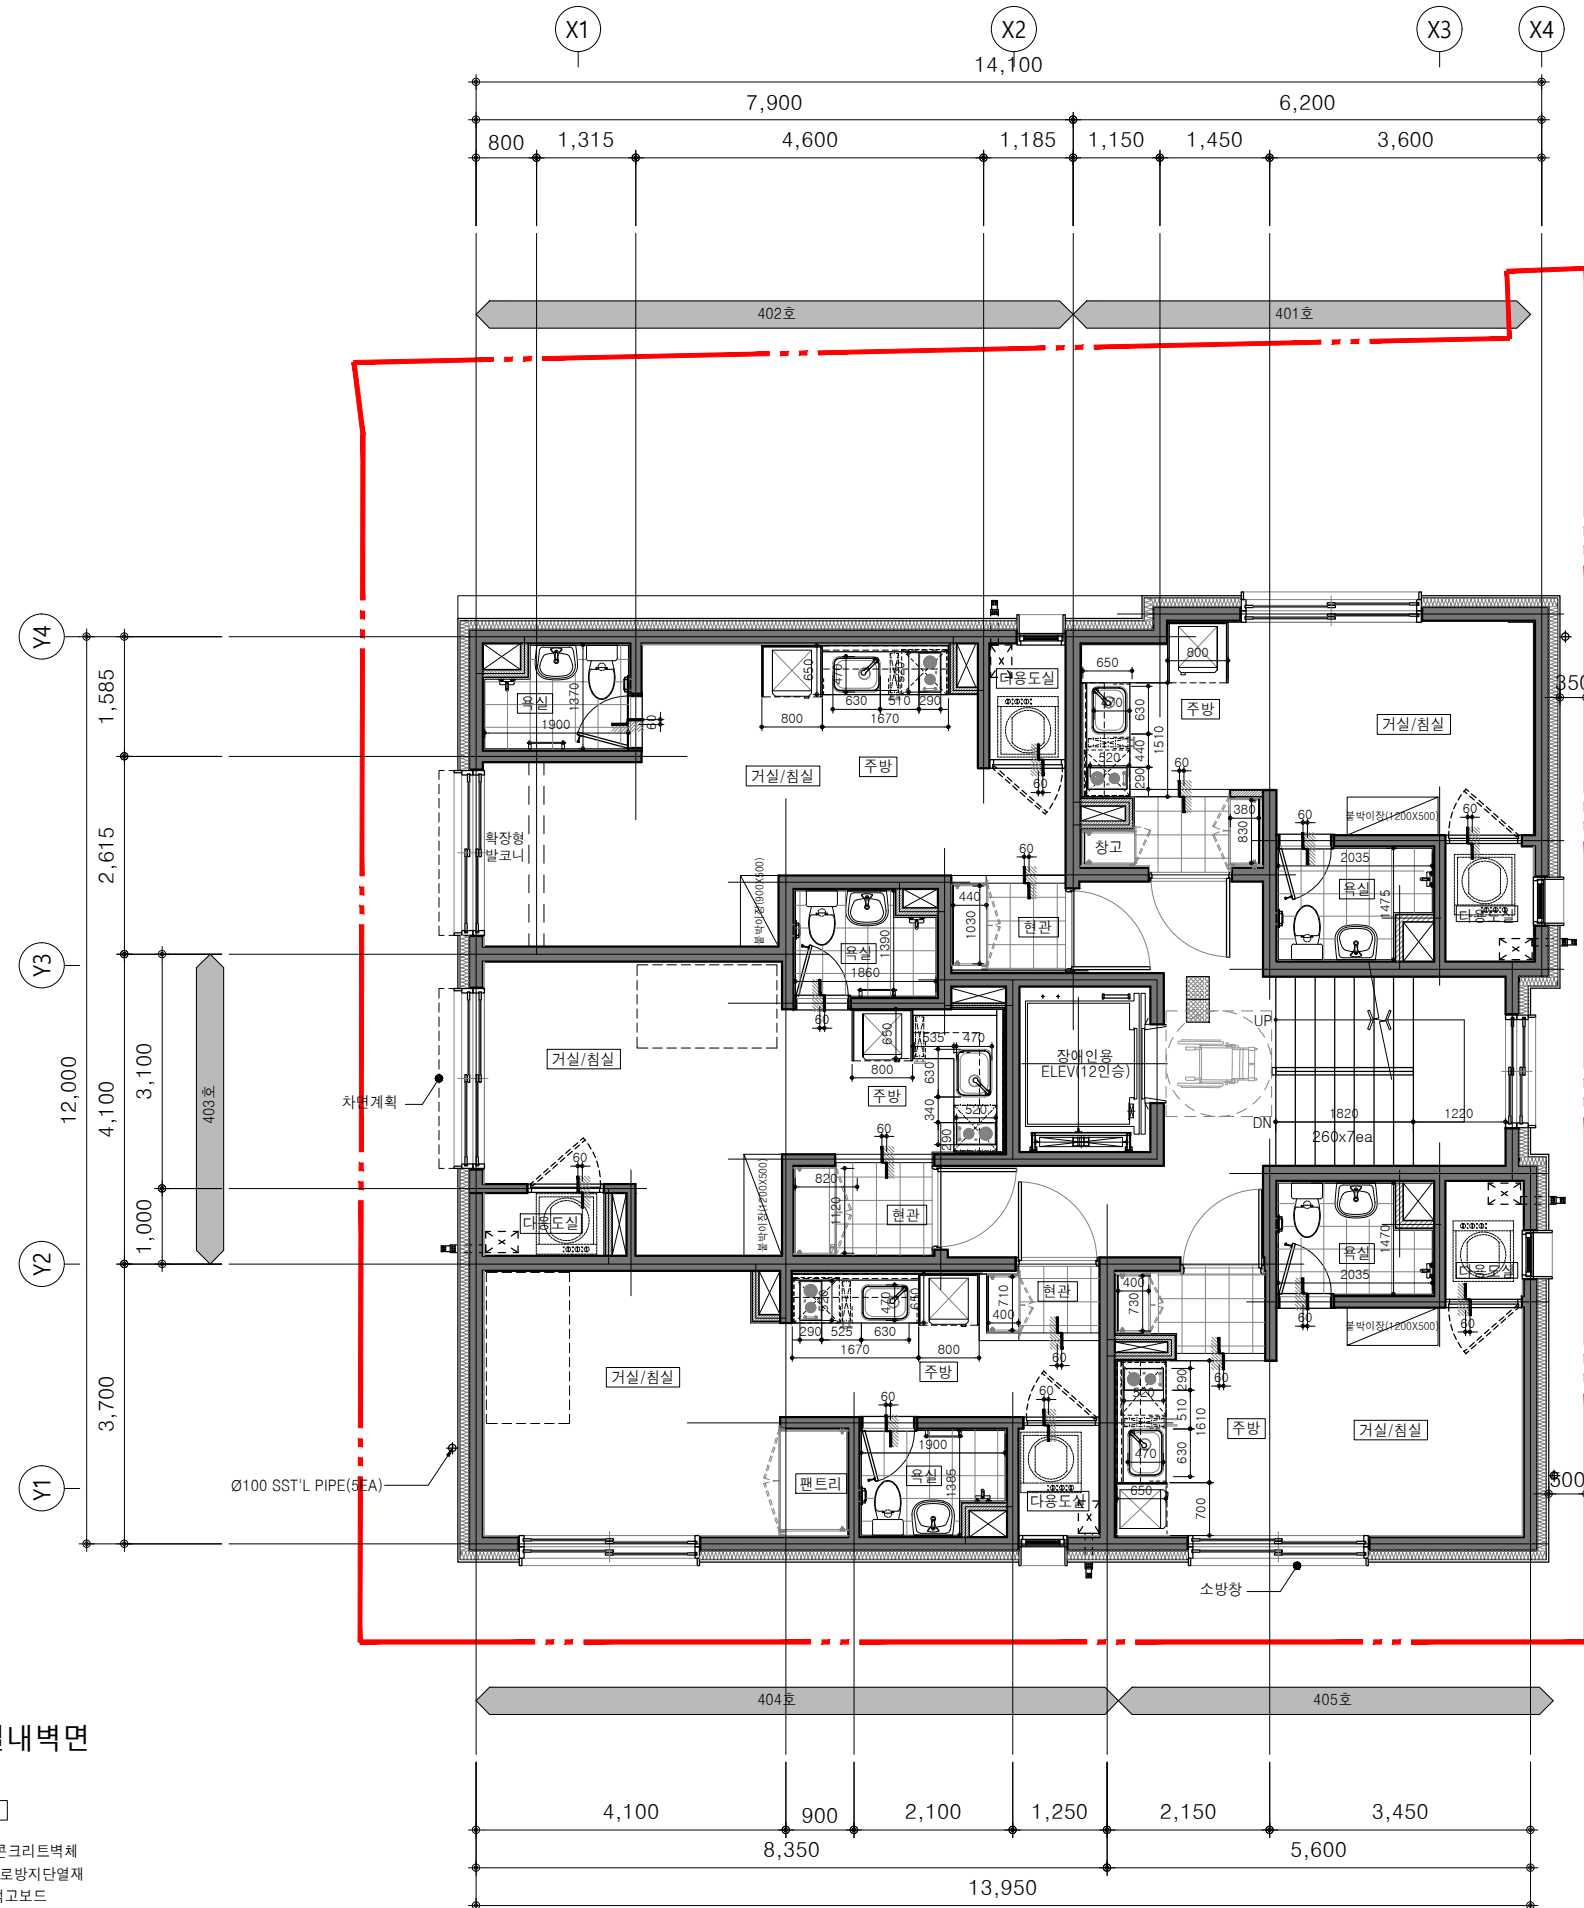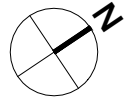

■ 간접외기에 면한 실내벽면

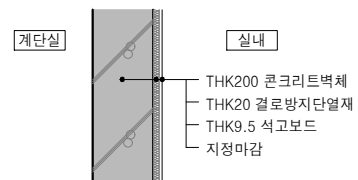

■ 빌트인설치 내역

구분	세탁기	냉장고	에어컨 (벽걸이)	전자 레인지
설치 유무	○	○	○	○

* 냉장고 상부 전자레인지 / 쿡탑 하부 세탁기 설치

4층 평면도
SCALE : A3=1/100

NO. DATE REVISION DRAWN APP.

1				
2				
3				

설 계 DRAWN 검토 CHECK

심 사 SUBMIT 승인 APPROVE

축 척 SCALE

A1	1 / 50
A3	1 / 100

일 자 DATE

설계번호 PROJECT NO.



도면파일명 DWG. FILE NAME

도면번호 SHEET NO.


A - 103

도면명 SUBJECT TITLE

4층 평면도

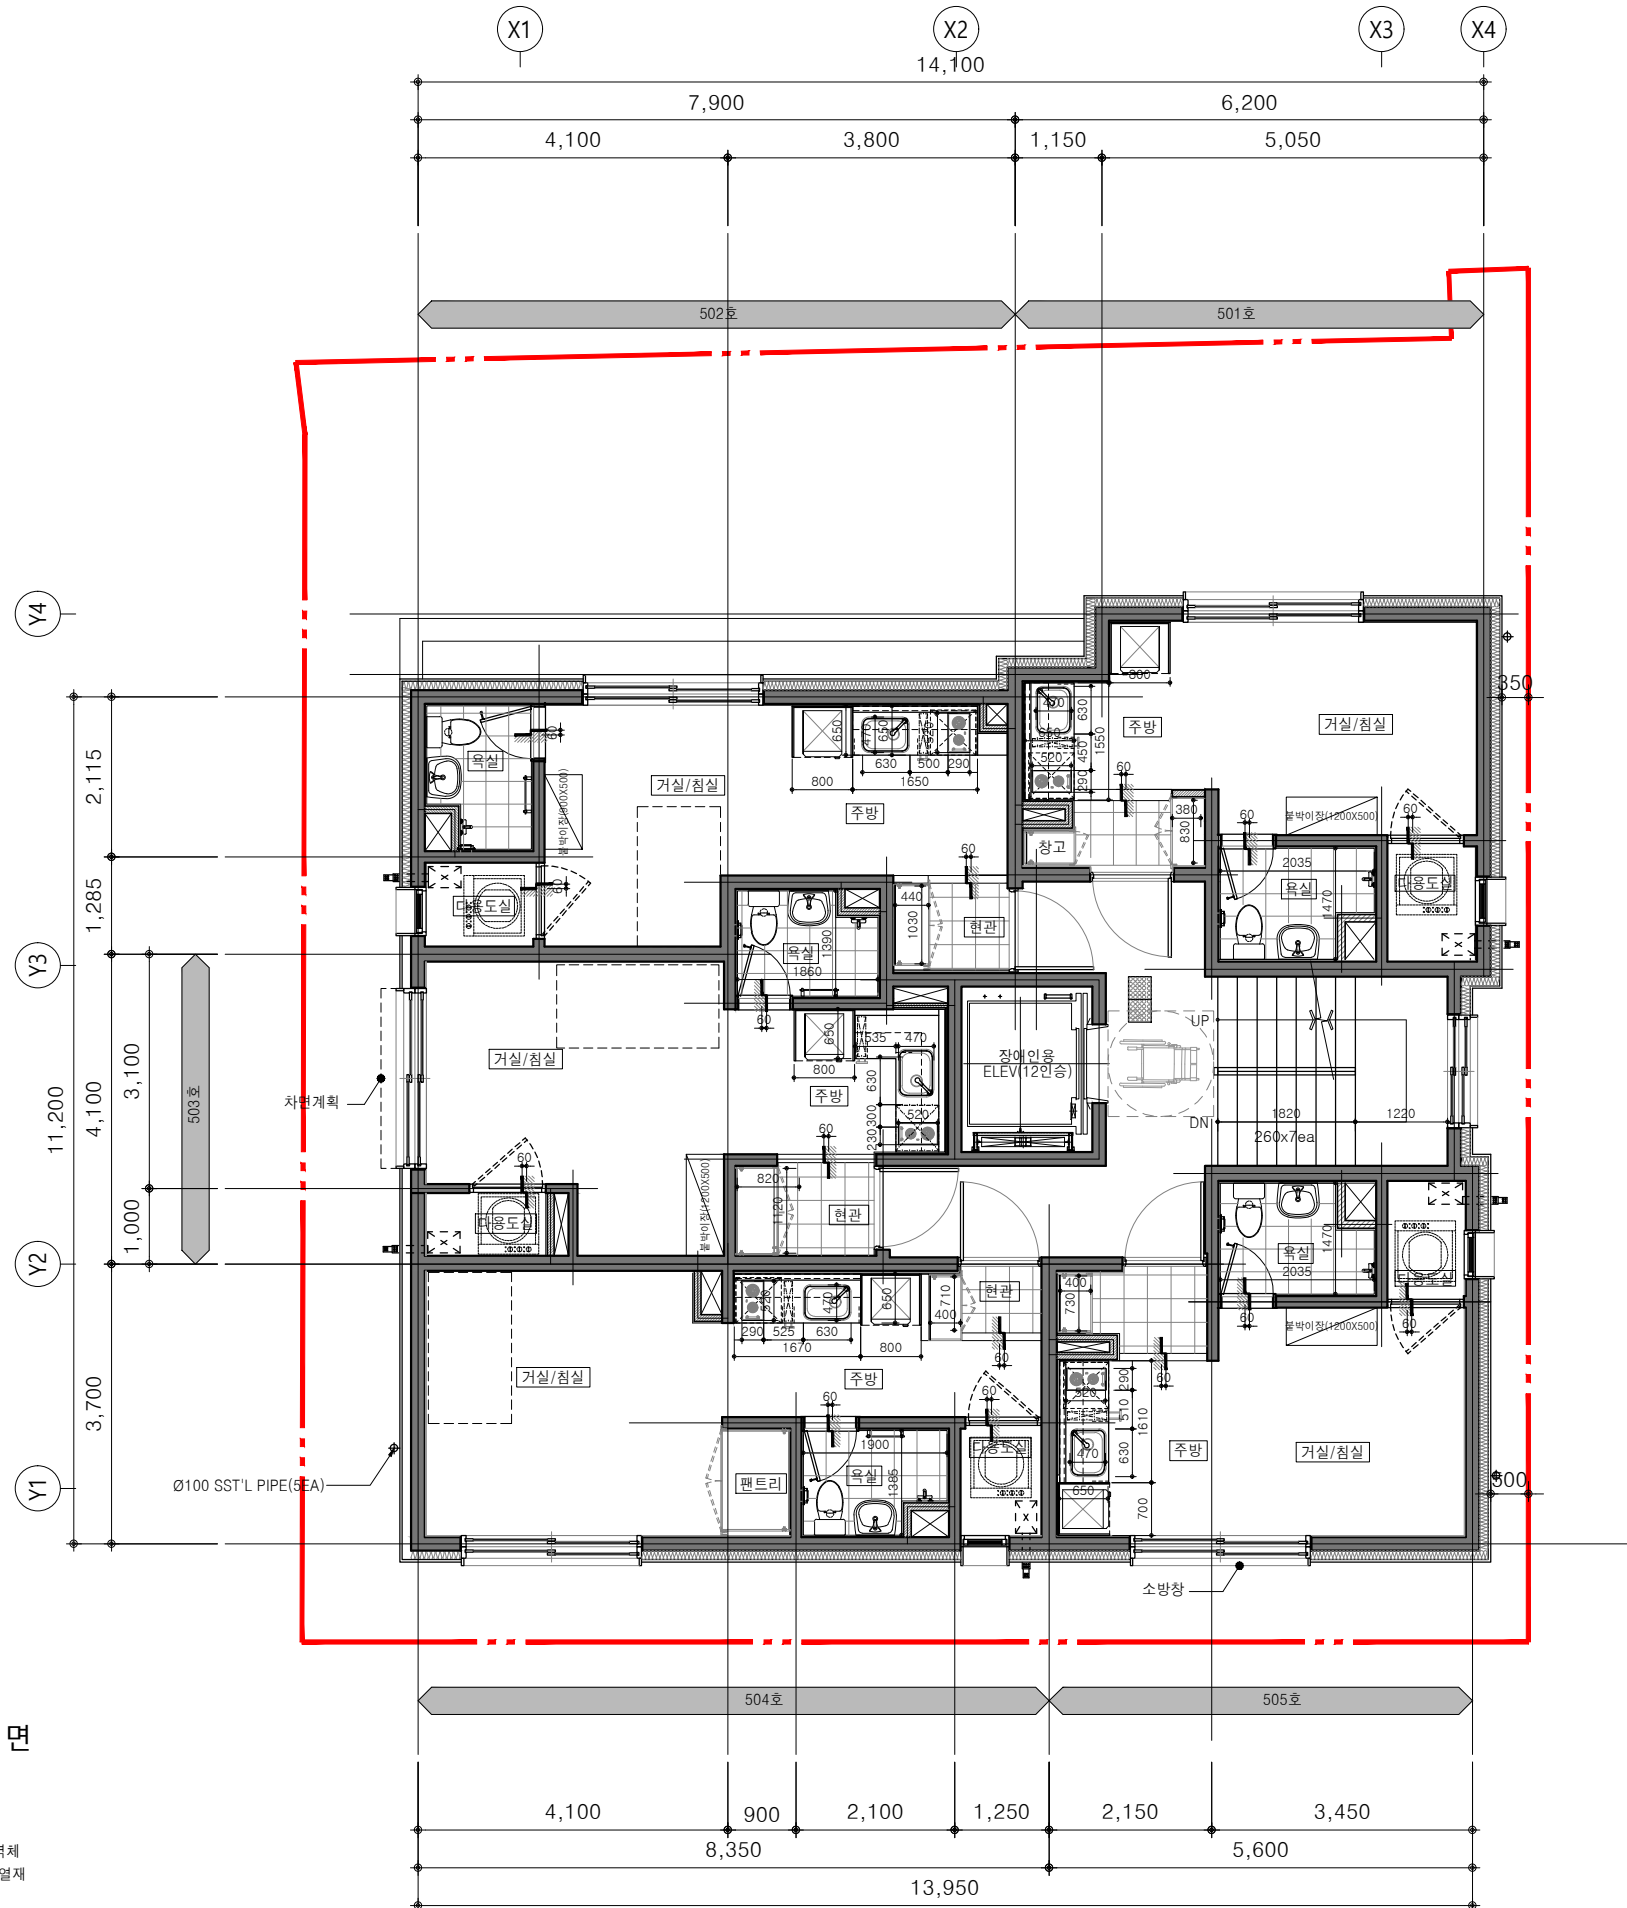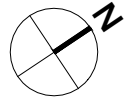

■ 간접외기에 면한 실내벽면

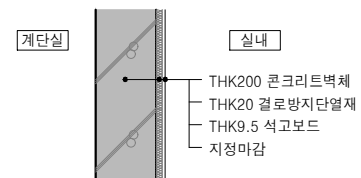

■ 빌트인설치 내역

구분	세탁기	냉장고	에어컨 (벽걸이)	전자 레인지
설치 유무	○	○	○	○

* 냉장고 상부 전자레인지 / 쿡탑 하부 세탁기 설치

1
A 5층 평면도
SCALE : A3=1/100

NO. DATE REVISION DRAWN APP.

1				
2				
3				

설 계 DRAWN 검토 CHECK

심 사 SUBMIT 승인 APPROVE

축 척 SCALE

A1	1 / 50
A3	1 / 100

일 자 DATE

설계번호 PROJECT NO.



도면파일명 DWG. FILE NAME

도면번호 SHEET NO.

A - 104


도면명 SUBJECT TITLE

5층 평면도

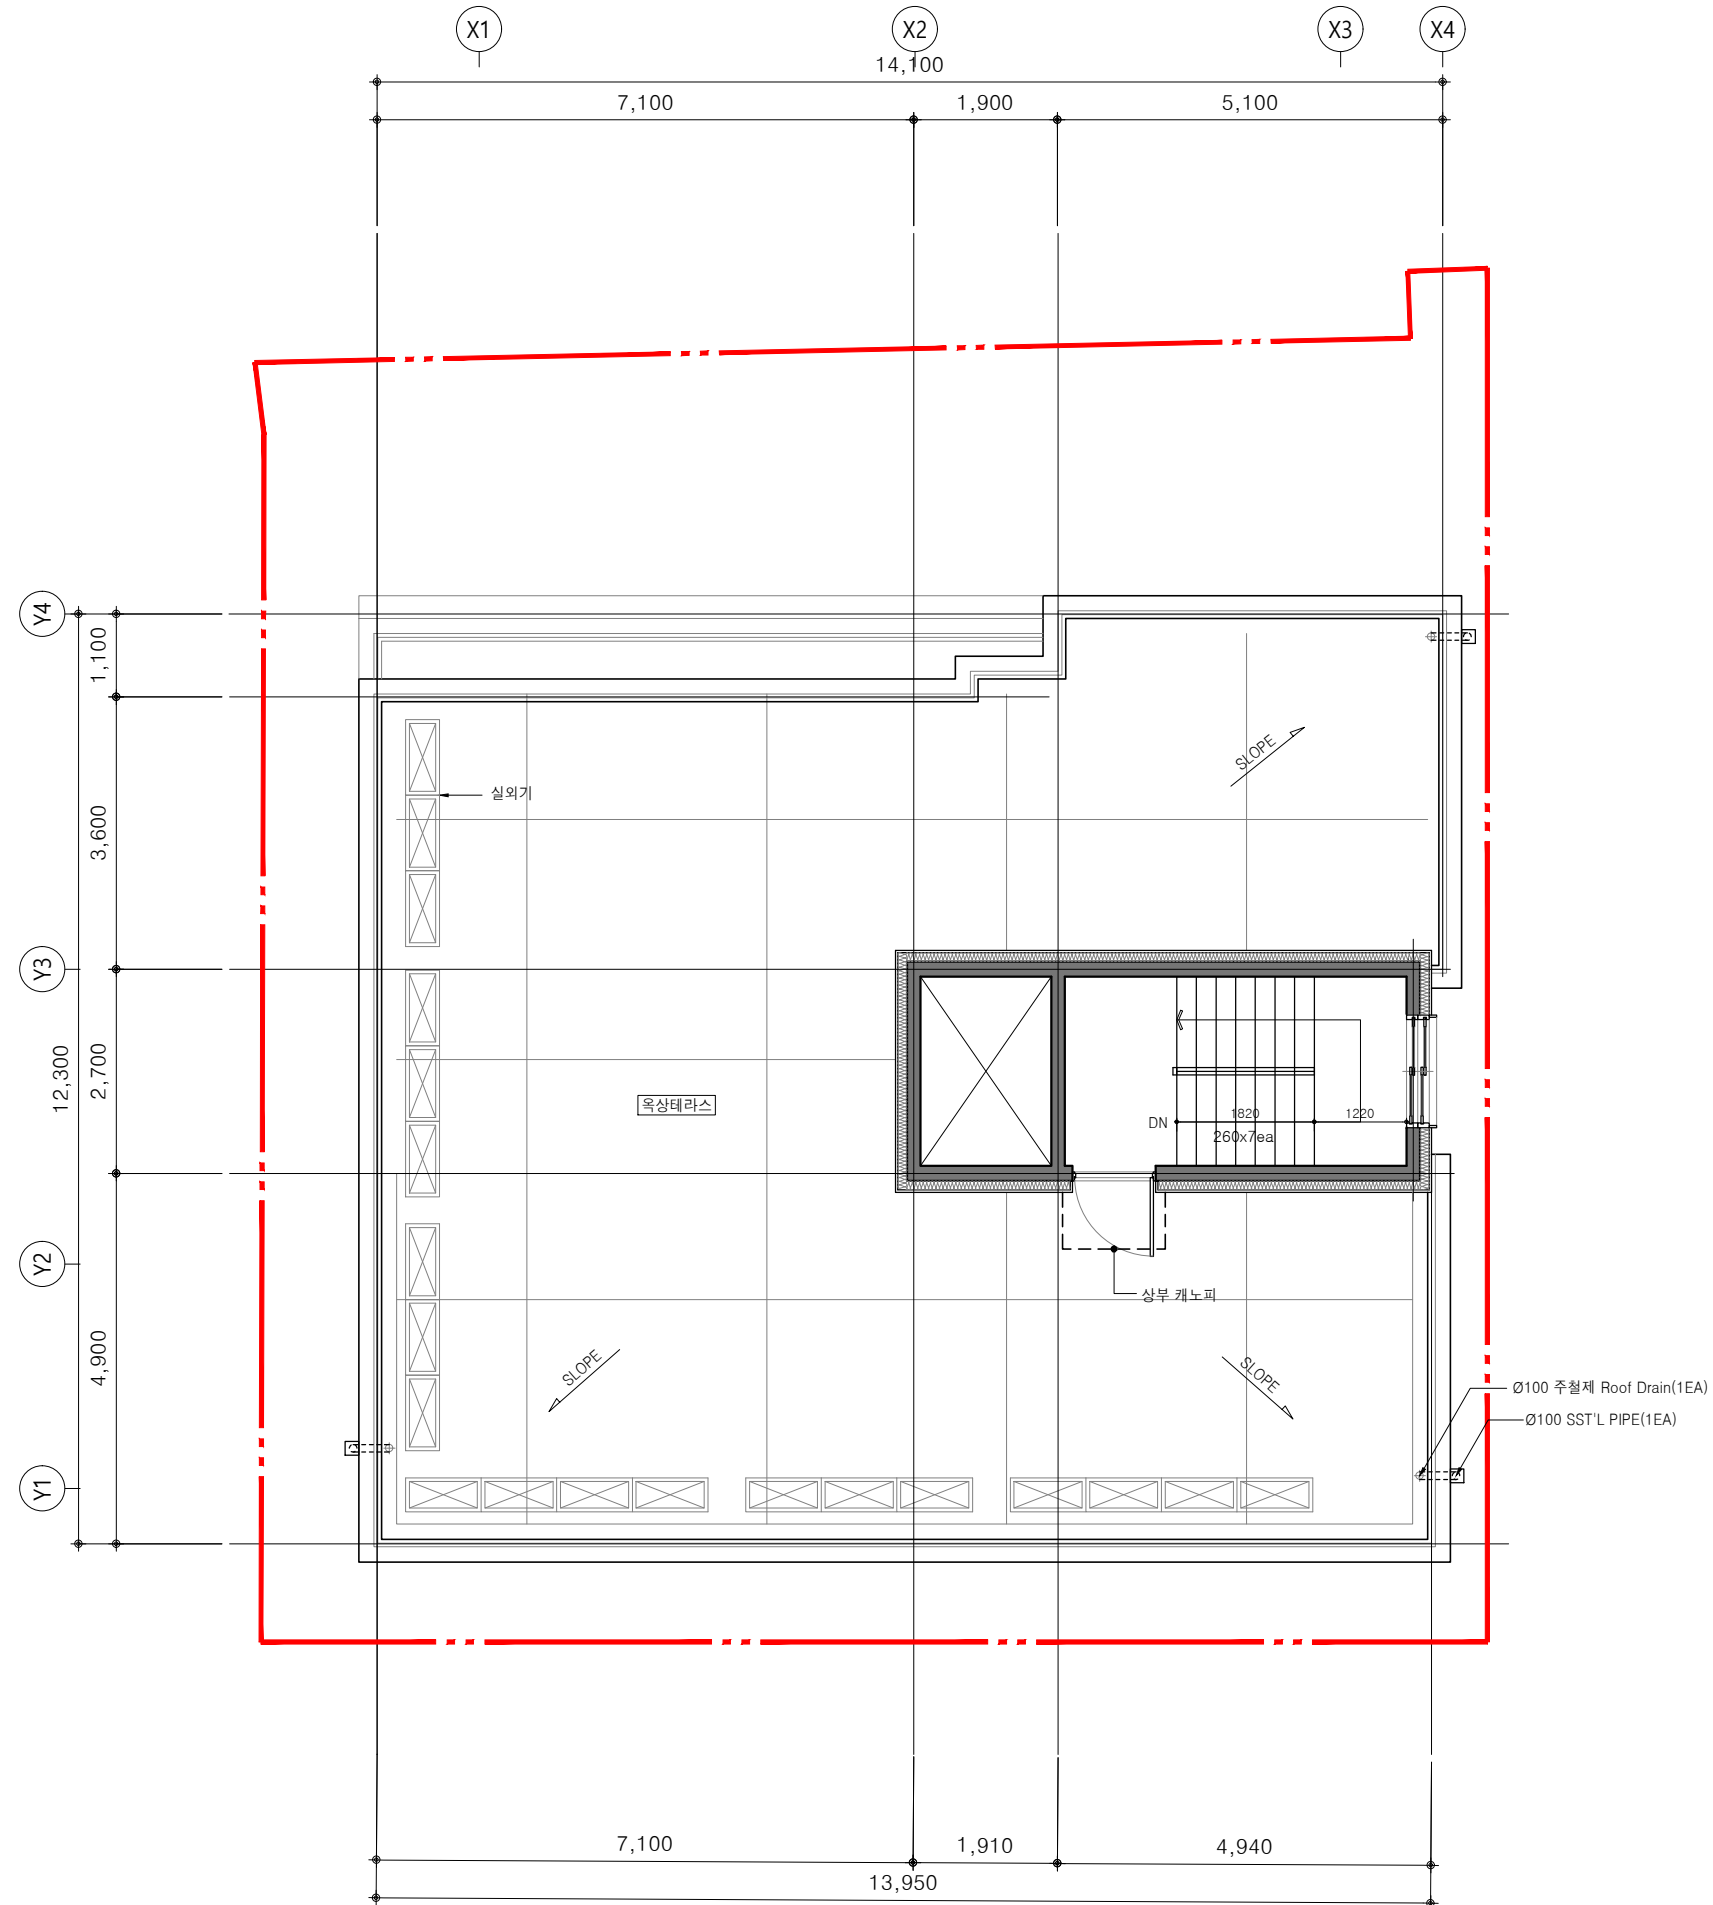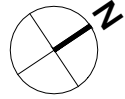

■ 파라펫 입면도

매립박스 설치 파라펫

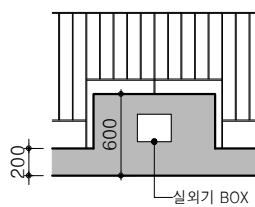

■ 빌트인설치 내역

구분	세탁기	냉장고	에어컨 (벽걸이)	전자 레인지
설치 유무	○	○	○	○

* 냉장고 상부 전자레인지 / 쿡탑 하부 세탁기 설치

지붕층 평면도
SCALE : A3=1/100

NO. DATE REVISION DRAWN APP.

1				
2				
3				

설 계 DRAWN 검토 CHECK

심 사 SUBMIT 승인 APPROVE

축 척 SCALE

A1	1 / 50
A3	1 / 100

일 자 DATE

설계번호 PROJECT NO.

도면파일명 DWG. FILE NAME

도면번호 SHEET NO.

A - 105

도면명 SUBJECT TITLE

지붕층 평면도





(주) 동심원건축사사무소

TEL : 02)3452-0597
FAX : 02)3452-0598

설계명 PROJECT TITLE

송파구 송파동
도시형생활주택 신축공사

주 기 NOTE

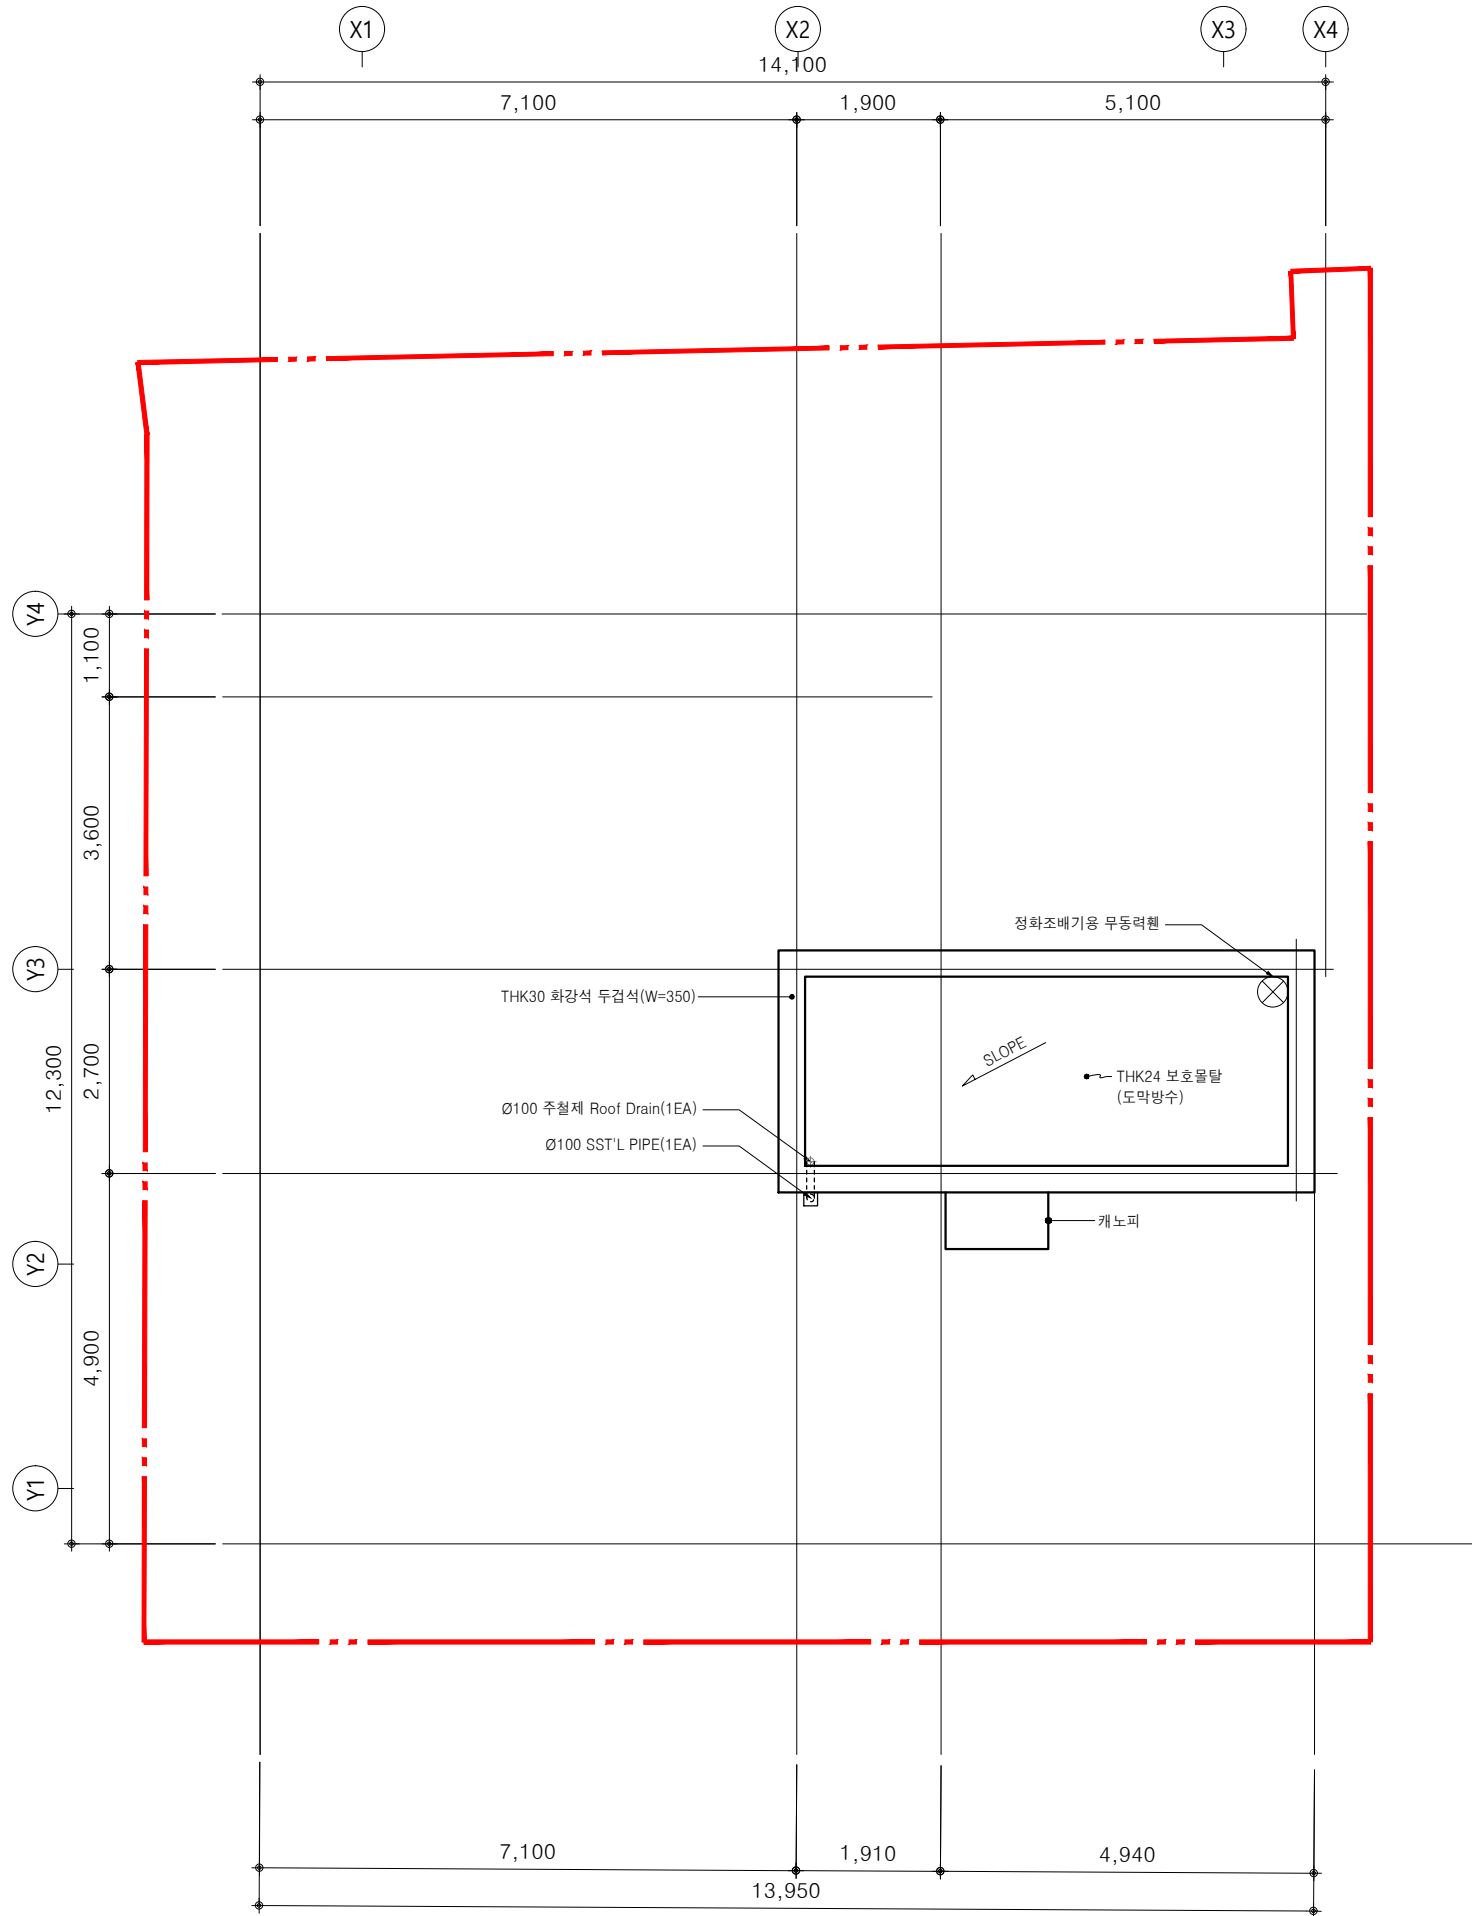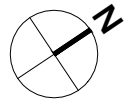

NO. DATE REVISION DRAWN APP.

1				
2				
3				

설 계 DRAWN 검 토 CHECK

심 사 SUBMIT 승 인 APPROVE

축 척 SCALE

A1	1 / 50
A3	1 / 100

일 자 DATE

설계번호 PROJECT NO.

도면파일명 DWG. FILE NAME

도면번호 SHEET NO.

A - 106

도면명 SUBJECT TITLE

지붕층 평면도




(주) 동심원건축사사무소

TEL : 02)3452-0597
FAX : 02)3452-0598


설계명 PROJECT TITLE
송파구 송파동
도시형생활주택 신축공사

주 기 NOTE

■ Key plan

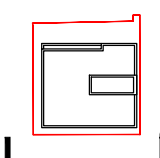

■ Key plan

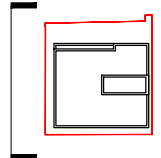

차면시설 설치
(블투명 PVC - 액산쉬트)



정 면 도
SCALE : A3=1/150



좌 측 면 도
SCALE : A3=1/150

NO. DATE REVISION DRAWN APP.

1				
2				
3				

설 계 DRAWN 검토 CHECK

심 사 SUBMIT 승인 APPROVE

축 척 SCALE

A1	1 /
A3	1 / 150

일 자 DATE


설계번호 PROJECT NO.

도면파일명 DWG. FILE NAME


도면번호 SHEET NO.
A - 301

도면명 SUBJECT TITLE
입면도-1


■ Key plan

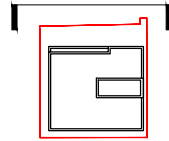

■ Key plan

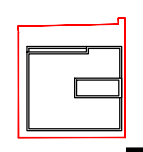

배면도
SCALE : A3=1/150

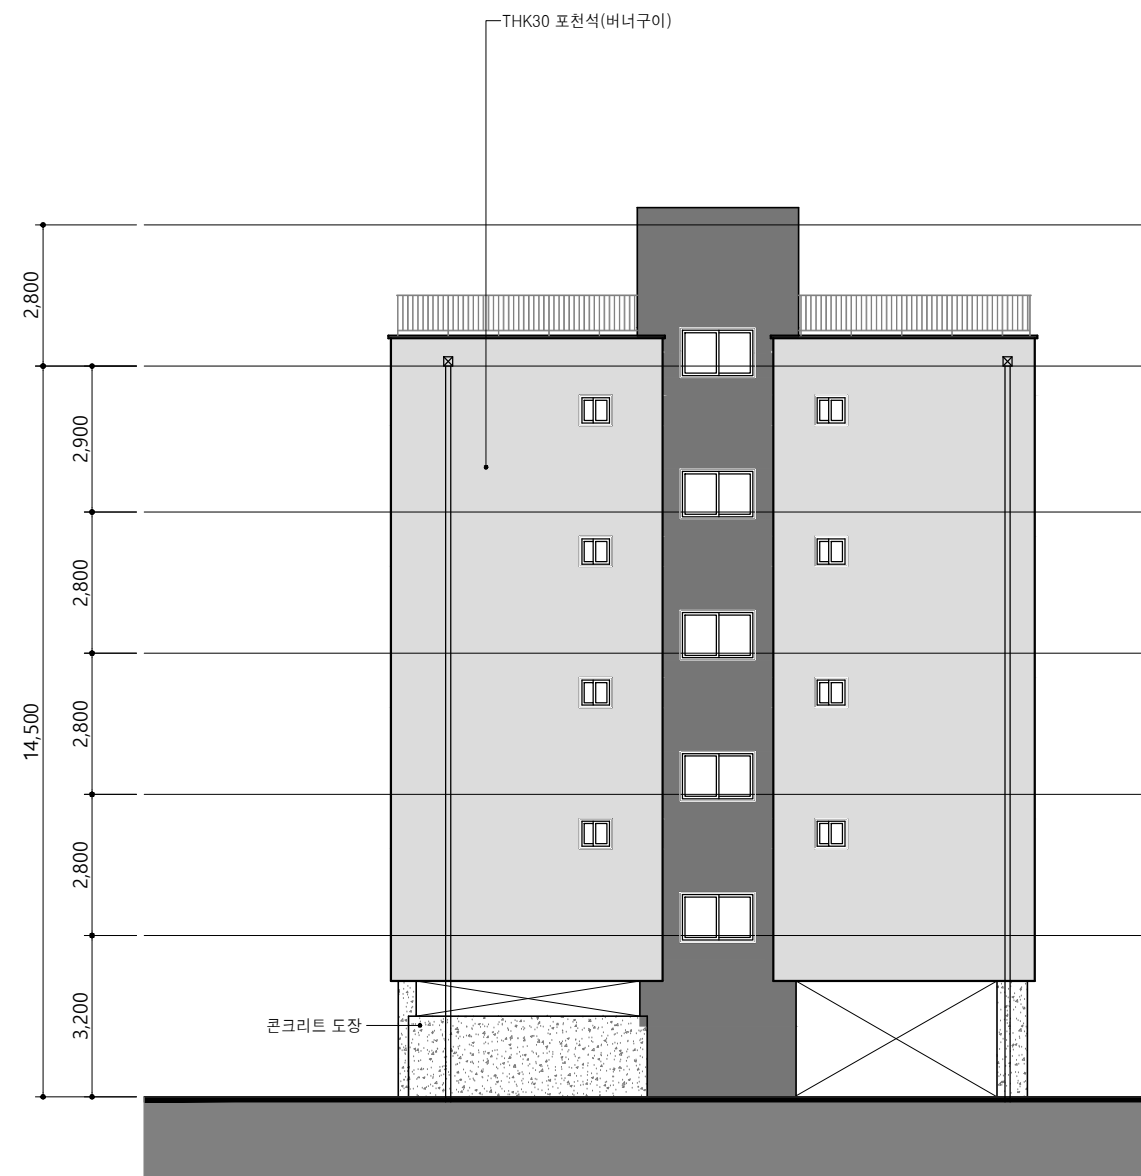

우측면도
SCALE : A3=1/150

NO. DATE REVISION DRAWN APP.

1				
2				
3				

설 계 DRAWN 검토 CHECK

심 사 SUBMIT 승인 APPROVE

축척 SCALE

A1 1 /

A3 1 / 150

일 자 DATE

설계번호 PROJECT NO.

도면파일명 DWG. FILE NAME


도면번호 SHEET NO.

A - 302

도면명 SUBJECT TITLE

입면도-2

■ Key plan

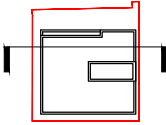

송파동 118-40



(주) 동심원건축사사무소

TEL : 02)3452-0597
FAX : 02)3452-0598

설계명 PROJECT TITLE

송파구 송파동
도시형생활주택 신축공사

주 기 NOTE

▽옥탑지붕

▽지붕

▽5층


▽4층

▽3층

▽2층

▽G.L

△1층

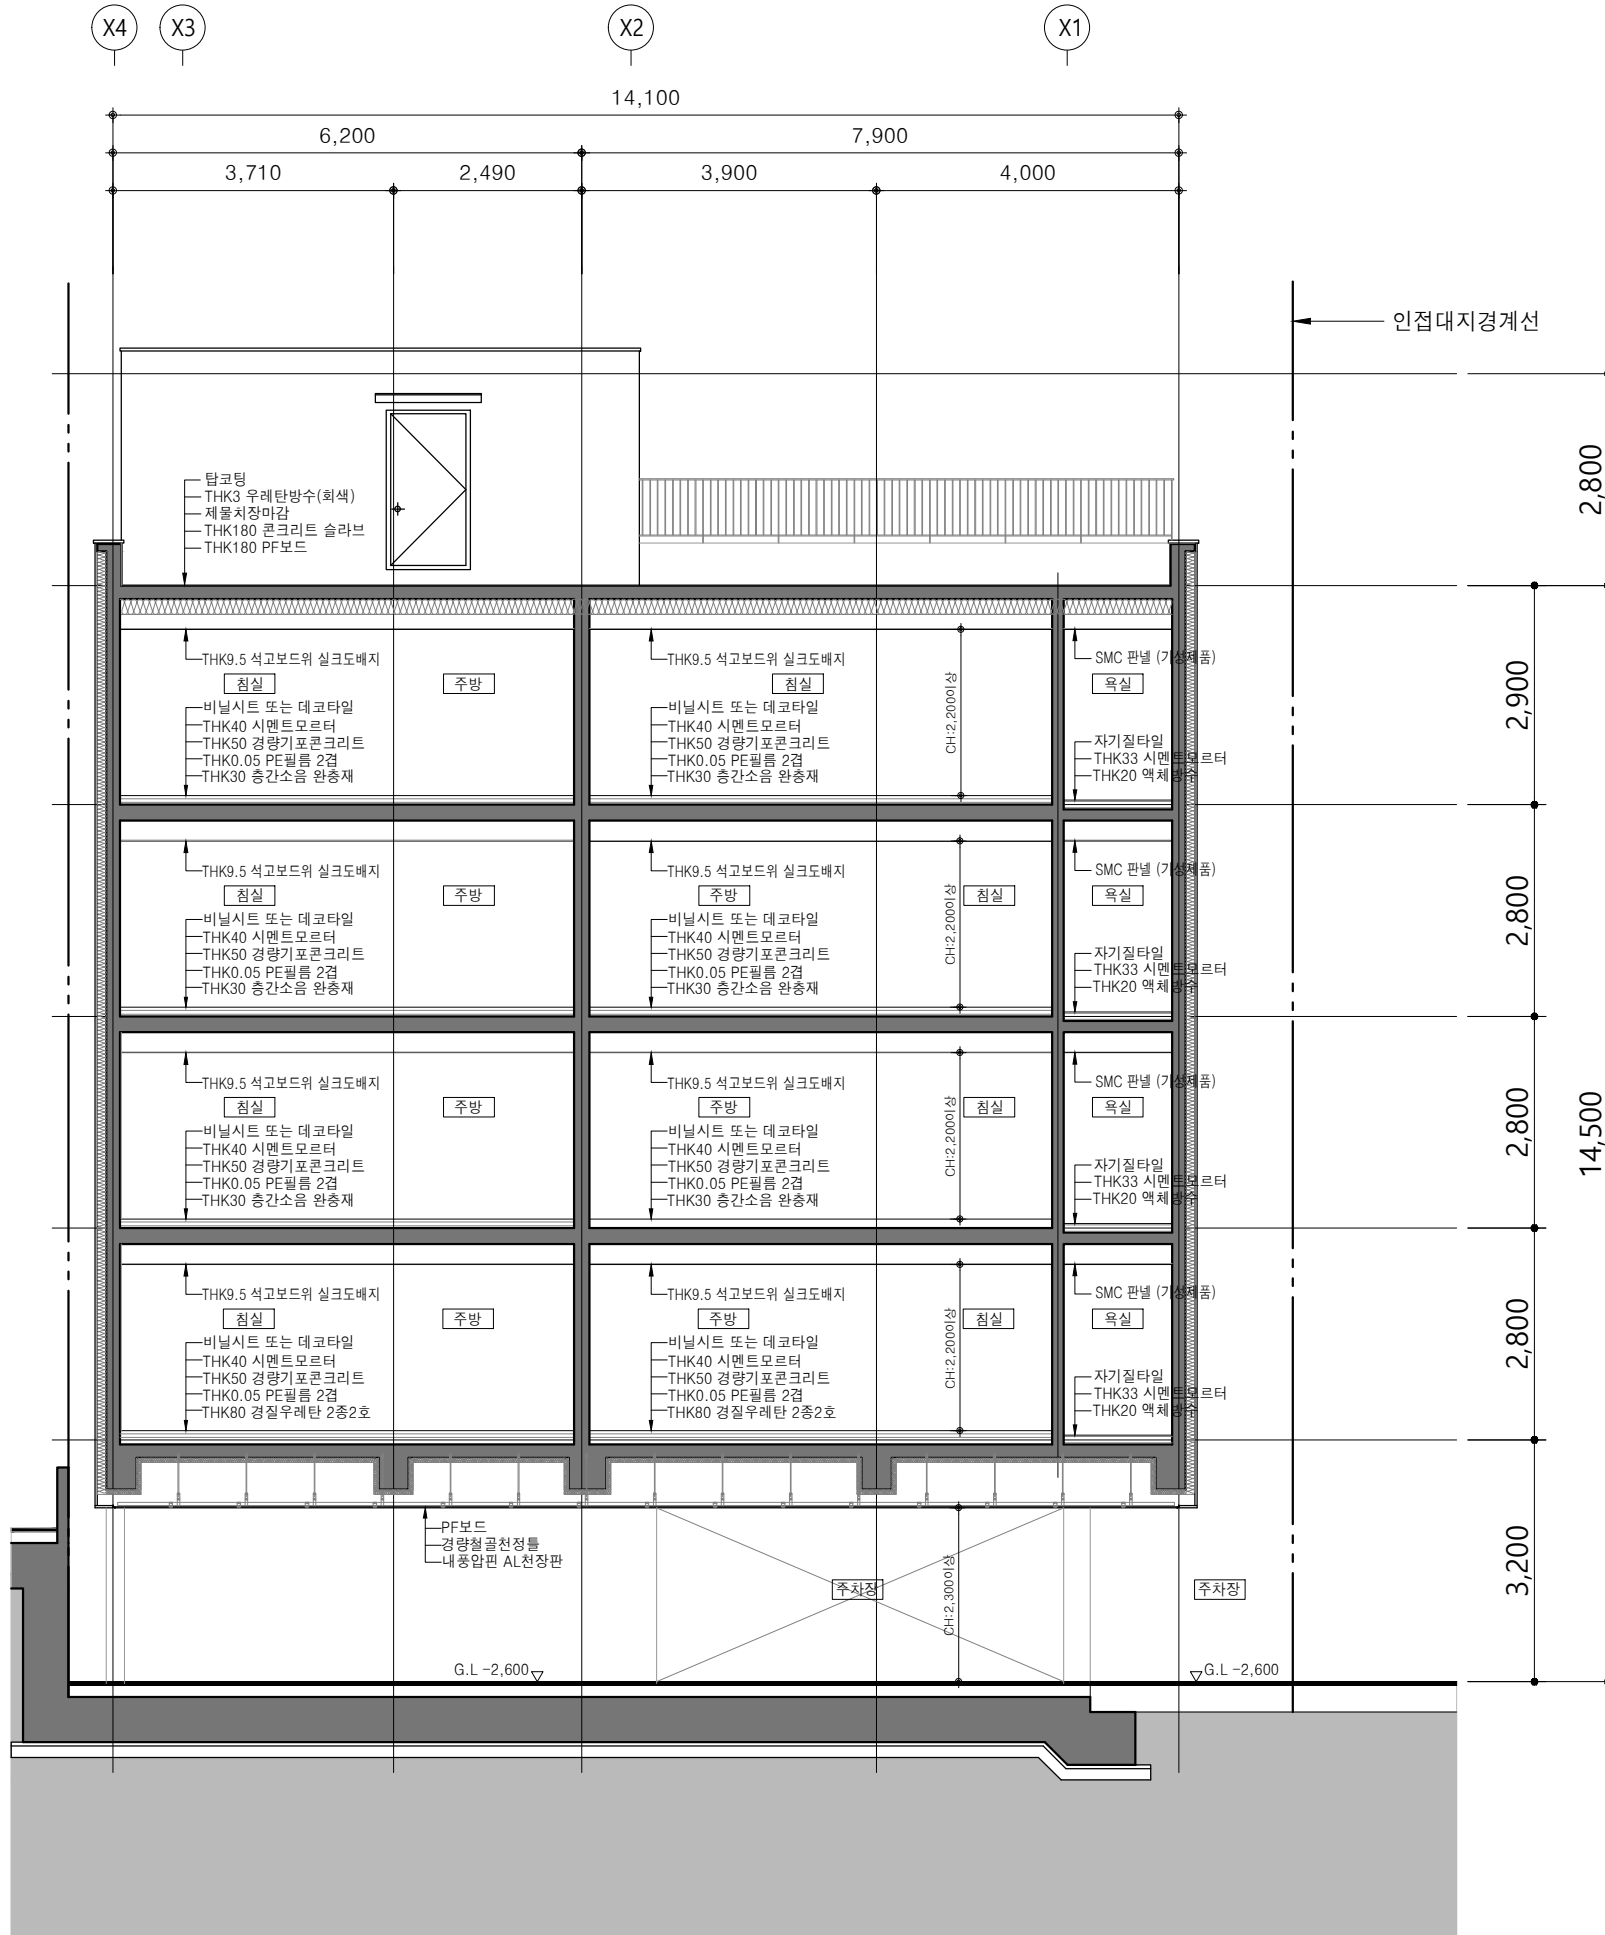

NO. DATE REVISION DRAWN APP.

1				
2				
3				

설 계 DRAWN 검토 CHECK

심 사 SUBMIT 승인 APPROVE

축 척 SCALE

A1	1 /
A3	1 / 150

일 자 DATE

설계번호 PROJECT NO.

도면파일명 DWG. FILE NAME

도면번호 SHEET NO.

A - 401

도면명 SUBJECT TITLE


주단면도-1



TEL : 02)3452-0597
FAX : 02)3452-0598

송파구 송파동
도시형생활주택 신축공사

A diagram of a rectangular building with a red outline and a black crosshair. The building has a main rectangular body and a smaller rectangular extension on the right side. A black crosshair is centered over the building, with a vertical line passing through the center and a horizontal line passing through the center. The building is labeled with 'a' and 'b' in the top left corner.

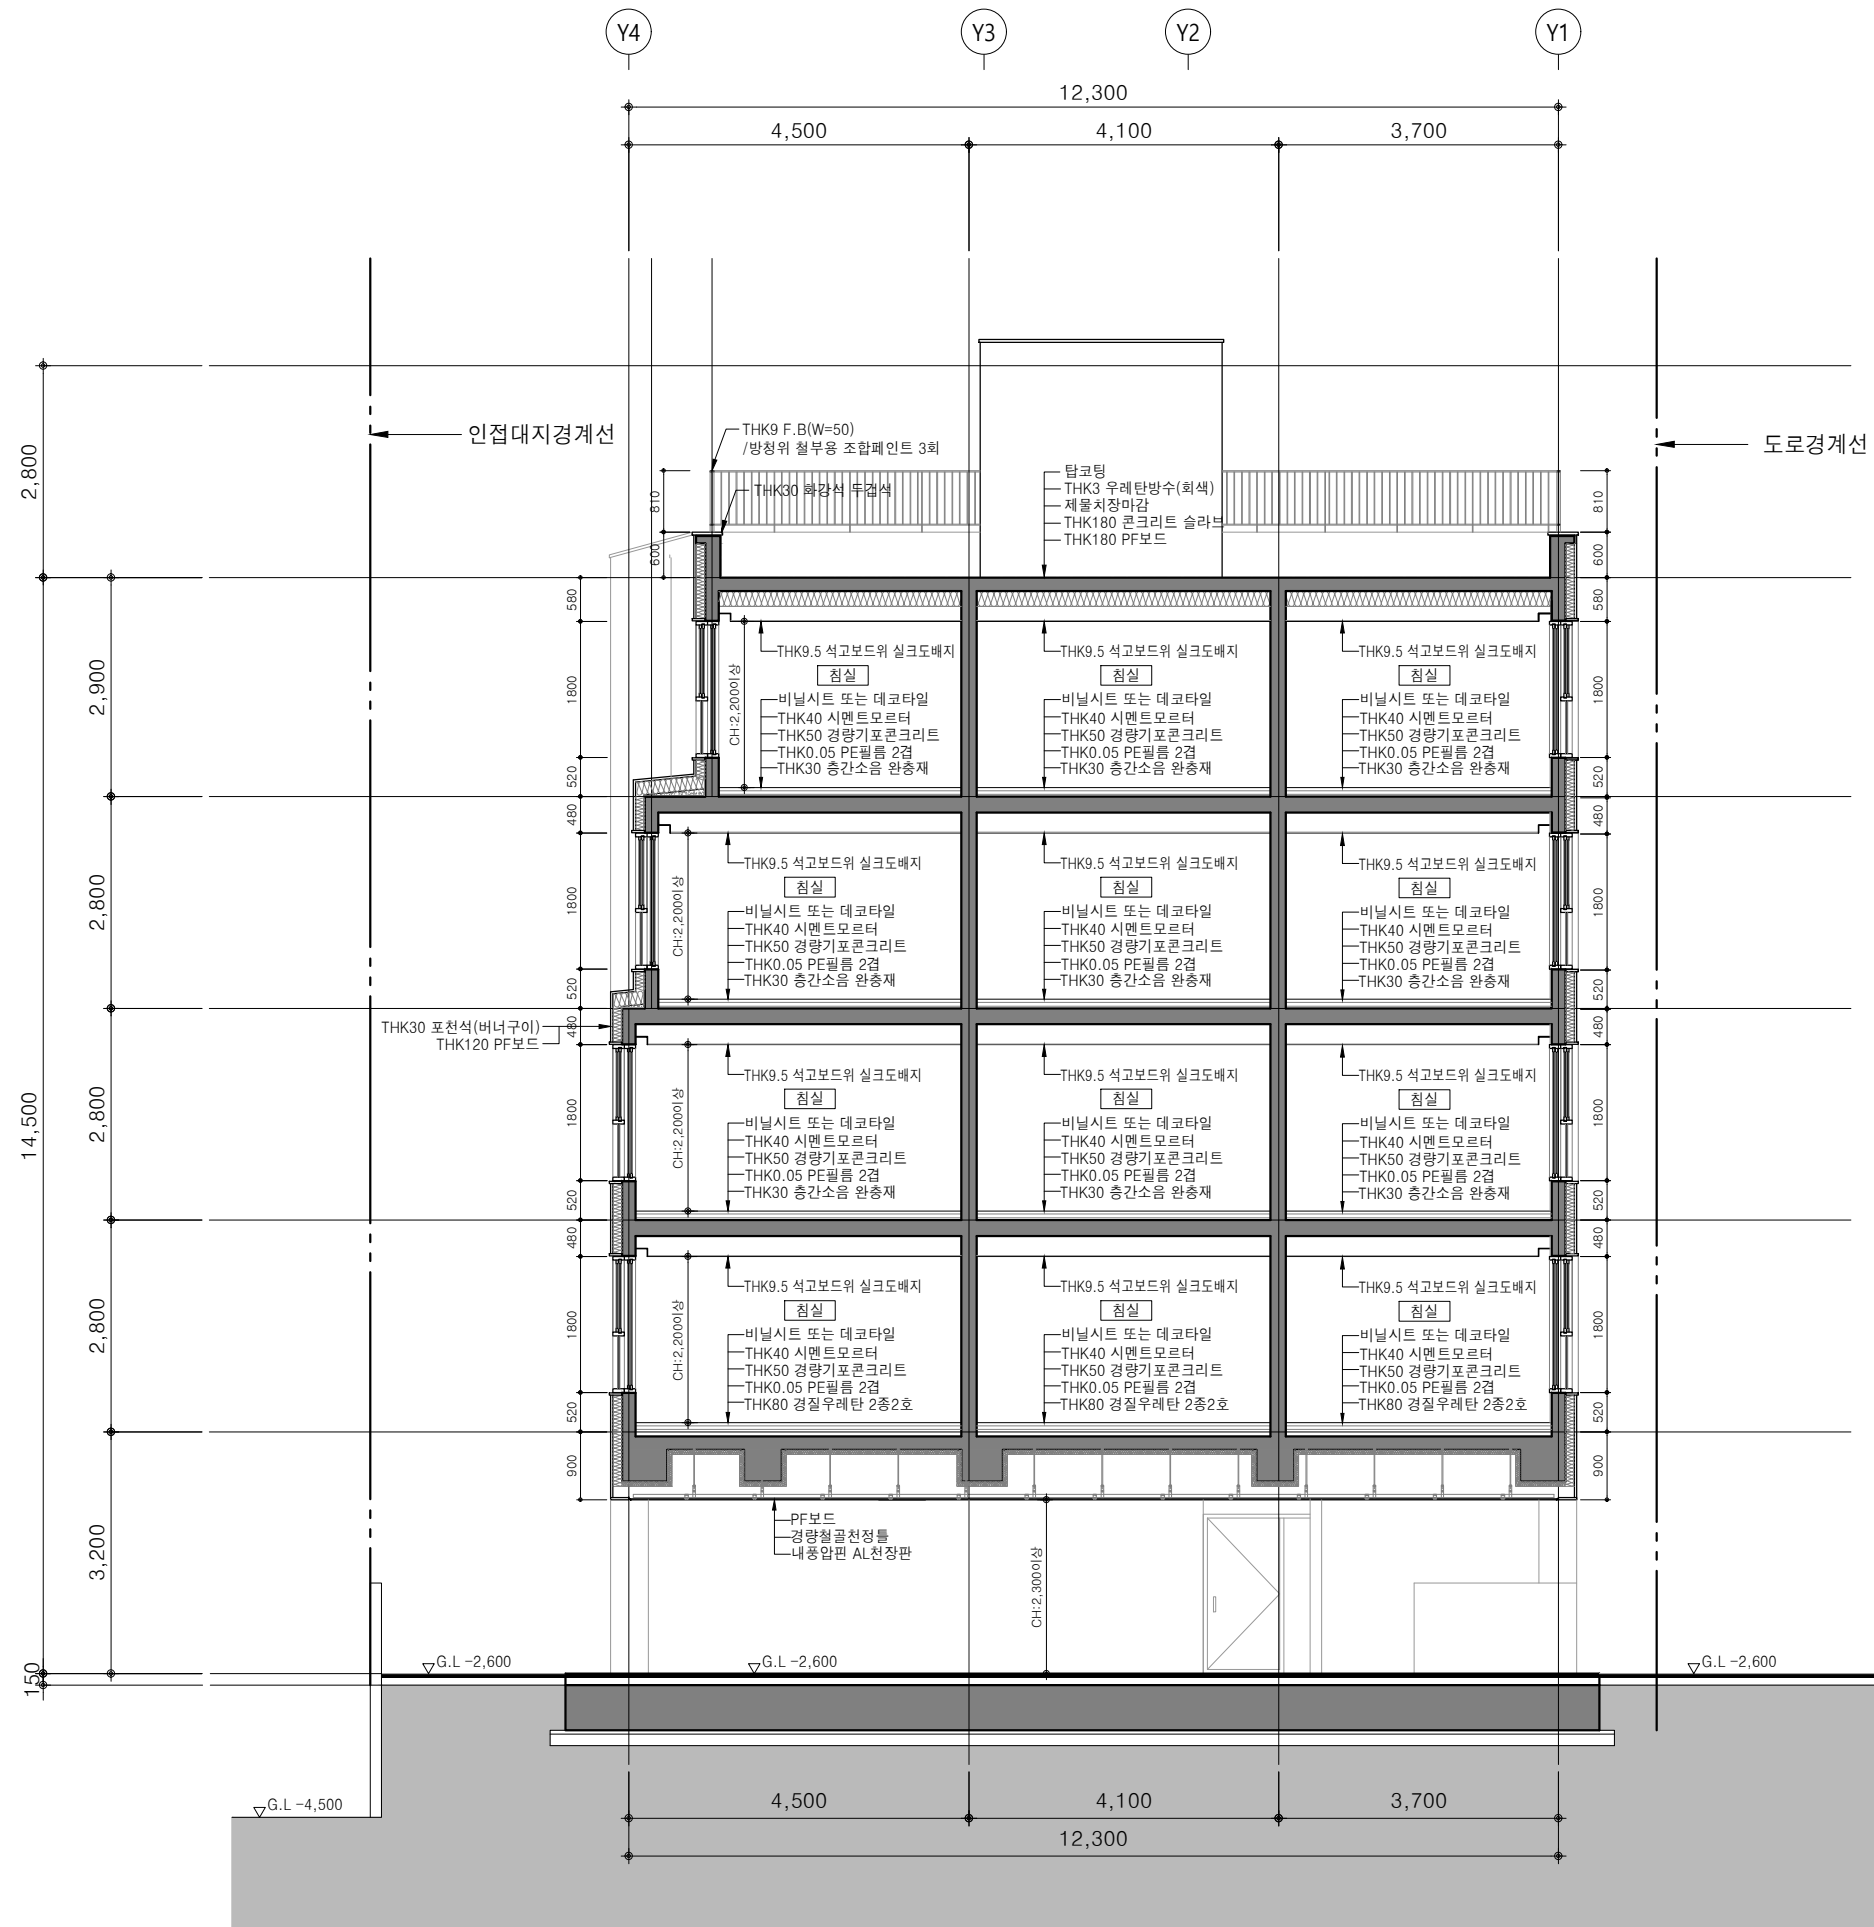

SCALE : A3=1/100

NO.	DATE	REVISION	DRAWN	APP.
-----	------	----------	-------	------

1				
2				
3				

설 계 DRAWN	검 토 CHECK
-----------	-----------

심 사 SUBMIT	승 인 APPROVE
------------	-------------

축척 SCALE	
A1	1 /
A3	1 / 150

일 자 DATE

설계번호 PROJECT NO.

도면 파일명 DWG. FILE NAME

도면번호 SHEET NO.

A - 402

도면명 SUBJECT TITLE

주단면도-2