


1. 조감도 또는 투시도




2. 건축개요

■건축개요

- 설 계 명 : 문정동 도시형생활주택 신축공사
- 대 지 위 치 : 서울특별시 송파구 문정동 13-7번지
- 지 역·지 구 : 제2종 일반주거지역
- 건 물 용 도 : 도시형생활주택(원룸(청년))
- 건 물 규 모 : 지상 5층, 1개동
- 대 지 면 적 : 294.00㎡ (15M,8M도로에 접함)
- 건 축 면 적 : 176.14㎡
- 연 면 적 : 587.64㎡
- 건 폐 율 : 59.91%
- 용 적 륜 : 199.88%
- 최 고 높 이 : 14.35m
- 건 물 구 조 : 철근콘크리트조
- 주 차 대 수 : 5.6대(법정), 7대(계획)
- 조 경 면 적 : 14.70㎡(법정), 17.86㎡(계획)


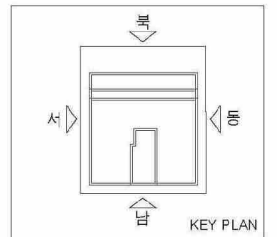


3. 입면도

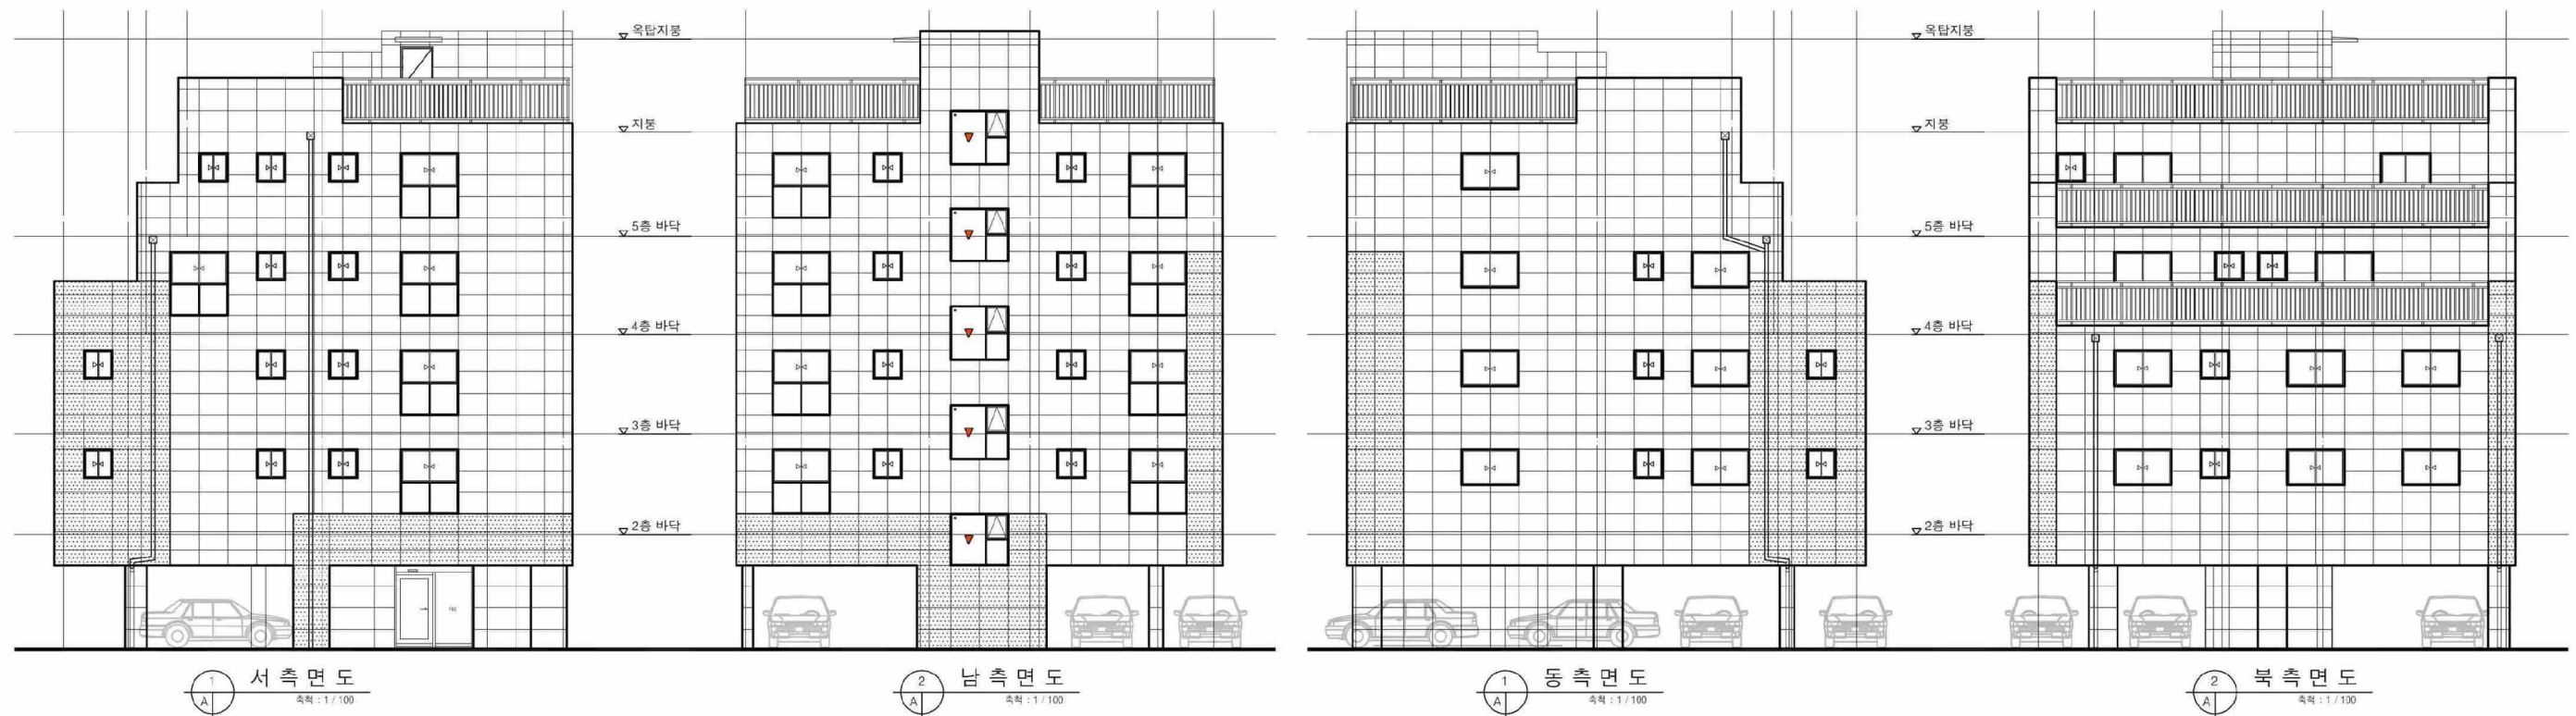

4. 설계자 의도

- 1.도로와 필지가 만나는 방식에 있어서 최우선적으로 주차영역과 보행자진입영역을 구분하는 동시에 건축이격선에 의해 발생하는 여유공간을 보행로의 확장으로 인식되도록 함.
- 2.정북일조사선제한으로 인한 4,5층 매스변화와 실구성에 의한 창배치와 외관재료들의 적절한 분배와 조합으로 주변과 어울리면서도 보다 감각적인 느낌의 주택을 계획하려함.
- 3.확실적인 구성이 아닌 입주자들의 특성에 맞춰 선택이 가능한 단위세대구성.

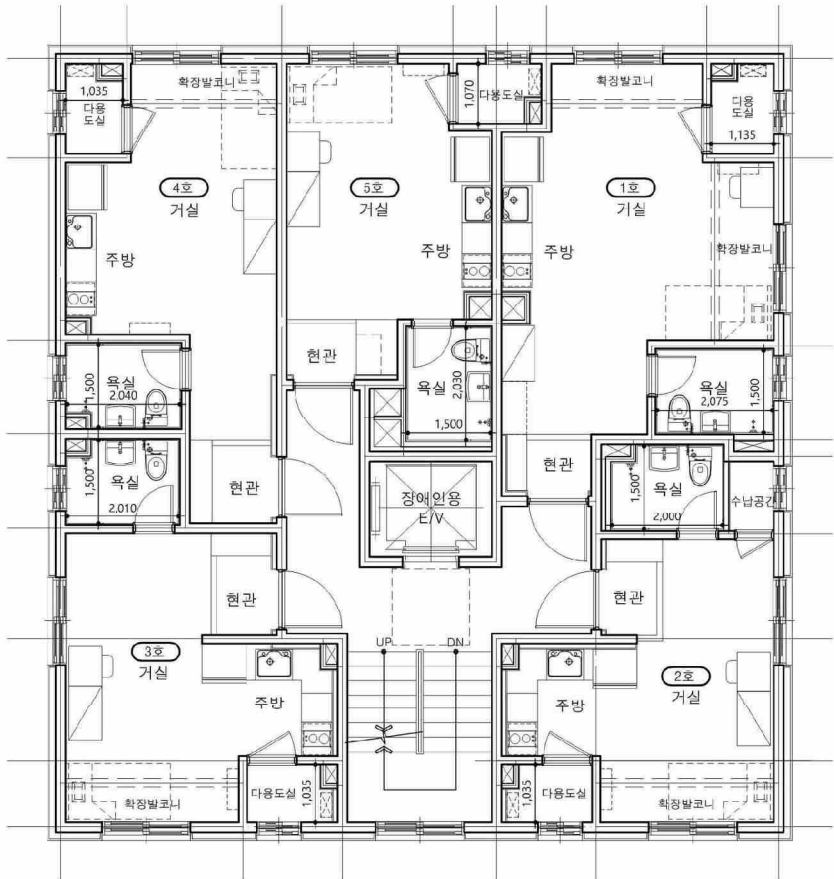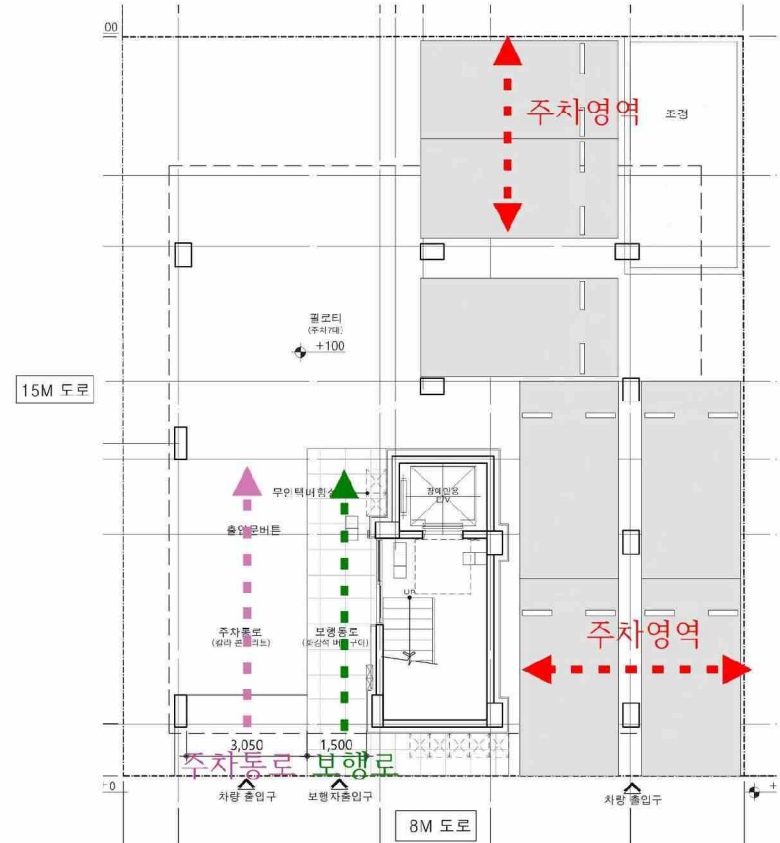

5. 재료계획

포천석과 마천석을 사용하여 같은 화강석이지만 다른색을 사용하여 밋밋한 외관의 입면분절느낌을 유도하여 모던한 주택외관을 계획함.

모든 재료는 KS표시제품 사용을 원칙으로 하였으며 KS표시제품이 없는 품목은 동등이상의 제품을 사용토록 함.

다세대 내부마감
바닥 : 판넬티팅 / 비닐장판마감
벽 : 실크벽지
천정 : 9.5mm석고보드/실크천정지


계단실 내부마감
바닥 : 천연화강석
벽,천정 : 다재 무늬 도료

■외장재


■내장재

6. 색채계획

주변과 조화를 이룰수있도록 무채색의 저채도계열 색상의 재료를 사용하여 계획

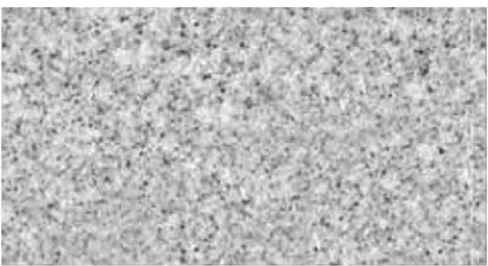

포천석

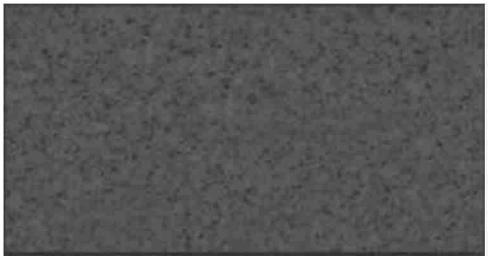

마천석



PROJECT TITLE


문정동 13-7
도시형생활주택
신축공사

매매계약


제이케이건축사사무소(주)
Architects & Planners
TEL : 02-533-9431 FAX : 02-532-9431

NOTE

설 계 변 경 DESCRIPTION OF REVISION				
번 호	내 용			
일 자	설 계	검 토	심 사	승 인
△	2021.06			
승인 APPROVED BY				
축 척 SCALE	A1	1 /		
	A3	1 /		
도면명 DRAWING TITLE				
조 감 도				
도면번호 DRAWING NO.				
A - 004				

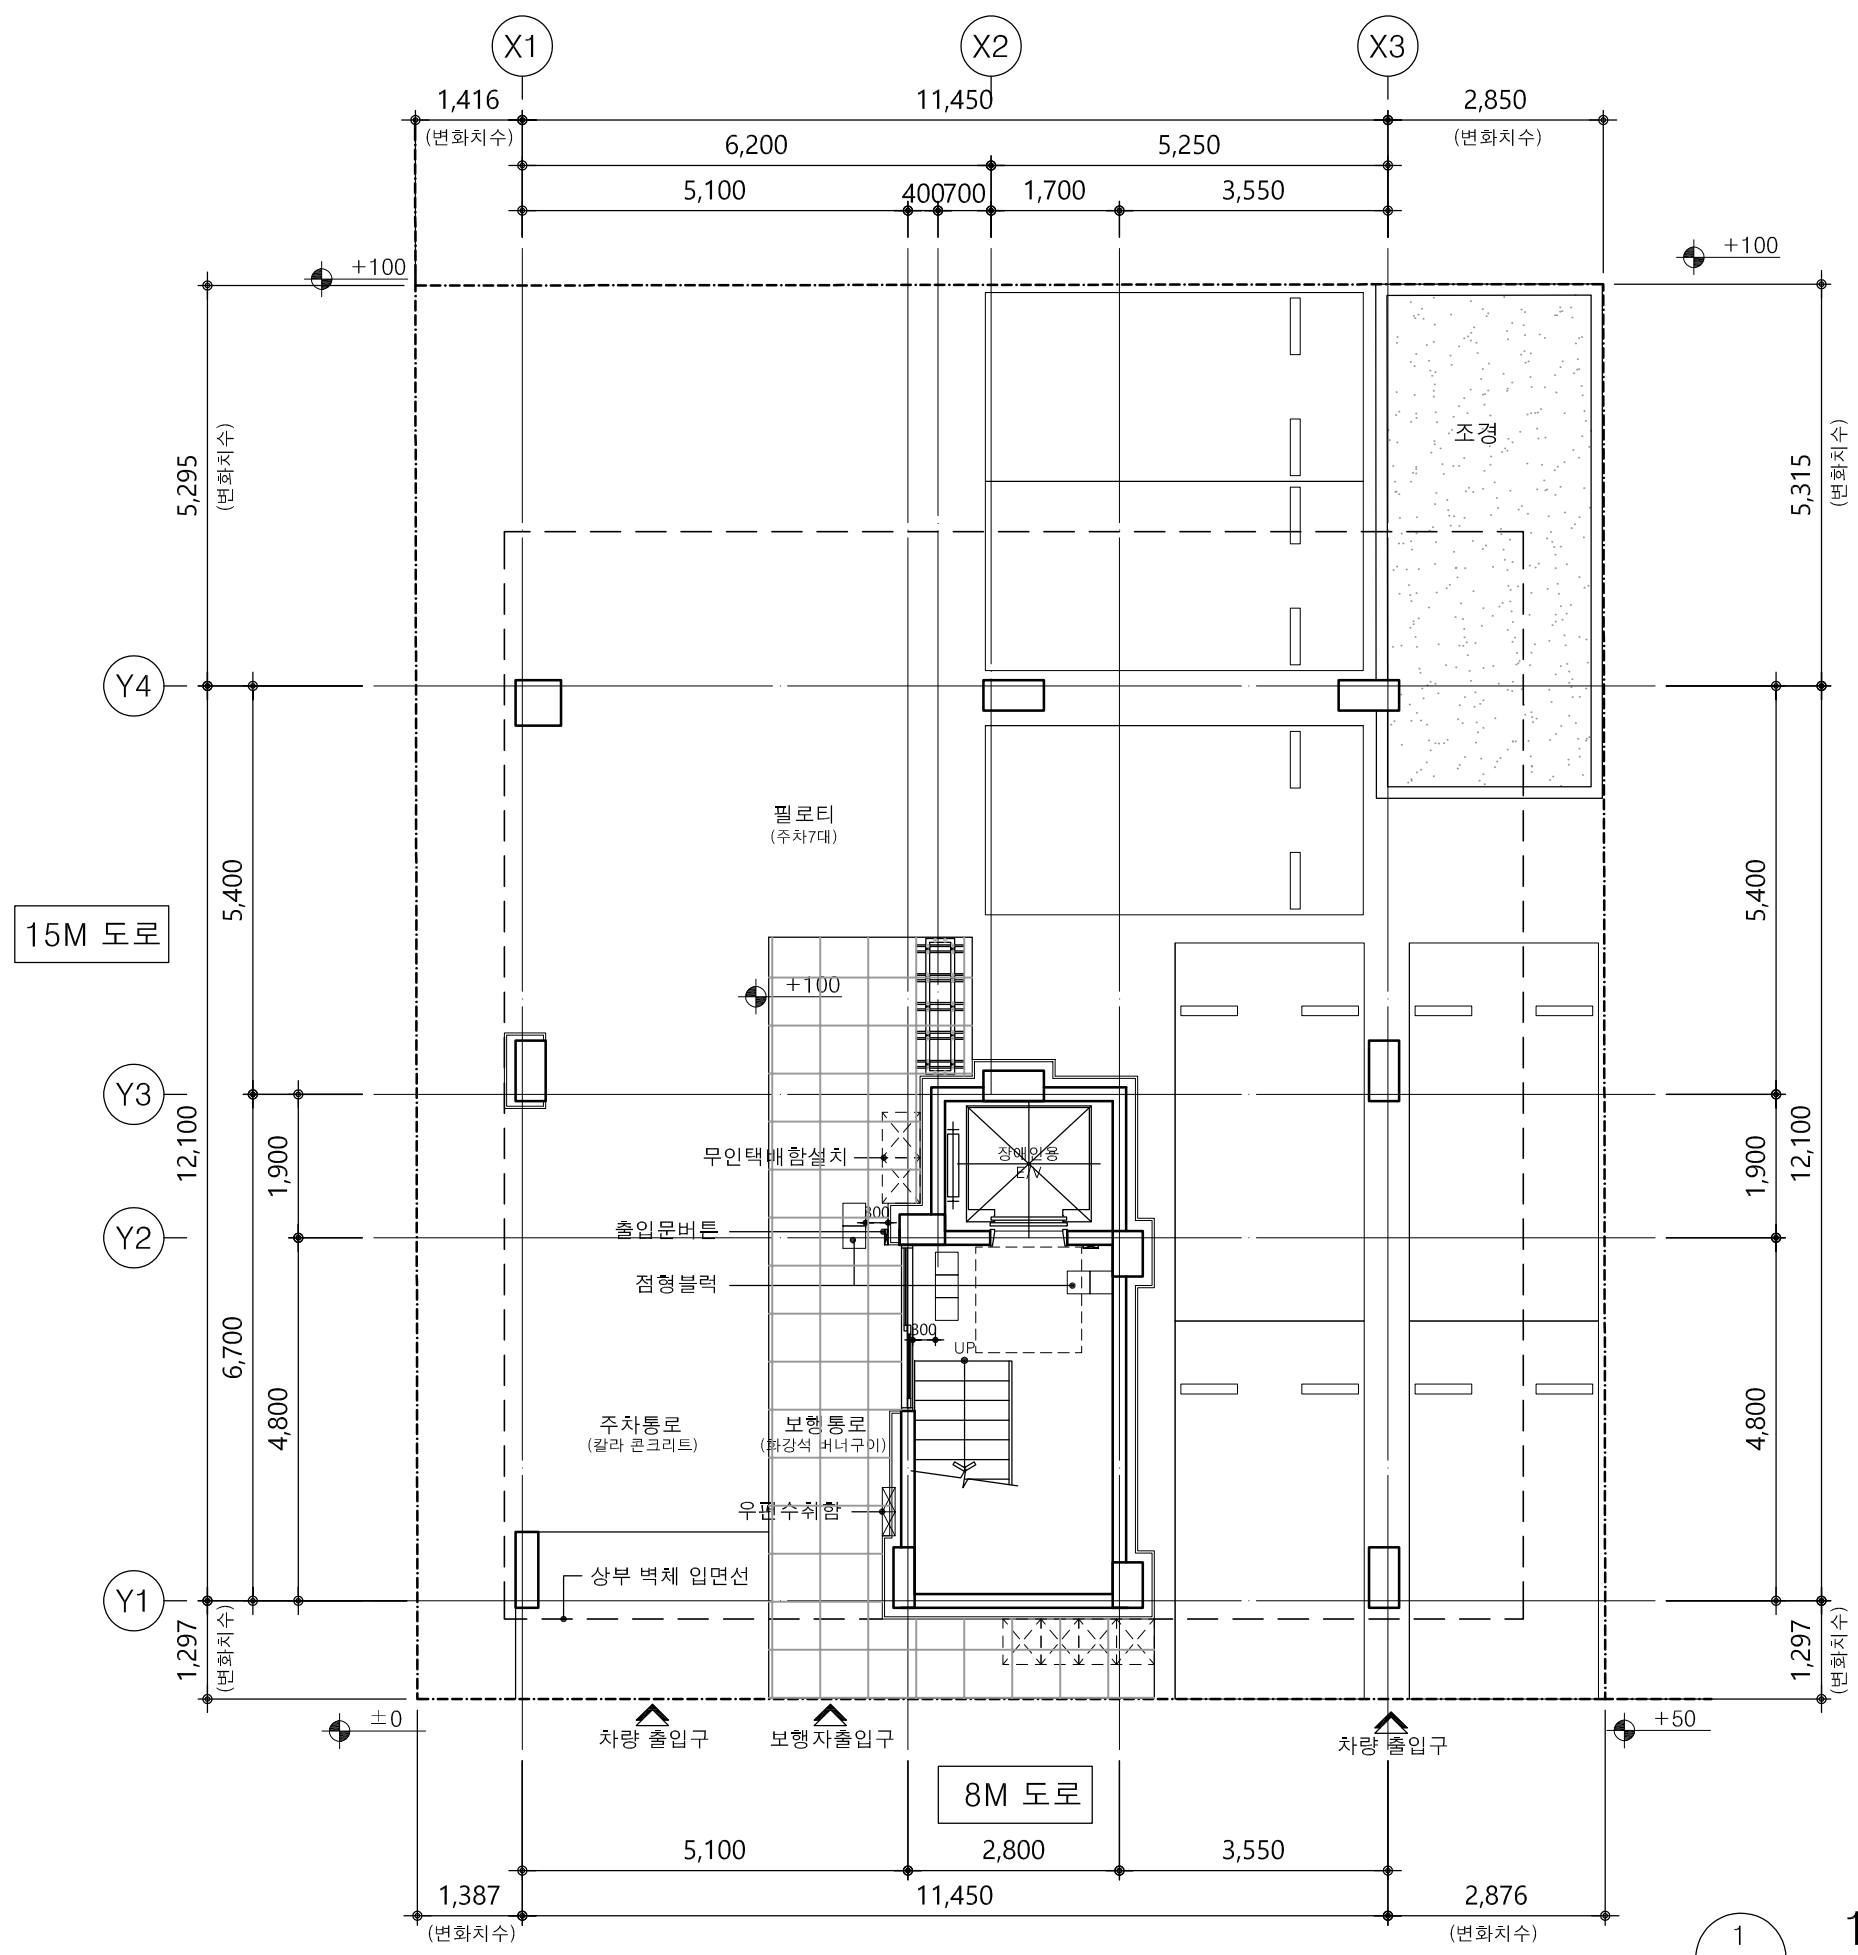

PROJECT TITLE

문정동 13-7
도시형생활주택
신축공사

매매계약



제이케이건축사사무소(주)
Architects & Planners
TEL : 02-533-9431 FAX : 02-532-9431

NOTE

1. 콘크리트: fck = 24 MPa

2. 철근: fy = 400 MPa

3. 세대내벽두께: 150mm (복배근)

4. 외벽두께: 180mm (복배근)

5. 코아벽두께: 180mm (복배근)

6. 세대간벽두께: 180mm (복배근)

7. 슬라브두께: 210mm (3~5층)

8. 슬라브두께: 180mm (2층, 지붕)

설 계 변 경
DESCRIPTION OF REVISION

번 호	내 용
일 자	설 계
2021.06	검 토
	심 사
	승 인

승인 APPROVED BY

축척
SCALE




A1	1 /
A3	1 / 100

도면명 DRAWING TITLE

1층 평면도

도면번호 DRAWING NO.

A - 201

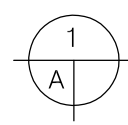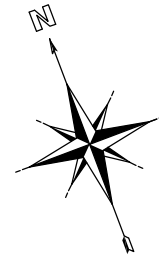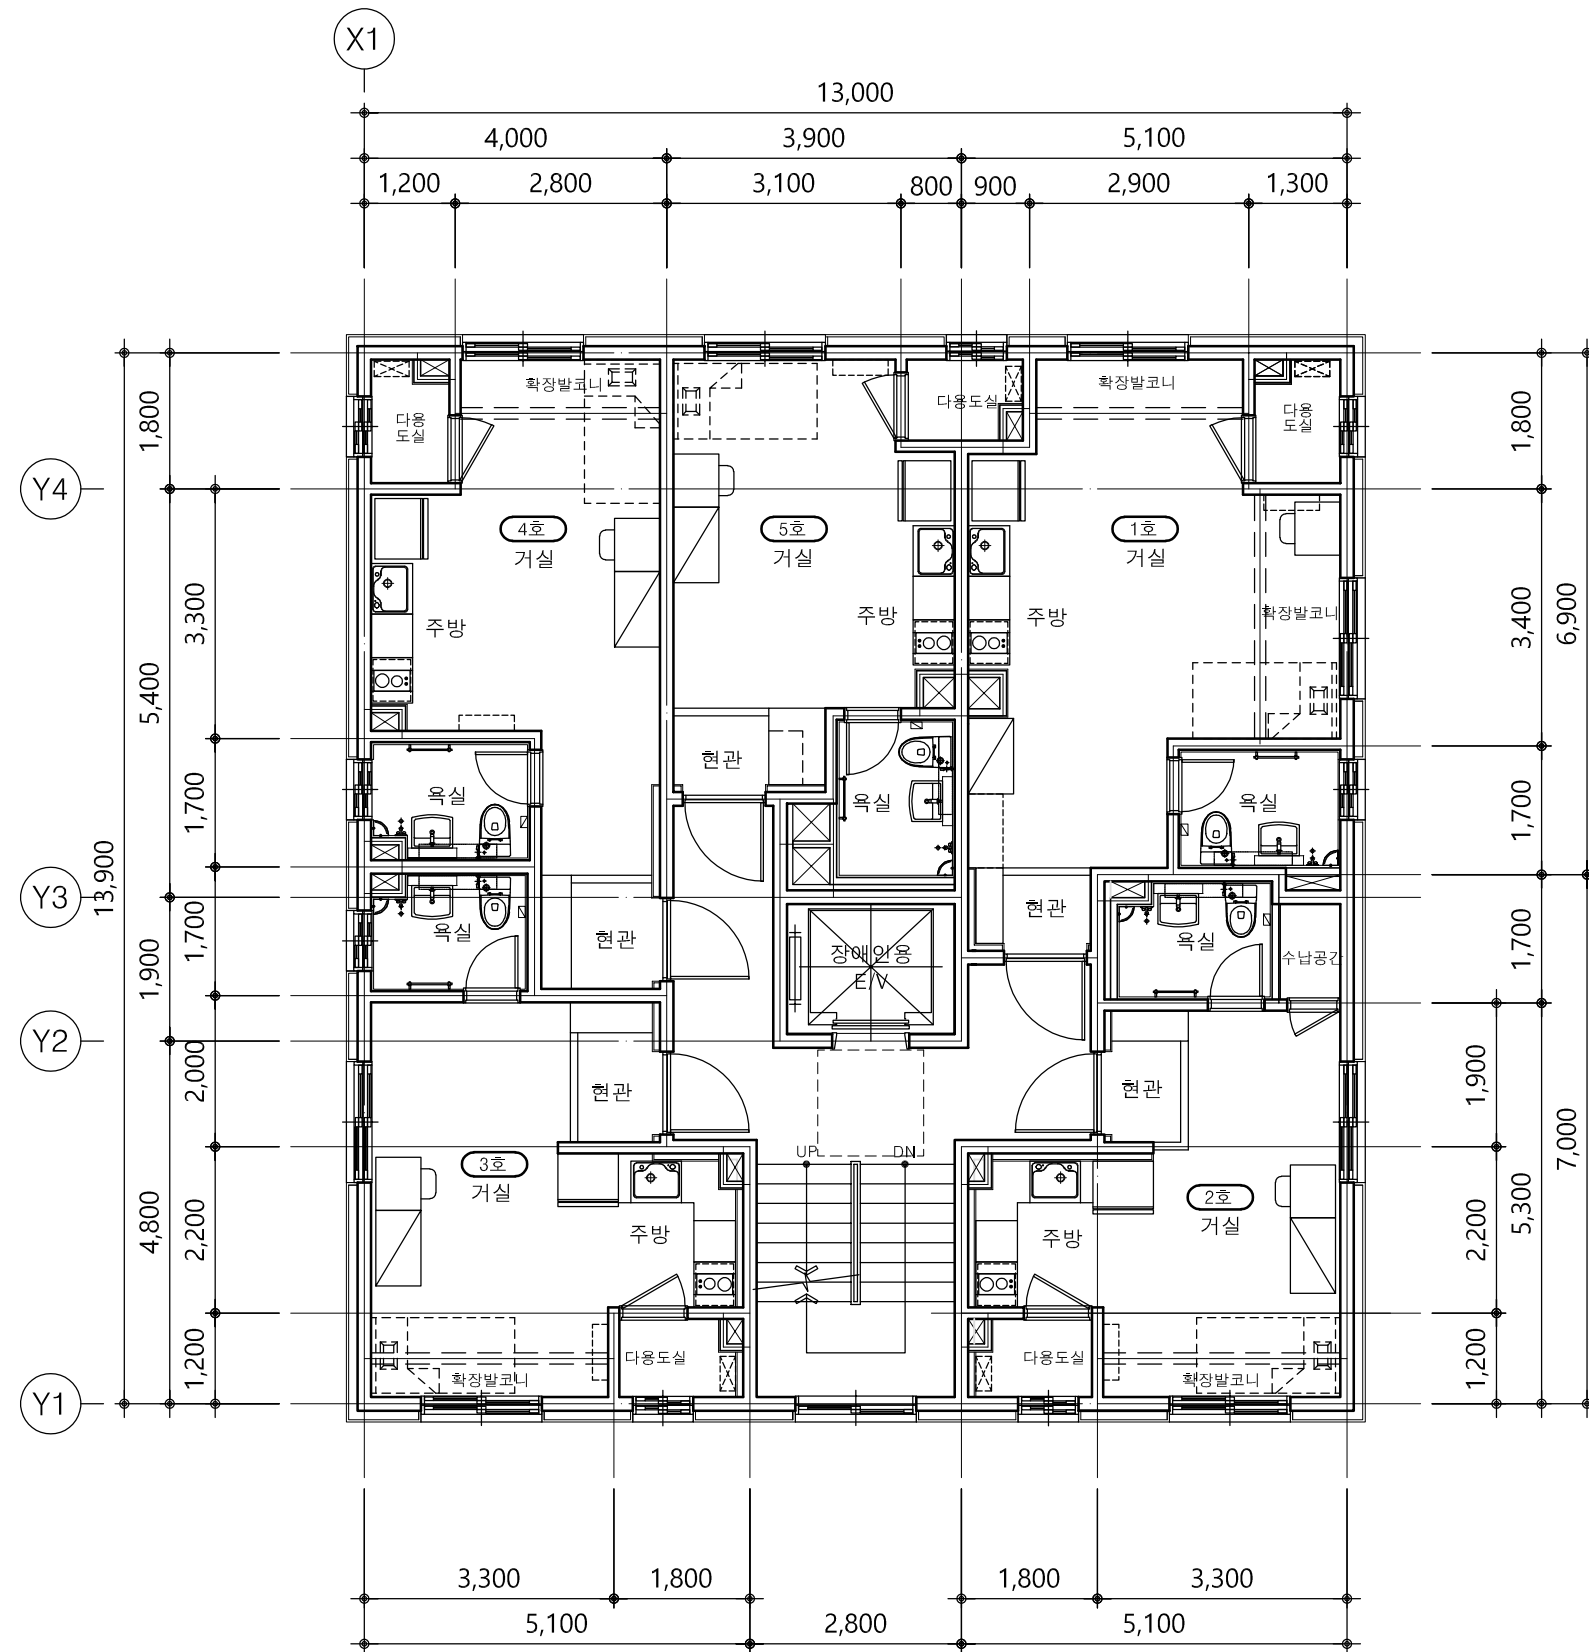

2-3층 평면도

축척 : 1 / 100

PROJECT TITLE
문정동 13-7
도시형생활주택
신축공사

매매계약

제이케이건축사사무소(주)
Architects & Planners
TEL : 02-533-9431 FAX : 02-532-9431

NOTE
1. 콘크리트: fck = 24 MPa
2. 철근 : fy = 400 MPa
3. 세대내벽두께: 150mm (복배근)
4. 외벽두께: 180mm (복배근)
5. 코아벽두께: 180mm (복배근)
6. 세대간벽두께: 180mm (복배근)
7. 슬라브두께: 210mm (3~5층)
8. 슬라브두께: 180mm (2층, 지붕)




설 계 변 경 DESCRIPTION OF REVISION				
번 호	내 용			
일 자	설 계	검 토	심 사	승 인
△	2021.06			

승인 APPROVED BY

축 척 SCALE	A1	1 /
	A3	1 / 100

도면명 DRAWING TITLE
2-3층 평면도

도면번호 DRAWING NO.
A - 202

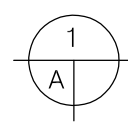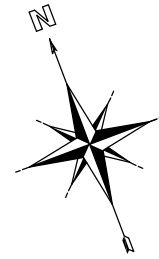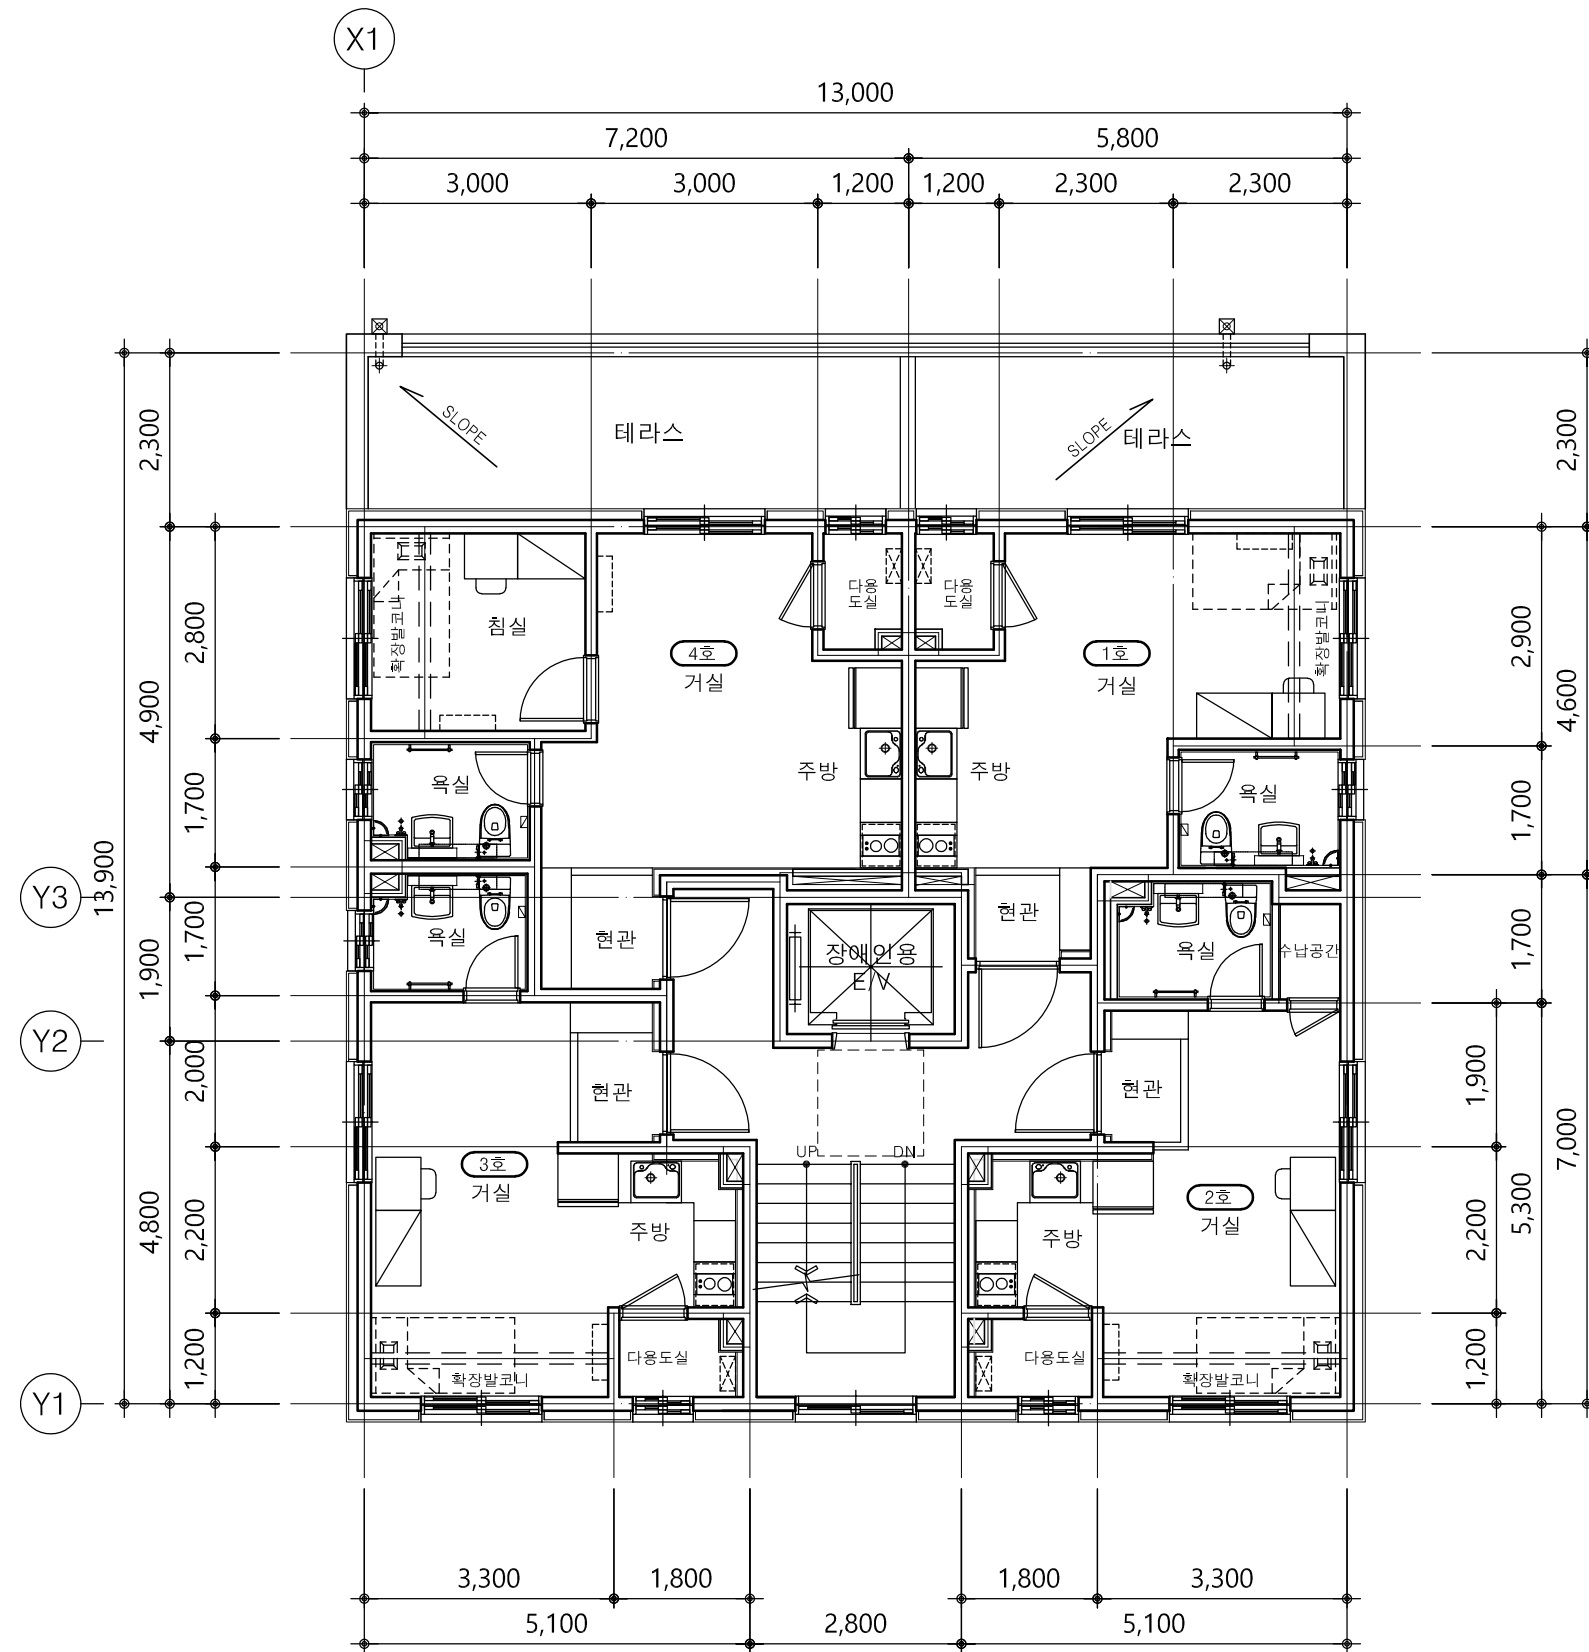

4층 평면도

축척 : 1 / 100

PROJECT TITLE

문정동 13-7
도시형생활주택
신축공사

매매계약

제이케이건축사사무소(주)
Architects & Planners
TEL : 02-533-9431 FAX : 02-532-9431

NOTE

1.콘크리트: fck = 24 MPa
2. 철근 : fy = 400 MPa
3. 세대내벽두께:150mm(복배근)
4. 외벽두께:180mm(복배근)
5. 코아벽두께:180mm(복배근)
6. 세대간벽두께:180mm(복배근)
7. 슬라브두께:210mm(3~5층)
8. 슬라브두께:180mm(2층,지붕)

설 계 변 경
DESCRIPTION OF REVISION

번 호	내 용
일 자	설 계 경 토 심 사 승 인
△	2021.06

승인 APPROVED BY




축 척
SCALE

A1	1 /
A3	1 / 100

도면명 DRAWING TITLE

4층 평면도

도면번호 DRAWING NO.
A - 203

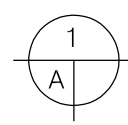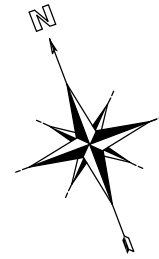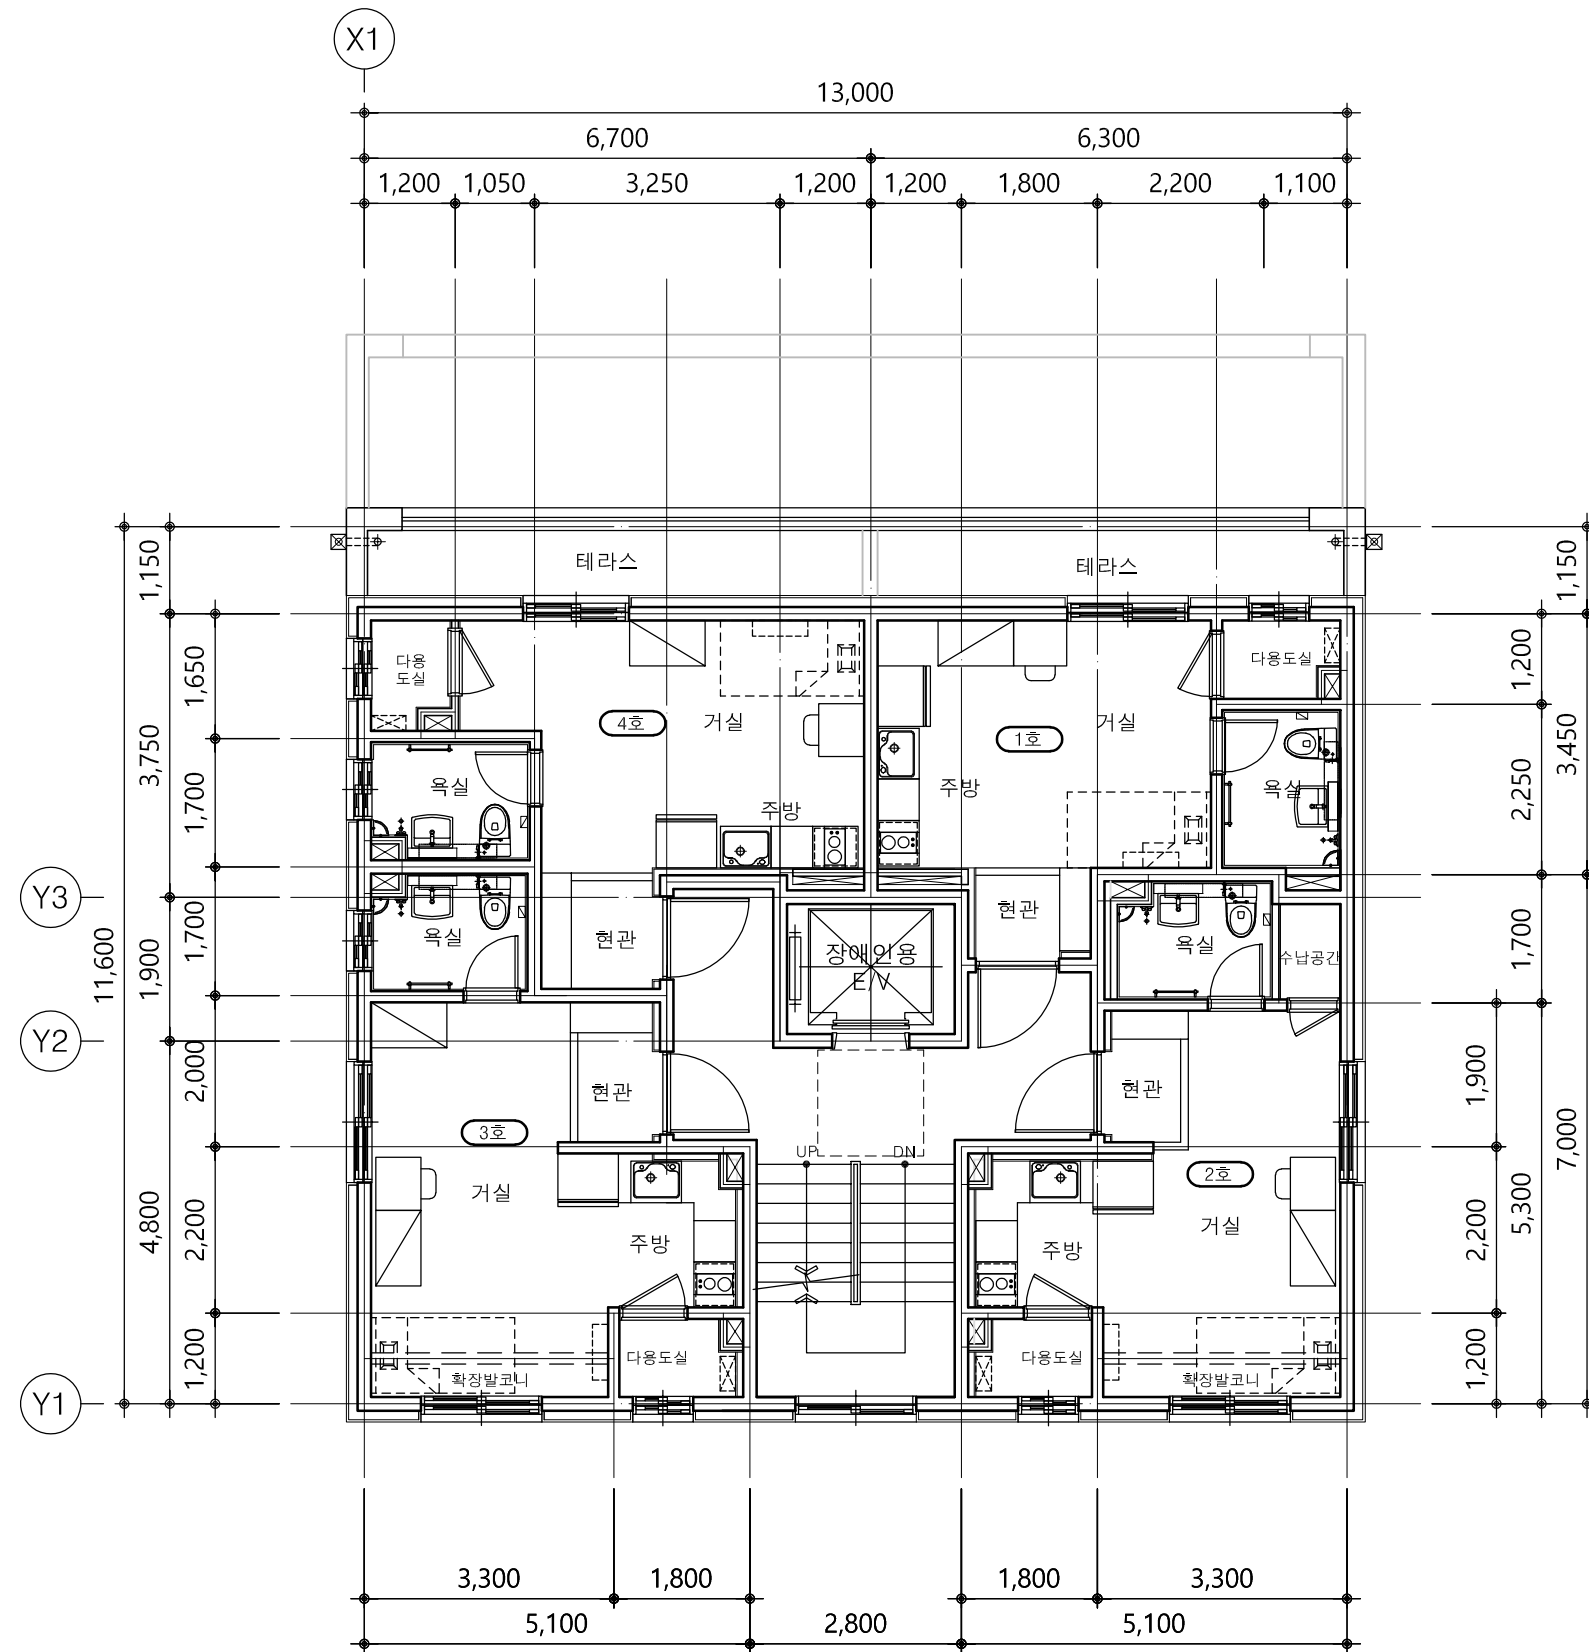

5 층 평면도

축척 : 1 / 100

PROJECT TITLE

문정동 13-7
도시형생활주택
신축공사

매매계약

jk

제이케이건축사사무소(주)
Architects & Planners
TEL : 02-533-9431 FAX : 02-532-9431

NOTE

1.콘크리트: fck = 24 MPa
2. 철근 : fy = 400 MPa
3. 세대내벽두께:150mm(복배근)
4. 외벽두께:180mm(복배근)
5. 코아벽두께:180mm(복배근)
6. 세대간벽두께:180mm(복배근)
7. 슬라브두께:210mm(3~5층)
8. 슬라브두께:180mm(2층,지붕)

설 계 변 경
DESCRIPTION OF REVISION

번 호	내 용
일 자	설 계 경 토 심 사 승 인
△	2021.06

승인 APPROVED BY


축척
SCALE

A1	1 /
A3	1 / 100

도면명 DRAWING TITLE

5 층 평면도

도면번호 DRAWING NO.
A - 204

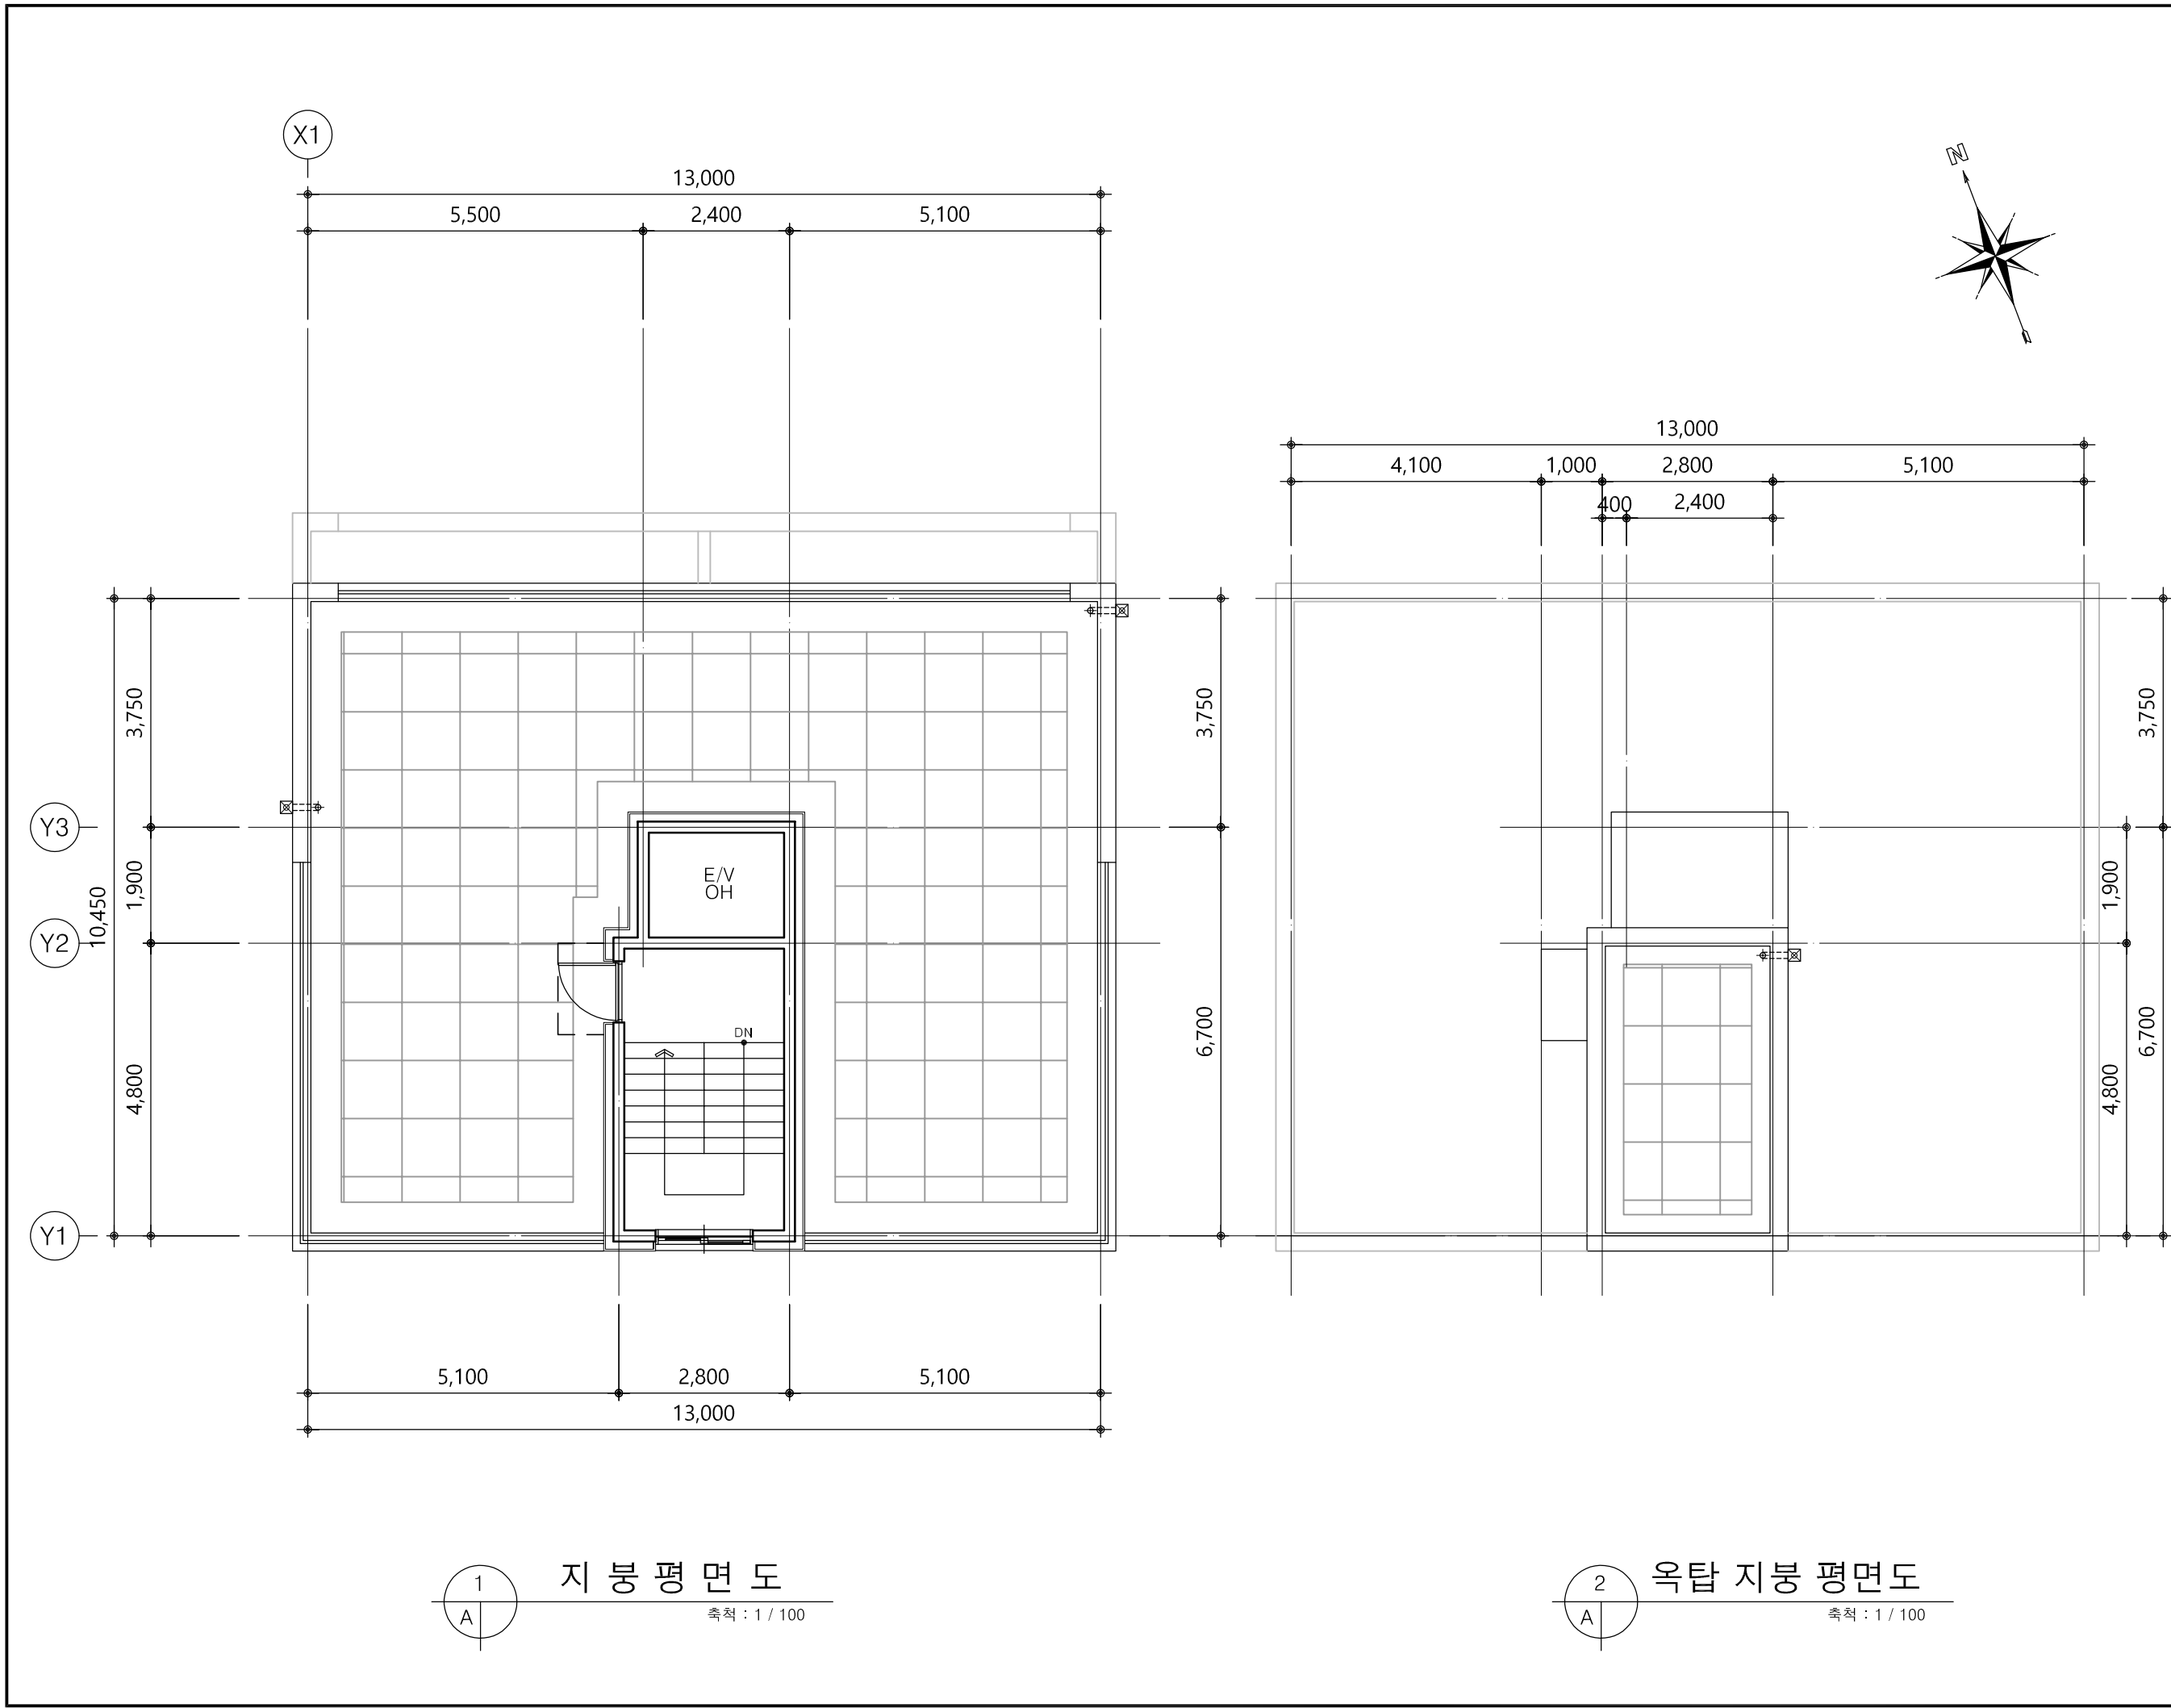

1 지붕 평면도
축척 : 1 / 100

2 옥탑 지붕 평면도
축척 : 1 / 100

PROJECT TITLE



문정동 13-7
도시형생활주택
신축공사

매매계약

jk
제이케이건축사사무소(주)
Architects & Planners
TEL : 02-533-9431 FAX : 02-532-9431

- NOTE
- 1. 콘크리트: fck = 24 MPa
 - 2. 철근 : fy = 400 MPa
 - 3. 세대내벽두께: 150mm(복배근)
 - 4. 외벽두께: 180mm(복배근)
 - 5. 코아벽두께: 180mm(복배근)
 - 6. 세대간벽두께: 180mm(복배근)
 - 7. 슬라브두께: 210mm(3~5층)
 - 8. 슬라브두께: 180mm(2층, 지붕)

설 계 변 경 DESCRIPTION OF REVISION				
번 호	내 용			
일 자	설 계	검 토	심 사	승 인
	2021.06			
승인 APPROVED BY				
축 척 SCALE	A1	1 /		
	A3	1 / 100		
도면명 DRAWING TITLE				
지붕,옥탑지붕평면도				
도면번호 DRAWING NO.				
A - 205				

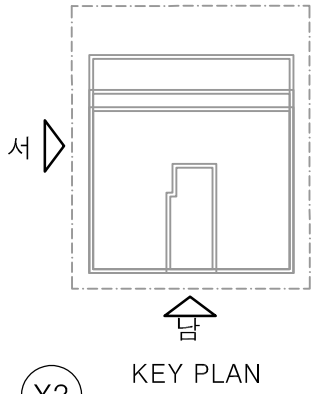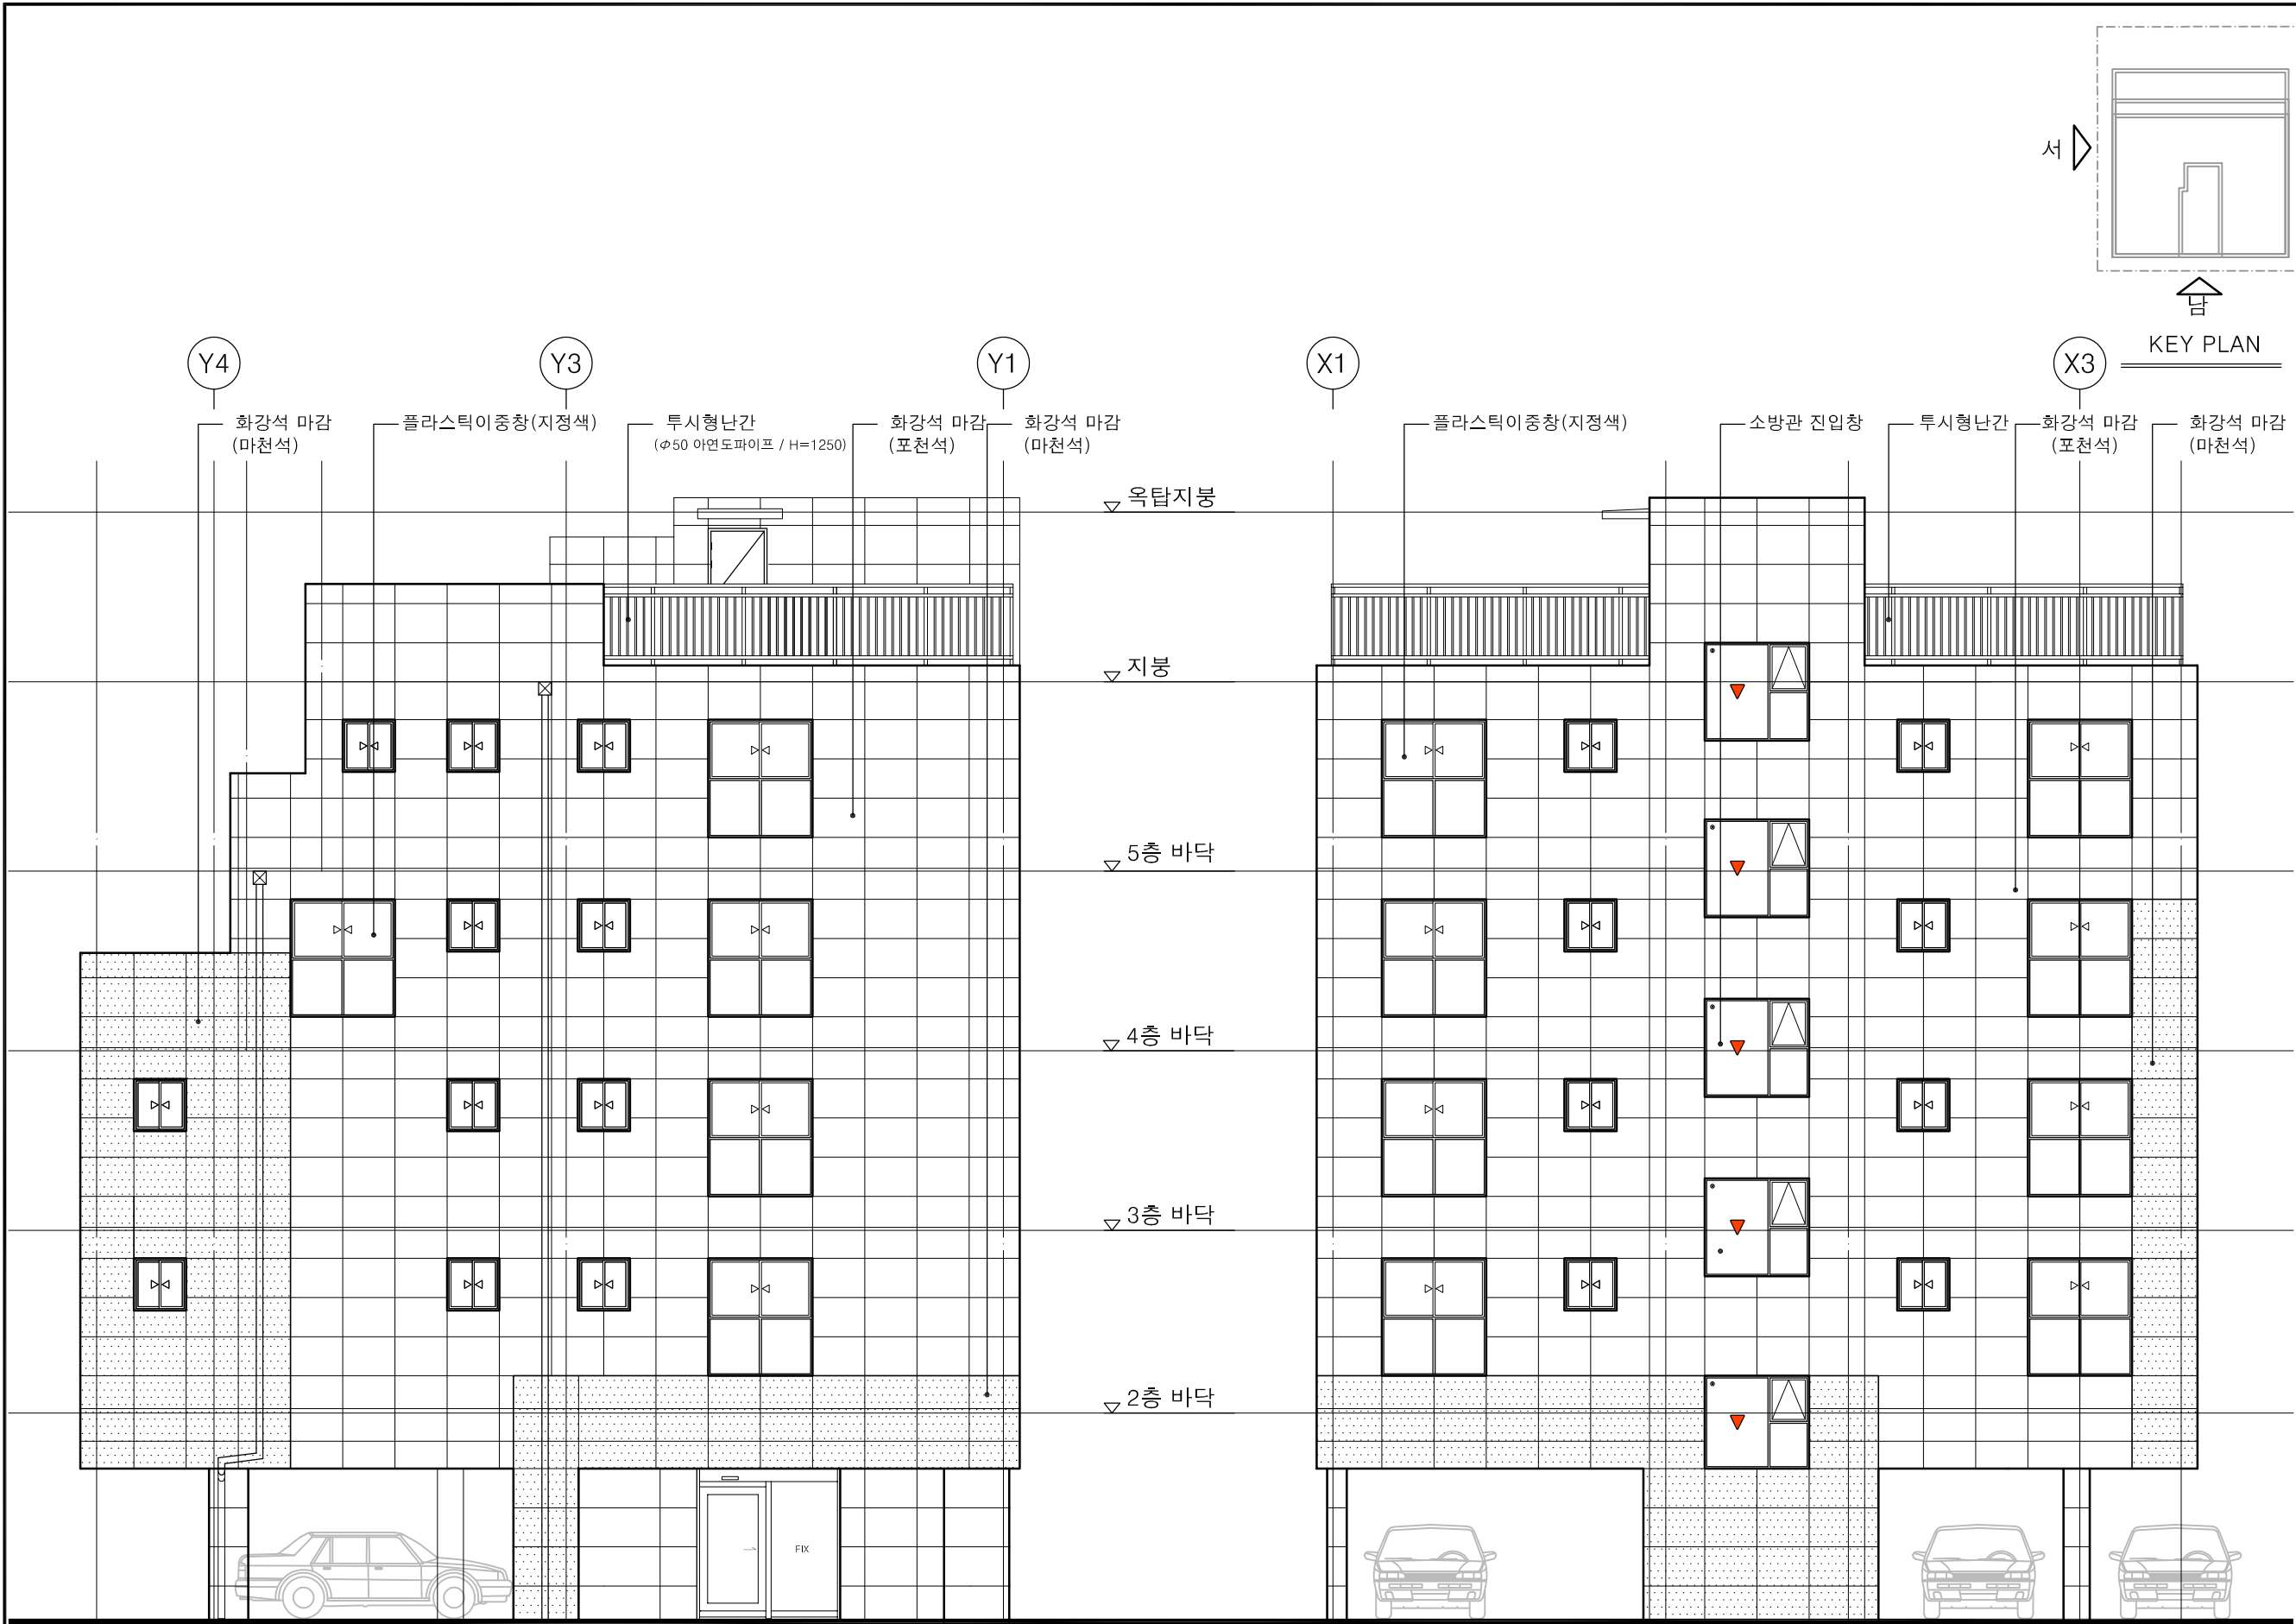

PROJECT TITLE


문정동 13-7
도시형생활주택
신축공사

매매계약

jk
제이케이건축사사무소(주)
Architects & Planners
TEL : 02-533-9431 FAX : 02-532-9431

NOTE

설 계 변 경 DESCRIPTION OF REVISION				
번 호	내 용			
일 자	설 계	감 토	심 사	승 인
	2021.06			
승인 APPROVED BY				
축 척 SCALE	A1	1 /		
	A3	1 / 100		
도면명 DRAWING TITLE				
서측면도,남측면도				
도면번호 DRAWING NO.				
A - 301				

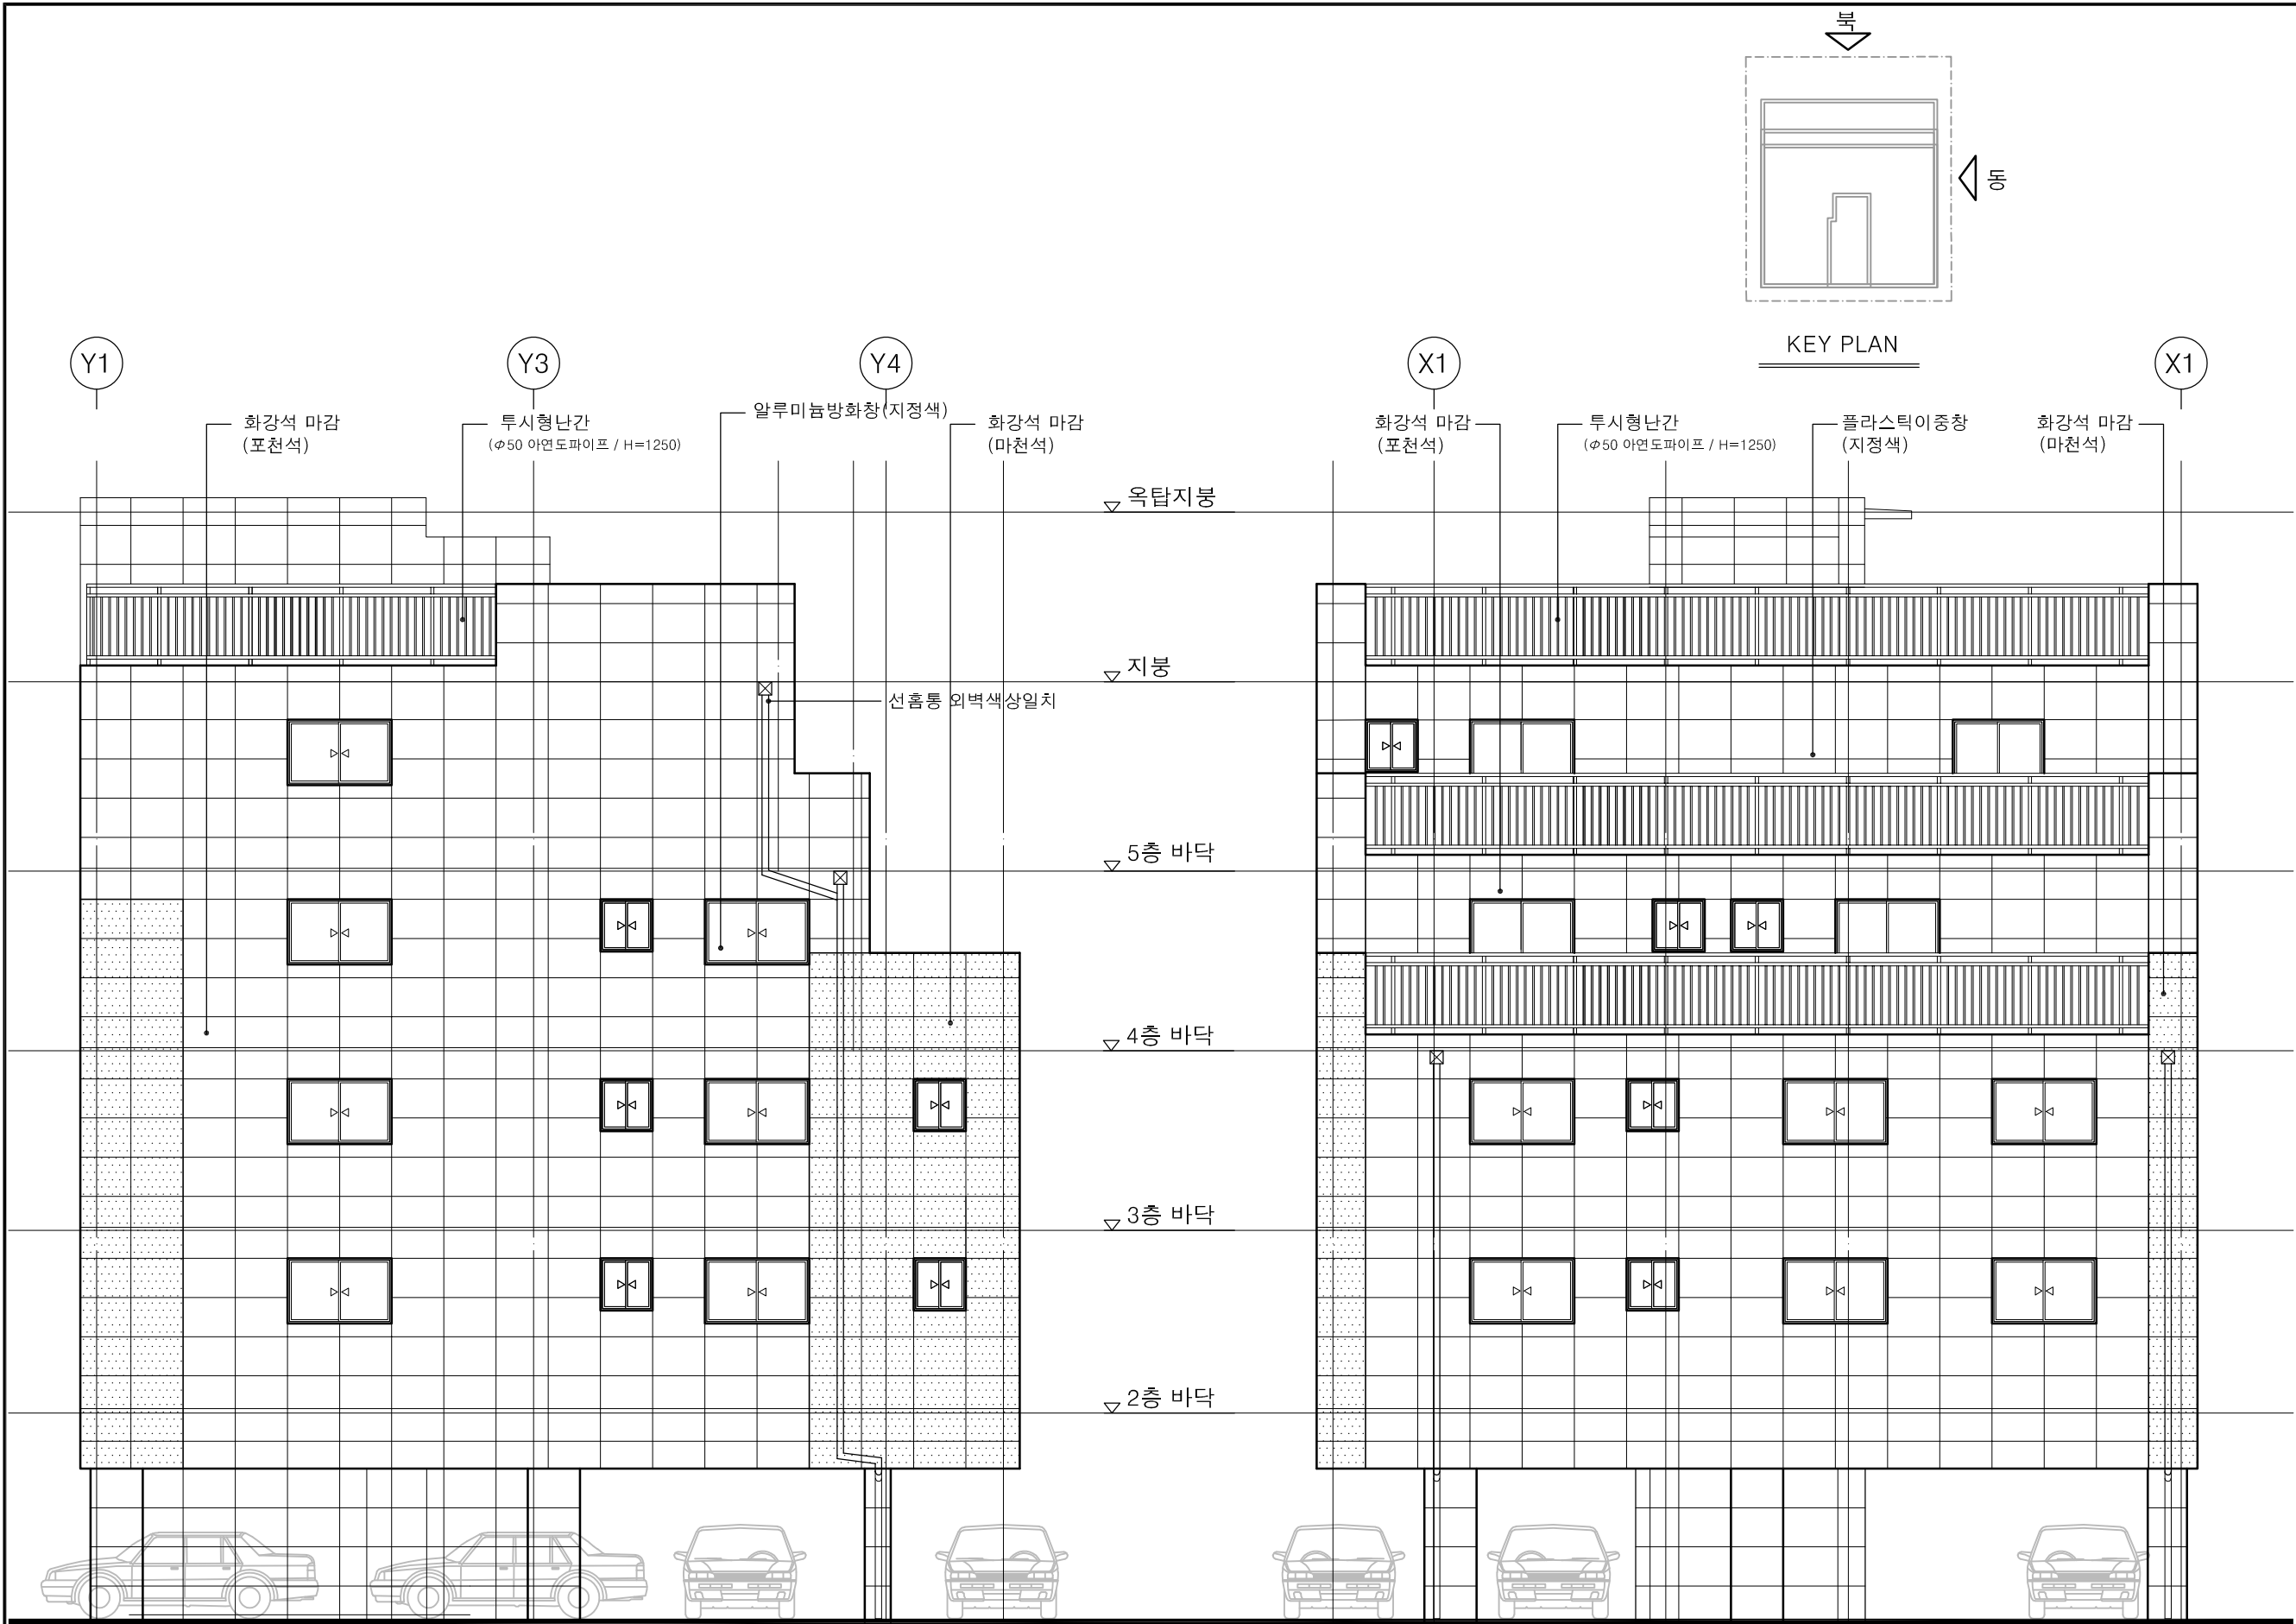

1 동측면도
축척 : 1 / 100

2 북측면도
축척 : 1 / 100

NOTE

설 계 변 경 DESCRIPTION OF REVISION				
번 호	내 용			
일 자	설 계	검 토	심 사	승 인
	2021.06			
승인 APPROVED BY				
축 척 SCALE	A1	1 /		
	A3	1 / 100		
도면명 DRAWING TITLE				
동측면도,북측면도				
도면번호 DRAWING NO.				
A - 302				