
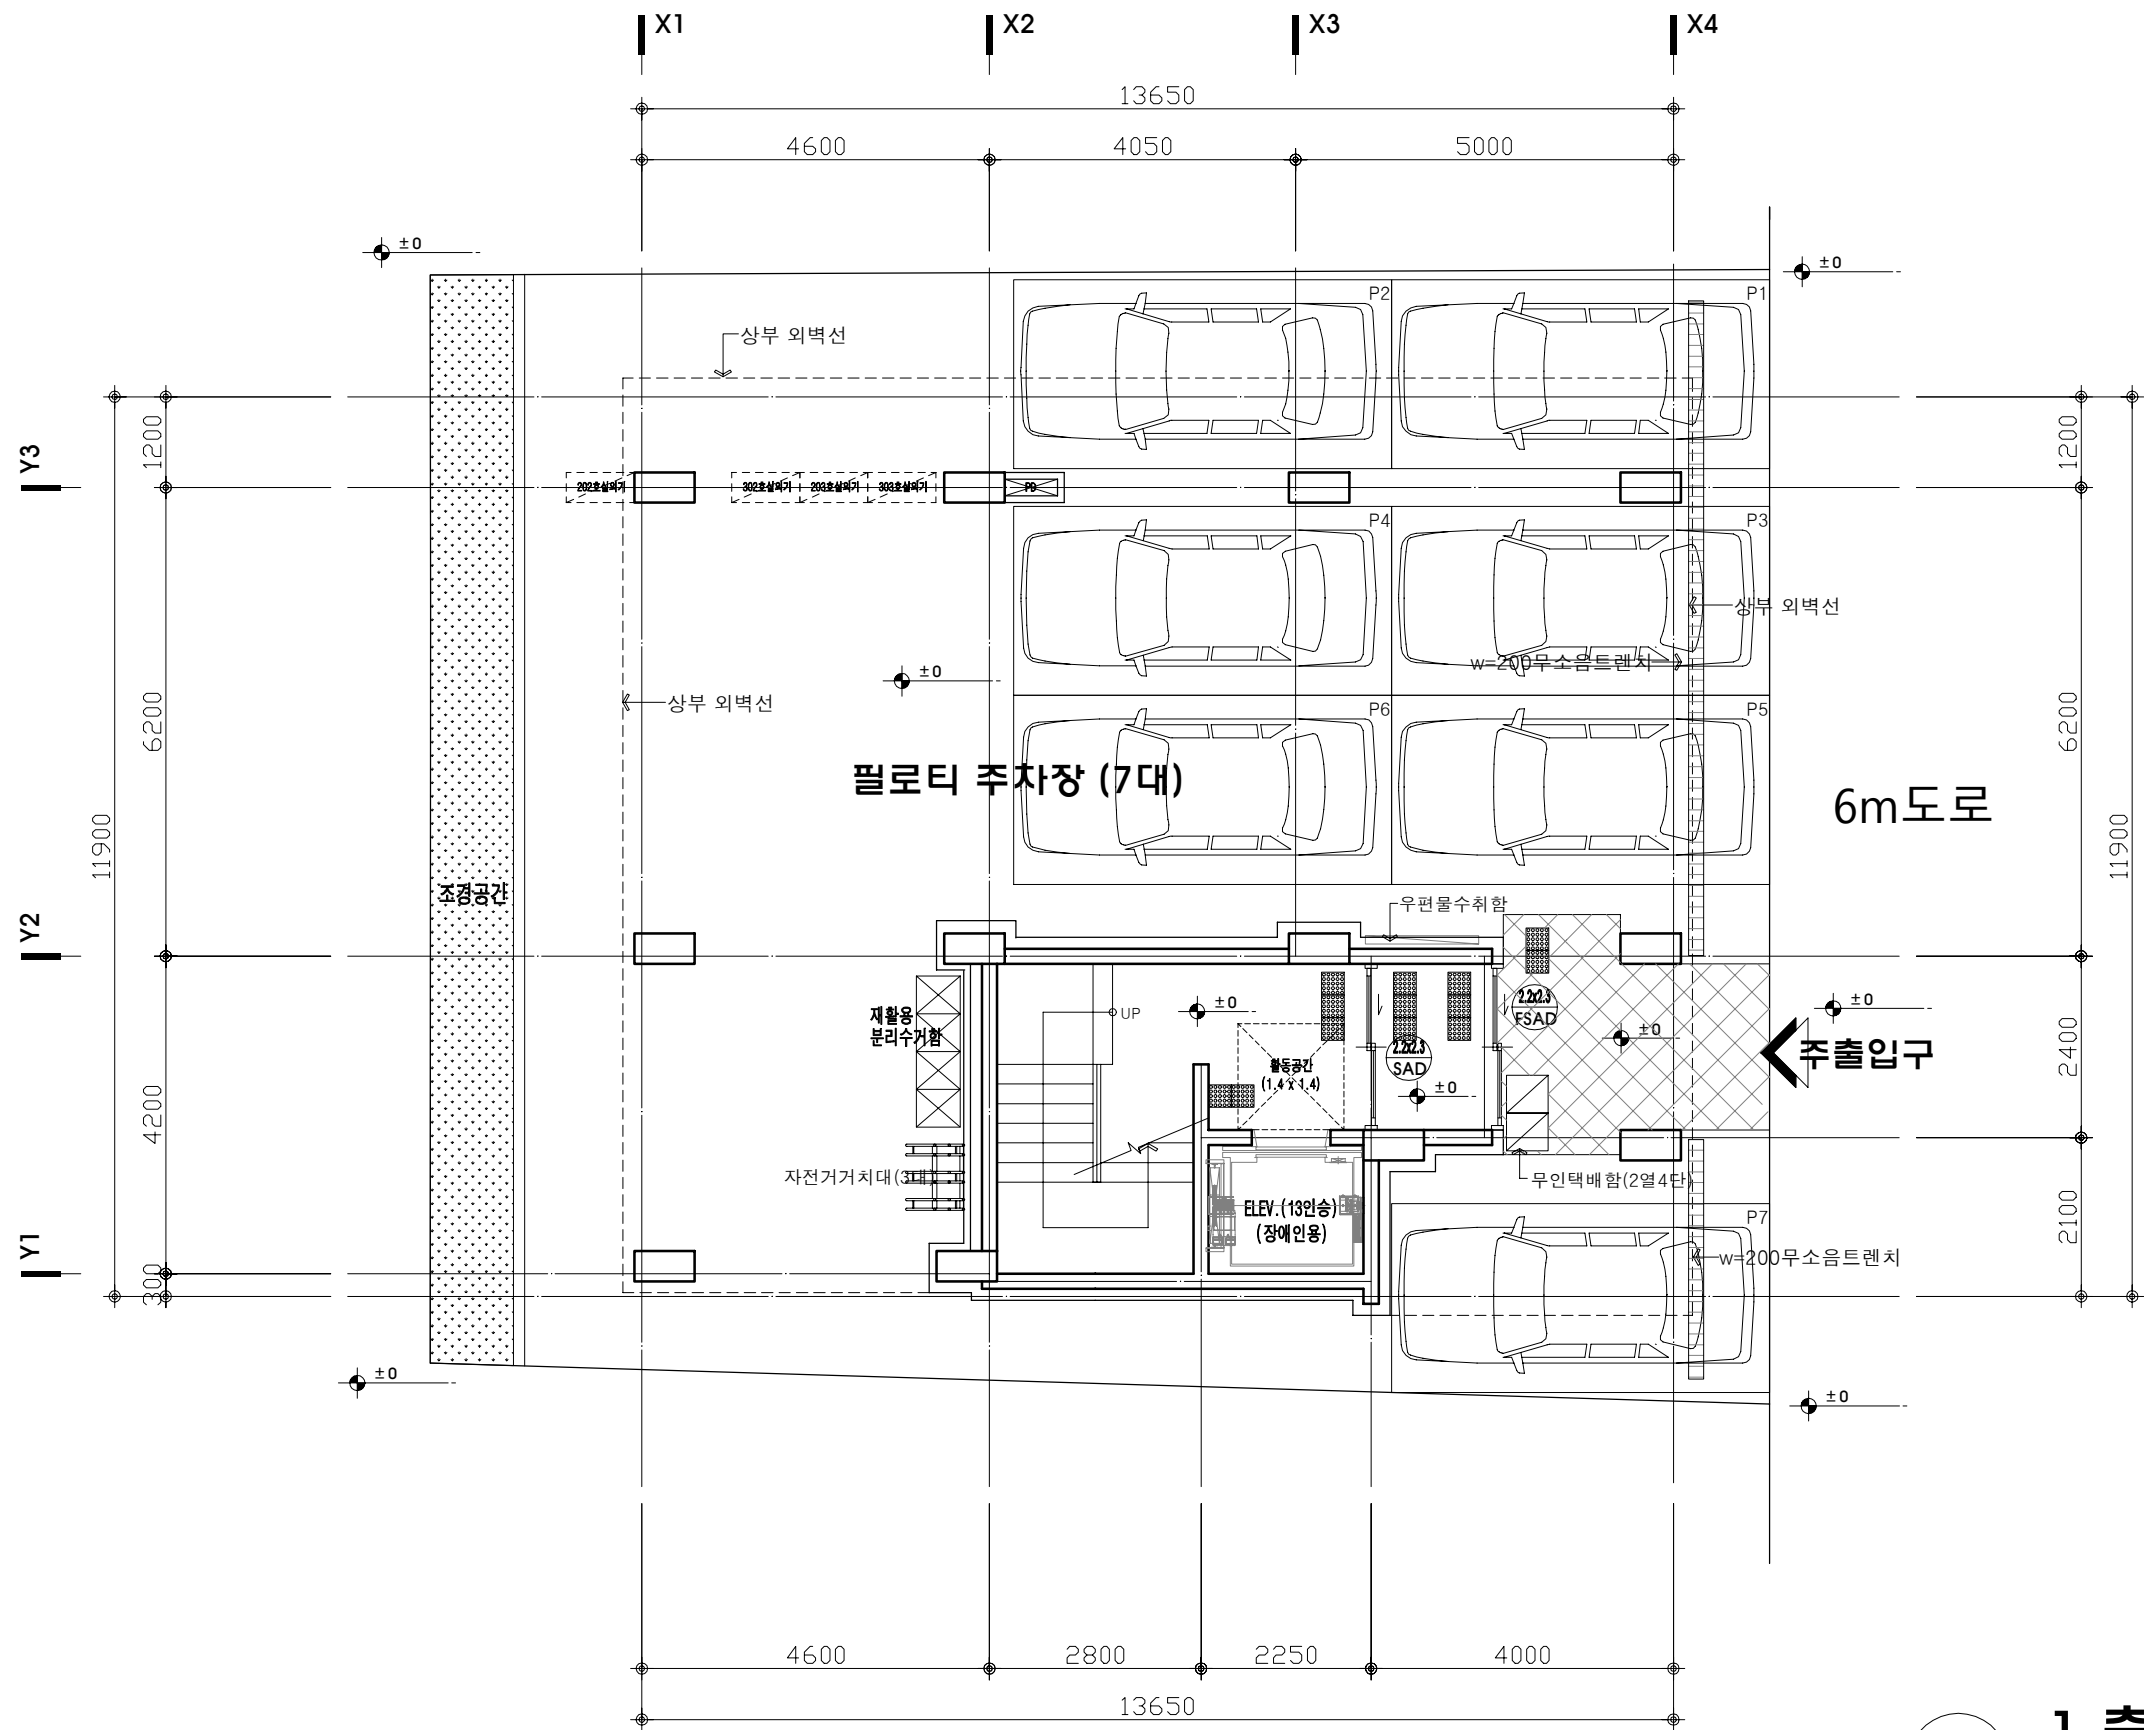
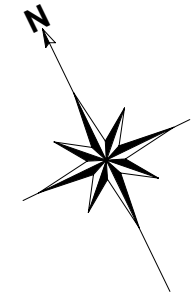
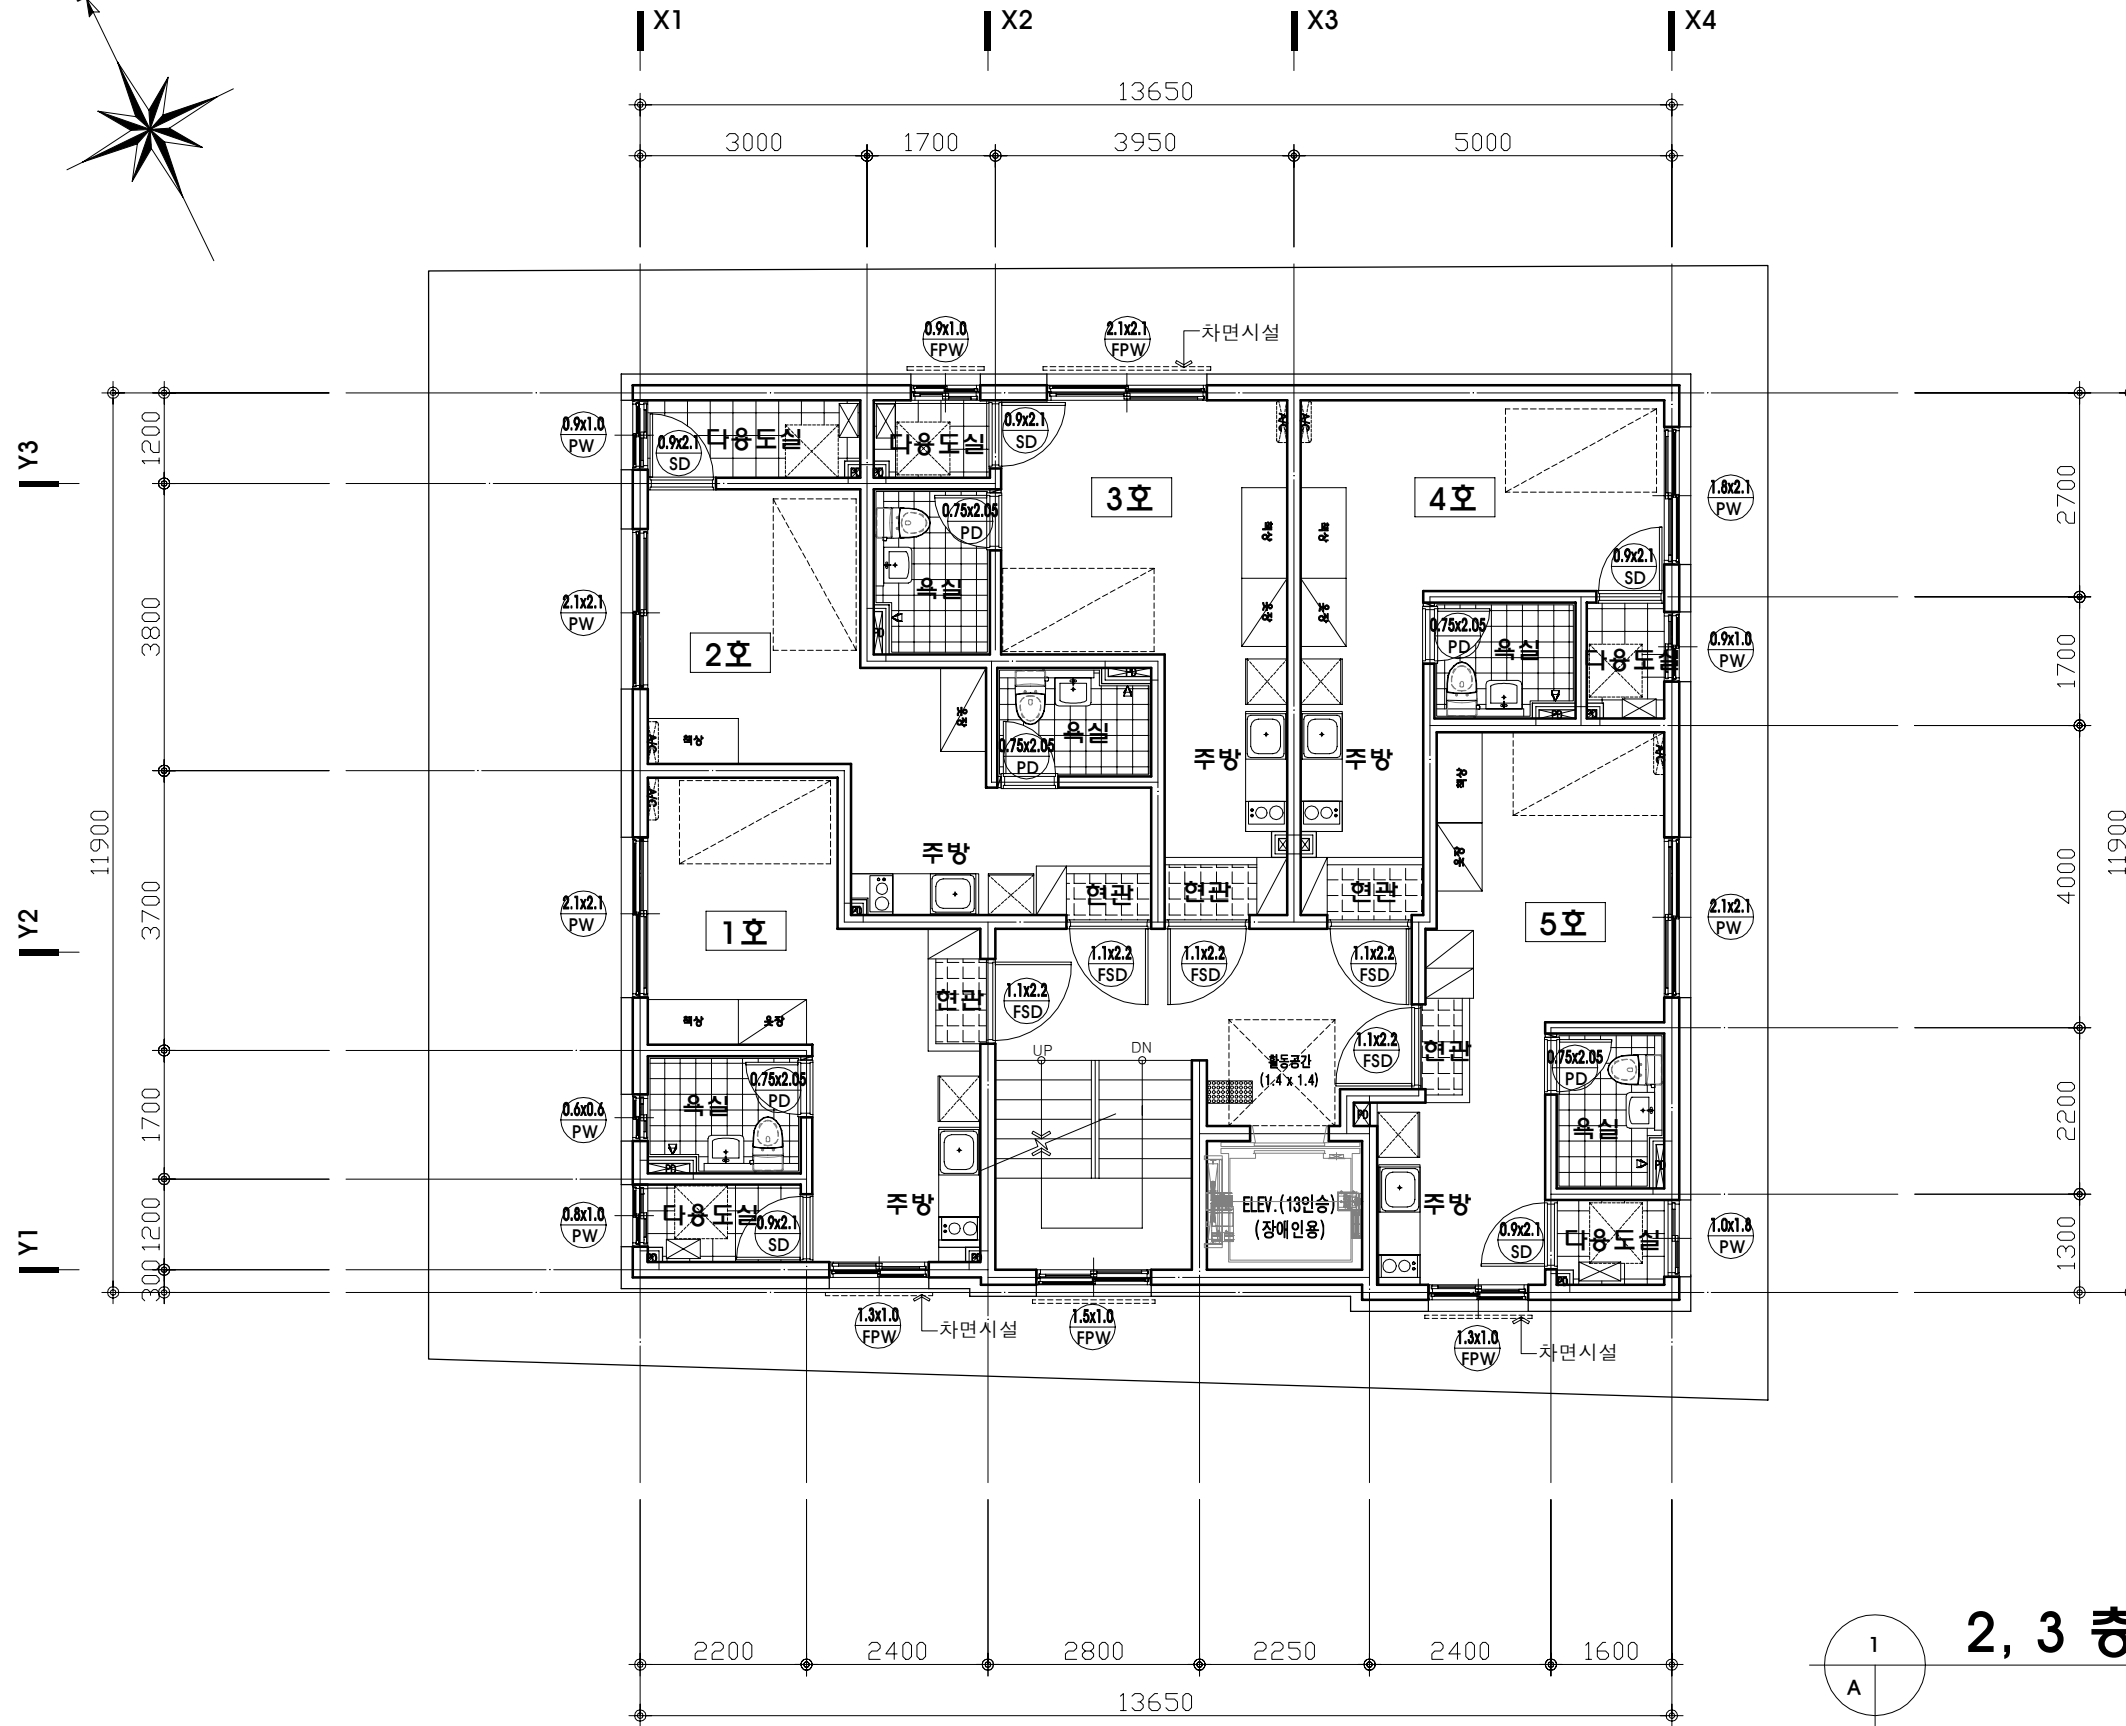




1 층 평 면 도

SCALE : 1/100

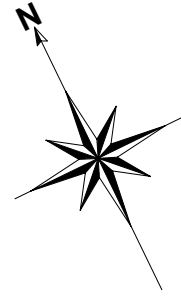

2, 3 층 평 면 도
SCALE : 1/100

PROJECT TITLE 사 업 명 칭 (종남동 408-10)
종남동 도시형생활주택 신축 공사
NAME OF DRAWING 도 면 명
2, 3 층 평 면 도
NOTE 주 기
청년주택
빌트인가전가구
(냉장고, 세탁기,
벽걸이에어컨,불박이장,책상)
☒ 보일러
벽걸이에어컨
에어컨 실외기
차면시설
1.콘크리트: fck = 24 MPa
2. 철근 : fy = 400 MPa
3. 세대간벽두께:180mm(복배근)
4. 외벽두께:200mm(복배근)
5. 코아벽두께:180mm(복배근)
6. 스라브두께:210mm(복배근)
(최상층은180mm)
7.욕실,다용도실-50슬라브다운
DATE 일 자
REVISIONS 수 정
NO.
DESIGNED BY 설 계
CHECKED BY 심 사
APPROVED BY 승 인
CONSULTANTS 협 동 설 계
SCALE 축 척 1 / 100
DATE 일 자 2023 . 10
DWG NO. 도 면 번 호 A - 202
FILE NAME. 파 일 명
테크원 건축사사무소 TECHONE ARCHITECTS & ENGINEERS CO., LTD TEL. 02)482-2466(대) FAX. 02)488-2466

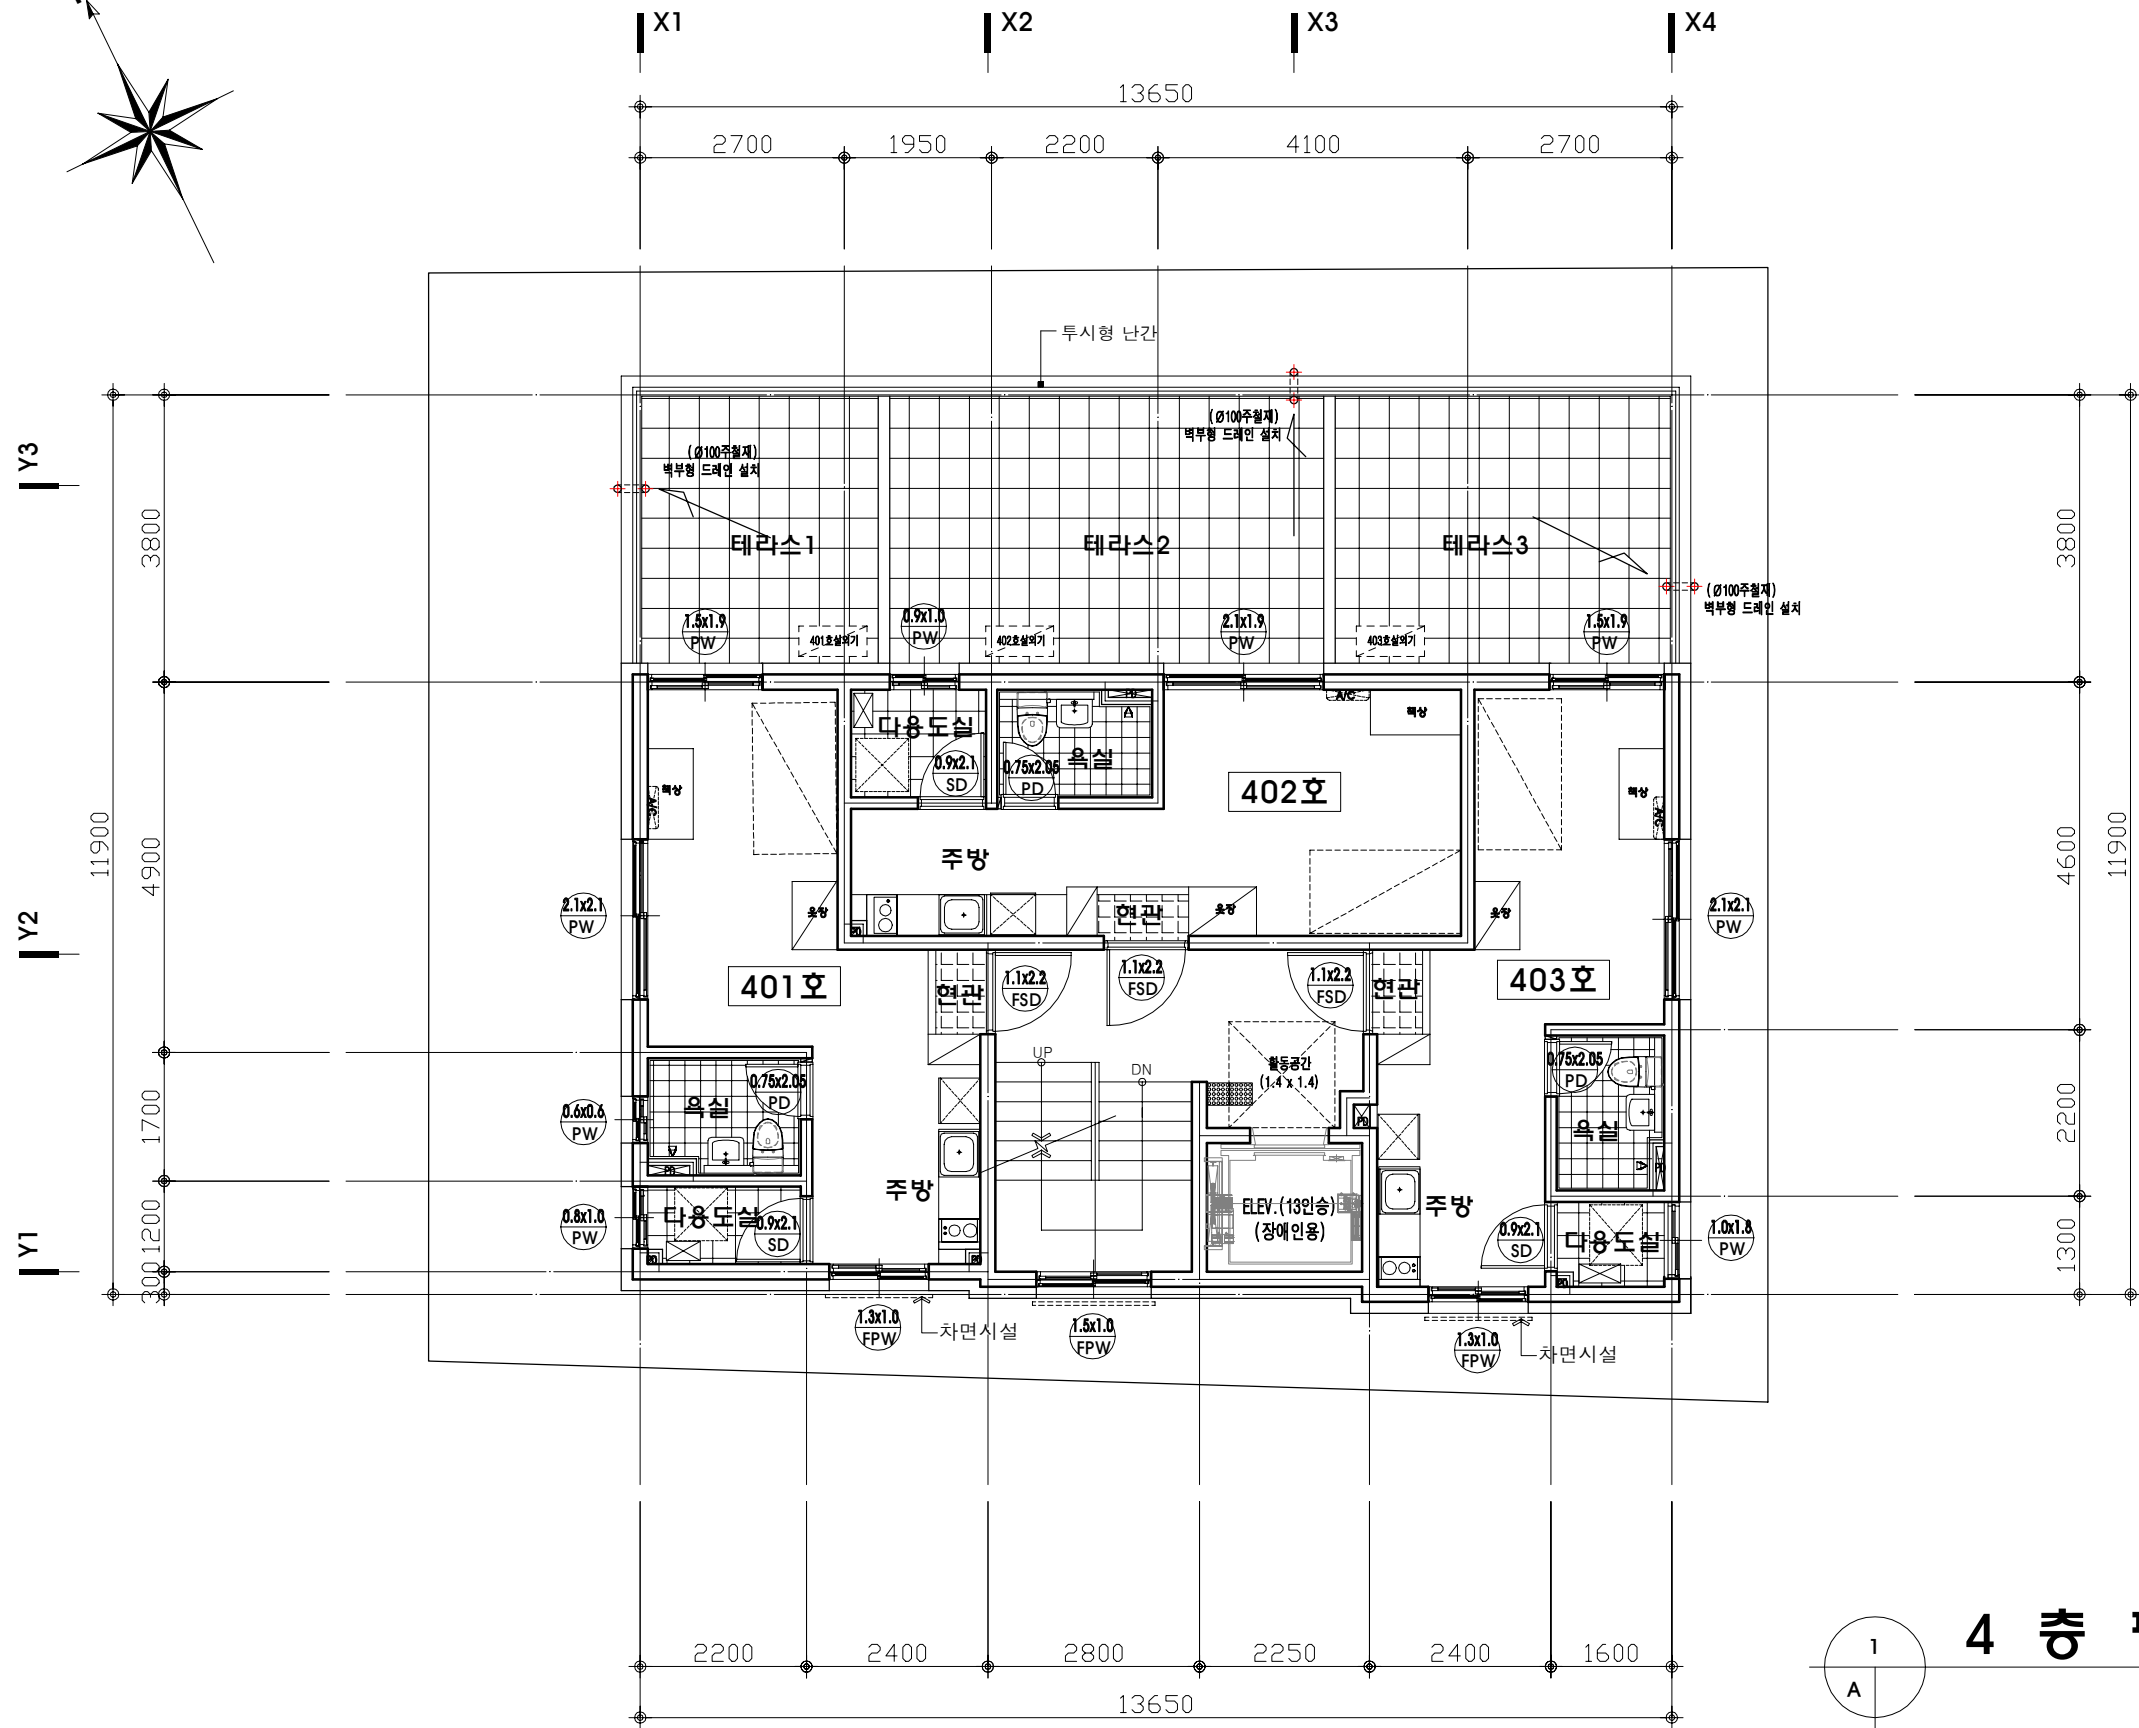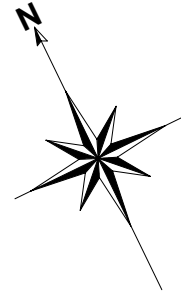

4 층 평면도
SCALE : 1/100

PROJECT TITLE
사 업 명
(종남동 408-10)

종남동 도시영생활주택
신축 공사

NAME OF DRAWING
도 면 명

4 층 평면도

NOTE
주 기

- ▼ ▼
- 청년주택
- 빌트인가전가구
- (냉장고, 세탁기,
- 벽걸이에어컨,불박이장,책상)
- ☒ 보일러
- 벽걸이에어컨
- 에어컨 실외기
- 차면시설

1. 콘크리트: fck = 24 MPa
2. 철근: fy = 400 MPa
3. 세대간벽두께: 180mm(복배근)
4. 외벽두께: 200mm(복배근)
5. 코아벽두께: 180mm(복배근)
6. 스라브두께: 210mm(복배근)
- (최상층은180mm)
7. 욕실, 다용도실-50슬라브다운

DATE
일 자

REVISIONS
수 정

NO.

DESIGNED BY
설 계

CHECKED BY
심 사

APPROVED BY
승 인

CONSULTANTS
협 동 설 계

SCALE
축 척

1 / 100

DATE
일 자

2023 . 10

DWG NO.
도 면 번 호



A - 203

FILE NAME.
화 일 명

TECH 1 테크원
건축사사무소

TECHONE ARCHITECTS & ENGINEERS
CO., LTD

TEL. 02)482-2466(대)
FAX. 02)488-2466

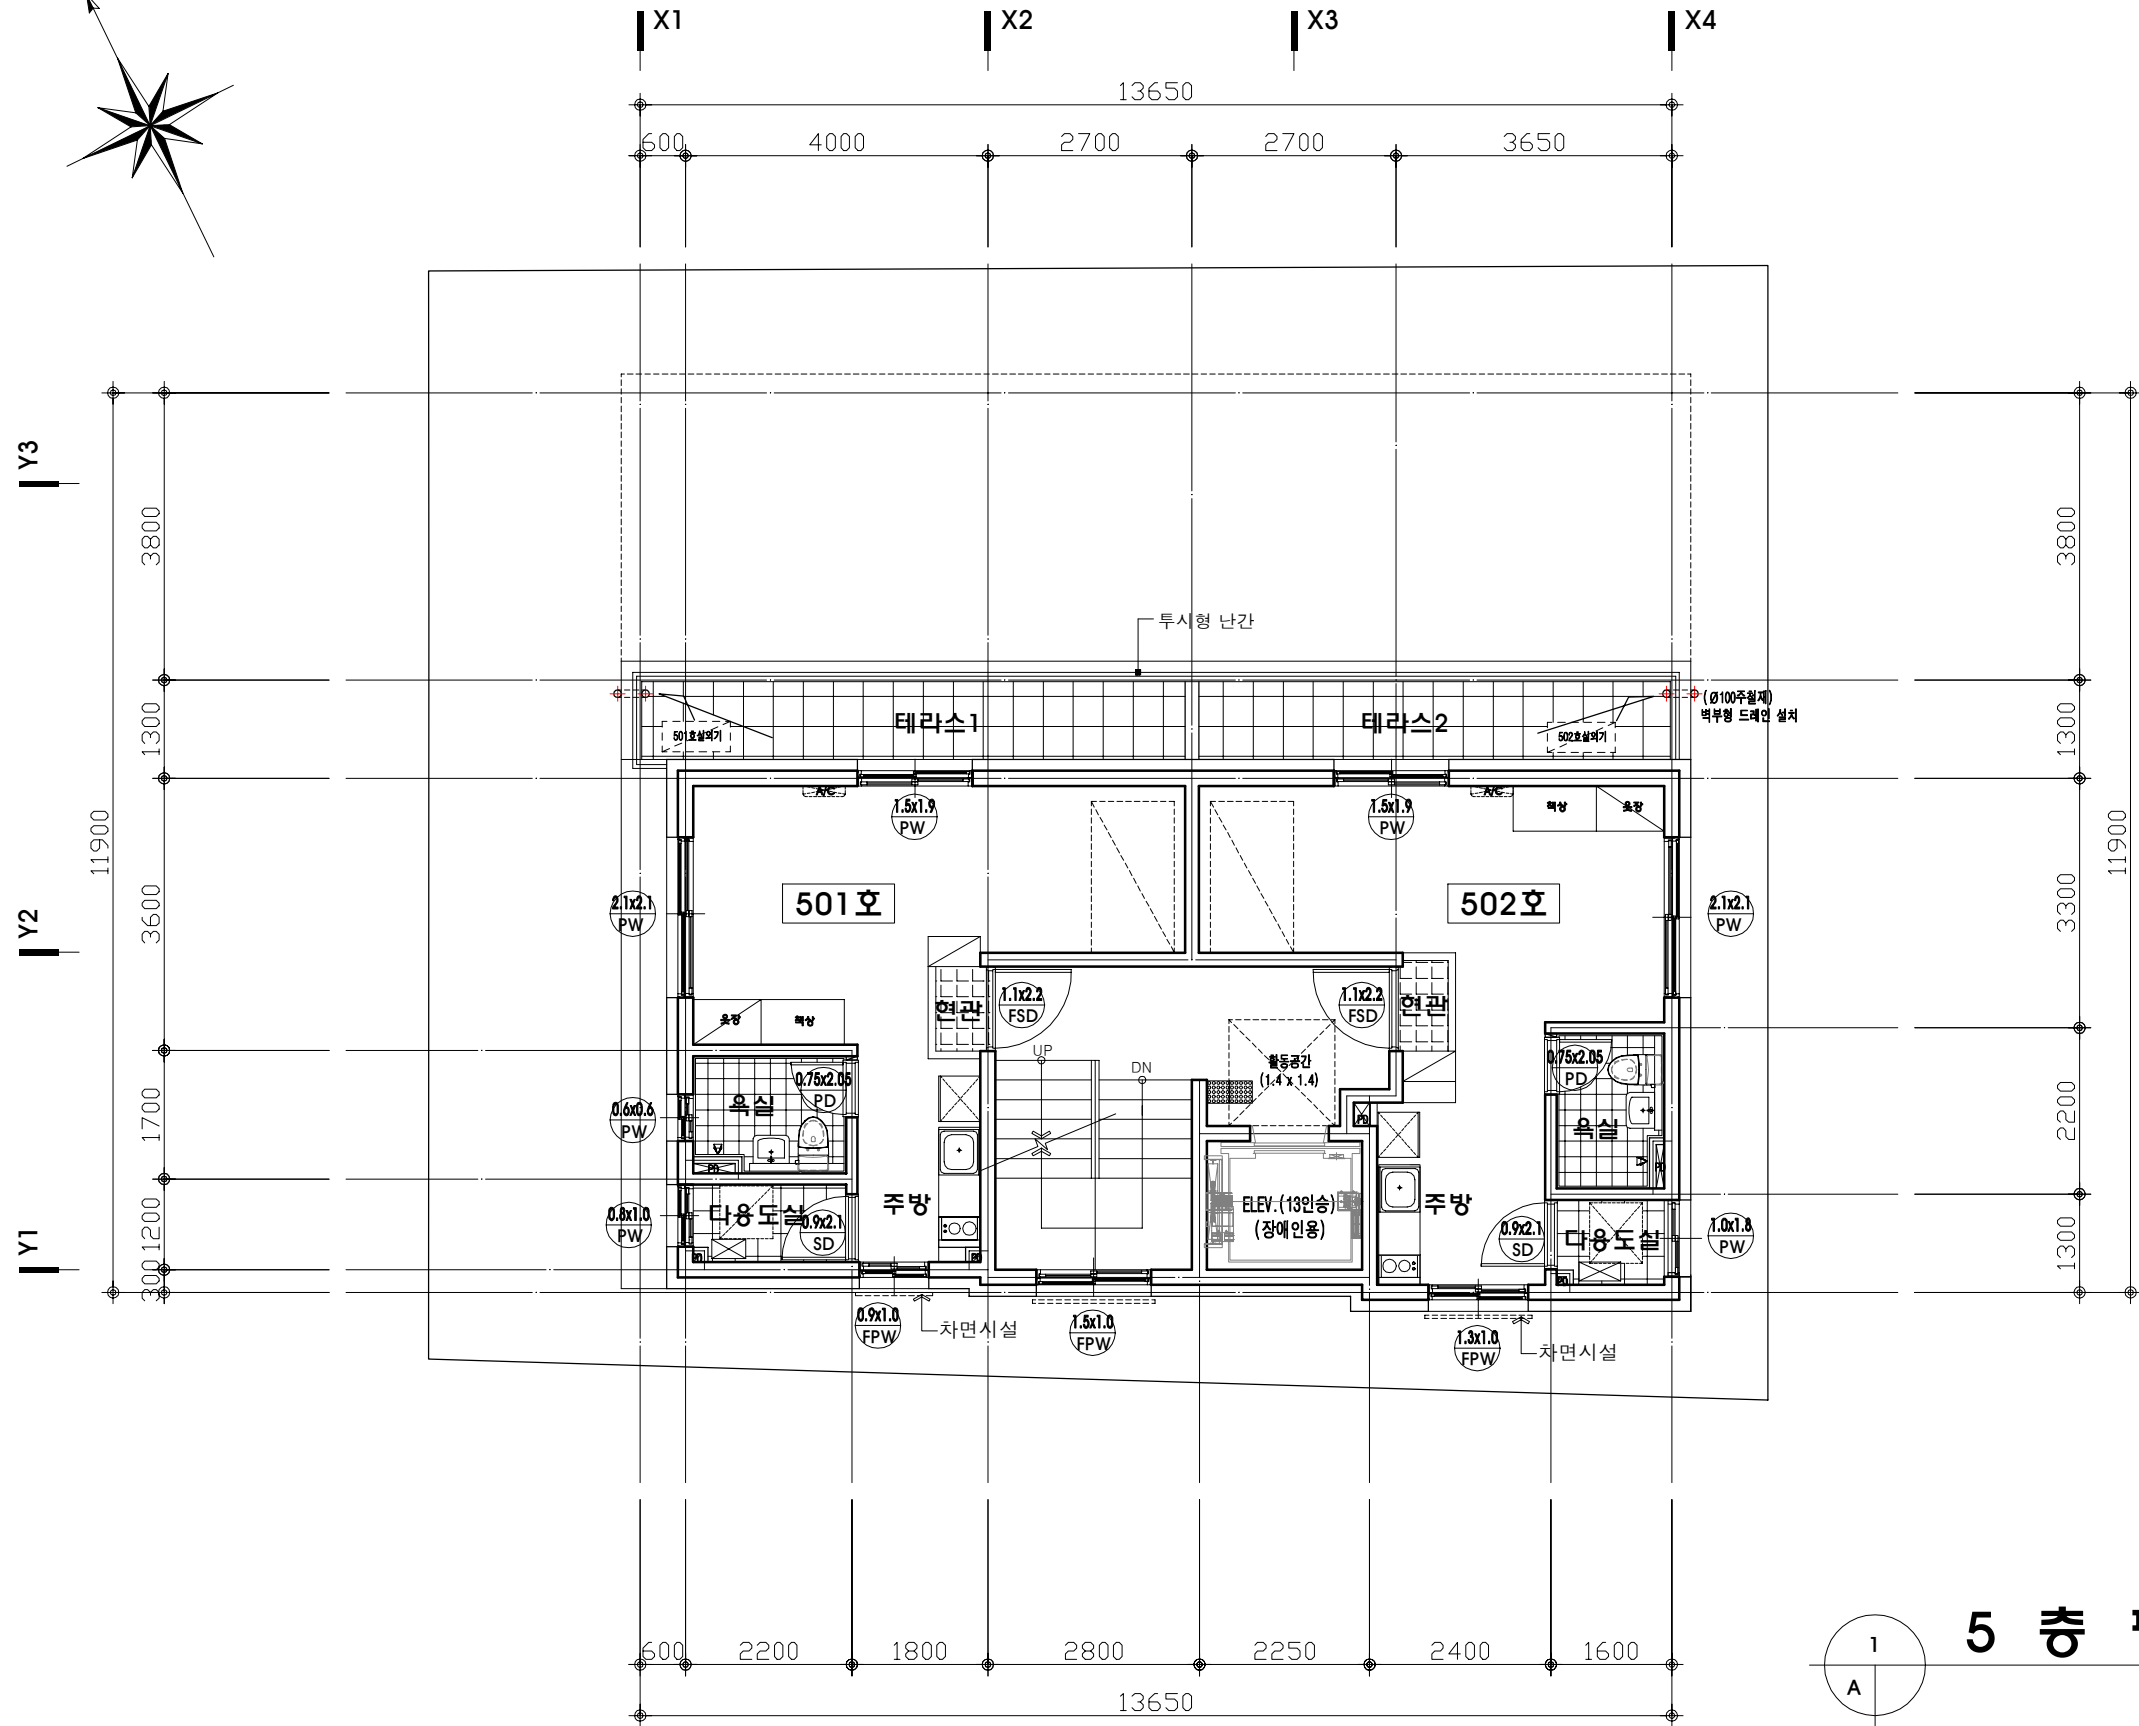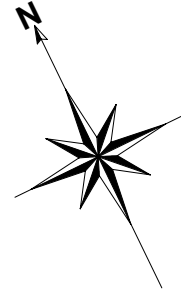

5 층 평면도
SCALE : 1/100

PROJECT TITLE
사 업 명
(종남동 408-10)

종남동 도시형생활주택
신축 공사

NAME OF DRAWING
도 면 명

5 층 평면도

NOTE
주 기

- ▼
- 청년주택
- 빌트인가전가구
- (냉장고, 세탁기,
- 벽걸이에어컨,불박이장,책상)
- ☒ 보일러
- 벽걸이에어컨
- 에어컨 실외기
- 차면시설
- 1.콘크리트: fck = 24 MPa
2. 철근 : fy = 400 MPa
3. 세대간벽두께:180mm(복배근)
4. 외벽두께:200mm(복배근)
5. 코아벽두께:180mm(복배근)
6. 스라브두께:210mm(복배근)
- (최상층은180mm)
- 7.욕실,다용도실-50슬라브다운

DATE
일 자

REVISIONS
수 정

NO.

DESIGNED BY
설 계

CHECKED BY
심 사

APPROVED BY
승 인

CONSULTANTS
협 동 설 계

SCALE
축 척

1 / 100

DATE
일 자

2023 . 10

DWG NO.
도 면 번 호



A - 204

FILE NAME.
화 일 명

TECH 1 테크원
건축사사무소

TECHONE ARCHITECTS & ENGINEERS
CO., LTD

TEL. 02)482-2466(대)
FAX. 02)488-2466

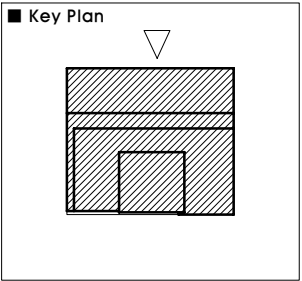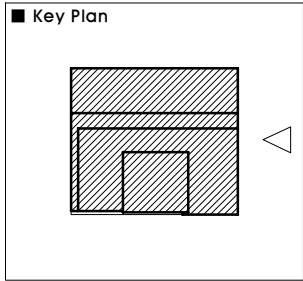

PROJECT TITLE
사 업 명 칭
(종남동 408-10)

종남동 도시영생활주택
신축 공사

NAME OF DRAWING
도 면 명

정면도, 우측면도

NOTE
주 기

▽외벽 석재 색상 조감도 참고.

DATE	REVISIONS	NO.
일 자	수 정	

DESIGNED BY
설 계

CHECKED BY
심 사

APPROVED BY
승 인

CONSULTANTS
협 동 설 계

SCALE
축 척 1 / 150

DATE
일 자 2023 . 10


DWG NO.
도 면 번 호 A - 301

FILE NAME
파 일 명

TECH 1 테크원
건축사사무소





TECHONE ARCHITECTS & ENGINEERS
CO., LTD

TEL. 02)482-2466(대)
FAX. 02)488-2466

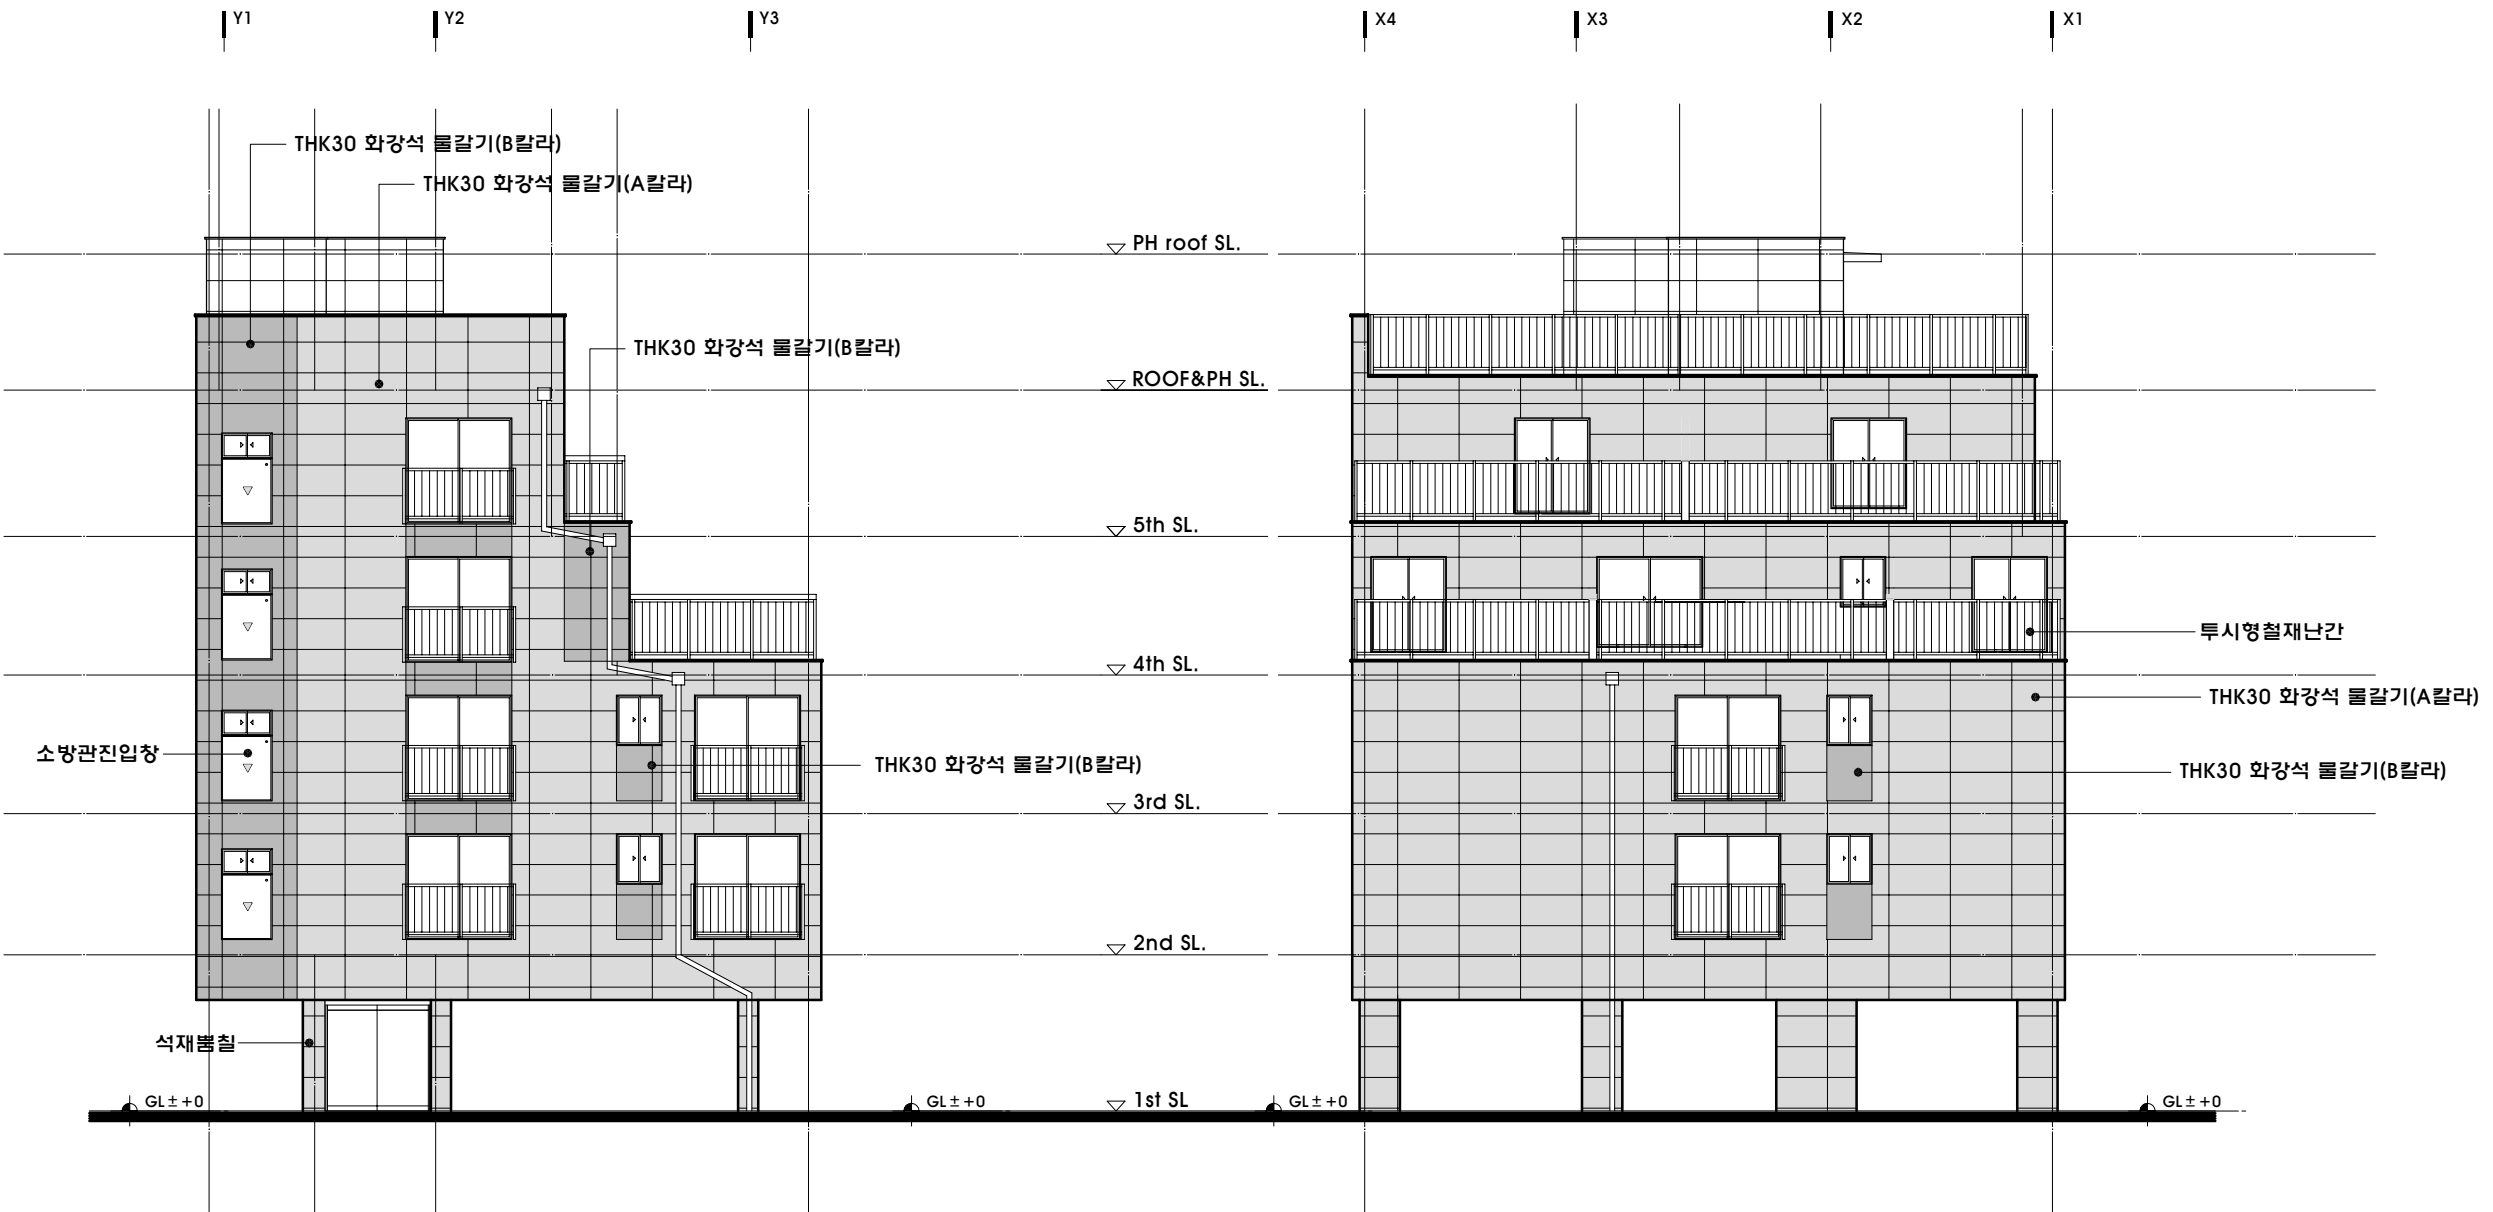


정 면 도 (동측)
SCALE : 1/150

우 측 면 도 (북측)
SCALE : 1/150

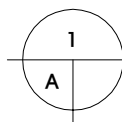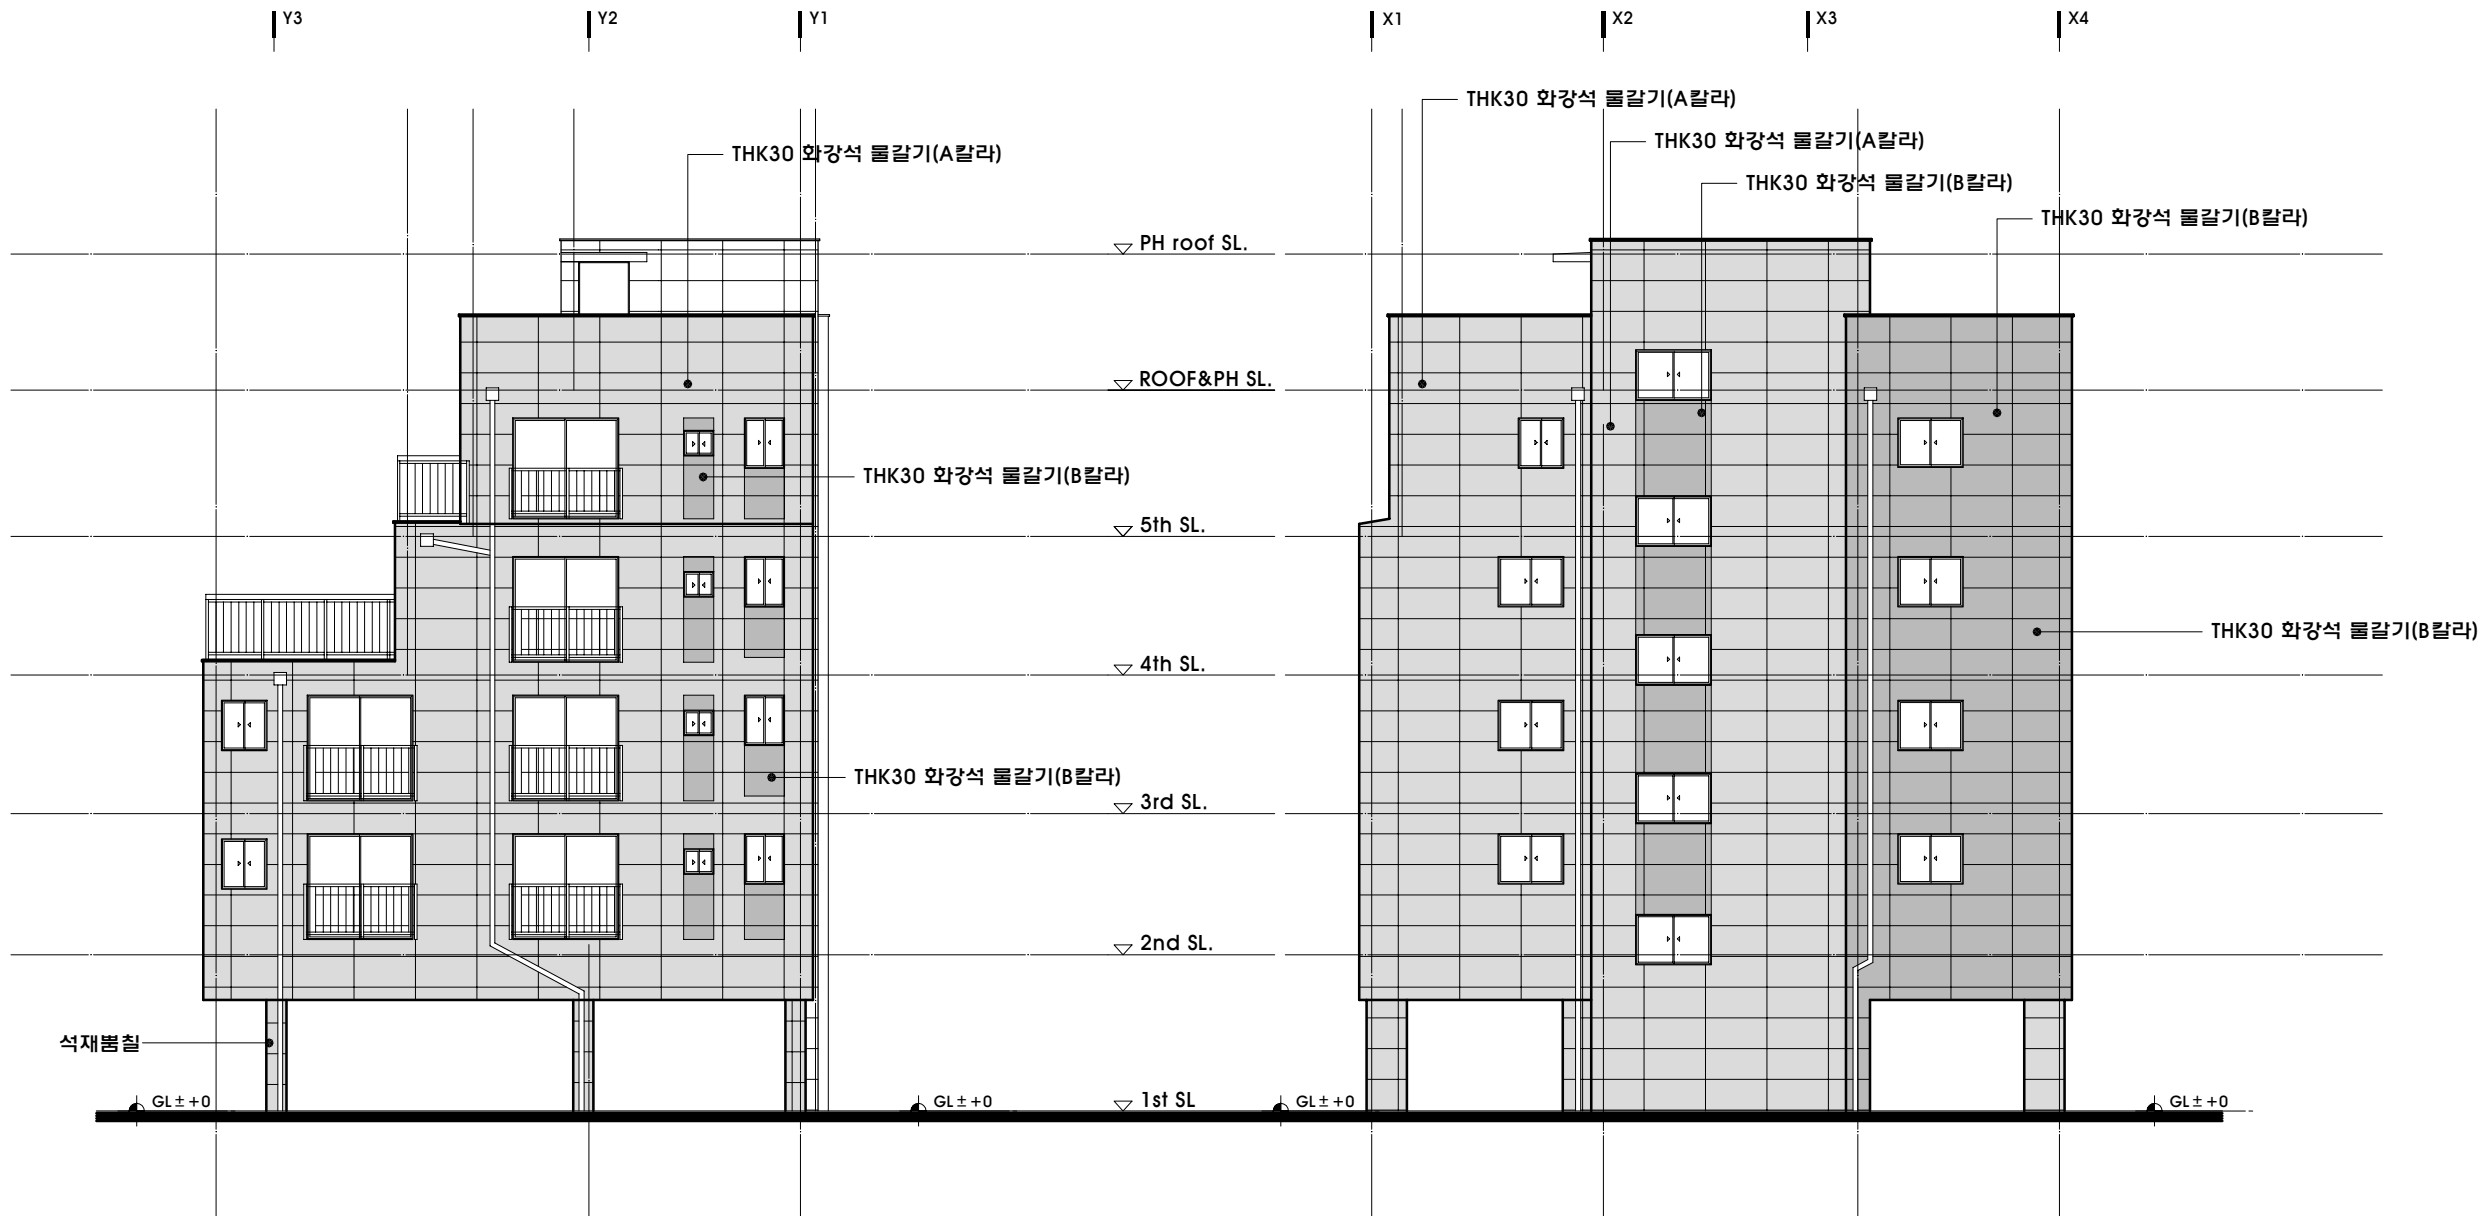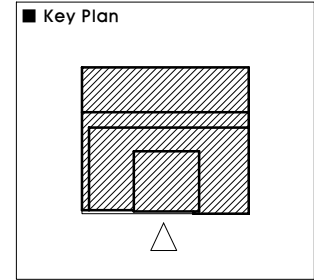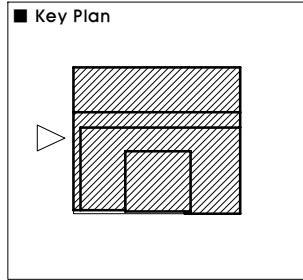

배면도 (서측)
SCALE : 1/150

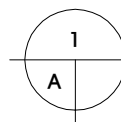

좌측면도 (남측)
SCALE : 1/150

PROJECT TITLE
사업명칭
(용남동 408-10)

용남동 도시영생활주택
신축 공사

NAME OF DRAWING
도면명

배면도, 좌측면도

NOTE
주 기

▽
▽
*외벽 석재 색상 조감도 참고.

DATE ▲ REVISIONS ▲ NO.
일 자 수 장

DESIGNED BY
설 계

CHECKED BY
심 사

APPROVED BY
승 인

CONSULTANTS
협 동 설 계

SCALE
축 척 1 / 150

DATE
일 자 2023 . 10

DWG NO.
도 면 번 호 A - 302

FILE NAME
파 일 명

TECH 1 테크원
건축사사무소

TECHONE ARCHITECTS & ENGINEERS
CO., LTD

TEL. 02)482-2466(대)
FAX. 02)488-2466