


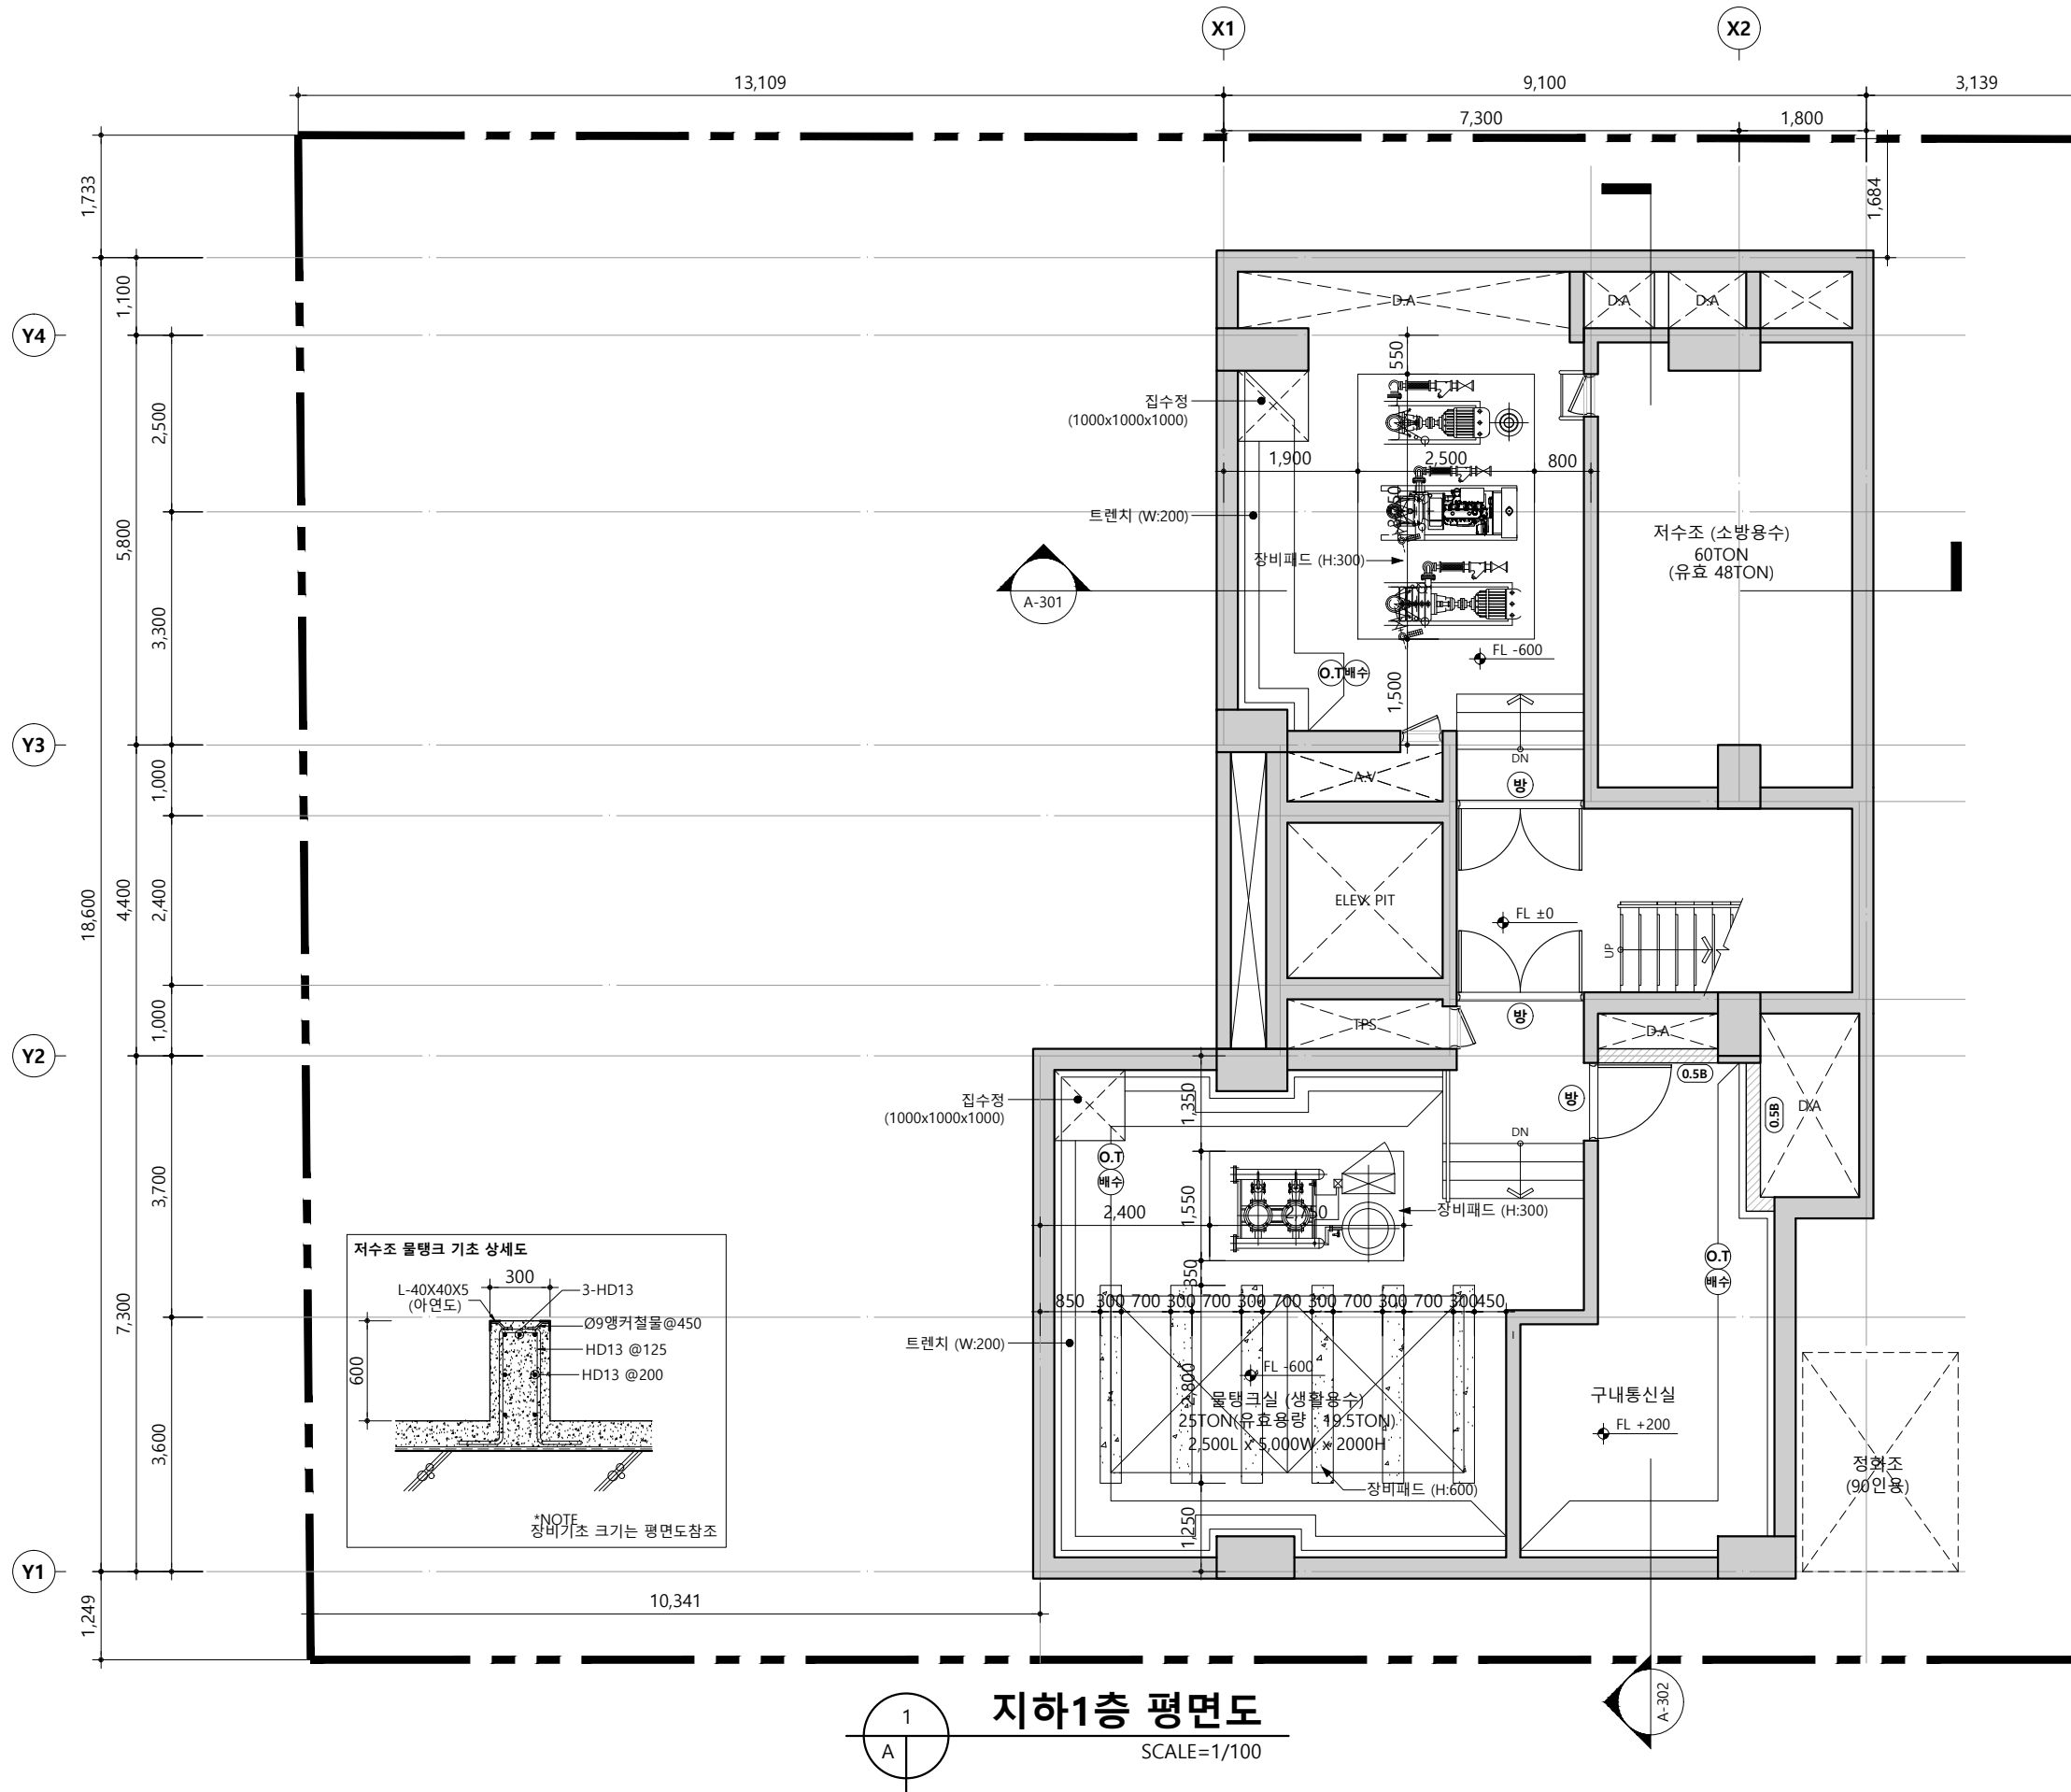

지하1층 평면도

SCALE=1/100

설계명
PROJECT TITLE
영등포구
대림동 740-2
오피스텔 신축공사

설계번호
PROJECT NO.

특기사항
NOTE

*범례

- (완) : 완강기 (3층 이상, 격층으로 설치)
- (배) : 배연창
- (방) : 방음방화문
- (재) : 재료분리대
- (0.5B) : 0.5B 시멘트벽돌
- (배수) : T60 벽체배수판
- (O.T) : OPEN 트랜치


변경사항
REVISION

제도
DRAWN BY
검토
CHECKED BY
설계
DESIGNED BY
승인
APPROVED BY 최익환

도면명
NAME OF DRAWING
지하1층 평면도
축척
SCALE
날짜
DATE
A1 1/100 2022. 06
A3 1/100 2022. 06

도면번호
DRAWING NO.
A-101
일련번호
SHEET NO.

SNA
(주)에스엔에이 건축사사무소
Space & Architecture Design Group
서울 송파구 법원로 128, C동 1017호
TEL. (02) 6071-3403 FAX. (02) 6213-3403

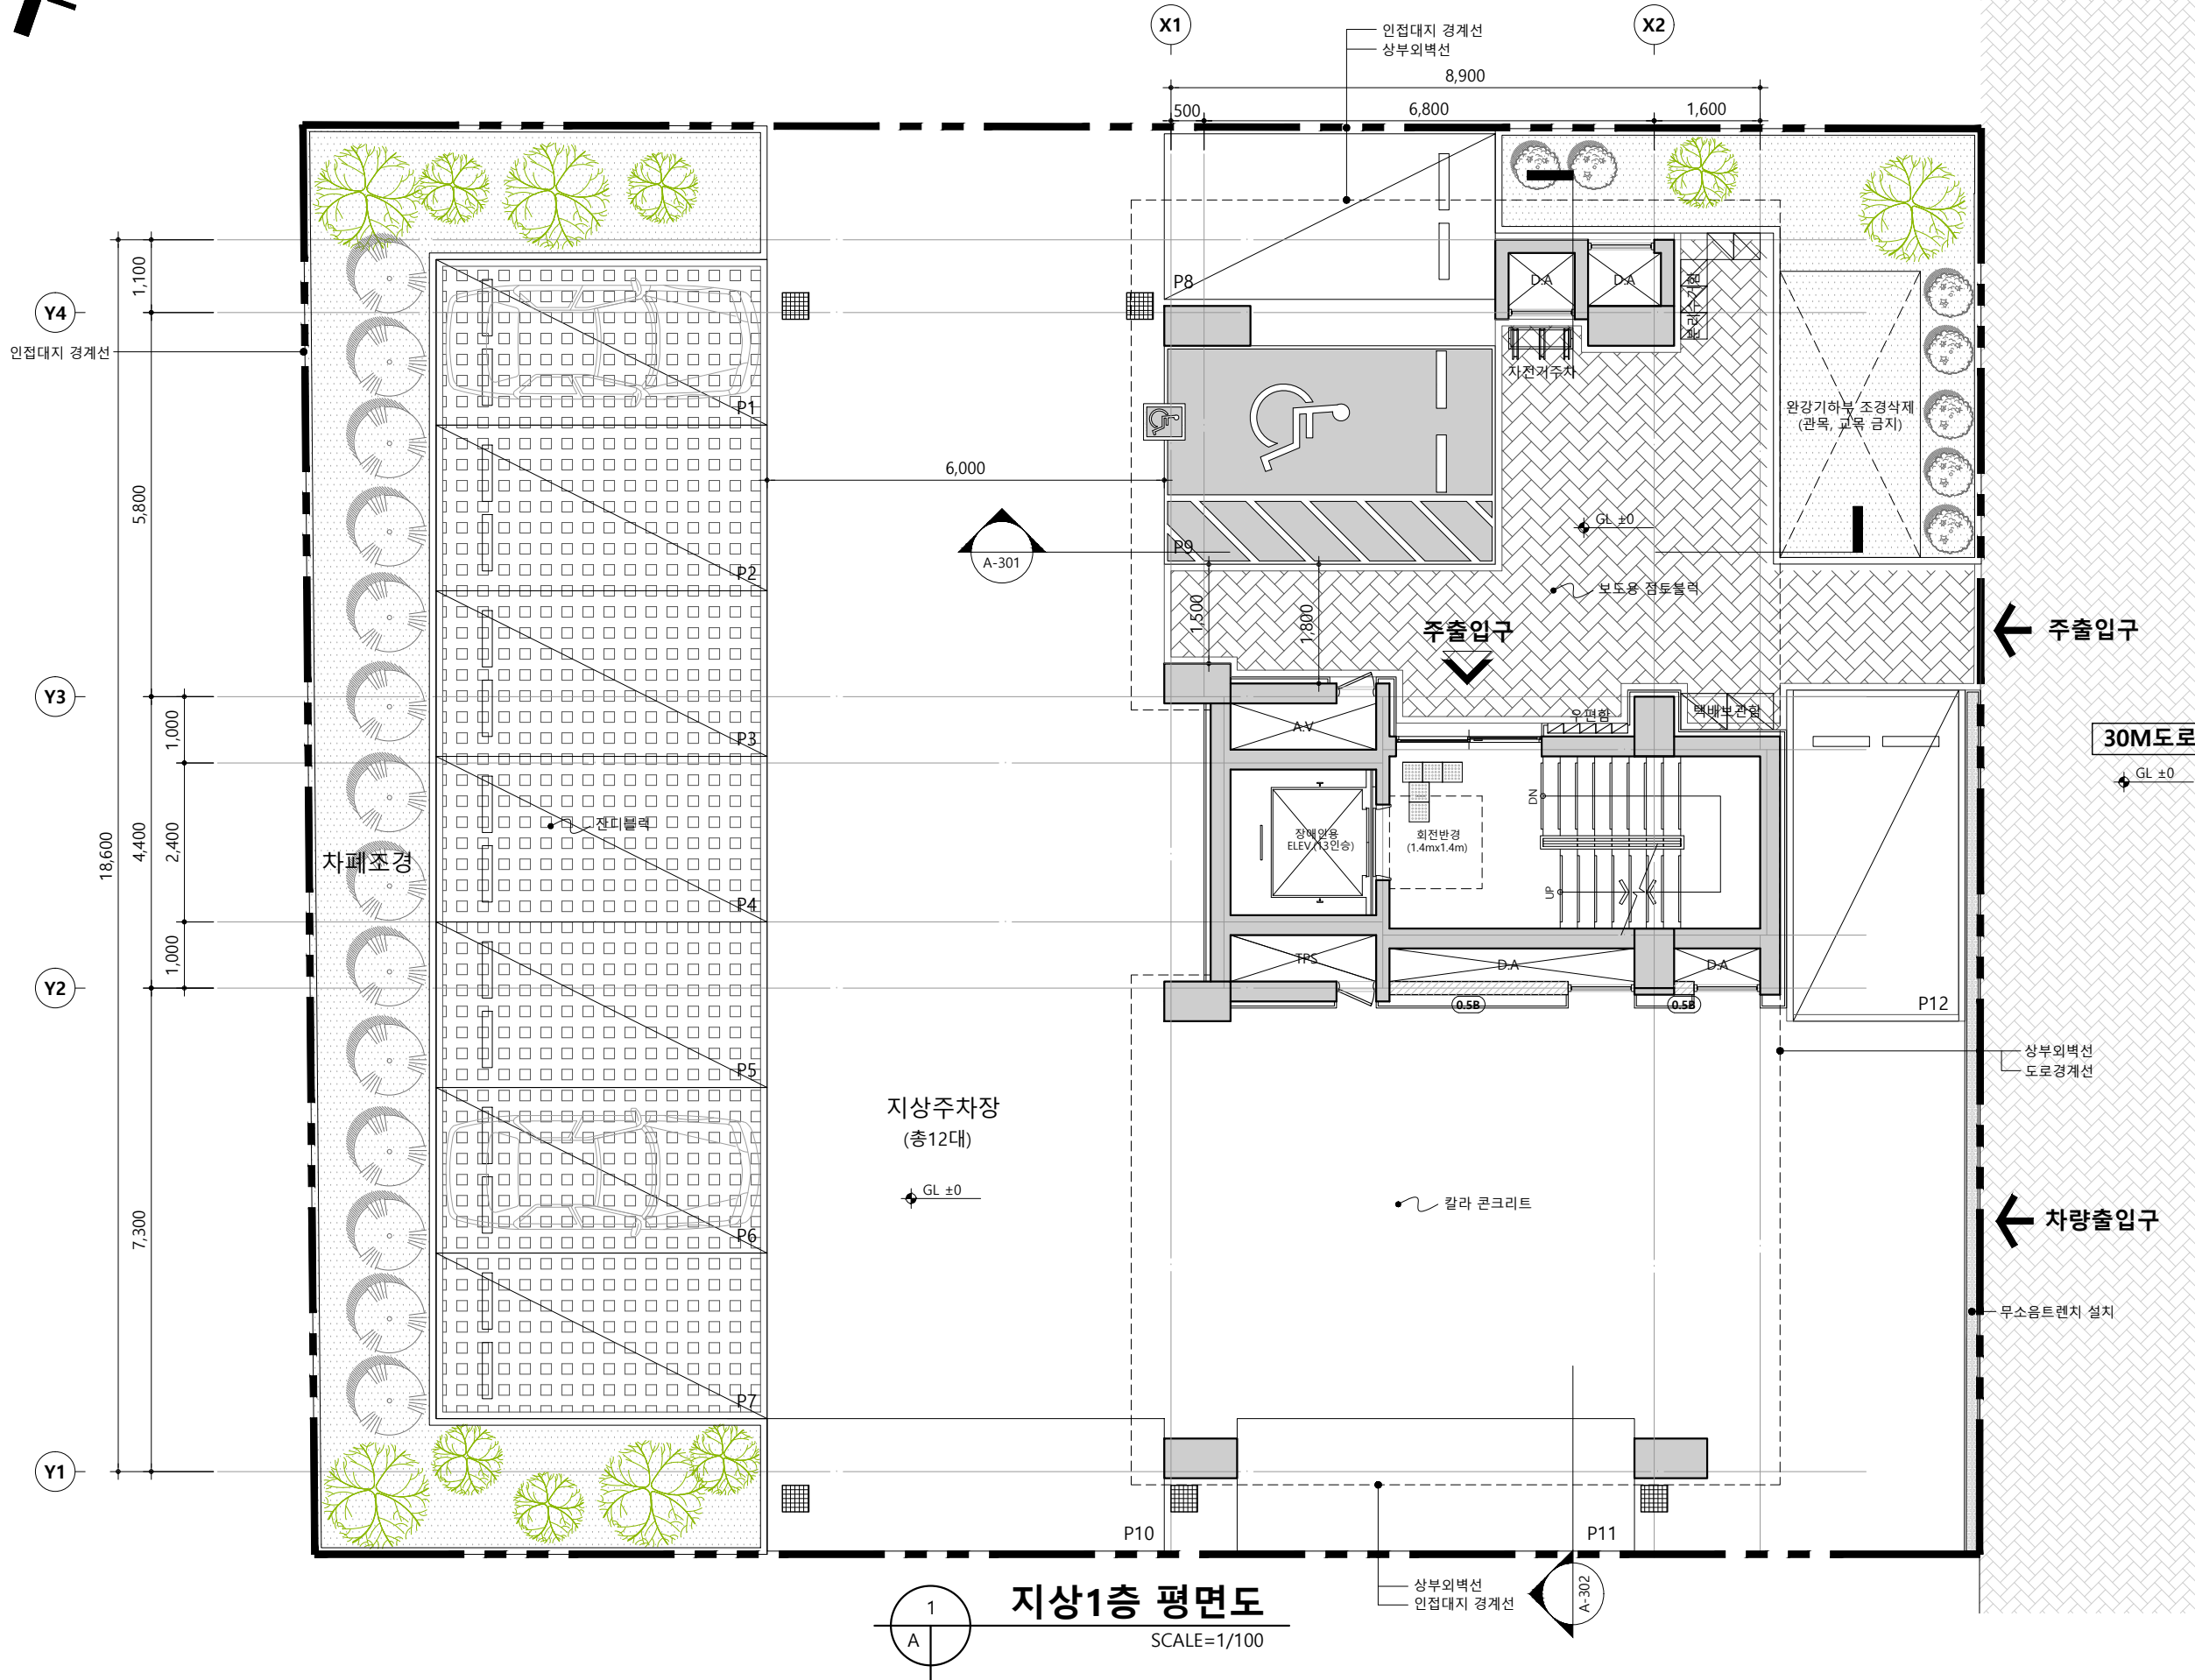

설 계 명
PROJECT TITLE

영등포구
대림동 740-2
오피스텔 신축공사

설 계 번 호
PROJECT NO.

특기사항
NOTE

법 레

(완) : 완강기 (3층 이상, 격층으로 설치)

(배) : 배연창

(방) : 방화문

(재) : 재료분리대

(0.5B) : 0.5B 시멘트벽돌

(T60) : T60 벽체배수판

(O.T) : OPEN 트랜치

변경사항
REVISION

번 호	내 용	일	월	년

제 도
DRAWN BY

검 도
CHECKED BY

설 계
DESIGNED BY

승 인
APPROVED BY

최 의 환

도 면 명
NAME OF DRAWING

지상1층 평면도

축 척
SCALE

날 짜
DATE

A1
A3

1/100

2022. 06


도 면 번 호
DRAWING NO.

A-102


일련 번 호
SHEET NO.

SNA

(주)에스엔에이 건축사사무소
Space & Architecture Design Group
서울 송파구 법원로 128, C동 1017호
TEL (02) 6071-3403 FAX (02) 6213-3403

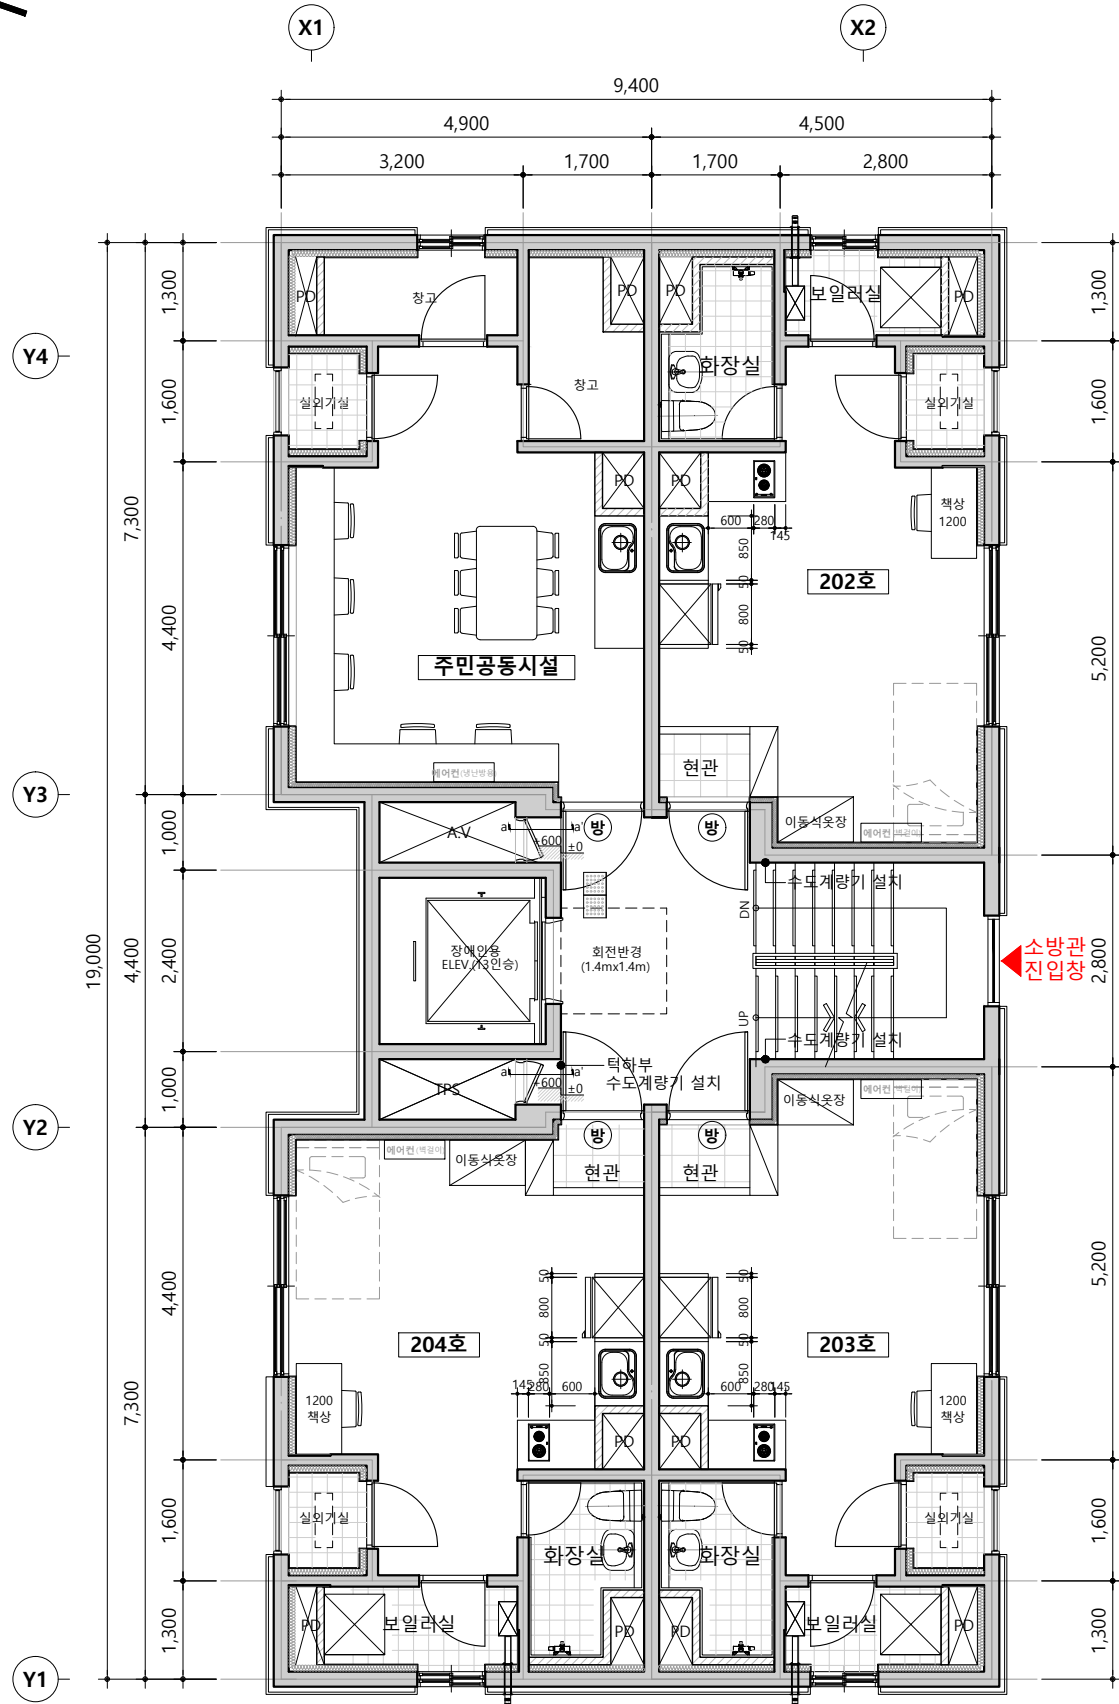

1
A 지상2층 평면도
SCALE=1/100

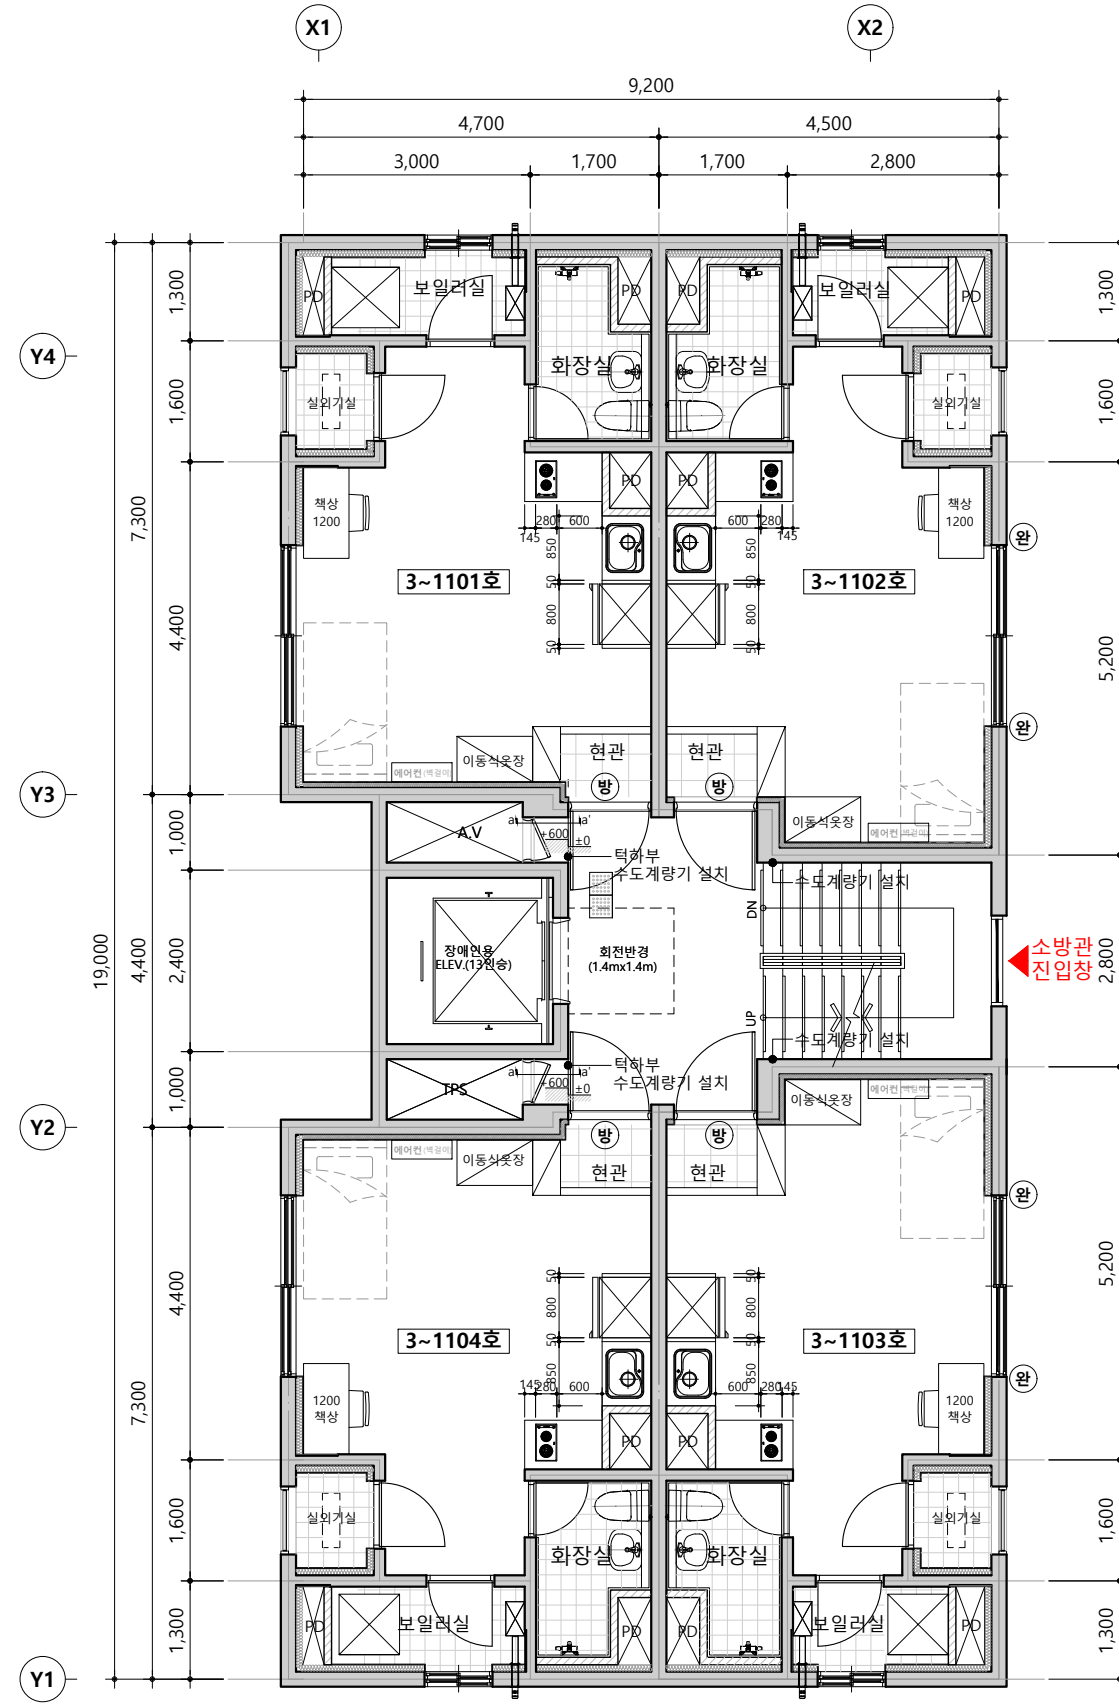

2
A 지상3~11층 평면도
SCALE=1/100

설 계 명
PROJECT TITLE
영등포구
대림동 740-2
오피스텔 신축공사

설 계 번 호
PROJECT NO.

특기사항
NOTE

- * 범 례
- (완) : 환강기 (3층 이상, 격층으로 설치)
 - (배) : 배연창
 - (방) : 간접방화문
 - (재) : 재료분리대
 - (0.5B) : 0.5B 시멘트벽돌
 - (특) : T60 벽체배수판
 - (O.T) : OPEN 트랜치


변경사항
REVISION

제 도
DRAWN BY
검 도
CHECKED BY
설 계
DESIGNED BY
승 인
APPROVED BY 최 의 환


도 면 명
NAME OF DRAWING
지상2~10층,
11층 평면도
축 척
SCALE
A1
A3 1/100
날 짜
2022. 06

도 면 번 호
DRAWING NO.
A-103
일련 번 호
SHEET NO.

SNA
(주)에스앤에이 건축사사무소
Space & Architecture Design Group
서울 송파구 법원로 128, C동 1017호
TEL. (02) 6071-3403 FAX. (02) 6213-3403

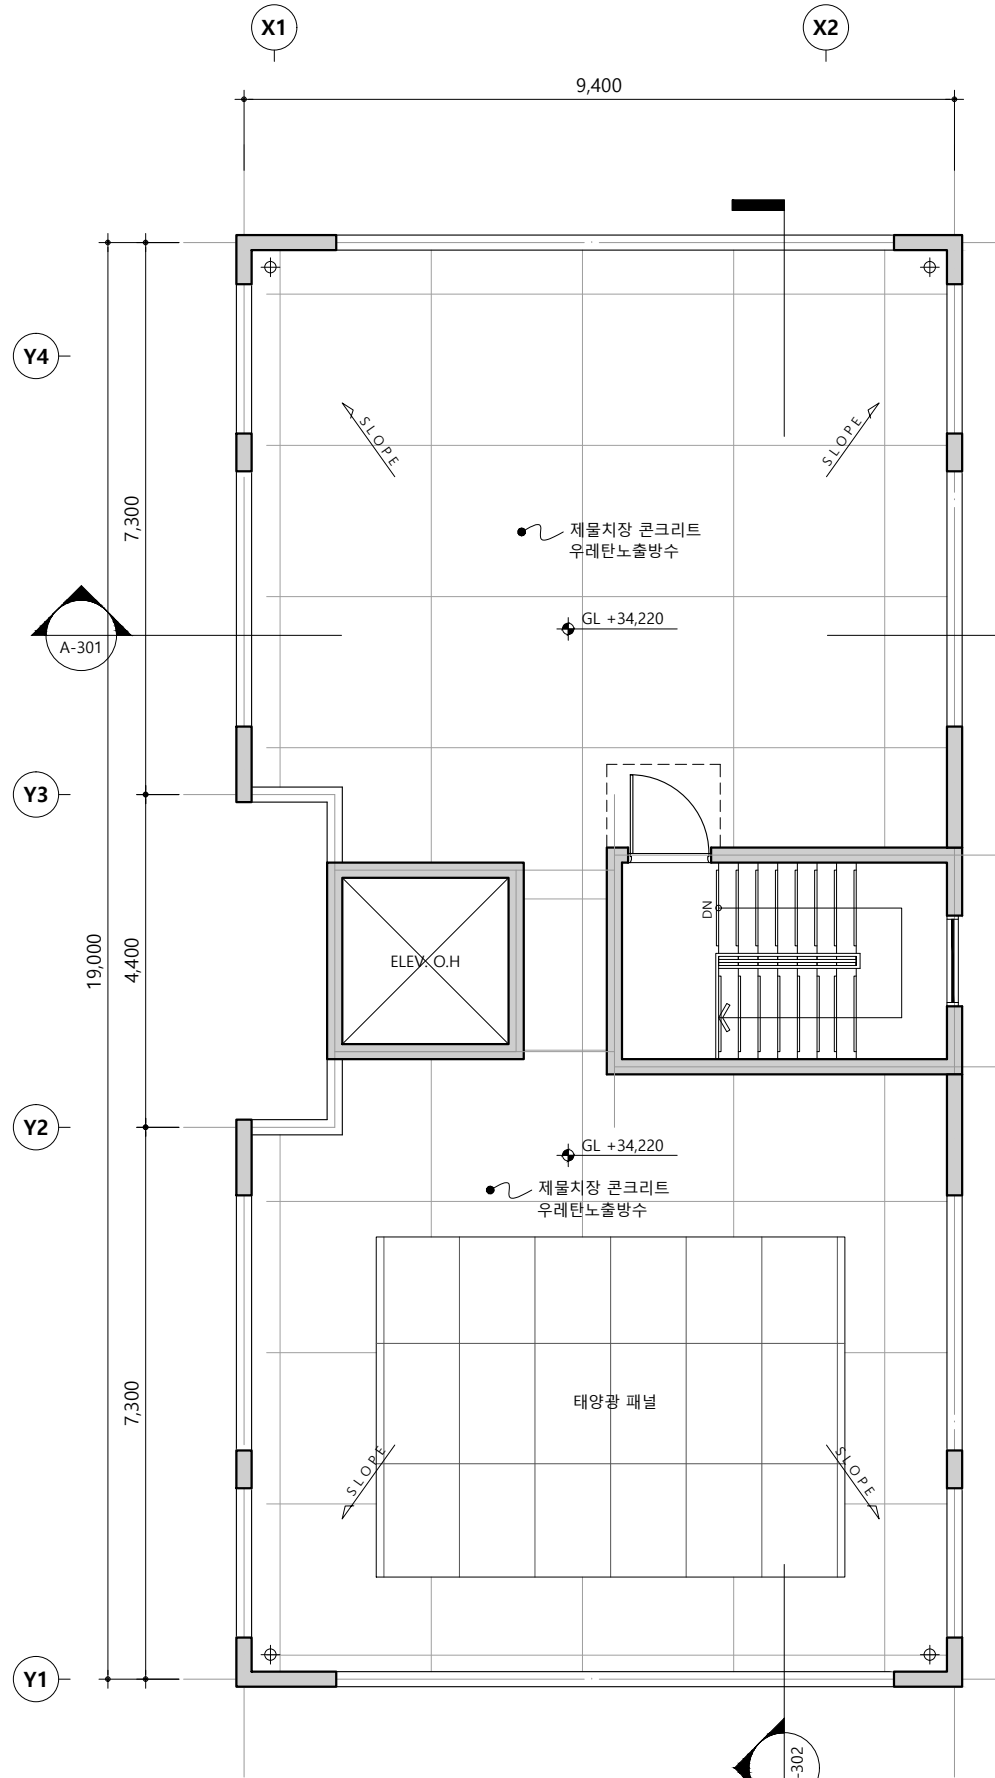

1 옥탑층 평면도
SCALE=1/100

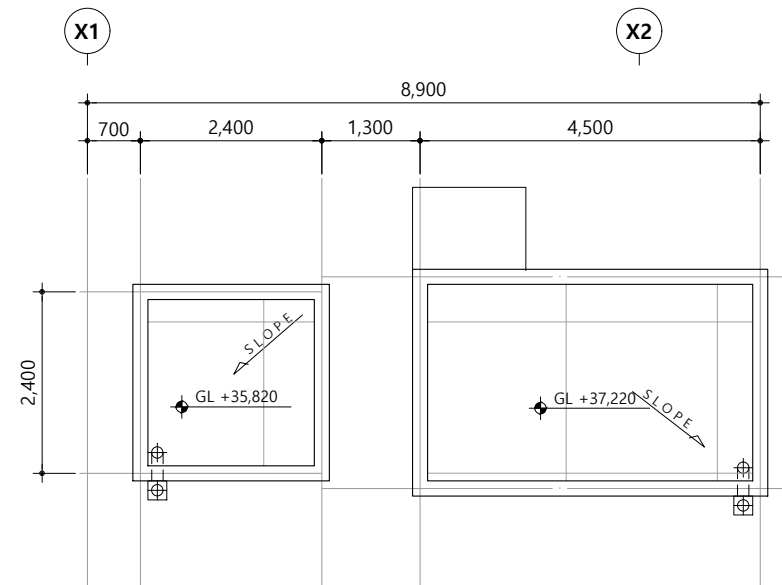

2 옥탑지붕 평면도
SCALE=1/100

설 계 명
PROJECT TITLE
영등포구
대림동 740-2
오피스텔 신축공사

설 계 번 호
PROJECT NO.

특기사항
NOTE

* 법 레

(완) : 완강기 (3층 이상, 격층으로 설치)

(배) : 배연창

(방) : 방풍방화문

(재) : 재료분리대

(0.5B) : 0.5B 시멘트벽돌

(배수) : T60 벽체배수판

(O.T) : OPEN 트랜치

변경사항
REVISION

제 도
DRAWN BY
검 도
CHECKED BY
설 계
DESIGNED BY
승 인
APPROVED BY 최 의 환

도 면 명
NAME OF DRAWING

옥탑층, 옥탑지붕 평면도

축척	SCALE	날짜
A1		2022. 06
A3	1/100	

도 면 번 호
DRAWING NO.

A-104

일련 번 호
SHEET NO.

SNA
(주)에스엔에이 건축사사무소
Space & Architecture Design Group
서울 송파구 법원로 128, C동 1017호
TEL (02) 6071-3403 FAX (02) 6213-3403

설 계 명
PROJECT TITLE

영등포구
대림동 740-2
오피스텔 신축공사

설 계 번 호
PROJECT NO.

특기사항
NOTE

변경사항
REVISION

제 도
DRAWN BY
검 토
CHECKED BY
설 계
DESIGNED BY
승 인
APPROVED BY 최 의 환

도 면 명
NAME OF DRAWING

입 면 도 -1

축척	SCALE	날 짜
A1		2022. 12
A3	1/300	

도 면 번 호
DRAWING NO.

A-201

일련번호
SHEET NO.

SNA

(주)에스엔에이 건축사사무소
Space & Architecture Design Group
서울 송파구 법원로 128, C동 1017호
TEL. (02) 6071-3403 FAX. (02) 6213-3403


KEY MAP



1
A

정 면 도
SCALE=1/300

KEY MAP

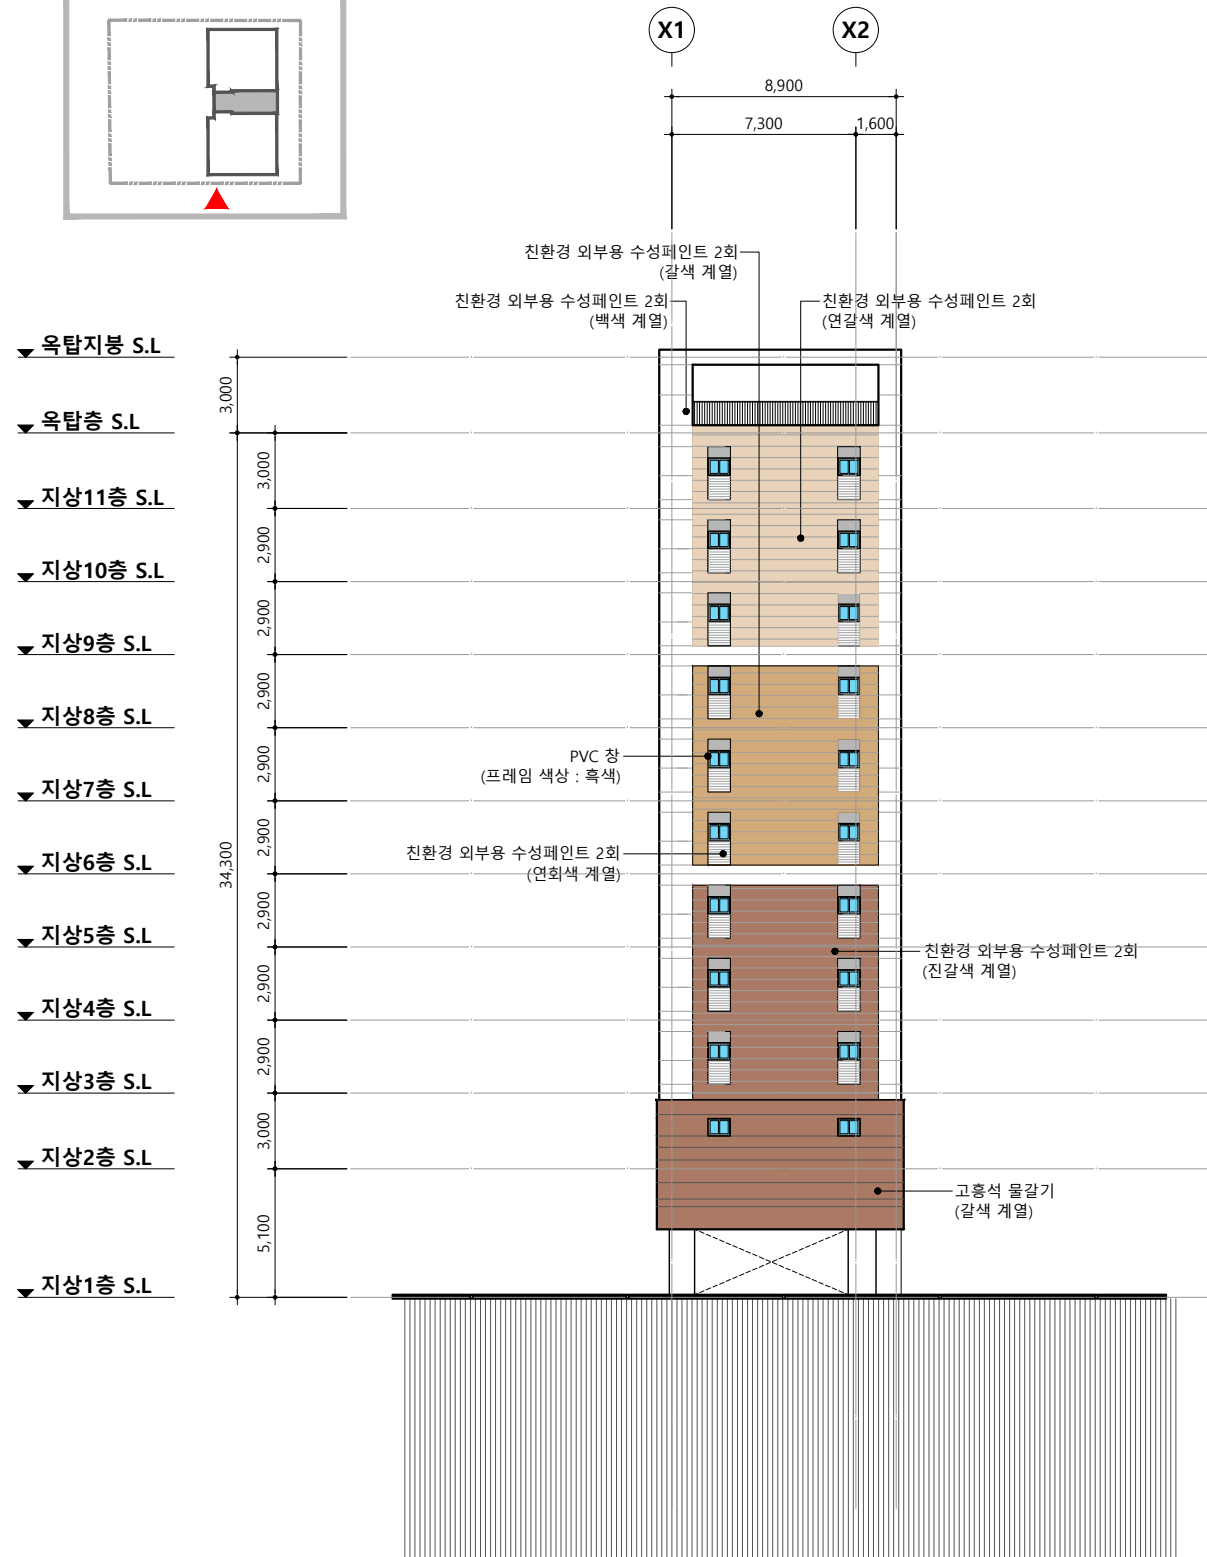

2
A

좌 측 면 도
SCALE=1/300

설 계 명
PROJECT TITLE

영등포구
대림동 740-2
오피스텔 신축공사

설 계 번 호
PROJECT NO.

특기사항
NOTE

변경사항
REVISION

제 도
DRAWN BY
검 토
CHECKED BY
설 계
DESIGNED BY
승 인
APPROVED BY 최 의 환

도 면 명
NAME OF DRAWING

입 면 도 -2

축척	SCALE	날 짜
A1		2022. 12
A3	1/300	



도 면 번 호
DRAWING NO.

A-202



일련번호
SHEET NO.

SNA

(주)에스엔에이 건축사사무소
Space & Architecture Design Group
서울 송파구 법원로 128, C동 1017호
TEL. (02) 6071-3403 FAX. (02) 6213-3403

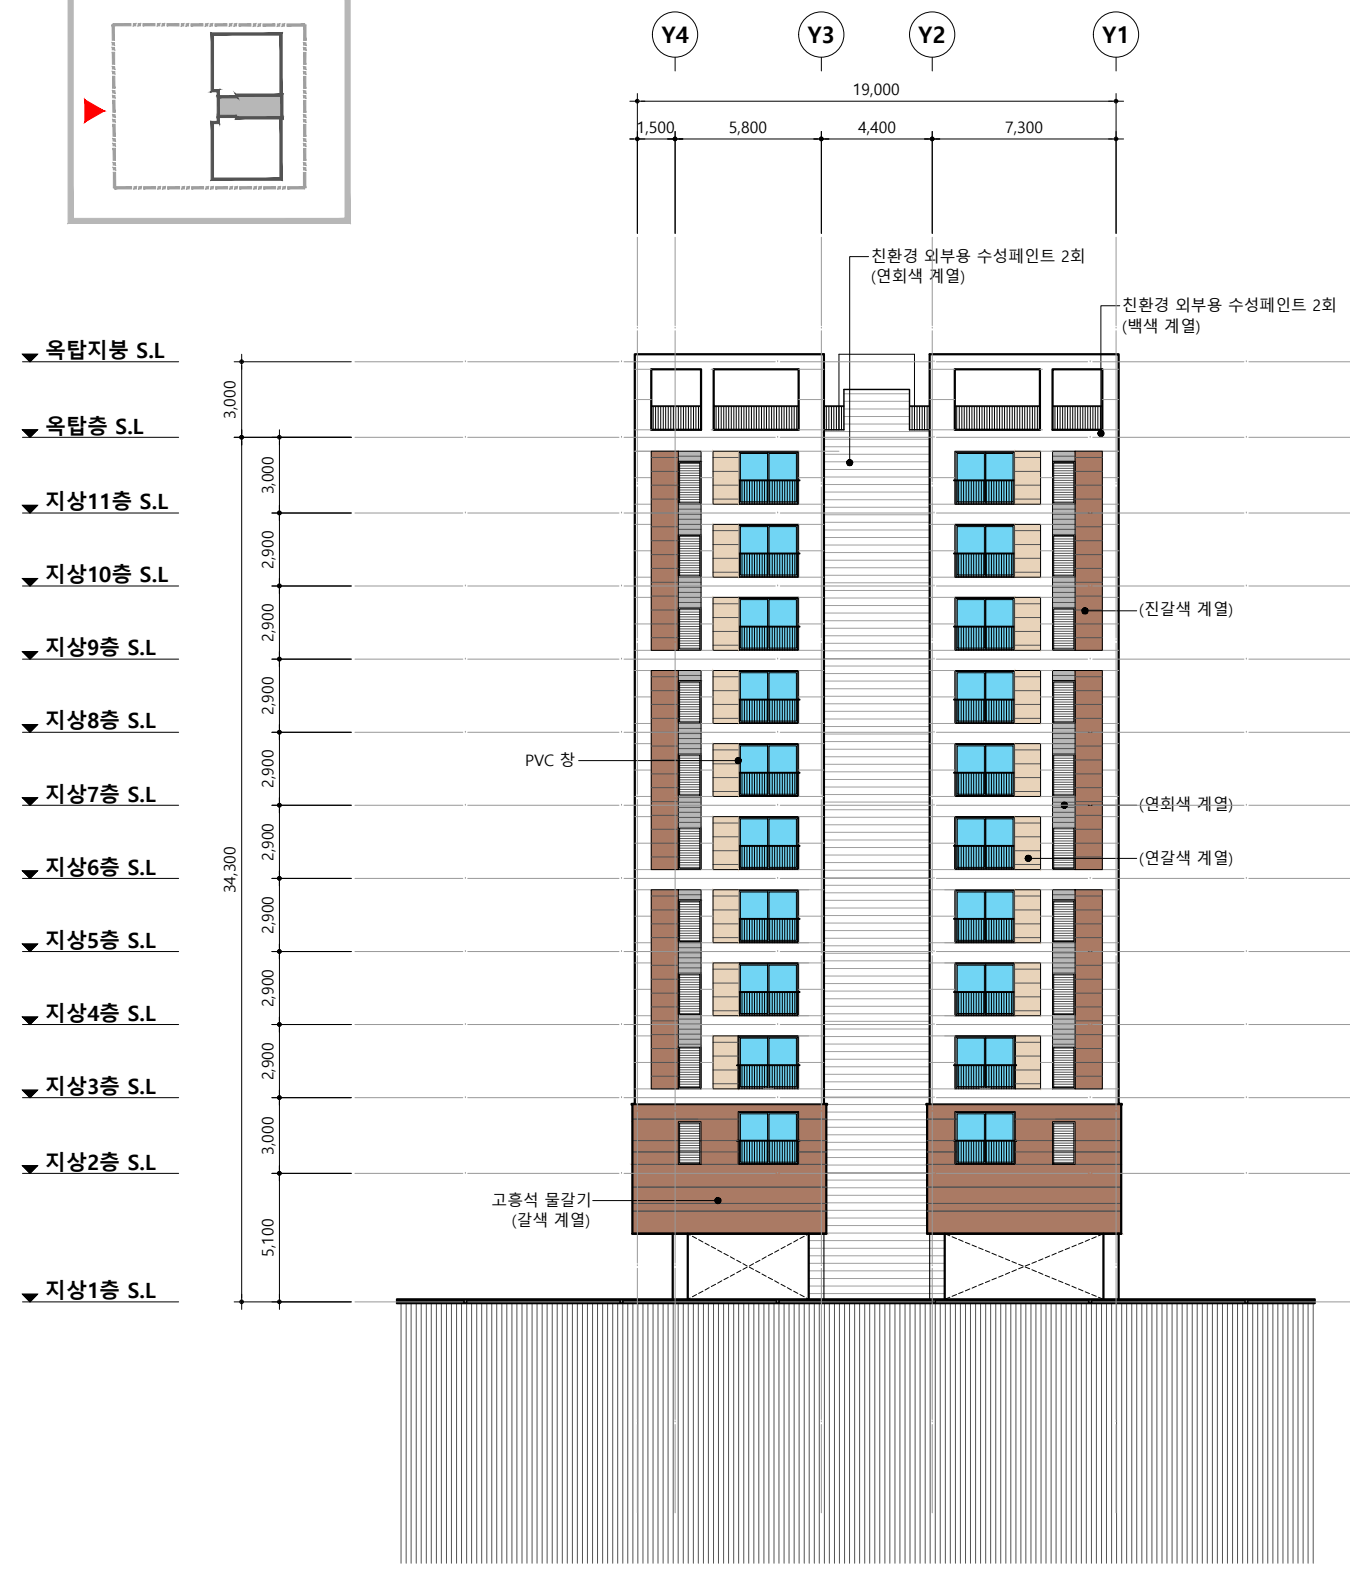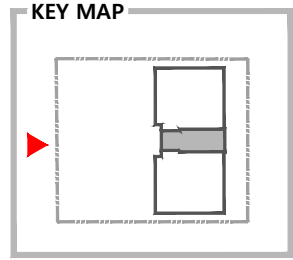

1 배 면 도
SCALE=1/300

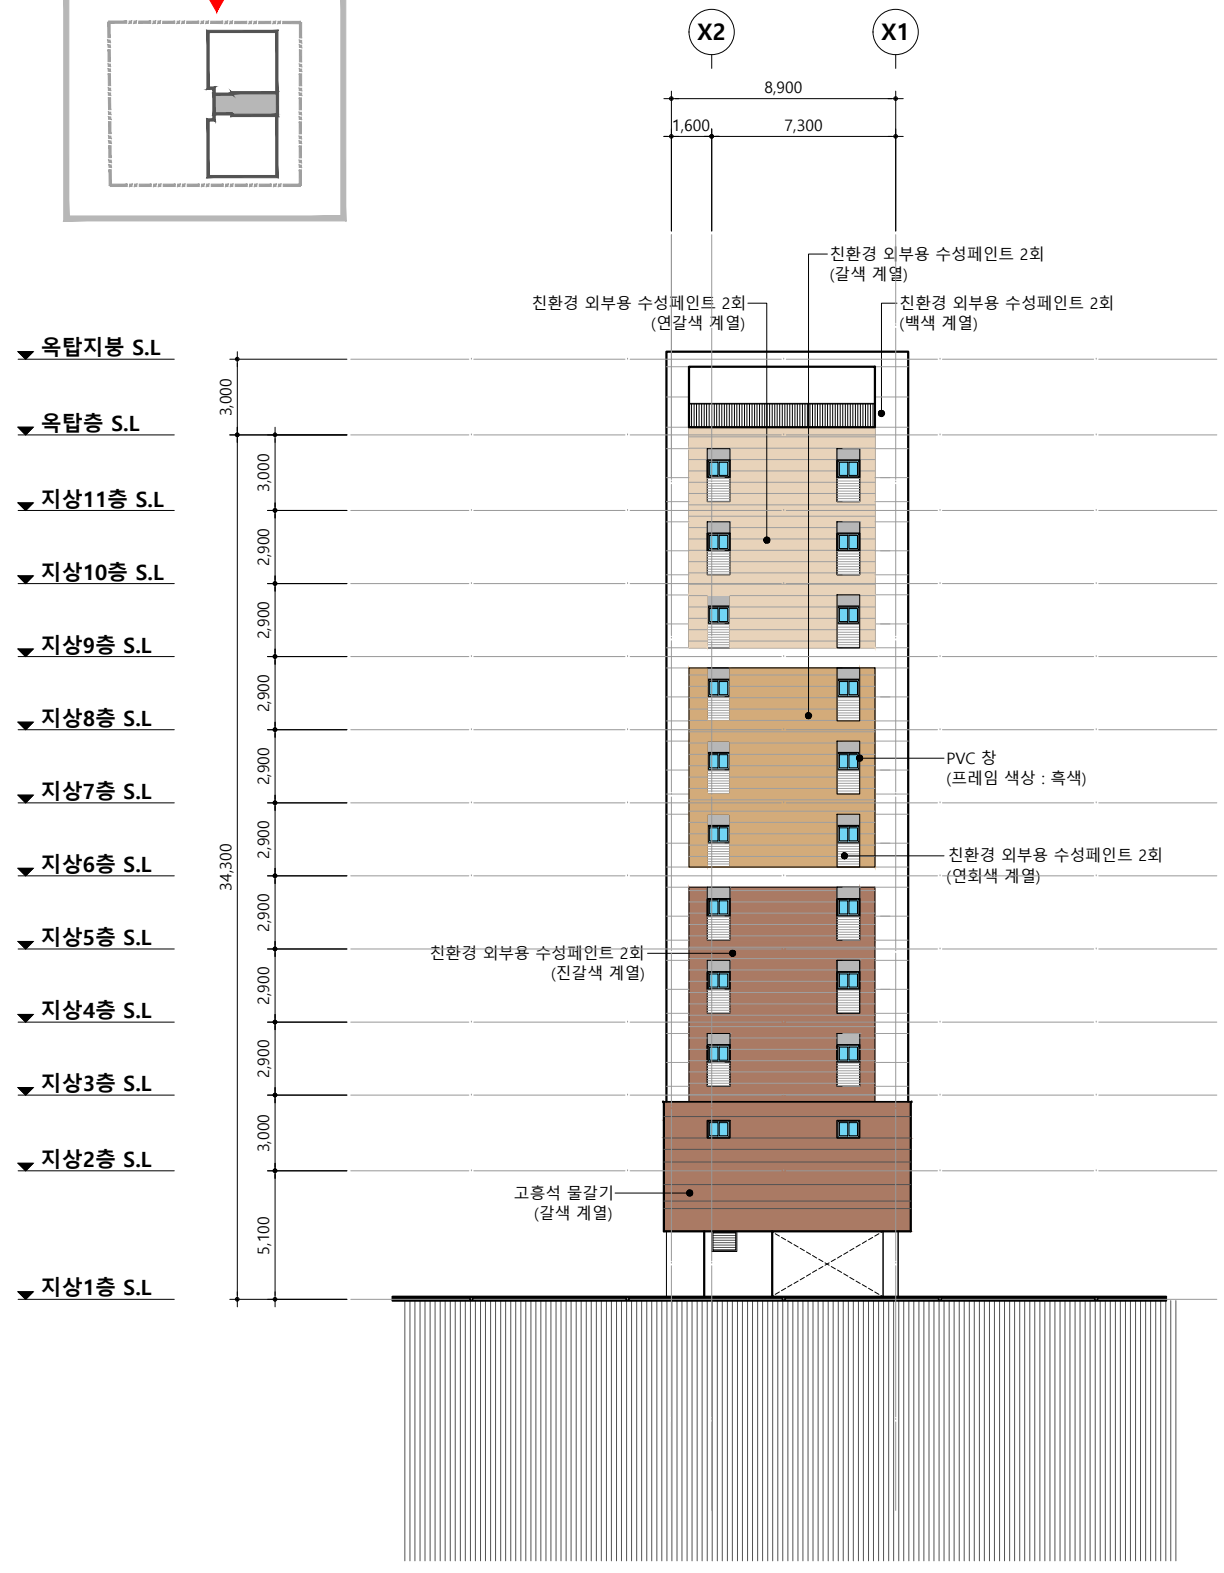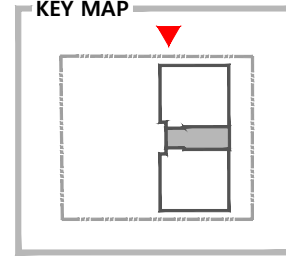

2 우 측 면 도
SCALE=1/300