

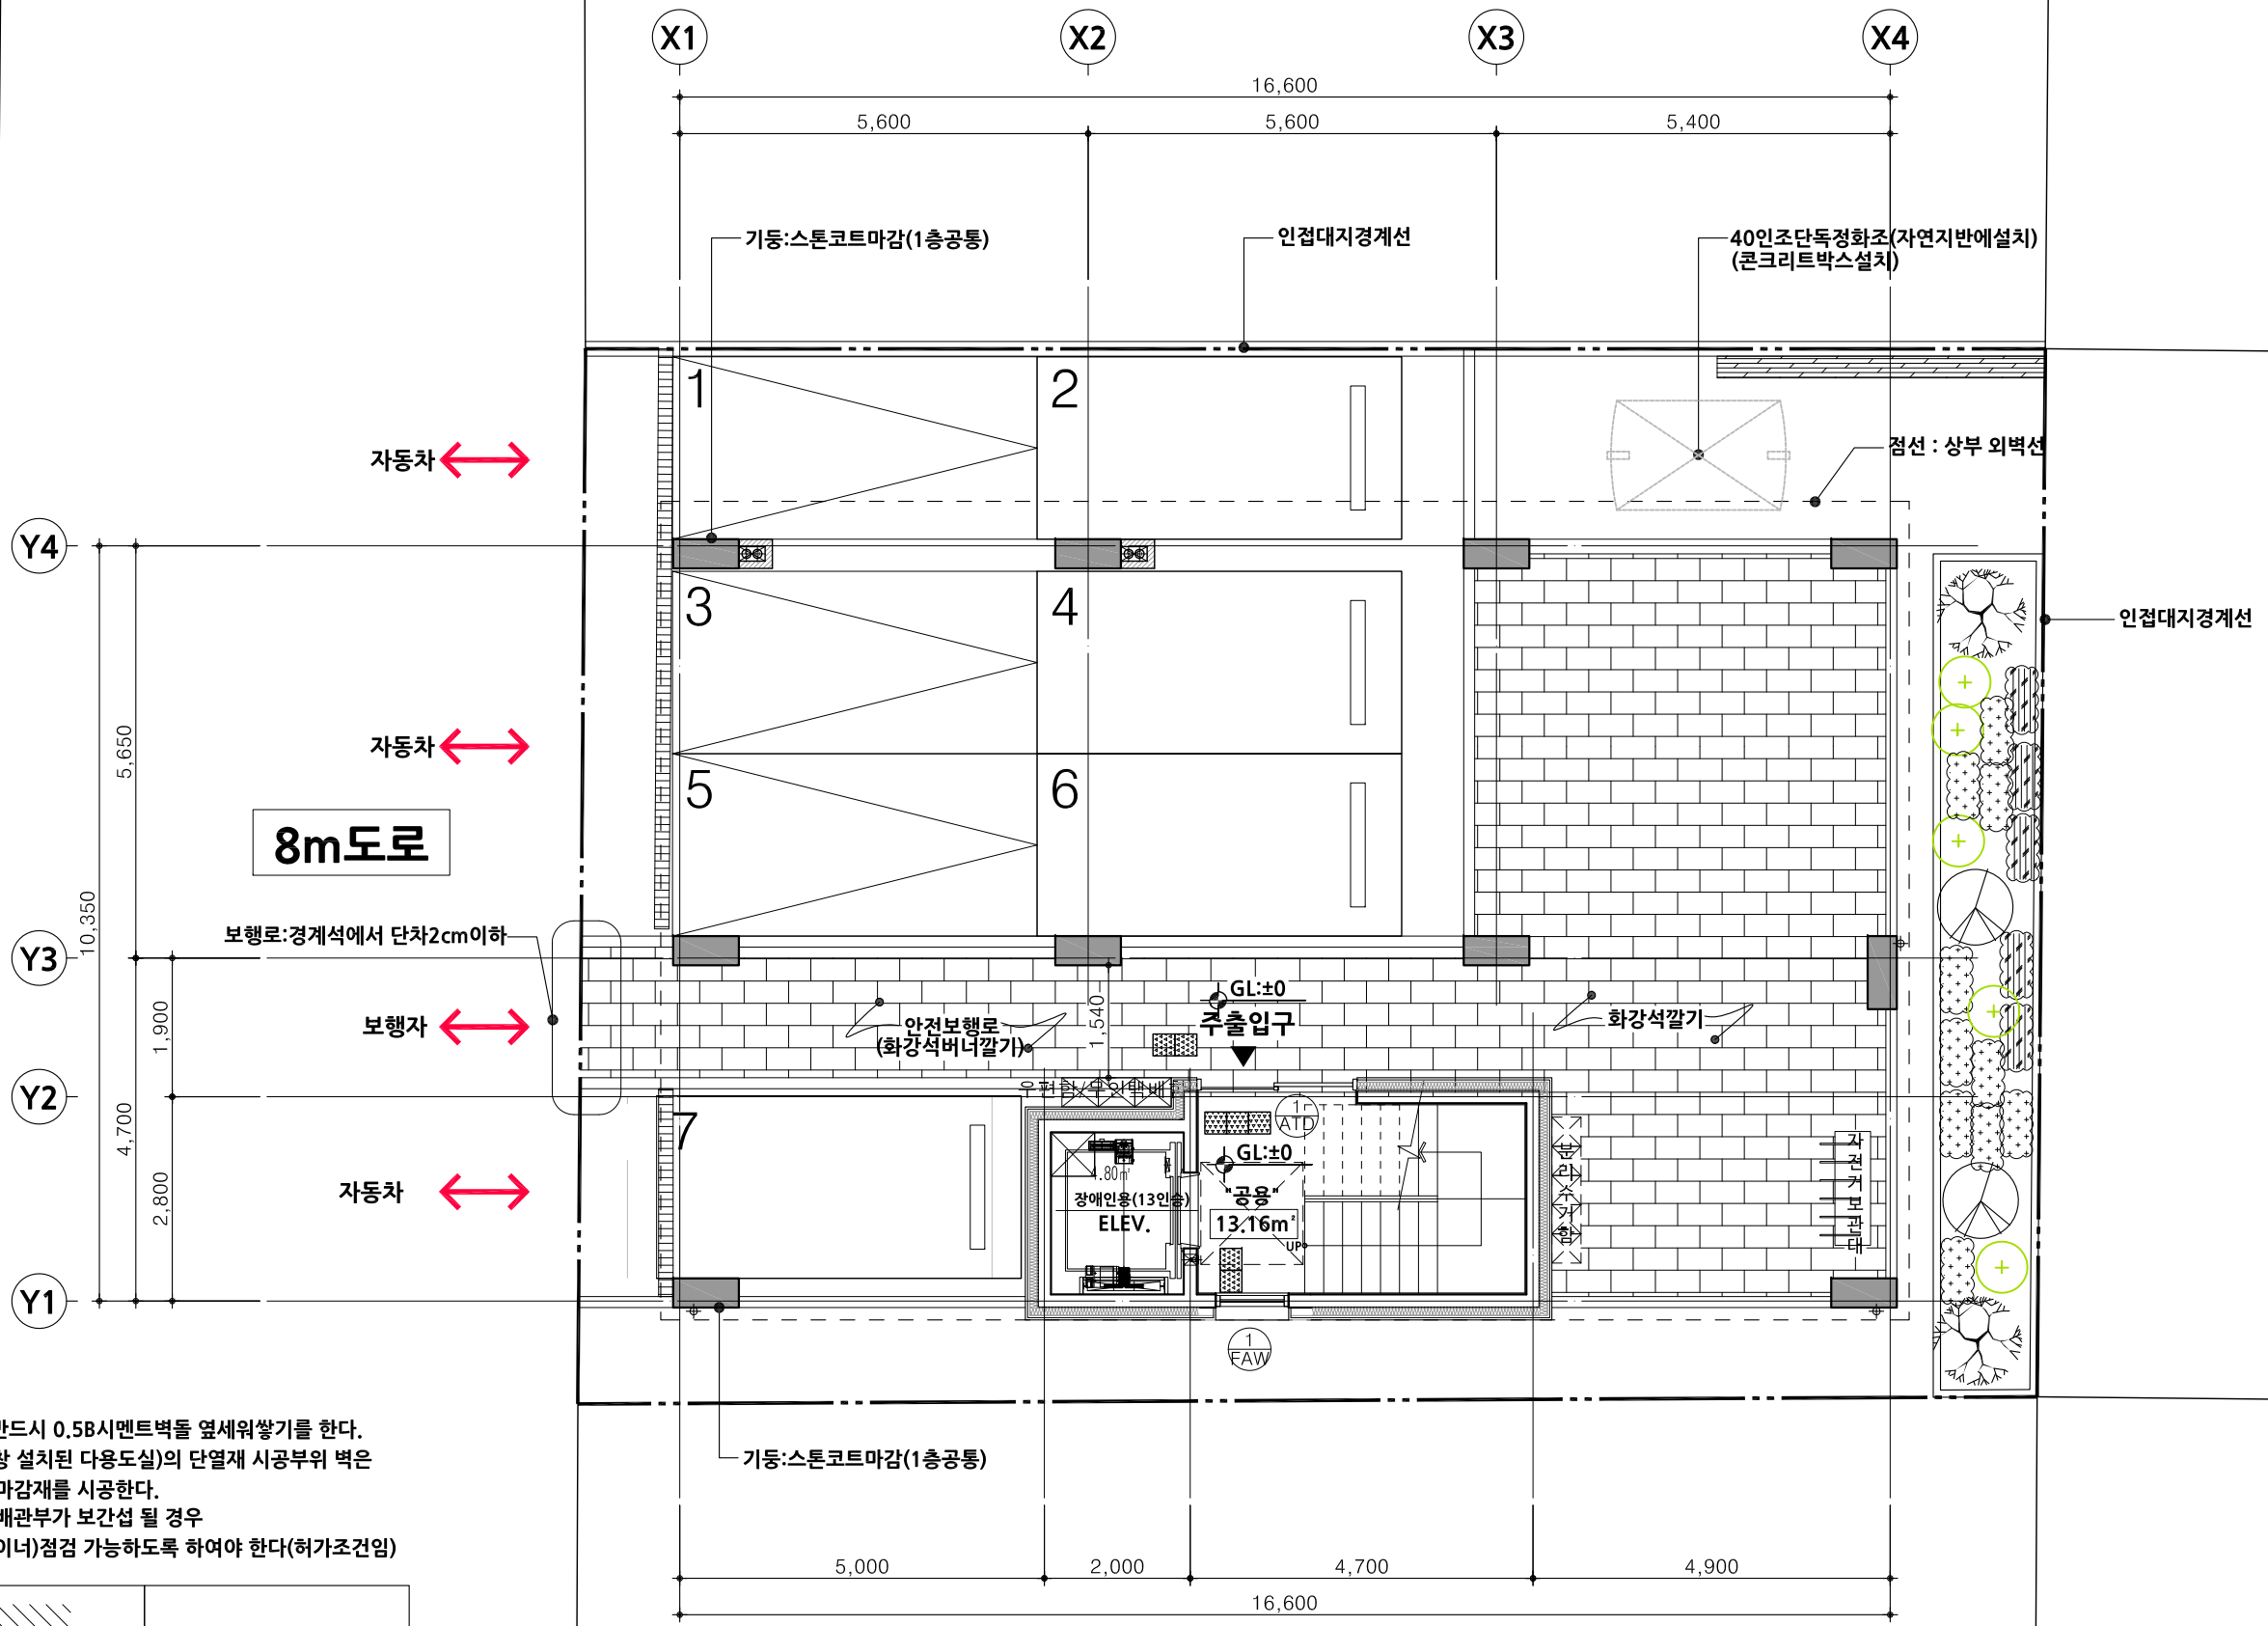
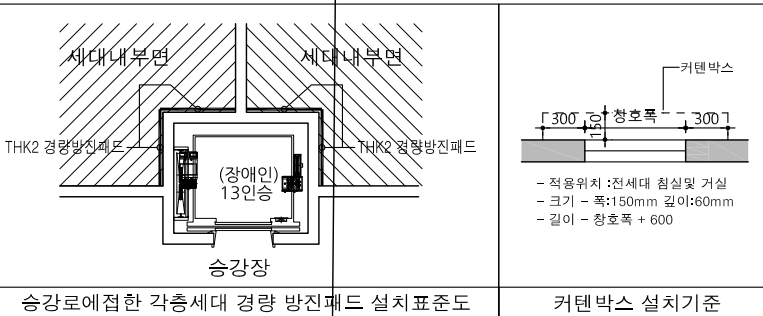


- * NOTE *
1. 간접외기에 연결하는 화강실벽은 반드시 0.5B시멘트벽돌 옆세워쌓기를 한다.
 2. 간접외기부분(복도 및 소방관진입창 설치된 다용도실)의 단열재 시공부위 벽은 반드시 내수석고보드 시공 후 지점마감재를 시공한다.
 3. 2층 바닥, 1층 필로티 상부의 수직배관부가 보간성 될 경우 배관 격임시공부에 소재구(스트레이너)점검 가능하도록 하여야 한다(허가조건임)

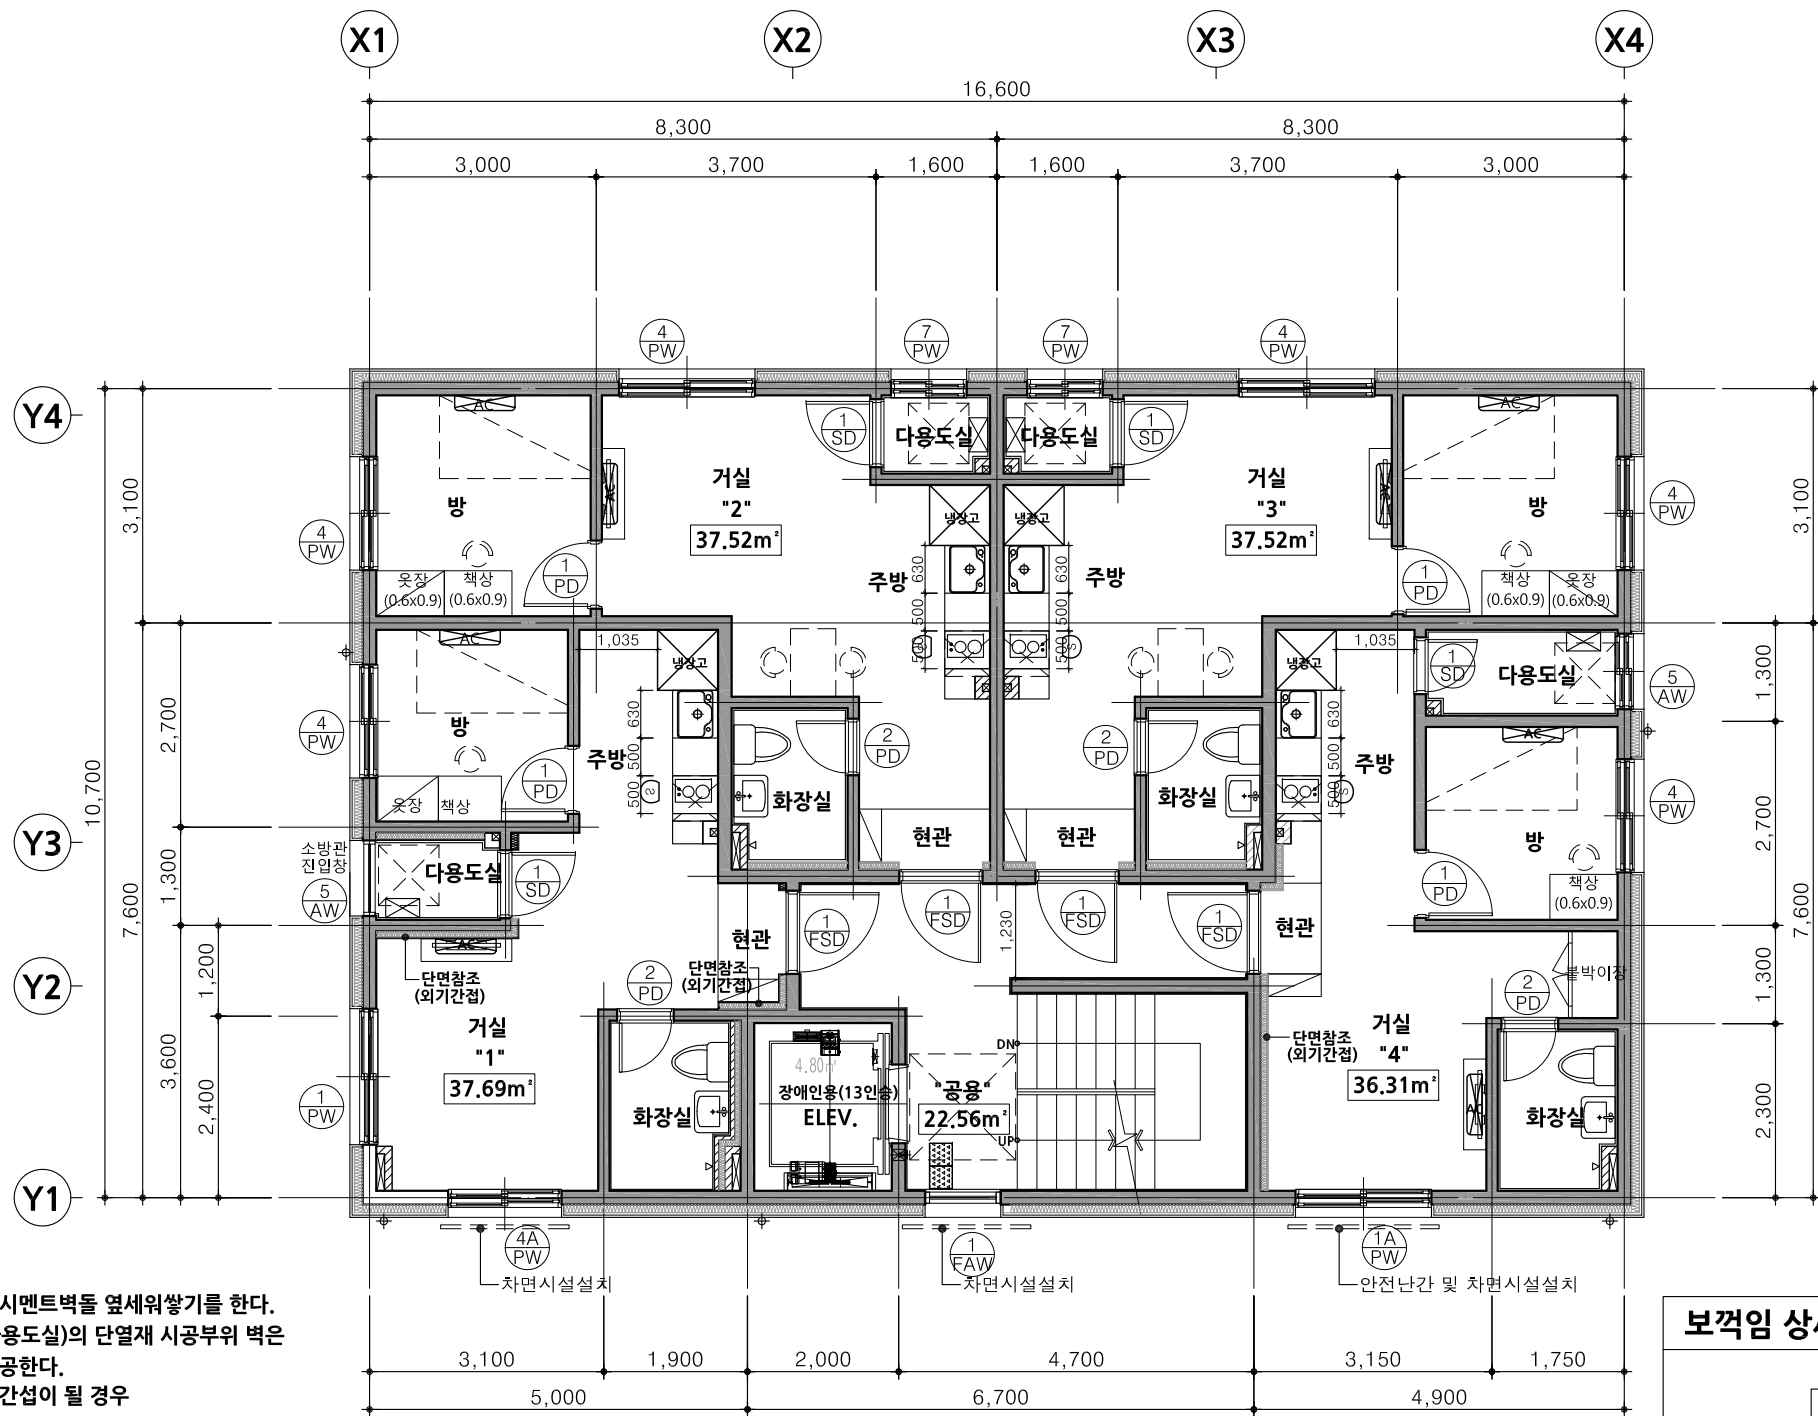


1층 평면도
축척 1:100

NO.	DATE	REVISION DESCRIPTION
NOTES.		
영등포구 대림동 729-7번지 도시형생활주택 (소형주택) 신축공사		
건축사사무소 여 현		
YEOHEON ARCHITECT & ENGINEERS		
PHONE : (02) 2057 - 8005~6		
PROJECT NO.		
DRAWN BY. KIM,K.R		
CHECKED BY.		
APPROVED BY.		
DRAWING TITLE		
1층 평면도		
SCALE. A3 1/100		
DATE. 2022.07.		
DRAWING NO. A - 201		
SHEET NO.		

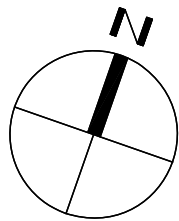


- * NOTE ***
- 간접외기에 연결하는 화장실벽은 반드시 0.5B시멘트벽돌 옆세워쌓기를 한다.
 - 간접외기부분(복도 및 소방관진입창 설치된 다용도실)의 단열제 시공부위 벽은 반드시 내수석고보드 시공 후 지정마감재를 시공한다.
 - 2층 바닥, 1층 필로티 상부의 수직배관부가 보간성이 될 경우 배관 격임시공부에 소재구(스트레이너)점검 가능하도록 하여야 한다(허가조건임)

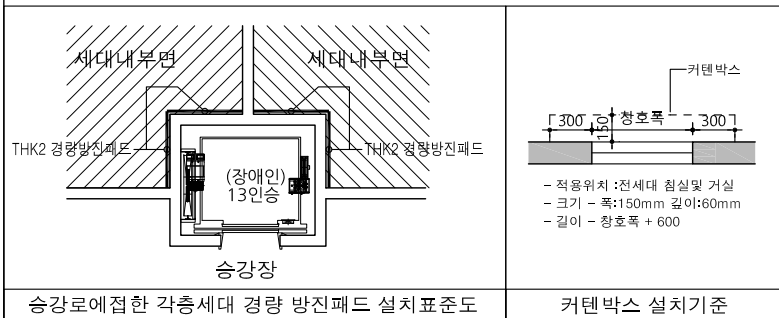

1 2, 3층 평면도
축척 1:100

보격임 상세"A" - (2층바닥적용)

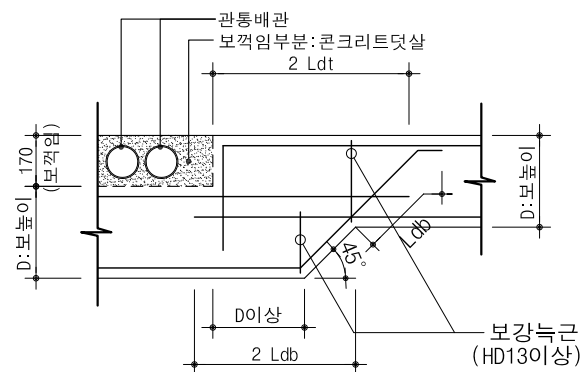

NO.	DATE	REVISION DESCRIPTION




NOTES.

각 세대의 바닥마감 시공시
소음방지를 위한 층간 바닥
충격을 차단구조기준
(국토부고시)을 만족할 것.

영등포구 대림동
729-7번지
도시형생활주택
(소형주택)
신축공사

건축사사무소
여
현
YEOHEON ARCHITECT & ENGINEERS
PHONE : (02) 2057 - 8005~6

PROJECT NO.
DRAWN BY. KIM.K.R
CHECKED BY.
APPROVED BY.
DRAWING TITLE 2층,3층 평면도
SCALE. A3 1/100
DATE. 2022.07.
DRAWING NO. A - 202
SHEET NO.

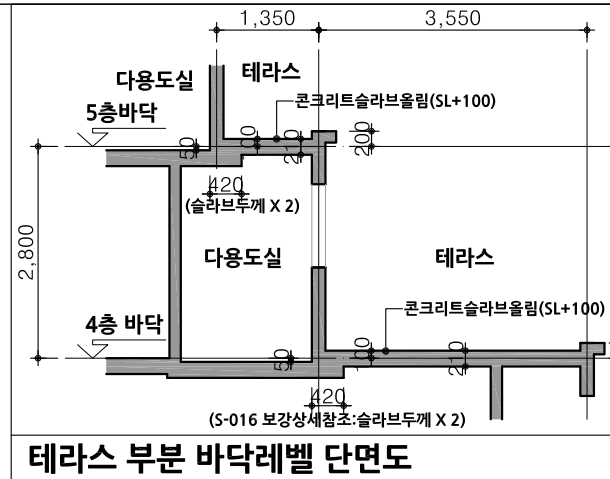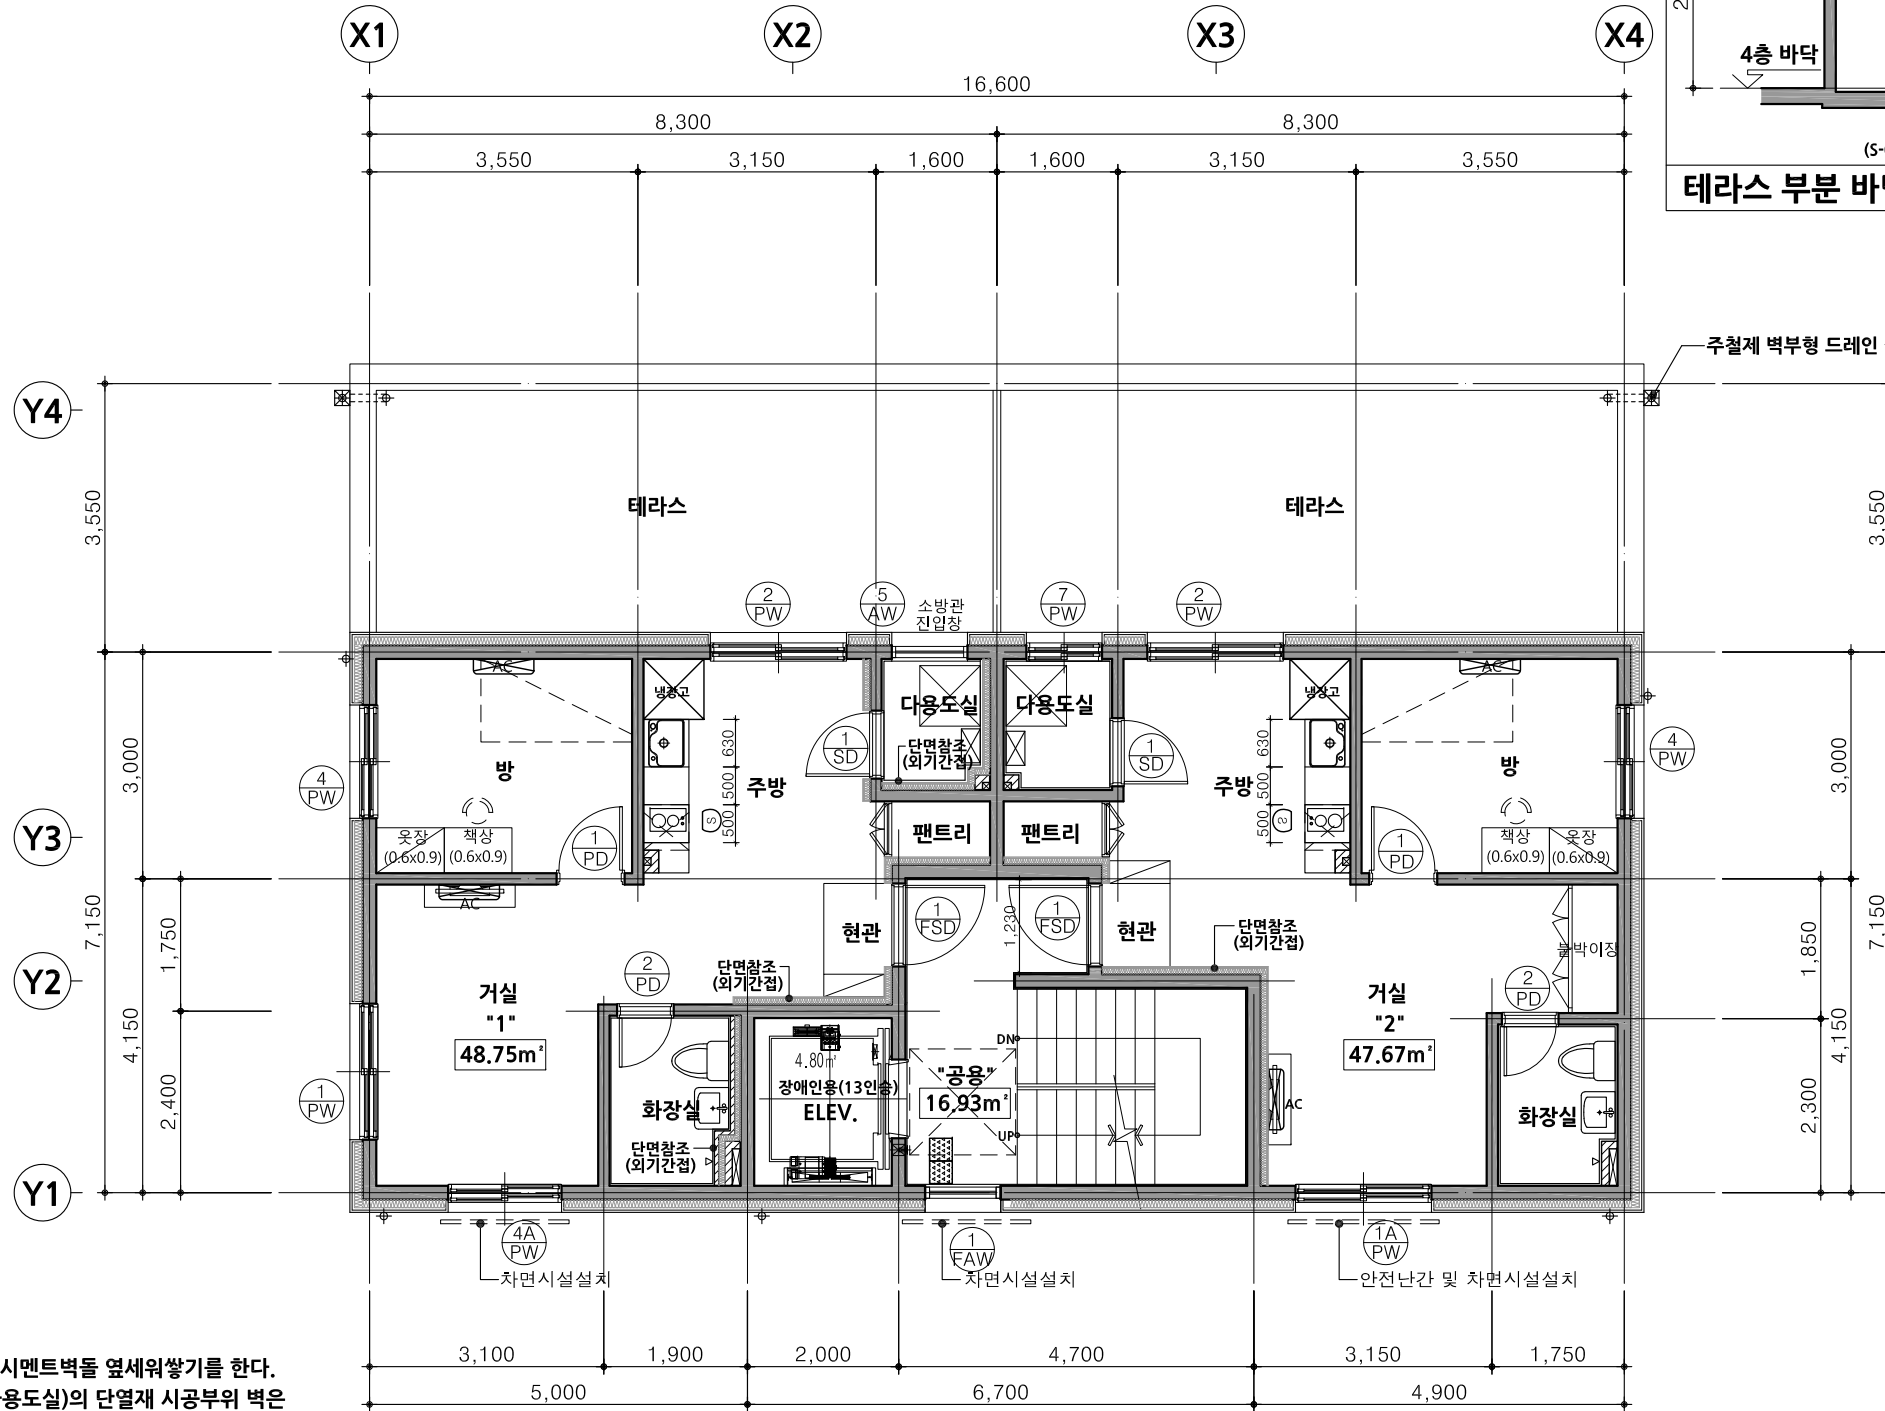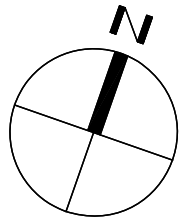

NO.	DATE	REVISION DESCRIPTION

NOTES.


각 세대의 바닥마감 시공시
소음방지를 위한 층간 바닥
충격을 차단구조기준
(국토부고시)을 만족할 것.

영등포구 대림동
729-7번지
도시형생활주택
(소형주택)
신축공사




건축사사무소
여
YEOHEON ARCHITECT & ENGINEERS
PHONE : (02) 2057 - 8005~6

PROJECT NO.	
DRAWN BY.	KIM.K.R
CHECKED BY.	
APPROVED BY.	
DRAWING TITLE	4층 평면도
SCALE	A3 1/100
DATE	2022.07.
DRAWING NO.	A - 203
SHEET NO.	

- * NOTE *
- 간접외기에 연결하는 화장실벽은 반드시 0.5B시멘트벽돌 옆세워쌓기를 한다.
 - 간접외기부분(복도 및 소방관진입창 설치된 다용도실)의 단열재 시공부위 벽은 반드시 내수석고보드 시공 후 지정마감재를 시공한다.

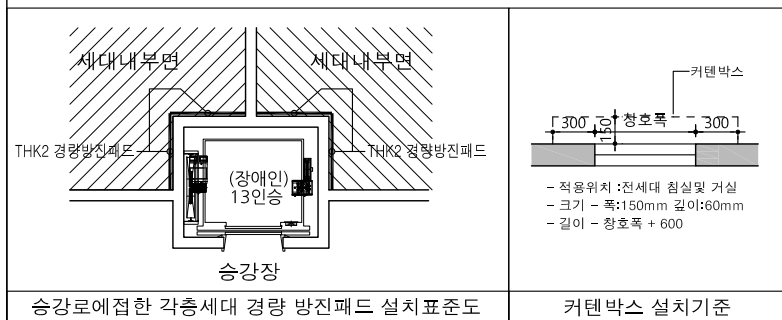

1 4층 평면도
축척 1:100

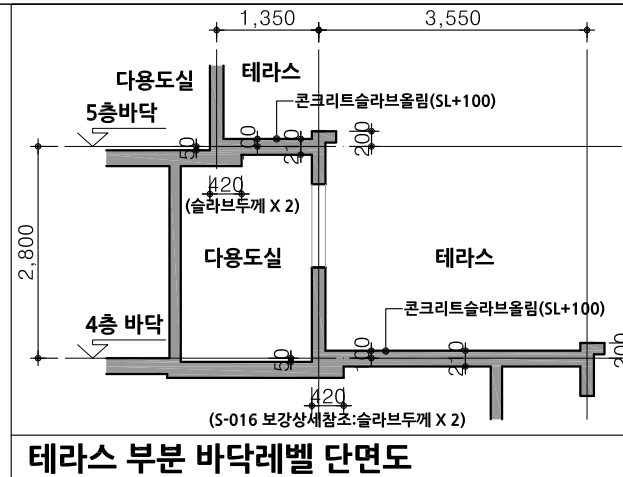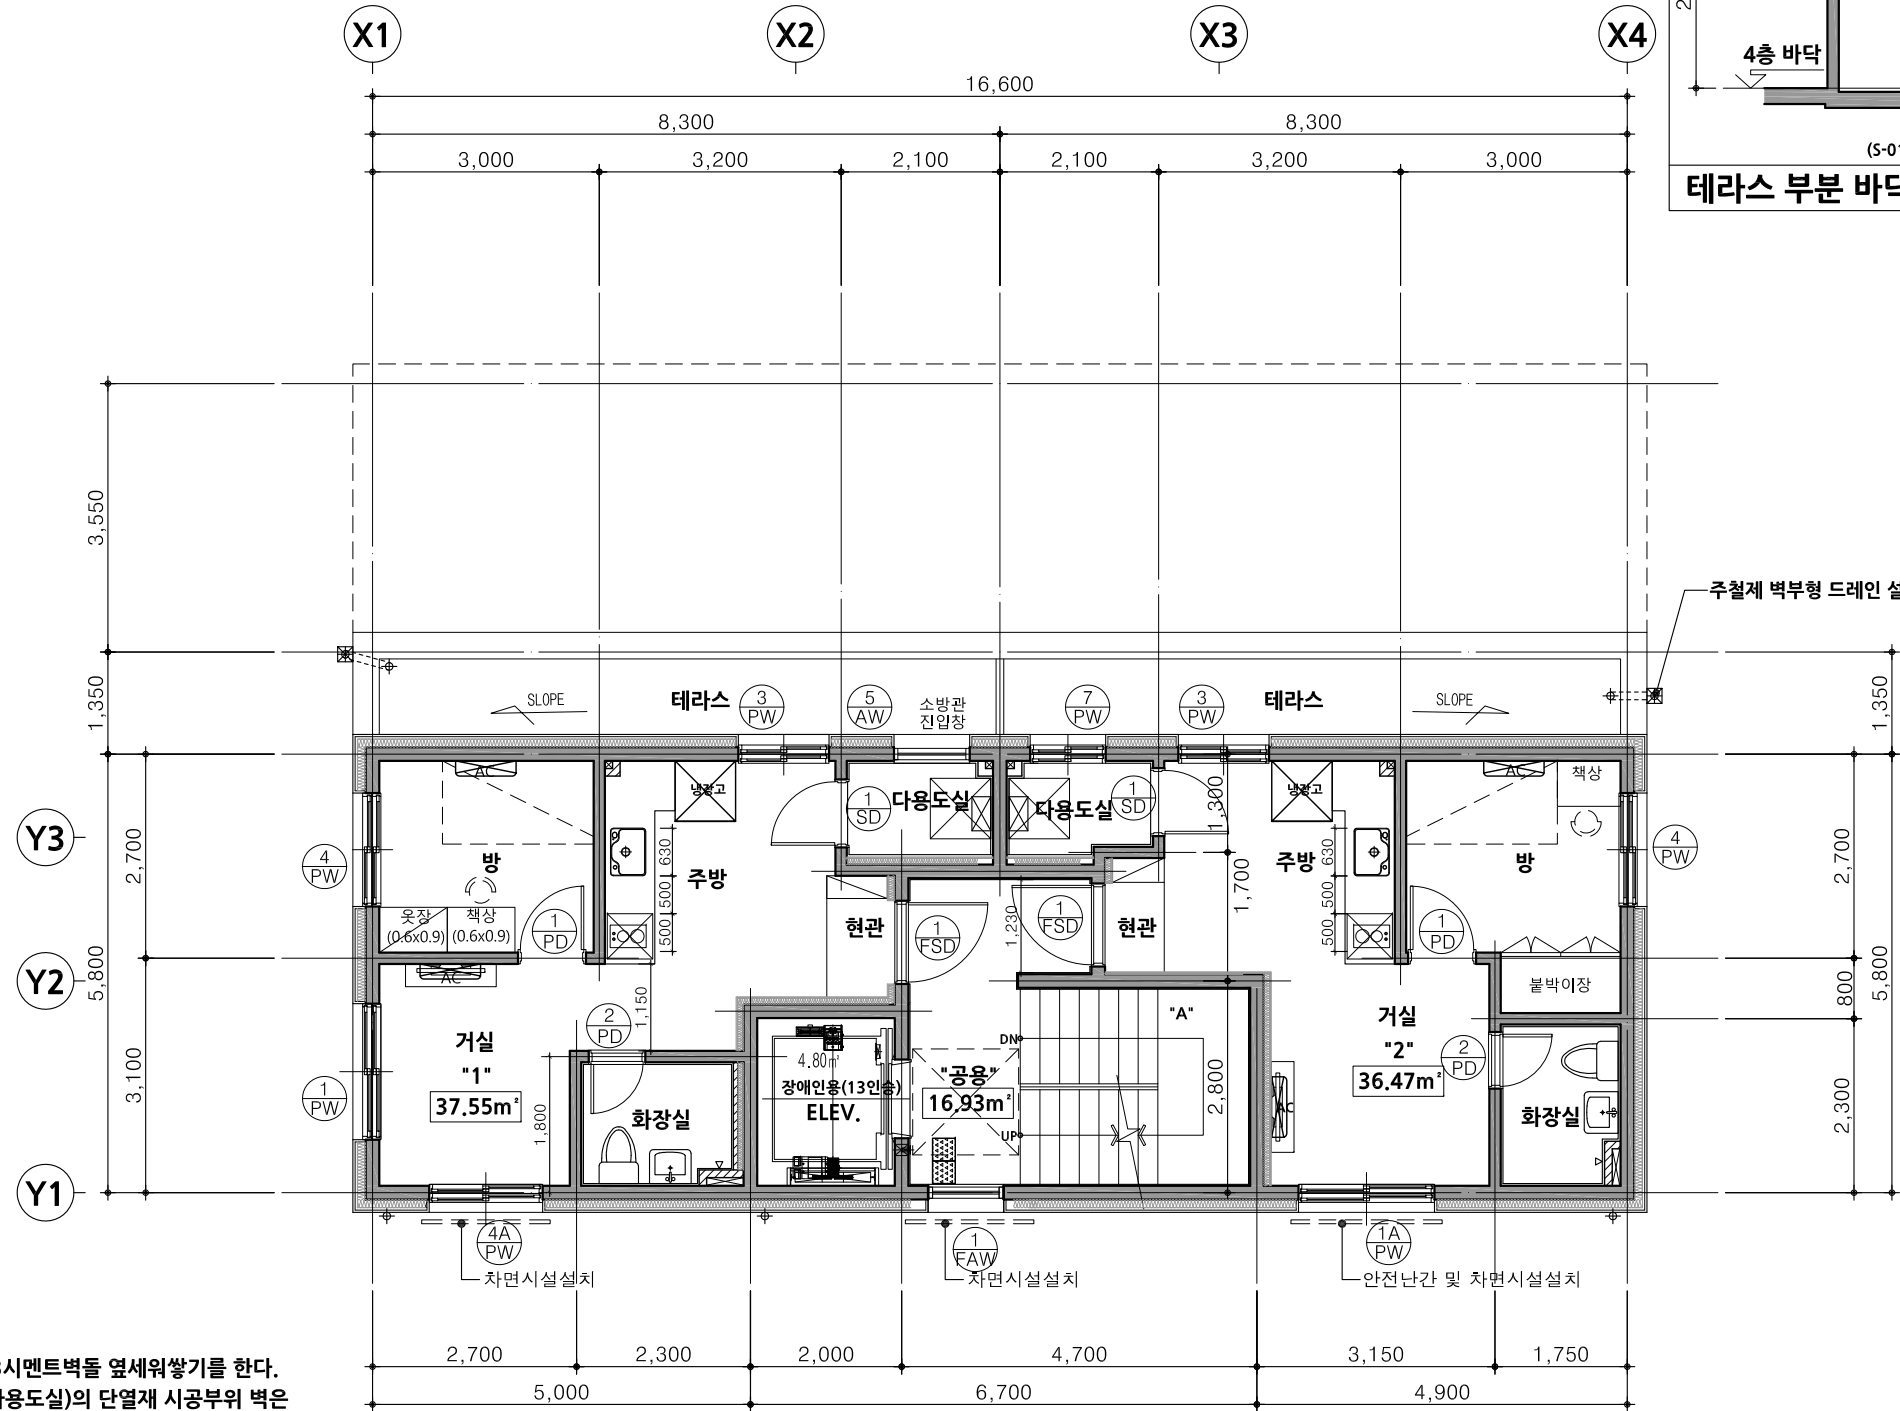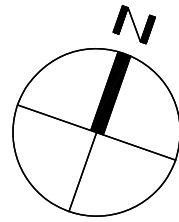

NO.	DATE	REVISION DESCRIPTION

NOTES.


각 세대의 바닥 마감 시공시
소음방지를 위한 층간 바닥
충격을 차단구조기준
(국토부고시)을 만족할 것.

영등포구 대림동
729-7번지
도시형생활주택
(소형주택)
신축공사

건축사사무소
여
현
YEONHEON ARCHITECT & ENGINEERS
PHONE : (02) 2057 - 8005~6



PROJECT NO.	
DRAWN BY.	KIM.K.R
CHECKED BY.	
APPROVED BY.	
DRAWING TITLE	5층 평면도
SCALE.	A3 1/100
DATE.	2023.07.
DRAWING NO.	A - 204
SHEET NO.	

- * NOTE *
- 간접외기에 연접하는 화장실벽은 반드시 0.5B시멘트벽돌 옆세워쌓기를 한다.
 - 간접외기부분(복도 및 소방관진입창 설치된 다용도실)의 단열재 시공부위 벽은 반드시 내수석고보드 시공 후 지정마감재를 시공한다.

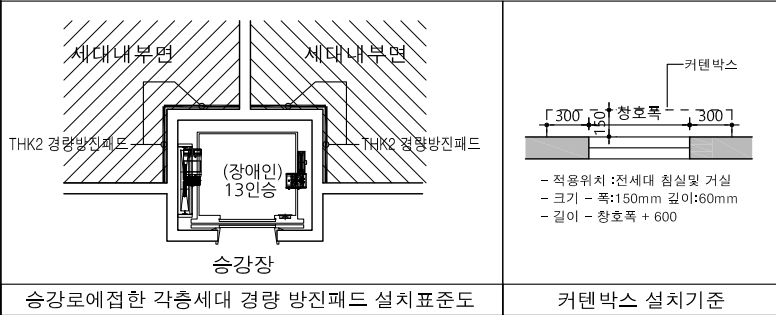


- * 변경내용 *
- A. 2호실 현관 내단열 T10진공단열재로 변경
 - B. 다용도실 도어 OPEN방향 변경
 - C. 소방관 진입창 열관류율 1.0(W/m.k)이하 다용도실 내단열 필요없음
 - D. 다용도실PS워치변경

1 5층 평면도
축척 1:100

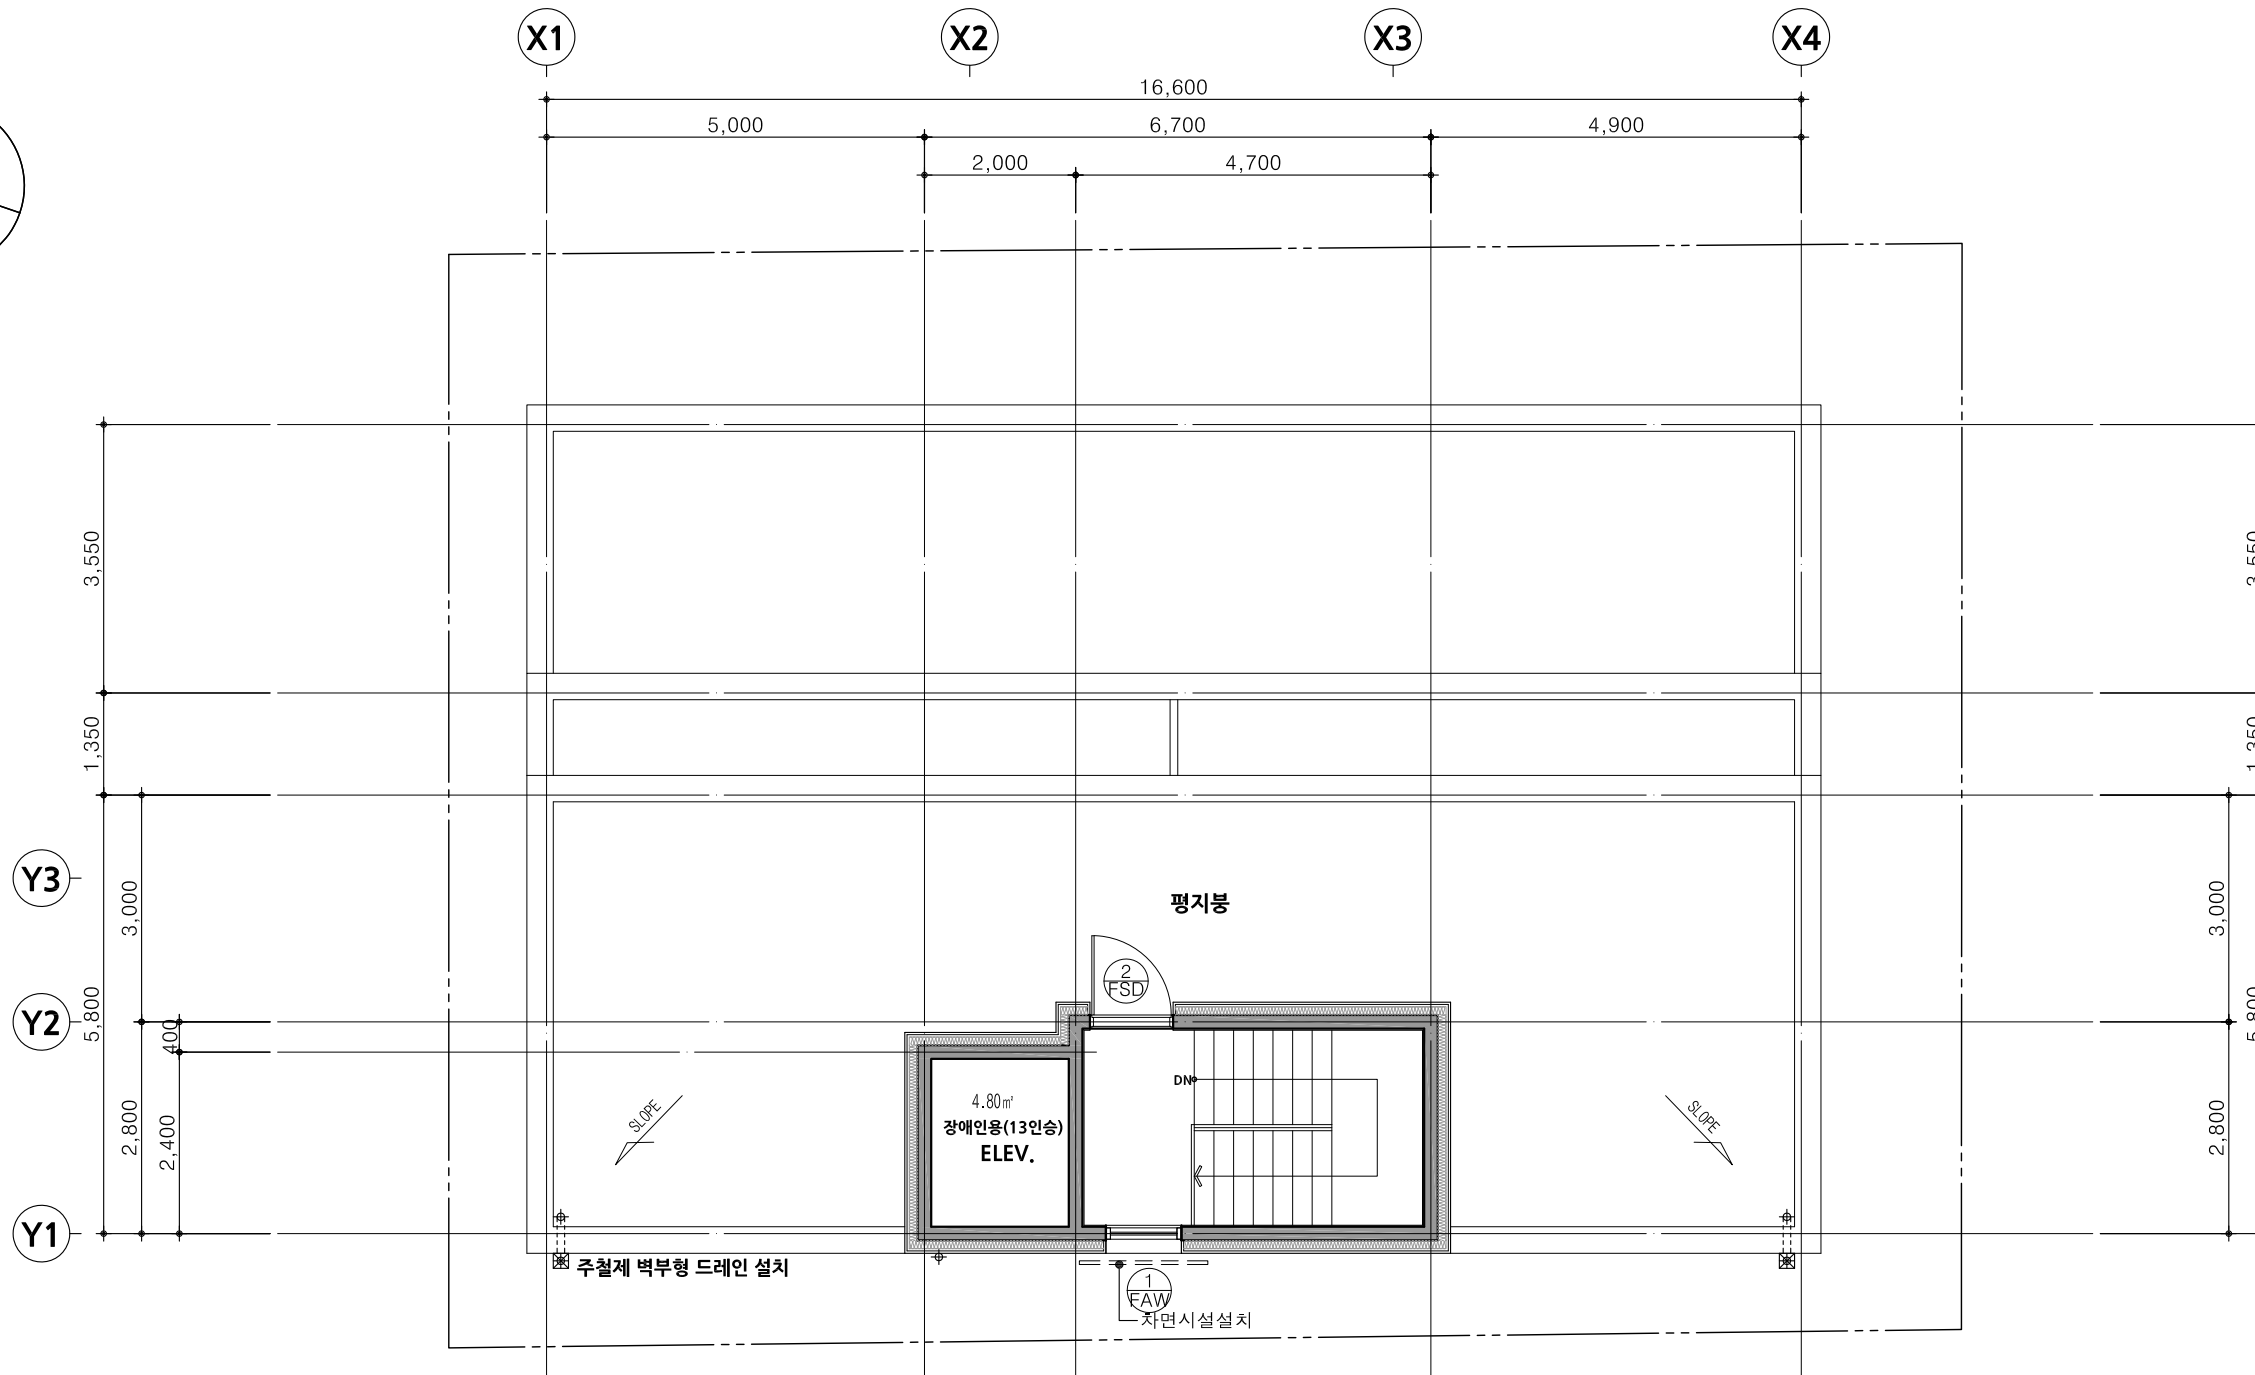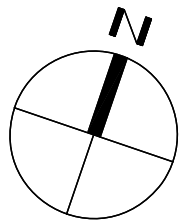

- * NOTE ***
- 간접외기에 연결하는 화장실벽은 반드시 0.5B시멘트벽돌 옆세워쌓기를 한다.
 - 간접외기부분(복도 및 소방관진입장 설치된 다용도실)의 단열재 시공부위 벽은 반드시 내수석고보드 시공 후 지정마감재를 시공한다.

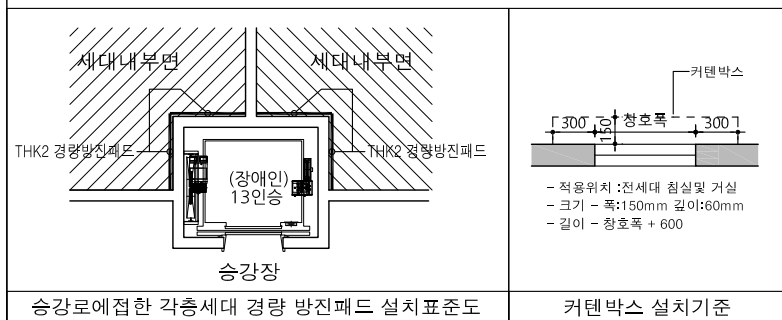

승강로에접한 각층세대 경량 방진패드 설치표준도

커튼박스 설치기준

1 옥탑 평면도
축척 1:100

2 옥탑 지붕 평면도
축척 1:100

NO.	DATE	REVISION DESCRIPTION


NOTES.

영등포구 대림동
729-7번지
도시형생활주택
(소형주택)
신축공사


건축사사무소
여
현
YEOHEON ARCHITECT & ENGINEERS
PHONE : (02) 2057 - 8005~6

PROJECT NO.
DRAWN BY. KIM.K.R
CHECKED BY.
APPROVED BY.
DRAWING TITLE 옥탑평면도 옥탑지붕평면도
SCALE. A3 1/100
DATE. 2022.07.
DRAWING NO. A - 205
SHEET NO.

"1" 

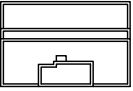

KEY PLAN

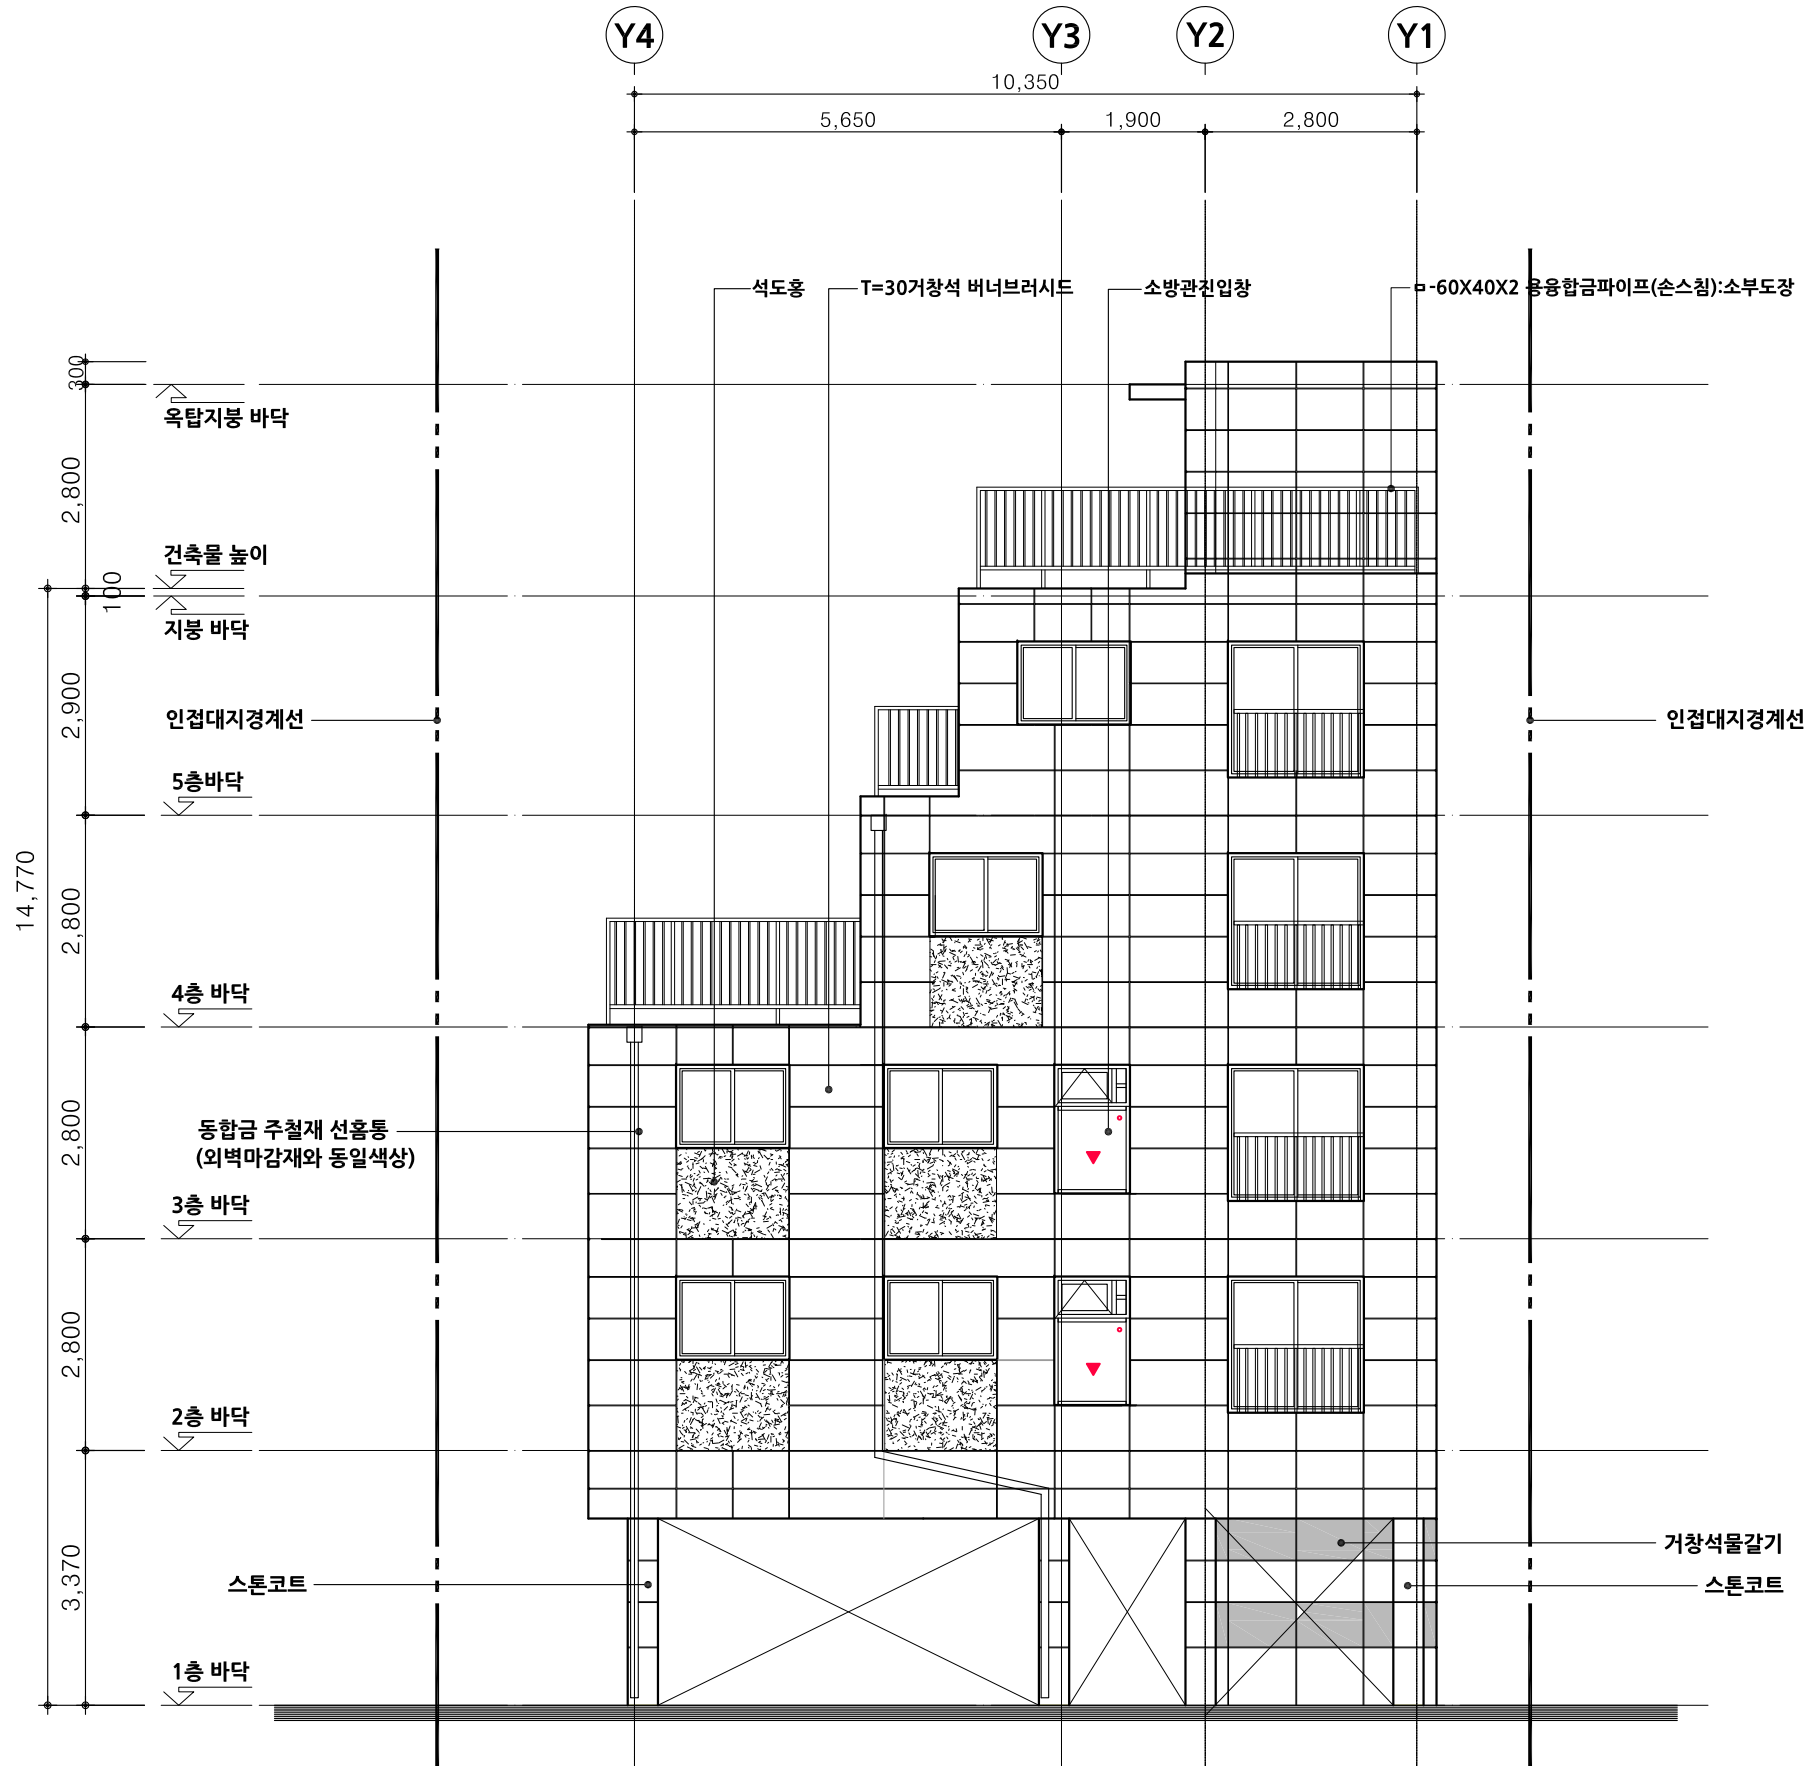

* 외부면 노출 창호프레임 칼라

건본색상
(질은회색)



1 정 면 도(서측면도)
축척 1:100

NO.	DATE	REVISION DESCRIPTION


NOTES.

영등포구 대림동
729-7번지
도시형생활주택
(소형주택)
신축공사

 건축사사무소
여현

YEOHEON ARCHITECT & ENGINEERS
PHONE : (02) 2057 - 8005~6

PROJECT NO.
DRAWN BY. KIM,K,R
CHECKED BY.
APPROVED BY.
DRAWING TITLE 정면도(서측면도)
SCALE. A3 1/100
DATE. 2022.07.
DRAWING NO. A - 301
SHEET NO.

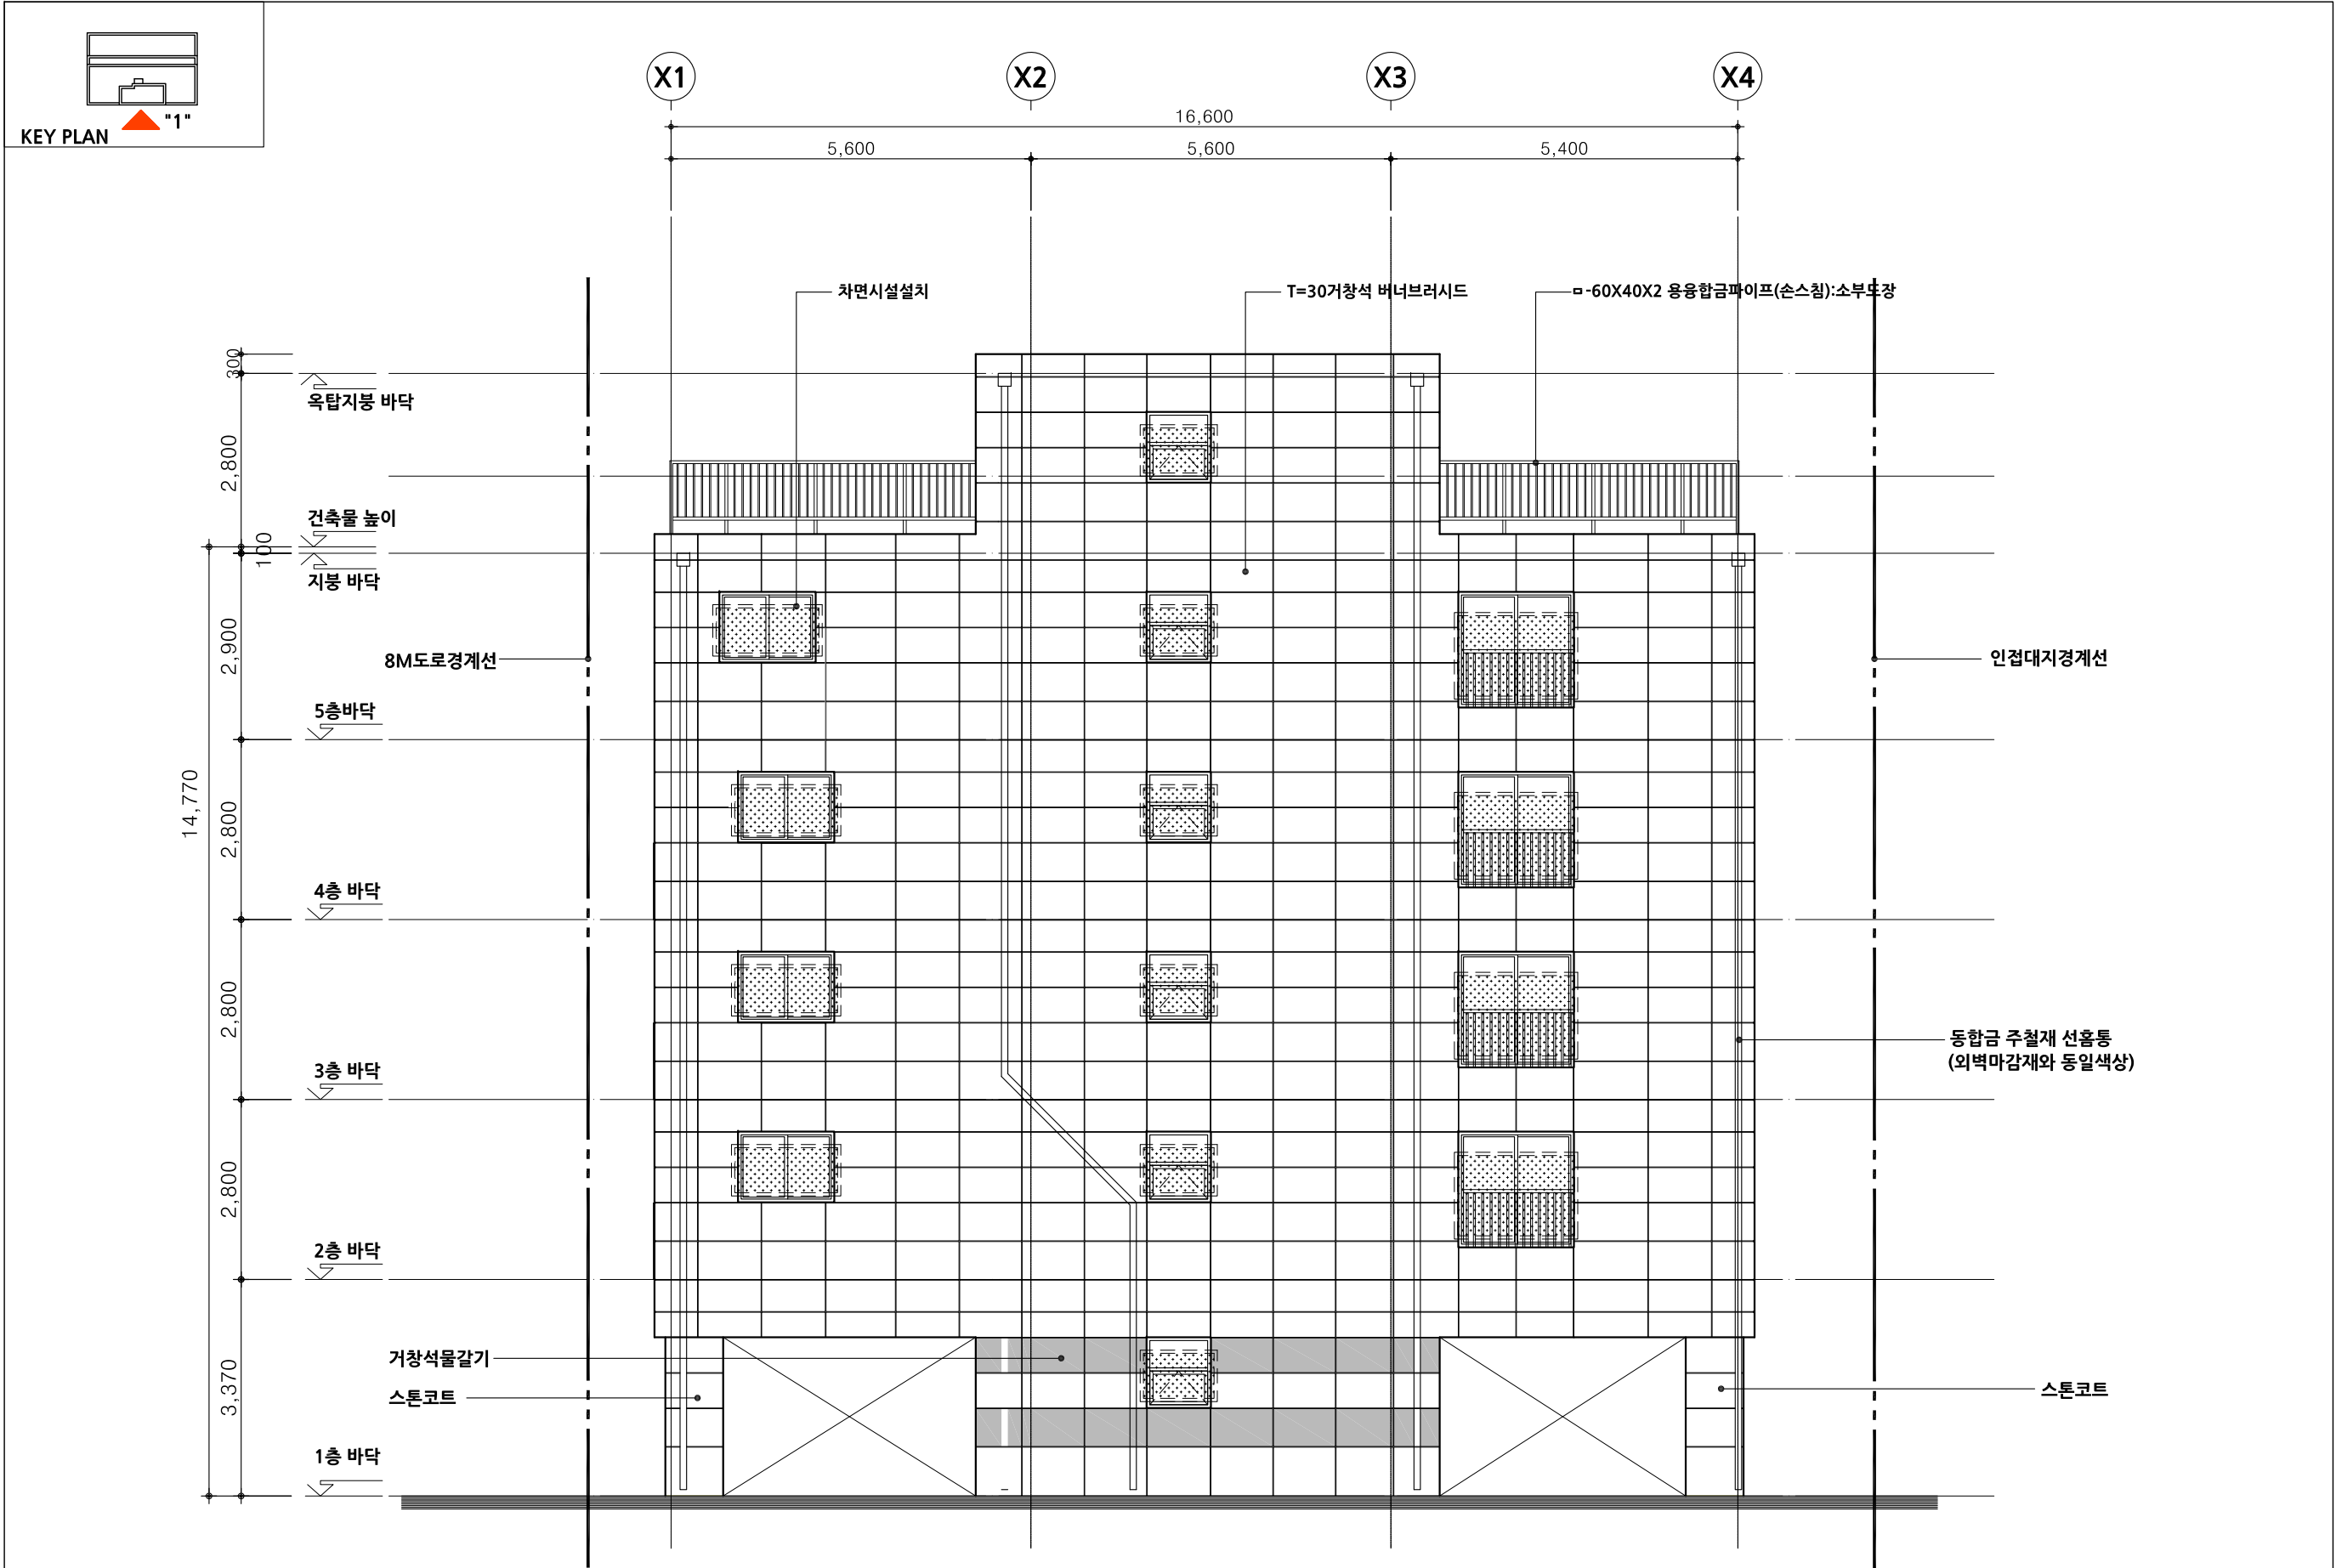

* 외부면 노출 창호프레임 칼라

건본색상 (질은회색)	
----------------	--

1 우측면도(남측면도)
축척 1:100

NO.	DATE	REVISION DESCRIPTION


NOTES.

차면시설설치


영등포구 대림동
729-7번지
도시형생활주택
(소형주택)
신축공사

건축사사무소
여
현
YEOHEON ARCHITECT & ENGINEERS
PHONE : (02) 2057 - 8005~6

PROJECT NO.
DRAWN BY. KIM.K.R
CHECKED BY.
APPROVED BY.
DRAWING TITLE 우측면도(남측면도)
SCALE. A3 1/100
DATE. 2022.07.
DRAWING NO. A - 302
SHEET NO.

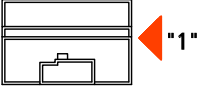

KEY PLAN

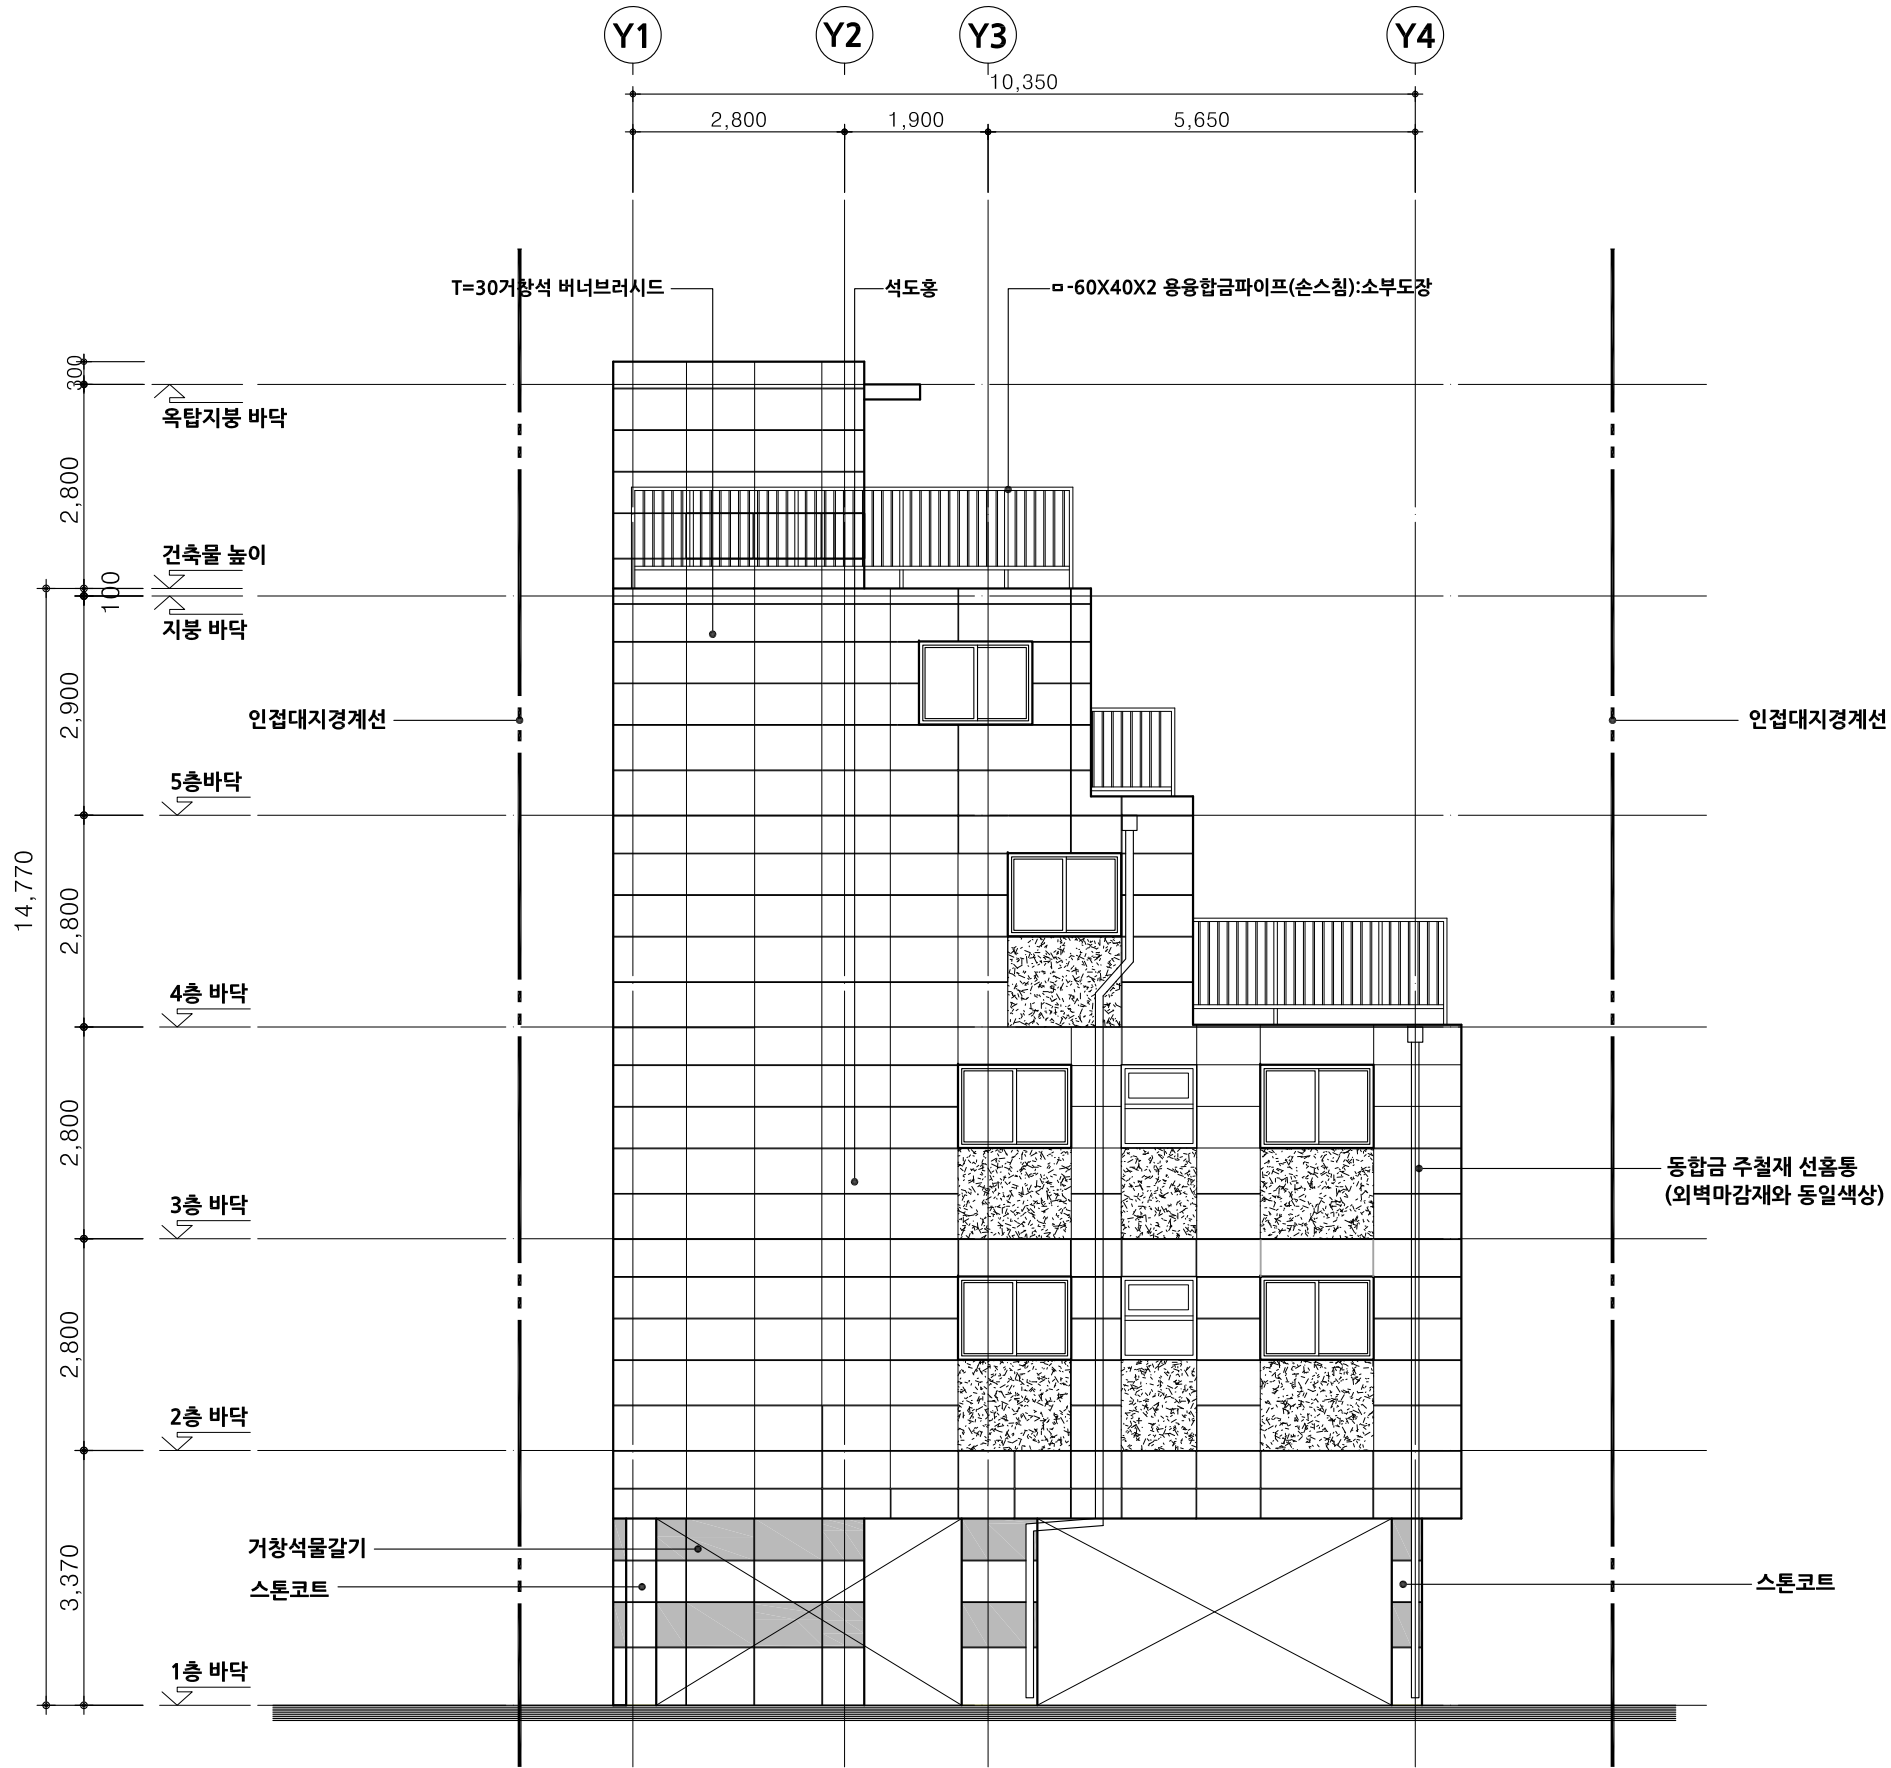

* 외부면 노출 창호프레임 칼라

건본색상
(질은회색)



1 배면도(동측면도)
축척 1:100

NO.	DATE	REVISION DESCRIPTION

NOTES.

영등포구 대림동
729-7번지
도시형생활주택
(소형주택)
신축공사



건축사사무소
여
현
YEOHEON ARCHITECT & ENGINEERS
PHONE : (02) 2057 - 8005~6

PROJECT NO.
DRAWN BY. KIM.K.R
CHECKED BY.
APPROVED BY.
DRAWING TITLE 배면도(동측면도)
SCALE. A3 1/100
DATE. 2022.07.
DRAWING NO. A - 304
SHEET NO.