


PROJECT TITLE
영등포구 대림동
685-24
도시형 생활주택 계획


NOTE

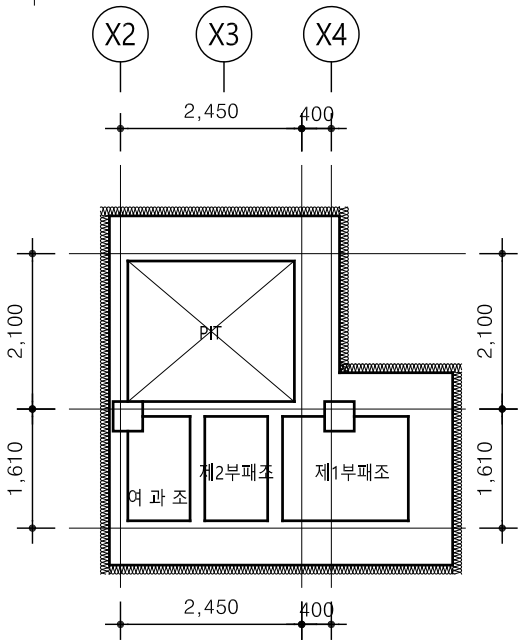

EV PIT 평면도

NOTE

구분	내 용
(방)	방화유리자동문
(+)	단독경보형감지기(연기식)
(실)	실외기
(우)	우편함 설치

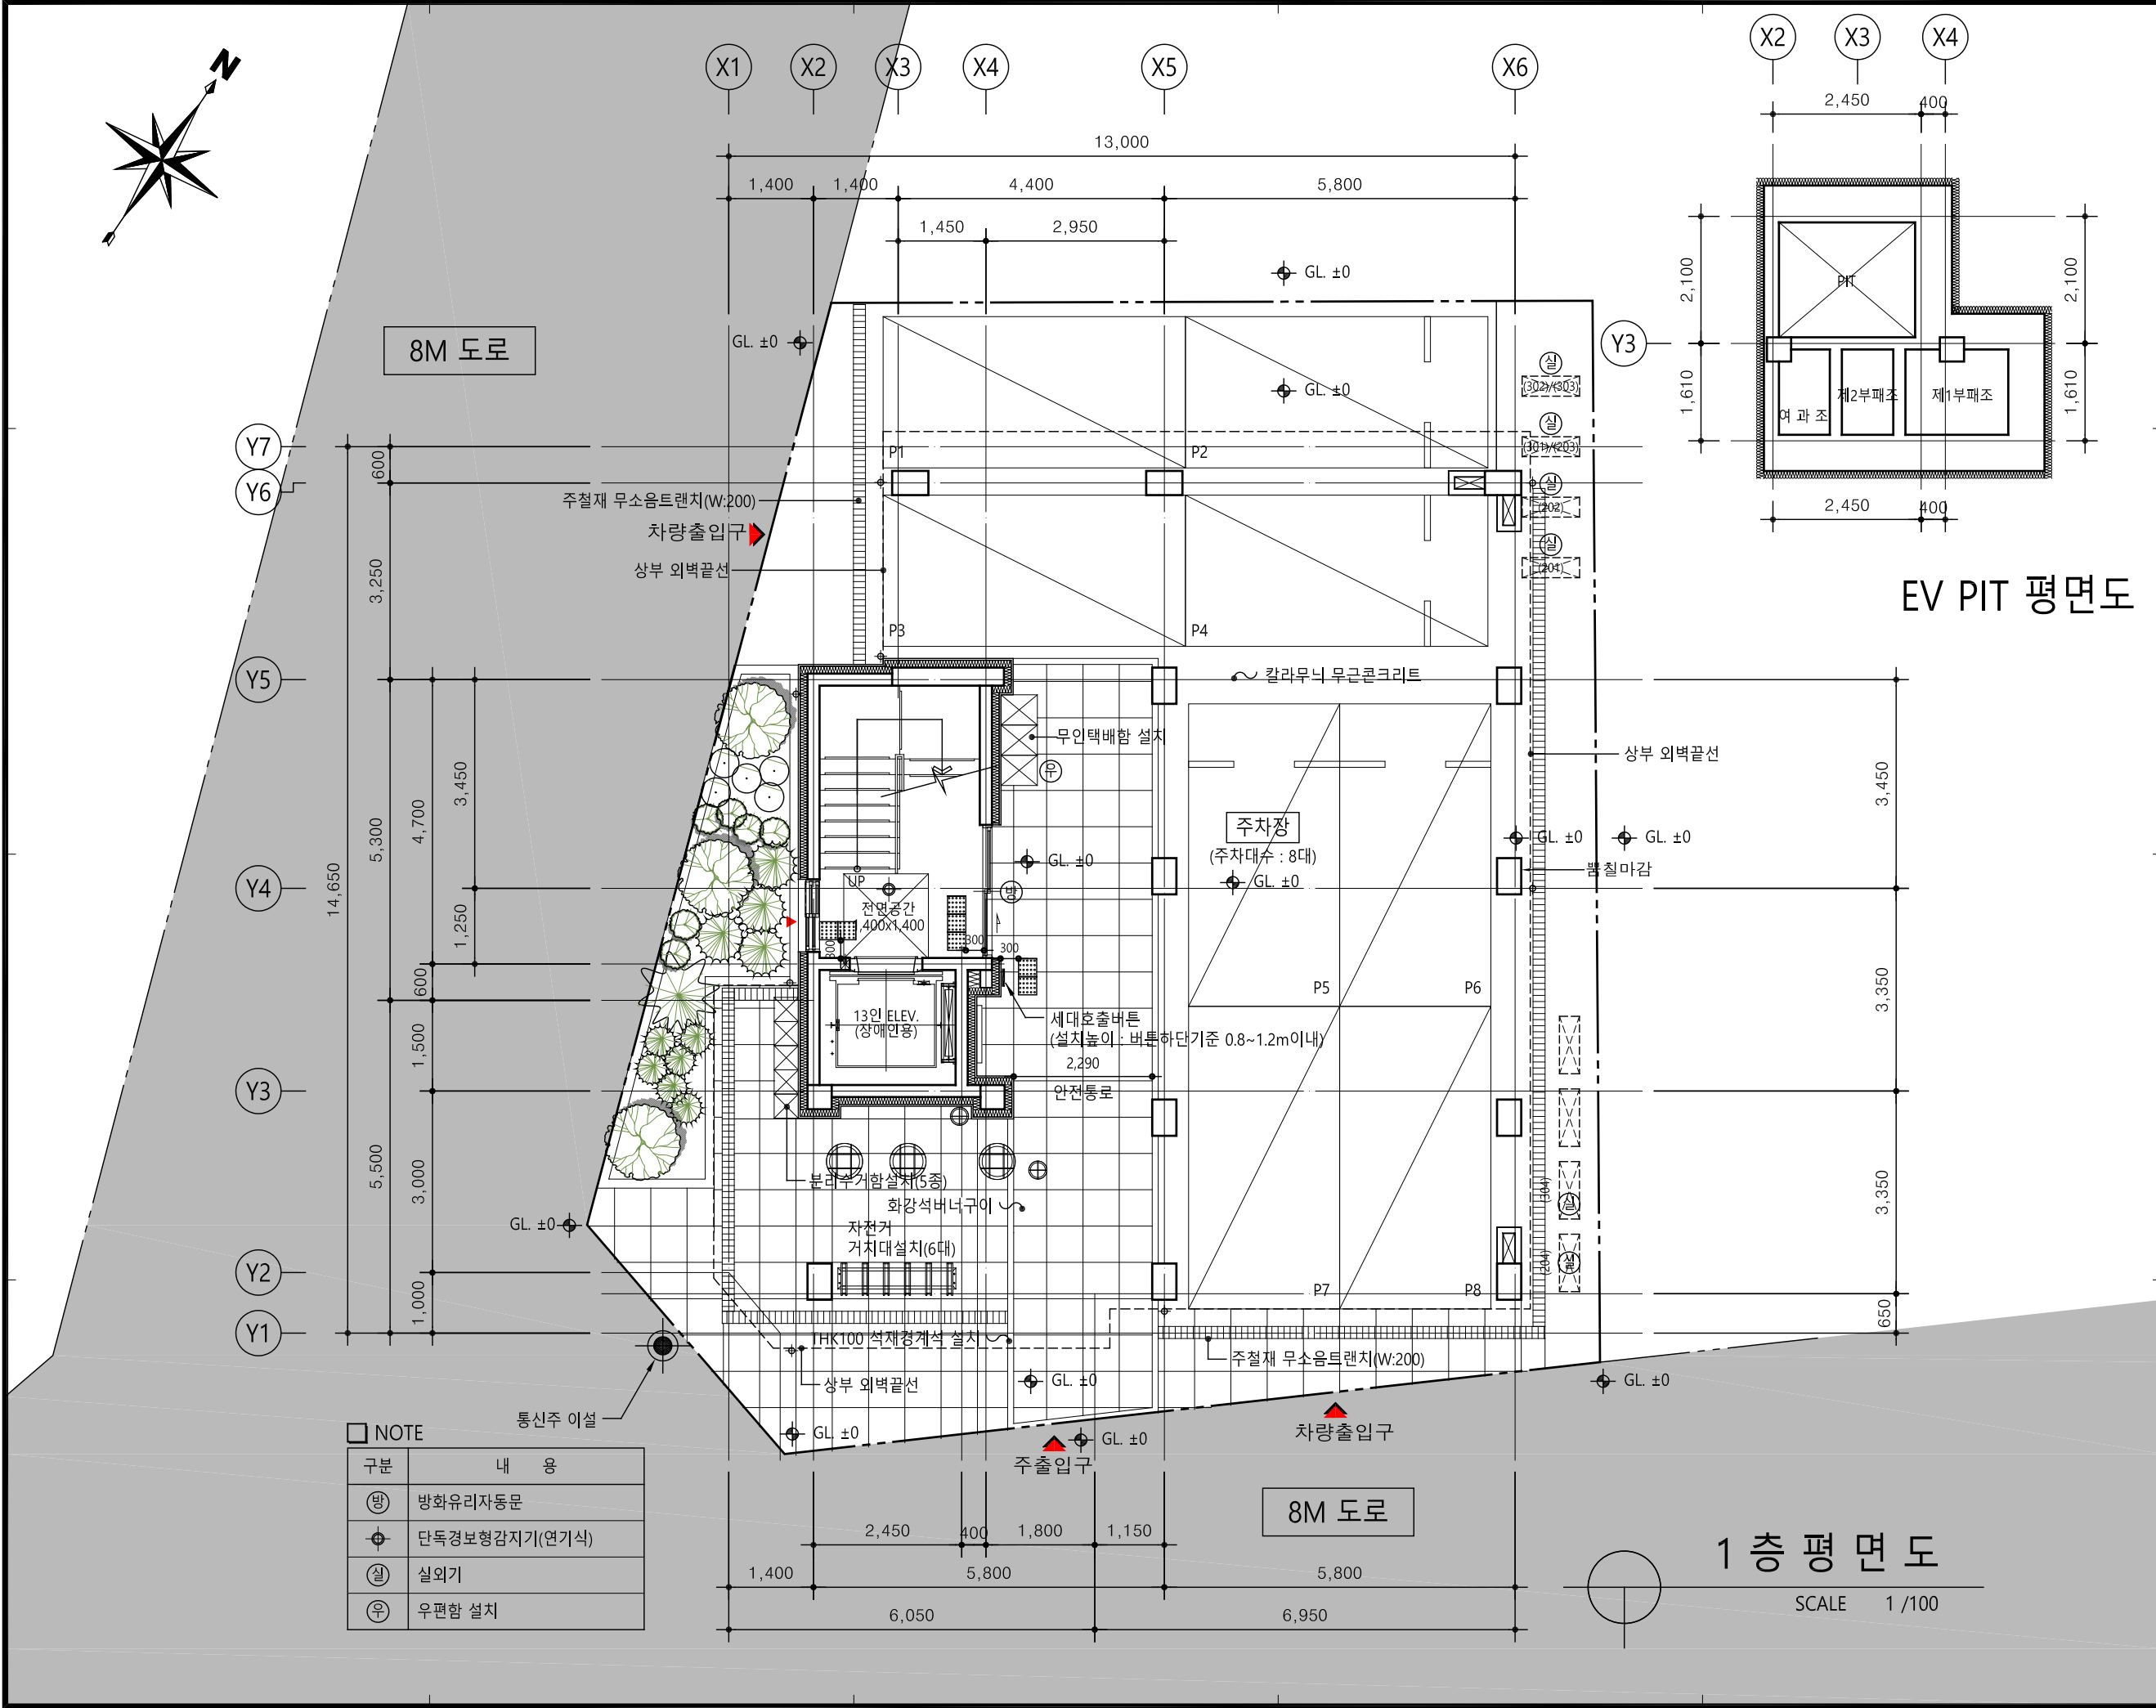

1층 평면도






SCALE 1/100

△			
△			
△			
△			
△			
△			
△			
△			
△			
NO.	DATE	DESCRIPTION	APP.

REVISION

(주)정다움 건축사사무소
JEONGDAUM ARCHITECTURE COMPANY
TEL. 02-438-3700
TEL. 010-8911-0941
FAX. 02-438-3800

DRAWING TITLE	
1층 평면도	
DRAWN BY	PROJECT NO.
CHECKED BY	SCALE
APPROVED BY	DATE
DRAWING FILE NAME	
DWG NO.	

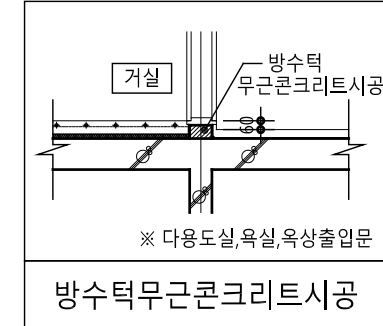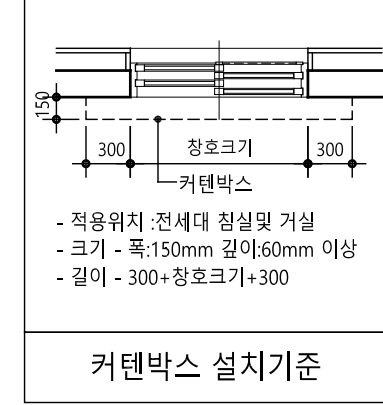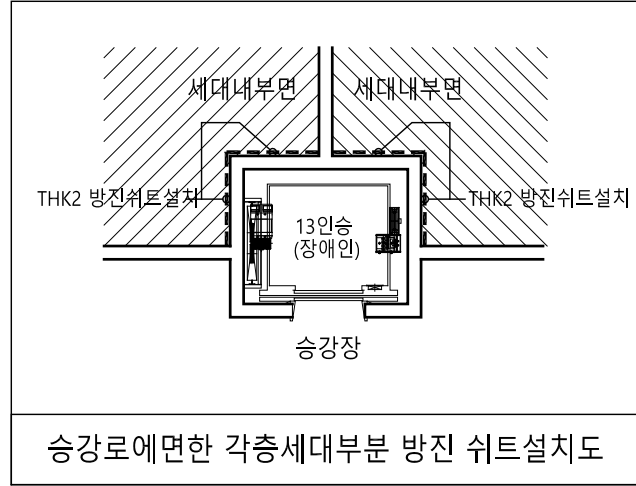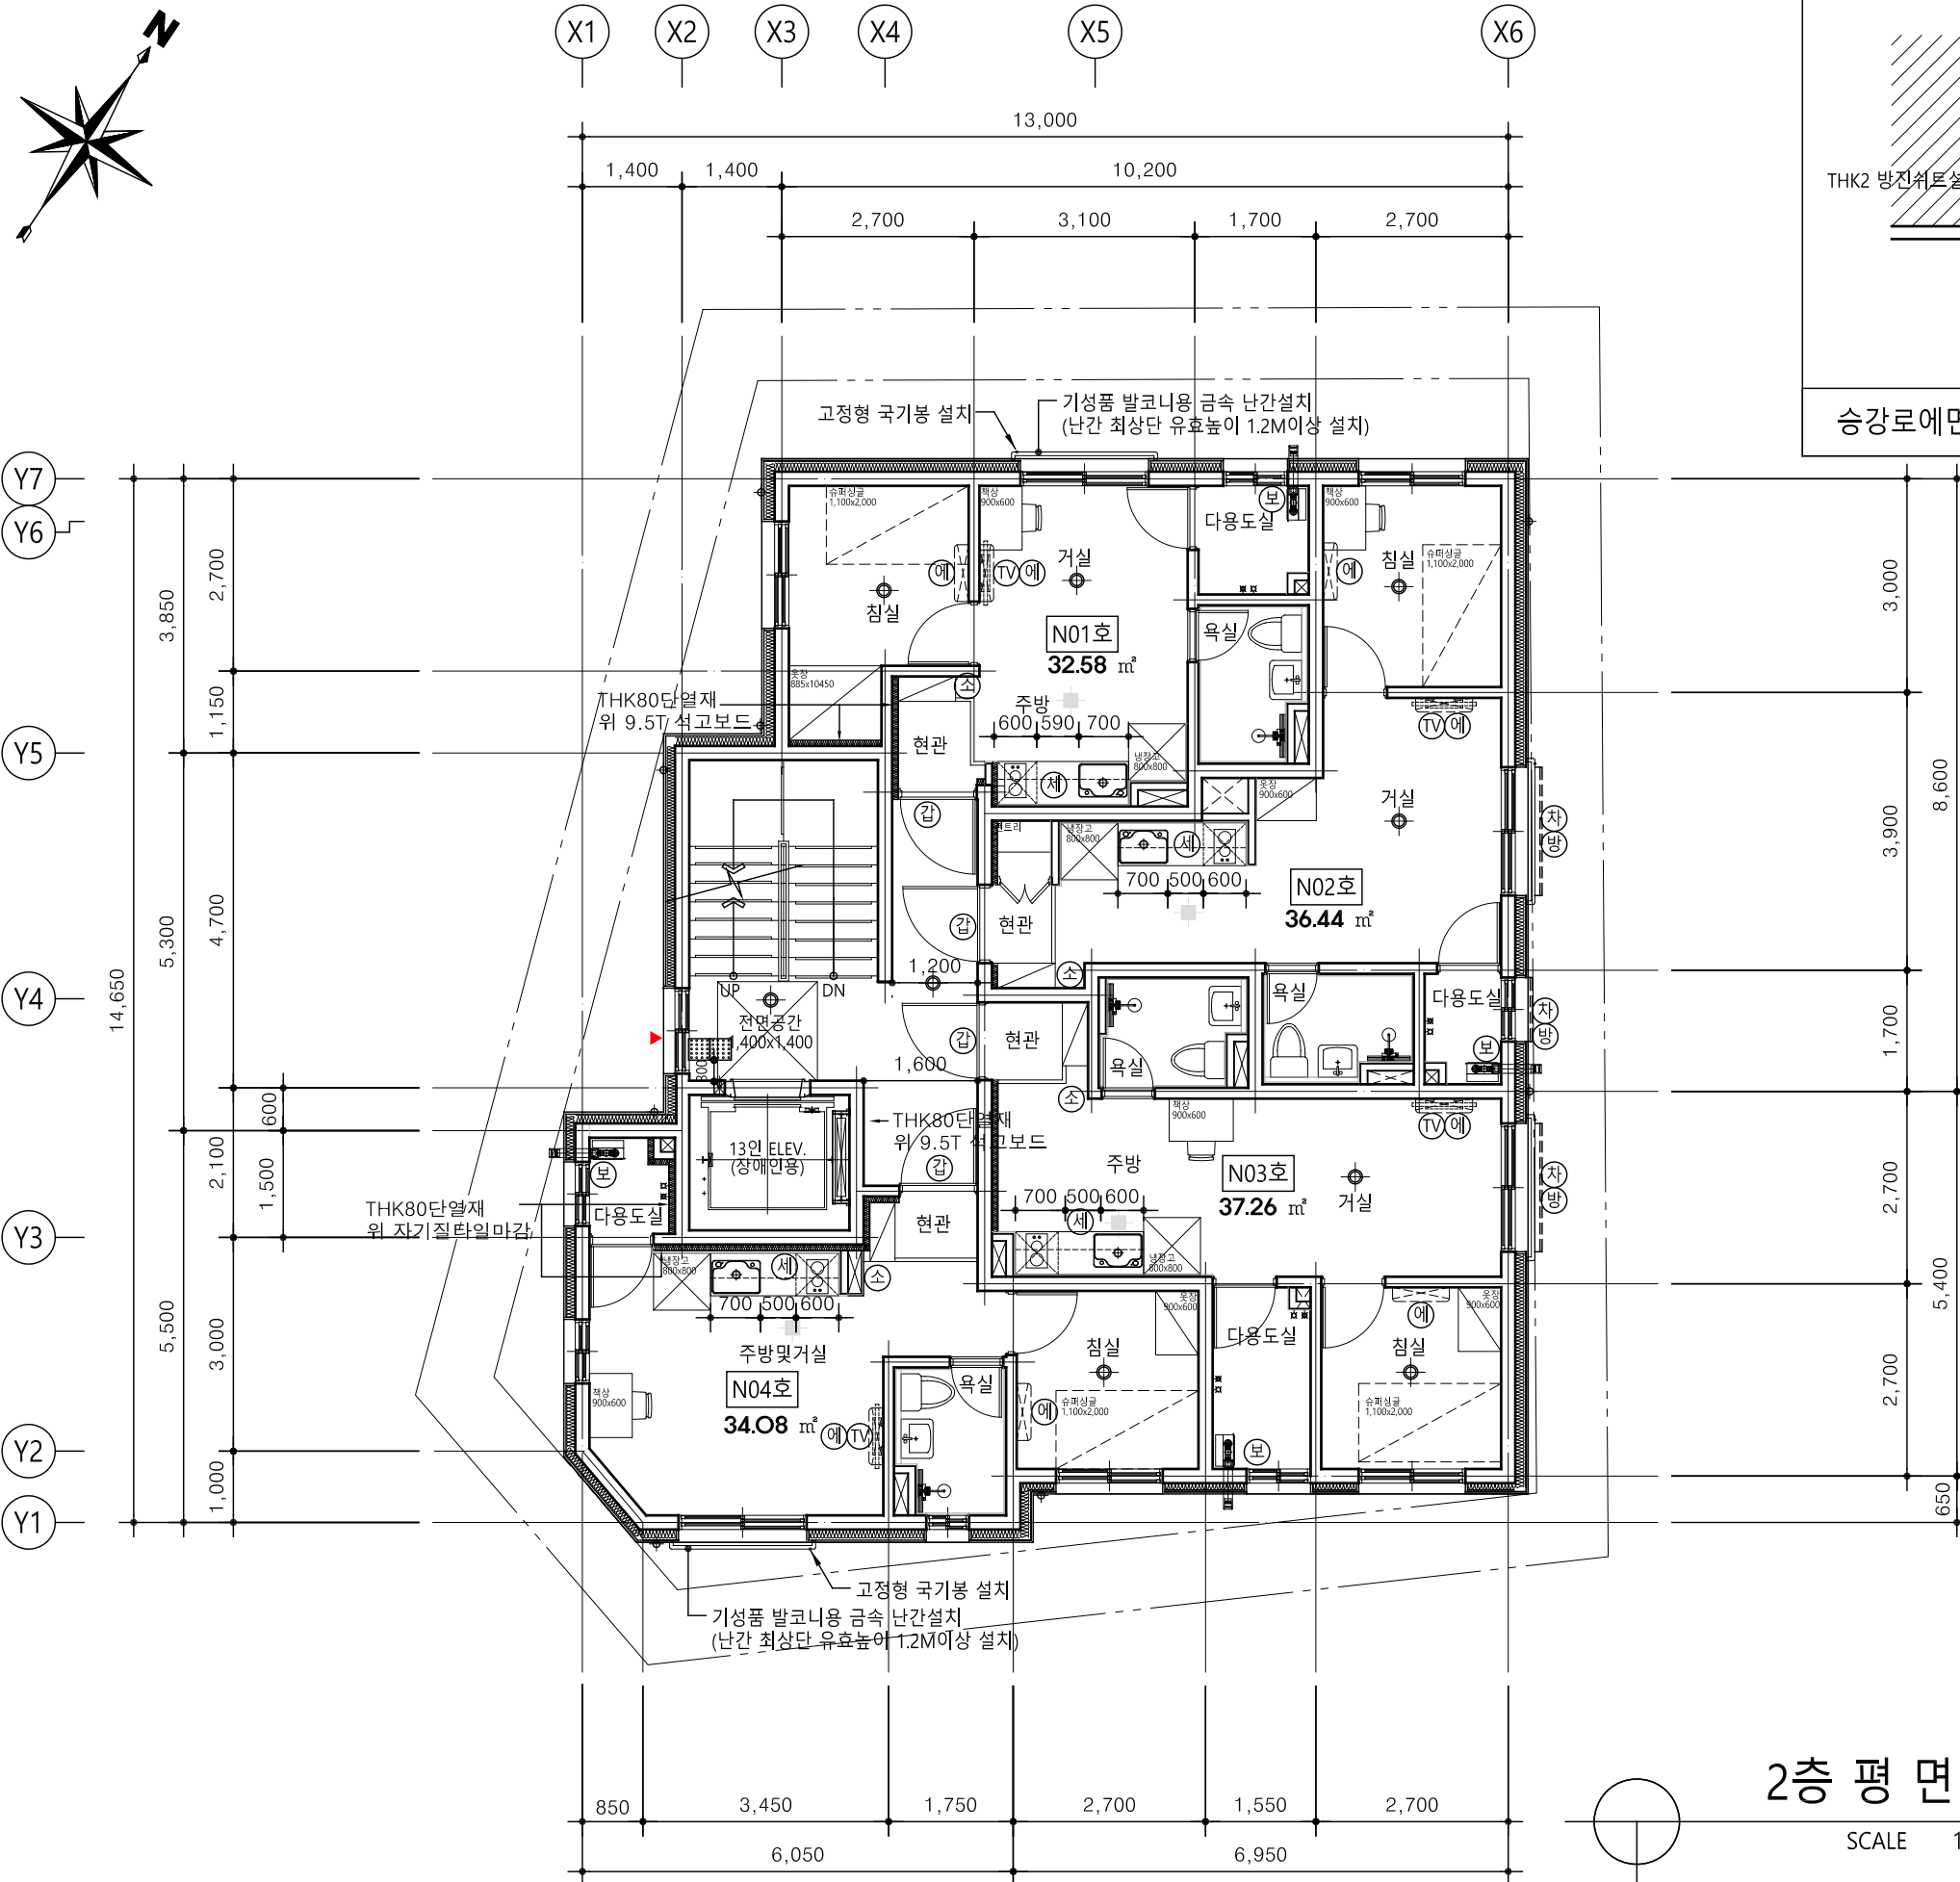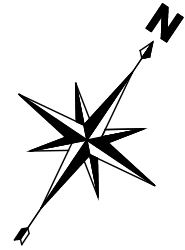






NOTE	
구분	내 용
①	갑종방화문(60분방화문)
②	단독경보형감지기(연기식)
③	단독경보형감지기(열감지)
④	분말 소화기(ABC급 3.3Kg)
⑤	보일러(친환경 1등급)
⑥	차면시설 설치
⑦	방화유리(비차열 20분이상)
⑧	소방진입창 설치
⑨	벽걸이 에어컨
⑩	벽걸이 TV
⑪	빌트인 세탁기

2층 평 면 도
SCALE 1 / 100

PROJECT TITLE
영등포구 대림동
685-24
도시형 생활주택 계획

NOTE

△			
△			
△			
△			
△			
△			
△			
△			
NO.	DATE	DESCRIPTION	APP.
REVISION			
(주)정다움 건축사사무소 JEONGDAUM ARCHITECTURE COMPANY TEL. 02-438-3700 TEL. 010-8911-0941 FAX. 02-438-3800			
DRAWING TITLE 2층 평 면 도			
DRAWN BY	PROJECT NO.		
CHECKED BY	SCALE 1/100		
APPROVED BY	DATE 2023.09.		
DRAWING FILE NAME			
DWG NO. A-102			

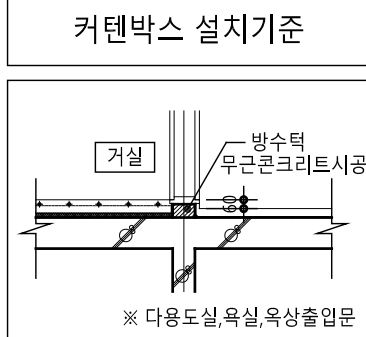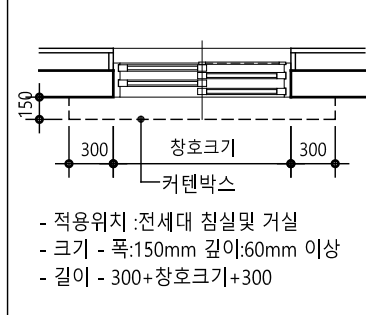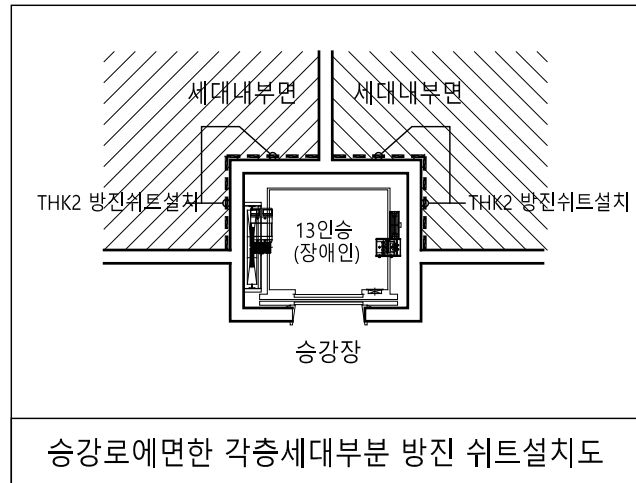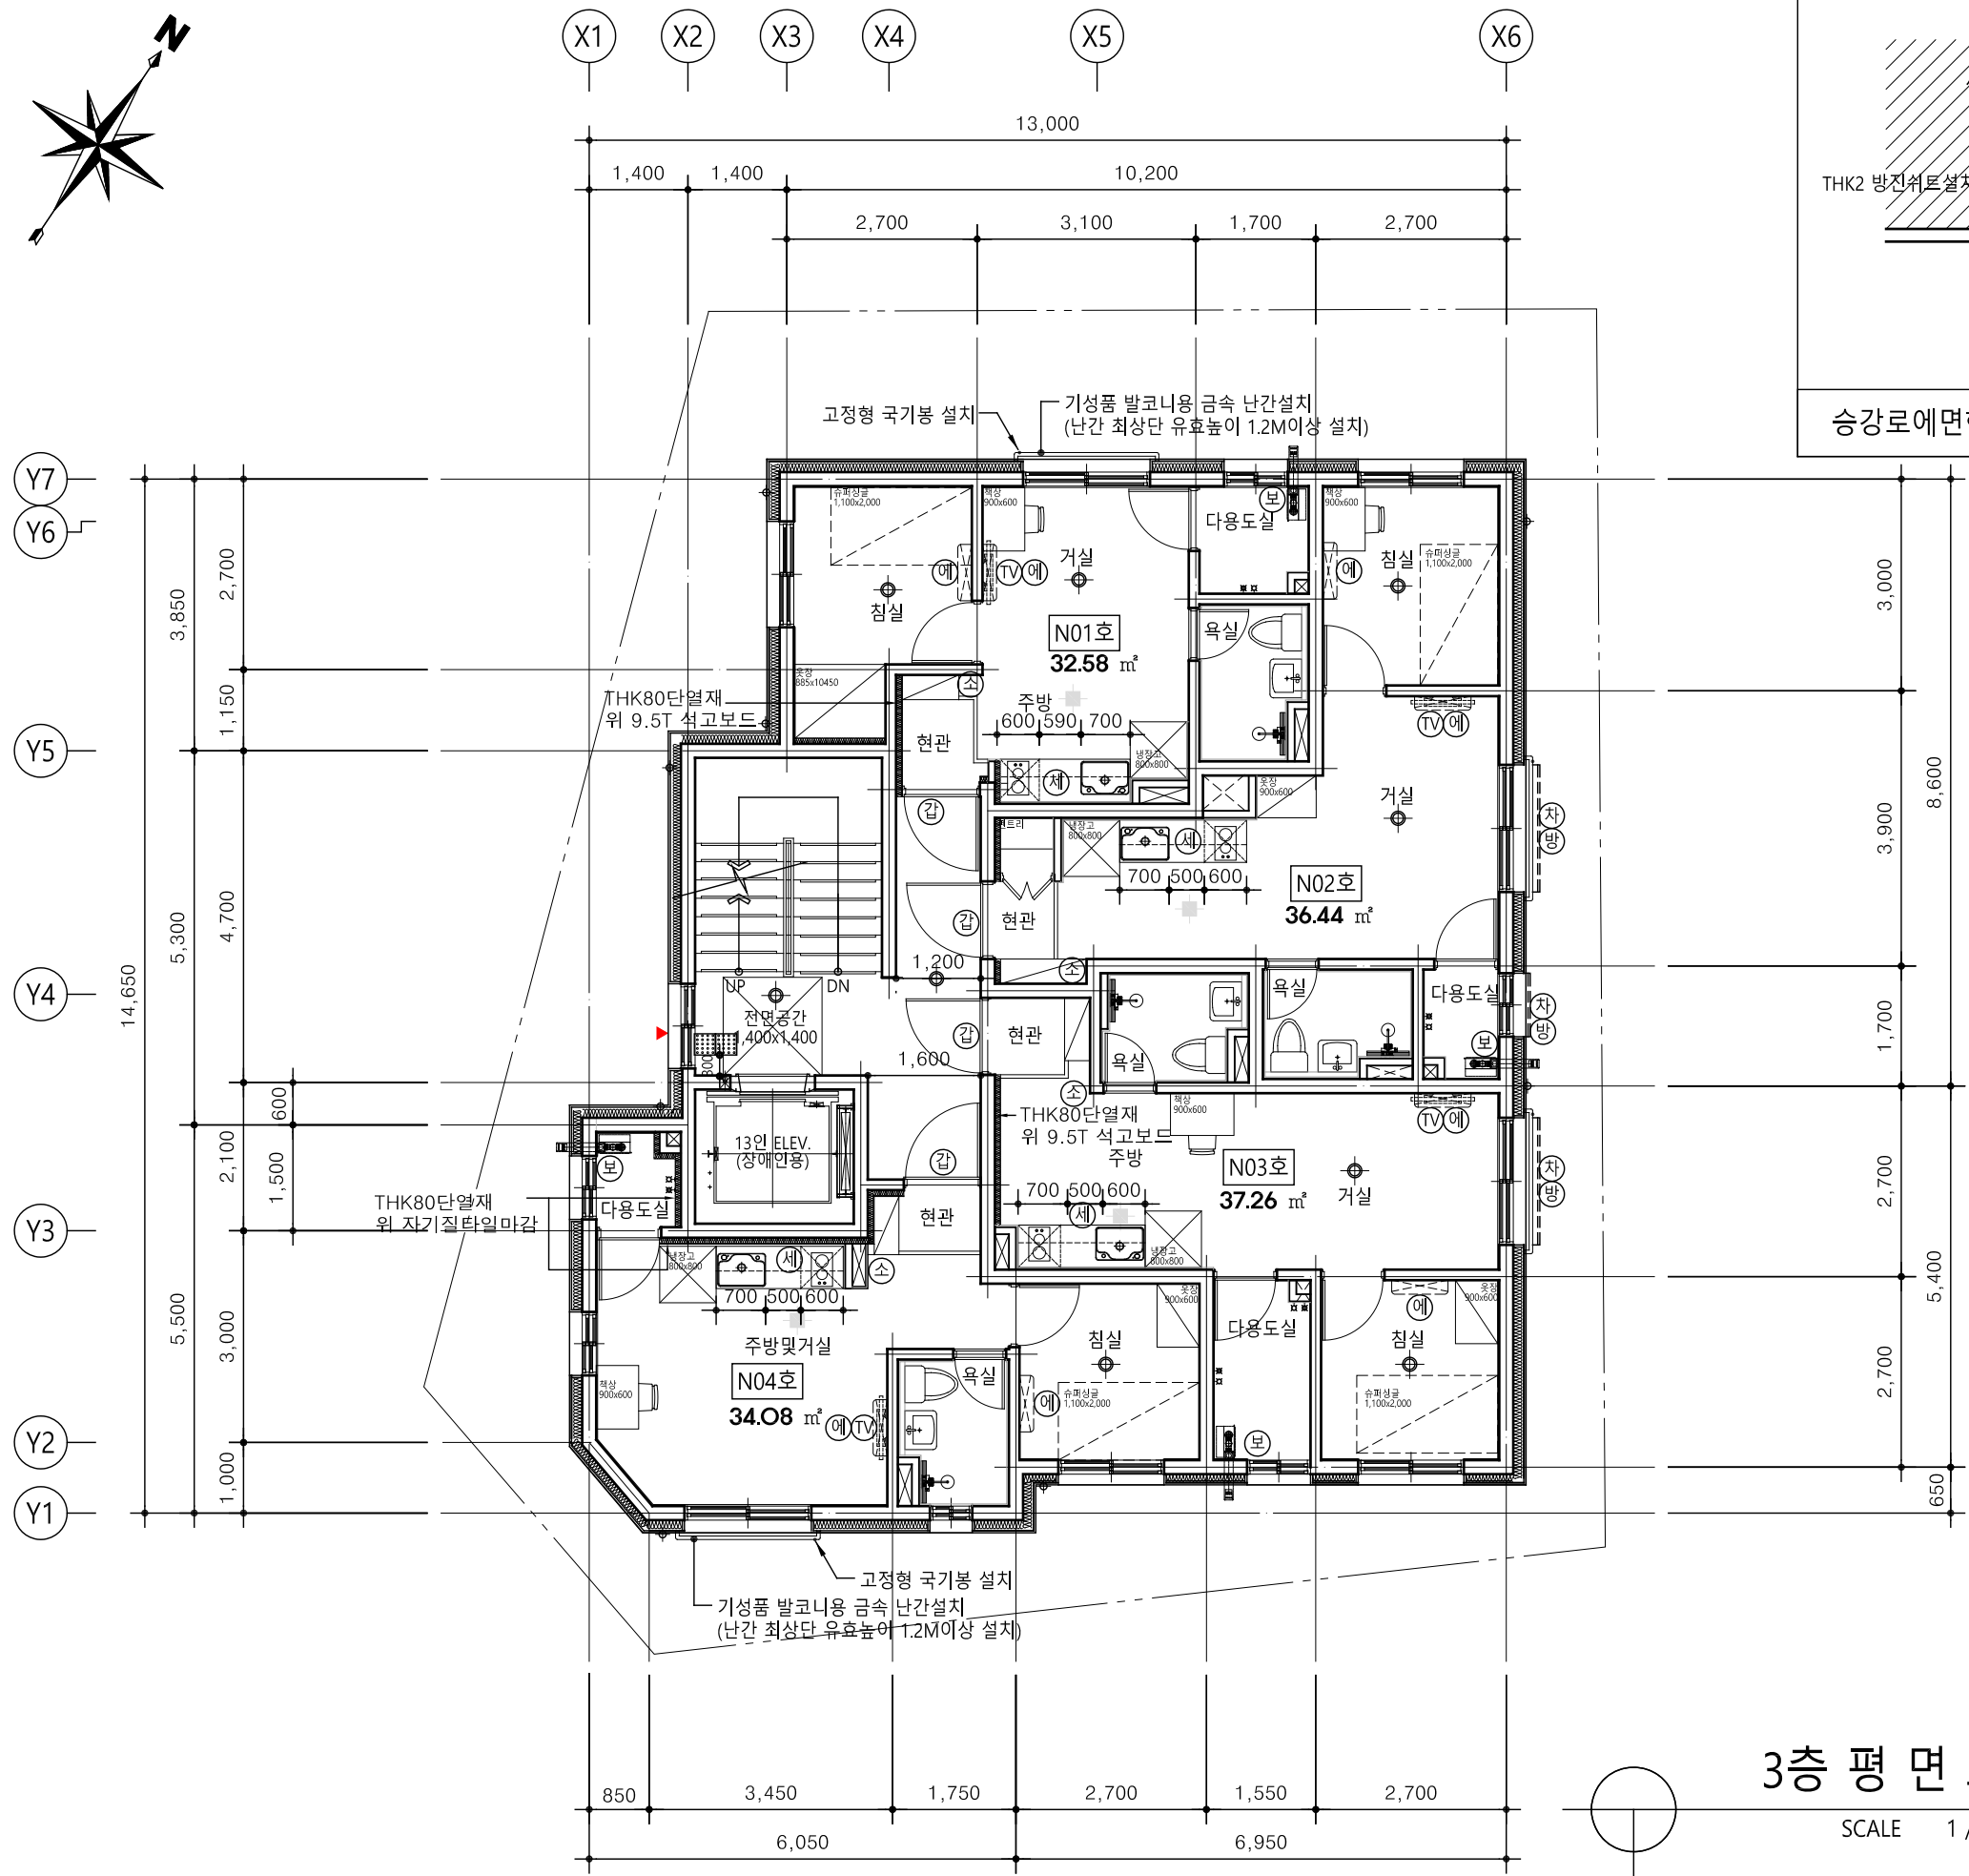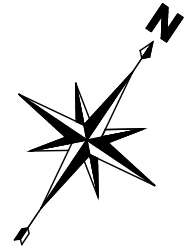

방수벽무근콘크리트시공

NOTE	
구분	내 용
①	갑종방화문(60분방화문)
②	단독경보형감지기(연기식)
③	단독경보형감지기(열감지)
④	분말 소화기(ABC급 3.3Kg)
⑤	보일러(친환경 1등급)
⑥	차면시설 설치
⑦	방화유리(비차열 20분이상)
⑧	소방진입창 설치
⑨	벽걸이 에어컨
⑩	벽걸이 TV
⑪	빌트인 세탁기

3층 평 면 도
SCALE 1 / 100






PROJECT TITLE

영등포구 대림동
685-24
도시형 생활주택 계획

NOTE

△						
△						
△						
△						
△						
△						
△						
△						
NO.	DATE	DESCRIPTION	APP.			
REVISION						
(주)정다움 건축사사무소 JEONGDAUM ARCHITECTURE COMPANY TEL. 02-438-3700 TEL. 010-8911-0941 FAX. 02-438-3800 DRAWING TITLE 3층 평 면 도						
DRAWN BY	PROJECT NO.					
CHECKED BY	SCALE					
APPROVED BY	DATE					
DRAWING FILE NAME						
DWG NO.						

A-102

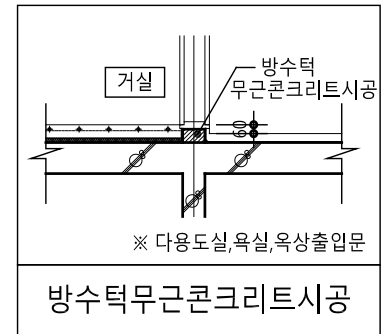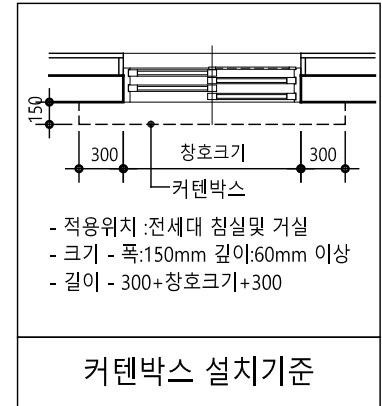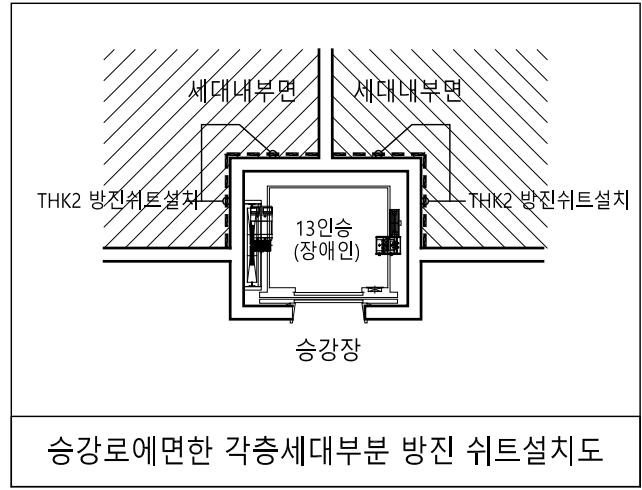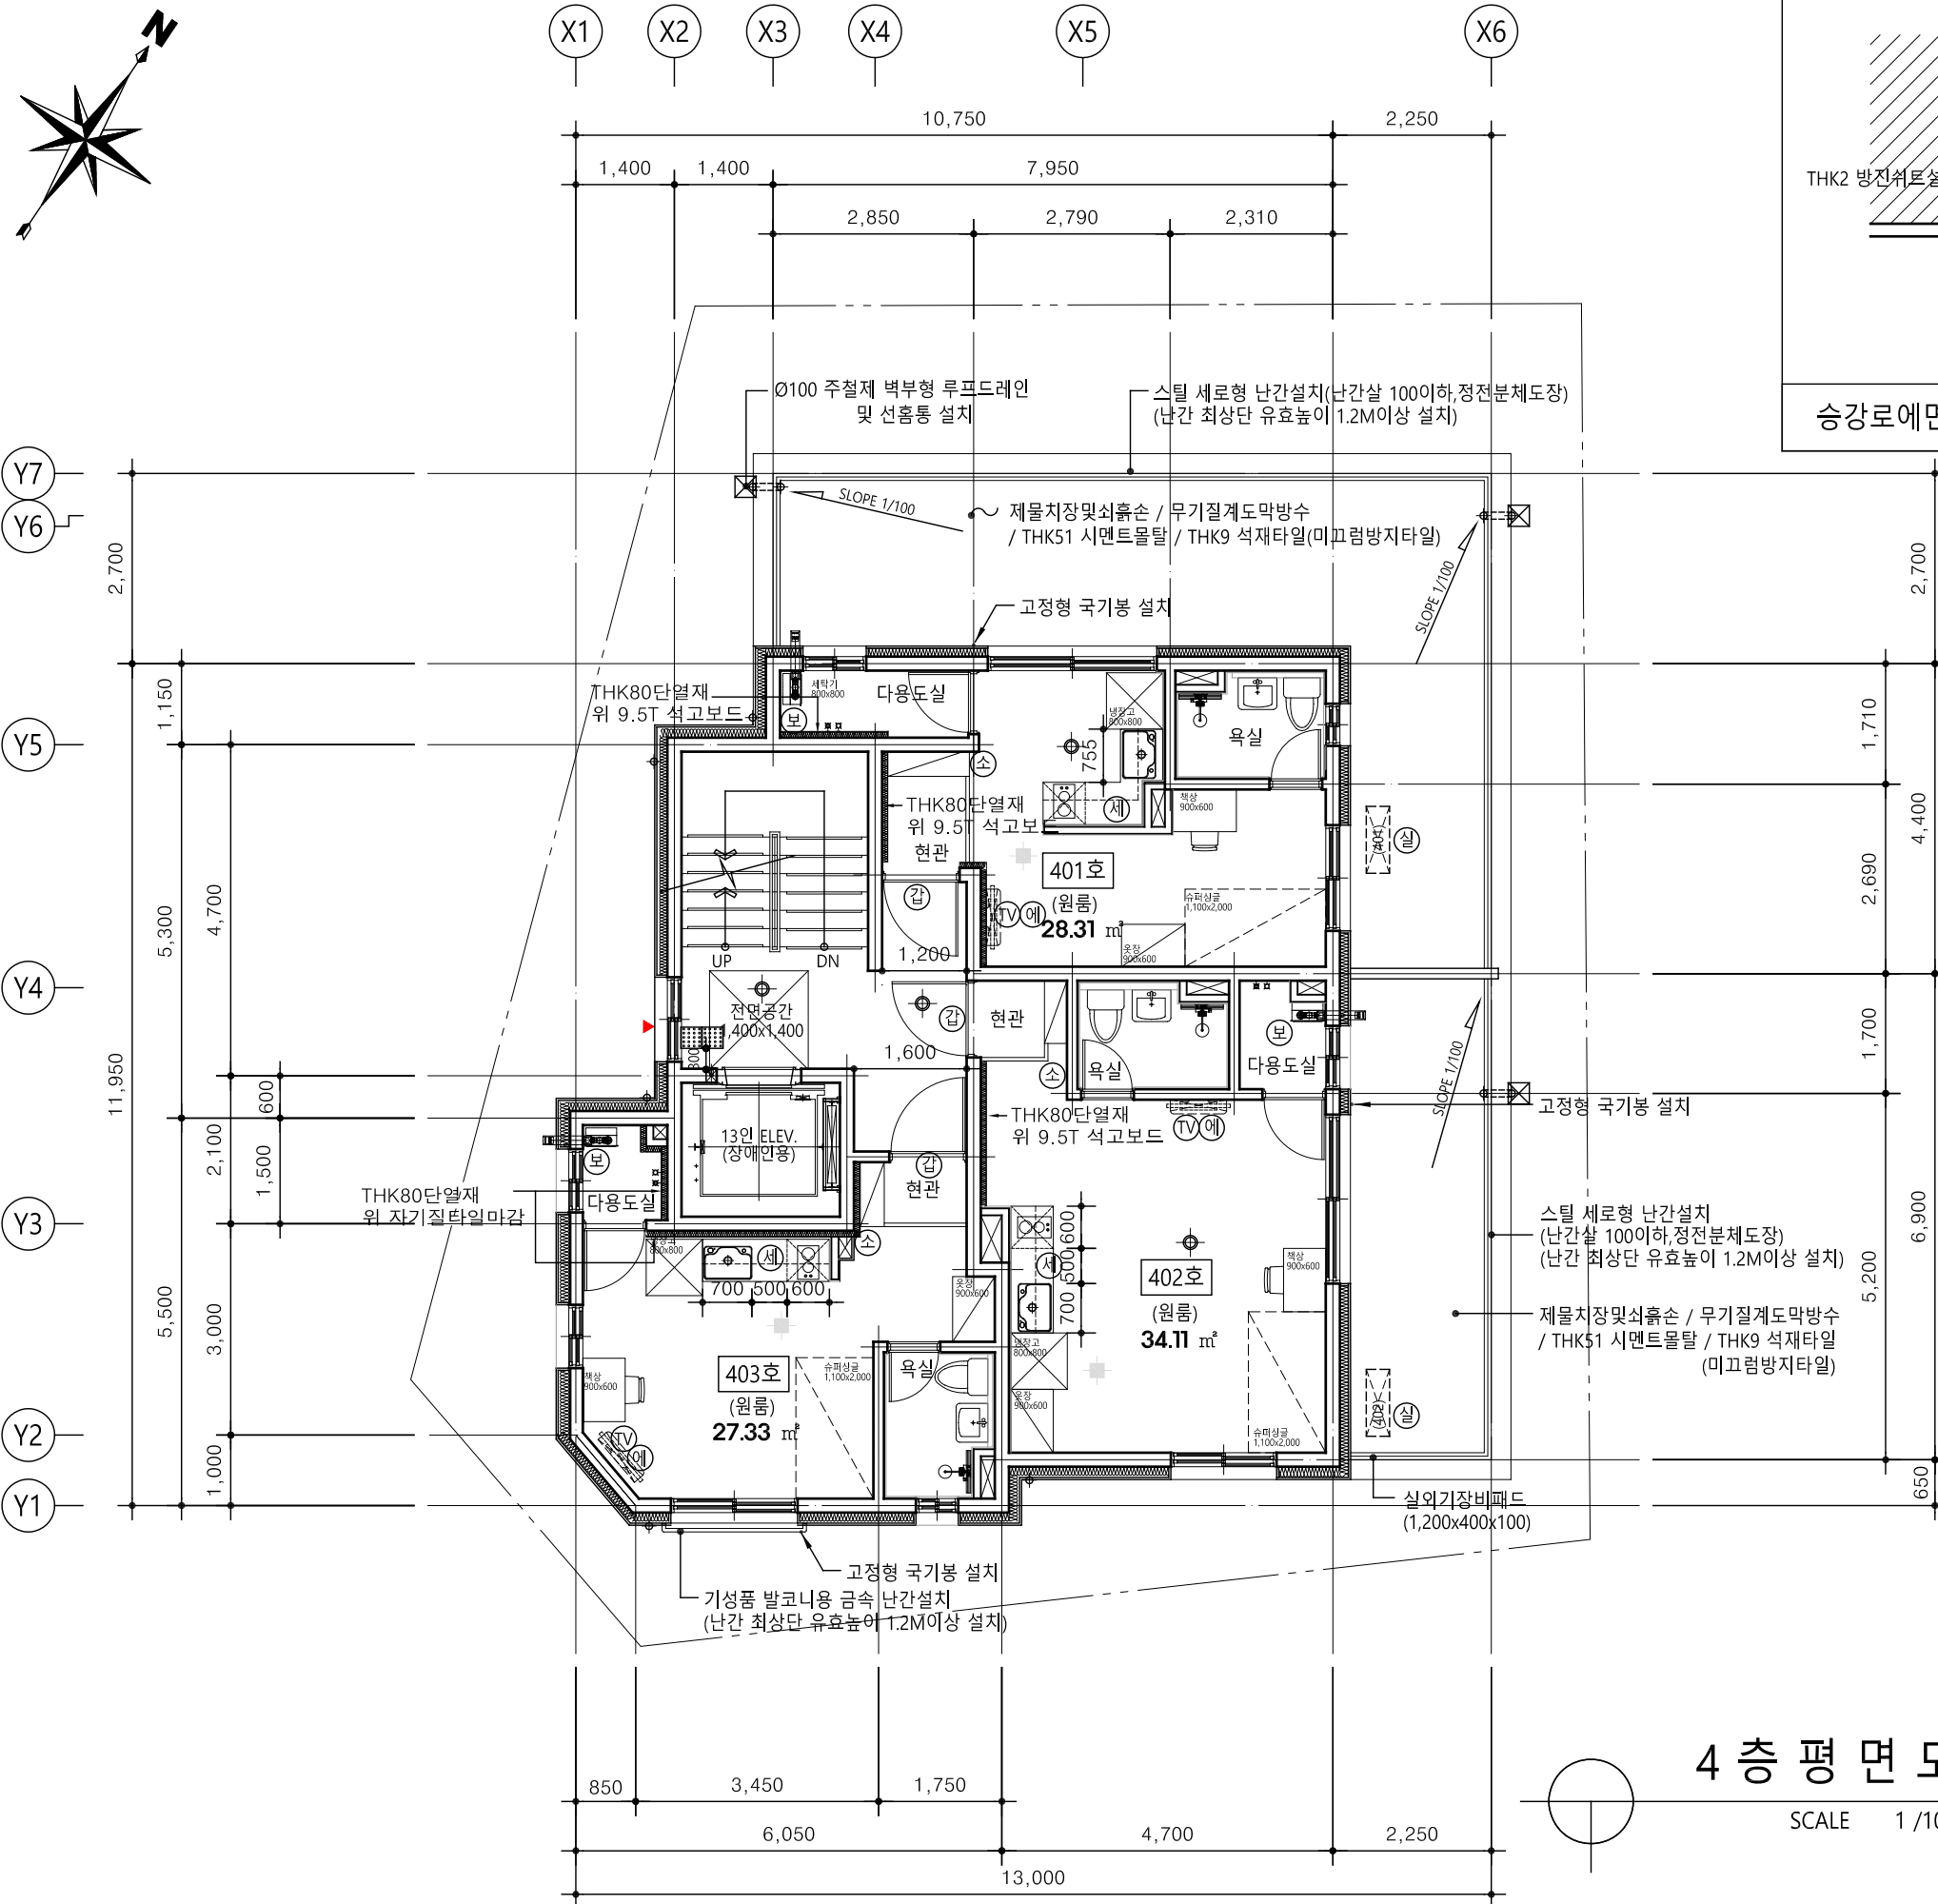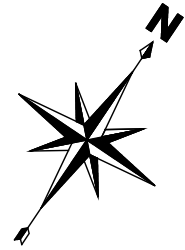

NOTE	
구분	내 용
갑	갑종방화문(60분방화문)
단	단독경보형감지기(연기식)
열	단독경보형감지기(열감지)
소	분말 소화기(ABC급 3.3Kg)
보	보일러(친환경 1등급)
차	차면시설 설치
방	방화유리(비차열 20분이상)
소	소방진입장 설치
에	벽걸이 에어컨
세	빌트인 세탁기
TV	벽걸이 TV
실	실외기

4 층 평 면 도

SCALE 1 / 100

PROJECT TITLE

영등포구 대림동
685-24
도시형 생활주택 계획

NOTE

△			
△			
△			
△			
△			
△			
△			
△			
NO.	DATE	DESCRIPTION	APP.






REVISION

(주)정다움 건축사사무소
JEONGDAUM ARCHITECTURE COMPANY
TEL. 02-438-3700
TEL. 010-8911-0941
FAX. 02-438-3800

DRAWING TITLE

4 층 평 면 도

DRAWN BY	PROJECT NO.
CHECKED BY	SCALE 1/100
APPROVED BY	DATE 2023.09.
DRAWING FILE NAME	
DWG NO.	A-103

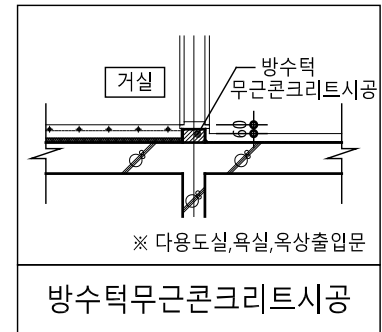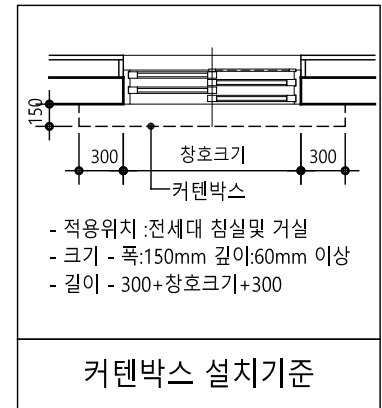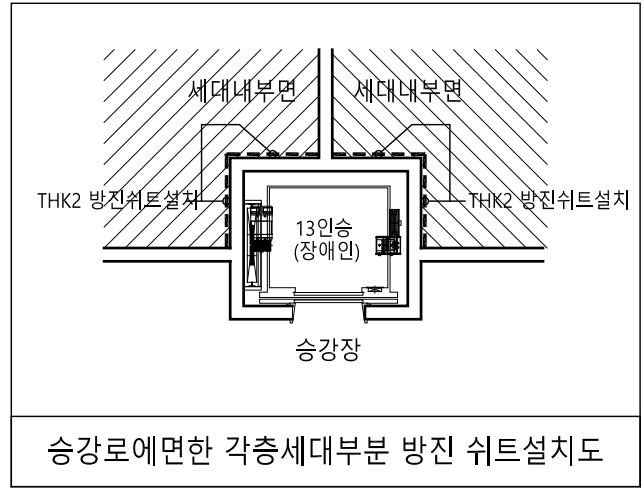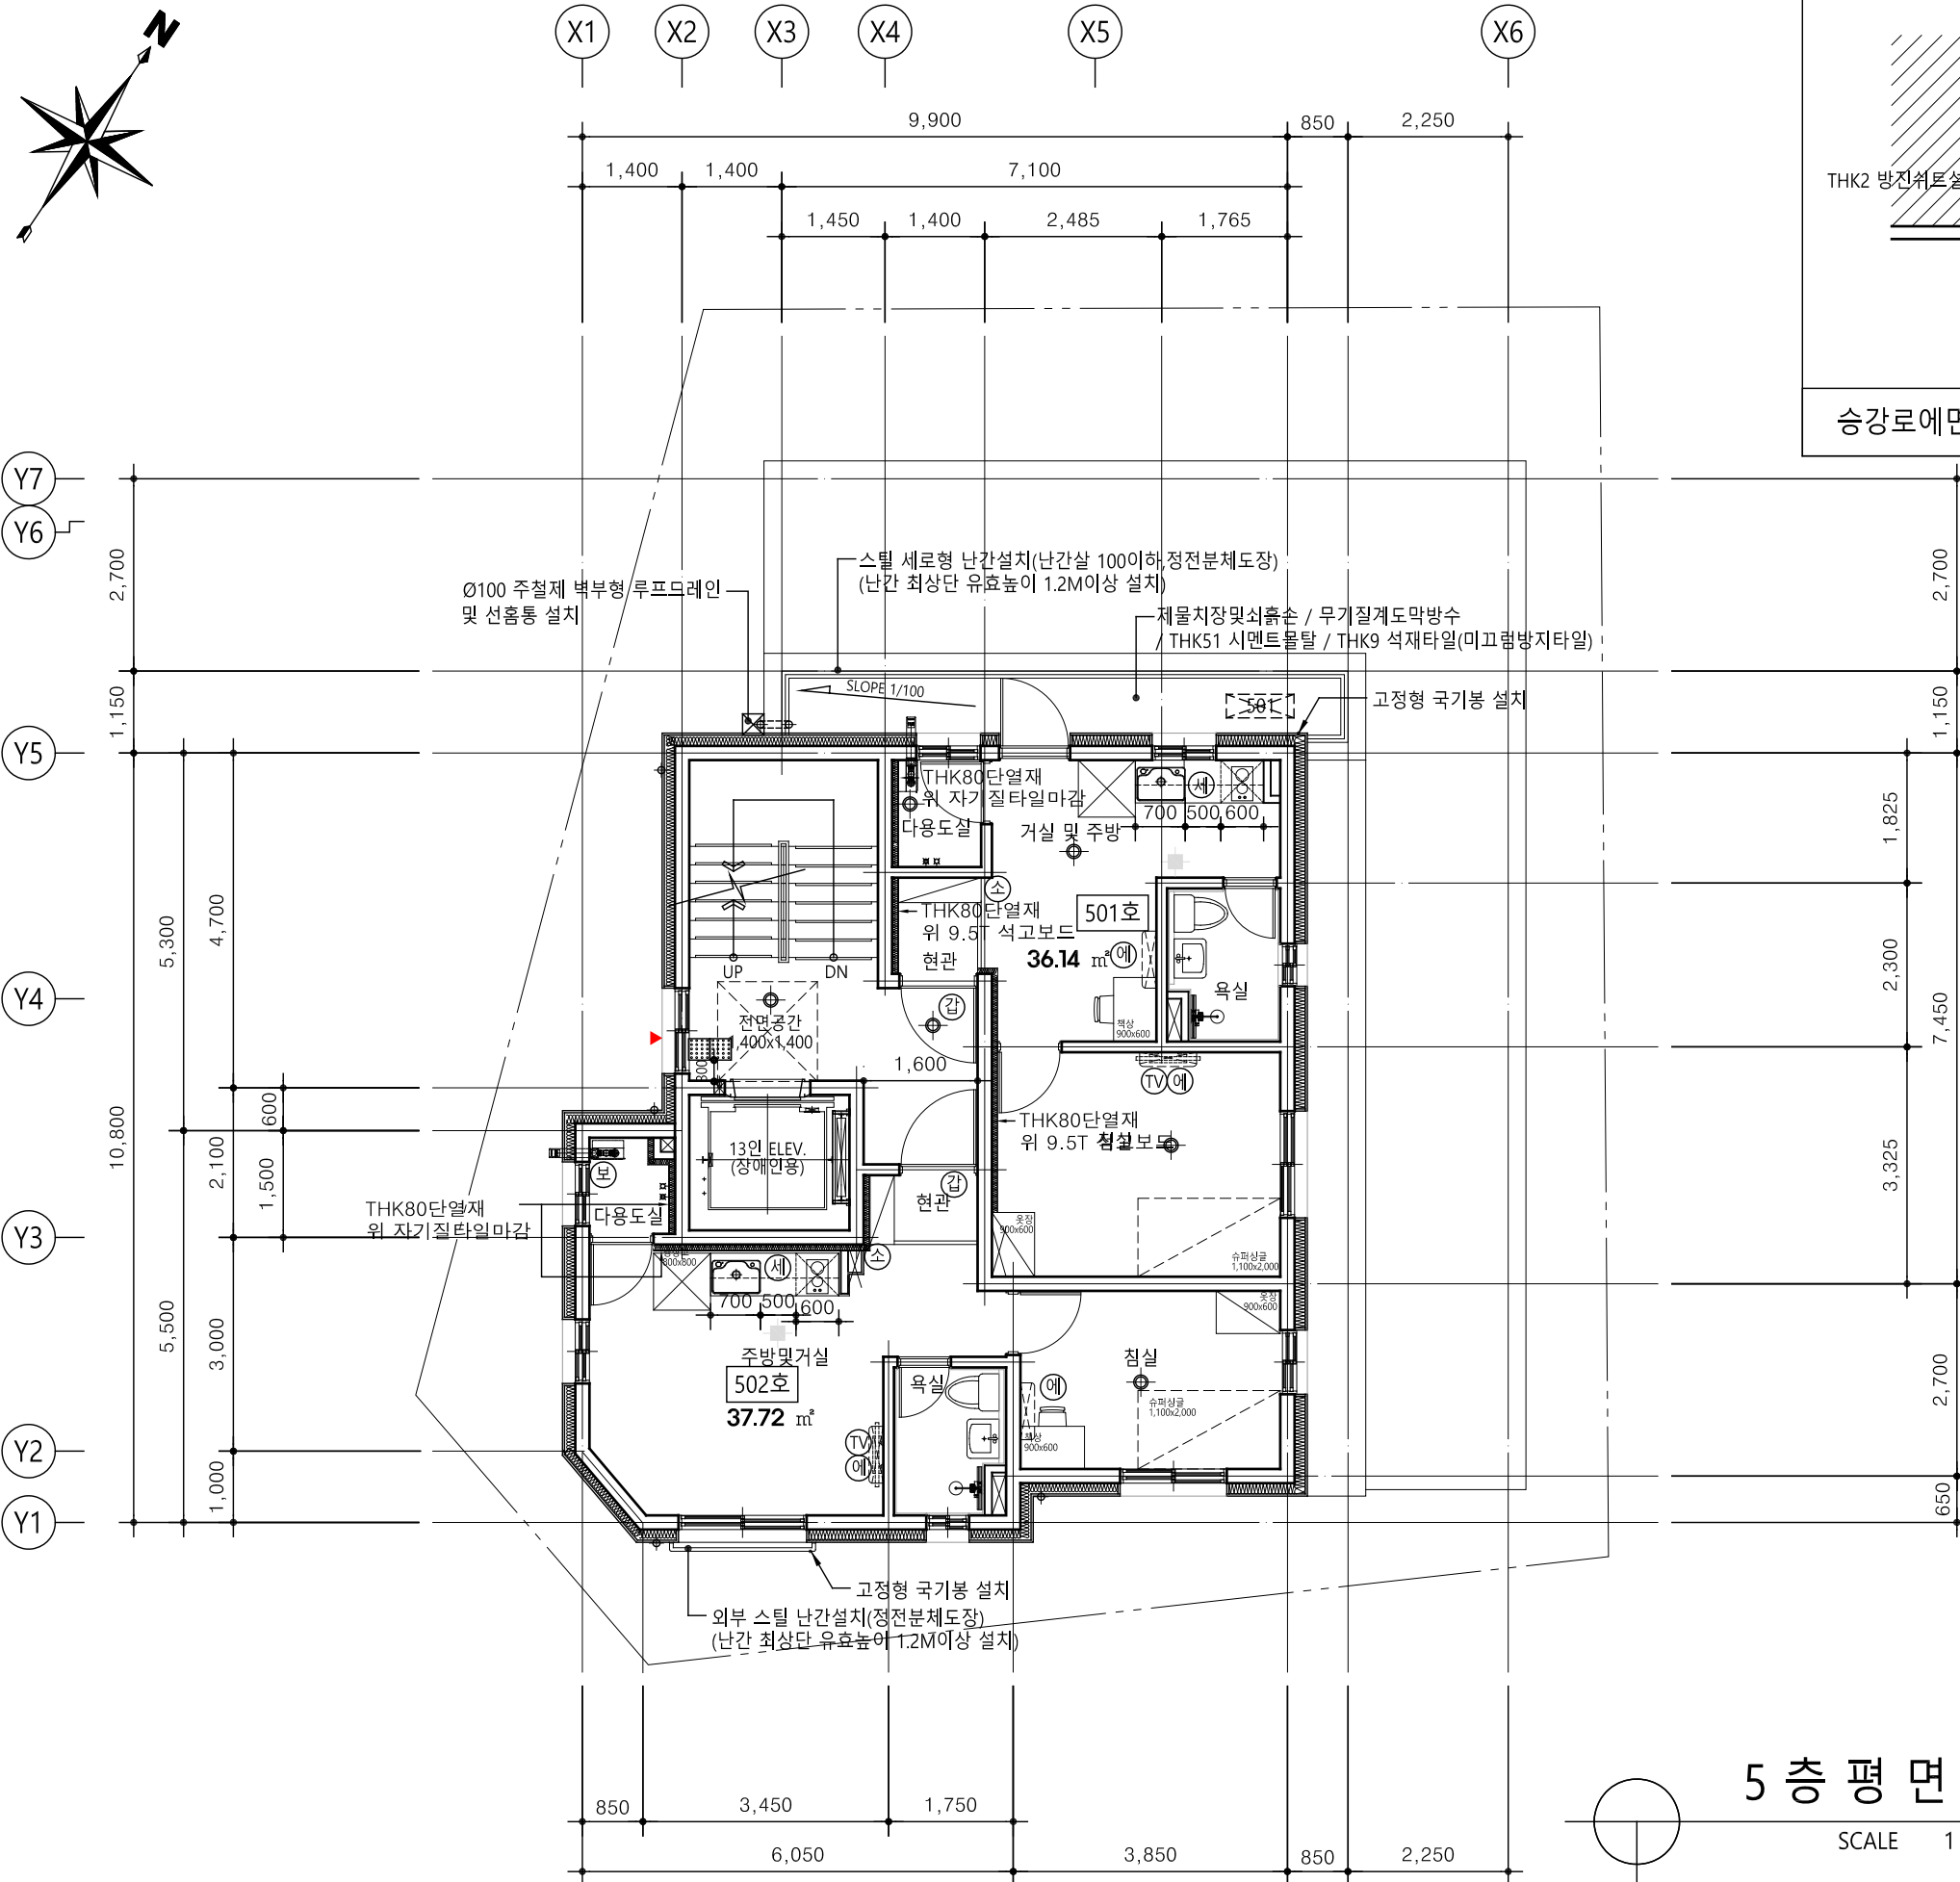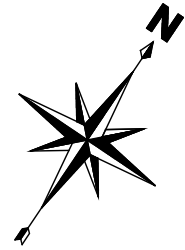

NOTE	
구분	내 용
①	갑종방화문(60분방화문)
②	단독경보형감지기(연기식)
③	단독경보형감지기(열감지)
④	분말 소화기(ABC급 3.3Kg)
⑤	보일러(친환경 1등급)
⑥	차면시설 설치
⑦	방화유리(비차열 20분이상)
⑧	소방진입창 설치
⑨	벽걸이 에어컨
⑩	벽걸이 TV
⑪	빌트인 세탁기

5 층 평 면 도
SCALE 1 / 100

PROJECT TITLE
영등포구 대림동
685-24
도시형 생활주택 계획

NOTE

△			
△			
△			
△			
△			
△			
△			
△			
NO.	DATE	DESCRIPTION	APP.

REVISION

(주)정다움 건축사사무소
JEONGDAUM ARCHITECTURE COMPANY
TEL. 02-438-3700
TEL. 010-8911-0941
FAX. 02-438-3800

DRAWING TITLE
5 층 평 면 도

DRAWN BY	PROJECT NO.
CHECKED BY	SCALE 1/100
APPROVED BY	DATE 2023.09.
DRAWING FILE NAME	
DWG NO.	A-104

PROJECT TITLE

영등포구 대림동
685-24
도시형 생활주택 계획

NOTE

△			
△			
△			
△			
△			
△			
△			
△			
△			
NO.	DATE	DESCRIPTION	APP.

REVISION

(주)정다움 건축사무소
JEONGDAUM ARCHITECTURE COMPANY
TEL. 02-438-3700
TEL. 010-8911-0941
FAX. 02-438-3800

DRAWING TITLE

옥 탑 평 면 도

DRAWN BY	PROJECT NO.
CHECKED BY	SCALE 1/100
APPROVED BY	DATE 2023.09.


DRAWING FILE NAME

DWG NO.

A-105

NOTE

구분	내 용
실	실외기

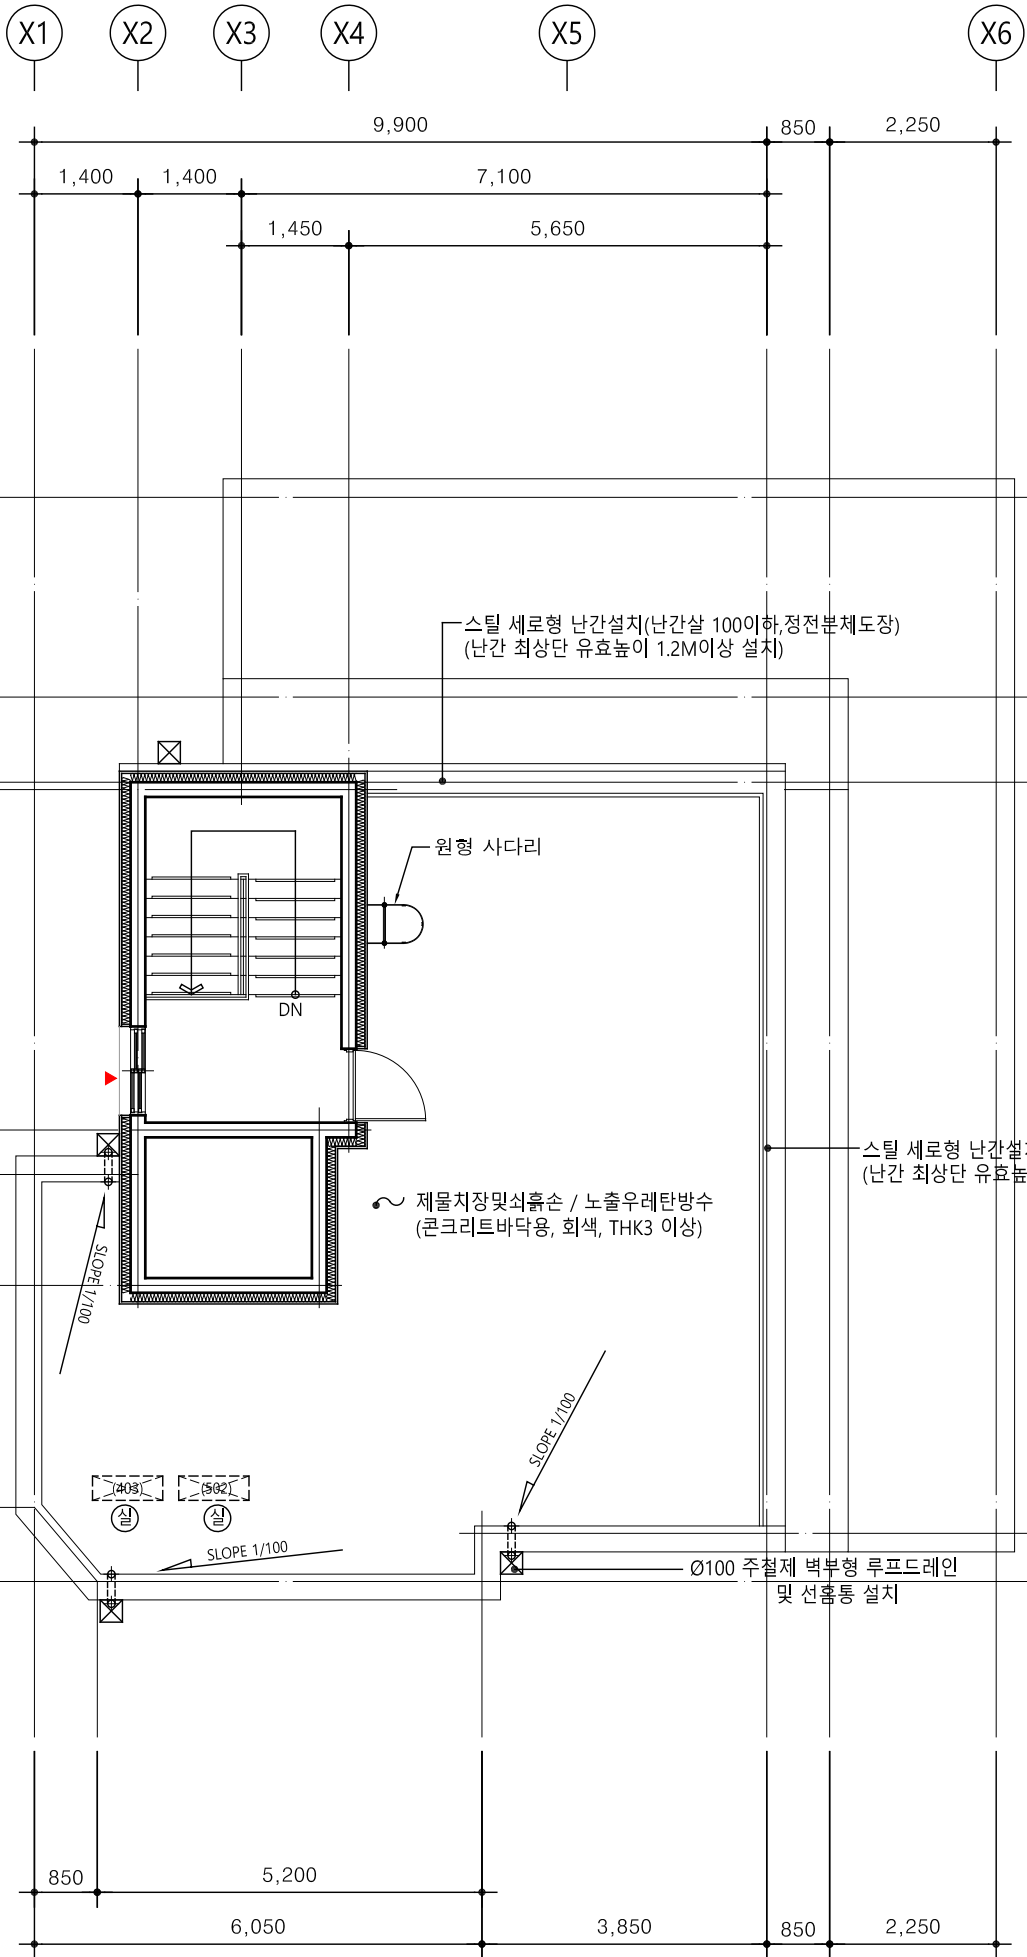

Ø100 주철제 벽부형 루프드레인
및 선홈통 설치

스틸 세로형 난간설치(난간살 100이하, 정전분체도장)
(난간 최상단 유효높이 1.2M이상 설치)

제물치장및쇠흙손 / 노출우레탄방수
(콘크리트바닥용, 회색, THK3 이상)

스틸 세로형 난간설치(난간살 100이하, 정전분체도장)
(난간 최상단 유효높이 1.2M이상 설치)


Ø100 주철제 벽부형 루프드레인
및 선홈통 설치

옥탑지붕 평면도

SCALE 1 / 100

옥 탑 평 면 도

SCALE 1 / 100

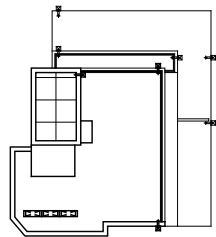

KEY PLAN

▼ 옥탑지붕 SL.

▼ 옥탑 SL.

▼ 5층 SL.

▼ 4층 SL.

▼ 3층 SL.

▼ 2층 SL.

⚡ 1층 SL.
GL. ±0

X1

X2

X3

X4

X5

X6

기성품 발코니용 금속 난간설치
(난간 최상단 유효높이 1.2M이상 설치)

THK30 화강석

THK50 두겹석

스틸 세로형 난간설치(난간살 100이하,정전분체도장)
(난간 최상단 유효높이 1.2M이상 설치)

THK22 복층유리(외부/내부)

THK30 화강석(블랙)

2,900

2,900

2,800

2,800

2,800

3,250

PROJECT TITLE

영등포구 대림동
685-24
도시형 생활주택 계획

NOTE

△			
△			
△			
△			
△			
△			
△			
△			
△			

NO.	DATE	DESCRIPTION	APP.
-----	------	-------------	------

REVISION

(주)정다움 건축사무소
JEONGDAUM ARCHITECTURE COMPANY
TEL. 02-438-3700
TEL. 010-8911-0941
FAX. 02-438-3800

DRAWING TITLE

정 면 도

DRAWN BY	PROJECT NO.
CHECKED BY	SCALE 1/100
APPROVED BY	DATE 2023.09.


DRAWING FILE NAME

DWG NO.

A-201

정 면 도

SCALE 1 / 100

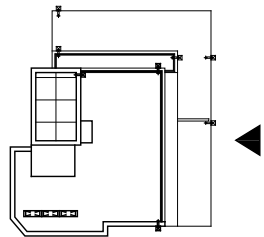

KEY PLAN

▼ 옥탑지붕 SL.

▼ 옥탑 SL.

▼ 5층 SL.

▼ 4층 SL.

▼ 3층 SL.

▼ 2층 SL.

⚡ 1층 SL.
GL. ±0

Y1

Y2

Y3

Y4

Y5

Y6

Y7

스틸 세로형 난간설치(난간살 100이하, 정전분체도장)
(난간 최상단 유효높이 1.2M이상 설치)

THK50 두겹석

THK30 화강석

THK30 화강석(블랙)

2,900

2,900

2,800

2,800

2,800

3,250

우 측 면 도

SCALE 1 / 100

PROJECT TITLE

영등포구 대림동
685-24
도시형 생활주택 계획

NOTE

△			
△			
△			
△			
△			
△			
△			
△			
△			

NO.	DATE	DESCRIPTION	APP.
-----	------	-------------	------

REVISION

(주)정다움 건축사사무소
JEONGDAUM ARCHITECTURE COMPANY
TEL. 02-438-3700
TEL. 010-8911-0941
FAX. 02-438-3800

DRAWING TITLE


우 측 면 도

DRAWN BY	PROJECT NO.
CHECKED BY	SCALE 1/100
APPROVED BY	DATE 2023.09.

DRAWING FILE NAME

DWG NO.

A-202

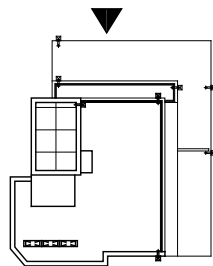

KEY PLAN

▼ 옥탑지붕 SL.

▼ 옥탑 SL.

▼ 5층 SL.

▼ 4층 SL.

▼ 3층 SL.

▼ 2층 SL.

⌵ 1층 SL.
GL. ±0

THK30 화강석(블랙)

2,900

2,900

2,800

2,800

2,800

3,250

PROJECT TITLE

영등포구 대림동
685-24
도시형 생활주택 계획

NOTE

△			
△			
△			
△			
△			
△			
△			
△			
△			

NO.	DATE	DESCRIPTION	APP.
-----	------	-------------	------

REVISION

(주)정다움 건축사무소
JEONGDAUM ARCHITECTURE COMPANY
TEL. 02-438-3700
TEL. 010-8911-0941
FAX. 02-438-3800

DRAWING TITLE

배 면 도

DRAWN BY	PROJECT NO.
----------	-------------

CHECKED BY	SCALE
------------	-------

1/100


APPROVED BY	DATE
-------------	------

2023.09.

DRAWING FILE NAME


DWG NO.

A-203

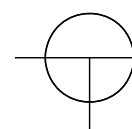

배 면 도

SCALE 1 / 100

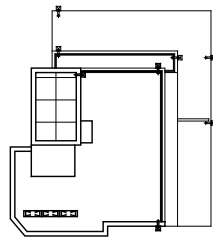

KEY PLAN

▼ 옥탑지붕 SL.

▼ 옥탑 SL.

▼ 5층 SL.

▼ 4층 SL.

▼ 3층 SL.

▼ 2층 SL.

1층 SL.
GL. ±0

THK30 화강석(블랙)

Y7 Y6

Y5

Y4

Y3

Y2

Y1

2,900

2,900

2,800

2,800

2,800

3,250

좌 측 면 도

SCALE 1 / 100

PROJECT TITLE

영등포구 대림동
685-24
도시형 생활주택 계획

NOTE

△			
△			
△			
△			
△			
△			
△			
△			
△			

NO.	DATE	DESCRIPTION	APP.
-----	------	-------------	------

REVISION

(주)정다움 건축사무소
JEONGDAUM ARCHITECTURE COMPANY
TEL. 02-438-3700
TEL. 010-8911-0941
FAX. 02-438-3800

DRAWING TITLE

좌 측 면 도

DRAWN BY	PROJECT NO.
CHECKED BY	SCALE 1/100
APPROVED BY	DATE 2023.09.

DRAWING FILE NAME

DWG NO. A-204