


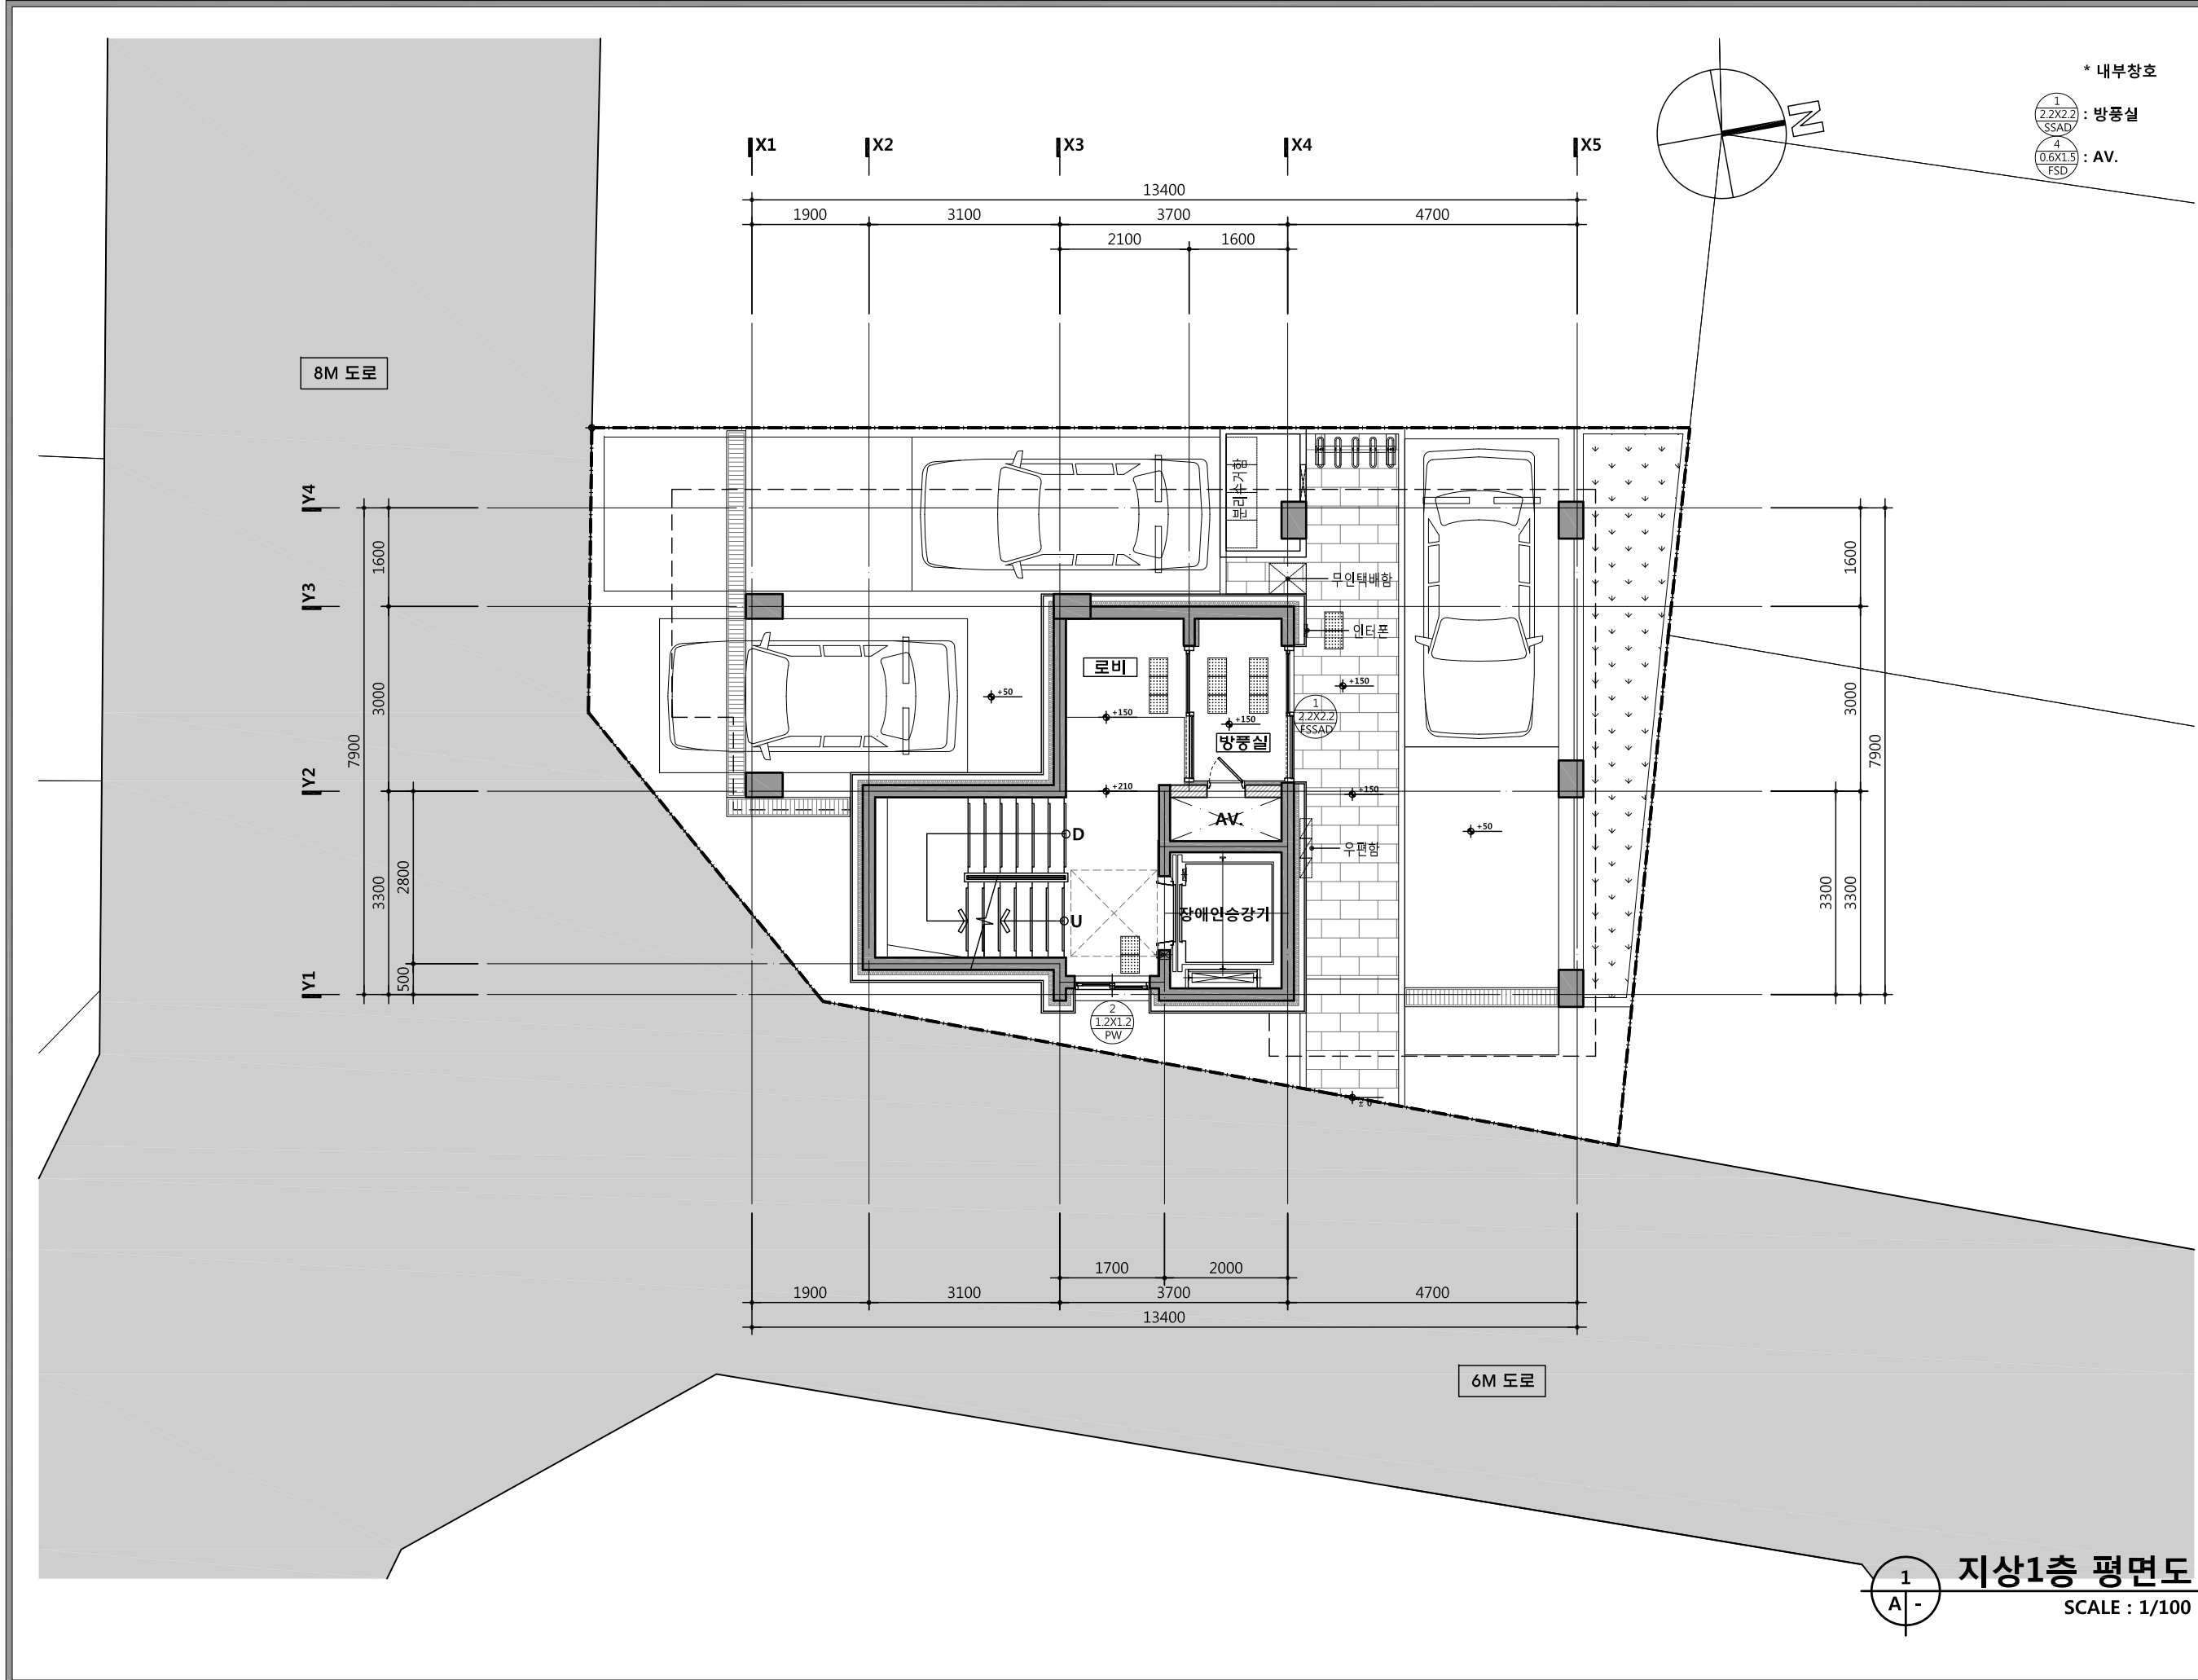

* 내부창호

1
2.2X2.2
SSAD : 방풍실

4
0.6X1.5
FSD : AV.

FORUM
Hanwon
한원포럼건축사사무소

서울시 송파구 법원로8길 7
901호 (문정동 화엄타워)
TEL : 3445-8361
FAX : 3445-8363

작품번호
PROJ. NO

작품명
PROJ. TITLE

양평동1가 31-7
오피스텔 신축공사

기

사

수정
REVISED

건축설계
ARC. DESIGNED BY

구조설계
STR. DESIGNER BY

설비설계
MEC. DESIGNED BY

전기설계
ELE. DESIGNED BY

제도
DRAWIN BY

심사
CHECKED BY

승인
APPROVED BY

도면명
DRAWING TITLE

지상1층 평면도

축척
SCALE 1 / 100

일
DATE 2022. 08.


도면번호
DRAWING NO

A 202

일련번호
SHEET NO

1
A -

지상1층 평면도
SCALE : 1/100

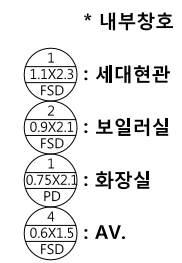


입 련 번 호
SHEET NO

지상2~6층 평면도




"A" TYPE

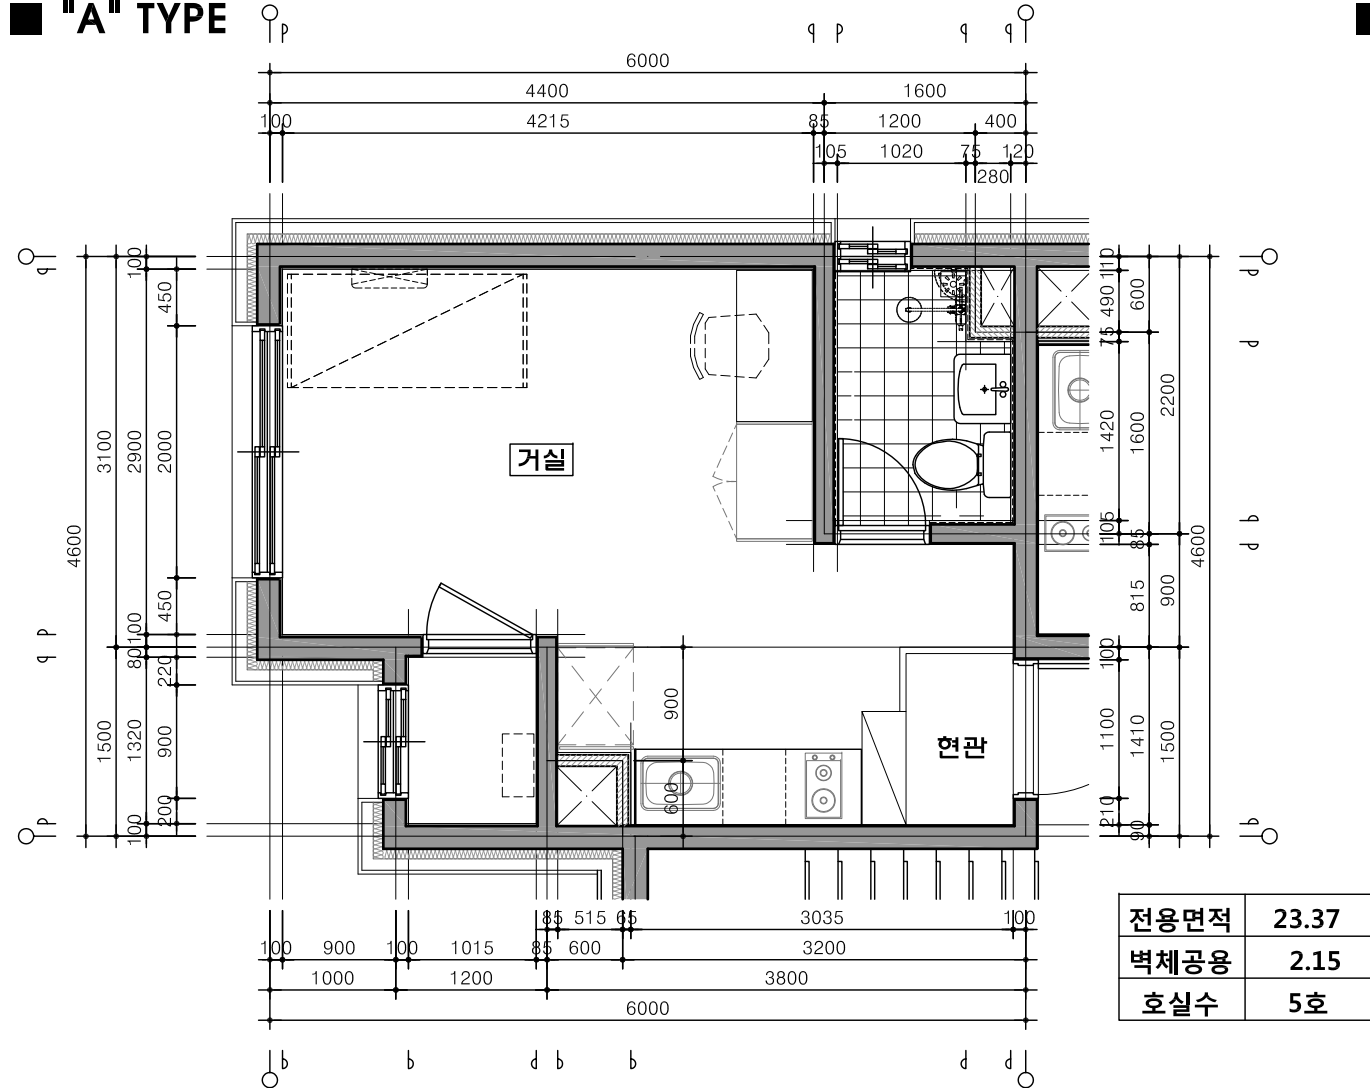


전용면적	23.37
벽체공용	2.15
호실수	5호

"B" TYPE

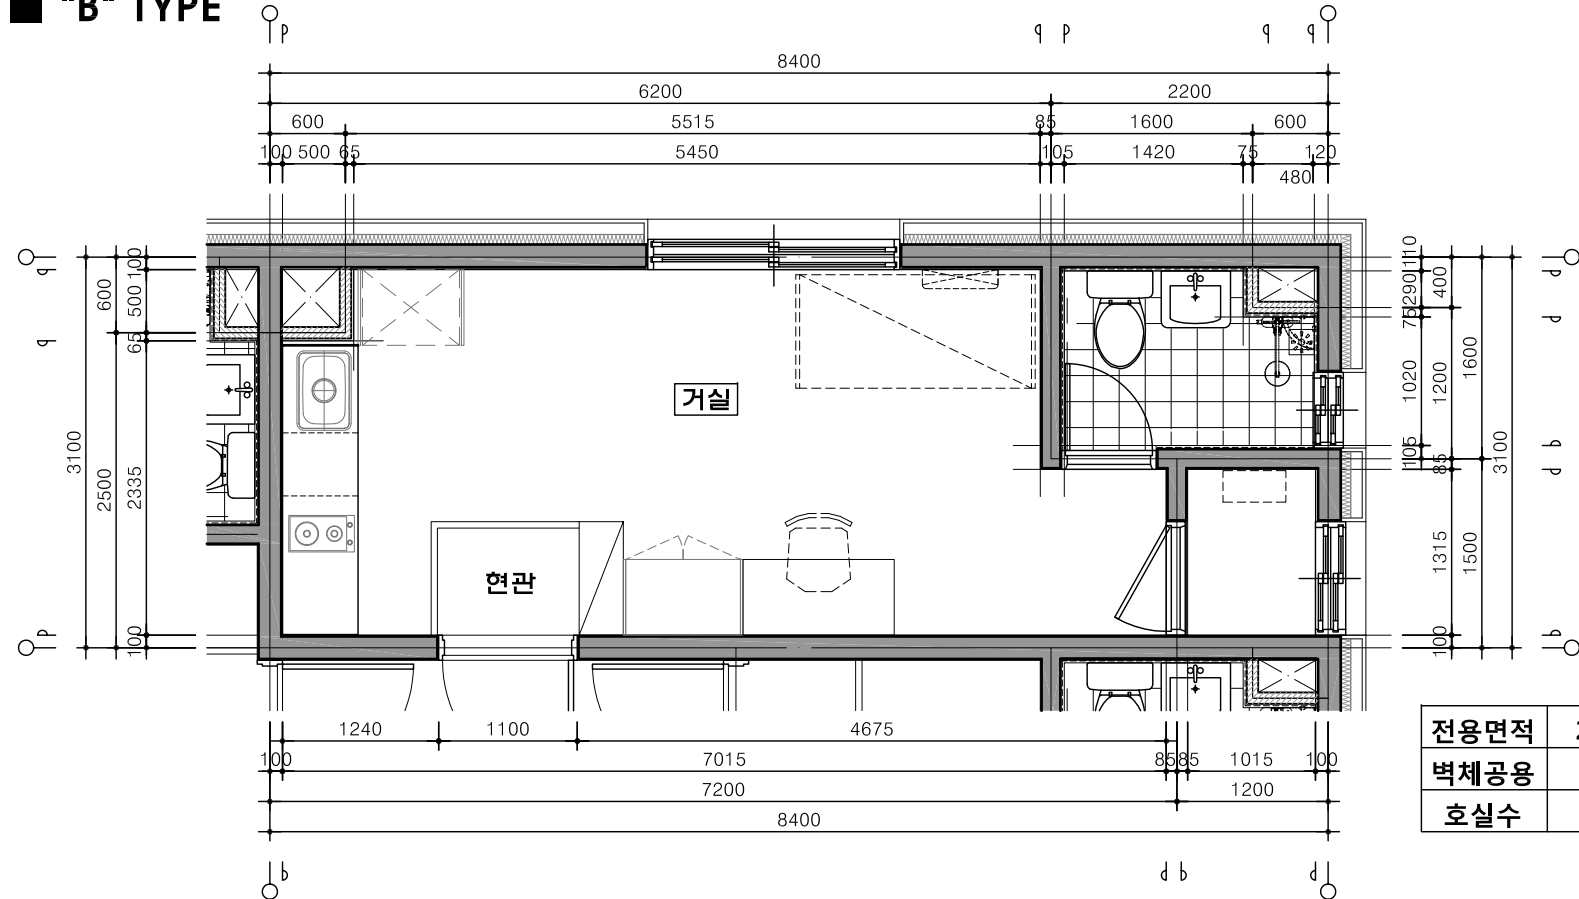

전용면적	23.22
벽체공용	2.22
호실수	5호

"C" TYPE

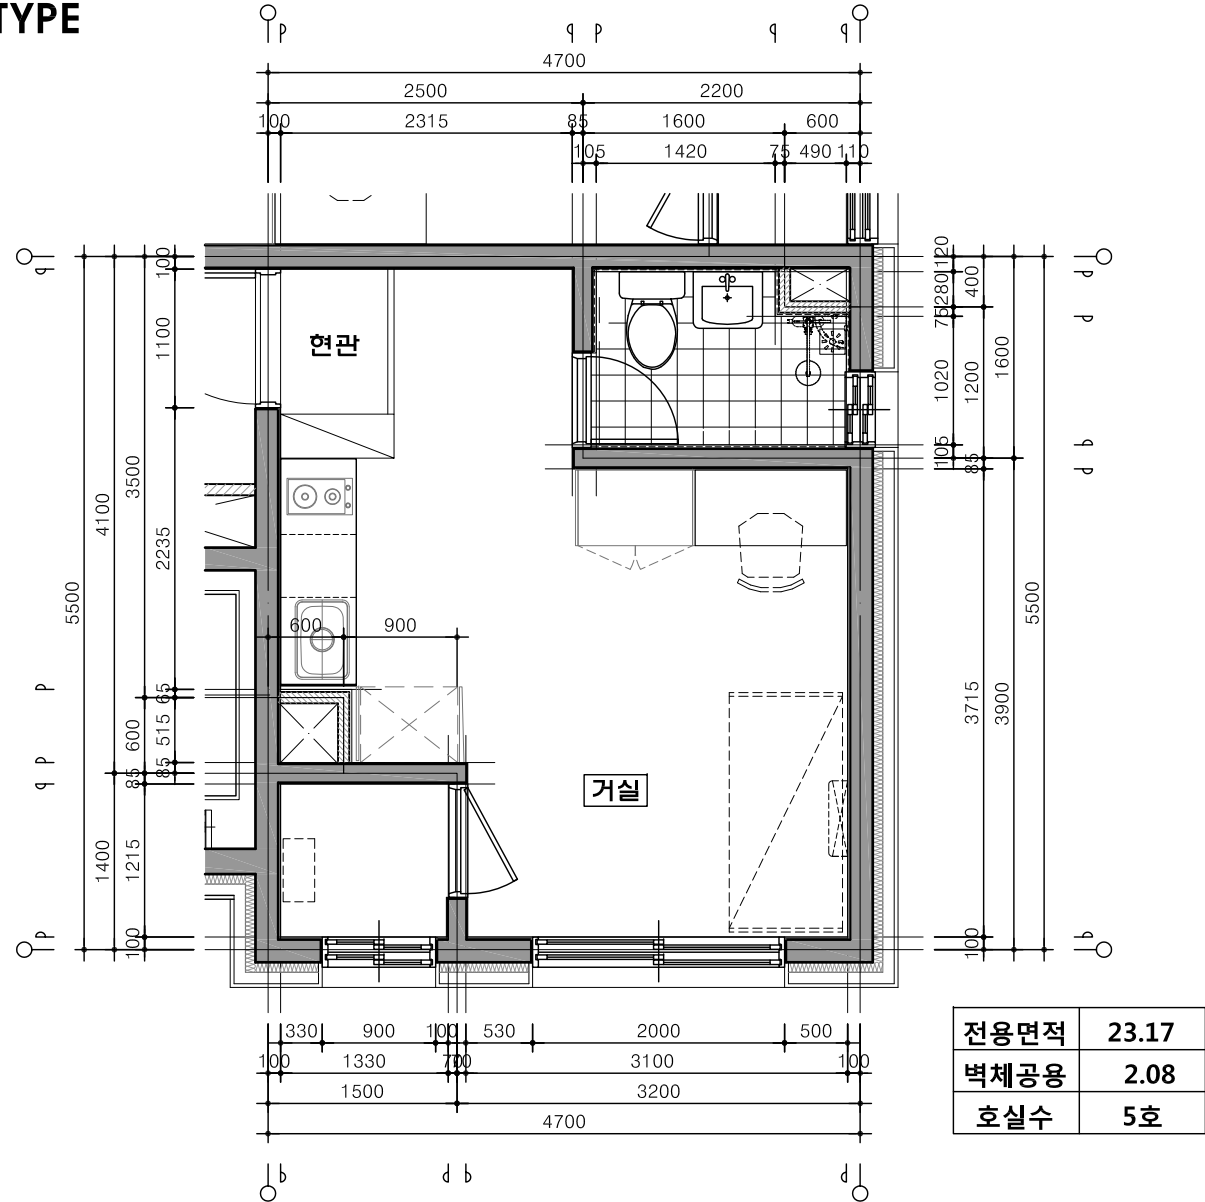

전용면적	23.17
벽체공용	2.08
호실수	5호

FORUM
Hanwon
한원포럼건축사사무소
서울시 송파구 법원로8길 7
901호 (문정동 화명타워)
TEL : 3445-8361
FAX : 3445-8363

작품번호
PROJ. NO

작품명
PROJ. TITLE

양평동1가 31-7
오피스텔 신축공사

기 사

수 정
REVISED

건축 설계
ARC. DESIGNED BY

구조 설계
STR. DESIGNER BY

설비 설계
MEC. DESIGNED BY

전기 설계
ELE. DESIGNED BY

도
DRAWN BY

심 사
CHECKED BY

승 인
APPROVED BY

도면명
DRAWING TITLE

단위세대 평면도


축
SCALE 1 / 60

일 자
DATE 2022. 08.

도면번호
DRAWING NO

A — 205

일련번호
SHEET NO

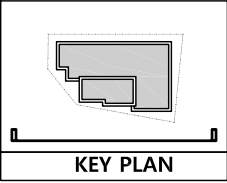

FORUM
Hanwon
한원포럼건축사사무소
서울시 송파구 법원로8길 7
901호 (문정동 화엄타워)
TEL : 3445-8361
FAX : 3445-8363

작품번호
PROJ. NO
작품명
PROJ. TITLE
양평동1가 31-7
오피스텔 신축공사

기
사
수
정
REVISED
건축설계
ARC. DESIGNED BY
구조설계
STR. DESIGNEN BY
설비설계
MEC. DESIGNED BY
전기설계
ELE. DESIGNED BY
계
도
DRAWIN BY
심
사
CHECKED BY
승
인
APPROVED BY
도
면
명
DRAWING TITLE

정
면
도
SCALE 1 / 100
일
자
2022. 08.
도면번호
DRAWING NO
A — 211
일련번호
SHEET NO

X1 X2 X3 X4 X5

사암 화강석 소방관진입창 T22 로이복층유리

Phr.SL

Ph.SL

6th.SL

5th.SL


4th.SL

3rd.SL


2nd.SL

1st.FL
GL.


정
면
도
SCALE : 1/100

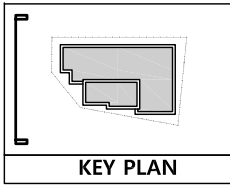


Y4 Y3 Y2 Y1

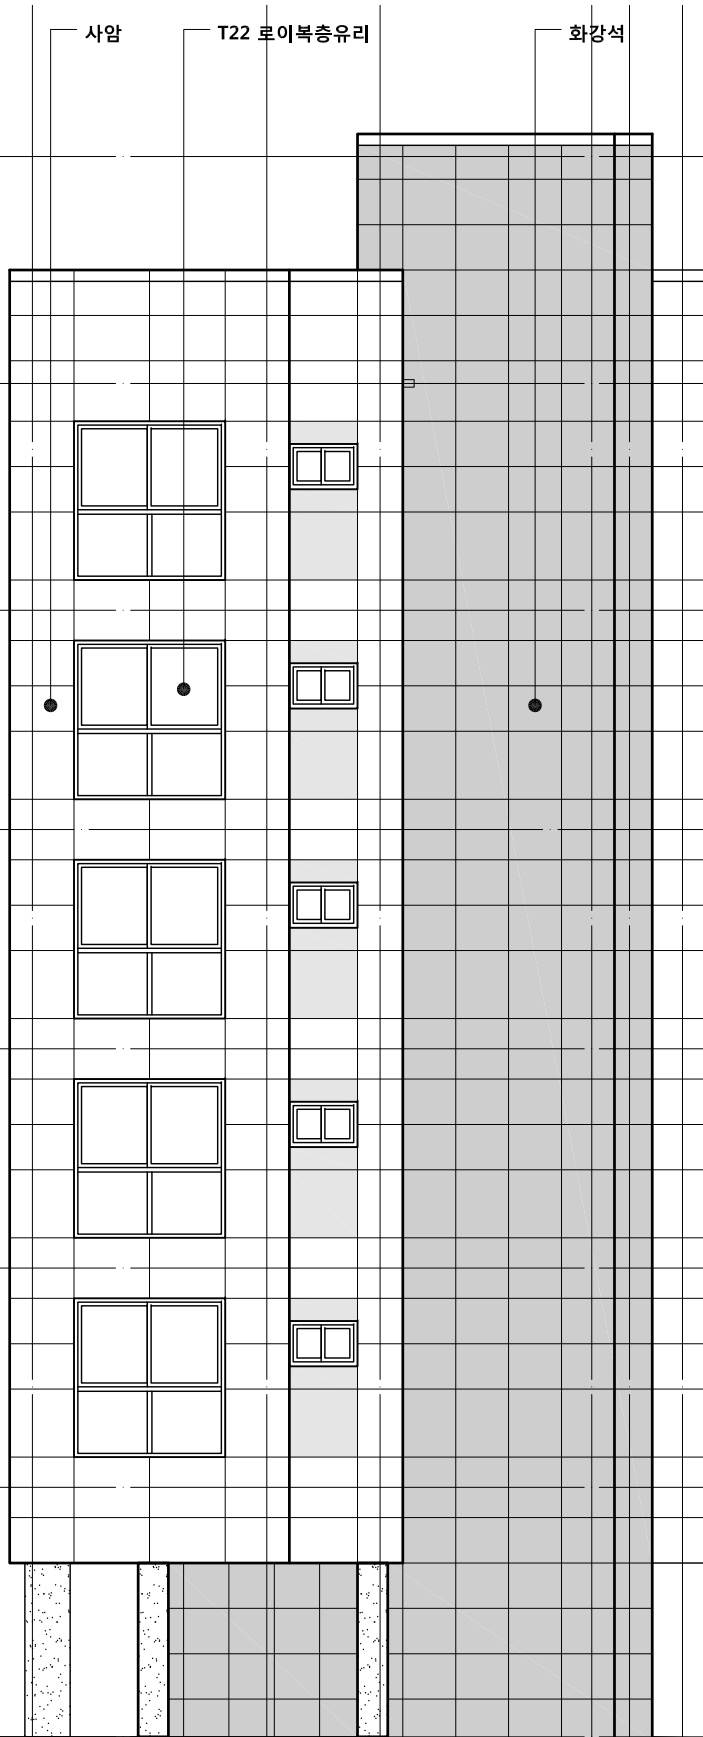

1 좌측면도
A - SCALE : 1/100

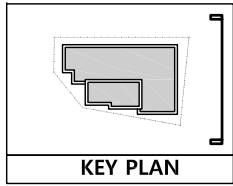

Y1 Y2 Y3 Y4

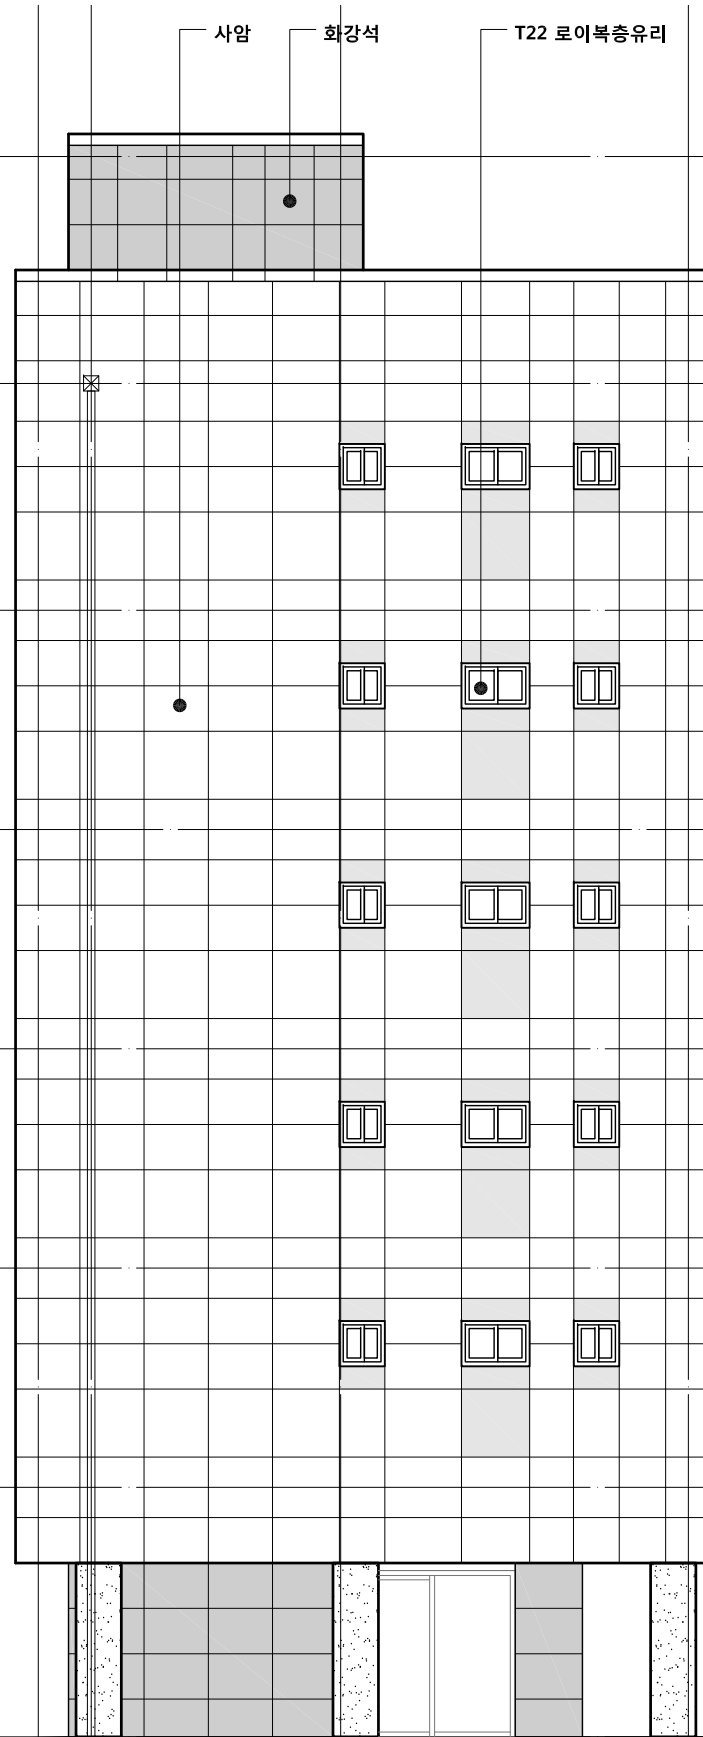

2 우측면도
A - SCALE : 1/100

FORUM
Hanwon
한원포럼건축사사무소
서울시 송파구 법원로8길 7
901호 (문정동 화엄타워)
TEL : 3445-8361
FAX : 3445-8363

작품번호
PROJ. NO

작품명
PROJ. TITLE

양평동1가 31-7
오피스텔 신축공사

기 사

수정
REVISED

건축설계
ARC. DESIGNED BY

구조설계
STR. DESIGNER BY

설비설계
MEC. DESIGNED BY

전기설계
ELE. DESIGNED BY

제 도
DRAWN BY

심 사
CHECKED BY

승 인
APPROVED BY

도면명
DRAWING TITLE

좌측면도
우측면도

축척
SCALE 1 / 100

일 자
DATE 2022. 08.

도면번호
DRAWING NO A - 212

시트번호
SHEET NO