

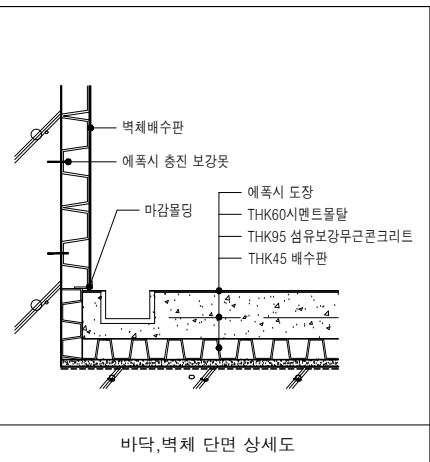


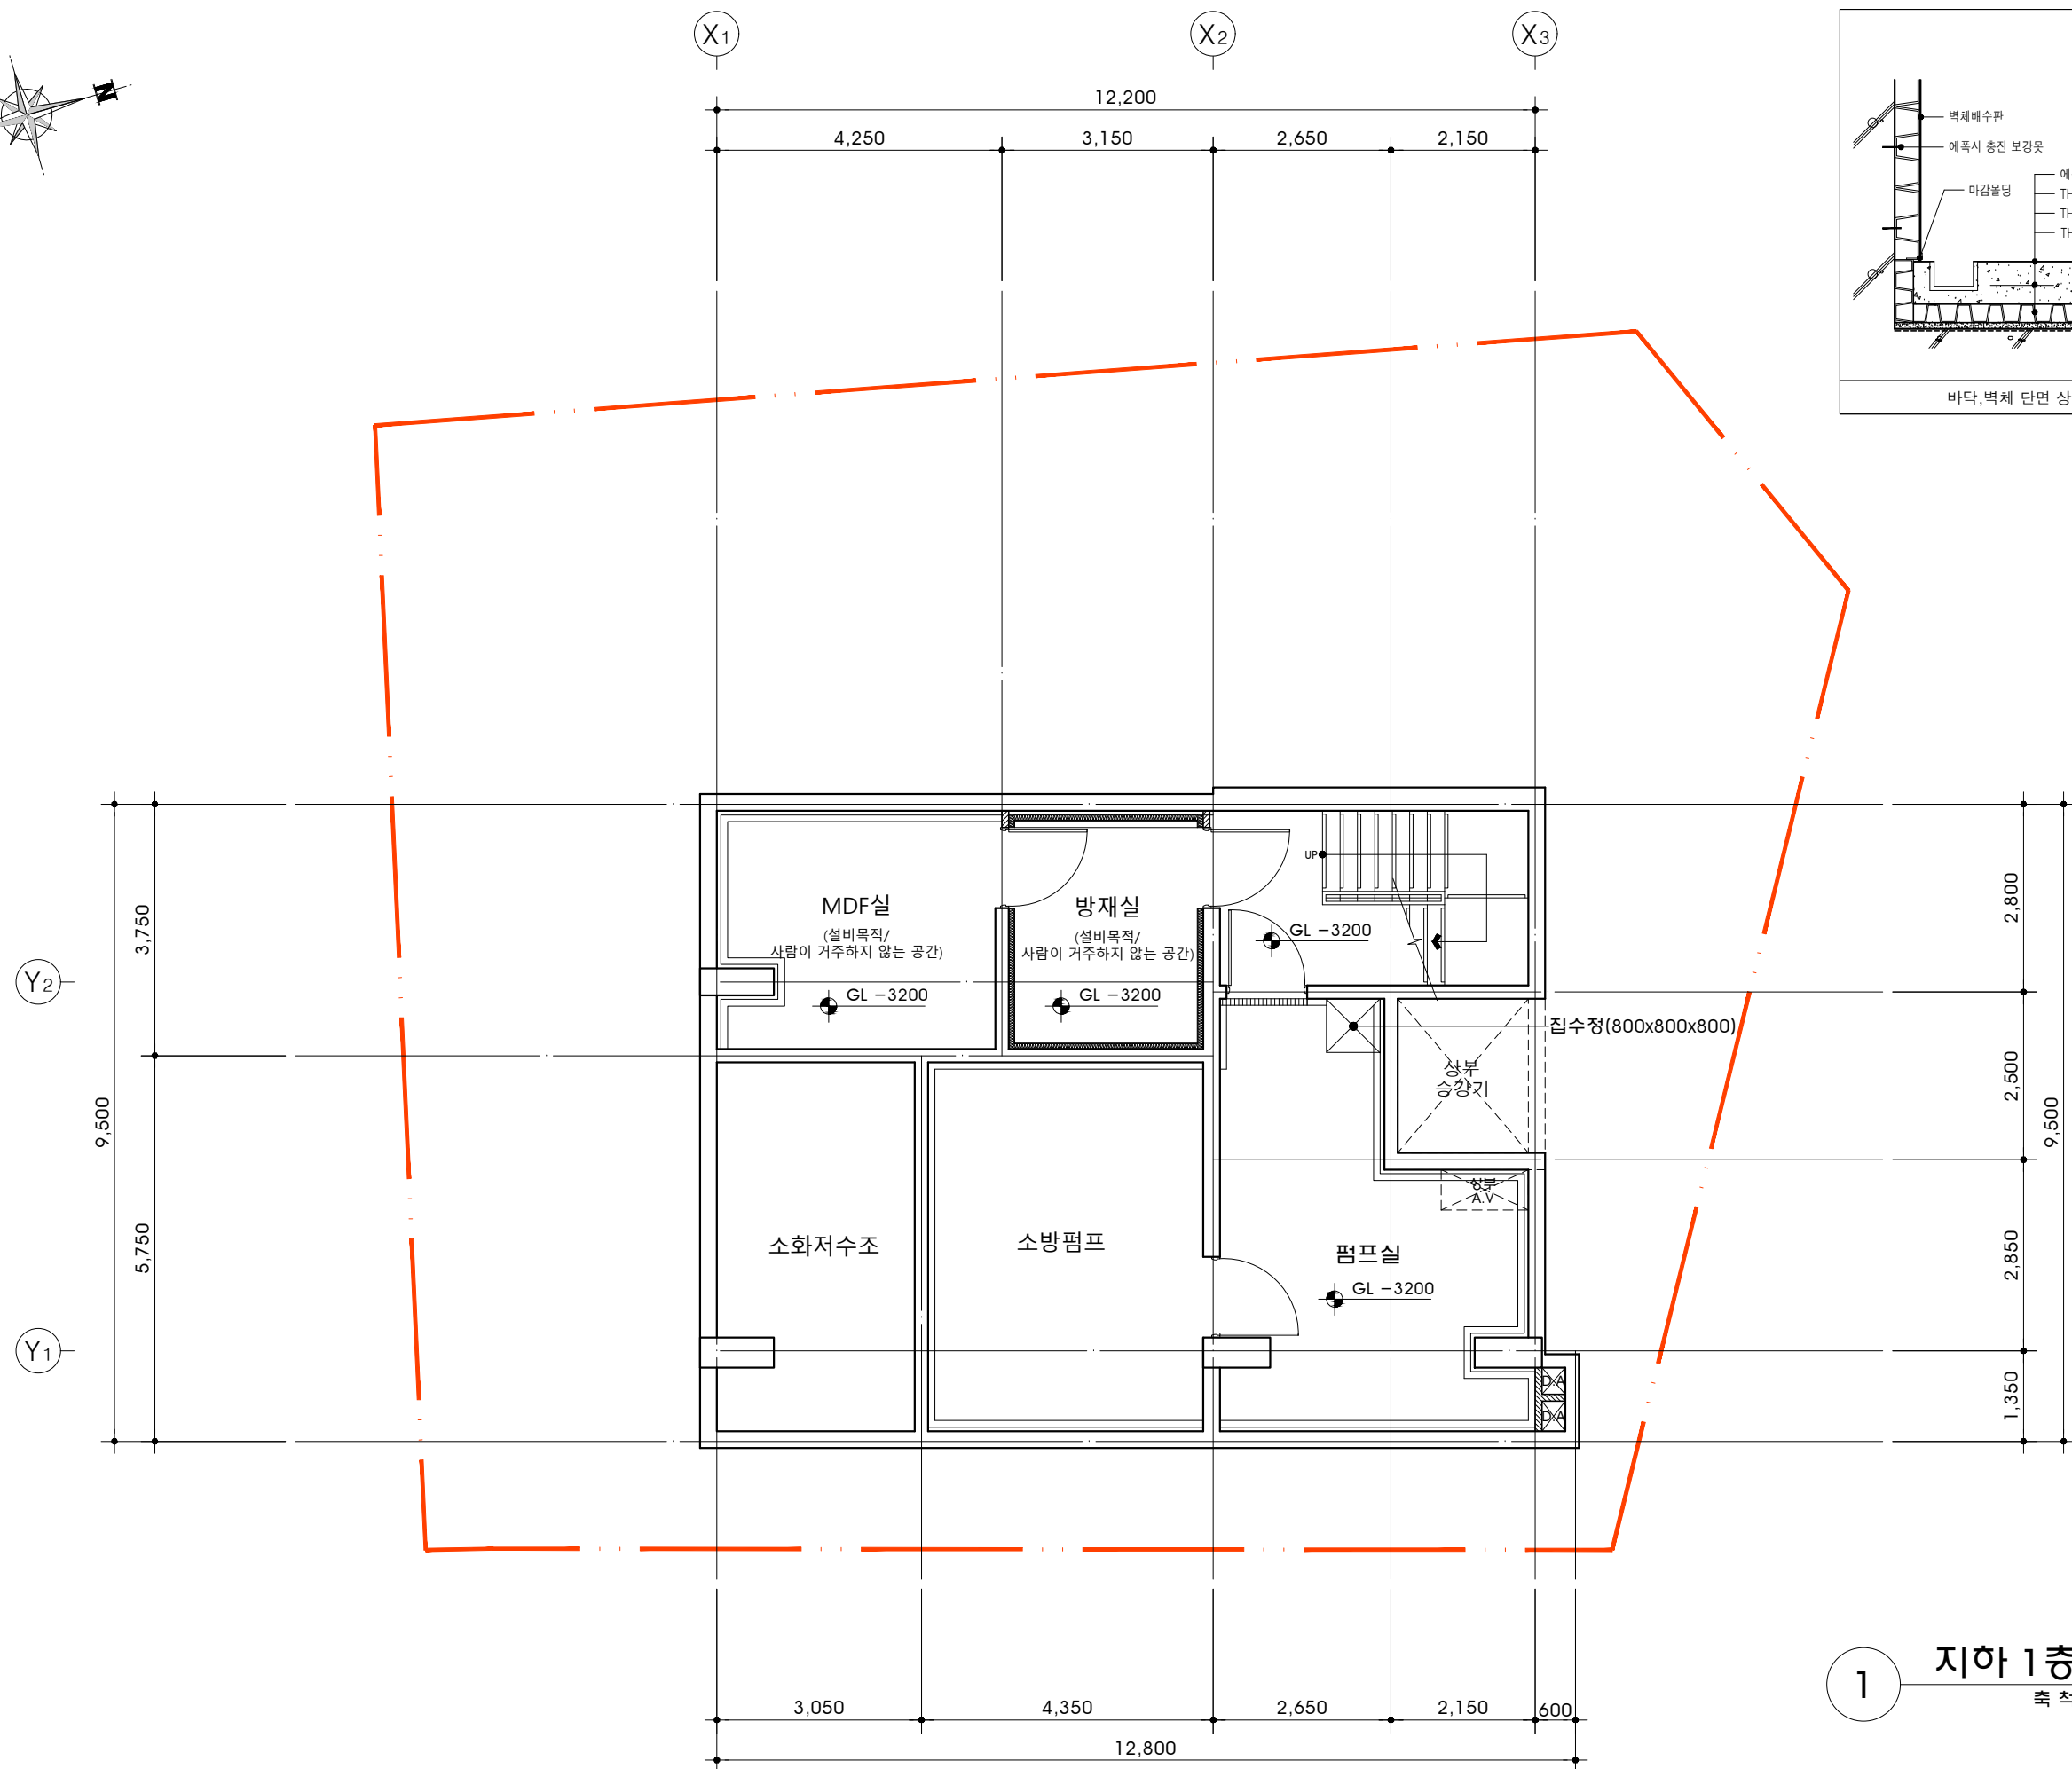

1 지하 1층 평면도
축척 - A3 : 1/100

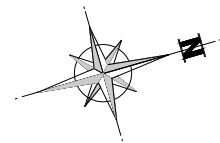

Architecture Construction Management
DESIGN GROUP

(주)아치씨엠 통합건축사사무소

서울특별시 송파구 오금로 130(송파동) 2층
TEL : 02-2202-0066
FAX : 02-2202-0076

공 사 명
PROJECT TITLE

은평구 응암동 120-40번지
오피스텔(청년주택)
신축공사

NOTE

- ㉠ 단독경보감지기
- ㉡ ABC분말소화기(3.3KG)
- ㉢ 60분+방화문, 60분 방화문
- ㉣ 보일러
- ㉤ 에어컨
- ㉥ 실외기
- ㉦ 차면시설

*기둥 주위에 차량 보호대 설치
*각세대 거실난간 국기꽃이 설치
*승강기에 면한 침실 및 거실,
주방 방진패드 설치
*저소음배관 시공
*평면도 상세 치수는 단위세대
타입별 도면 참조

번호	수정내용	월	일	검토
△				
△				
△				
△				
△				
△				
△				
△				

작성일자
DATE

설 계 자
DRAWING BY

검 토 자
CHECKED BY

승 인 자
APPROVED BY

축 척
SCALE

1/100

도 면 명
DRAWING TITLE


지하1층 평면도

일련번호
SHEET NO.

□□-□□□□

도면번호
DRAWING NO.

□A-□101

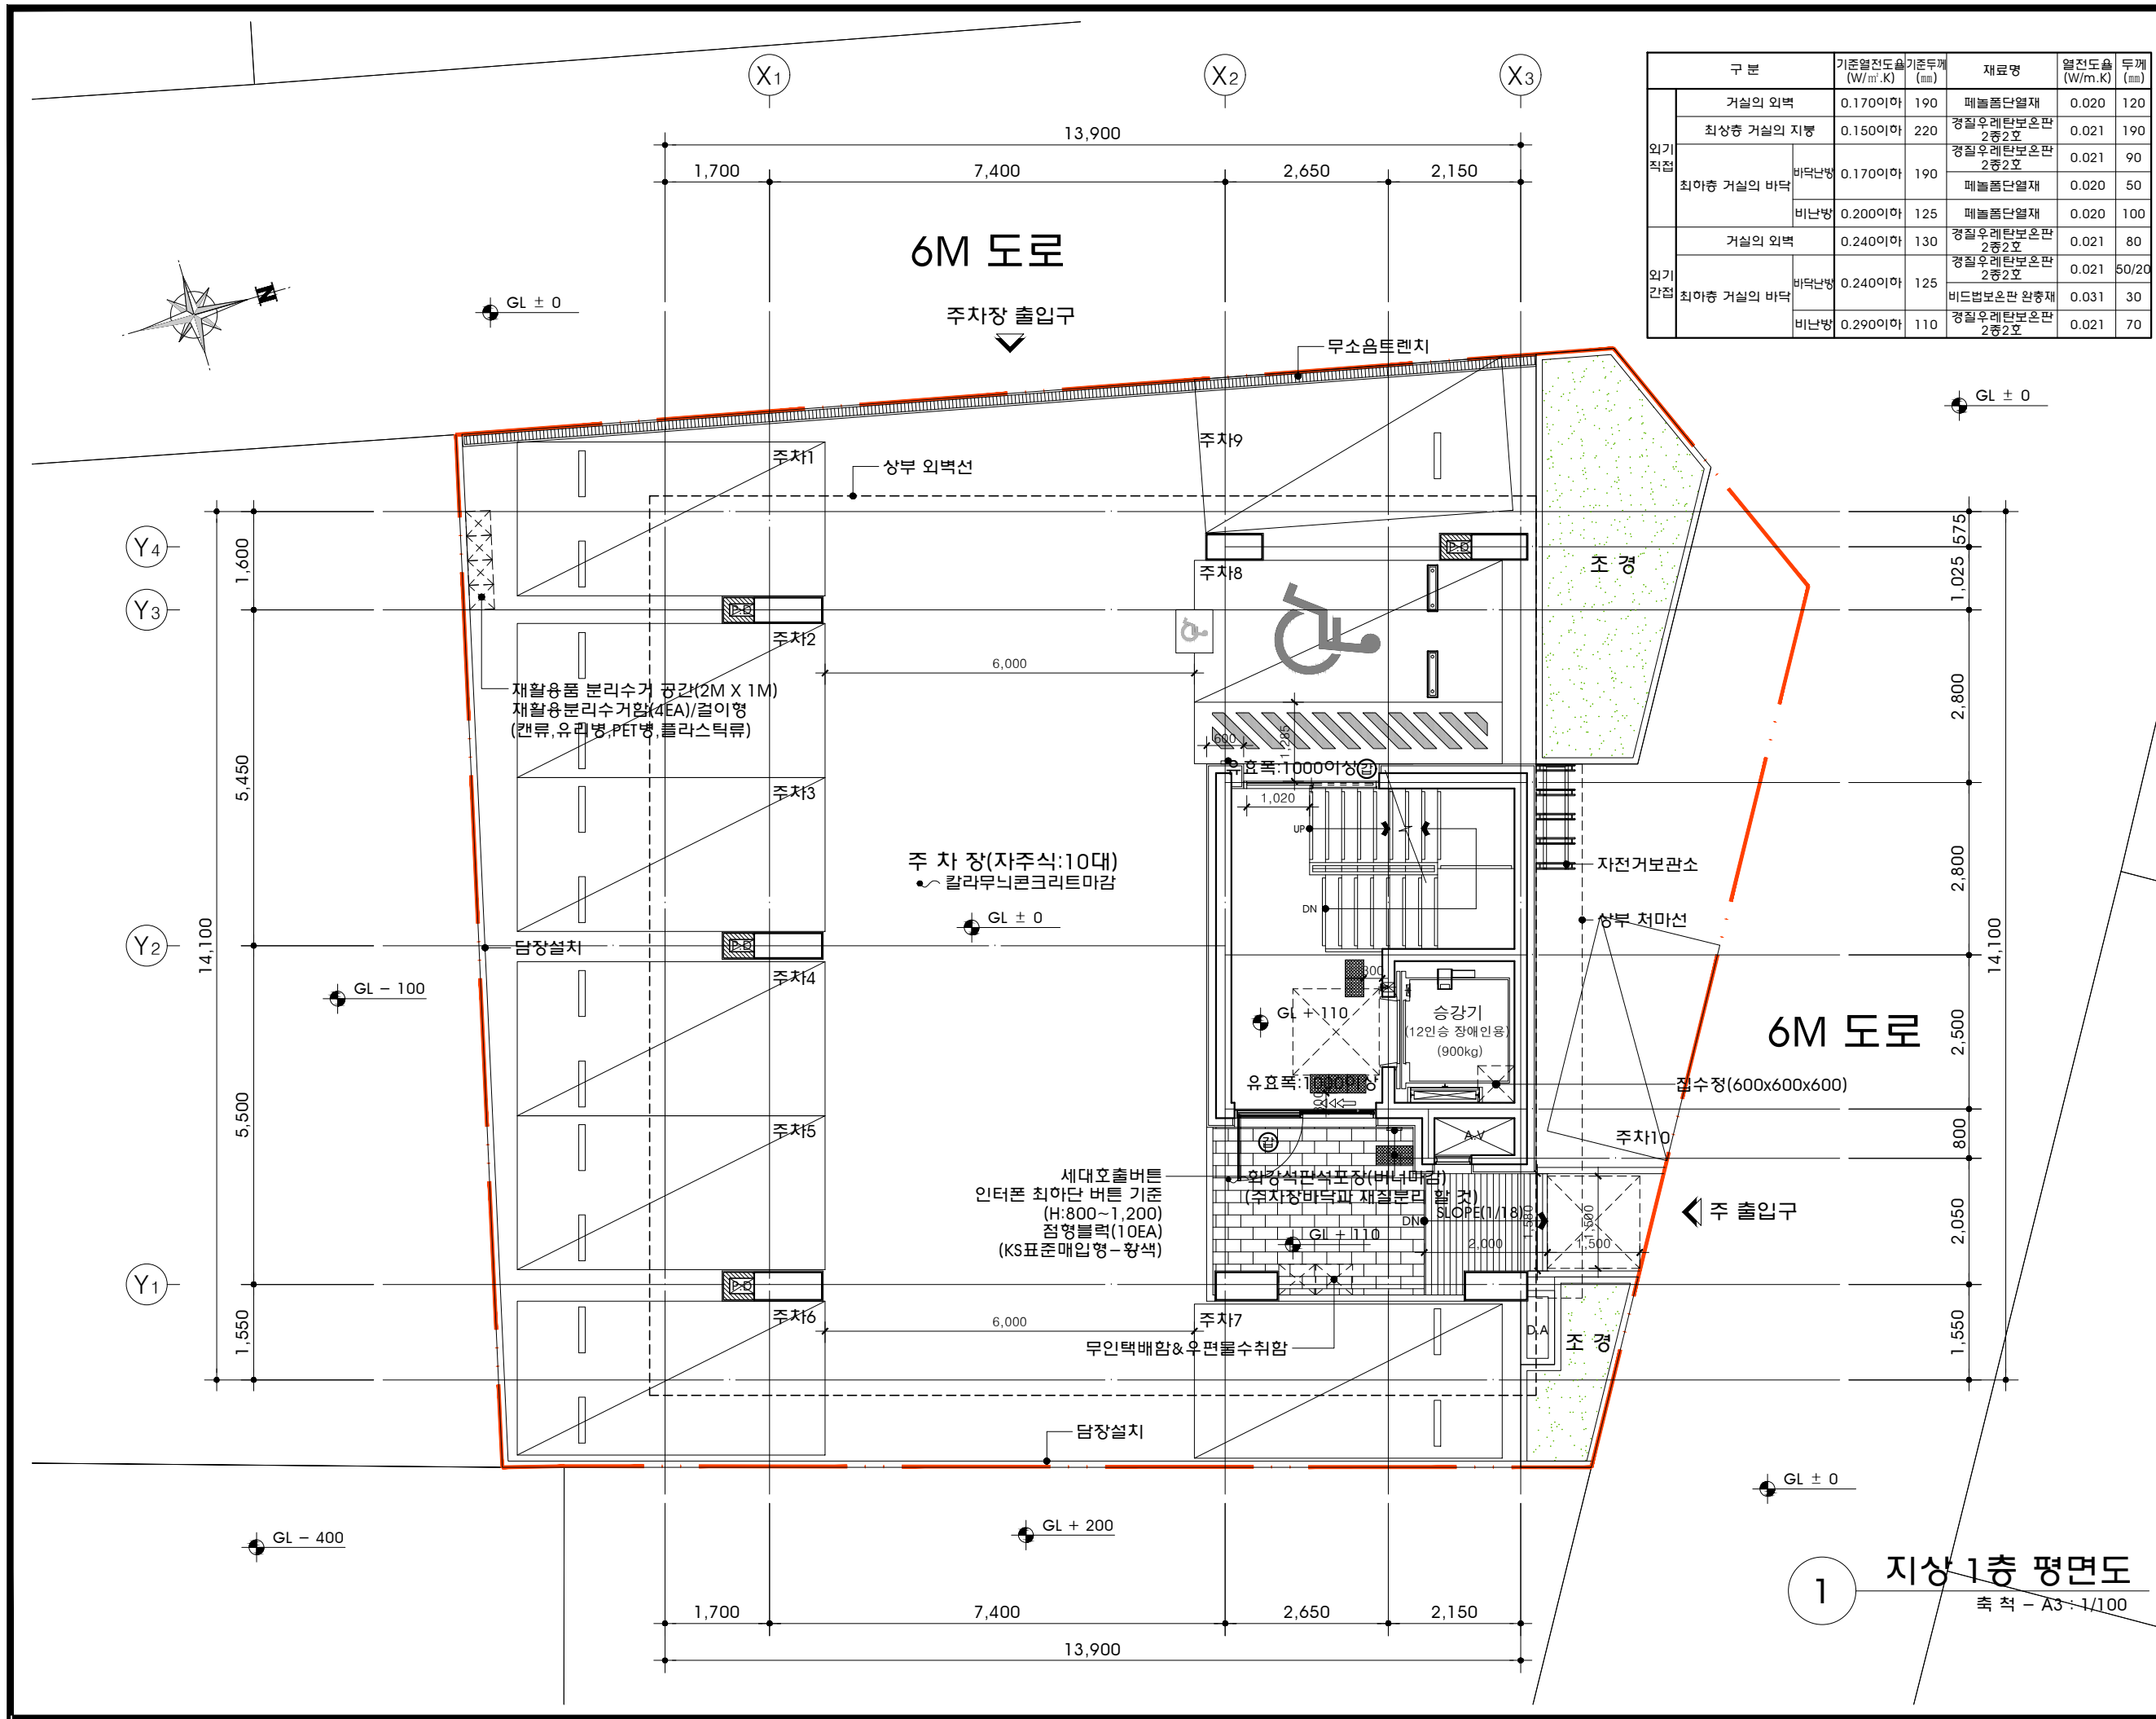

구분	기준열전도율 (W/m ² .K)	기준두께 (mm)	재료명	열전도율 (W/m.K)	두께 (mm)
외기 직접	거실의 외벽		페놀폼단열재	0.020	120
	최상층 거실의 지붕		경질우레탄보온판 2중2호	0.021	190
	최하층 거실의 바닥		경질우레탄보온판 2중2호	0.021	90
	비단난방		페놀폼단열재	0.020	50
외기 간접	비단난방		페놀폼단열재	0.020	100
	거실의 외벽		경질우레탄보온판 2중2호	0.021	80
	최하층 거실의 바닥		경질우레탄보온판 2중2호	0.021	50/20
	비단난방		비드법보온판 완충재	0.031	30
	비단난방		경질우레탄보온판 2중2호	0.021	70

Architecture Construction Management

DESIGN GROUP

(주)아키텍처 컨설팅

서울특별시 송파구 오금로 130(송파동) 2층
TEL : 02-2202-0066
FAX : 02-2202-0076

공사명
PROJECT TITLE

은평구 응암동 120-40번지
오피스텔(청년주택)
신축공사

NOTE

- 단독경보감지기
- ABC분말소화기(3.3KG)
- 60분+방화문, 60분 방화문
- 보일러
- 에어컨
- 실외기
- 차면시설
- *기둥 주위에 차량 보호대 설치
- *각세대 거실난간 국기꽃이 설치
- *승강기에 면한 침실 및 거실, 주방 방진패드 설치
- *저소음배관 시공
- *평면도 상세 치수는 단위세대 타입별 도면 참조

번호	수정내용	월	일	검토
△				
△				
△				
△				
△				
△				
△				
△				

작성일자
DATE

설계자
DRAWING BY

검토자
CHECKED BY

승인자
APPROVED BY

축척
SCALE

1/100

도면명
DRAWING TITLE

지상1층 평면도


일련번호
SHEET NO.

00-0000

도면번호
DRAWING NO.

A-102

1 지상 1층 평면도
축척 - A3 : 1/100

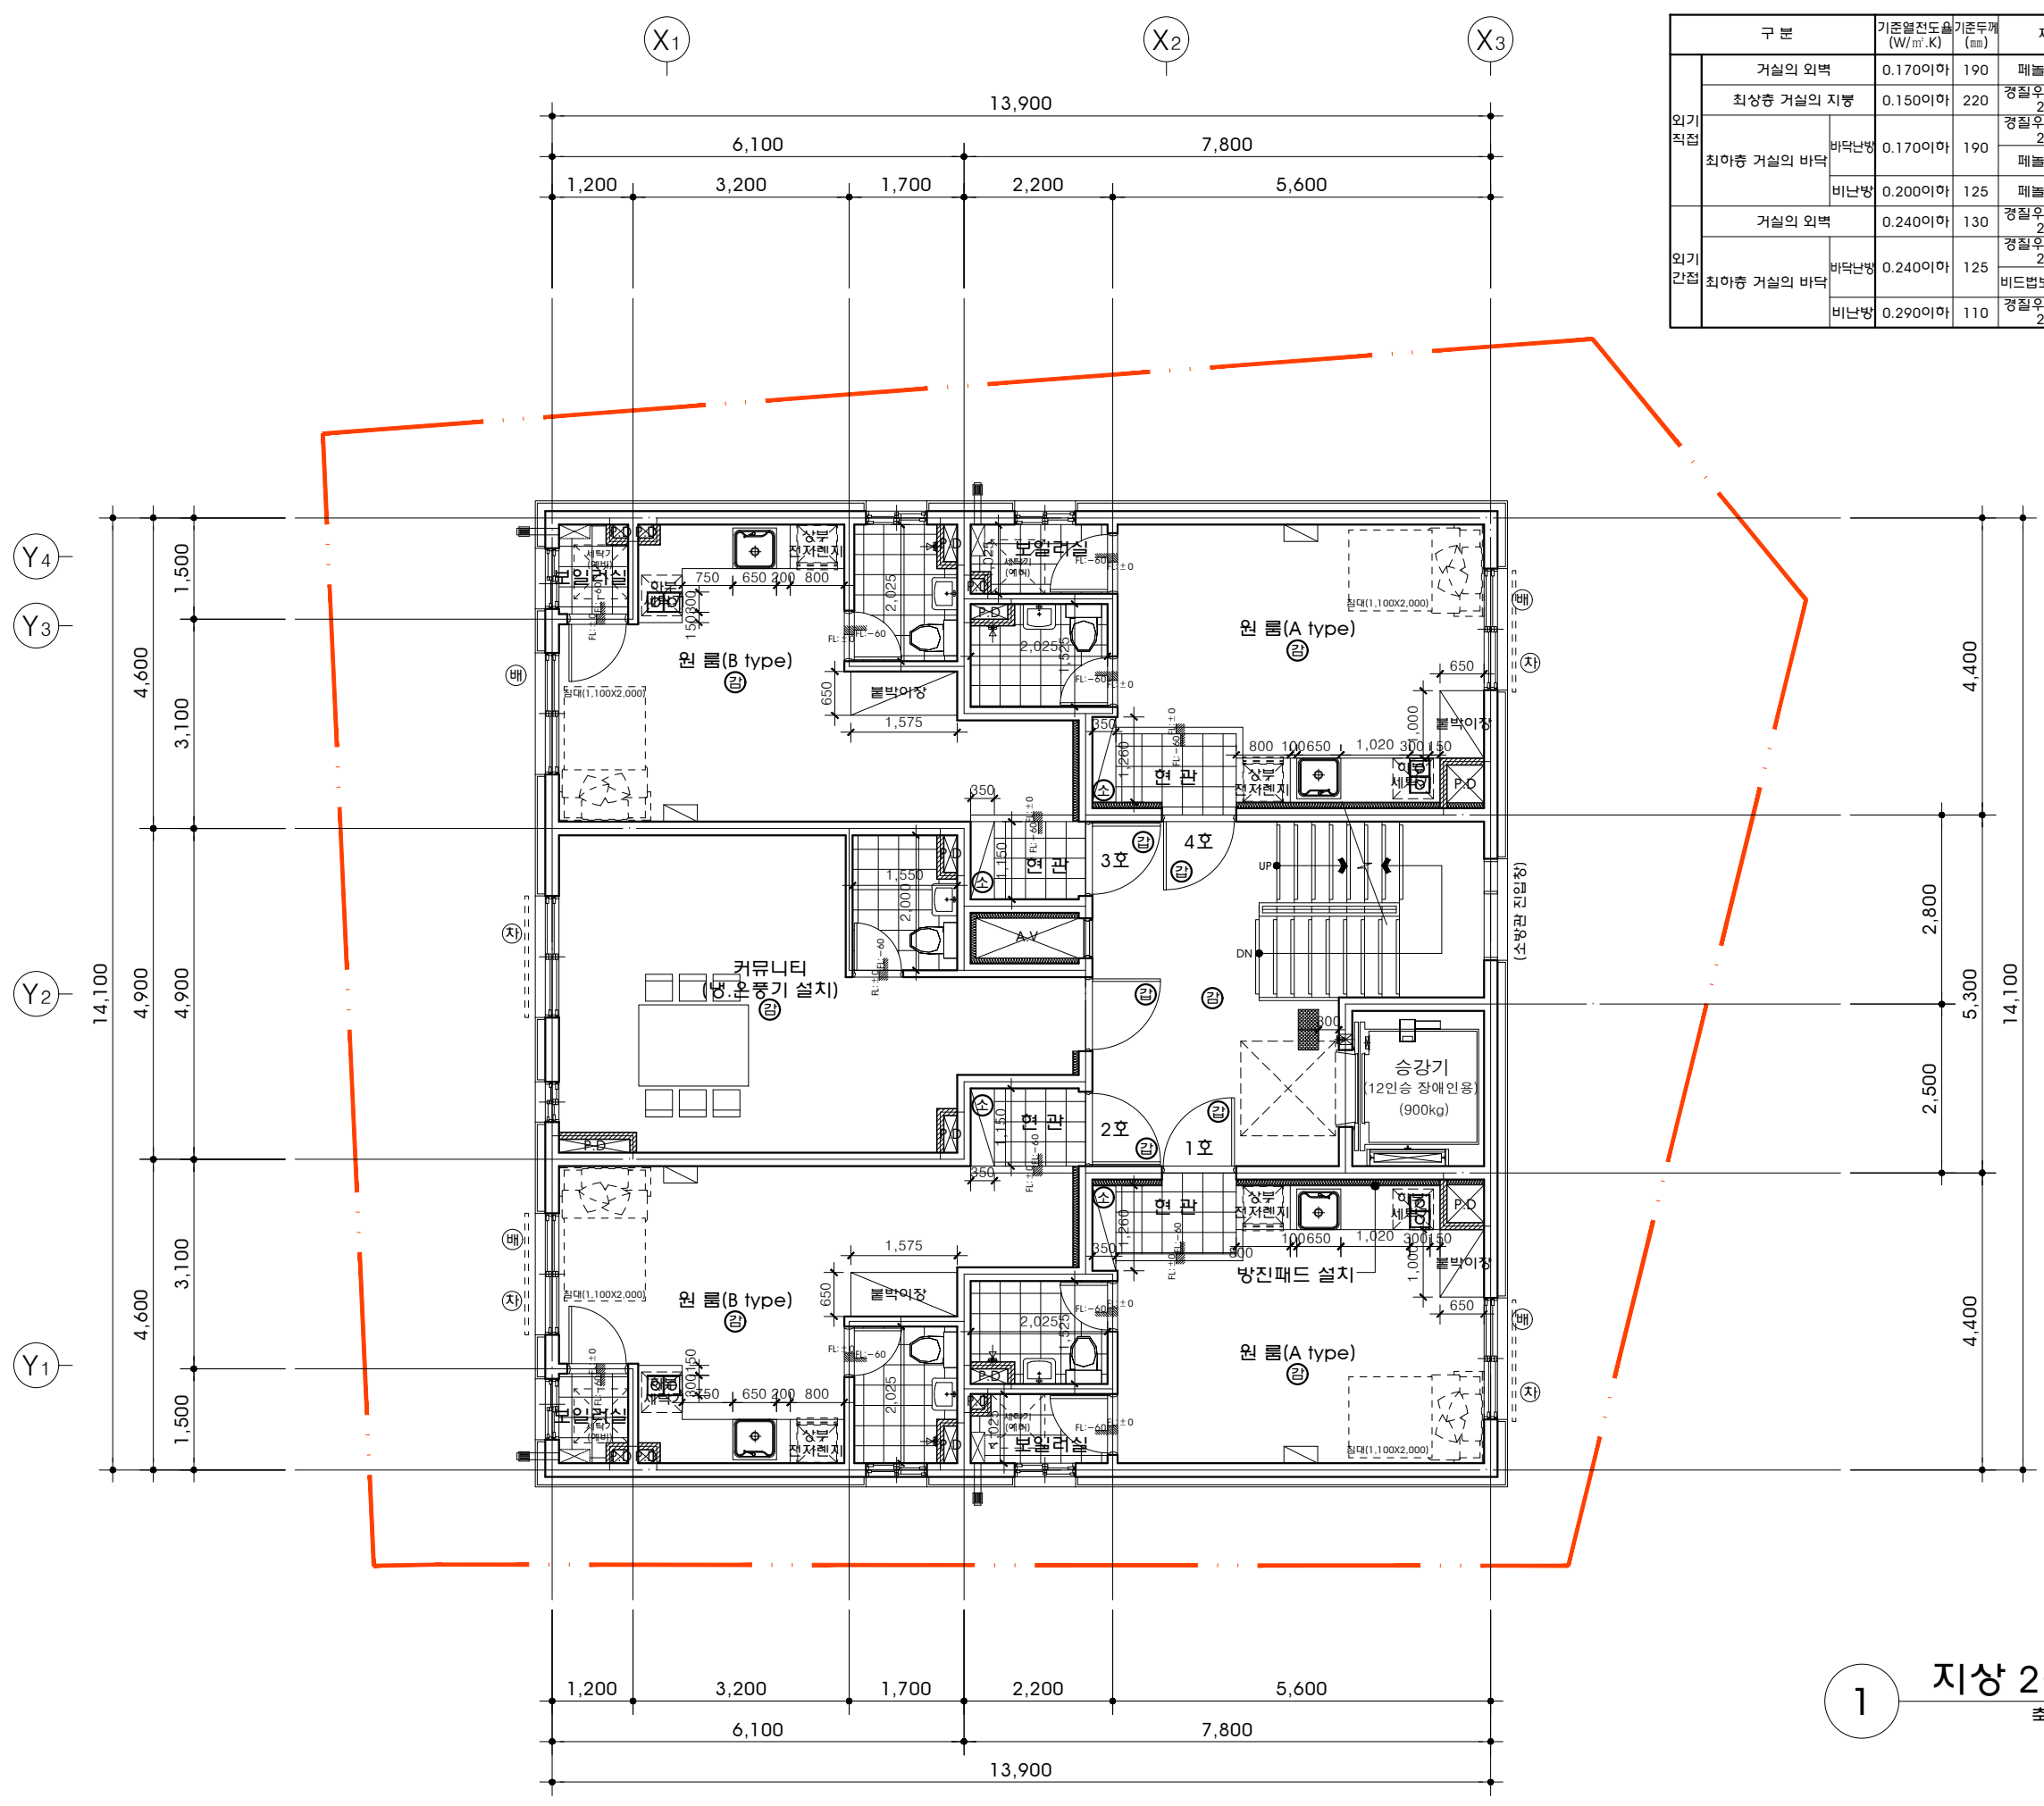

구분		기준열전도율 (W/m ² .K)	기준두께 (mm)	재료명	열전도율 (W/m.K)	두께 (mm)	
외기 직접	거실의 외벽		0.170이하	190	페놀폼단열재	0.020	120
	최상층 거실의 지붕		0.150이하	220	경질우레탄보온판 2중2호	0.021	190
	최하층 거실의 바닥	바닥난방	0.170이하	190	경질우레탄보온판 2중2호	0.021	90
		비난방	0.200이하	125	페놀폼단열재	0.020	50
					페놀폼단열재	0.020	100
외기 간접	거실의 외벽		0.240이하	130	경질우레탄보온판 2중2호	0.021	80
	최하층 거실의 바닥	바닥난방	0.240이하	125	경질우레탄보온판 2중2호	0.021	50/20
		비난방	0.290이하	110	비드법보온판 완충재	0.031	30
					경질우레탄보온판 2중2호	0.021	70

Architecture Construction Management

DESIGN GROUP

(주)아키텍처엔지니어링

서울특별시 송파구 오금로 130(송파동) 2층
TEL : 02-2202-0066
FAX : 02-2202-0076

공사명
PROJECT TITLE

은평구 응암동 120-40번지
오피스텔(청년주택)
신축공사

NOTE

- 단독경보감지기
- ABC분말소화기(3.3KG)
- 60분+방화문, 60분 방화문
- 보일러
- 에어컨
- 실외기
- 차면시설

*기둥 주위에 차량 보호대 설치
*각세대 거실난간 국기꽃이 설치
*승강기에 면한 침실 및 거실,
주방 방진패드 설치
*저소음배관 시공
*평면도 상세 치수는 단위세대
타입별 도면 참조

번호	수정내용	월	일	검토
△				
△				
△				
△				
△				
△				
△				
△				

작성일자
DATE

설계자
DRAWING BY

검토자
CHECKED BY

승인자
APPROVED BY

축척
SCALE

1/100

도면명
DRAWING TITLE

지상2층 평면도

일련번호
SHEET NO.

□□-□□□□

도면번호
DRAWING NO.

□A-□103

1 지상 2층 평면도
축척 - A3 : 1/100



archi CM
 Architecture Construction Management
 DESIGN GROUP

(주)아키텍처원 통합건축사사무소
 서울특별시 송파구 오금로 130(송파동) 2층
 TEL : 02-2202-0066
 FAX : 02-2202-0076

공사명
 PROJECT TITLE
 은평구 응암동 120-40번지
 오피스텔(청년주택)
 신축공사

NOTE

- ㉔ 단독경보감지기
- ㉔ ABC분말소화기(3.3KG)
- ㉔ 60분+방화문, 60분 방화문
- ㉔ 보일러
- ㉔ 에어컨
- ㉔ 실외기
- 차면시설

*기둥 주위에 차량 보호대 설치
 *각세대 거실난간 국기꽃이 설치
 *승강기에 면한 침실 및 거실, 주방 방진패드 설치
 *저소음배관 시공
 *평면도 상세 치수는 단위세대 타입별 도면 참조

번호	수정내용	월	일	검토
△				
△				
△				
△				
△				
△				
△				
△				

작성일자
DATE

설계자
DRAWING BY

검토자
CHECKED BY

승인자
APPROVED BY

축척
SCALE

1/100

도면명
DRAWING TITLE

지상3~7층 평면도


일련번호
SHEET NO.

□□-□□□□

도면번호
DRAWING NO.


□A-□104

구분		기준열전도율 (W/m ² .K)	기준두께 (mm)	재료명	열전도율 (W/m.K)	두께 (mm)
외기 직접	거실의 외벽	0.170이하	190	페놀폼단열재	0.020	120
	최상층 거실의 지붕	0.150이하	220	경질우레탄보온판 2중2호	0.021	190
	최하층 거실의 바닥	0.170이하	190	경질우레탄보온판 2중2호	0.021	90
				페놀폼단열재	0.020	50
외기 간접	거실의 외벽	0.240이하	130	경질우레탄보온판 2중2호	0.021	80
				경질우레탄보온판 2중2호	0.021	50/20
	최하층 거실의 바닥	0.240이하	125	비드법보온판 원충재	0.031	30
				경질우레탄보온판 2중2호	0.021	70

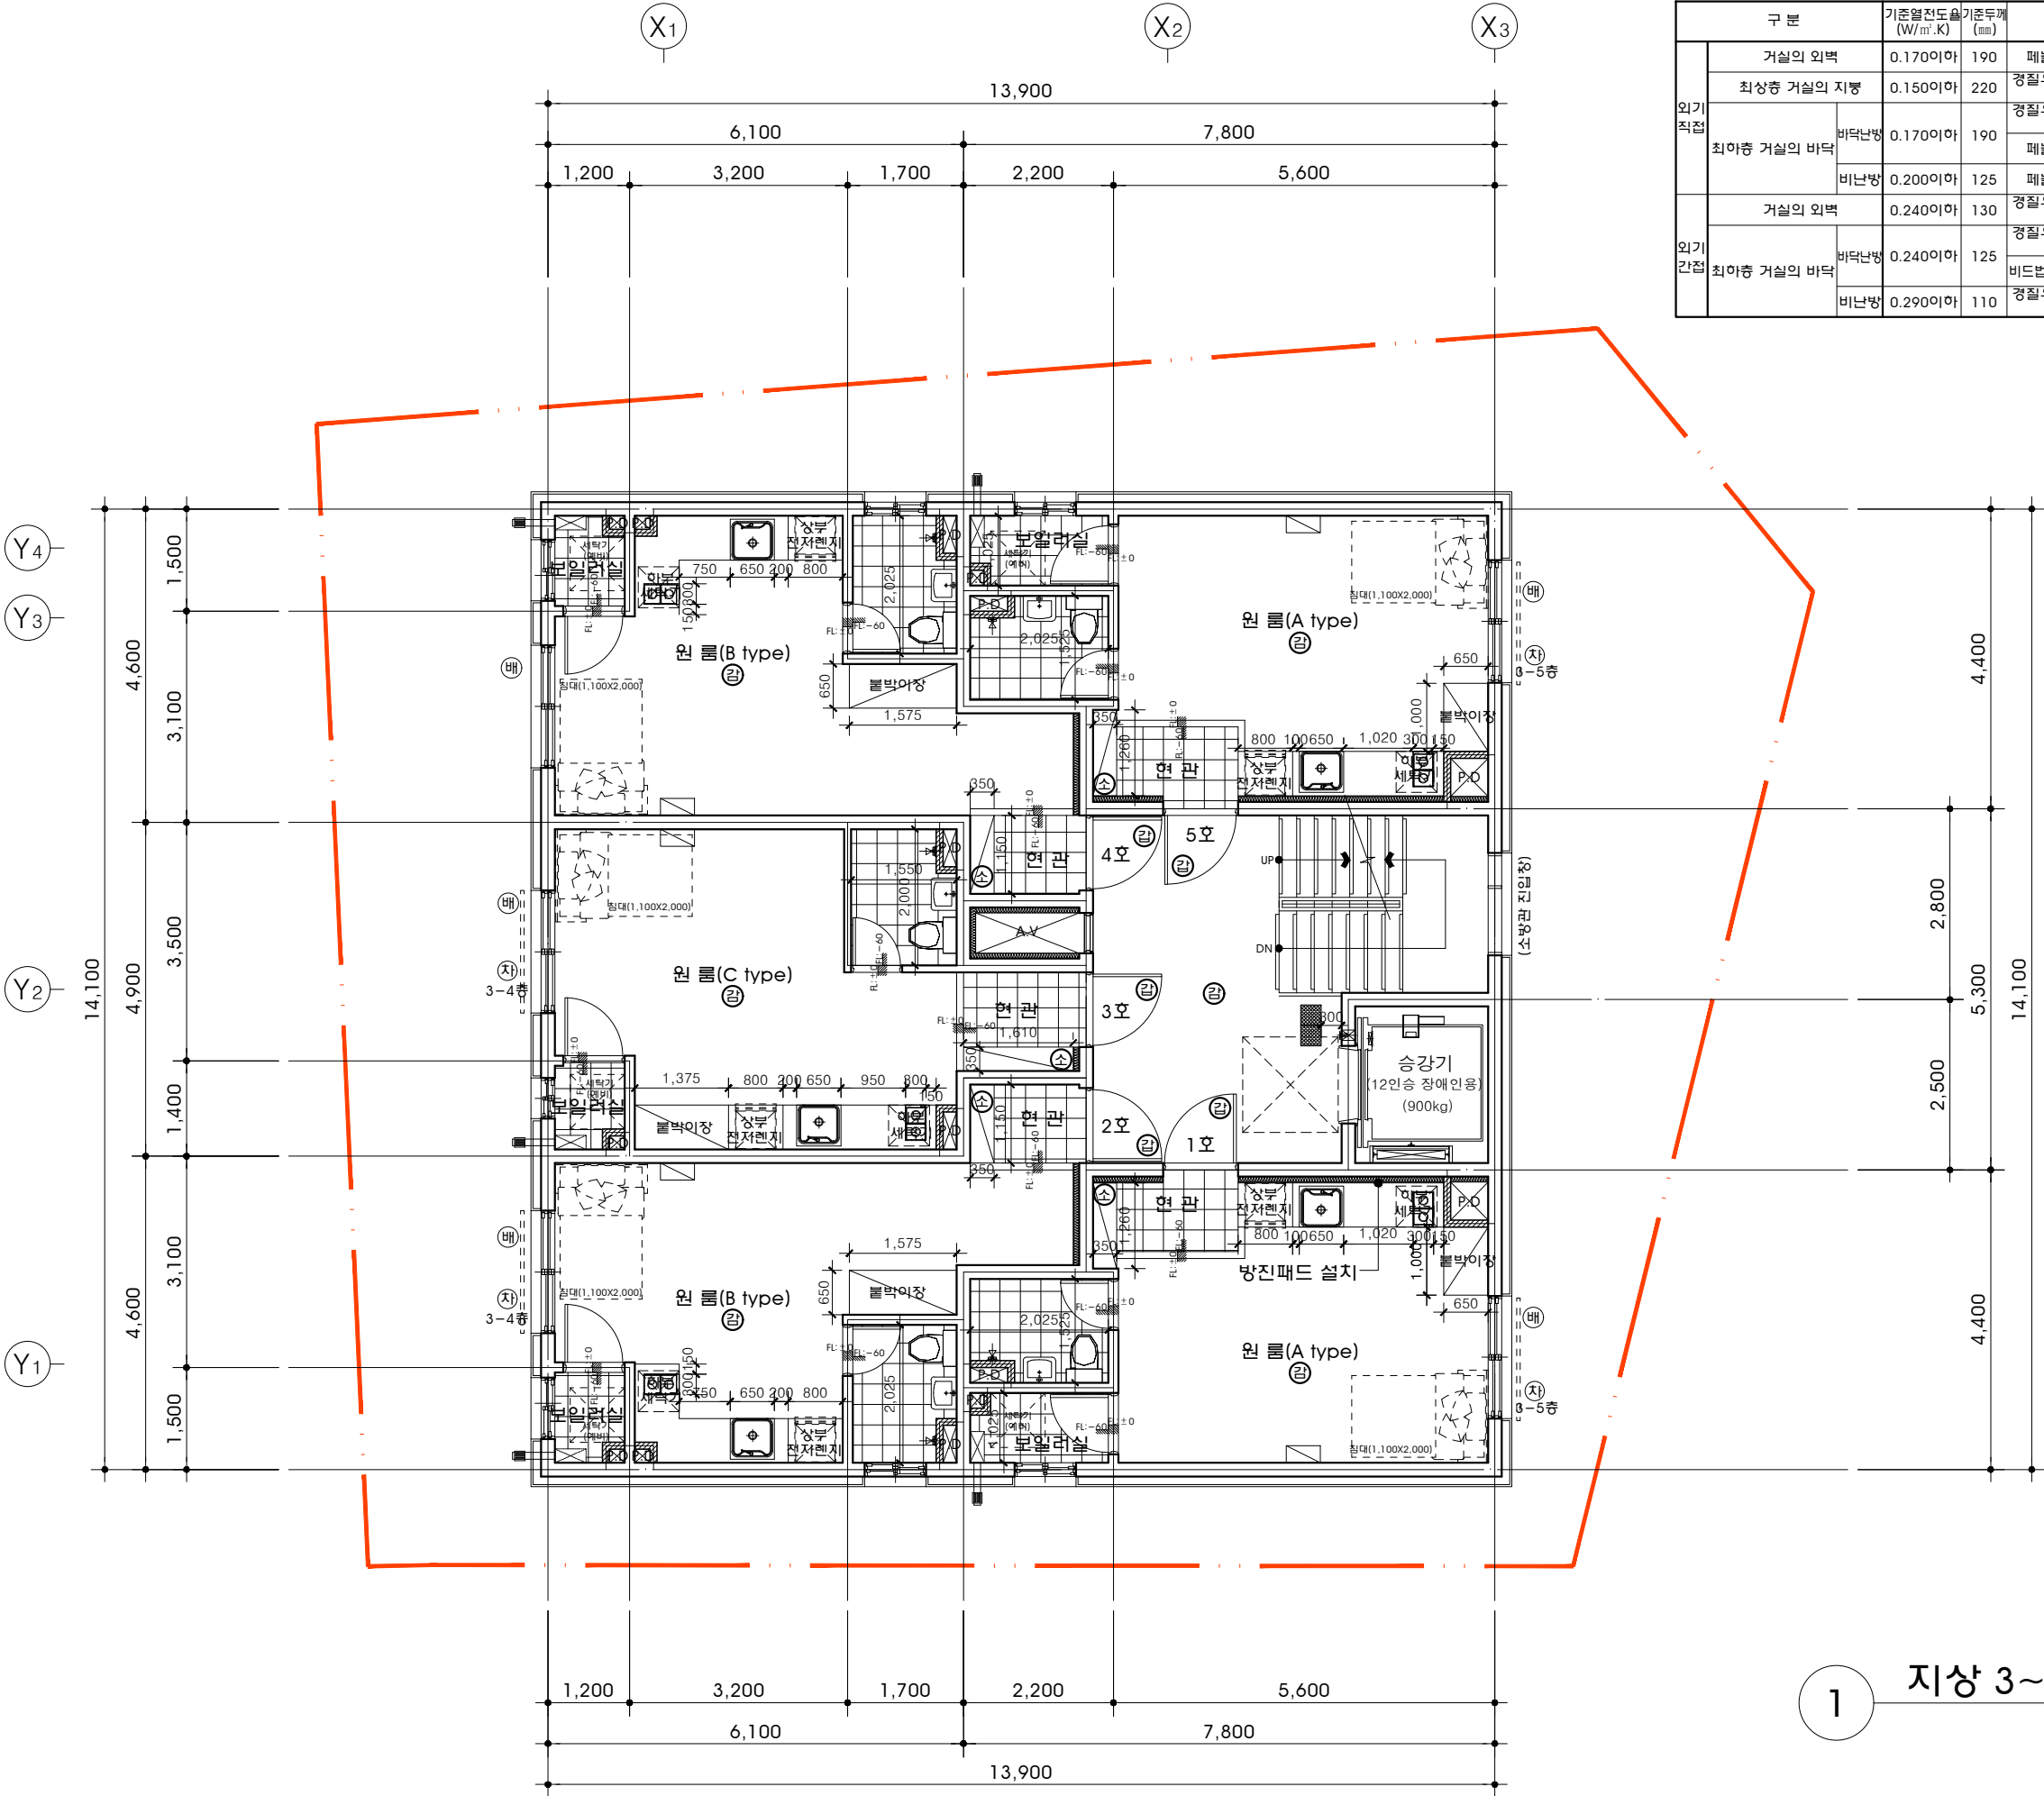

1

지상 3~7층 평면도
 축척 - A3 : 1/100

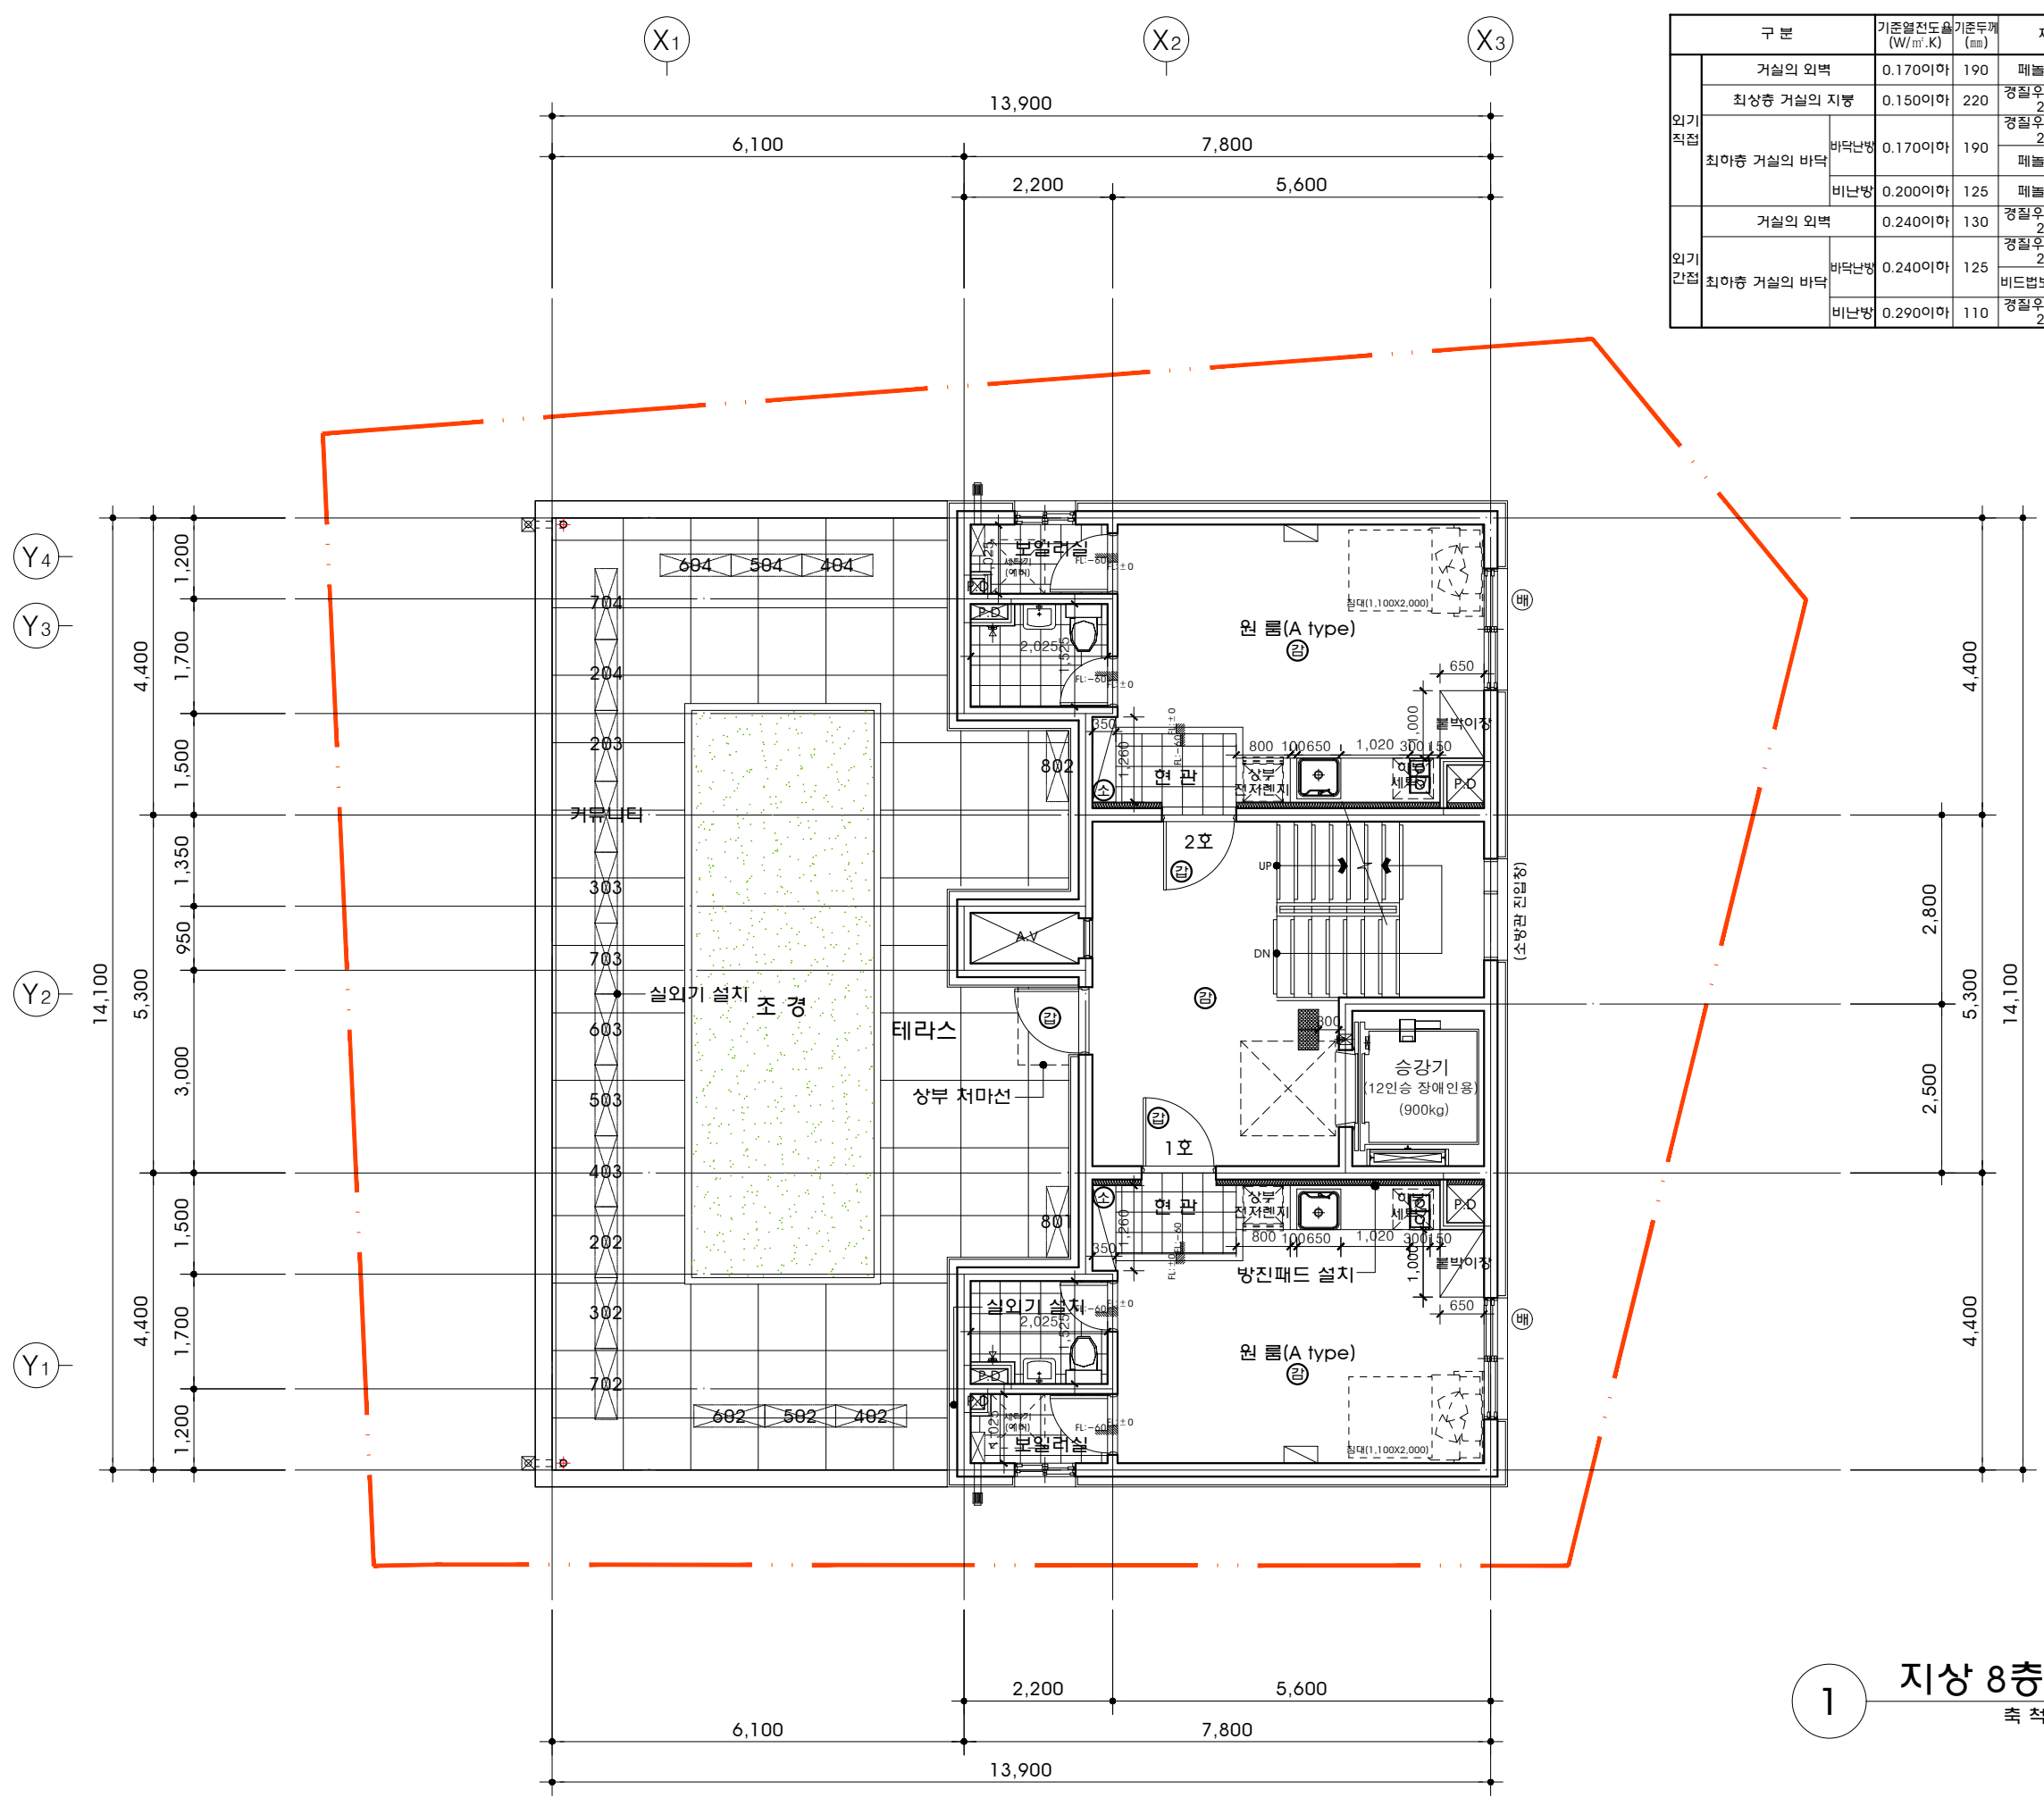

구분		기준열전도율 (W/m ² .K)	기준두께 (mm)	재료명	열전도율 (W/m.K)	두께 (mm)
외기 직접	거실의 외벽	0.170이하	190	페놀폼단열재	0.020	120
	최상층 거실의 지붕	0.150이하	220	경질우레탄보온판 2중2호	0.021	190
	최하층 거실의 바닥	0.170이하	190	경질우레탄보온판 2중2호	0.021	90
				페놀폼단열재	0.020	50
외기 간접	거실의 외벽	0.240이하	130	경질우레탄보온판 2중2호	0.021	80
				경질우레탄보온판 2중2호	0.021	50/20
	최하층 거실의 바닥	0.240이하	125	비드법보온판 완충재	0.031	30
				경질우레탄보온판 2중2호	0.021	70

Architecture Construction Management

DESIGN GROUP

(주)아키텍처엔지니어링

서울특별시 송파구 오금로 130(송파동) 2층
TEL : 02-2202-0066
FAX : 02-2202-0076

공사명
PROJECT TITLE

은평구 응암동 120-40번지
오피스텔(청년주택)
신축공사

NOTE

- 단독경보감지기
- ABC분말소화기(3.3KG)
- 60분+방화문, 60분 방화문
- 보일러
- 에어컨
- 실외기
- 차면시설

*기둥 주위에 차량 보호대 설치
*각세대 거실난간 국기꽃이 설치
*승강기에 면한 침실 및 거실, 주방 방진패드 설치
*저소음배관 시공
*평면도 상세 치수는 단위세대 타입별 도면 참조

번호	수정내용	월	일	검토
△				
△				
△				
△				
△				
△				
△				
△				

작성일자
DATE

설계자
DRAWING BY

검토자
CHECKED BY

승인자
APPROVED BY

축척
SCALE

1/100

도면명
DRAWING TITLE

지상8층 평면도


일련번호
SHEET NO.

□□-□□□□

도면번호
DRAWING NO.

□A-□105

1 지상 8층 평면도
축척 - A3 : 1/100

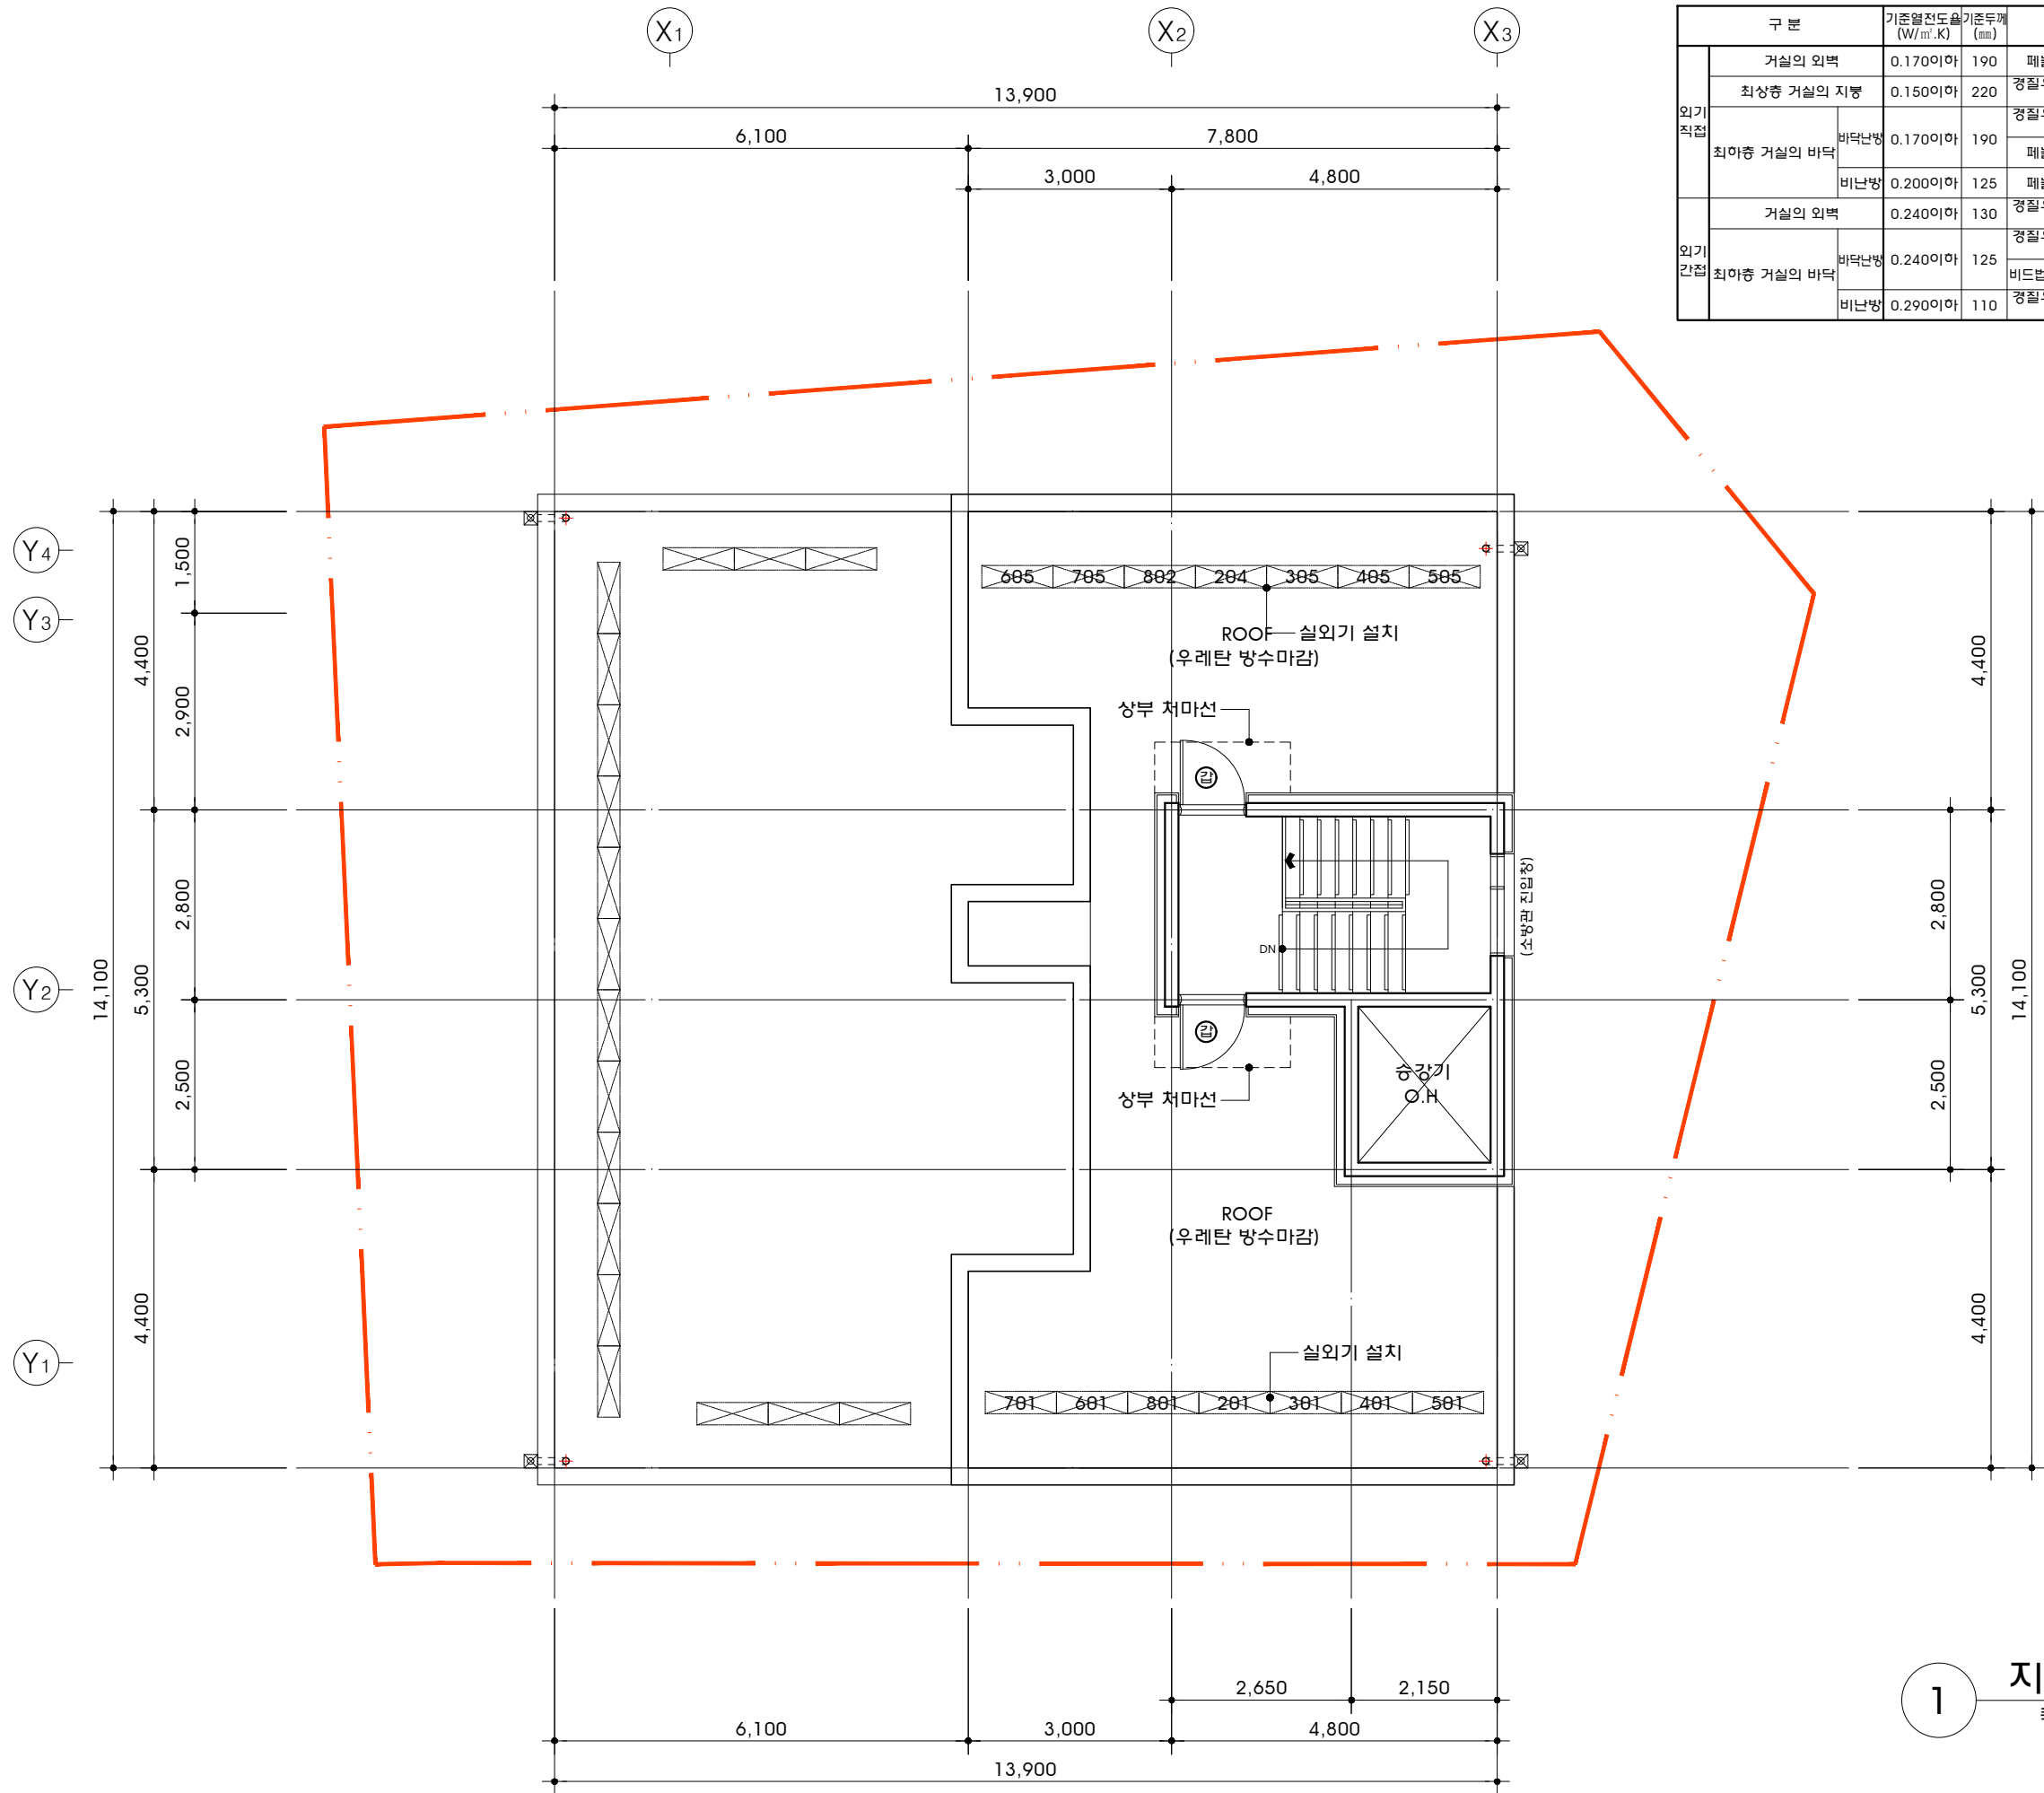

1 지붕 평면도
축척 - A3 : 1/100

archi CM
Architecture Construction Management
DESIGN GROUP

(주)아키텍처엔지니어링
서울특별시 송파구 오금로 130(송파동) 2층
TEL : 02-2202-0066
FAX : 02-2202-0076

공사명
PROJECT TITLE
은평구 응암동 120-40번지
오피스텔(청년주택)
신축공사

NOTE
 (단) 단독경보감지기
 (ABC) ABC분말소화기(3.3KG)
 (방) 60분+방화문, 60분 방화문
 (보) 보일러
 (에) 에어컨
 (실) 실외기
 (차) 차면시설
 *기둥 주위에 차방 보호대 설치
 *각세대 거실난간 국기꽃이 설치
 *승강기에 면한 침실 및 거실, 주방 방진패드 설치
 *저소음배관 시공
 *평면도 상세 치수는 단위세대 타입별 도면 참조

번호	수정내용	월	일	검토
△				
△				
△				
△				
△				
△				
△				
△				

작성일자
DATE

설계자
DRAWING BY

검토자
CHECKED BY


승인자
APPROVED BY

축척
SCALE
1/100

도면명
DRAWING TITLE
지붕 평면도


일련번호
SHEET NO.
□□-□□□□

도면번호
DRAWING NO.
□A-□106

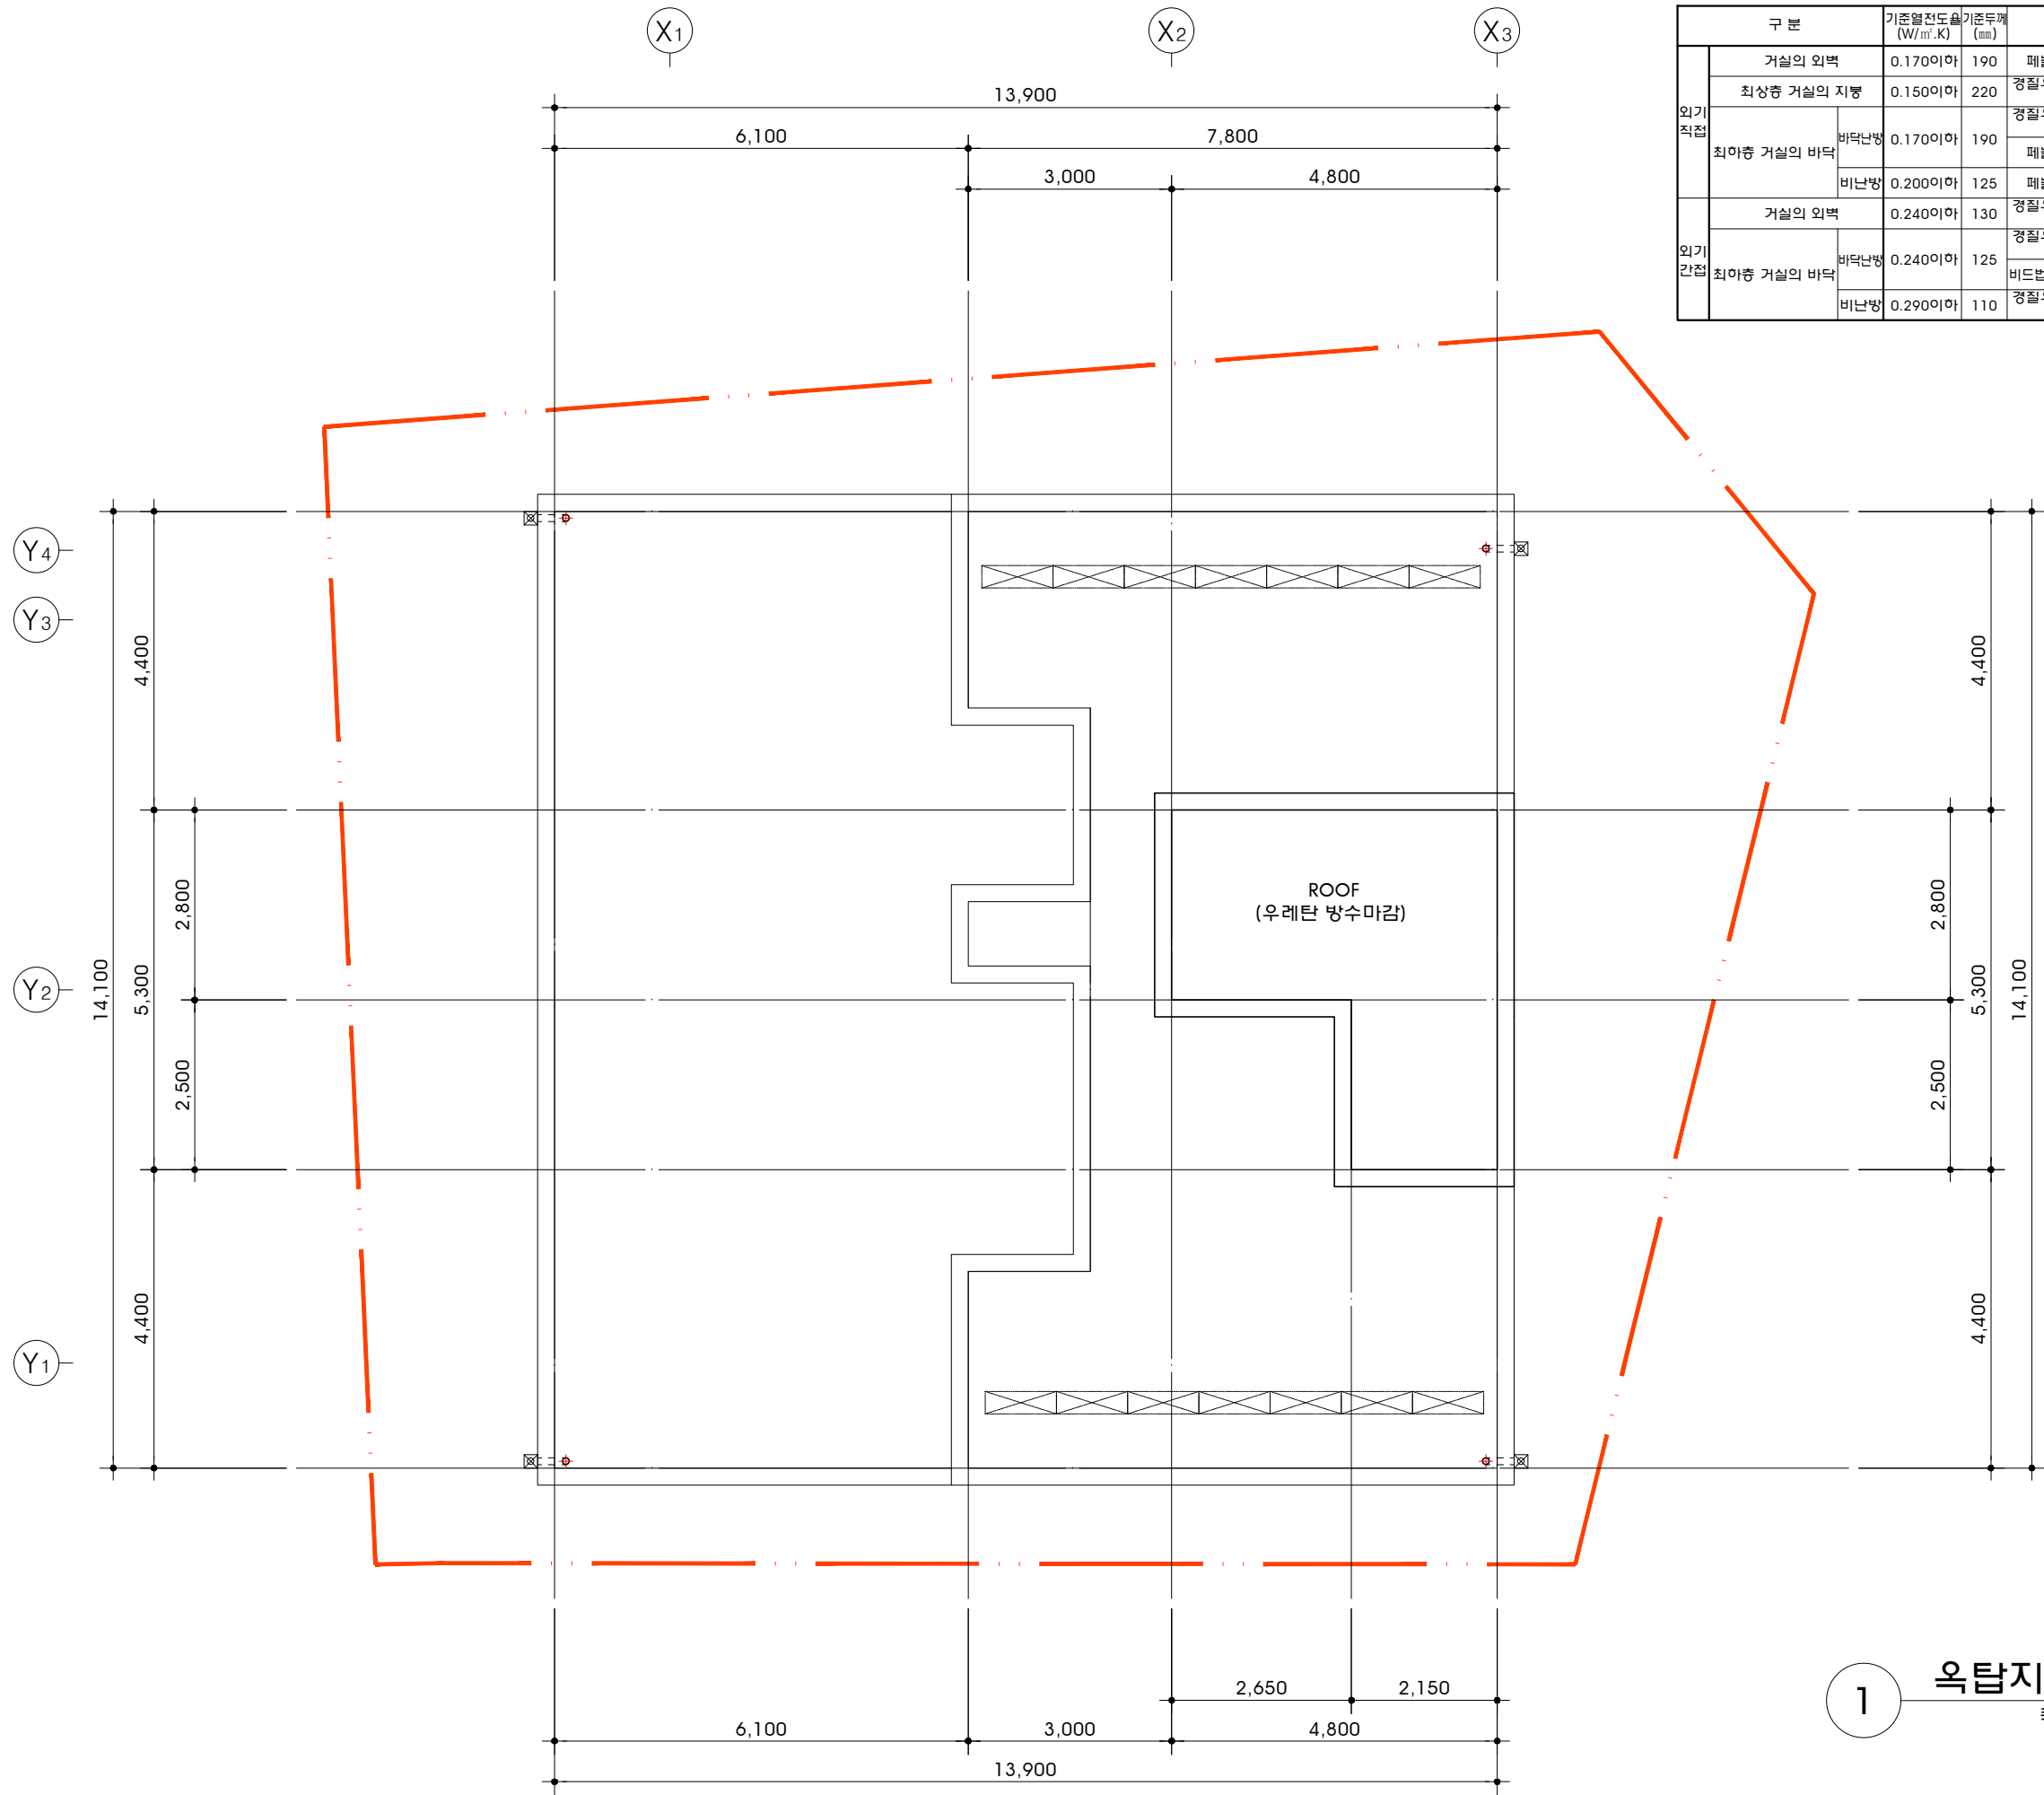

구분		기준열전도율 (W/m ² .K)	기준두께 (mm)	재료명	열전도율 (W/m.K)	두께 (mm)
외기 직접	거실의 외벽	0.170이하	190	페놀폼단열재	0.020	120
	최상층 거실의 지붕	0.150이하	220	경질우레탄보온판 2중2호	0.021	190
	최하층 거실의 바닥	0.170이하	190	경질우레탄보온판 2중2호	0.021	90
				페놀폼단열재	0.020	50
외기 간접	거실의 외벽	0.240이하	130	경질우레탄보온판 2중2호	0.021	80
				경질우레탄보온판 2중2호	0.021	50/20
	최하층 거실의 바닥	0.240이하	125	비드법보온판 완충재	0.031	30
				경질우레탄보온판 2중2호	0.021	70

번호	수정내용	월	일	검토
△				
△				
△				
△				
△				
△				
△				
△				

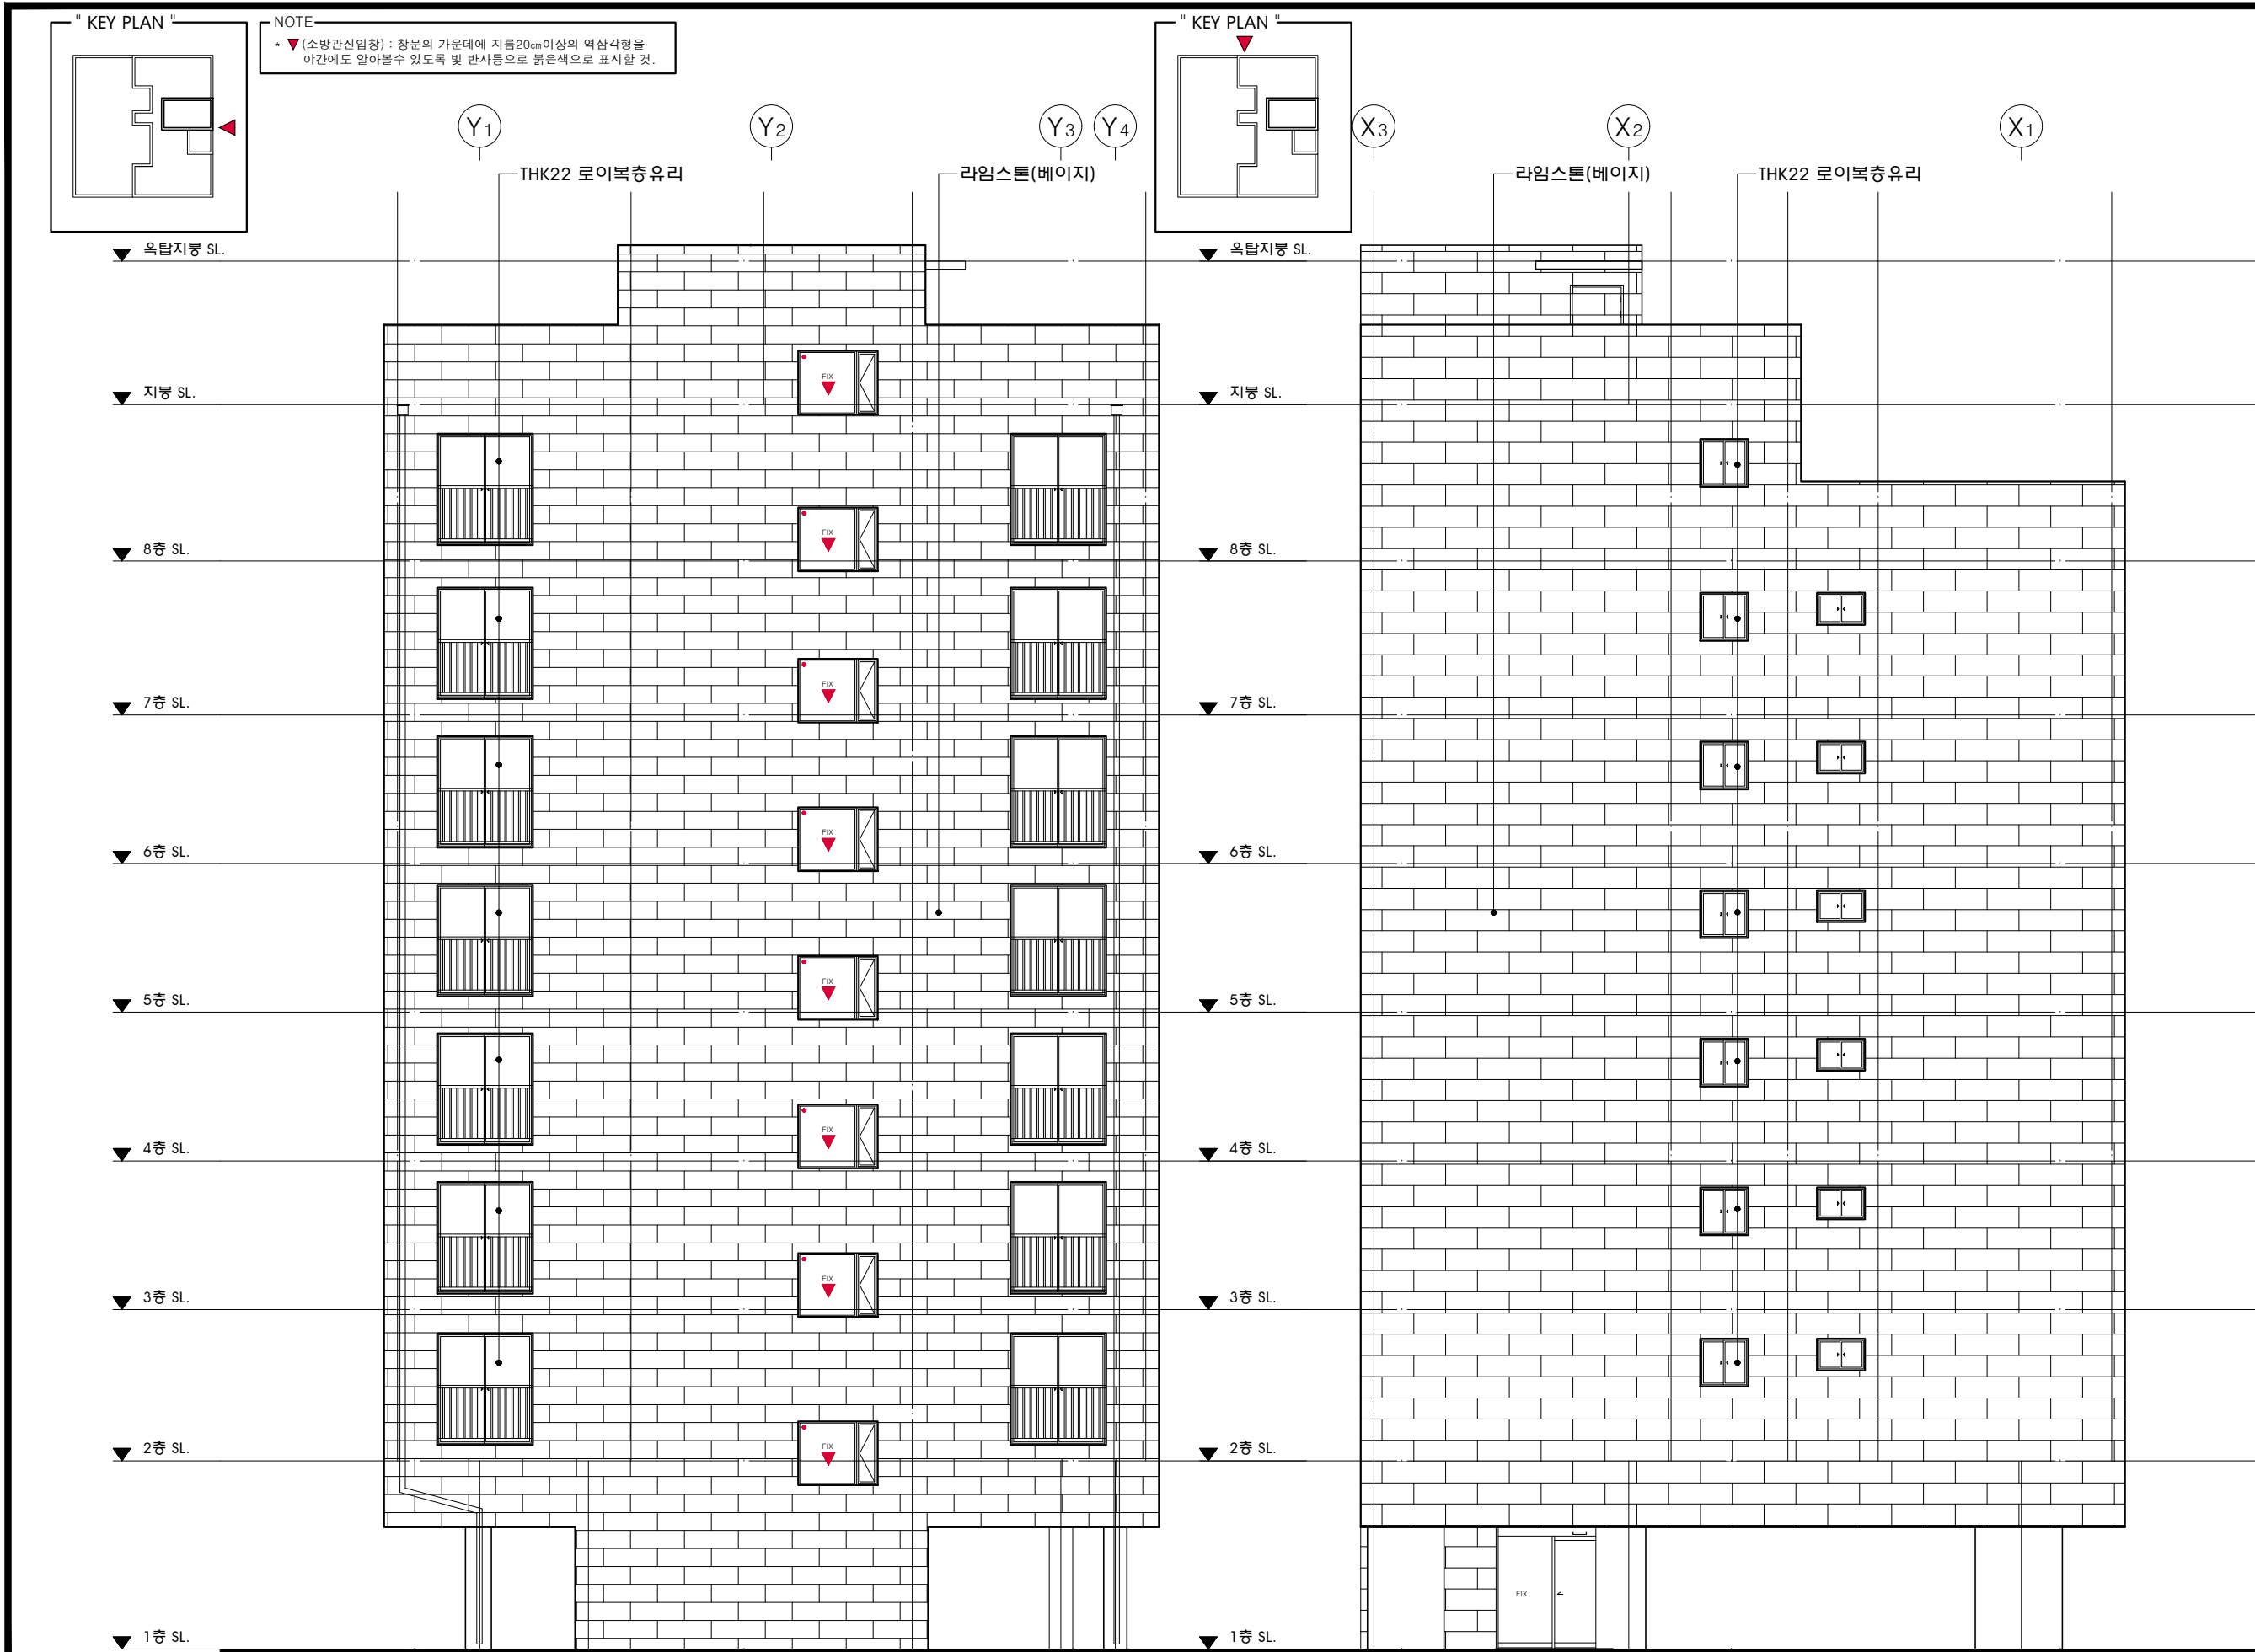

1 정 면 도
축척 - A3 : 1/120

2 우 측 면 도
축척 - A3 : 1/120

archi CM
Architecture Construction Management
DESIGN GROUP

(주)아키텍처 컨설팅
서울특별시 송파구 오금로 130(송파동) 2층
TEL : 02-2202-0066
FAX : 02-2202-0076

공사명
PROJECT TITLE
은평구 응암동 120-40번지
오피스텔(청년주택)
신축공사

NOTE

번호	수정내용	월	일	검토
△				
△				
△				
△				
△				
△				
△				
△				

작성일자
DATE

설계자
DRAWING BY

검토자
CHECKED BY


승인자
APPROVED BY

축척
SCALE
1/120

도면명
DRAWING TITLE
정면도, 우측면도

일련번호
SHEET NO.
00-0000

도면번호
DRAWING NO.
A-0301

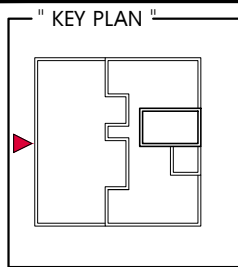

옥탑지붕 SL.

지붕 SL.

8층 SL.

7층 SL.

6층 SL.

5층 SL.

4층 SL.

3층 SL.

2층 SL.

1층 SL.

Y4 Y3


THK22 로이복층유리

Y2

THK22 로이복층유리

Y1

라임스톤(베이지)

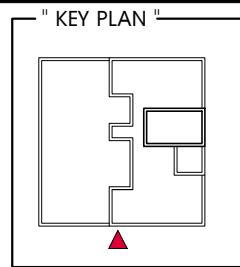

옥탑지붕 SL.

지붕 SL.

8층 SL.

7층 SL.

6층 SL.

5층 SL.

4층 SL.

3층 SL.

2층 SL.

1층 SL.

X1

X2

THK22 로이복층유리

X3

라임스톤(베이지)

1

배 면 도

축척 - A3 : 1/120

2

좌 측 면 도

축척 - A3 : 1/120

번호	수정내용	월	일	검토
△				
△				
△				
△				
△				
△				
△				

작성일자
DATE

설 계 자
DRAWING BY

검 토 자
CHECKED BY

승 인 자
APPROVED BY

축 척
SCALE
1/120

도 면 명
DRAWING TITLE









배 면 도, 좌 측 면 도

일련번호
SHEET NO.

00-0000

도면번호
DRAWING NO.

A-0302

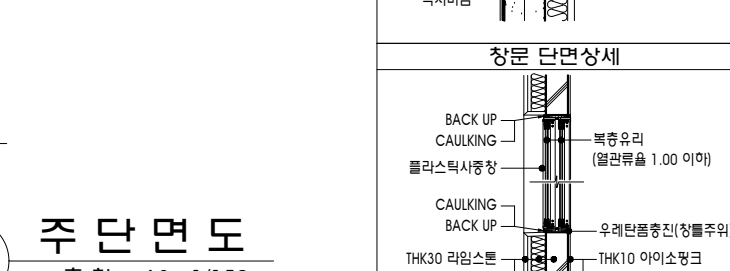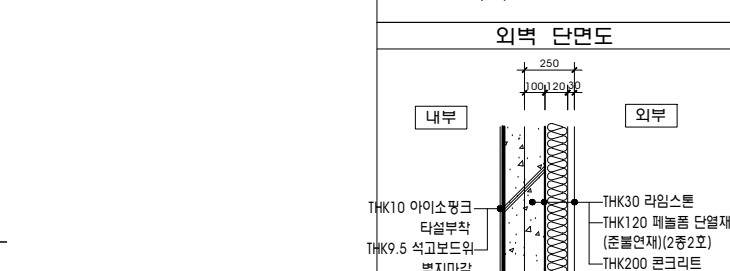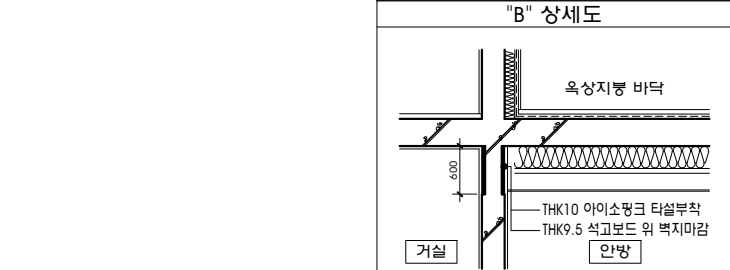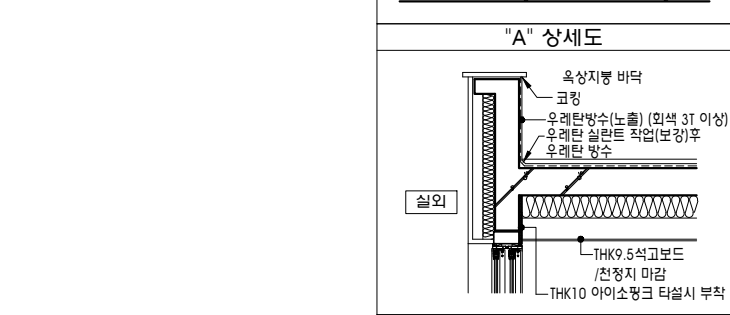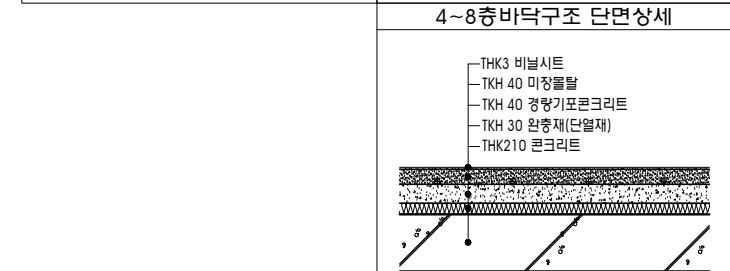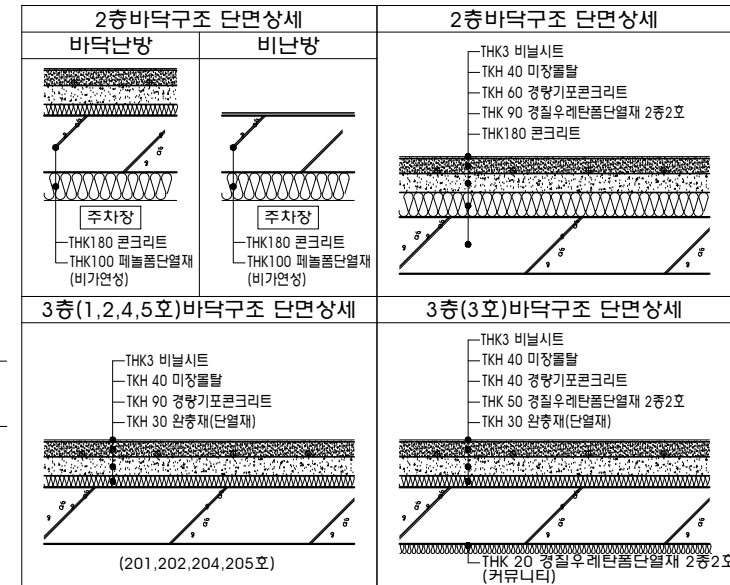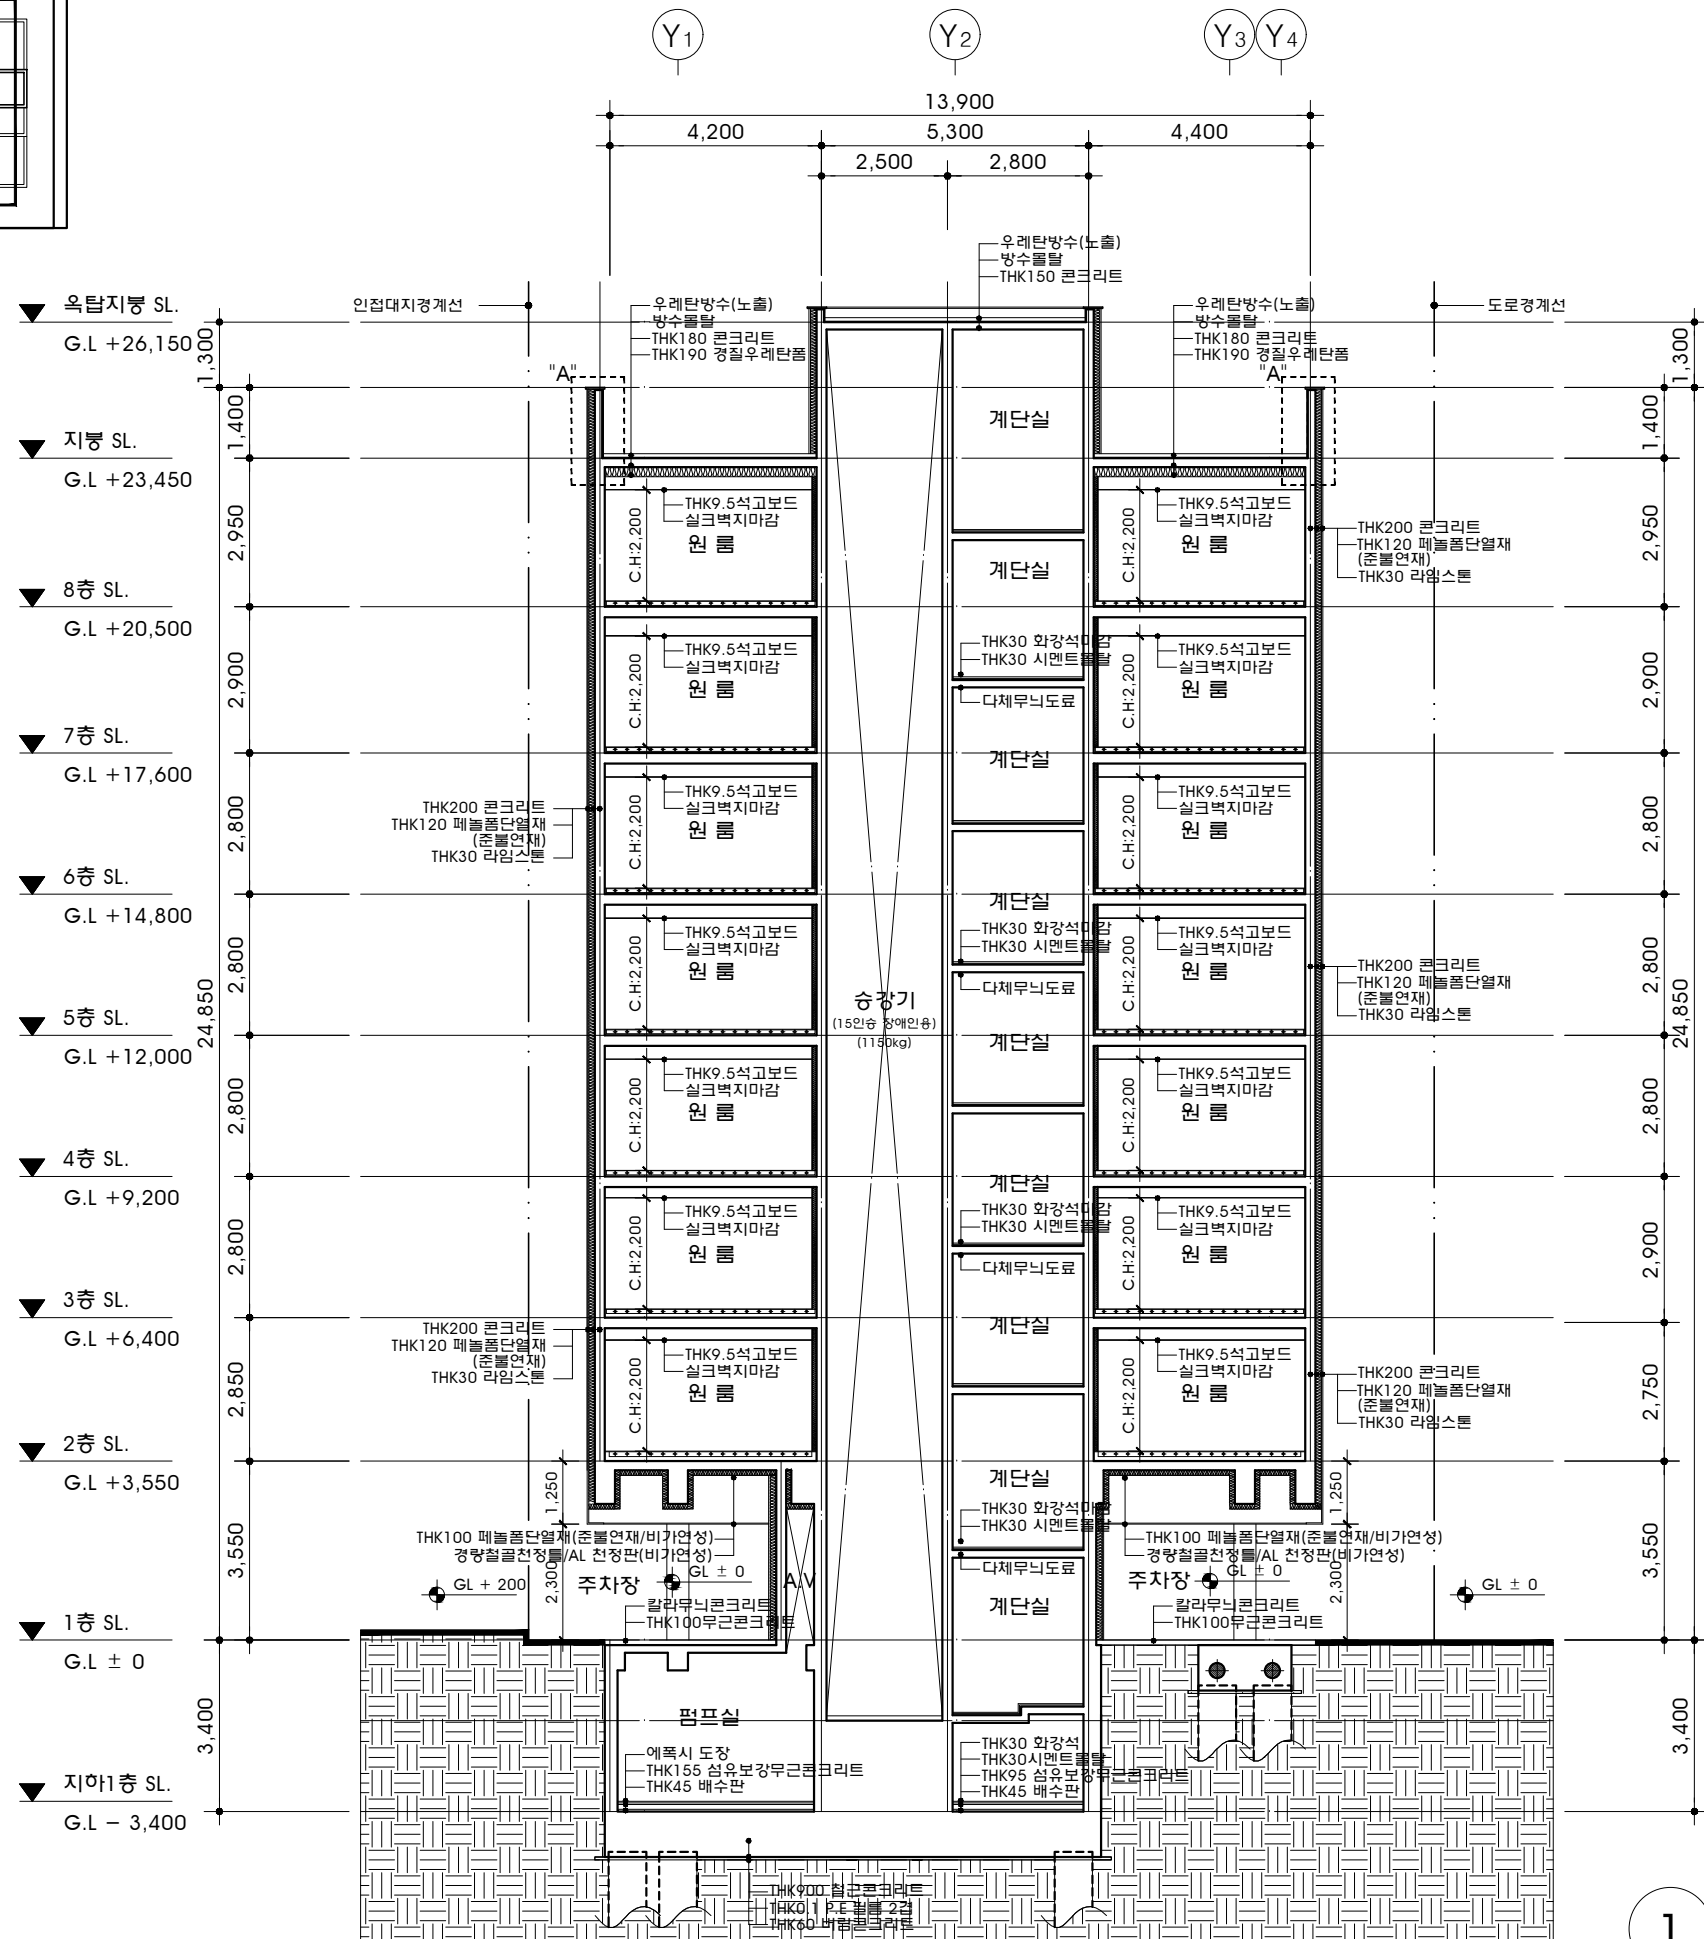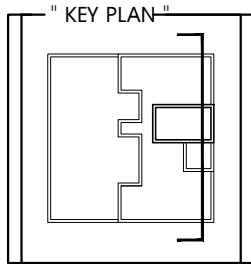

1 주 단면도
축척 - A3 : 1/150

Architecture Construction Management
DESIGN GROUP

(주)아치씨엠 통합건축사사무소

서울특별시 송파구 오금로 130(송파동) 2층
TEL : 02-2202-0066
FAX : 02-2202-0076

공사명
PROJECT TITLE

은평구 응암동 120-40번지
오피스텔(청년주택)
신축공사

NOTE

번호	수정내용	월	일	검토
△				
△				
△				
△				
△				
△				
△				

작성일자
DATE

설계자
DRAWING BY

검토자
CHECKED BY

승인자
APPROVED BY

축척
SCALE

1/150

도면명
DRAWING TITLE










주 단면도

일련번호
SHEET NO.

00-0000

도면번호
DRAWING NO.

A-401

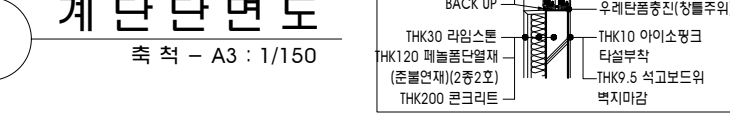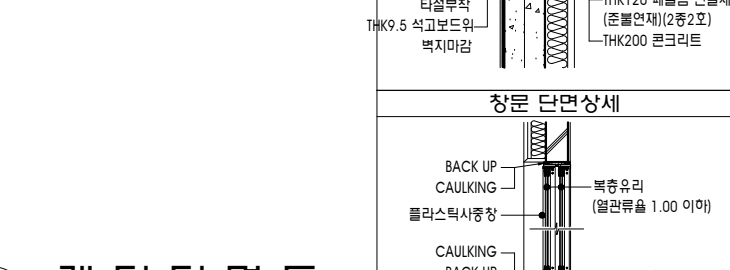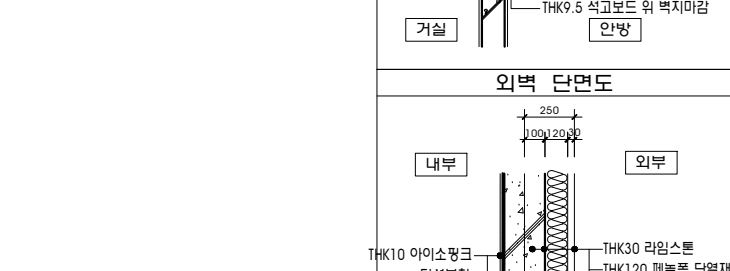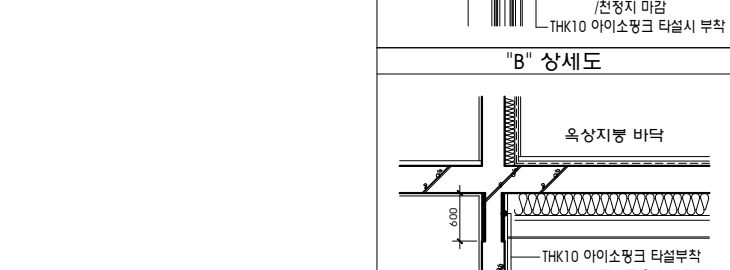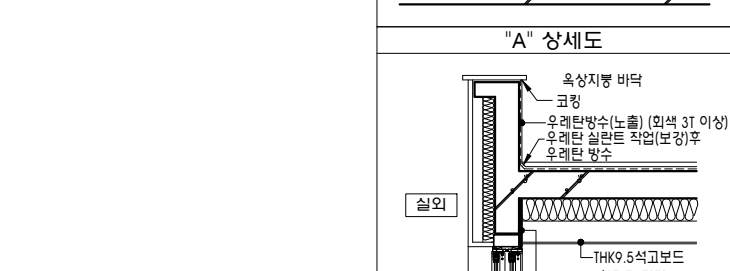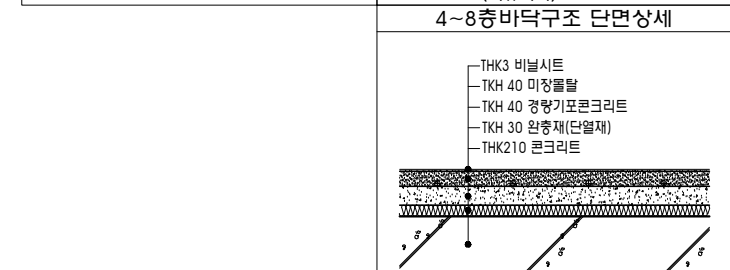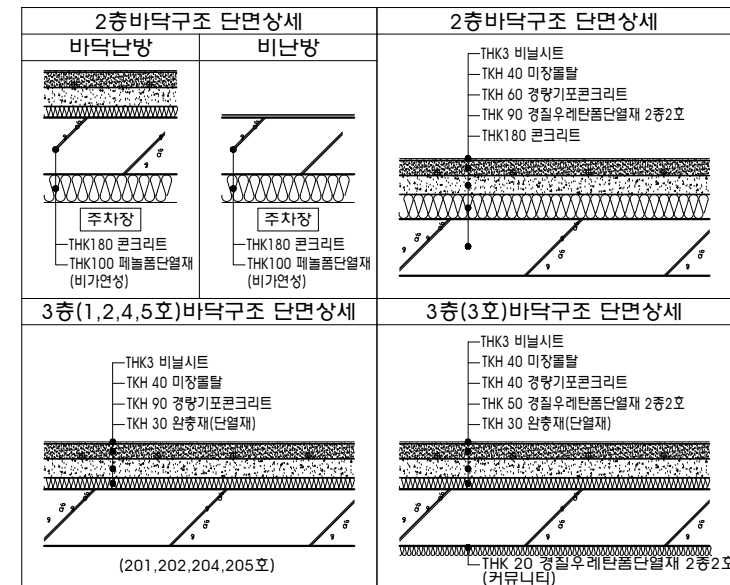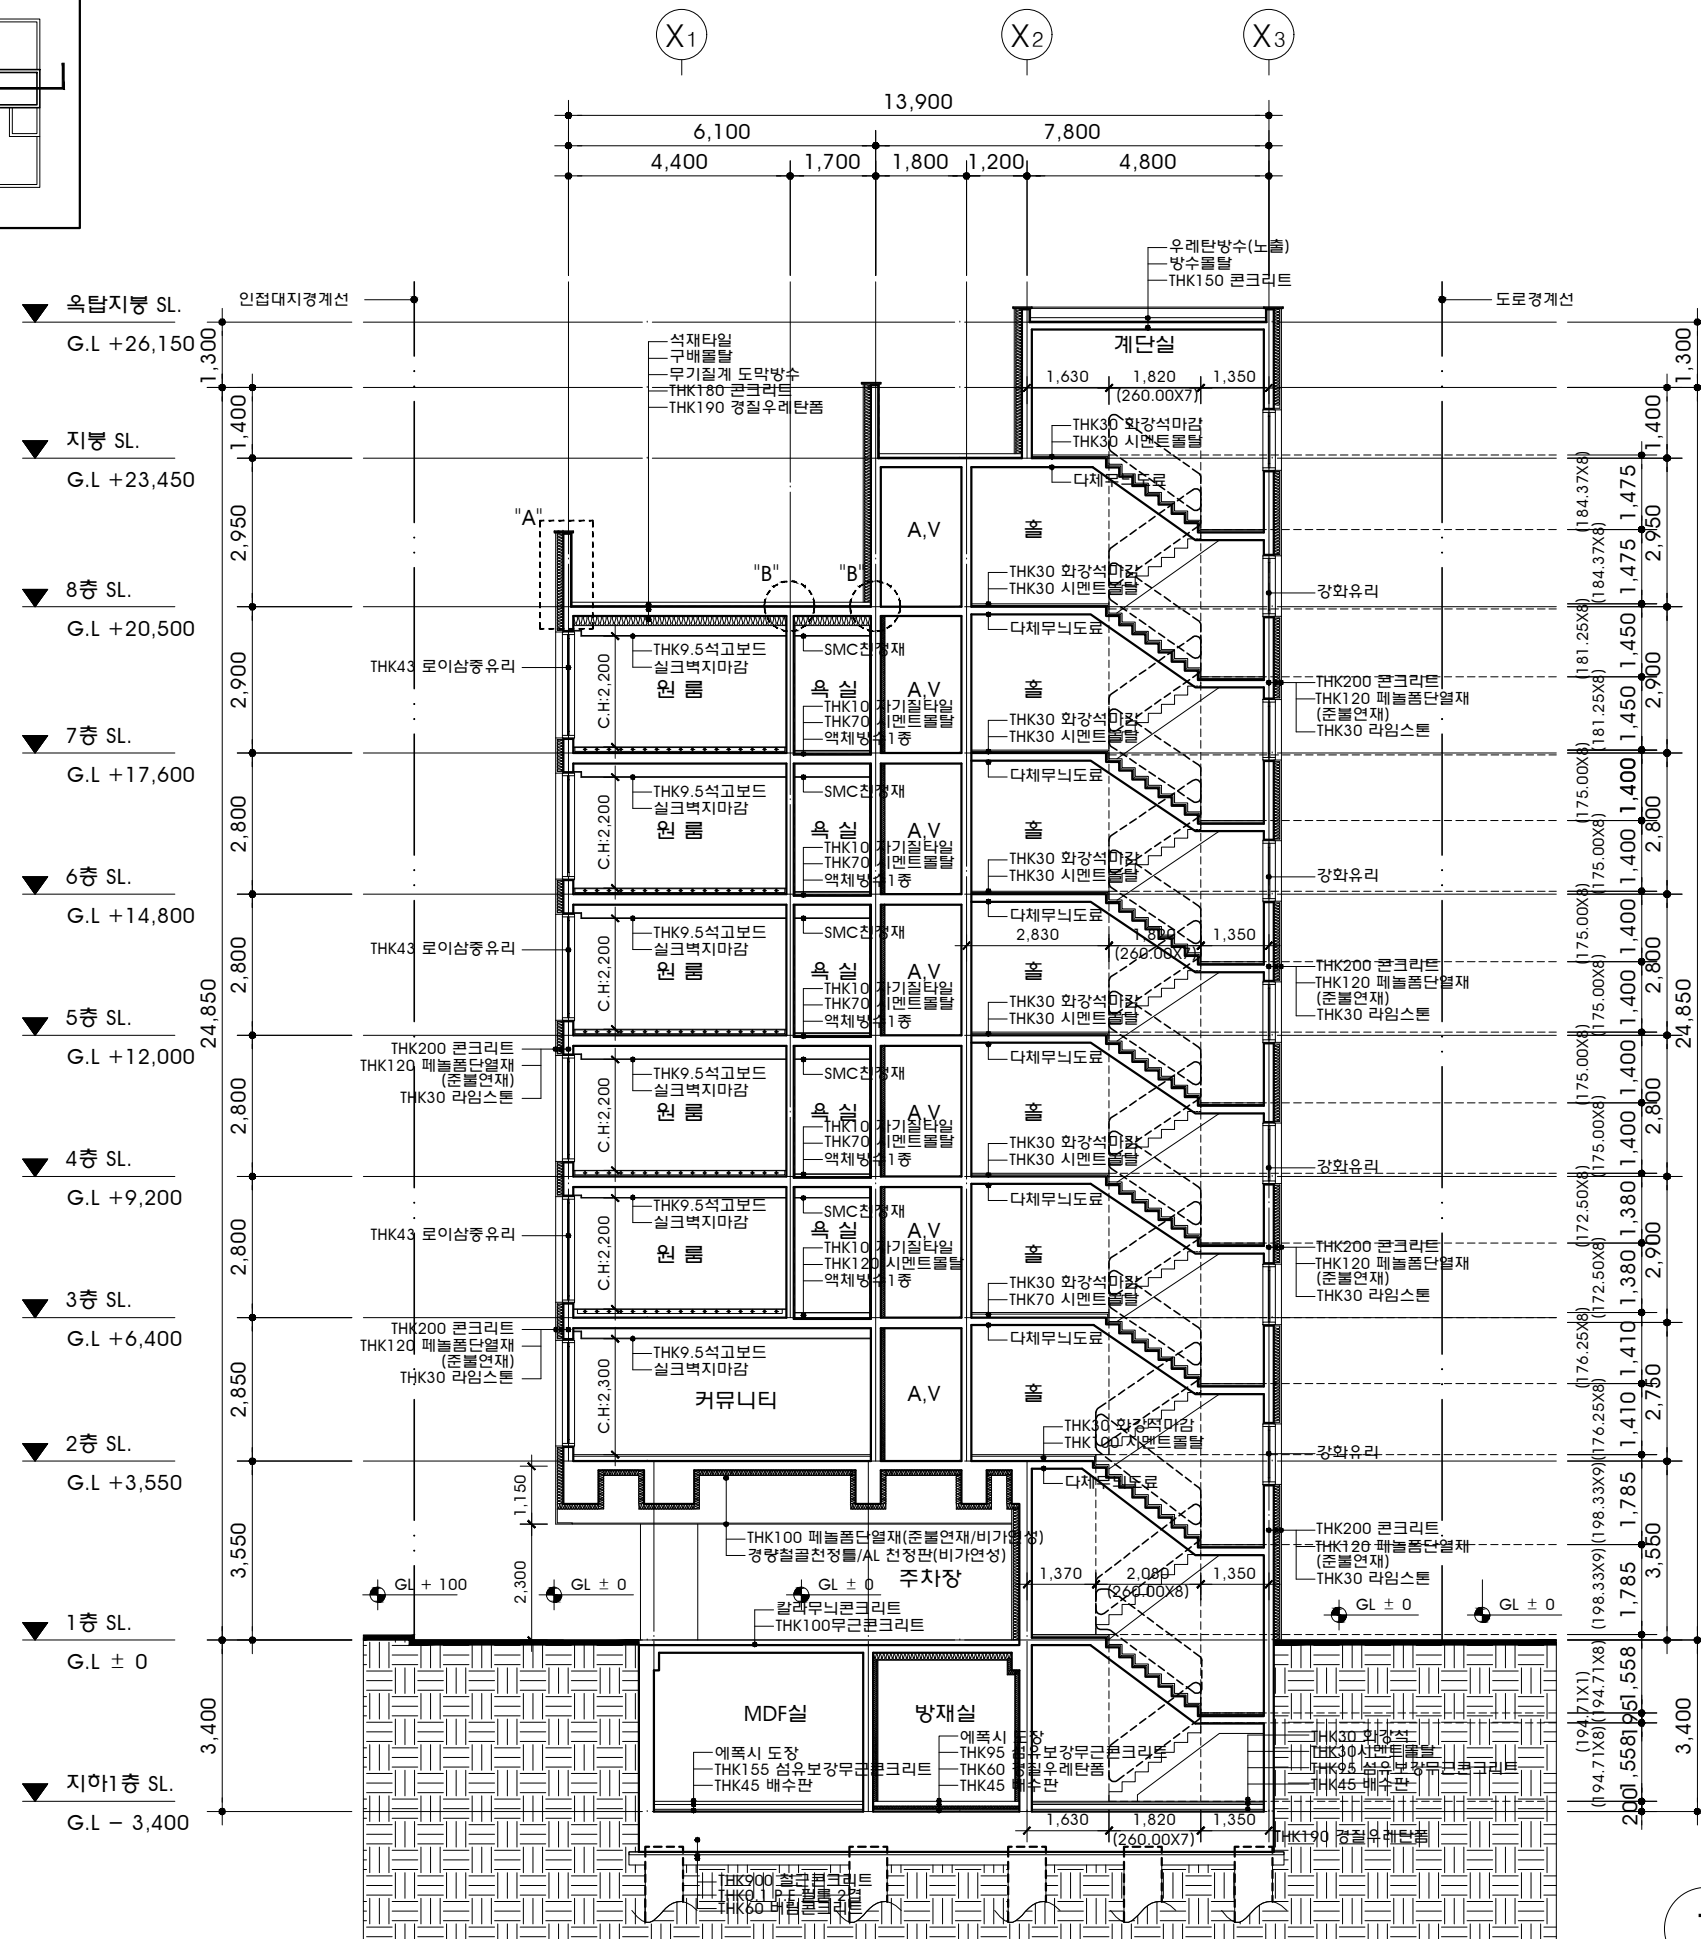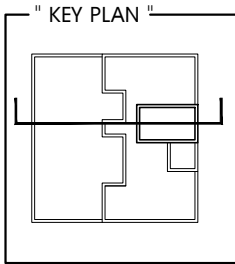

1 계단 단면도
축척 - A3 : 1/150

Architecture Construction Management
DESIGN GROUP

(주)아치씨엠 통합건축사사무소

서울특별시 송파구 오곡로 130(송파동) 2층
TEL : 02-2202-0066
FAX : 02-2202-0076

공사명
PROJECT TITLE

은평구 응암동 120-40번지
오피스텔(청년주택)
신축공사

NOTE

번호	수정내용	월	일	검토
△				
△				
△				
△				
△				
△				
△				

작성일자
DATE

설계자
DRAWING BY

검토자
CHECKED BY

승인자
APPROVED BY

축척
SCALE

1/150

도면명
DRAWING TITLE

계단 단면도

일련번호
SHEET NO.

00-0000

도면번호
DRAWING NO.

A-402