



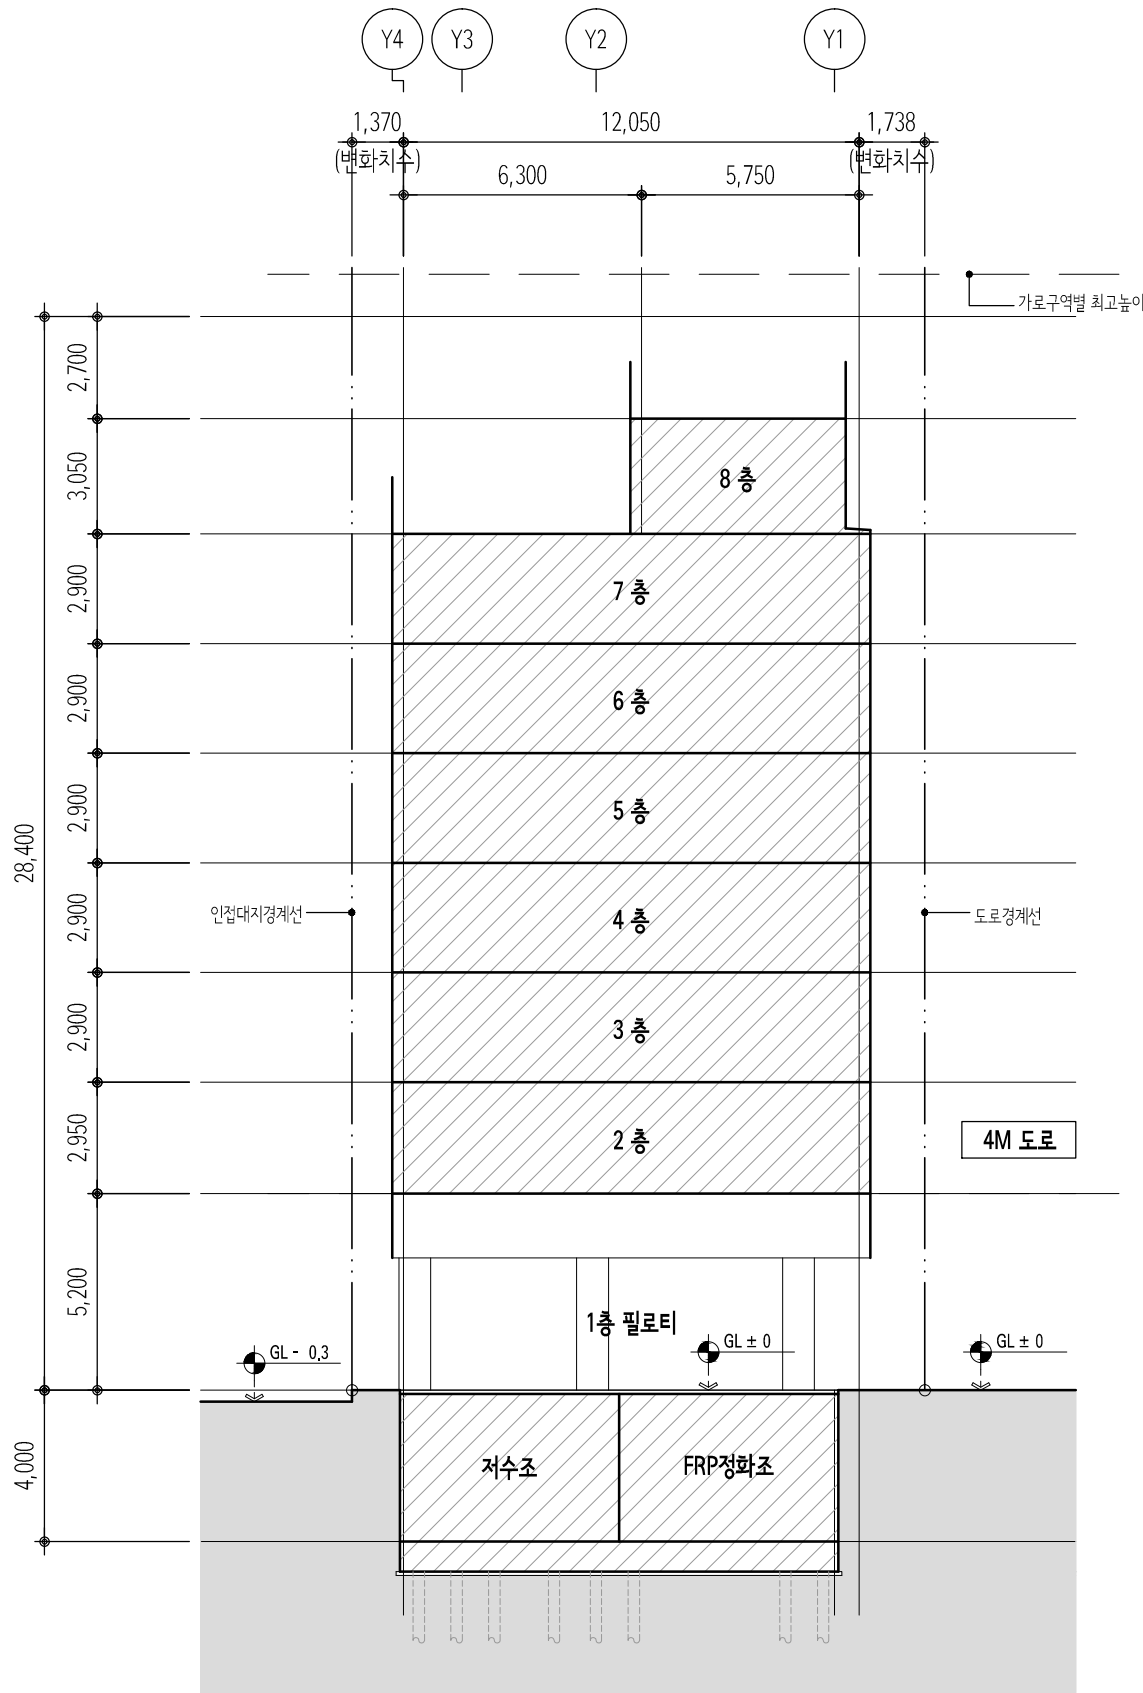

1
A
대지 "종" 단면도
축척 : 1 / 200

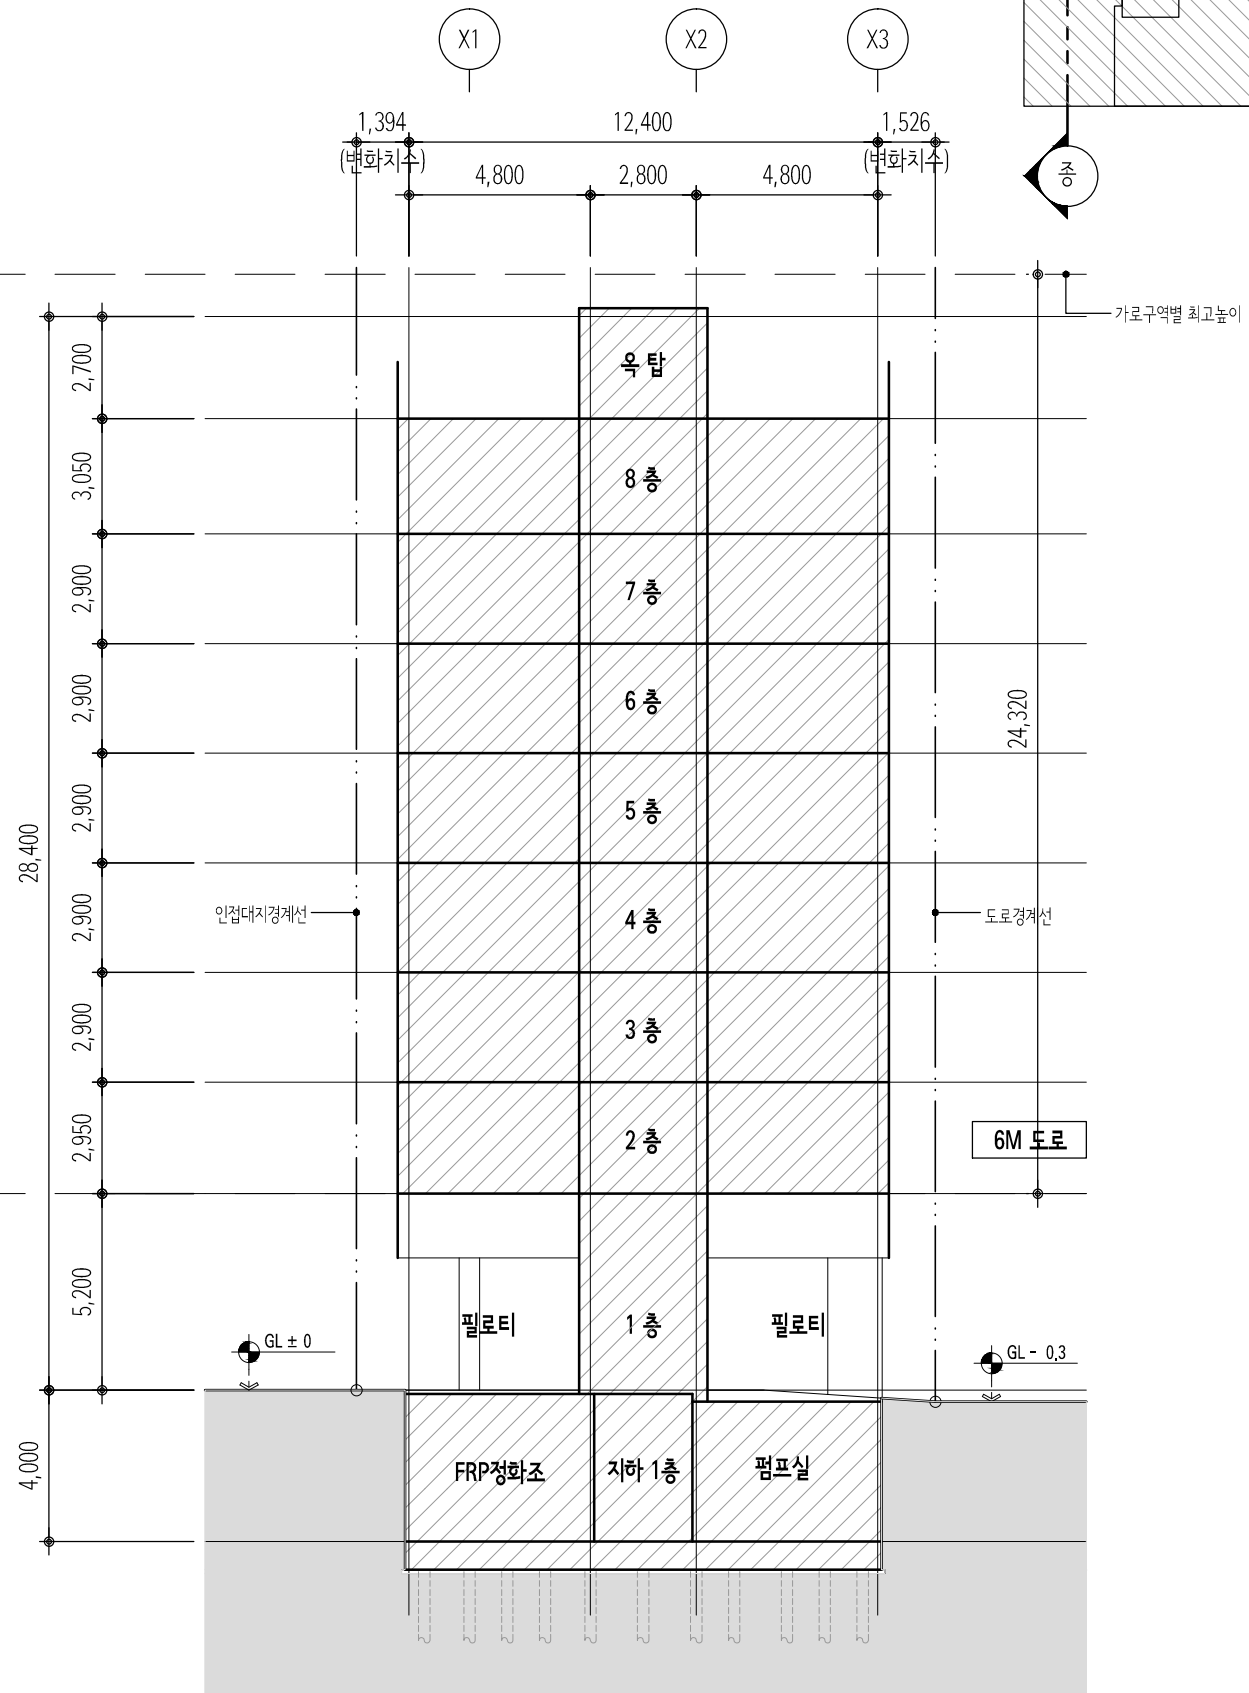

2
A
대지 "횡" 단면도
축척 : 1 / 200

PROJECT TITLE

응암동 121-56
오피스텔 및 단지형다세대주택
신축공사


매매계약

이로건축사사무소
Architecture & Planner
TEL : 070-4774-0134, FAX 050-4076-9431

NOTE

설계변경
DESCRIPTION OF REVISION

번호	내용
일자	설계 검토 심사 승인
승인 APPROVED BY	
날짜 DATE 2026. 05.	
축척 SCALE	A1 A3 1/200
도면명 DRAWING TITLE 대지 종,횡 단면도	
도면번호 DRAWING NO. A - 015	

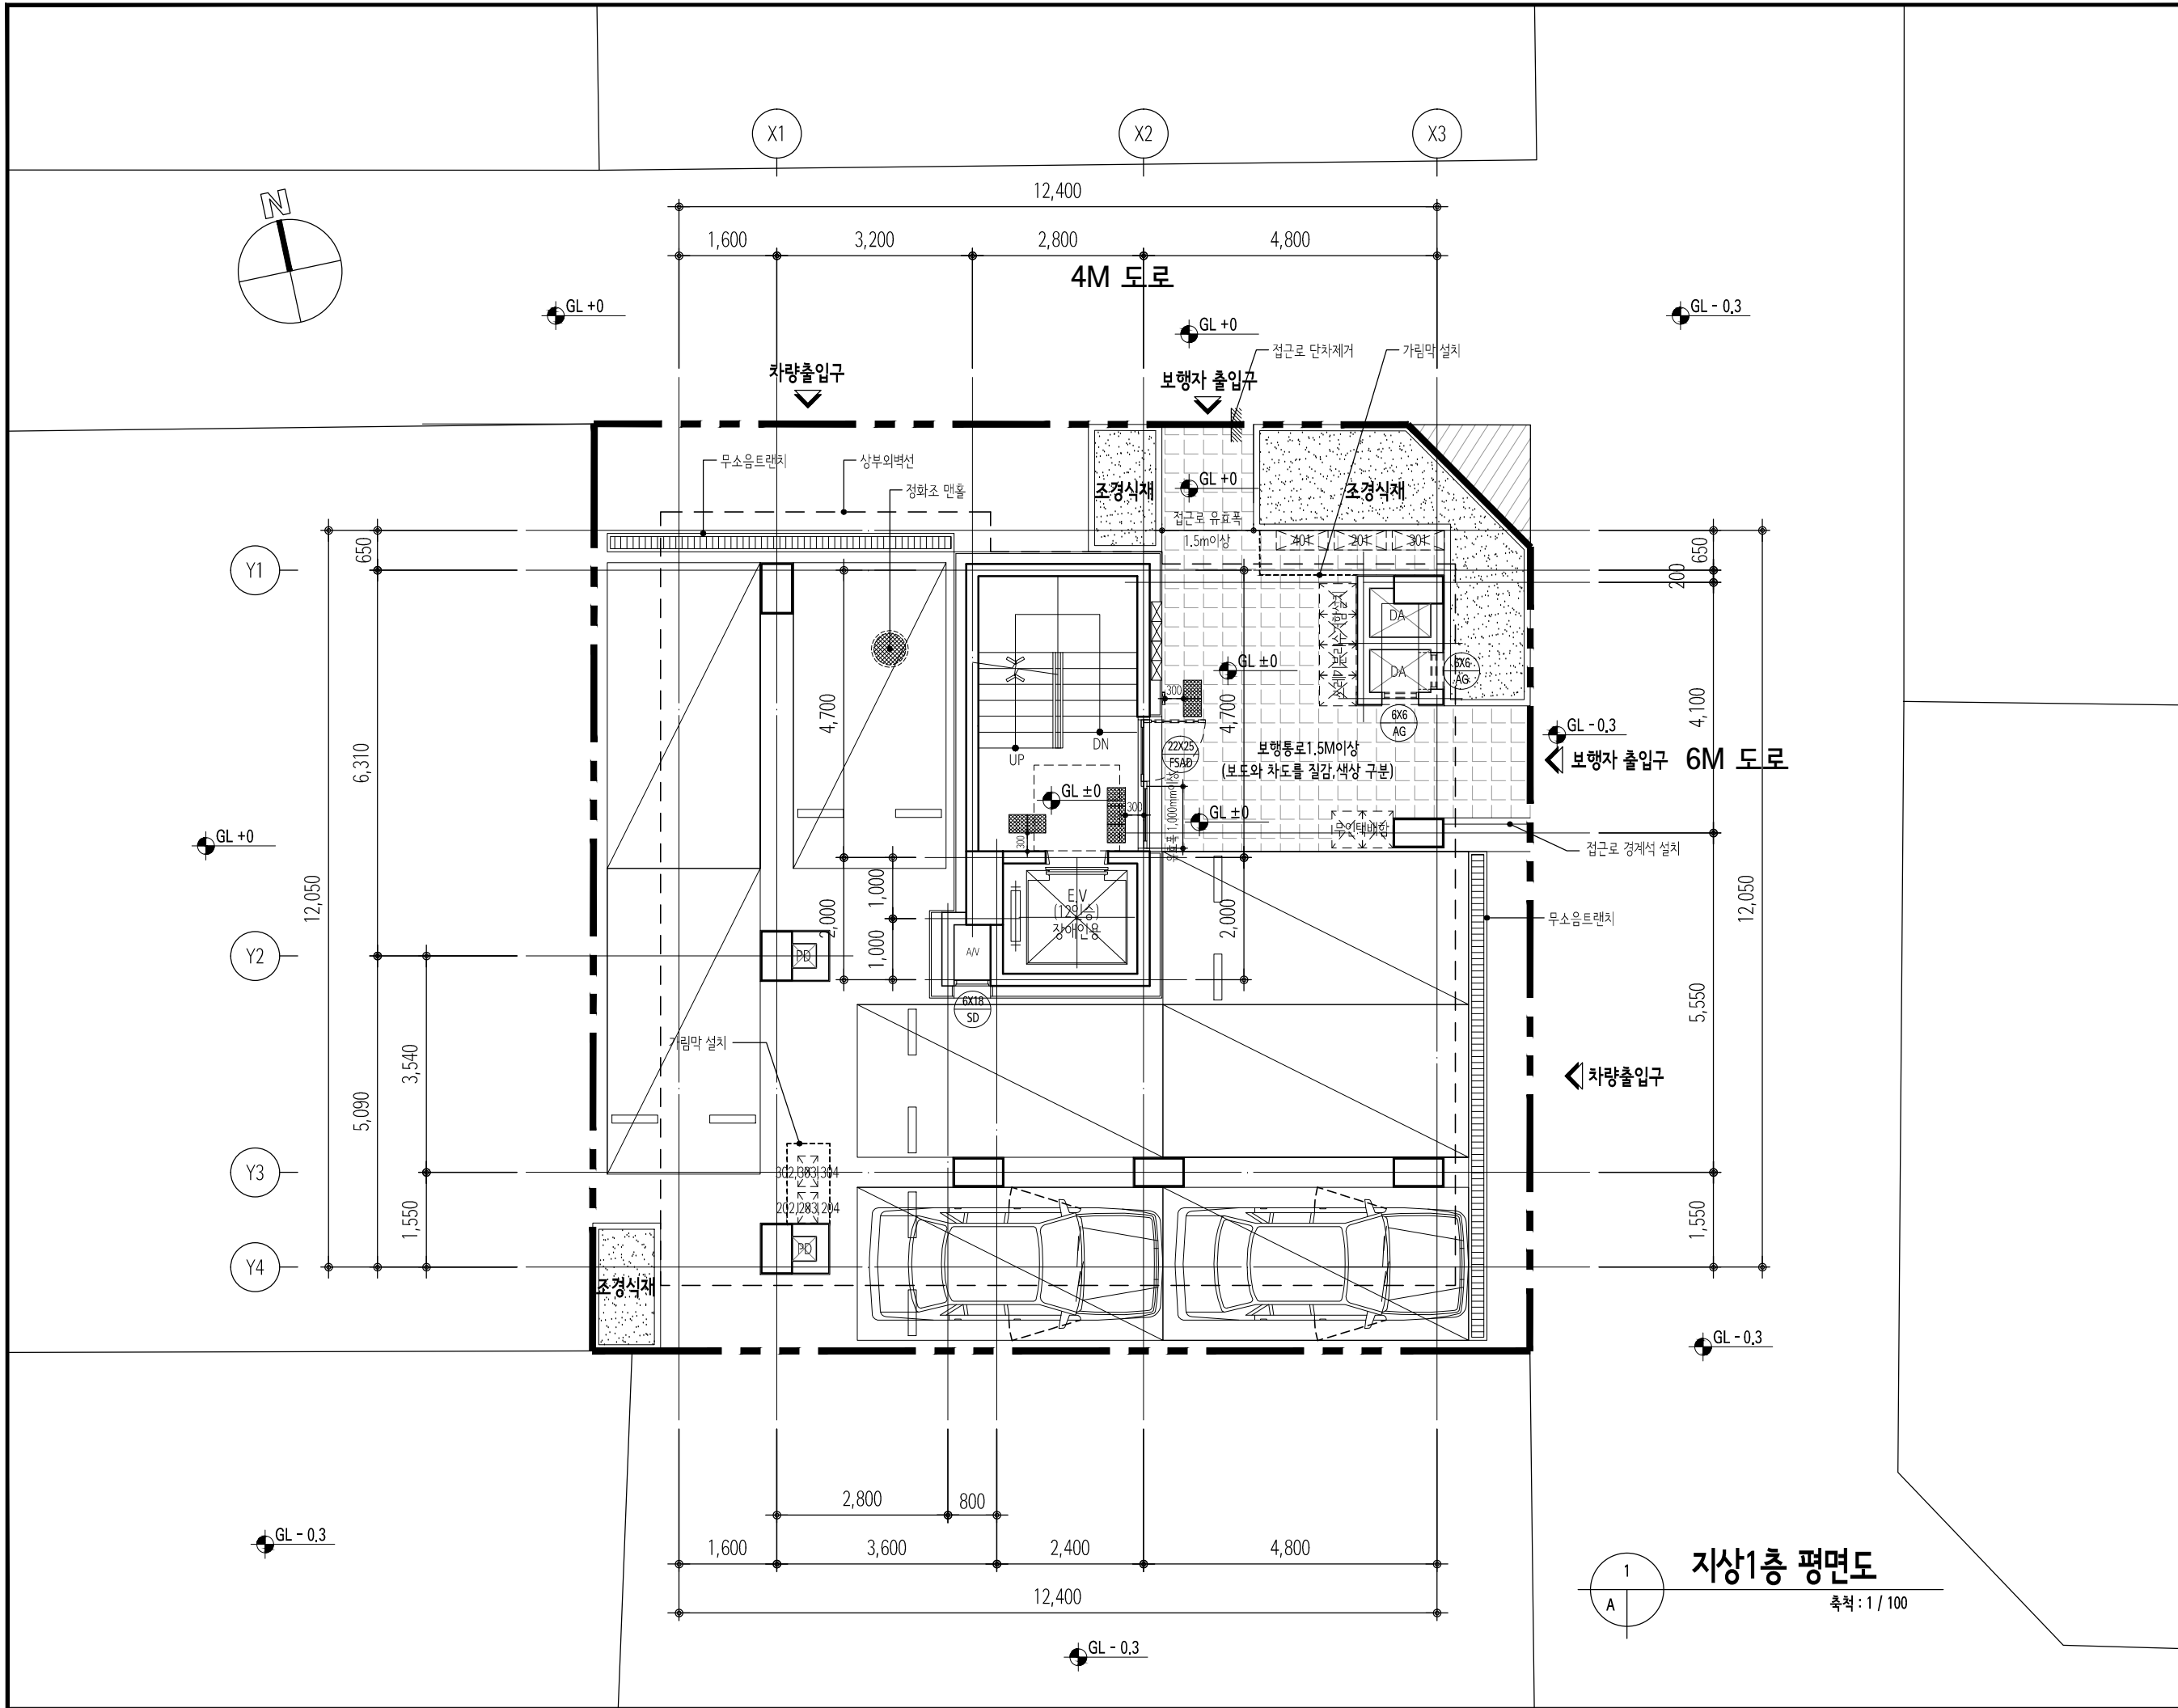

PROJECT TITLE

응암동 121-56
오피스텔 및 단지형다세대주택
신축공사

매 매 계 약

이토건축사사무소
Architecture & Planner
TEL : 070-4774-0134, FAX 050-4076-9431

NOTE

단독연기감지기

ABC분말소화기

보일러

벽걸이 에어컨

에어컨 실외기

차면시설(지상4층까지 설치)

배연창

- 신발장의 하부 바닥높이는 거실바닥
높이와 동일한 레벨에 설치

- 세대 신발장 350mm X 700mm이상 설치

- 계단은 계단단면도 확인할 것

- 정화조 맨홀위치는 현장상황에 따라
위치가 변경될 수도 있음.

- 장애인엘리베이터 앞 휠체어 회전공간
1400mm X 1400mm 확보할 것

설 계 변 경
DESCRIPTION OF REVISION

번 호	내 용
일 자	설계 검토 심사 승인

승인 APPROVED BY

날짜 DATE
2026. 05.



축 척 SCALE	A1	A3
		1/100

도면명 DRAWING TITLE
지상1층 평면도


도면번호 DRAWING NO.
A - 031

지상1층 평면도

축척 : 1 / 100

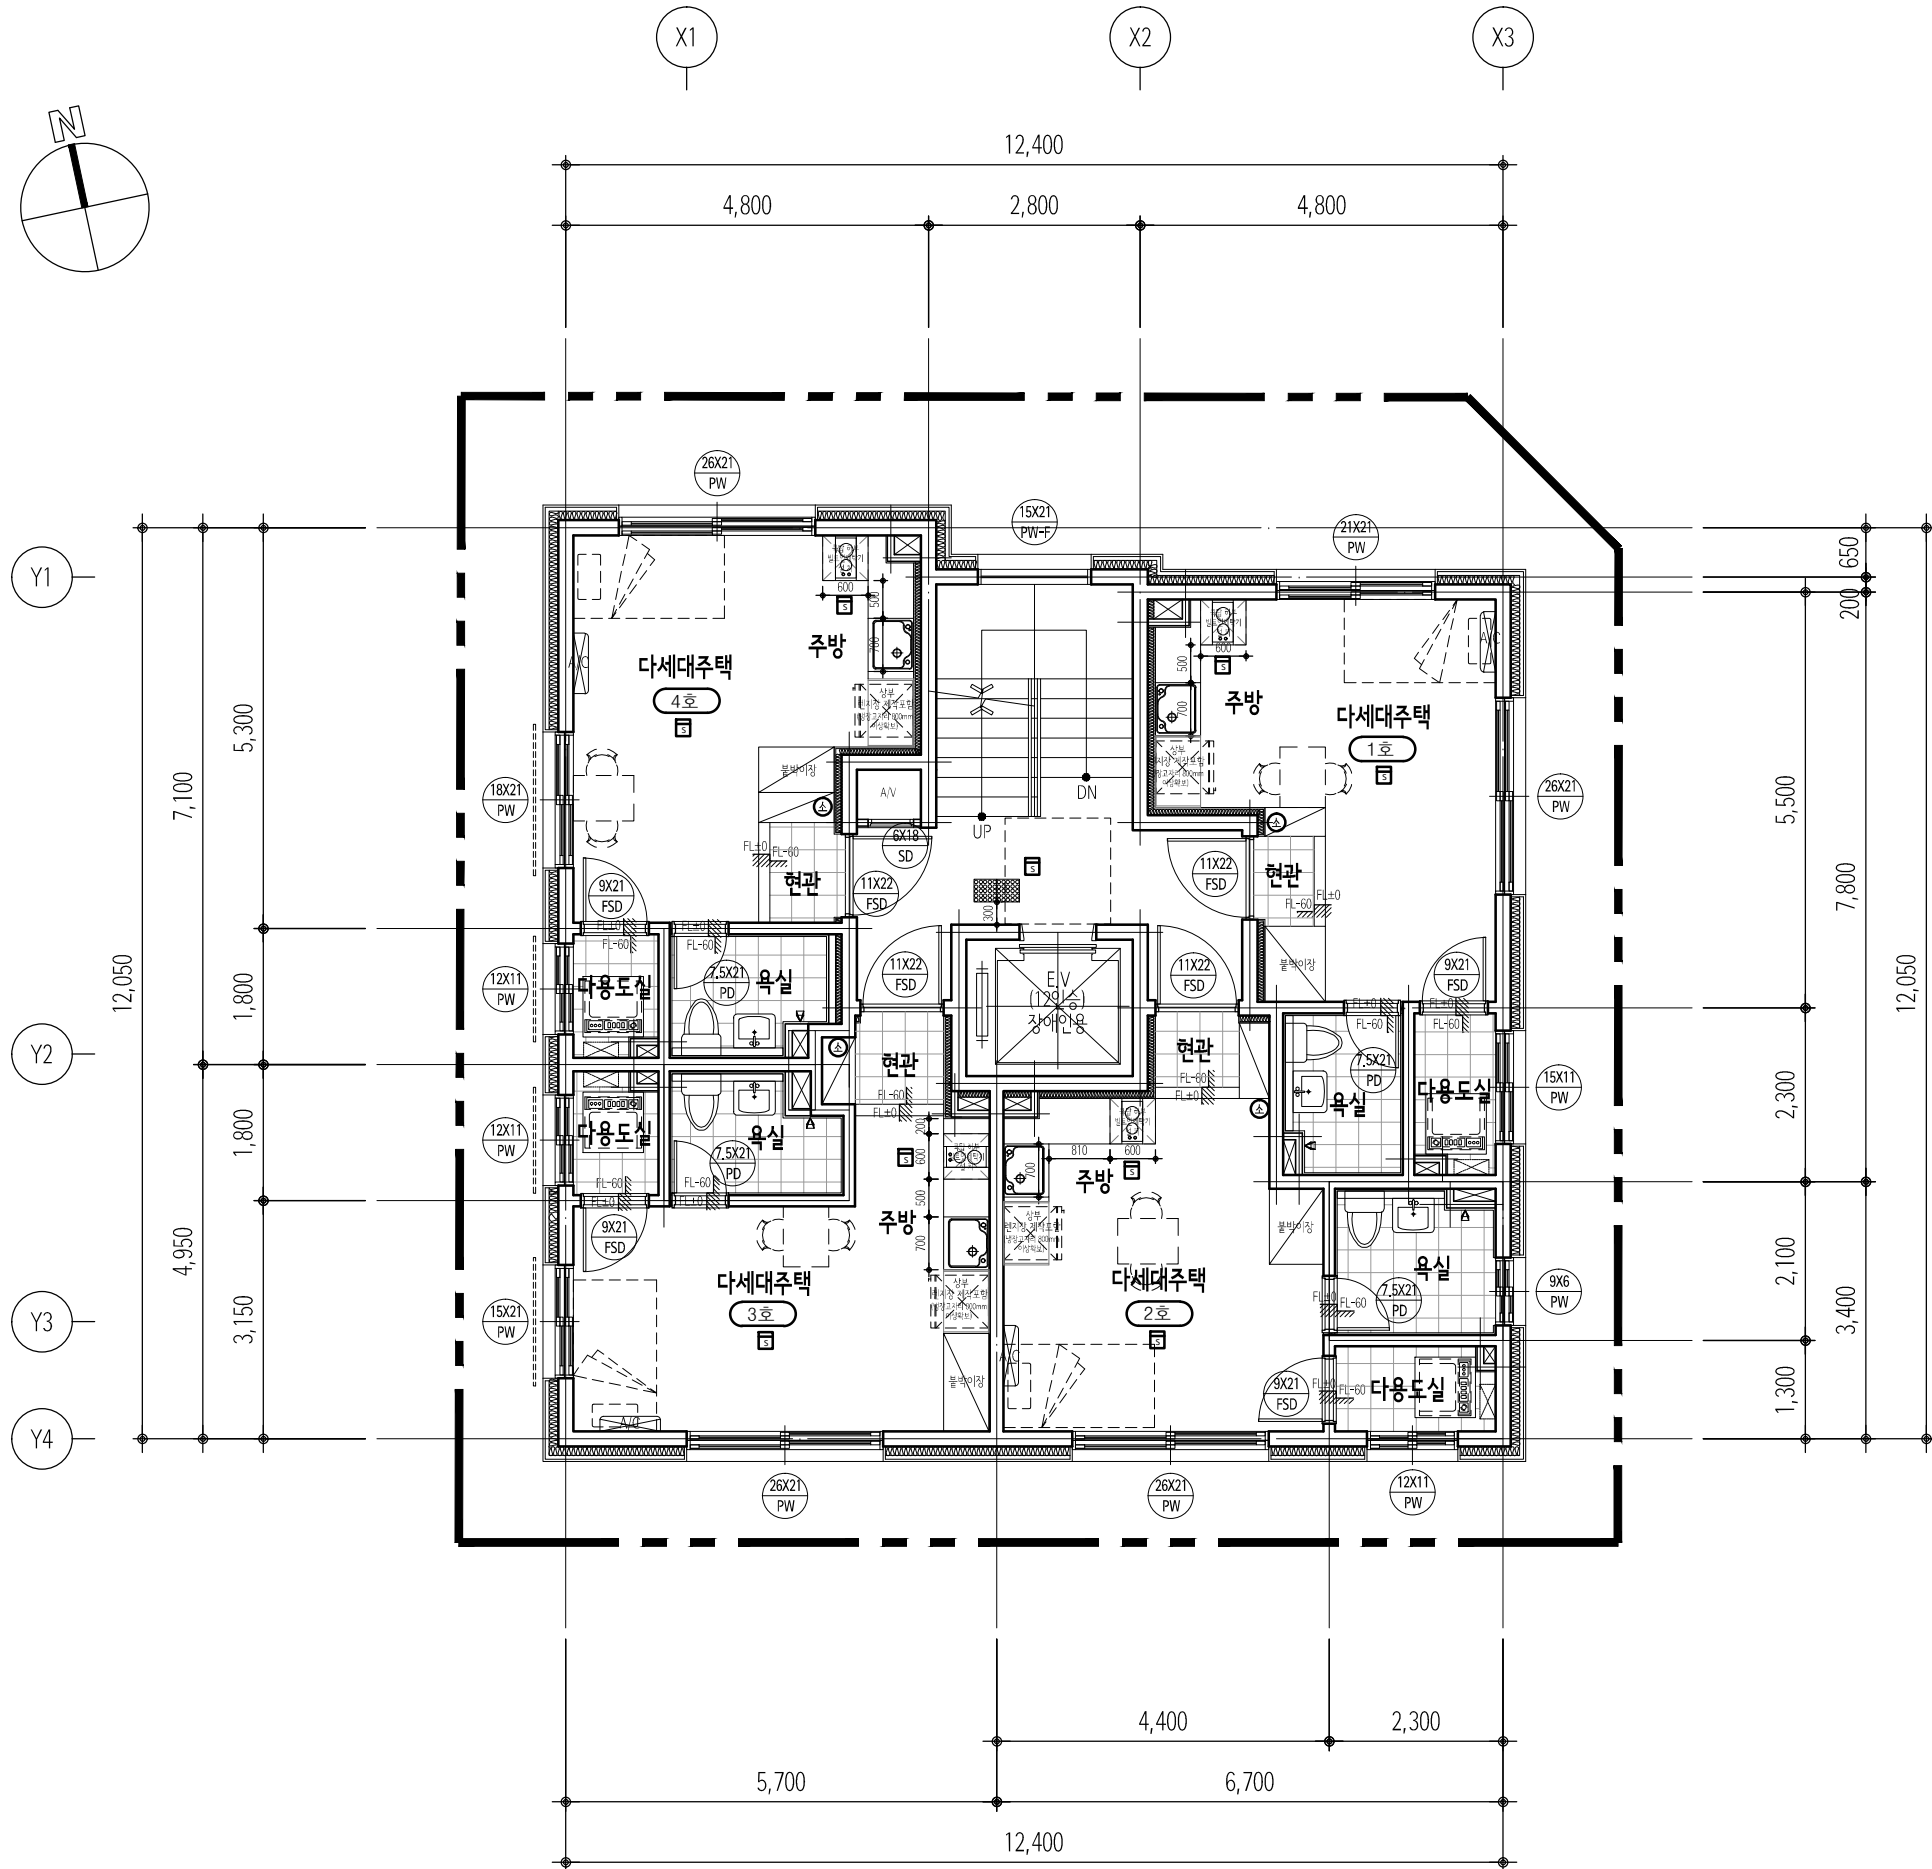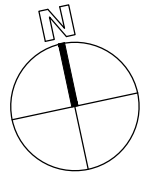

1
A 지상2층 평면도
(다세대주택) 축척: 1 / 100

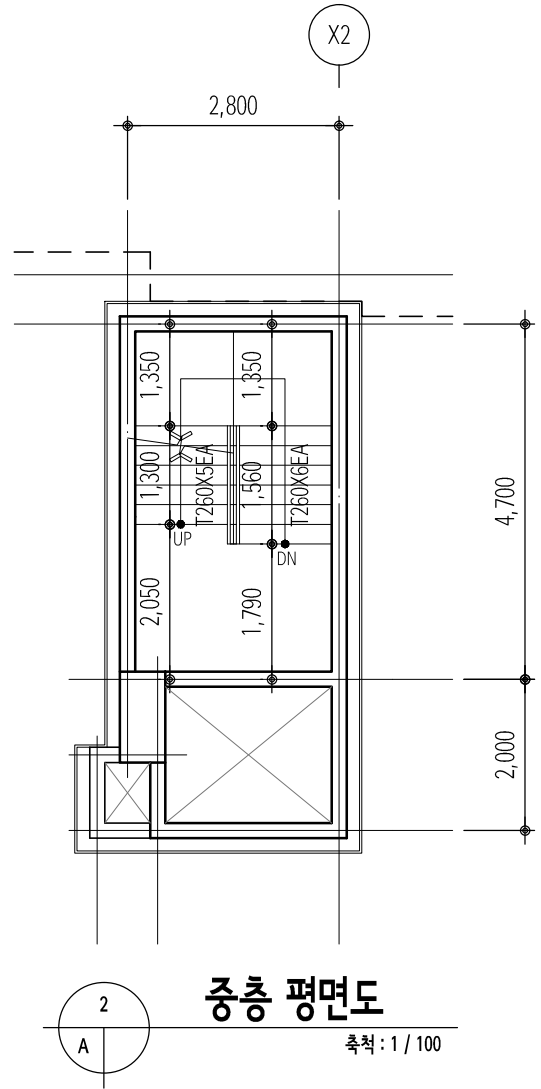

PROJECT TITLE
응암동 121-56
오피스텔 및 단지형다세대주택
신축공사

매 매 계 약

이토건축사사무소
Architecture & Planner
TEL : 070-4774-0134, FAX 050-4076-9431

NOTE

단독연기감지기

ABC분말소화기

보일러

벽걸이 에어컨

에어컨 실외기

차면시설(지상4층까지 설치)

배 배연창

- 신발장의 하부 바닥높이는 거실바닥
높이와 동일한 레벨에 설치

- 세대 신발장 350mm X 700mm이상 설치

- 계단은 계단단면도 확인할 것

- 정화조맨홀위치는 현장상황에 따라
위치가 변경될 수도 있음.

- 장애인엘리베이터 앞 휠체어 회전공간
1400mm X 1400mm 확보할 것

설 계 변 경
DESCRIPTION OF REVISION

번 호	내 용
일 자	설계 검토 심사 승인




승인 APPROVED BY

날짜 DATE
2026. 05.

축 척 SCALE	A1	A3
		1/100

도면명 DRAWING TITLE
지상2층 평면도
(다세대주택)

도면번호 DRAWING NO.
A - 032

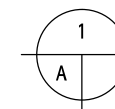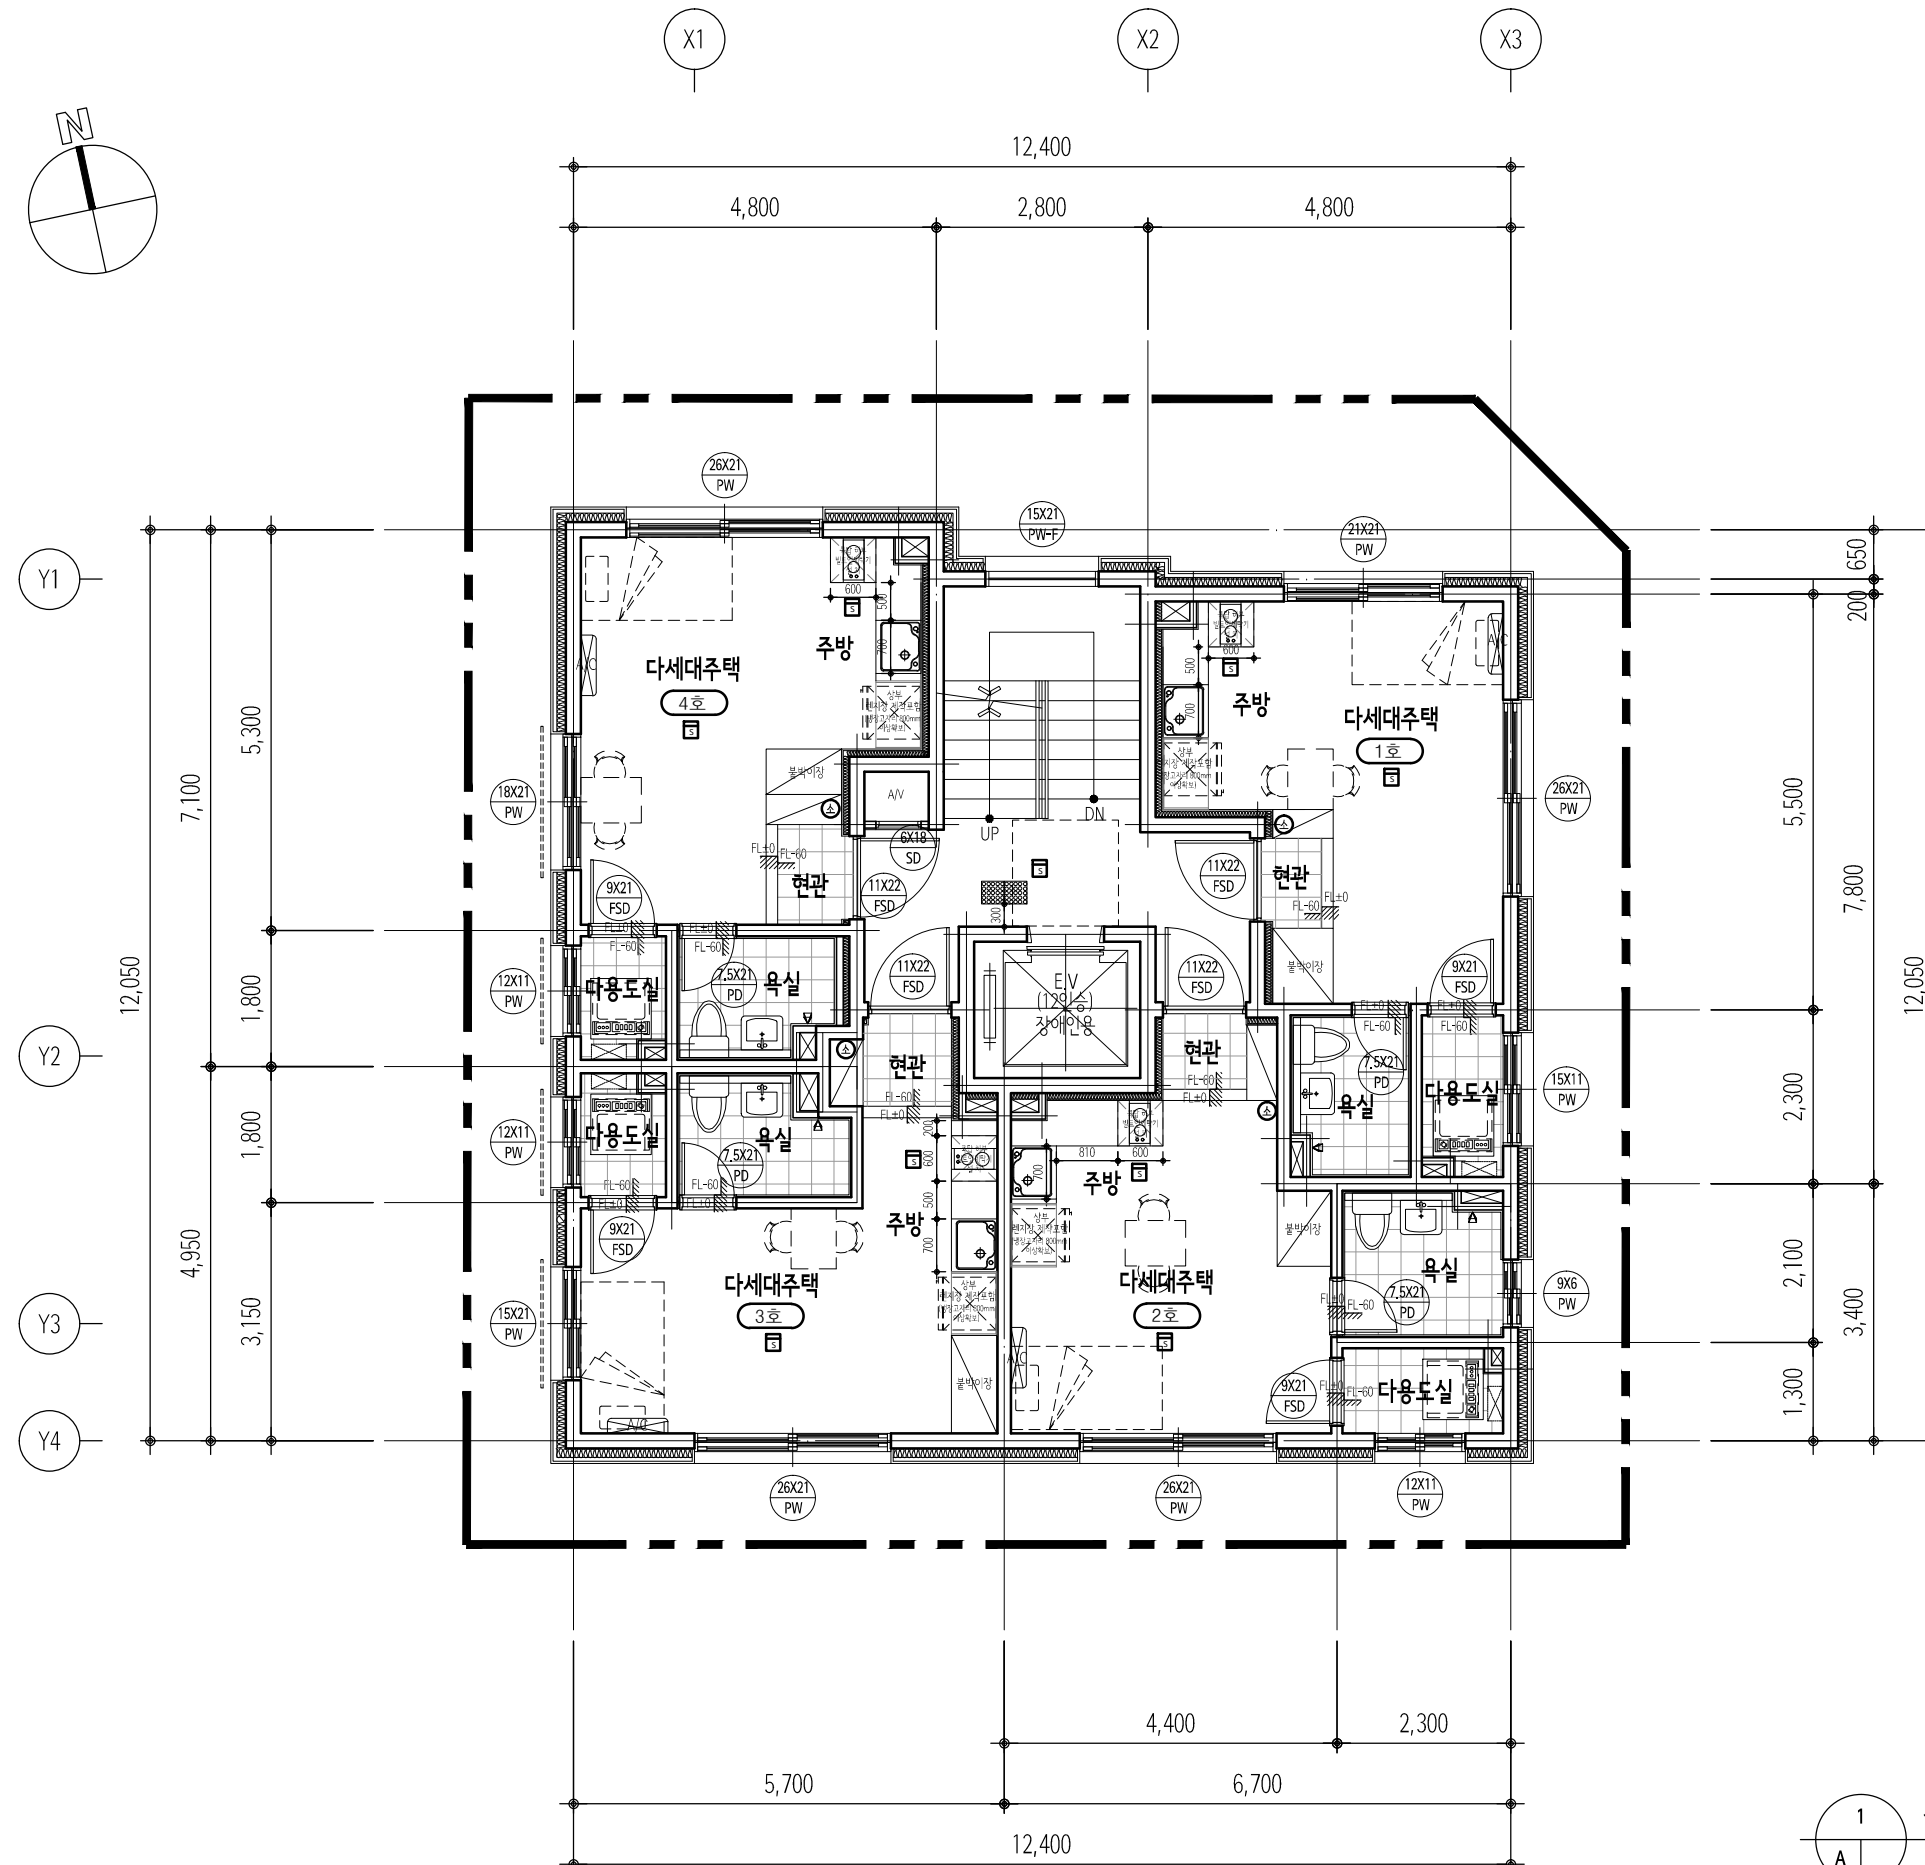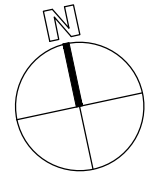

지상3~5층 평면도
(다세대주택)

축척 : 1 / 100

PROJECT TITLE

응암동 121-56
오피스텔 및 단지형다세대주택
신축공사


매 매 계 약



이로건축사사무소
Architecture & Planner
TEL : 070-4774-0134, FAX 050-4076-9431

NOTE

- 단독연기감지기
- ABC분말소화기
- 보일러
- 벽걸이 에어컨
- 에어컨 실외기
- 차면시설(지상4층까지 설치)
- 배연창
- 신발장의 하부 바닥높이는 거실바닥
높이와 동일한 레벨에 설치
- 세대 신발장 350mm X 700mm이상 설치
- 계단은 계단단면도 확인할 것
- 정화조맨홀위치는 현장상황에 따라
위치가 변경될 수도 있음.
- 장애인엘리베이터 앞 휠체어 회전공간
1400mm X 1400mm 확보할 것

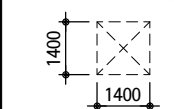

설 계 변 경
DESCRIPTION OF REVISION

번 호	내 용
일 자	설 계 검 토 심 사 승 인

승인 APPROVED BY




날짜 DATE
2026. 05.

축 척 SCALE	A1	A3
		1/100

도면명 DRAWING TITLE

지상2~5층 평면도
(다세대주택)

도면번호 DRAWING NO.
A - 033

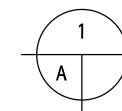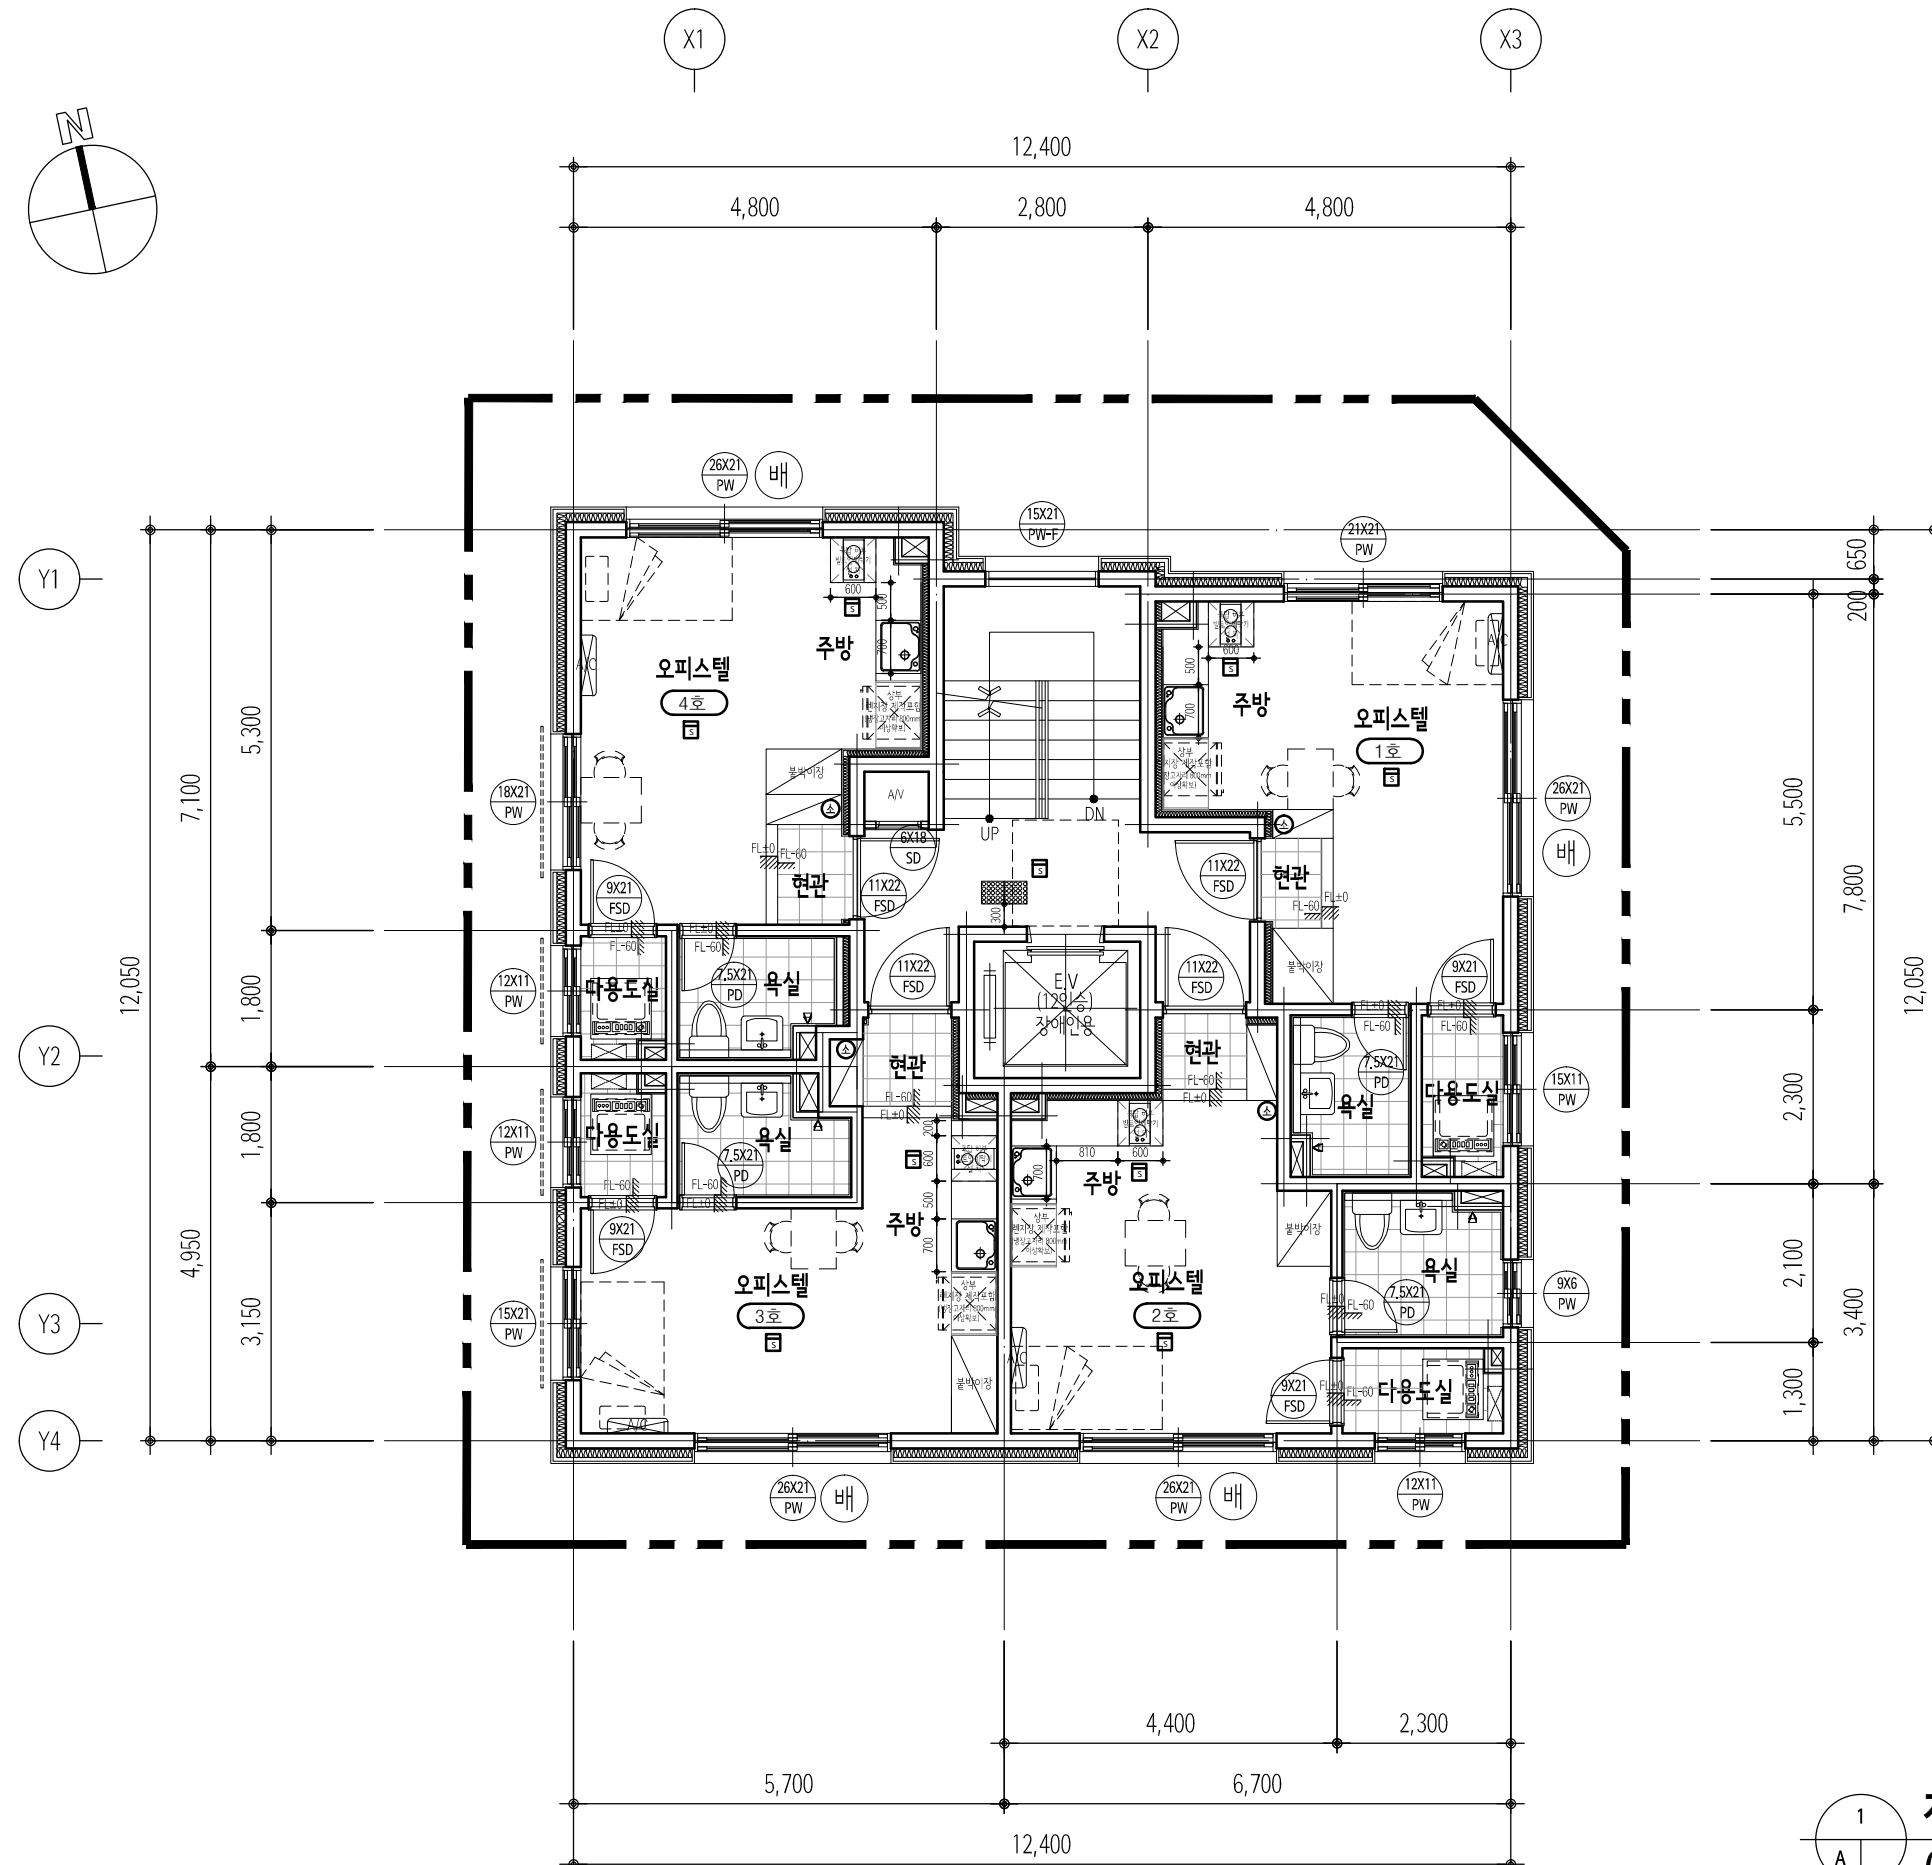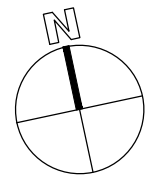

지상6~7층 평면도
(오피스텔)

축척 : 1 / 100

PROJECT TITLE

응암동 121-56
오피스텔 및 단지형다세대주택
신축공사


매 매 계 약



이로건축사사무소
Architecture & Planner
TEL : 070-4774-0134, FAX 050-4076-9431

NOTE

- 단독연기감지기
- ABC분말소화기
- 보일러
- 벽걸이 에어컨
- 에어컨 실외기
- 차면시설(지상4층까지 설치)
- 배연창
- 신발장의 하부 바닥높이는 거실바닥 높이와 동일한 레벨에 설치
- 세대 신발장 350mm X 700mm이상 설치
- 계단은 계단단면도 확인할 것
- 정화조맨홀위치는 현장상황에 따라 위치가 변경될 수도 있음.
- 장애인엘리베이터 앞 휠체어 회전공간 1400mm X 1400mm 확보할 것

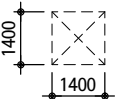

설 계 변 경
DESCRIPTION OF REVISION

번호	내 용
일 자	설계 검토 심사 승인

승인 APPROVED BY




날짜 DATE
2026. 05.

축척 SCALE	A1	A3
		1/100

도면명 DRAWING TITLE

지상6~7층 평면도
(오피스텔)

도면번호 DRAWING NO.
A - 034

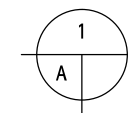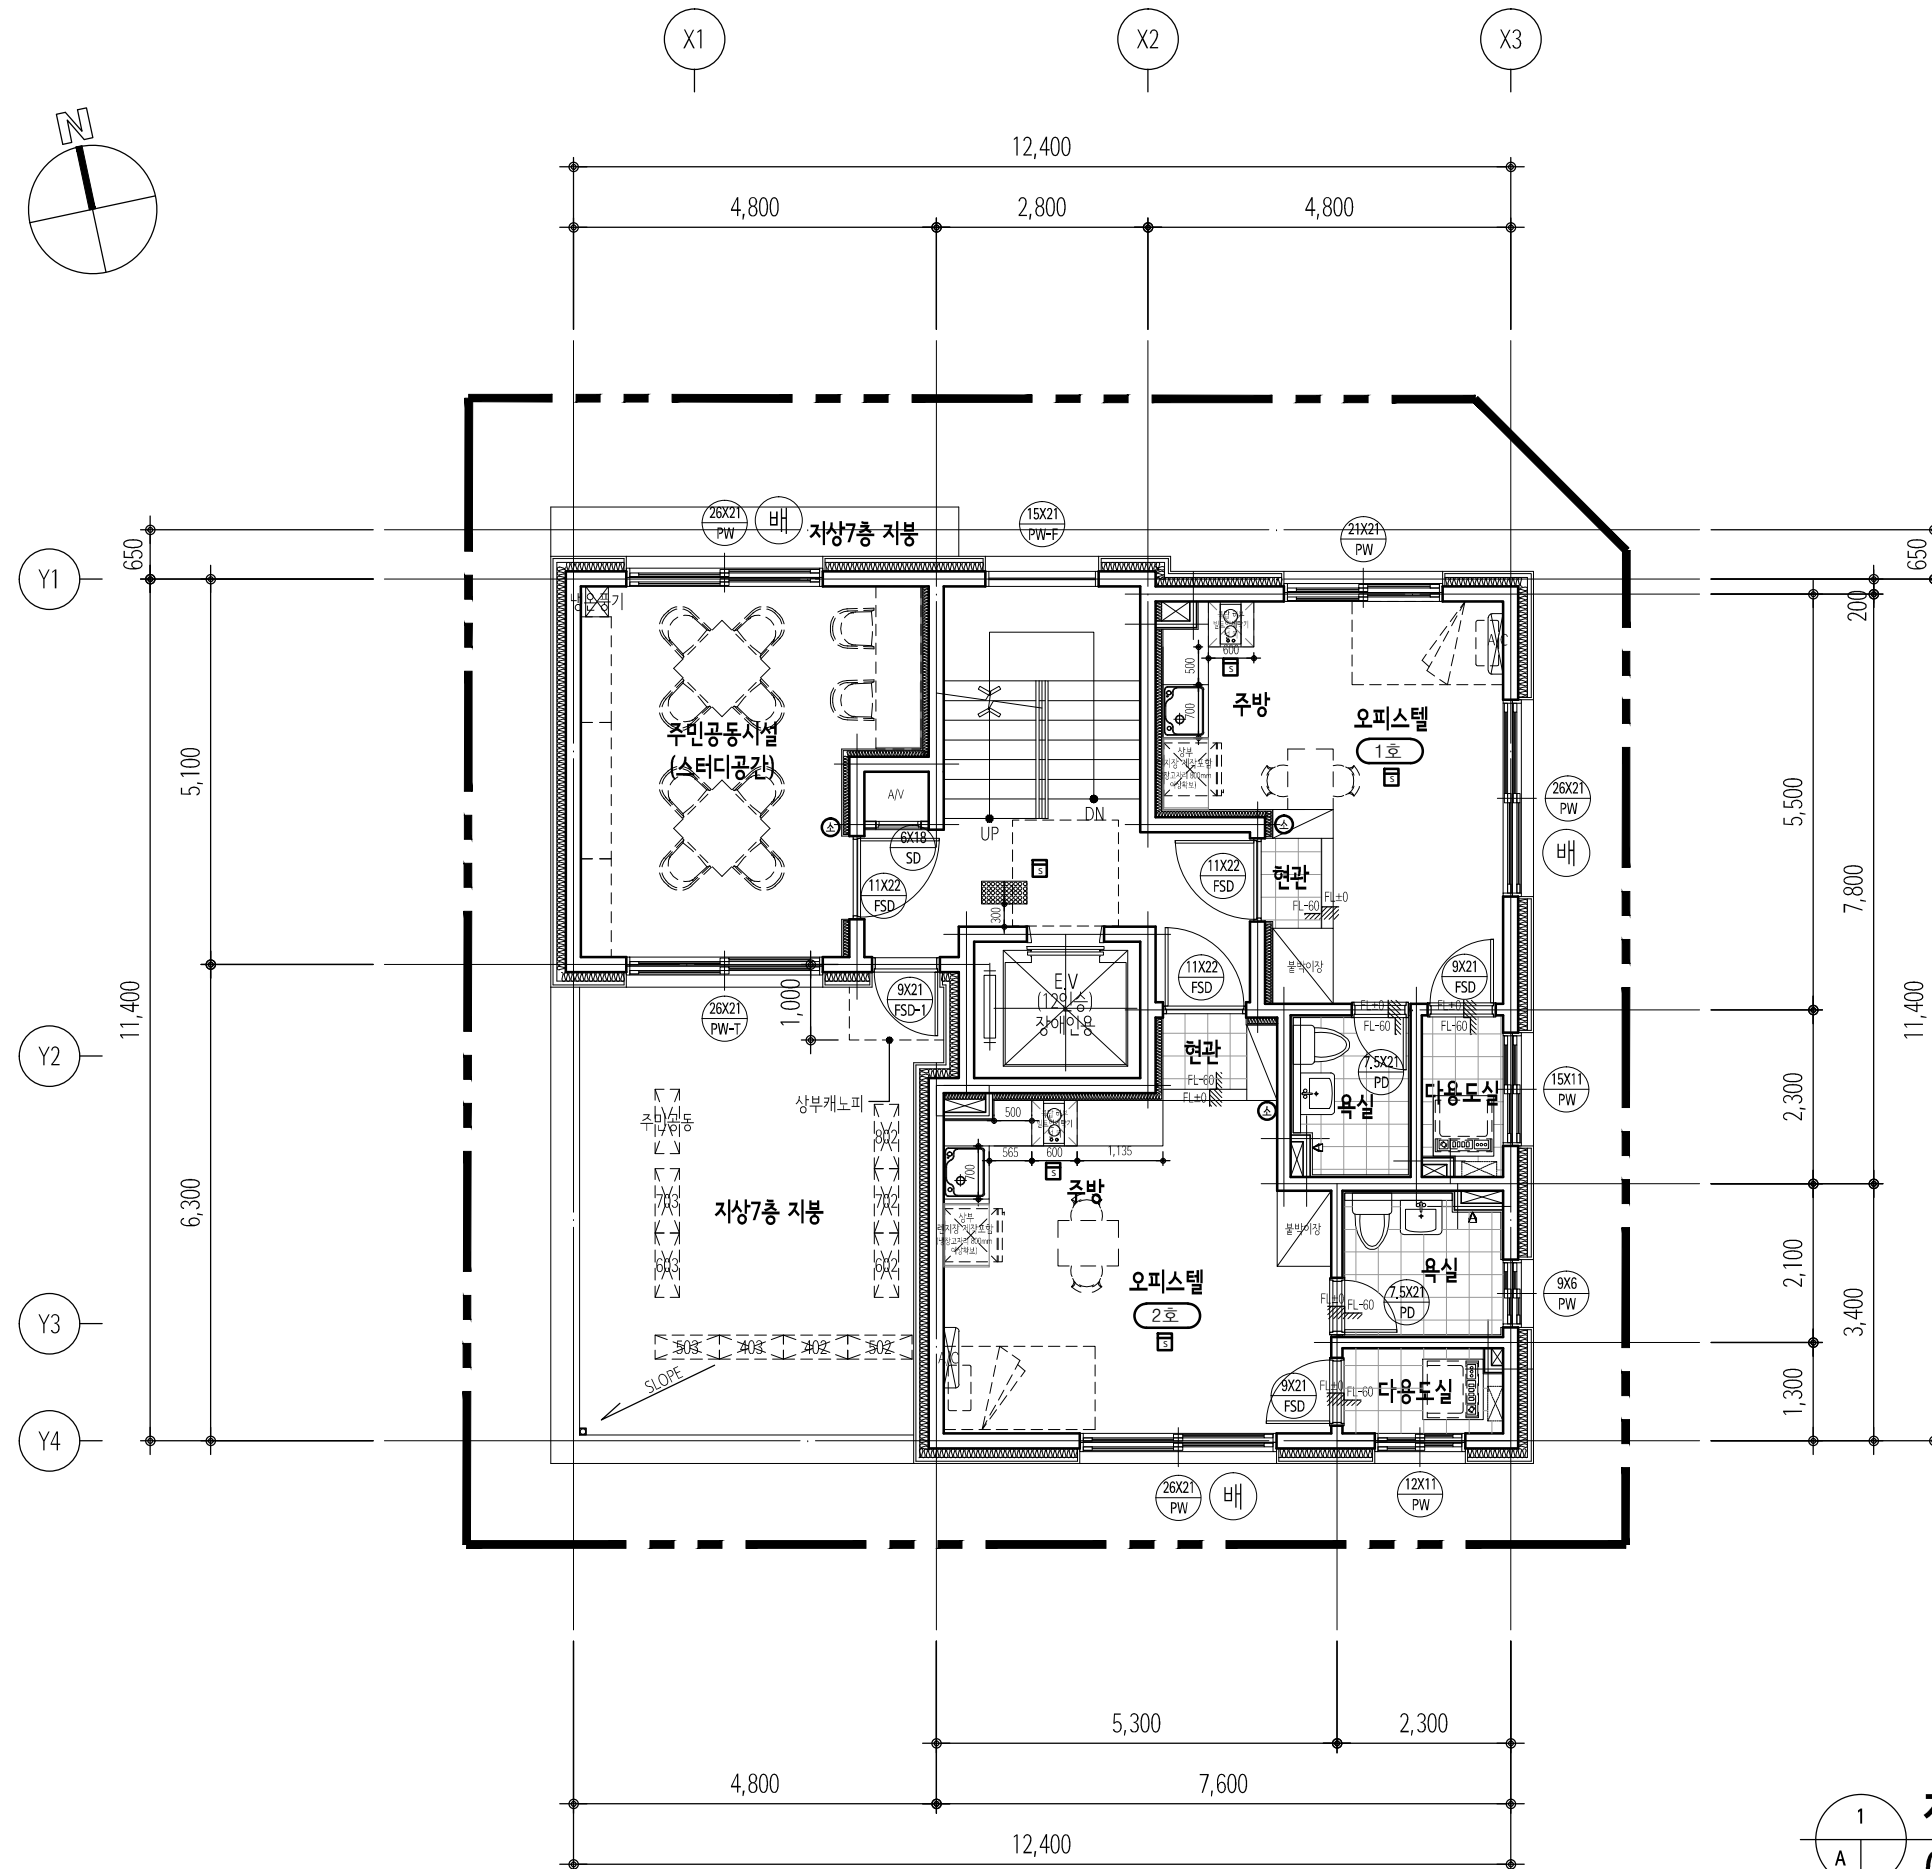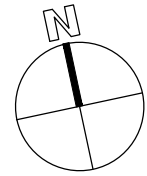

지상8층 평면도
(오피스텔)

축척 : 1 / 100

PROJECT TITLE

응암동 121-56
오피스텔 및 단지형다세대주택
신축공사


매 매 계 약



이로건축사사무소
Architecture & Planner
TEL : 070-4774-0134, FAX 050-4076-9431

NOTE

- 단독연기감지기
- ABC분말소화기
- 보일러
- 벽걸이 에어컨
- 에어컨 실외기
- 차면시설(지상4층까지 설치)
- 배연창
- 신발장의 하부 바닥높이는 거실바닥 높이와 동일한 레벨에 설치
- 세대 신발장 350mm X 700mm이상 설치
- 계단은 계단단면도 확인할 것
- 정화조맨홀위치는 현장상황에 따라 위치가 변경될 수도 있음.
- 장애인엘리베이터 앞 휠체어 회전공간 1400mm X 1400mm 확보할 것

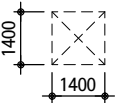

설 계 변 경
DESCRIPTION OF REVISION

번호	내 용
일 자	설계 검토 심사 승인
△	

승인 APPROVED BY

날짜 DATE

2026. 05.


축척 SCALE	A1	
	A3	1/100

도면명 DRAWING TITLE

지상8층 평면도
(오피스텔)

도면번호 DRAWING NO.

A - 035

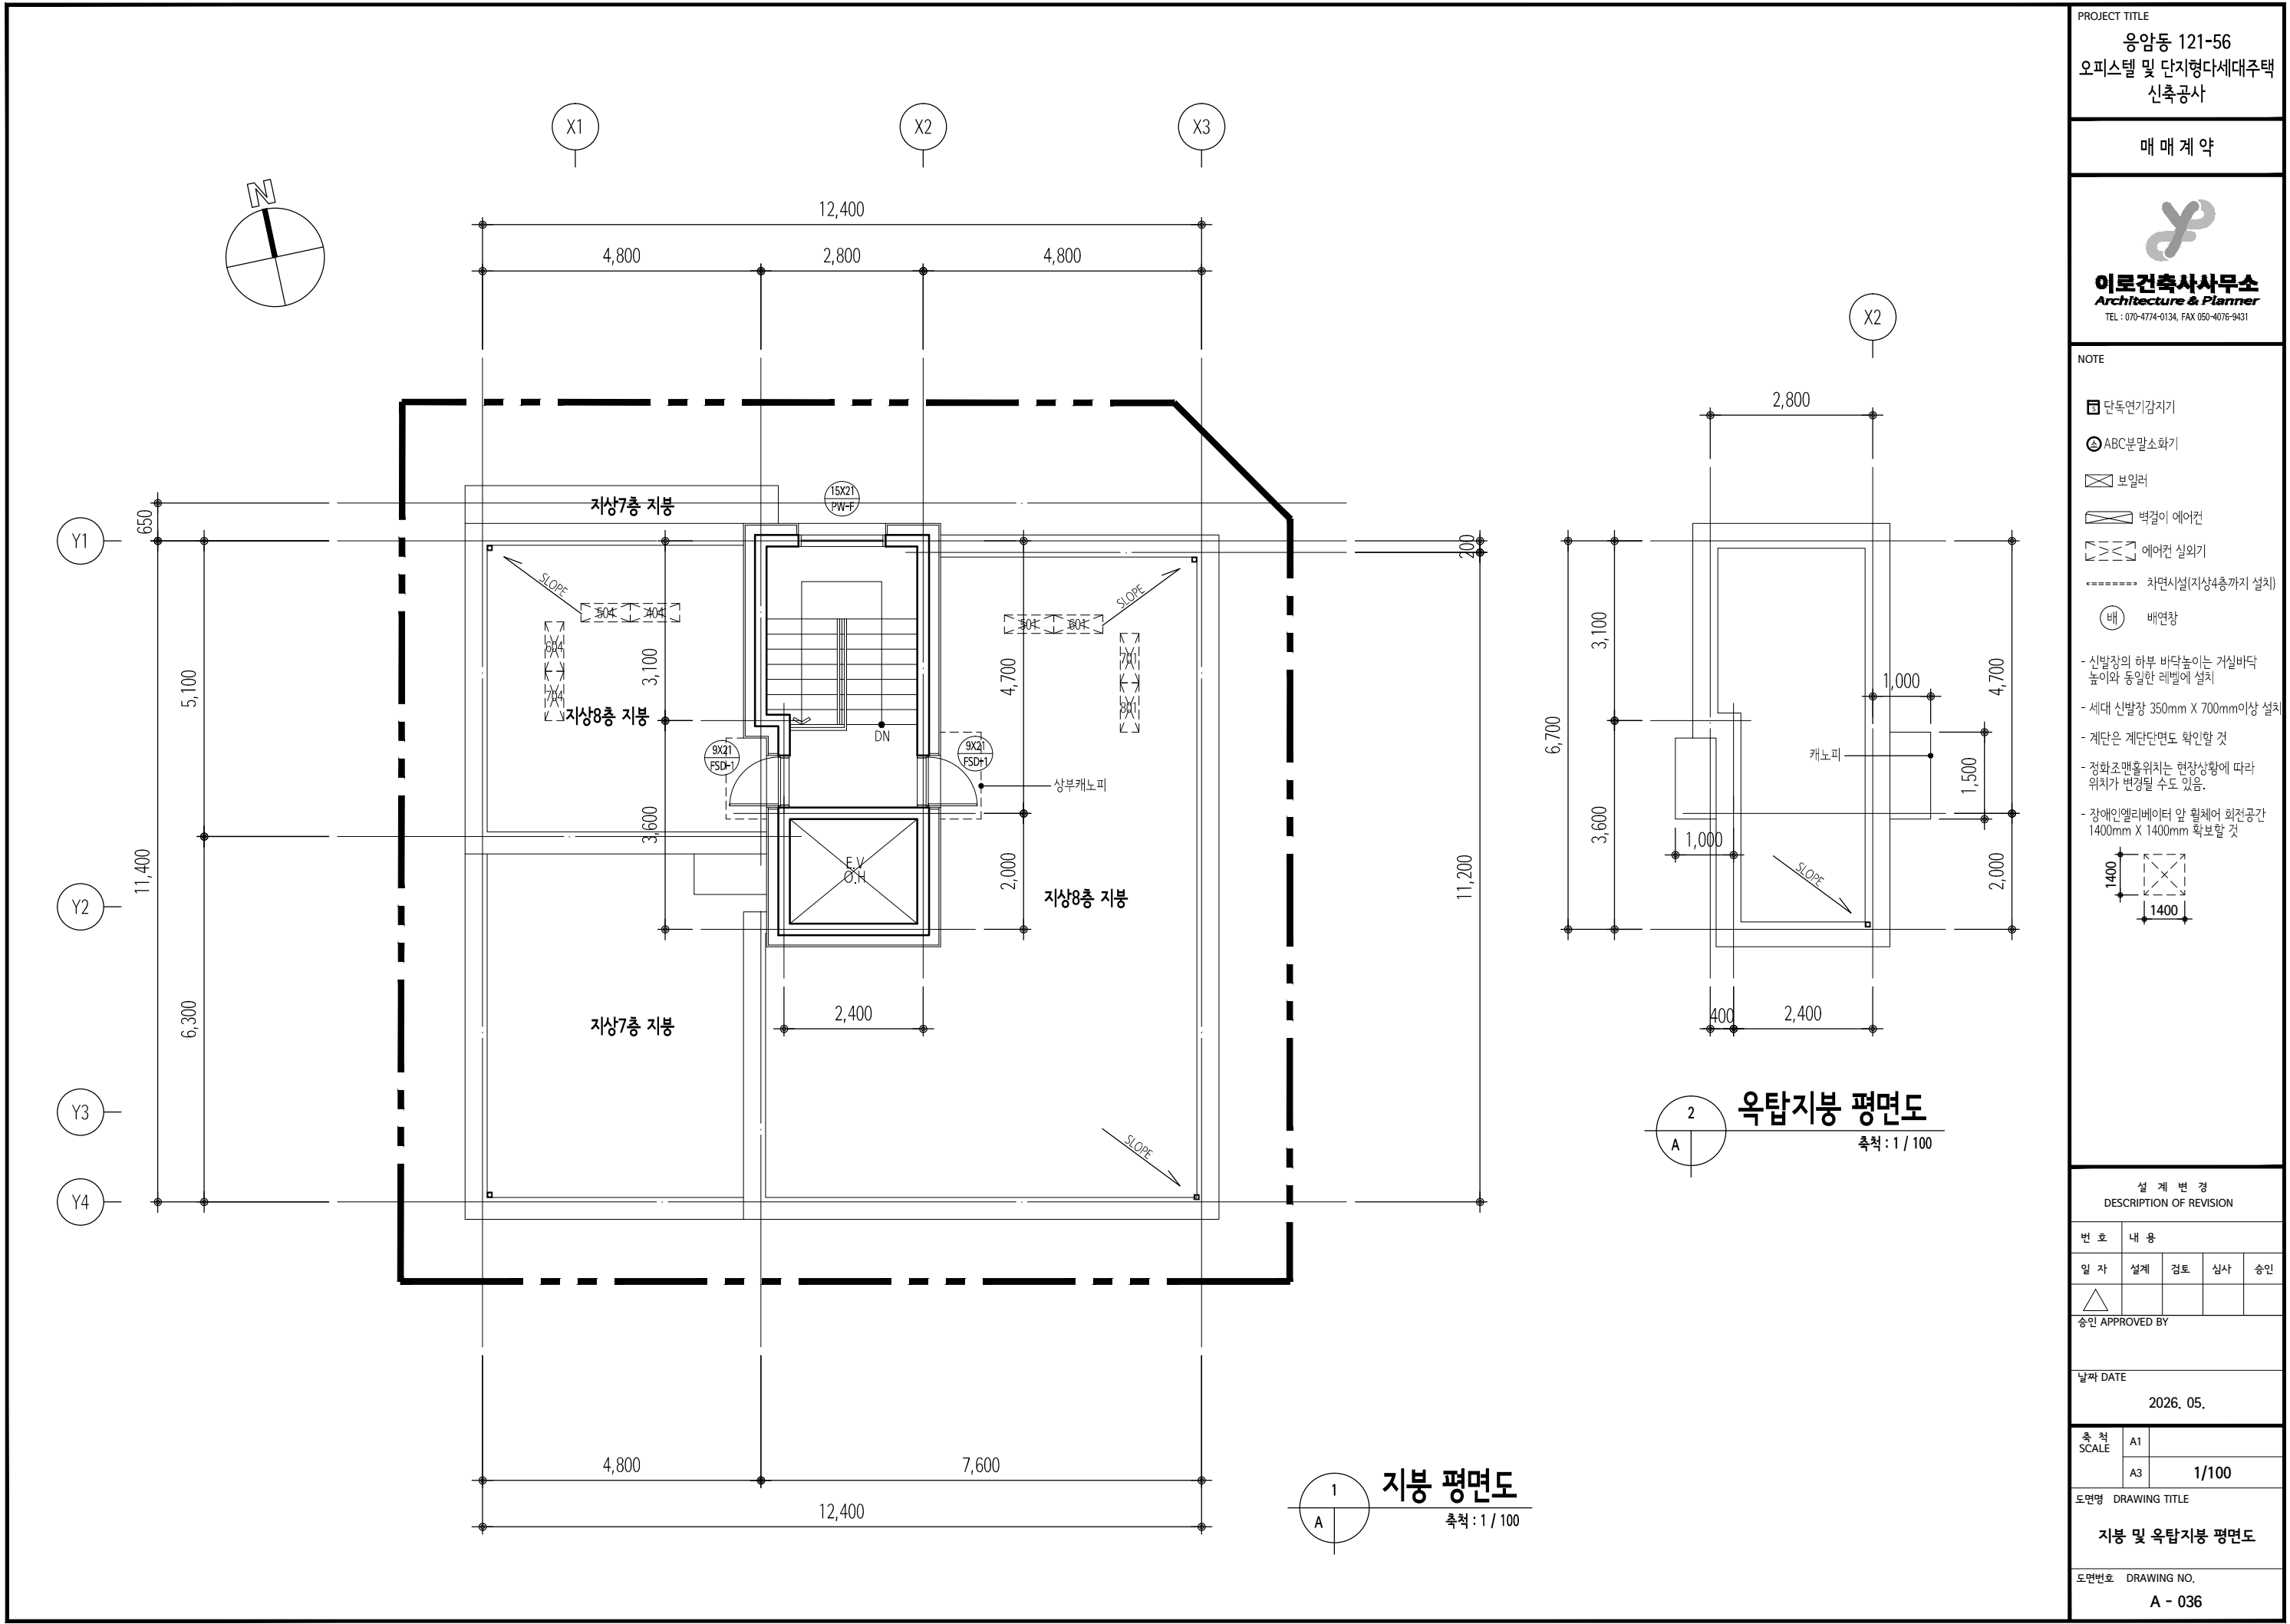

PROJECT TITLE
응암동 121-56
오피스텔 및 단지형다세대주택
신축공사

매 매 계 약

이토건축사사무소
Architecture & Planner
TEL : 070-4774-0134, FAX 050-4076-9431

NOTE

단독연기감지기

ABC분말소화기

보일러

벽걸이 에어컨

에어컨 실외기

차면시설(지상4층까지 설치)

배연창

- 신발장의 하부 바닥높이는 거실바닥
높이와 동일한 레벨에 설치

- 세대 신발장 350mm X 700mm이상 설치

- 계단은 계단단면도 확인할 것

- 정화조 맨홀위치는 현장상황에 따라
위치가 변경될 수도 있음.

- 장애인엘리베이터 앞 휠체어 회전공간
1400mm X 1400mm 확보할 것

1400

1400

설 계 변 경
DESCRIPTION OF REVISION

번 호	내 용
일 자	설 계 검 토 심 사 승 인

승인 APPROVED BY

날짜 DATE
2026. 05.

축 척 SCALE	A1	
	A3	1/100

도면명 DRAWING TITLE
지붕 및 옥탑지붕 평면도

도면번호 DRAWING NO.
A - 036



1 동측면도
축척 : 1 / 150

1 남측면도
축척 : 1 / 150

PROJECT TITLE
응암동 121-56
오피스텔 및 단지형다세대주택
신축공사

매매계약

이로건축사사무소
Architecture & Planner
TEL : 070-4774-0134, FAX 050-4076-9431

NOTE

설계변경
DESCRIPTION OF REVISION

번호	내용
일자	설계 검토 심사 승인
승인	APPROVED BY

날짜 DATE
2026. 05.

축척 SCALE	A1	A3
		1/150

도면명 DRAWING TITLE
동측면도, 남측면도

도면번호 DRAWING NO.
A - 060



1
A
서측면도
축척: 1 / 150

1
A
북측면도
축척: 1 / 150

PROJECT TITLE

응암동 121-56

오피스텔 및 단지형다세대주택

신축공사

매매계약



이로건축사사무소

Architecture & Planner

TEL : 070-4774-0134, FAX 050-4076-9431

NOTE

설계변경

DESCRIPTION OF REVISION

번호	내용				
일자	설계	검토	심사	승인	
					

승인 APPROVED BY

날짜 DATE

2026. 05.

축척 SCALE	A1	
	A3	1/150

도면명 DRAWING TITLE

서측면도, 북측면도

도면번호 DRAWING NO.

A - 061