

X1 X2 X3 X4 X5 X6 X7 X8 X9

14,000

3,000


8,000

3,000

3,500

3,200

1,300

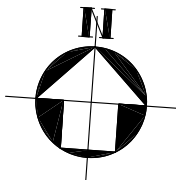


Y3

Y2

Y1

9,400
5,800
4,700
2,400
1,200

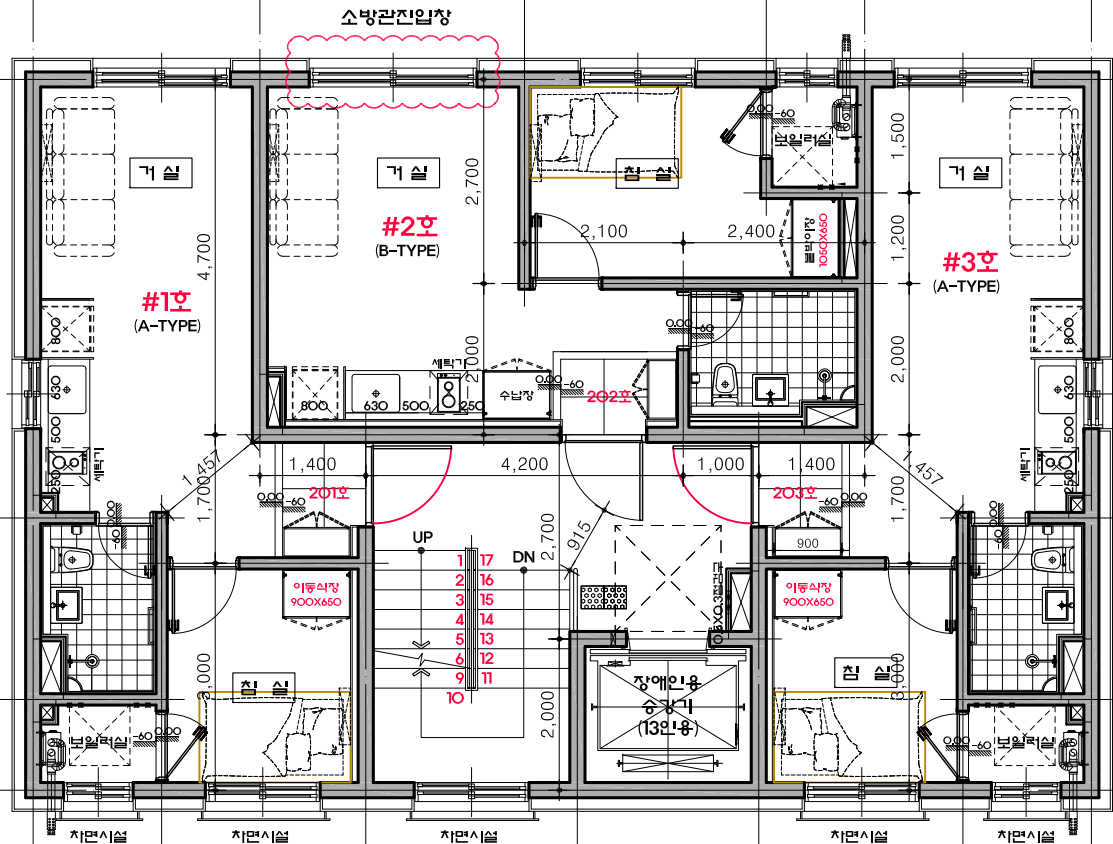

1,700 2,700 2,800 2,400 2,700 1,700

4,400

5,200

4,400

14,000

2 층 평 면 도

SCALE:1/100

15 전자레인지 및 장 설치



16 불박이장 설치



900 X 650 X 2200

17 신발장 설치




유효깊이 320mm, 유효폭 최소 700mm 이상
아래 SST 우산꽂이(문반)이도착(적용)
서랍 적용 시 불박이장 적용


주 기

- 1 세대 현관문 도어체크 및 스토퍼 계획
- 2 세대 발코니 설치시 세대간 분리벽 계획
- 3 세대내 비디오폰 설치
- 4 주차장내 CCTV 설치
- 5 벽체
입벽 직접 외기에 면한 실내벽면은 단열재 (아이소핑크10mm+석고보드 마감도면 표기)
계단실 간접 외기에 면한 실내벽면은 단열재 (강질폴리우레탄폼단열재2중2호80mm+석고보드 마감도면 표기)
/복도
- 6 에어컨 실외기 설치위치 및 에어컨 도면표기
- 7 불박이 가구 내부 다용도 수납기능토록 수평이동 칸막이 설치
- 8 콘크리트 골타이 제거후 마감공사 시공(방수 및 단열재 시공등)
- 9 구조
콘크리트 : fck=27Mpa
철근 : fy=400Mpa
세대 벽두께 : 150mm(복배근)
입벽 벽두께 : 210mm(복배근)
코어 벽두께 : 210mm(복배근)
2중 스크린 두께 : 210mm(복배근)

- 10 기타 실내 벽면은 시멘트 미장미감
- 11 욕실 & 다용도실 스위치 : 문열리는 방향으로 시공
- 12 공동주택 바닥충격음 차단구조기준

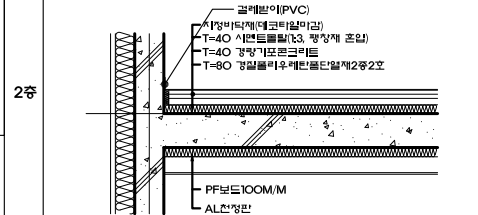

- 13 소방관 진입장의 기준
건축물의 피난방화구조등의 기준에 관한규칙 제18조외2에 의거
1. 2층이상 11층이하인 층에 각각 1개소 이상설치
2. 소방관진입로또는 소방차 진입이 가능한 공터에 면할것
3. 창문의 가운데에 지름20센티 이상의 역삼각형을 아간에도
열어줄 수 있도록 빛 반사 등으로 붉은색으로 표시할 것
4. 창문 한쪽 모서리에 타격지점 표시 (Ø30 이상의 원형)
5. 창문크기 : 폭900 높이1,000이상
(바닥에서 창아랫부분 높이800이내로 설치)
(난간이 설치된 노대등에 불기러미가 설치시 1200이내로 할것)
6. 다층 각 층의 어느 하나에 해당하는 유리 사용할 것
가. 플로트관유리로서 두께6mm이하인것
나. 강화유리/배강도유리로서 두께5mm이하인것
다. 기록 또는 기록에 해당하는 유리로 구성된 이중 유리
라. 기록 또는 기록에 해당하는 유리로 구성된 삼중유리

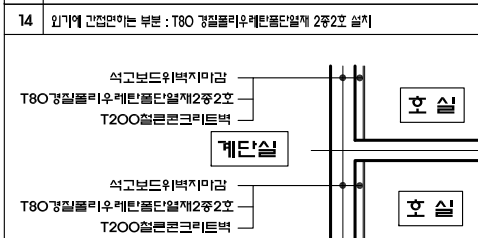

NOTE:

PROJECT 은평구 길연동 406-32번지 도시형 생활 주택
단지형 다세대주택 신축공사 (정년주택)

APPROVED BY 건축사







LINK (주)유엔케이 건축사사무소
Planners, Architects, Engineers, Consultants
서울특별시 서초구 미망로6길 29, 망성빌딩 4층
TEL : 070-7774-3988, FAX : 070-7966-3903
010-4422-4121

TITLE 2 층 평 면 도

날짜 DATE: 2026. 02.

SCALE 1 / 100 DWG NO. A - 027 REV.

X1

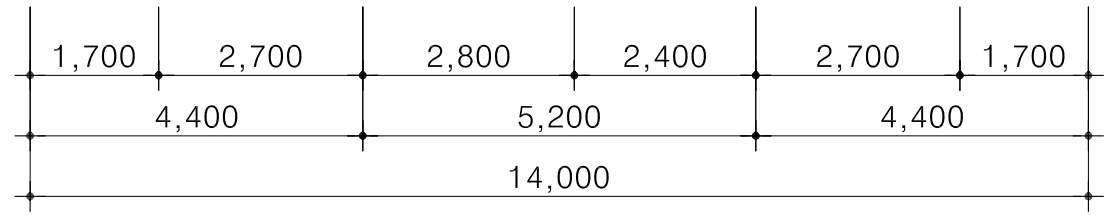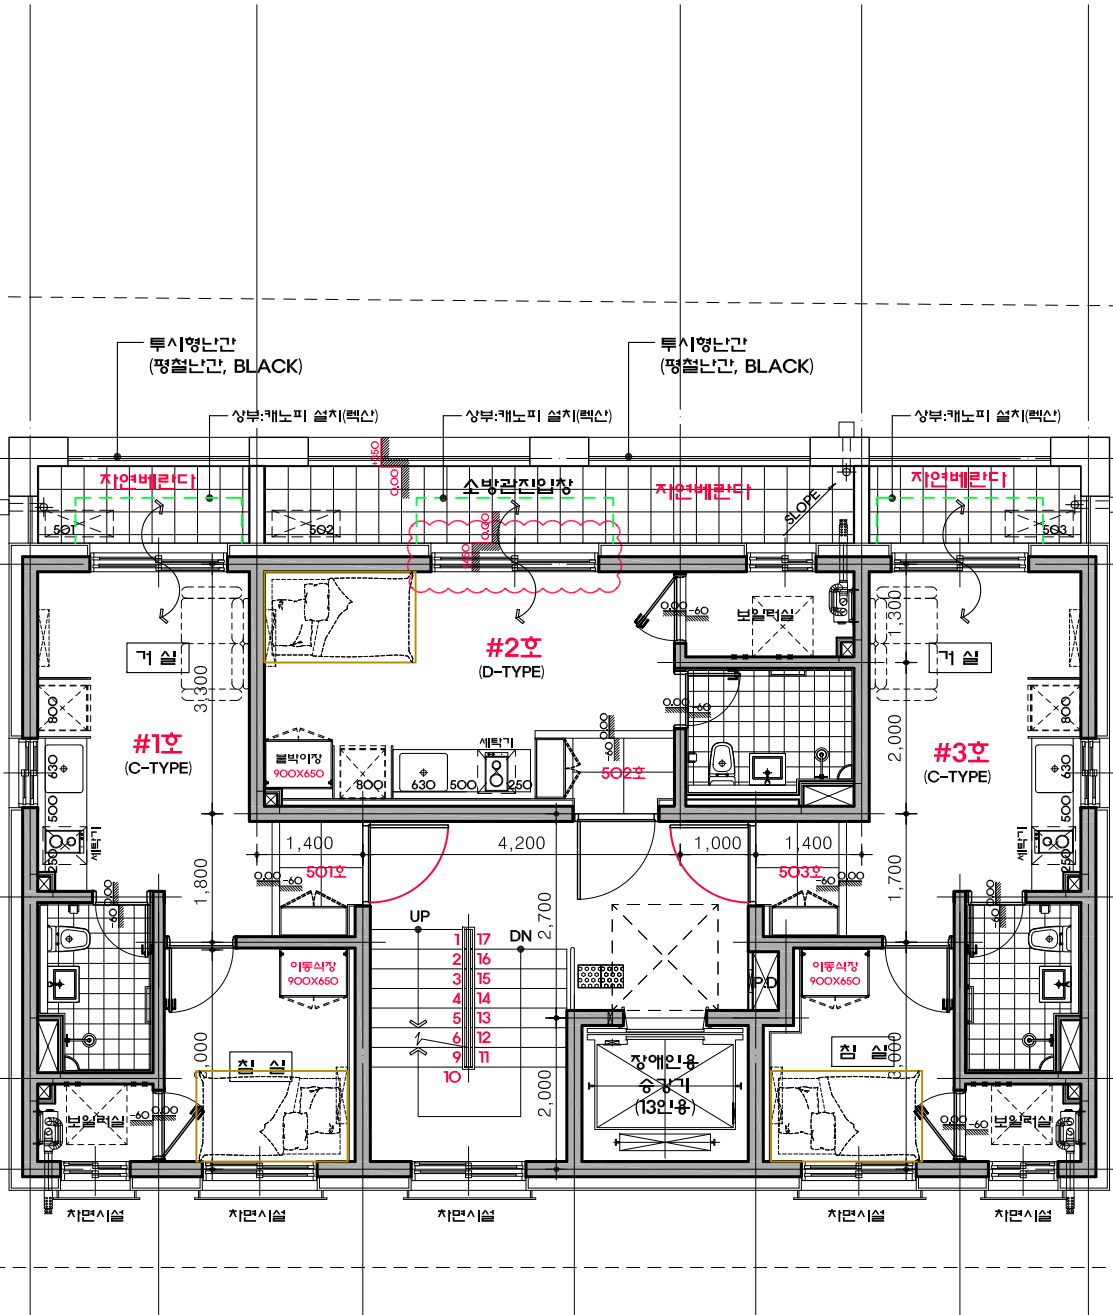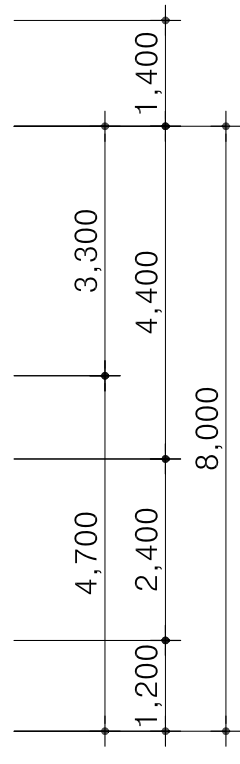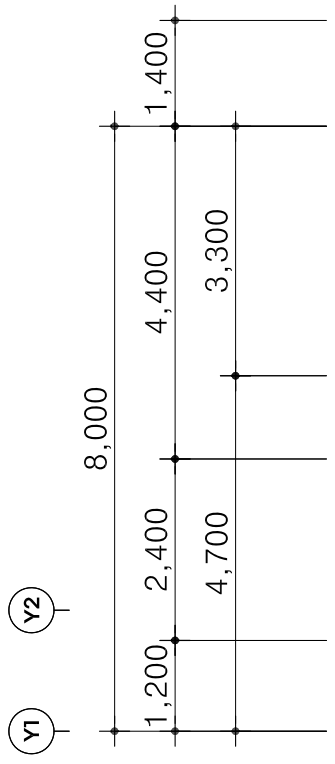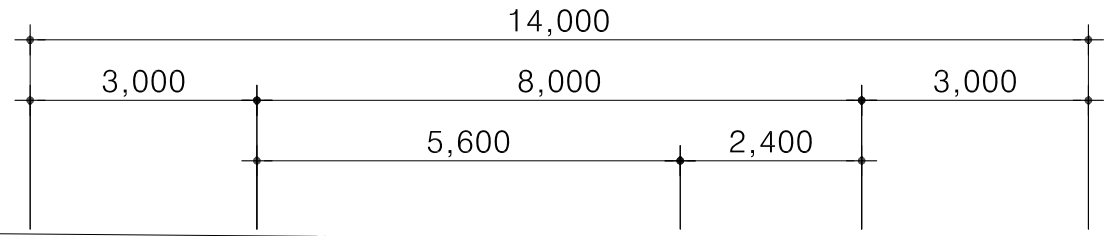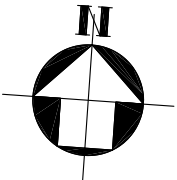

5 층 평 면 도
SCALE:1/100

15 전자레인지 및 장 설치		주 기	
	16 불박이장 설치	1	세대 현관문 도어체크 및 스토퍼 계획
		2	세대 발코니 설치시 세대간 분리벽 계획
		3	세대내 비디오폰 설치
		4	주차장내 CCTV 설치
	17 신발장 설치	5	벽체 입벽 직접 외기에 면한 실내벽면은 단열재 (아이소핑크10mm+석고보드 마감도면 표기) 계단실 간접 외기에 면한 실내벽면은 단열재 (강질물리우레탄폴단열재2종2호80mm+석고보드 마감도면 표기) /복도
		6	에어콘 실외기 설치위치 및 에어컨 도면표기
		7	불박이 가구 내부 다용도 수납기능토록 수평이동 칸막이 설치
		8	콘크리트 풀타이 제거후 마감공사 시공(방수 및 단열재 시공등)
	5층	9	콘크리트 : fck=27Mpa 철근 : fy=400Mpa 세대 벽두께 : 150mm(복배근) 입벽 벽두께 : 210mm(복배근) 코어 벽두께 : 210mm(복배근) 4층 스리브 두께 : 210mm(복배근)
		10	가터 실내 벽면은 시멘트 미장미감
		11	욕실 & 다용도실 스위치 : 문열리는 방향으로 시공
		12	공동주택 바닥충격음 차단구조기준
	13	소방관 진입장의 기준 건축물의 피난·방화구조등의 기준에 관한규칙 제18조의2에 의거 1. 2층이상 11층이하인 층에 각각 1개소 이상설치 2. 소방차진입로또는 소방차 진입이 가능한 공터에 면할것 3. 창문의 가운데에 지름20센티 이상의 역삼각형을 아간에도 알아볼 수 있도록 빛 반사 등으로 붉은색으로 표시할 것 4. 창문 한쪽 모서리에 타격지점 표시 (Ø30 이상의 원형) 5. 창문크기 : 폭900 높이1,000이상 (바닥에서 창아랫부분 높이800이내로 설치) (난간이 설치된 노대등에 불기라아게 설치시 1200이내로 할것) 6. 다들 각 폭의 어느 하나에 해당하는 유리 사용할 것 가. 플로트란유리로서 두께6mm이아인것 나. 강화유리/배강도유리로서 두께5mm이아인것 다. 기록 또는 기록에 해당하는 유리로 구성된 이중 유리 라. 기록 또는 기록에 해당하는 유리로 구성된 삼중유리	
		14	
		입기에 간접연하는 부분 : T80 강질물리우레탄폴단열재 2종2호 설치	

NOTE:

PROJECT 은평구 길연동 406-32번지 도시형 생활 주택
단지형 다세대주택 신축공사 (정년주택)


APPROVED BY 건축사

(주)유엔케이 건축사사무소
Planners, Architects, Engineers, Consultants
서울특별시 서초구 미망로6길 29, 망성빌딩 4층
TEL : 070-7774-3988, FAX : 070-7966-3903
010-4422-4121


TITLE 5 층 평 면 도


날짜 DATE: 2026. 02.

SCALE 1 / 100 DWG NO. A - 029 REV.

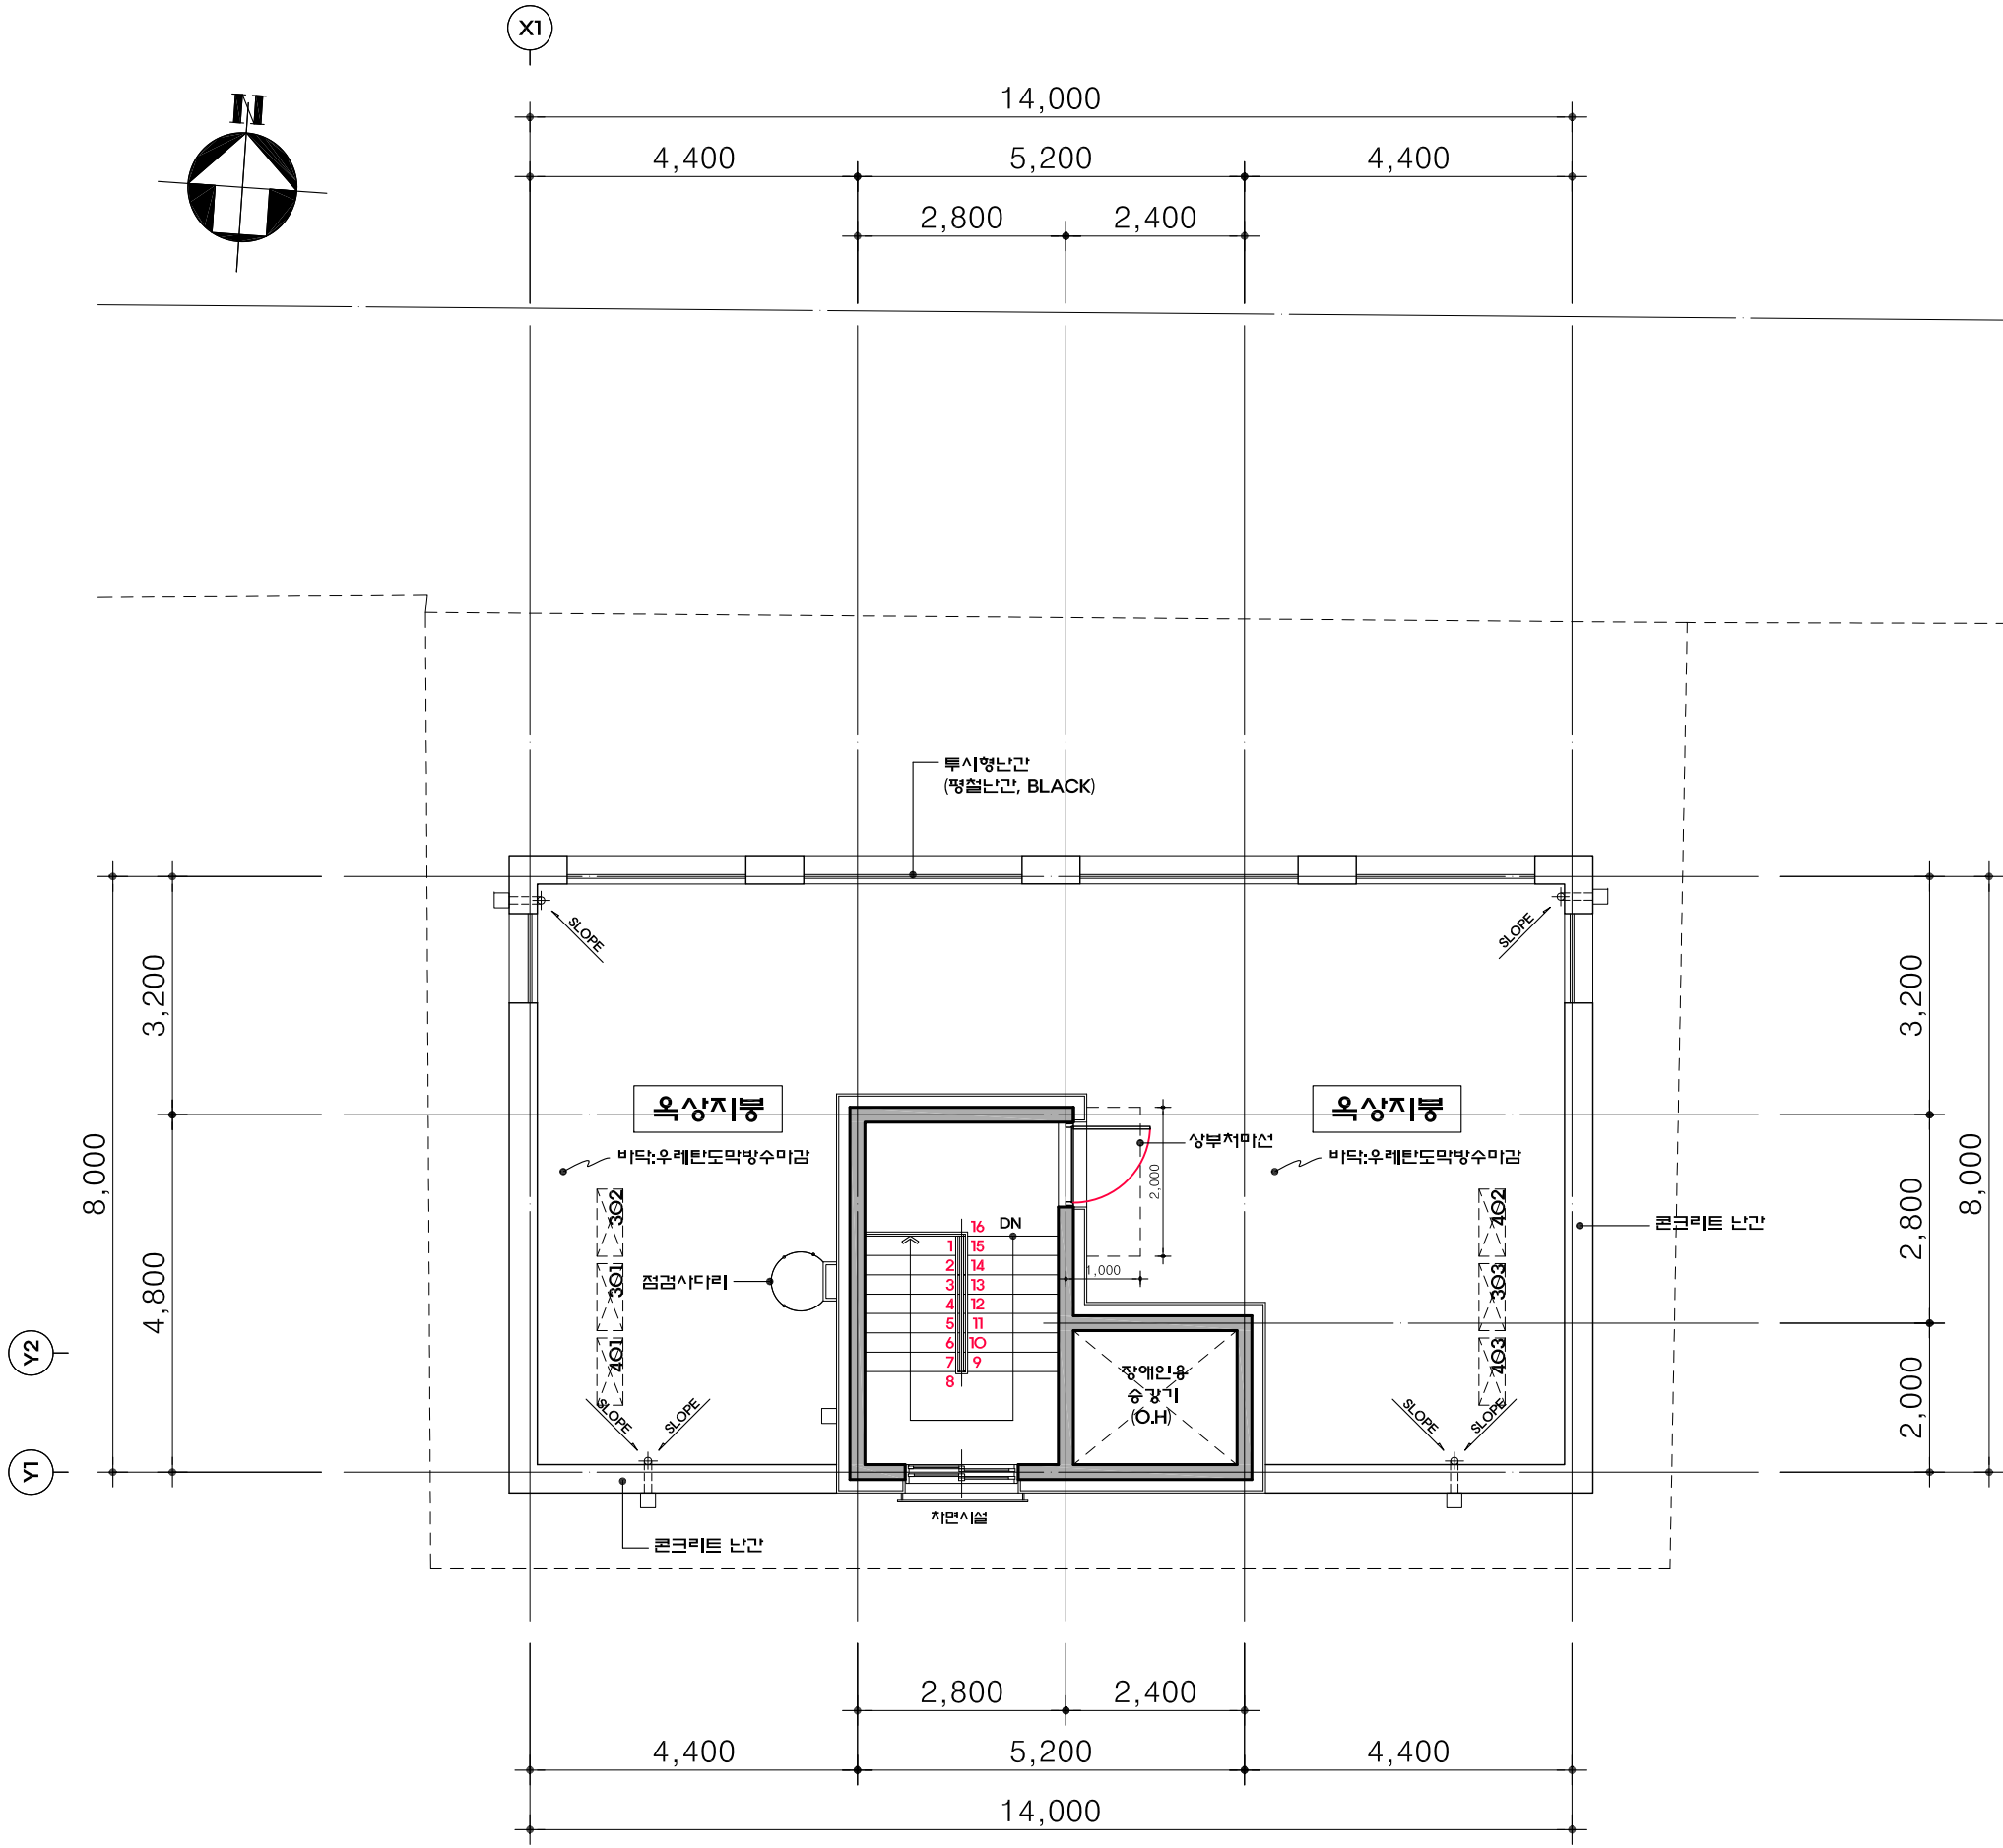


옥탑층 평면도
SCALE:1/100

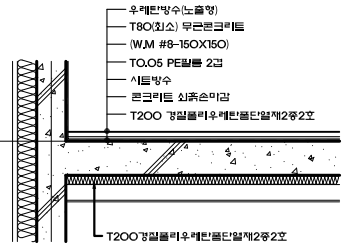주 기	
1	콘크리트 : fck=27Mpa 철근 : fy=400Mpa
구조	난간 벽두께 : 200mm(복배근)
	코아 벽두께 : 200mm(복배근)
	지붕 슬라브 두께 : 180mm(복배근)
2	

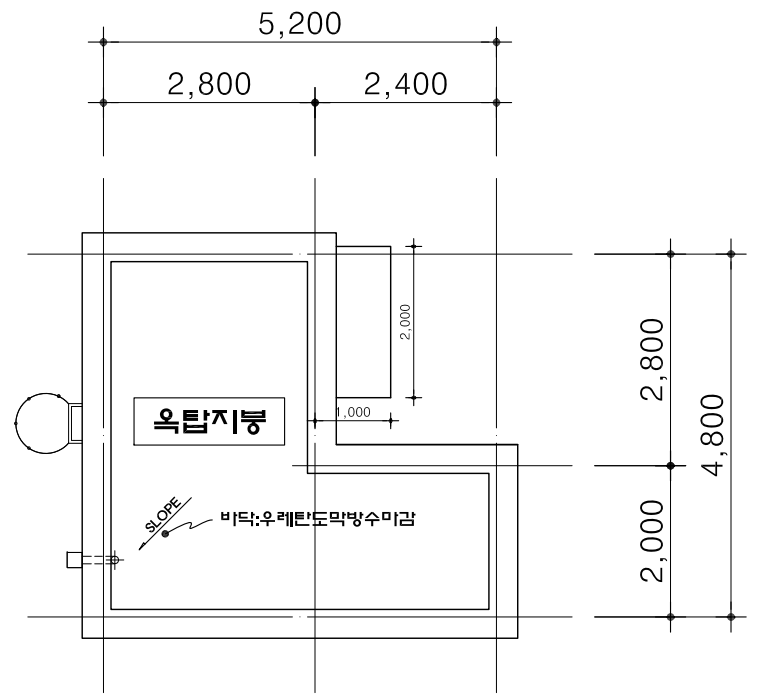

옥탑 지붕층 평면도
SCALE:1/100

NOTE:			
PROJECT 은평구 갈연동 406-32번지 도시형 생활 주택 단지형 다세대주택 신축공사 (정년주택)			
APPROVED BY 건축사 			
LINK (주)유엔케이 건축사사무소 Planners, Architects, Engineers, Consultants 서울특별시 서초구 미림로6길 29, 영성빌딩 4층 TEL : 070-7774-3988, FAX : 070-7966-3903 010-4422-4121			
TITLE 옥탑층 평면도 옥탑 지붕층 평면도			
날짜 DATE: 2026. 02.			
SCALE 1 / 100	DWG NO. A - 030	REV.	

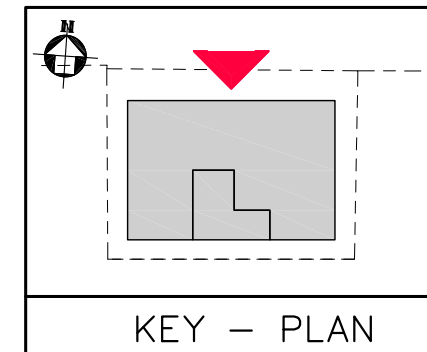

정 면 도
SCALE:1/100

NOTE:

PROJECT 은평구 길연동 406-32번지 도시형 생활 주택
단지형 다세대주택 신축공사 (정년주택)



APPROVED BY 건축사

UNK (주)유엔케이 건축사무소
Planners, Architects, Engineers, Consultants
서울특별시 서초구 미망로6길 29, 영성빌딩 4층
TEL : 070-7774-3988, FAX : 070-7966-3903
010-4422-4121

TITLE 정 면 도

날짜 DATE: 2026. 02

SCALE 1 / 100 DWG NO. A - 037 REV.

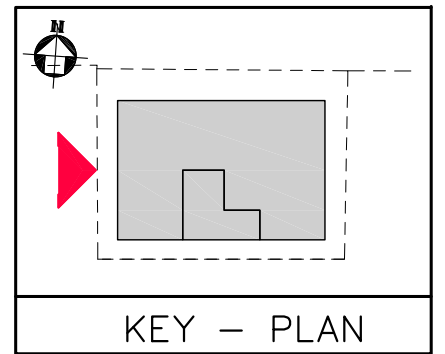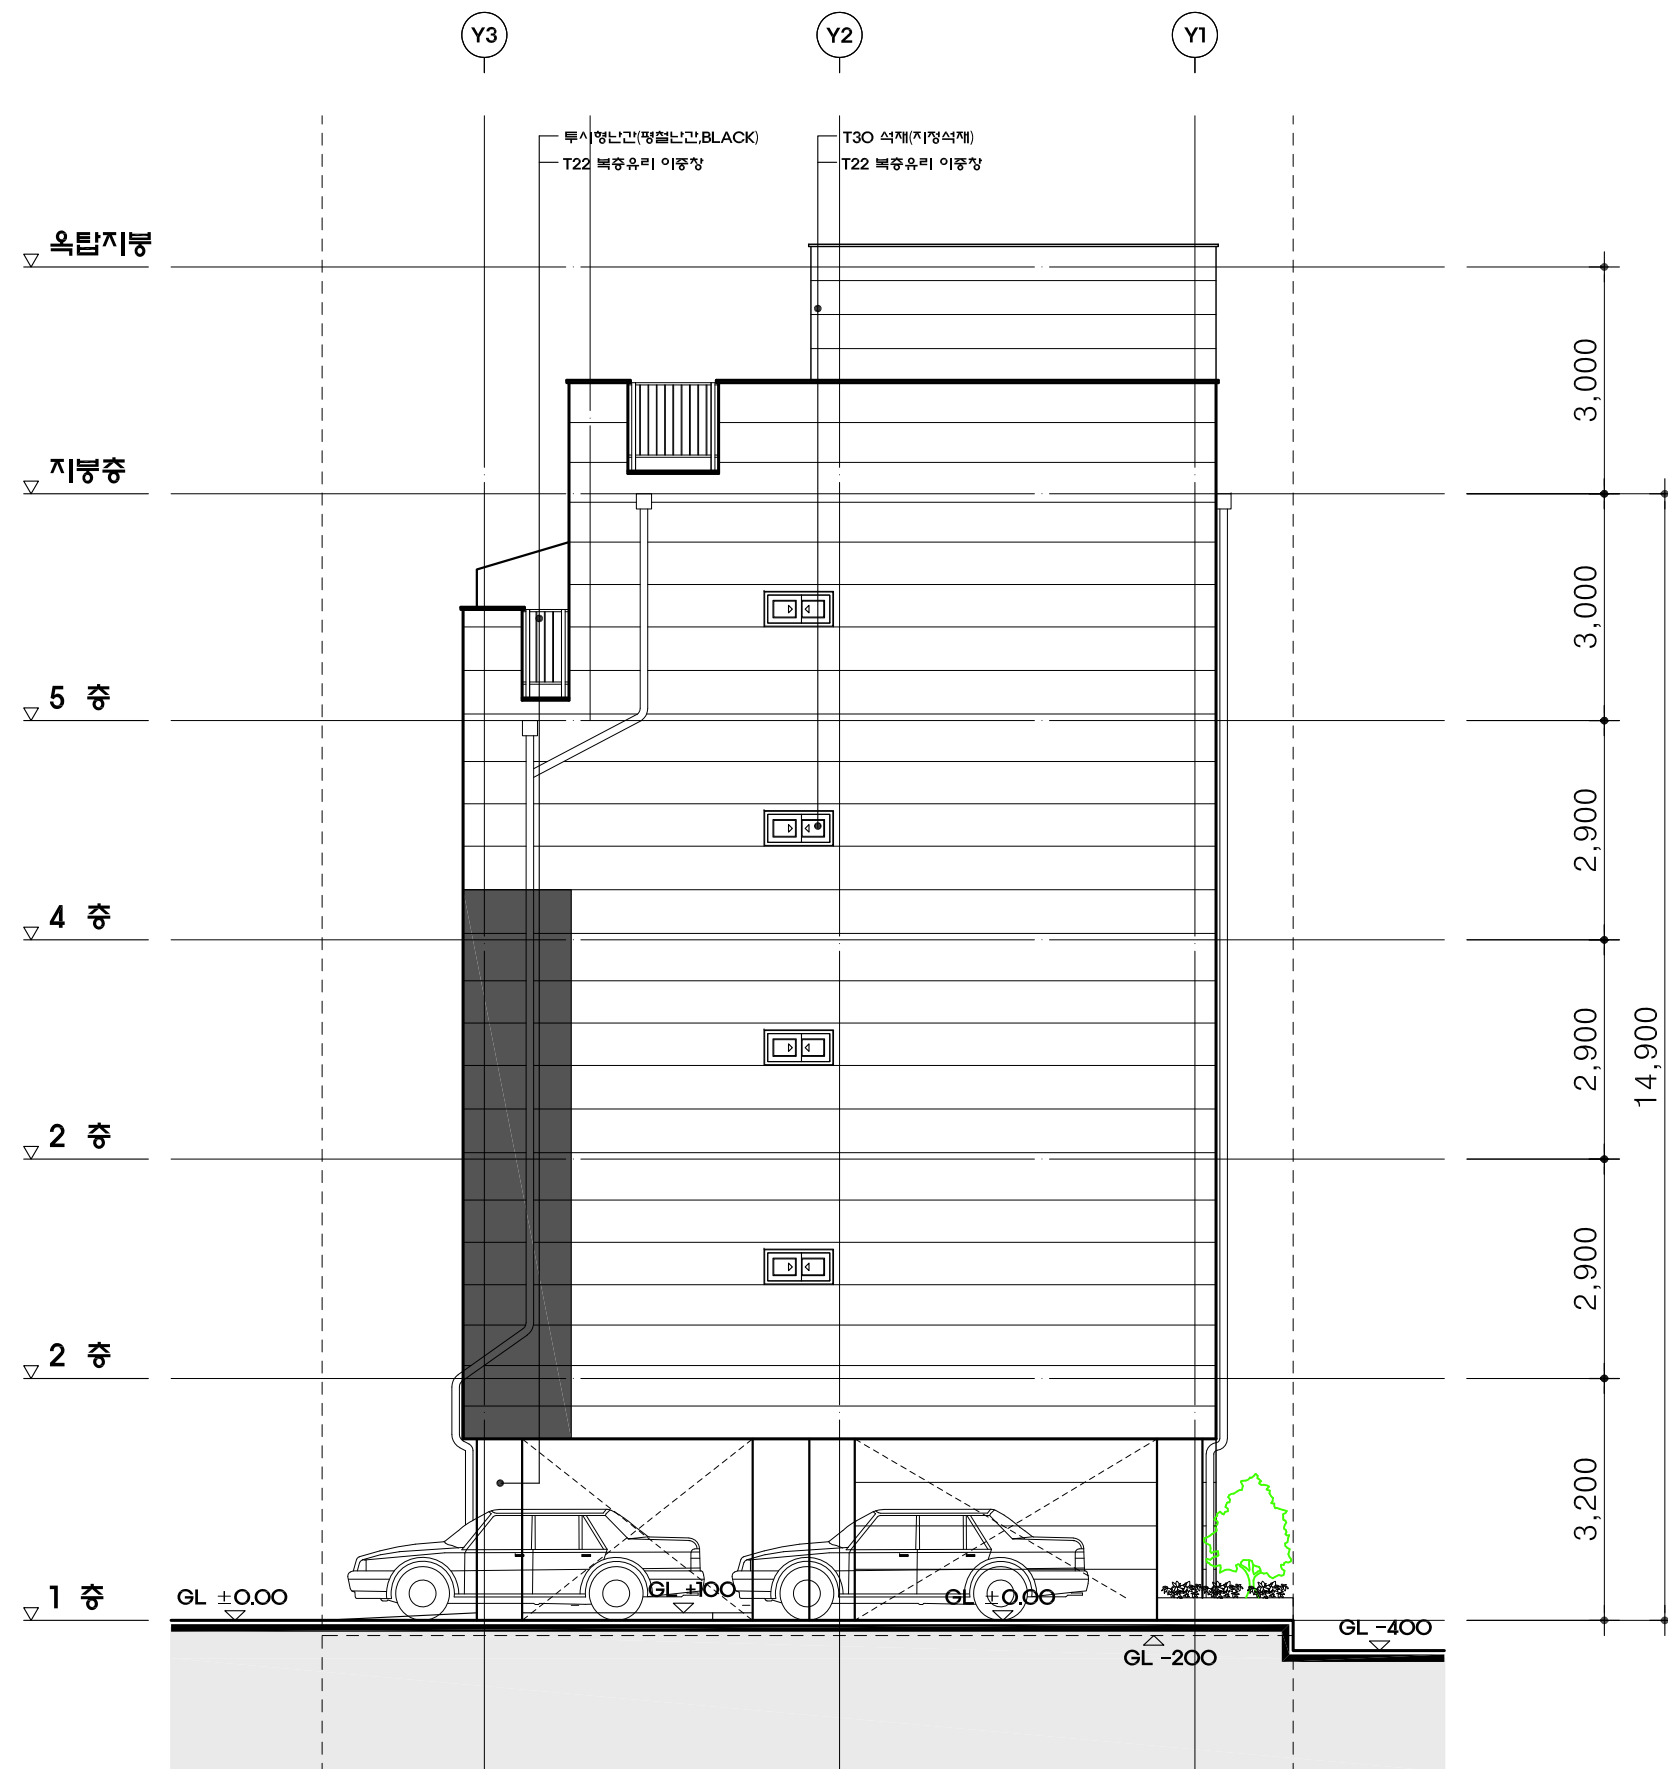

NOTE:

PROJECT 은평구 길연동 406-32번지 도시형 생활 주택
단지형 다세대주택 신축공사 (청년주택)



APPROVED BY 건축사 

UNK (주)유엔케이 건축사무소
Planners, Architects, Engineers, Consultants
서울특별시 서초구 미망로6길 29, 영성빌딩 4층
TEL : 070-7774-3988, FAX : 070-7966-3903
010-4422-4121

TITLE 우측면도

날짜 DATE: 2026. 02

SCALE 1 / 100	DWG NO. A - 038	REV.
---------------	-----------------	------

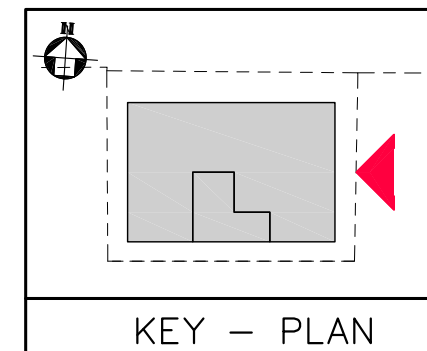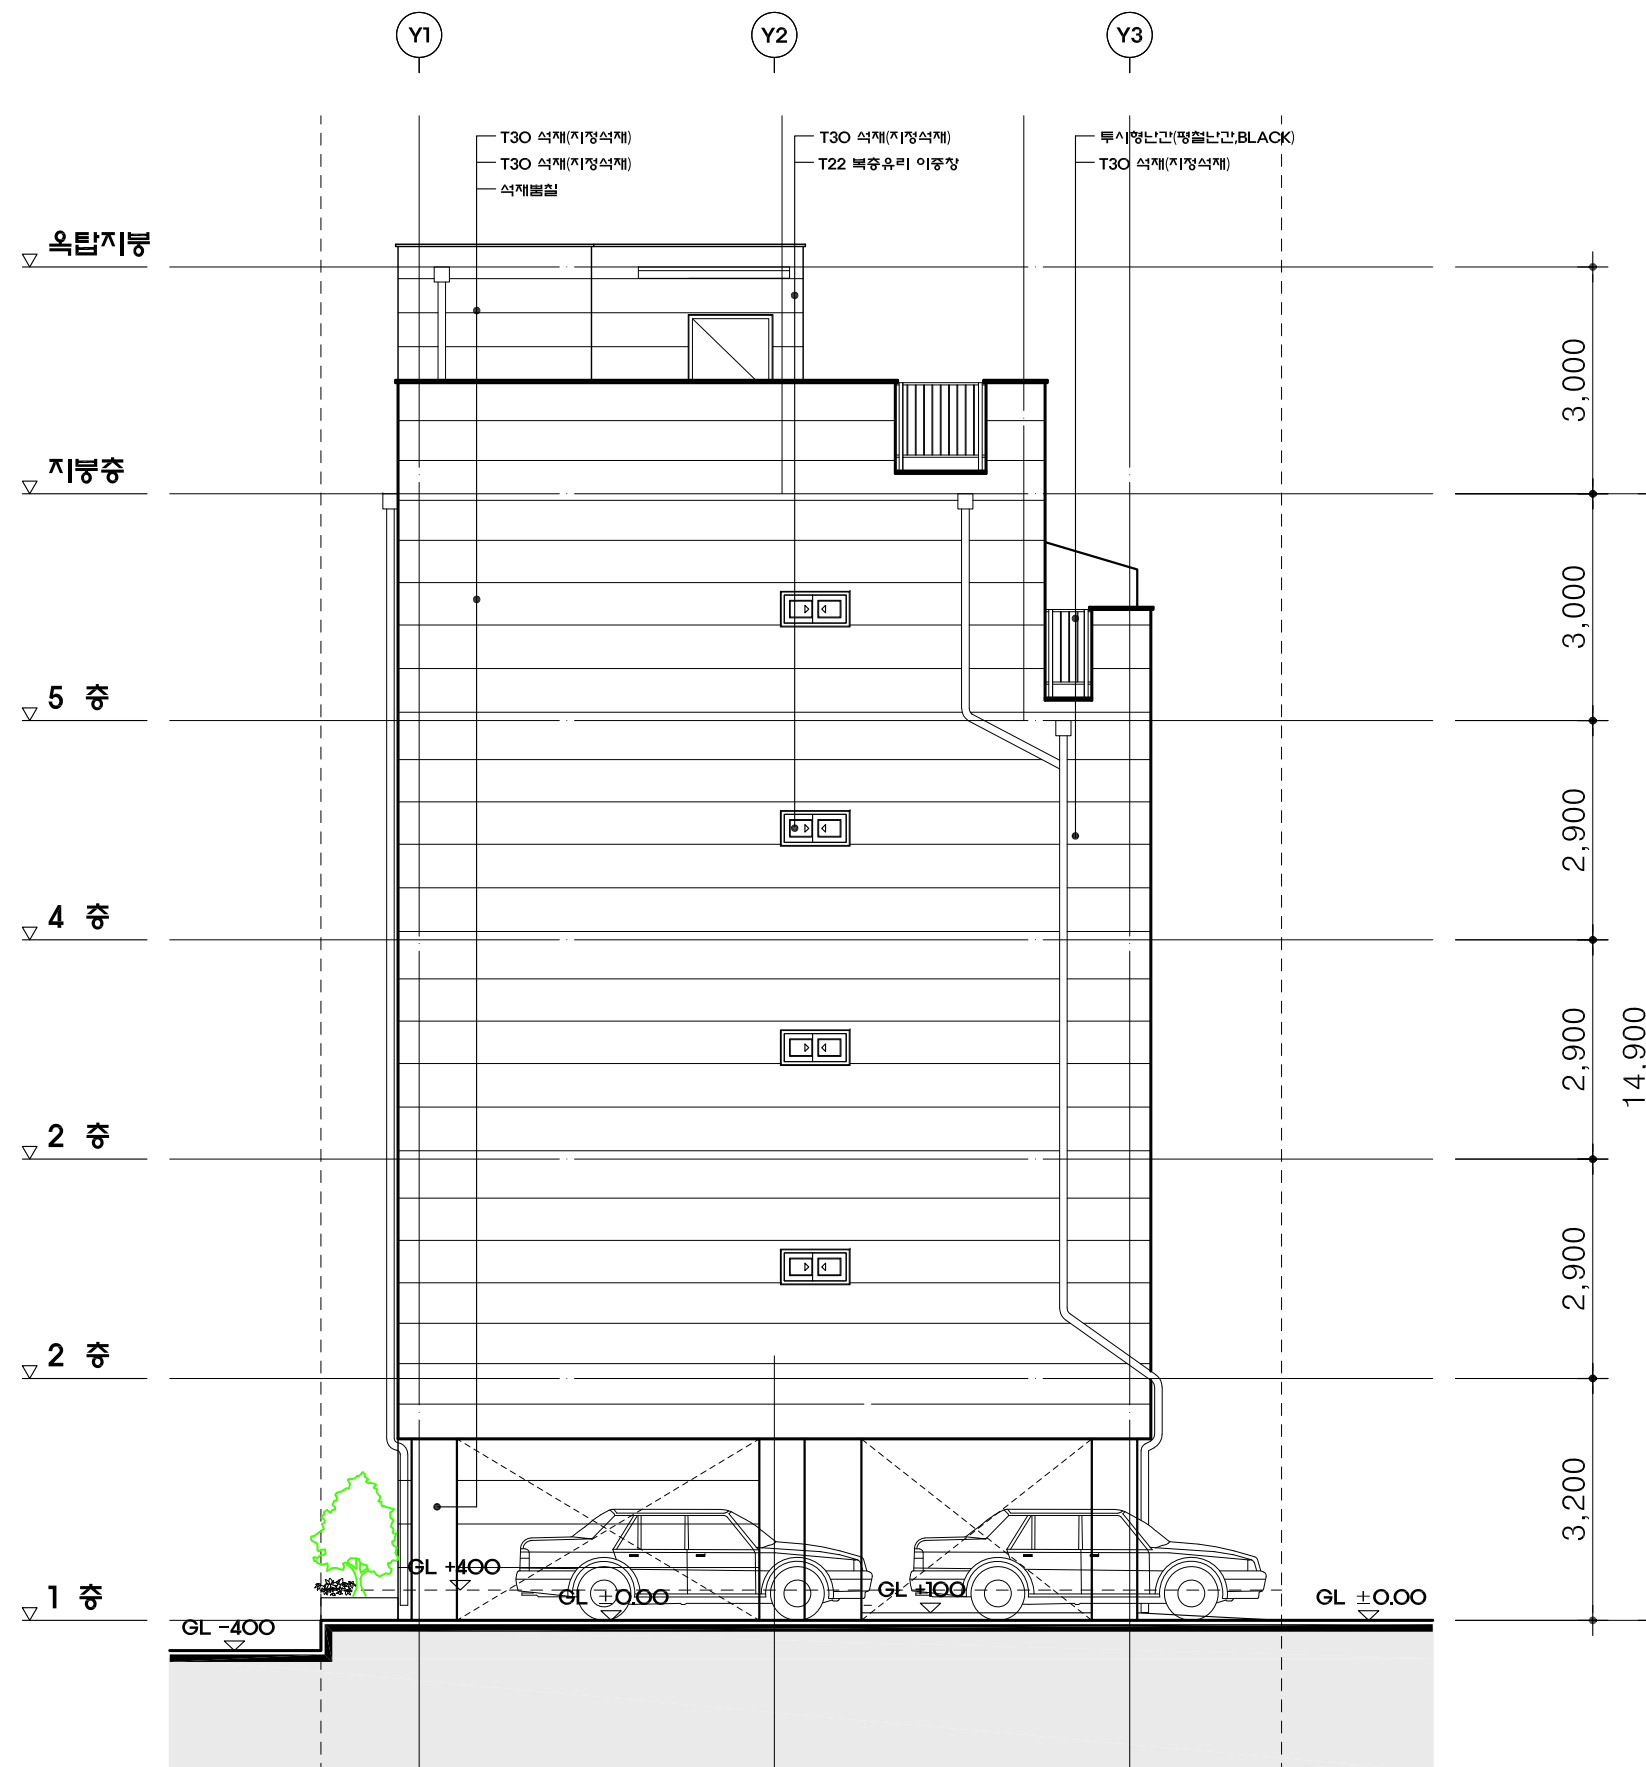

좌 측 면 도

SCALE:1/100

NOTE:

PROJECT 은평구 길원동 406-32번지 도시형 생활 주택
단지형 다세대주택 신축공사 (청년주택)



APPROVED BY 건축사

UNK (주)유엔케이 건축사무소
Planners, Architects, Engineers, Consultants
서울특별시 서초구 미망로6길 29, 영성빌딩 4층
TEL : 070-7774-3988, FAX : 070-7966-3903
010-4422-4121

TITLE 좌 측 면 도

날짜 DATE: 2026. 02

SCALE 1 / 100 DWG NO. A - 039 REV.

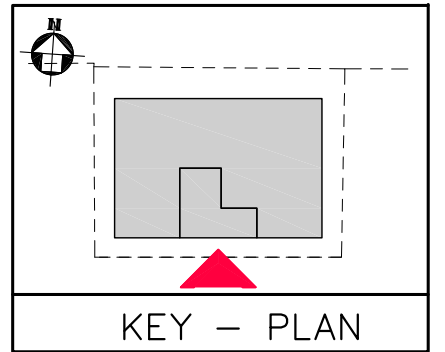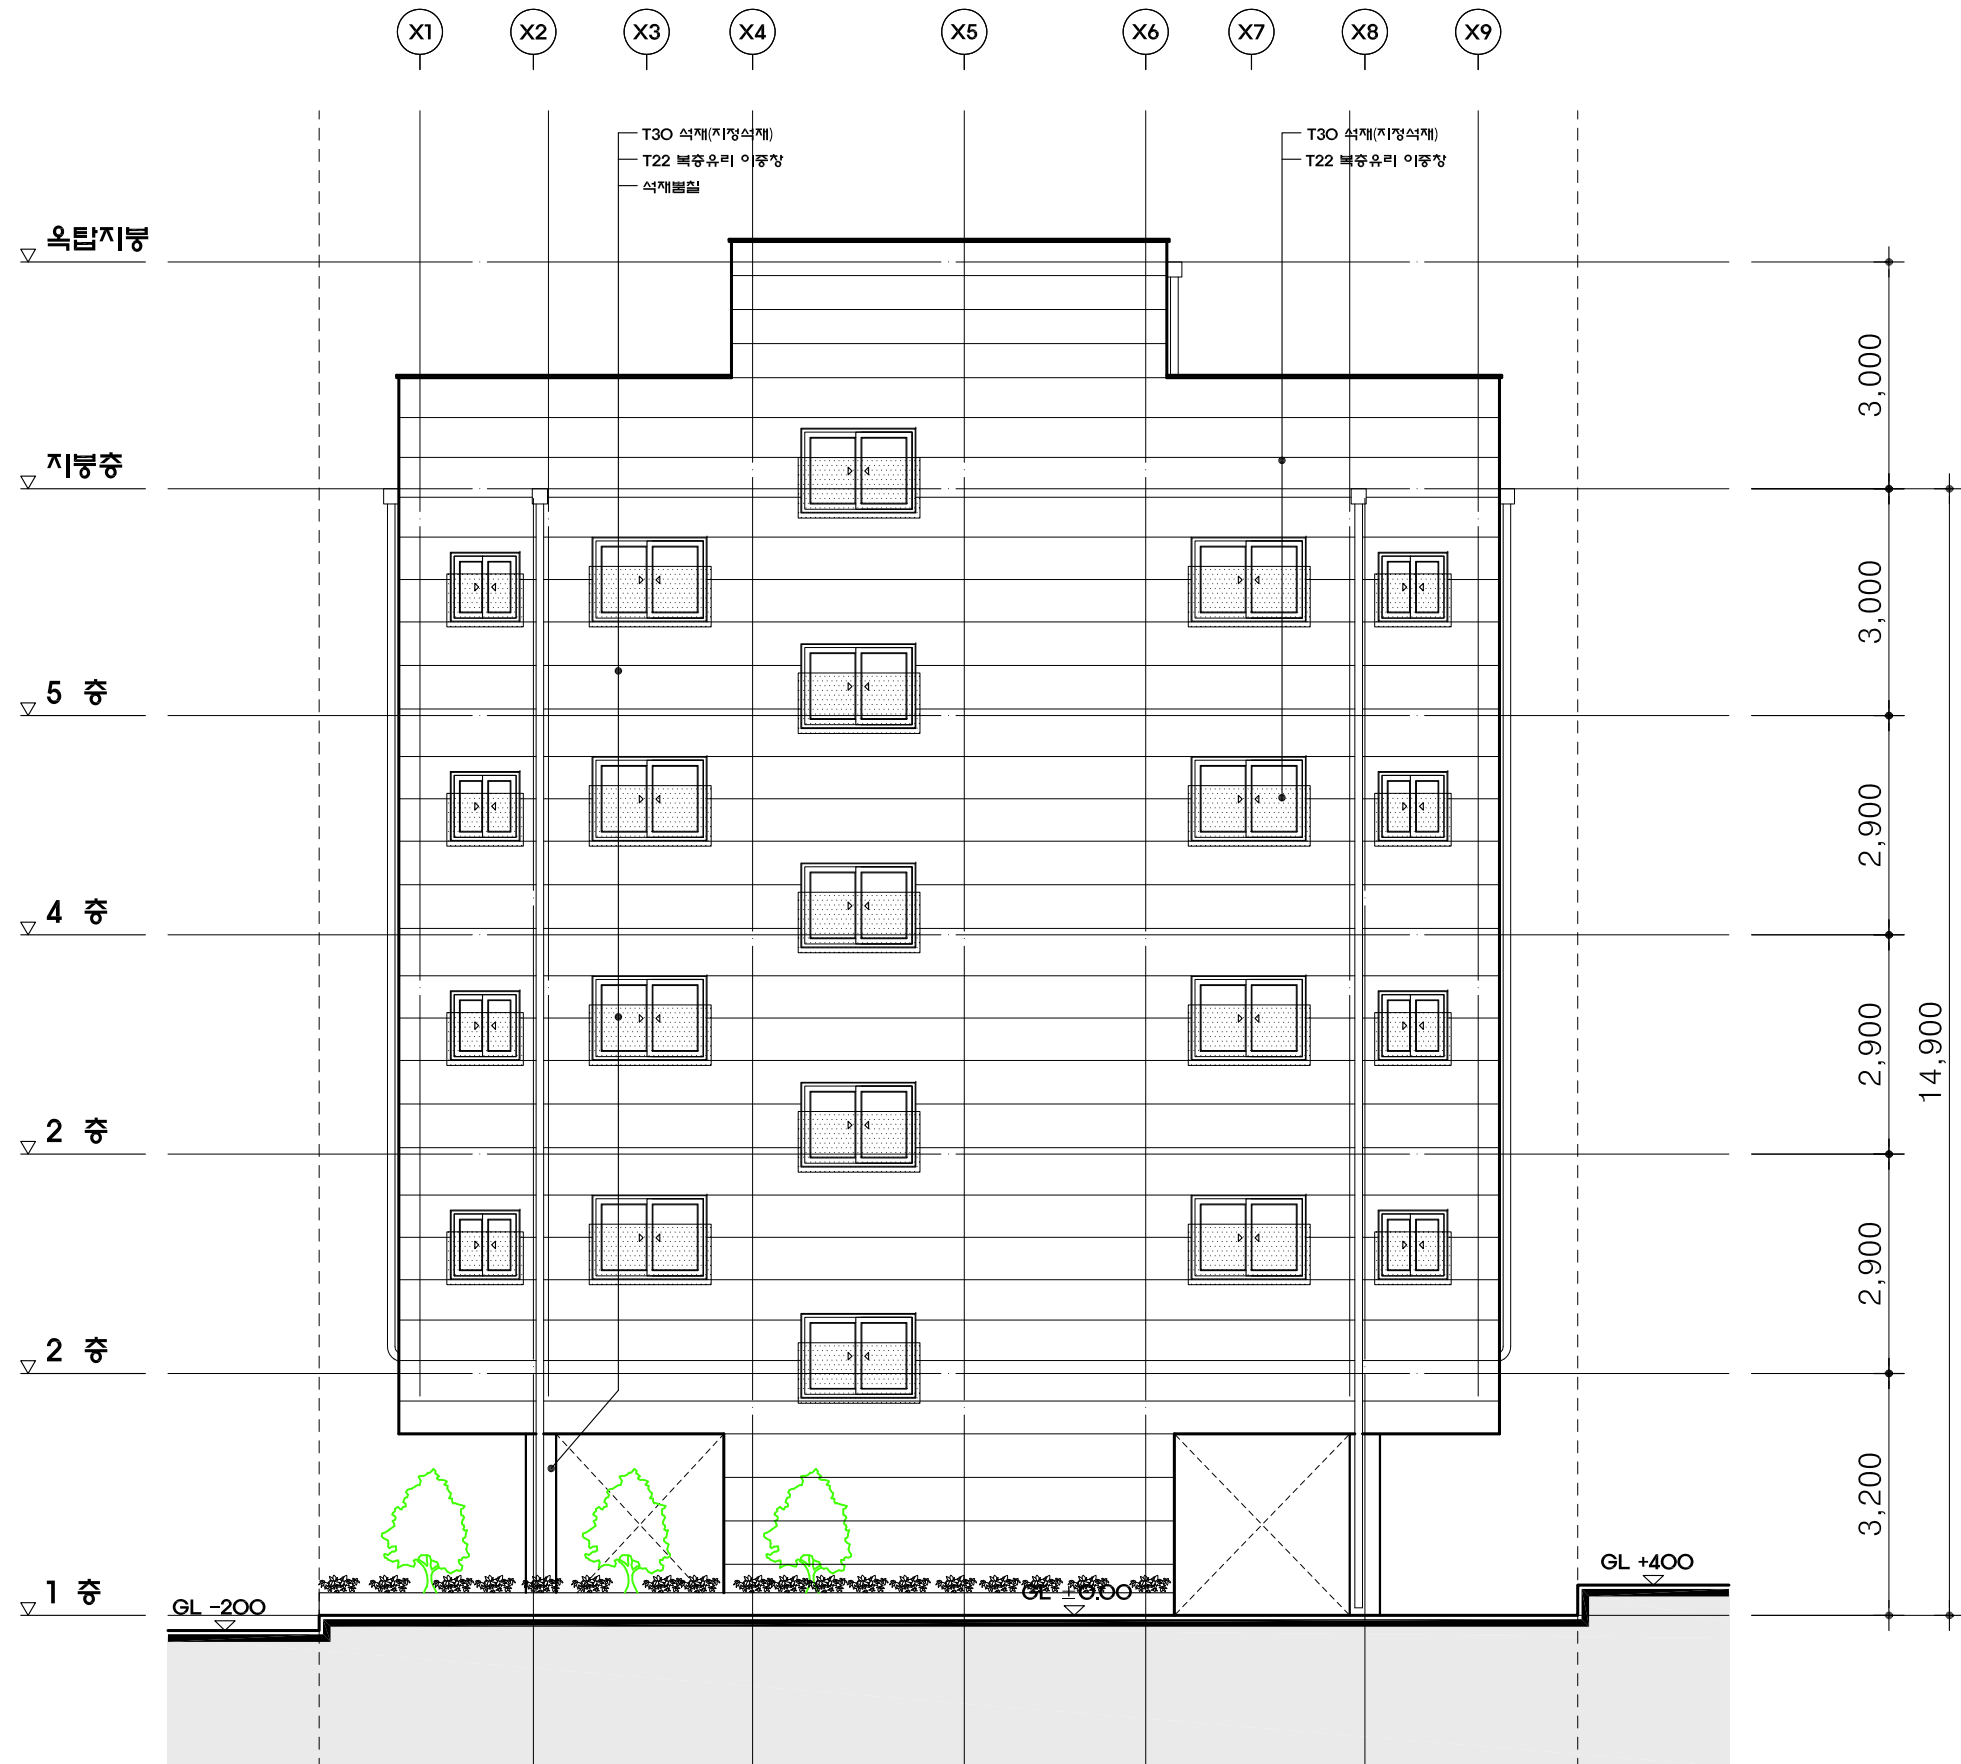

배 면 도
SCALE:1/100

NOTE:

PROJECT 은평구 길연동 406-32번지 도시형 생활 주택
단지형 다세대주택 신축공사 (청년주택)



APPROVED BY 건축사

UNK (주)유엔케이 건축사무소
Planners, Architects, Engineers, Consultants
서울특별시 서초구 미망로6길 29, 영성빌딩 4층
TEL : 070-7774-3988, FAX : 070-7966-3903
010-4422-4121

TITLE 배 면 도

날짜 DATE: 2026. 02

SCALE 1 / 100 DWG NO. A - 040 REV.

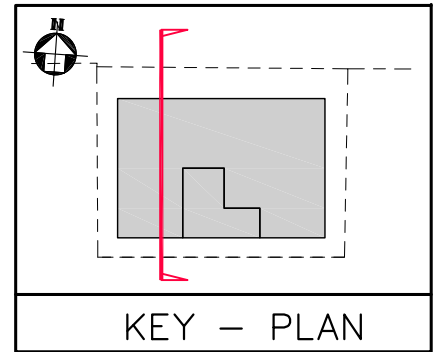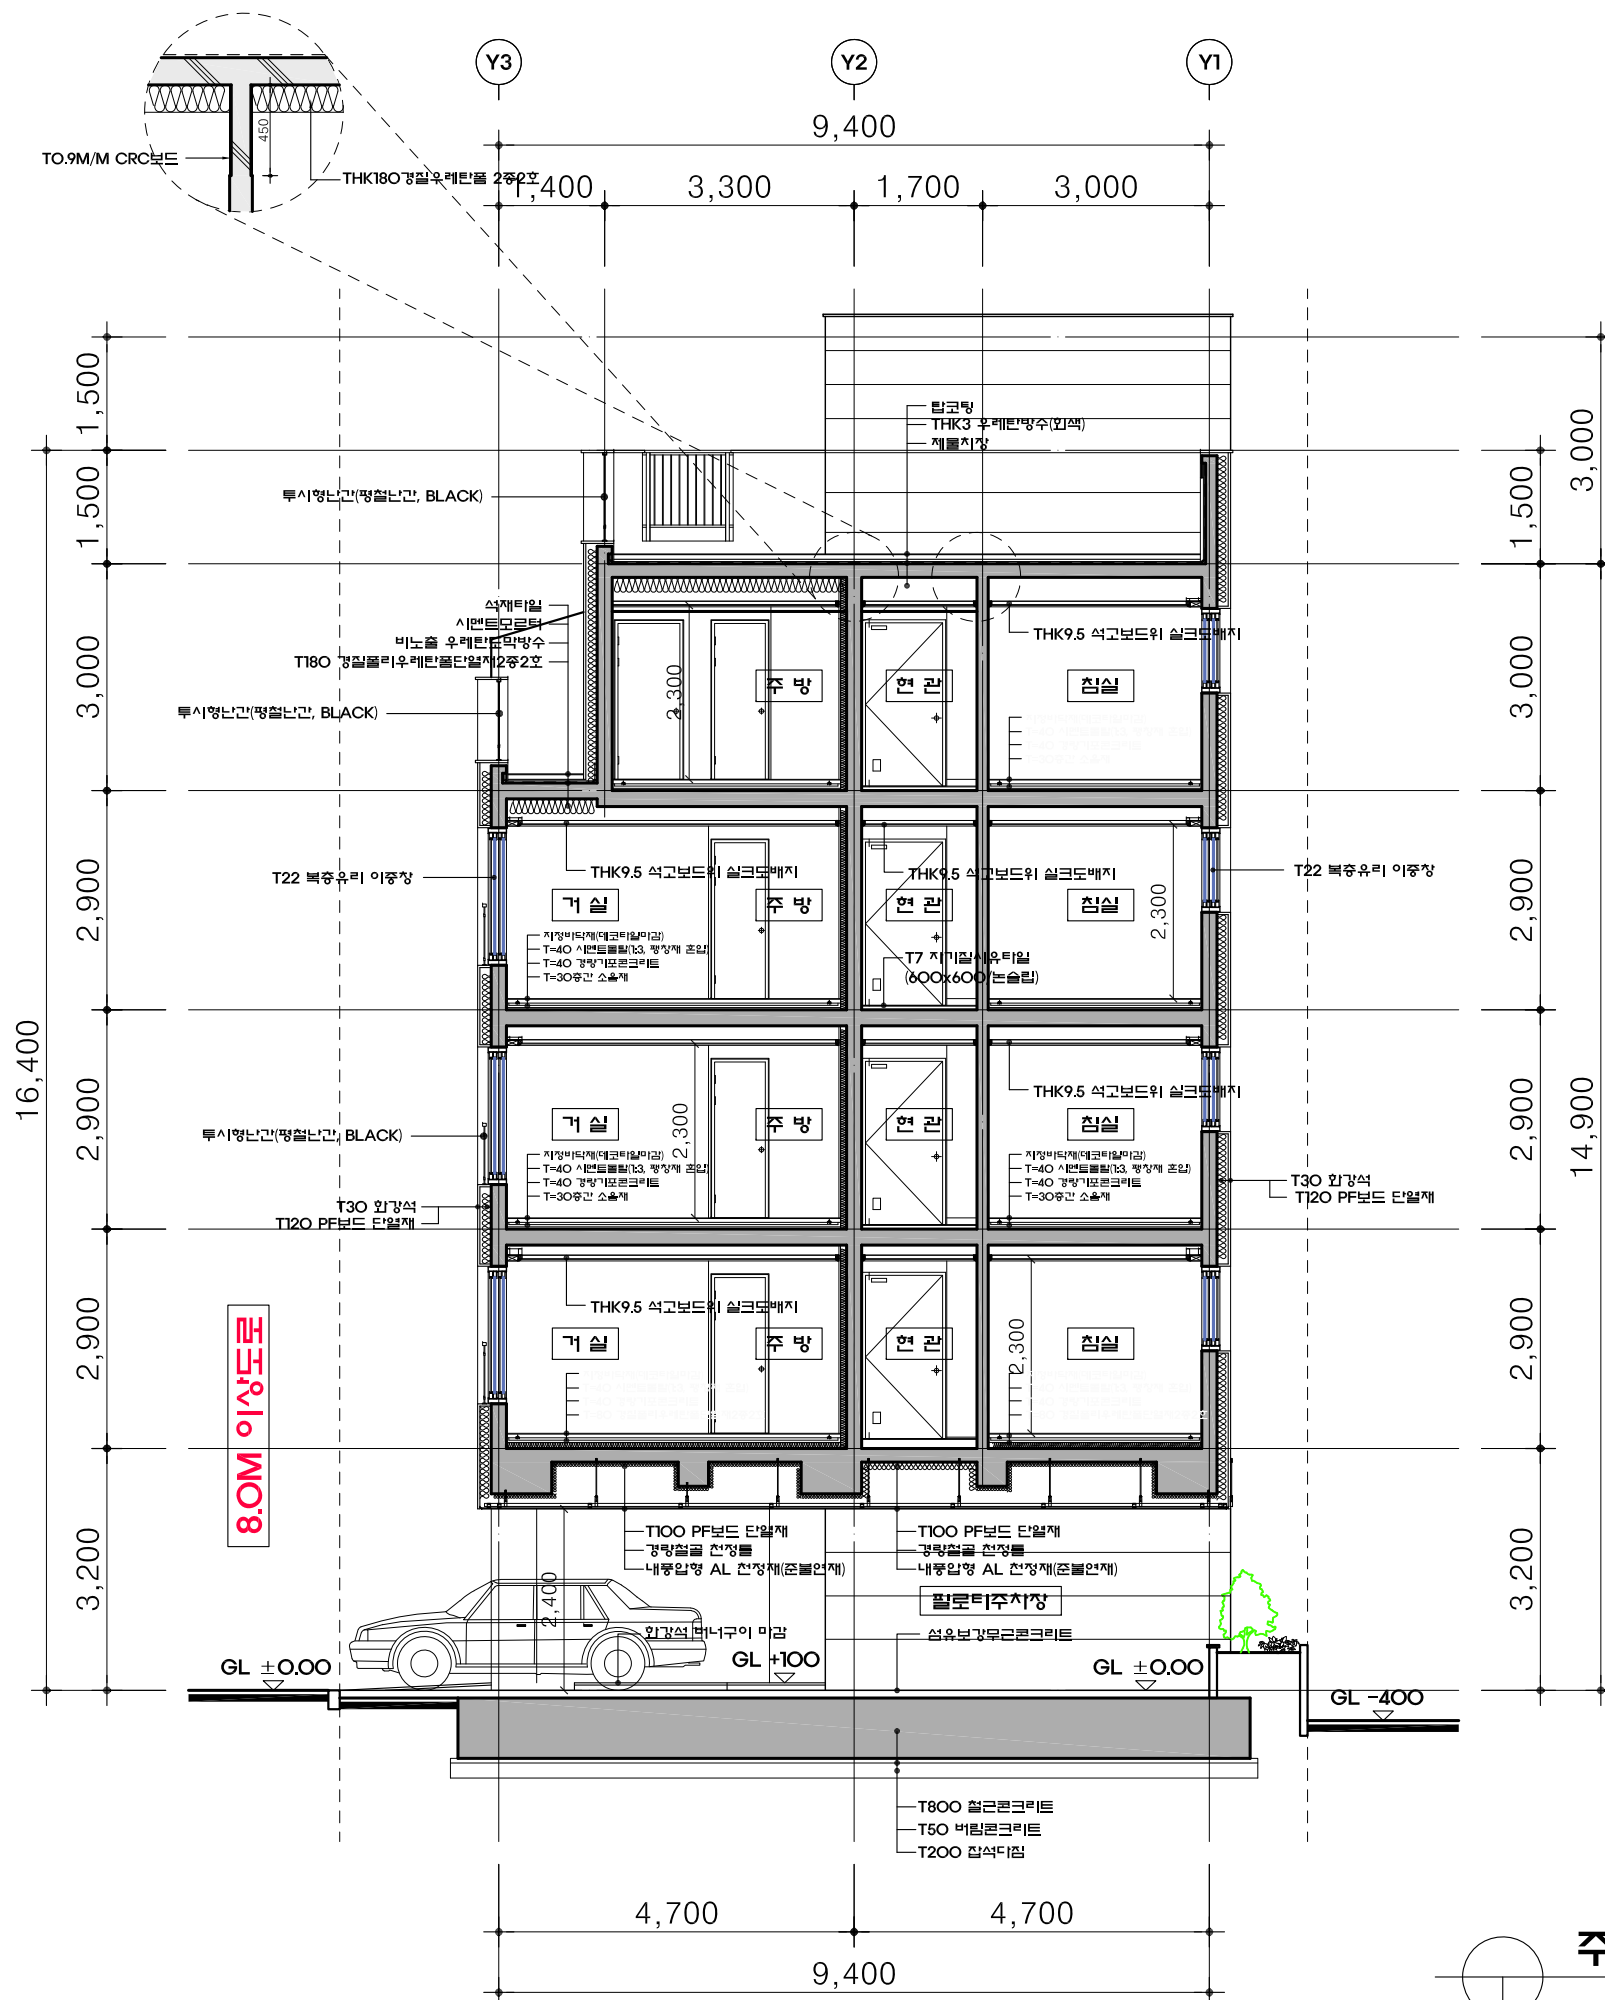

주 단 면 도

SCALE:1/100

NOTE:

PROJECT 은평구 길연동 406-32번지 도시형 생활 주택
단지형 다세대주택 신축공사 (정년주택)


APPROVED BY 건축사

LINK (주)유엔케이 건축사무소
Planners, Architects, Engineers, Consultants
서울특별시 서초구 미림로6길 29, 영성빌딩 4층
TEL : 070-7774-3988, FAX : 070-7966-3903
010-4422-4121

TITLE 주 단 면 도

날짜 DATE: 2026. 02

SCALE 1/100 DWG NO. A - 041 REV.

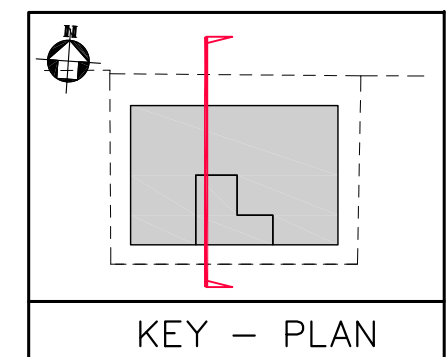

SCALE	1 / 100	DWG NO.	A - 042	REV.
-------	---------	---------	---------	------

SCALE:1/100