
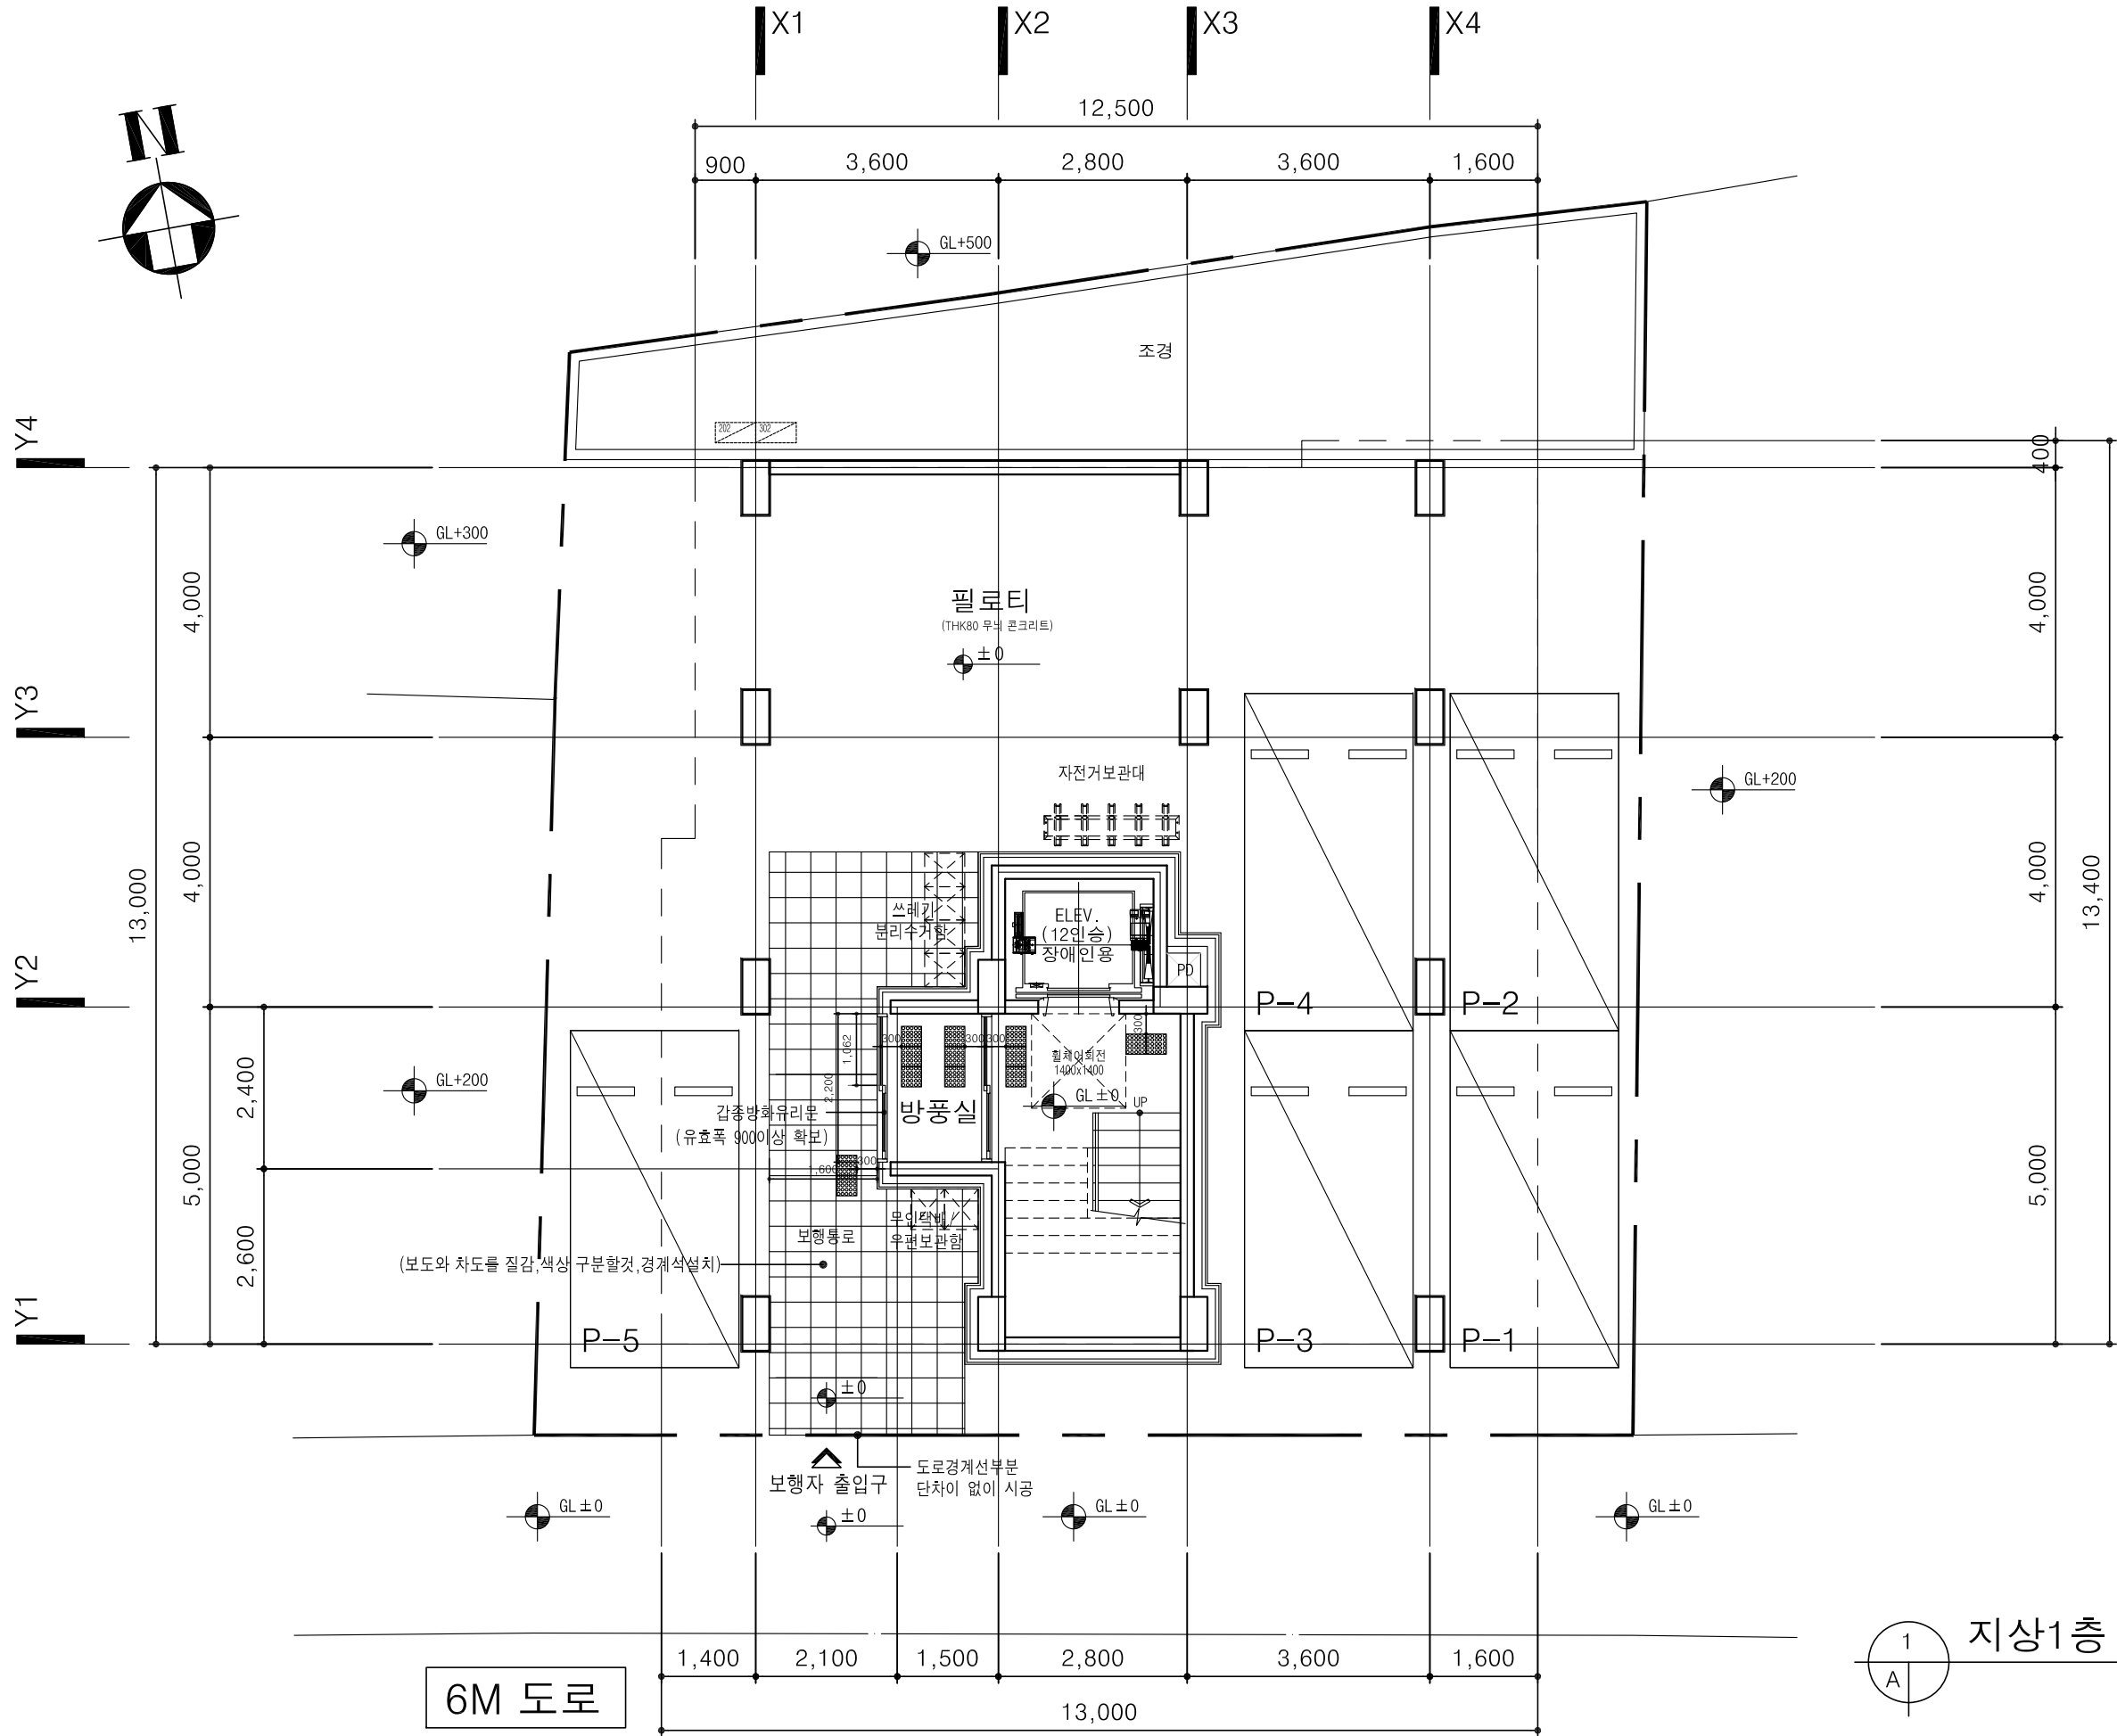


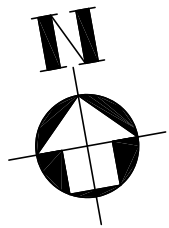

1 지상1층 평면도
축척 : 1 / 100

PROJECT TITLE
사업명칭

은평구 응암동
579-14호
도시형생활주택
신축공사

NAME OF DRAWING
도면명

지상1층 평면도

NOTE
주 기

- 단독경보감지기(연기식)
- 단독경보감지기(열감지)
- ABC분말소화기(2.5KG)
- 가스누설경보기
- 차면시설
- 보일러
- 에어컨 실외기

NO. REVISIONS DATE
번호 수정 일자

DESIGNED BY
설 계

CHECKED BY
심 사

APPROVED BY
승 인

CONSULTANTS
합 동 설 계



SCALE
축 척 A3 : 1 / 100

DATE
일 자 2023. 06.

SHEET NO.
일련 번호

OWG NO.
도면 번호 A-010

sig.A
(주)건축사사무소 시그에이
THE ARCHITECTS GROUP
TEL. 02.541.5516
FAX. 02.512.2882

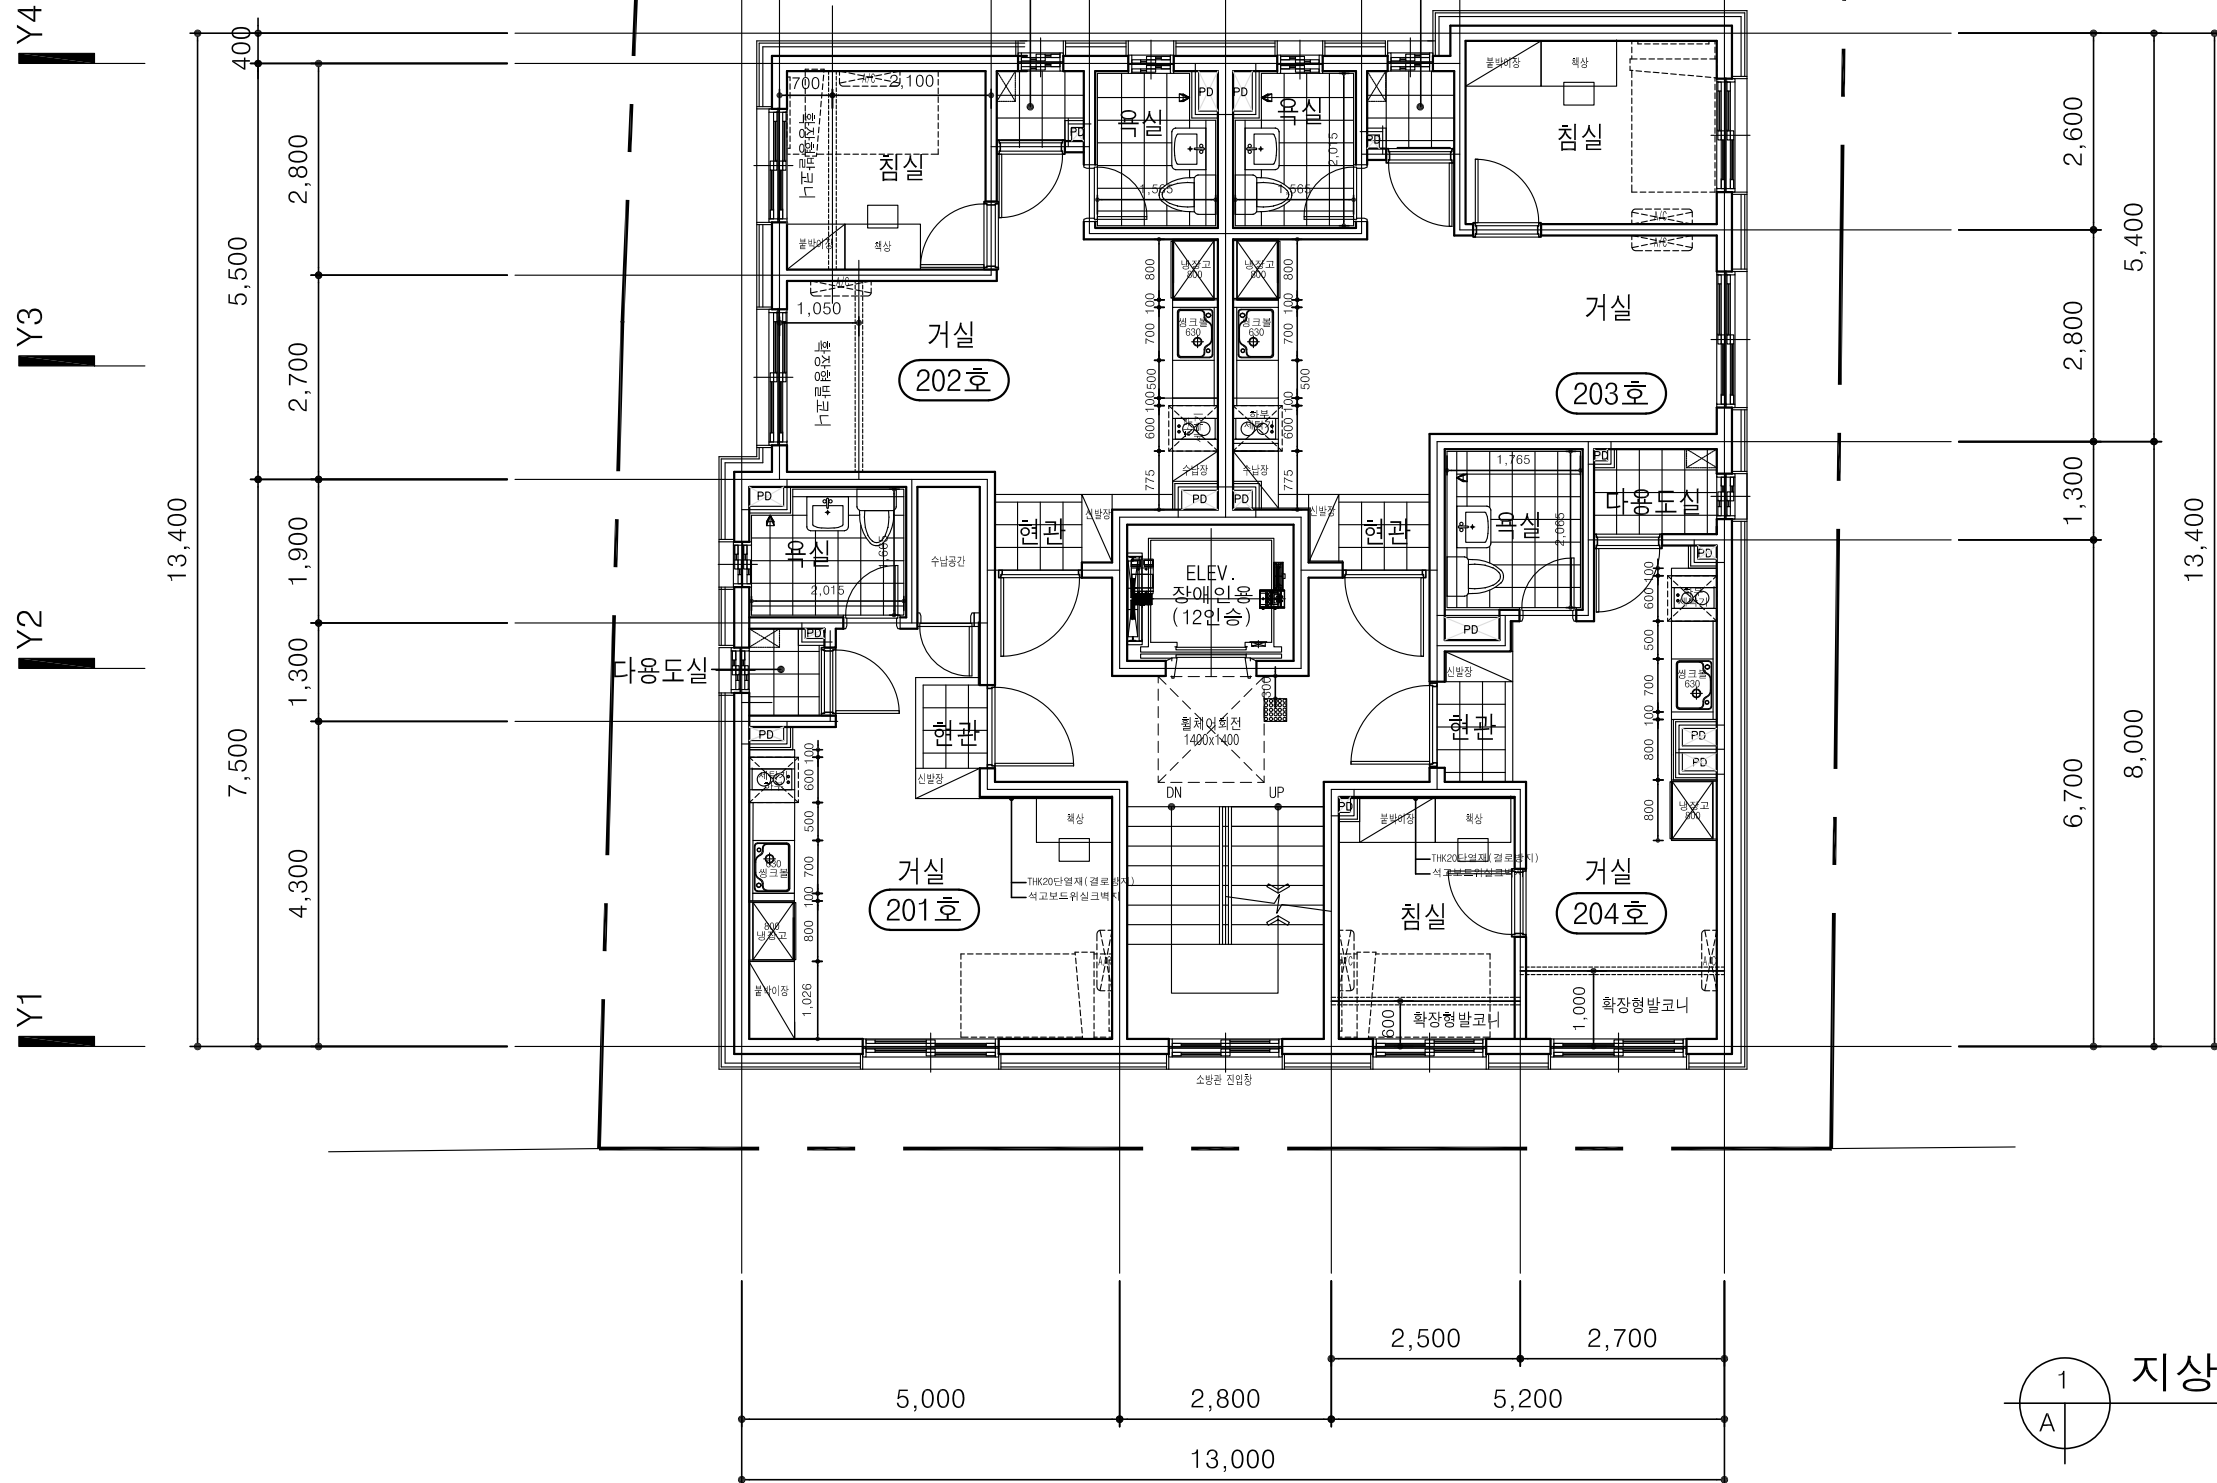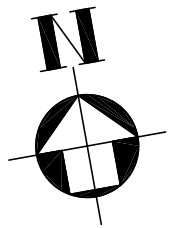

* 방풍실이 적용된 간접외기에 면한 실내벽면 :
결로방지 단열재20T + 석고보드 + 실크벽지
* 201,301호수납공간문은갤러리목문적용

PROJECT TITLE
사업명칭

은평구 응암동
579-14호
도시형생활주택
신축공사

NAME OF DRAWING
도면명

지상2층 평면도

NOTE
주 기

단독경보감지기(연기식)

단독경보감지기(열감지)

ABC분말소화기(2.5KG)

가스누설경보기

차면시설

보일러

에어컨 실외기

NO.
번호

REVISIONS
수정

DATE
일자

DESIGNED BY
설계

CHECKED BY
심사

APPROVED BY
승인

CONSULTANTS
합동설계

SCALE
축척

A3 : 1 / 100

DATE
일자

2023. 06.

SHEET NO.
절대 번호

1


DWG NO.
도면 번호

A-011



sig.A

(주)건축사사무소 시그에이

THE ARCHITECTS GROUP
TEL. 02.541.5516
FAX. 02.512.2882

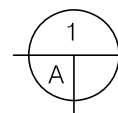

지상2층 평면도
축척 : 1 / 100

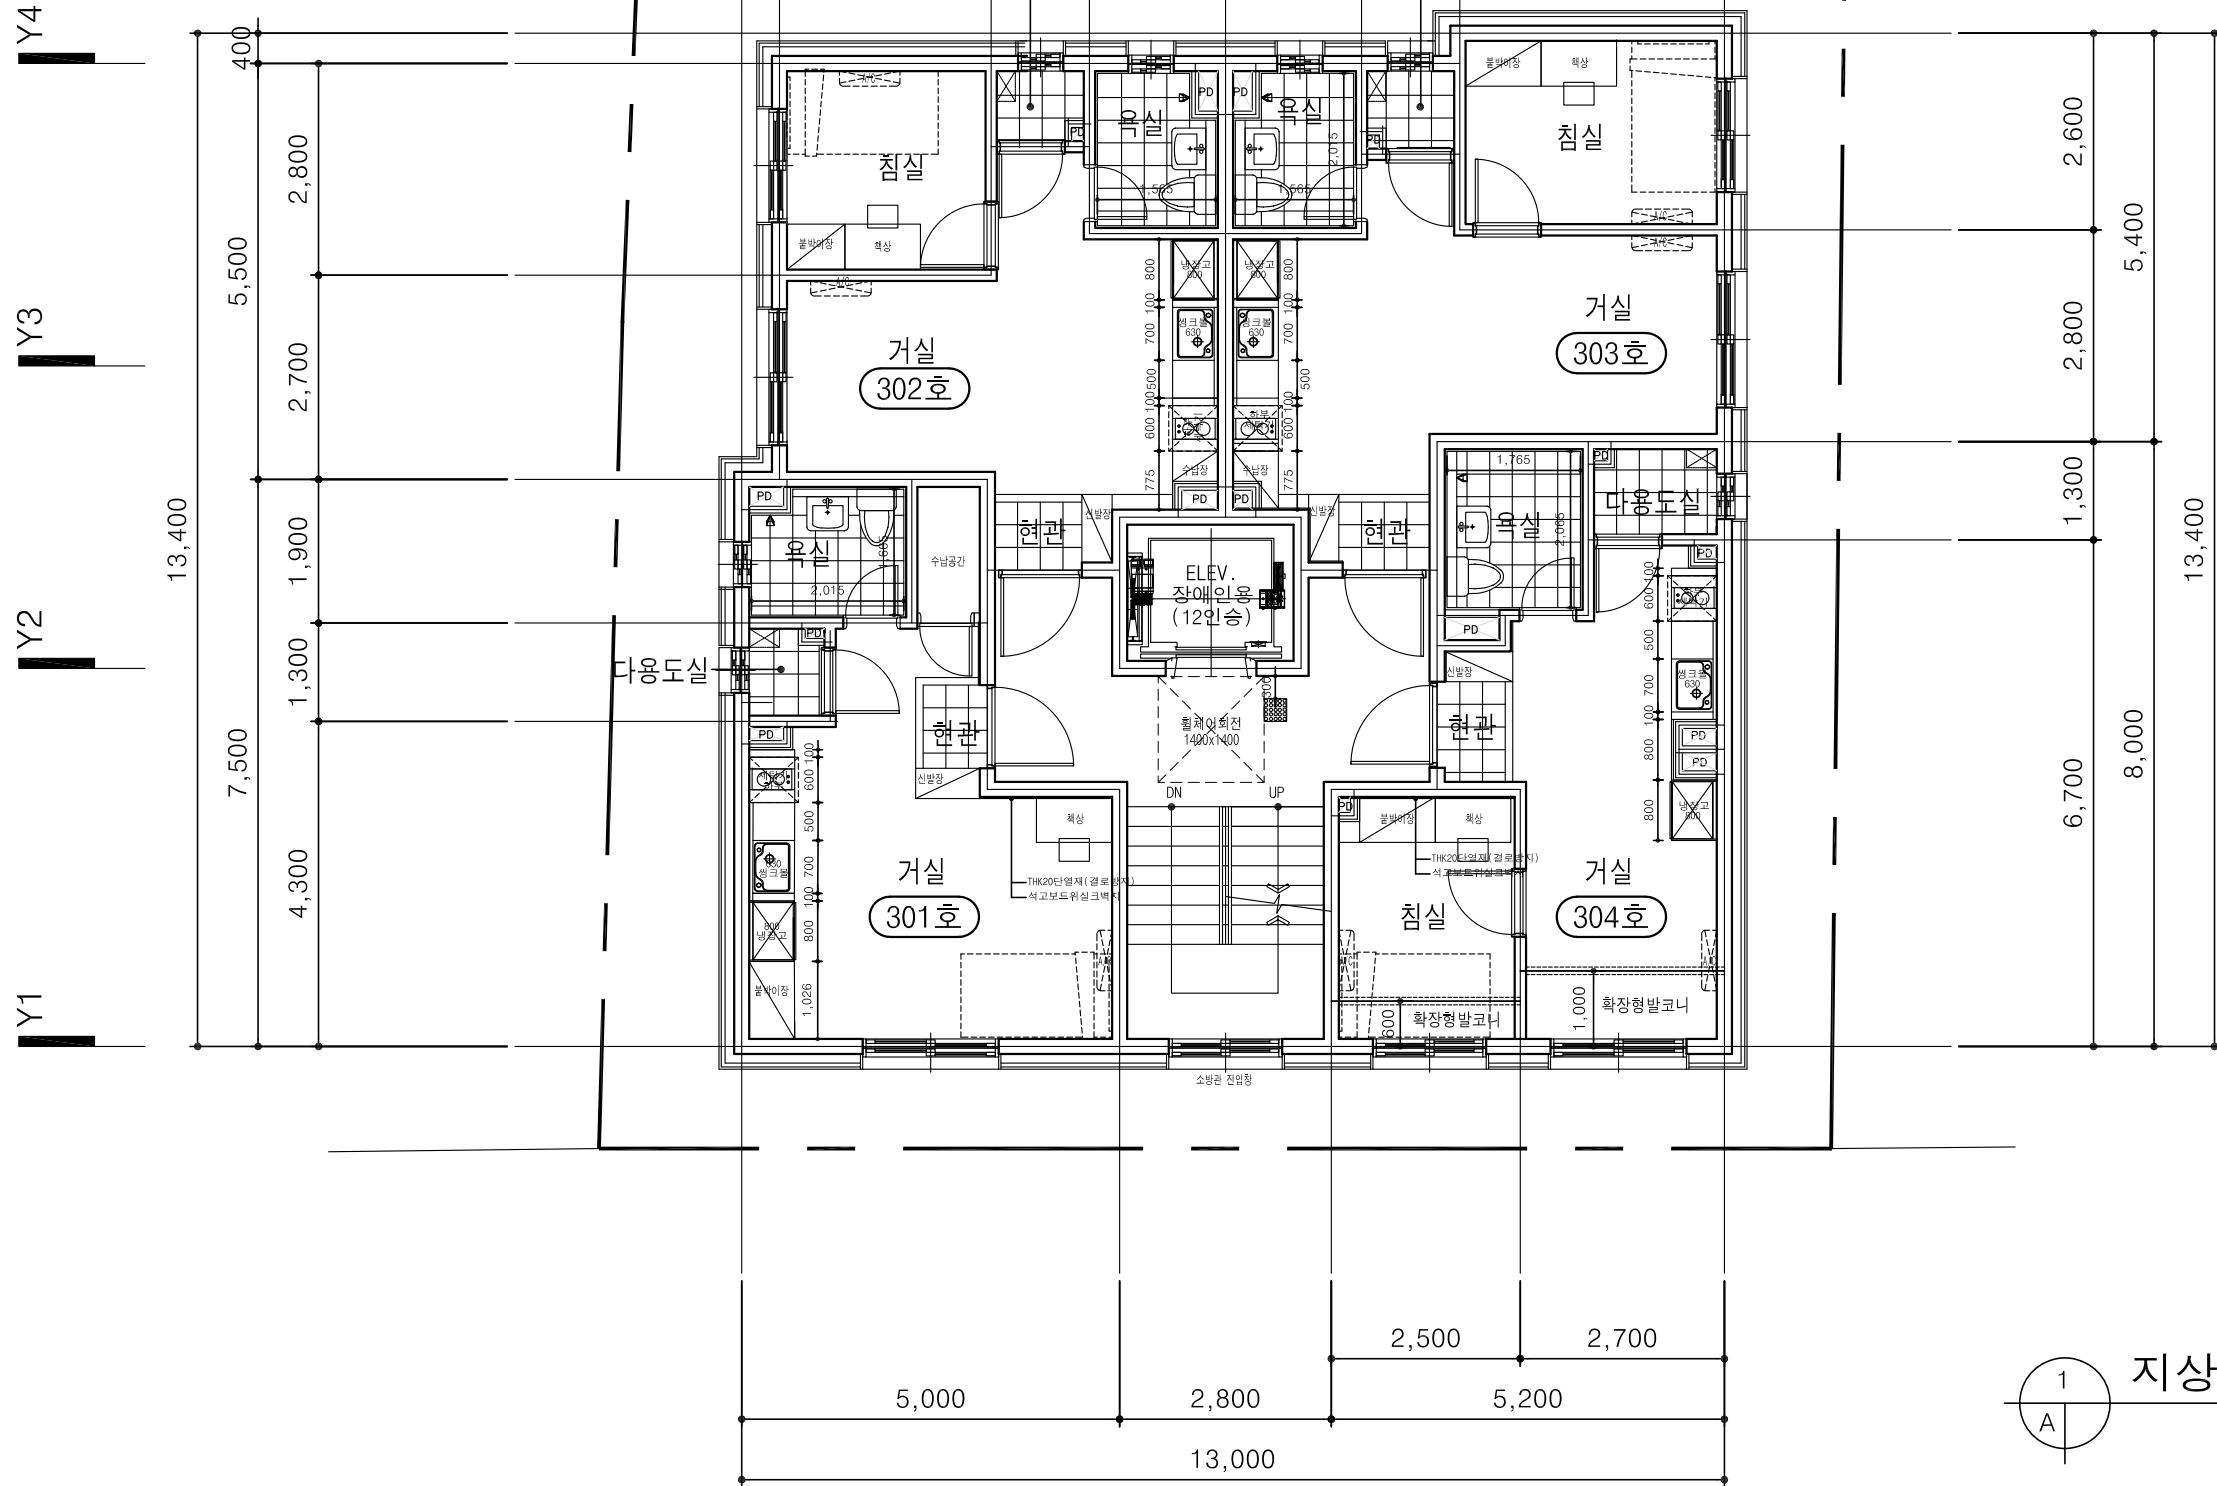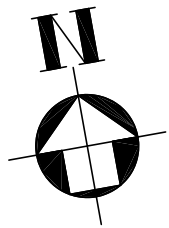

* 방풍실이 적용된 간접외기에 면한 실내벽면 :
결로방지 단열재20T + 석고보드 + 실크벽지
* 201,301호수납공간문은갤러리목문적용

PROJECT TITLE
사업명칭

은평구 응암동
579-14호
도시형생활주택
신축공사

NAME OF DRAWING
도면명

지상3층 평면도

NOTE
주 기

단독경보감지기(연기식)

단독경보감지기(열감지)

ABC분말소화기(2.5KG)

가스누설경보기

차면시설

보일러

에어컨 실외기

NO.
번호

▲ REVISIONS
수 정

▲ DATE
일 자

DESIGNED BY
설 계

CHECKED BY
심 사

APPROVED BY
승 인

CONSULTANTS
합 동 설 계

SCALE
축 척

A3 : 1 / 100

DATE
일 자

2023. 06.

SHEET NO.
일련 번호


OWG NO.
도면 번호

A-012



sig.A

(주)건축사사무소 시그에이

THE ARCHITECTS GROUP
TEL. 02.541.5516
FAX. 02.512.2882

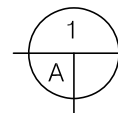

지상3층 평면도
축척 : 1 / 100

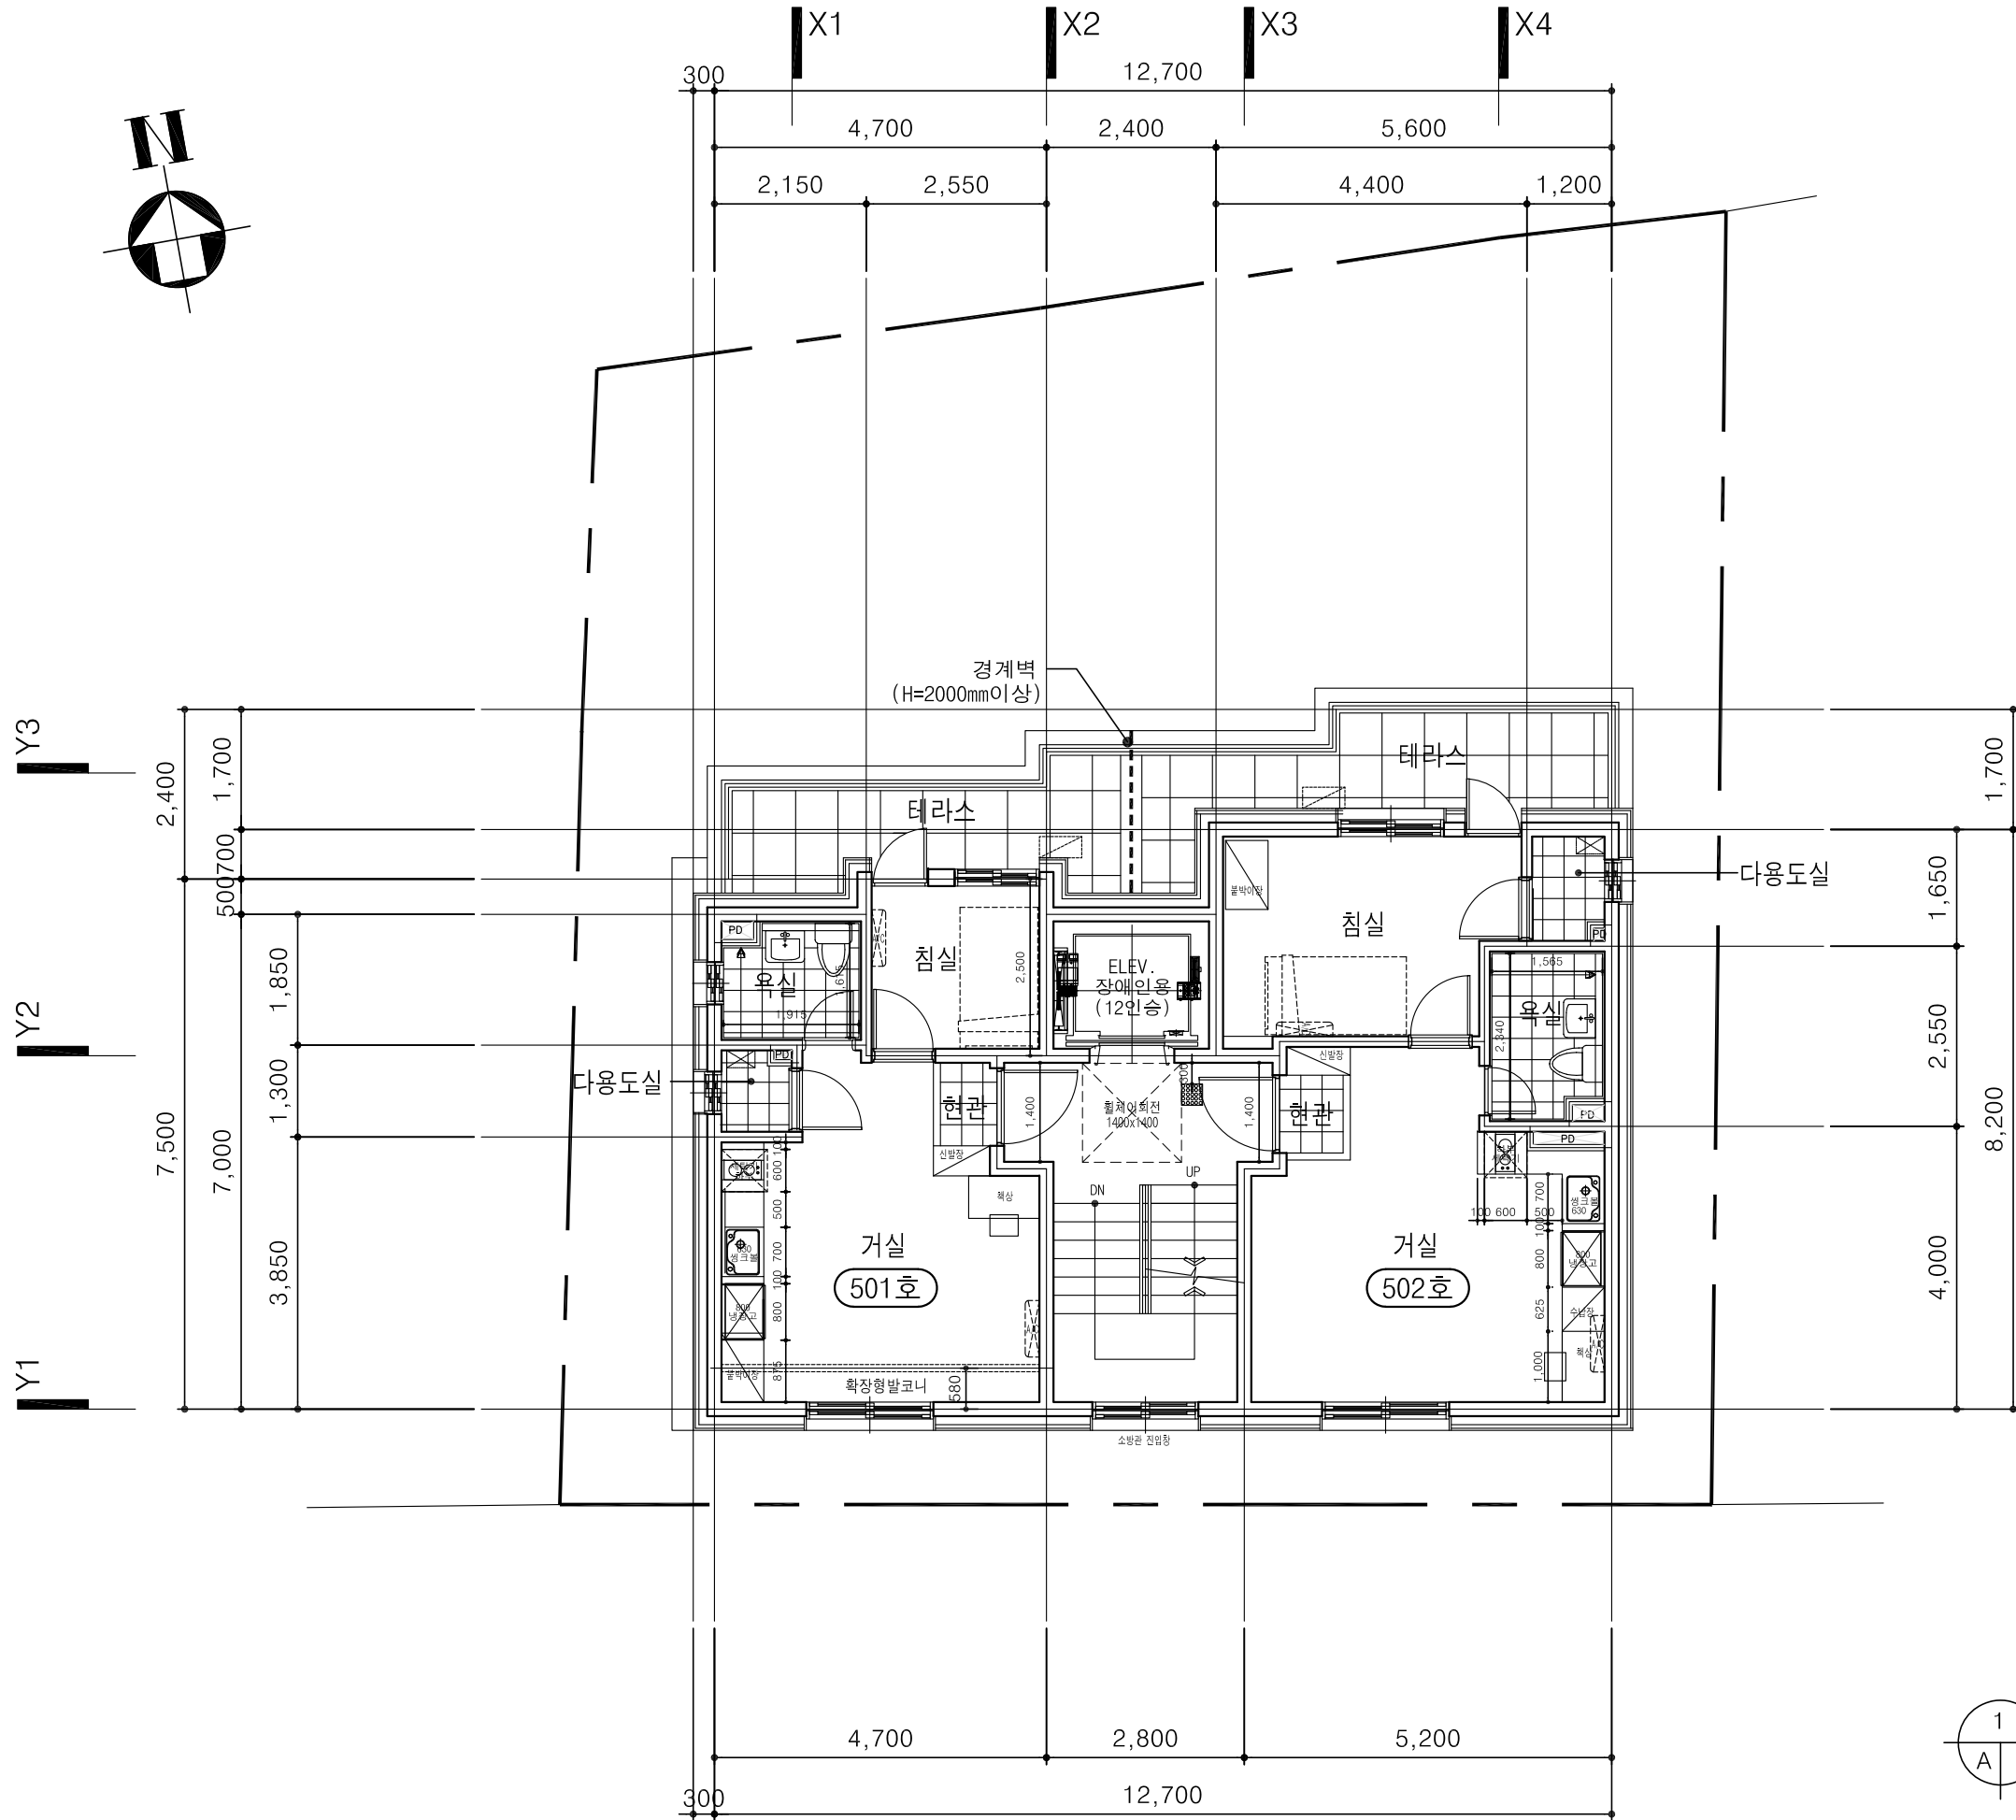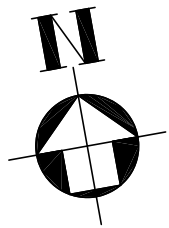

* 방풍실이 적용된 간접외기에 의한 실내벽면 :
결로방지 단열재20T + 석고보드 + 실크벽지

지상5층 평면도
축척 : 1 / 100

PROJECT TITLE
사업명칭

은평구 응암동
579-14호
도시형생활주택
신축공사

NAME OF DRAWING
도면명

지상5층 평면도

NOTE
주 기

단독경보감지기(연기식)

단독경보감지기(열감지)

ABC분말소화기(2.5KG)

가스누설경보기

차면시설

보일러

에어컨 실외기

NO. REVISIONS DATE
번호 수정 일자

DESIGNED BY
설 계

CHECKED BY
심 사

APPROVED BY
승 인

CONSULTANTS
합 동 설 계

SCALE
축 척

A3 : 1 / 100

DATE
일 자

2023. 06.

SHEET NO.
일련 번호


DWG NO.
도면 번호

A-014

sig.A

(주)건축사사무소 시그에이



THE ARCHITECTS GROUP
TEL. 02.541.5516
FAX. 02.512.2882

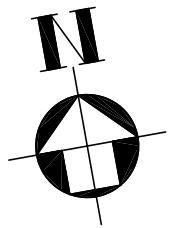

Y3


Y2

Y1

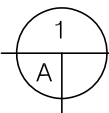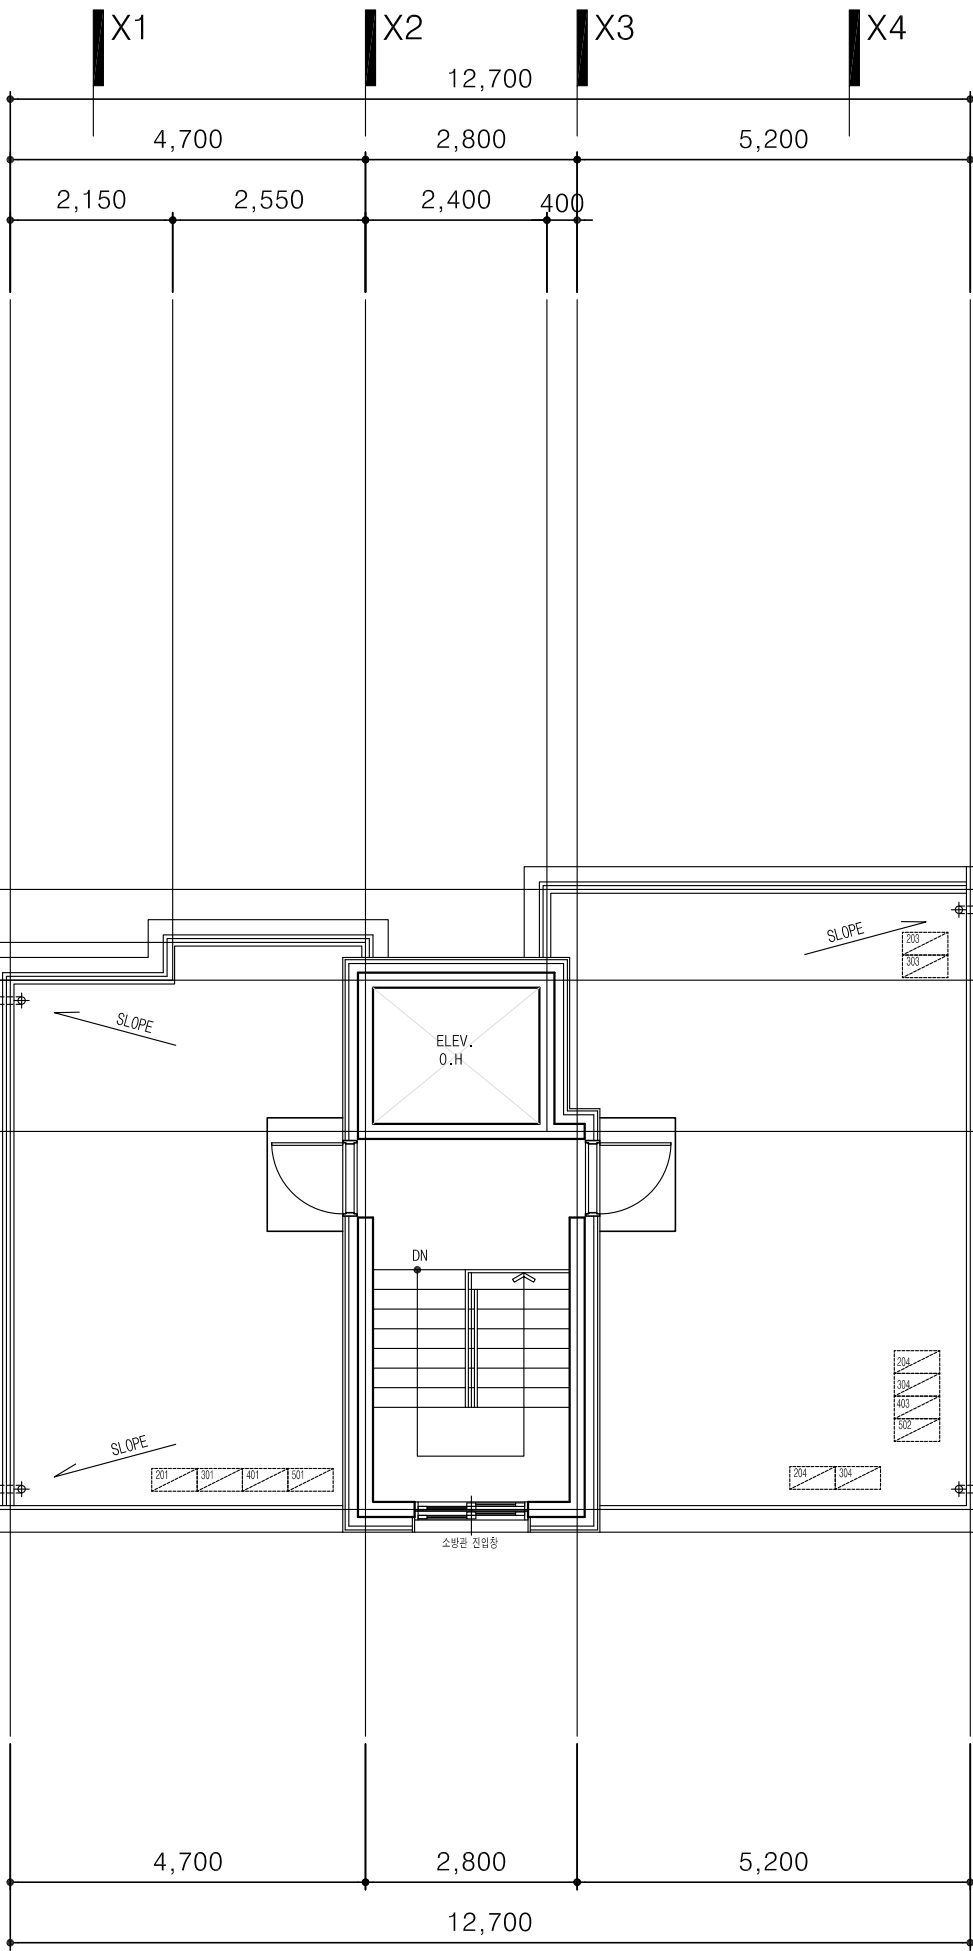

지붕 평면도

축척 : 1 / 100

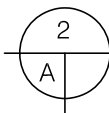

옥탑 지붕 평면도

축척 : 1 / 100

PROJECT TITLE
사업명칭

은평구 응암동
579-14호
도시형생활주택
신축공사

NAME OF DRAWING
도면명

지붕 평면도 / 옥탑 지붕 평면도

NOTE
주 기

- 단독경보감지기(연기식)
- 단독경보감지기(열감지)
- ABC분말소화기(2.5KG)
- 가스누설경보기
- 차면시설
- 보일러
- 에어컨 실외기

NO. ▲ REVISIONS ▲ DATE
번호 수정 일자

DESIGNED BY
설 계

CHECKED BY
심 사

APPROVED BY
승 인

CONSULTANTS
합 동 설 계


SCALE
축 척 A3 : 1 / 100

DATE
일 자 2023. 06.

SHEET NO.
일련 번호

DWG NO.
도면 번호 A-015

sig.A
(주)건축사사무소 시그에이
THE ARCHITECTS GROUP
TEL. 02.541.5516
FAX. 02.512.2882

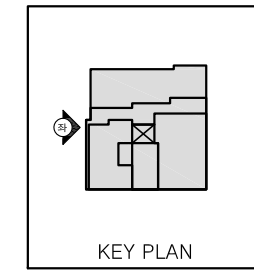

PROJECT TITLE
사업명칭

은평구 응암동
579-14호
도시형생활주택
신축공사

NAME OF DRAWING
도면명

좌측면도

NOTE
주 기

[illegible]

NO. 번호	▲	REVISIONS 수 정	▲	DATE 일 자
-----------	---	------------------	---	-------------

DESIGNED BY
설 계

CHECKED BY
심 사

APPROVED BY
승 인

CONSULTANTS
 顧問 設計



SCALE
축 척 A3 : 1 / 100

DATE
일 자 2023. 06.

SHEET NO.
일련 번호

DWG NO.
도면 번호

 sig.A
(주)건축사사무소 시그에이
THE ARCHITECTS GROUP
TEL. 02.541.5516
FAX. 02.512.2882

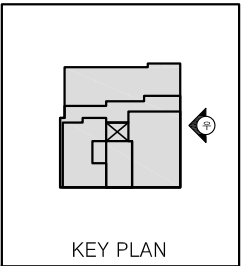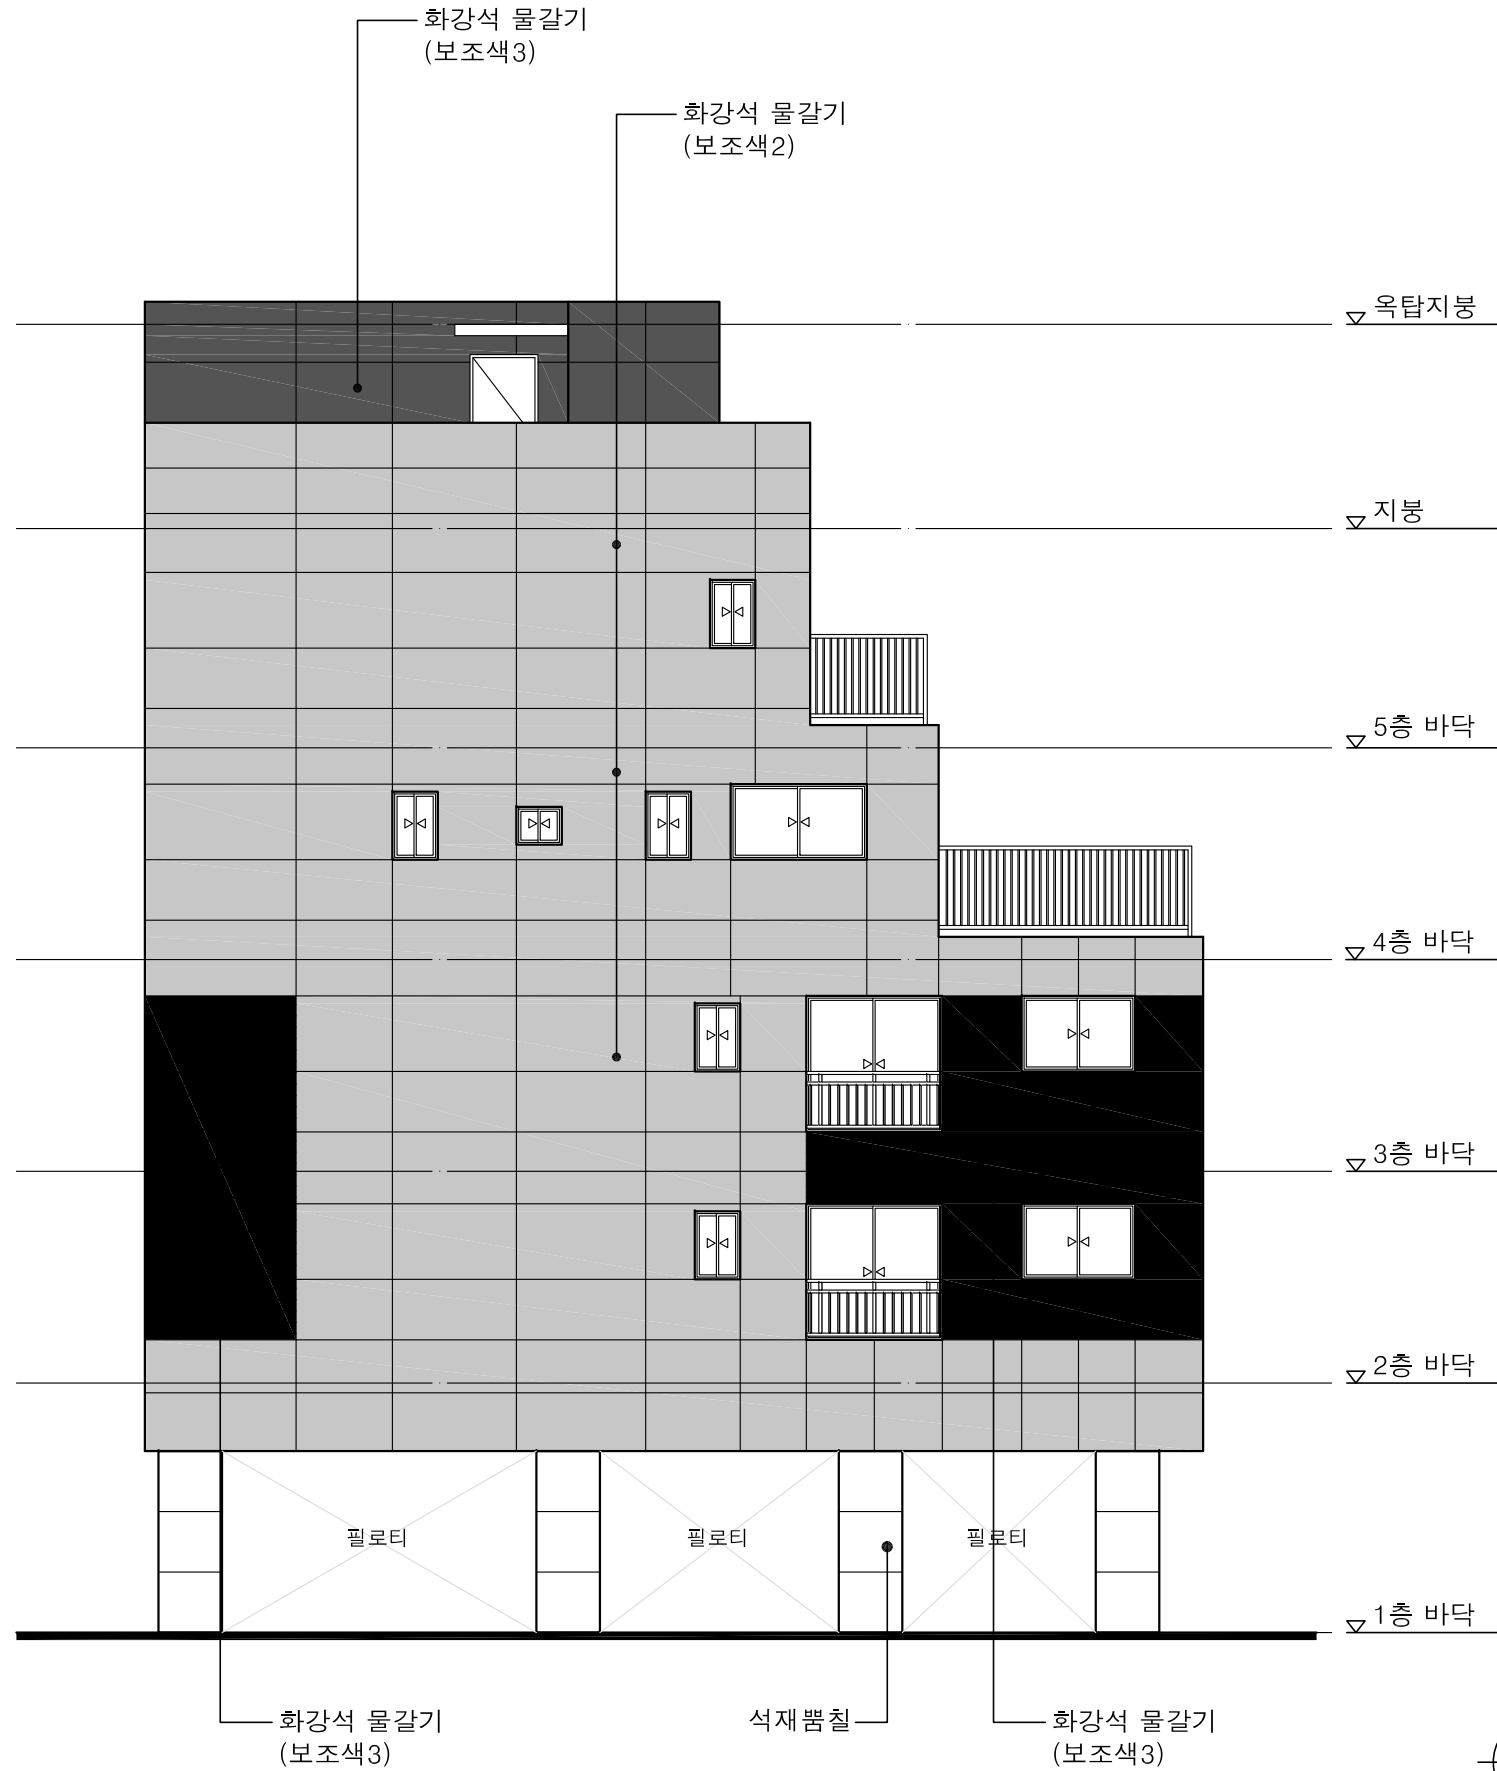

PROJECT TITLE
사업명칭

은평구 응암동
579-14호
도시형생활주택
신축공사

NAME OF DRAWING
도면명

우측면도

NOTE
주 기

▼ ▼

NO. ▲ REVISIONS ▲ DATE
번호 수정 일자

DESIGNED BY
설 계

CHECKED BY
심 사

APPROVED BY
승 인

CONSULTANTS
합 동 설 계

SCALE
축 척 A3 : 1 / 100

DATE
일 자 2023. 06.

SHEET NO.
일련 번호

DWG NO.
도면 번호 A-023

1
A 우측면도
축척 : 1 / 100

sig.A
(주)건축사사무소 시그에이
THE ARCHITECTS GROUP
TEL. 02.541.5516
FAX. 02.512.2882