

제로투엔  
건축사사무소

서울특별시 강남구 테헤란로 77길 13, 10층 (삼성동, 창조빌딩)  
T 02 6925 0745  
zero-to-n.com a@zero-to-n.com

project name

구산동 191-10 외7필지  
도시형생활주택 신축공사

revisions

| no. | date | note |
|-----|------|------|
|     |      |      |
|     |      |      |
|     |      |      |
|     |      |      |

note

title

외관디자인계획

scale

NONE

number

A0 - 03



제로투엔  
건축사사무소

서울특별시 강남구 테헤란로 77길 13, 10층 (삼성동, 청초빌딩)  
T 02 6925 0745  
zero-to-n.com a@zero-to-n.com

project name

구산동 191-10 외7필지  
도시형생활주택 신축공사

revisions

| no. | date | note |
|-----|------|------|
|     |      |      |
|     |      |      |
|     |      |      |
|     |      |      |

note

title


지하1층 평면도

scale

1/200

number

A3 - 01

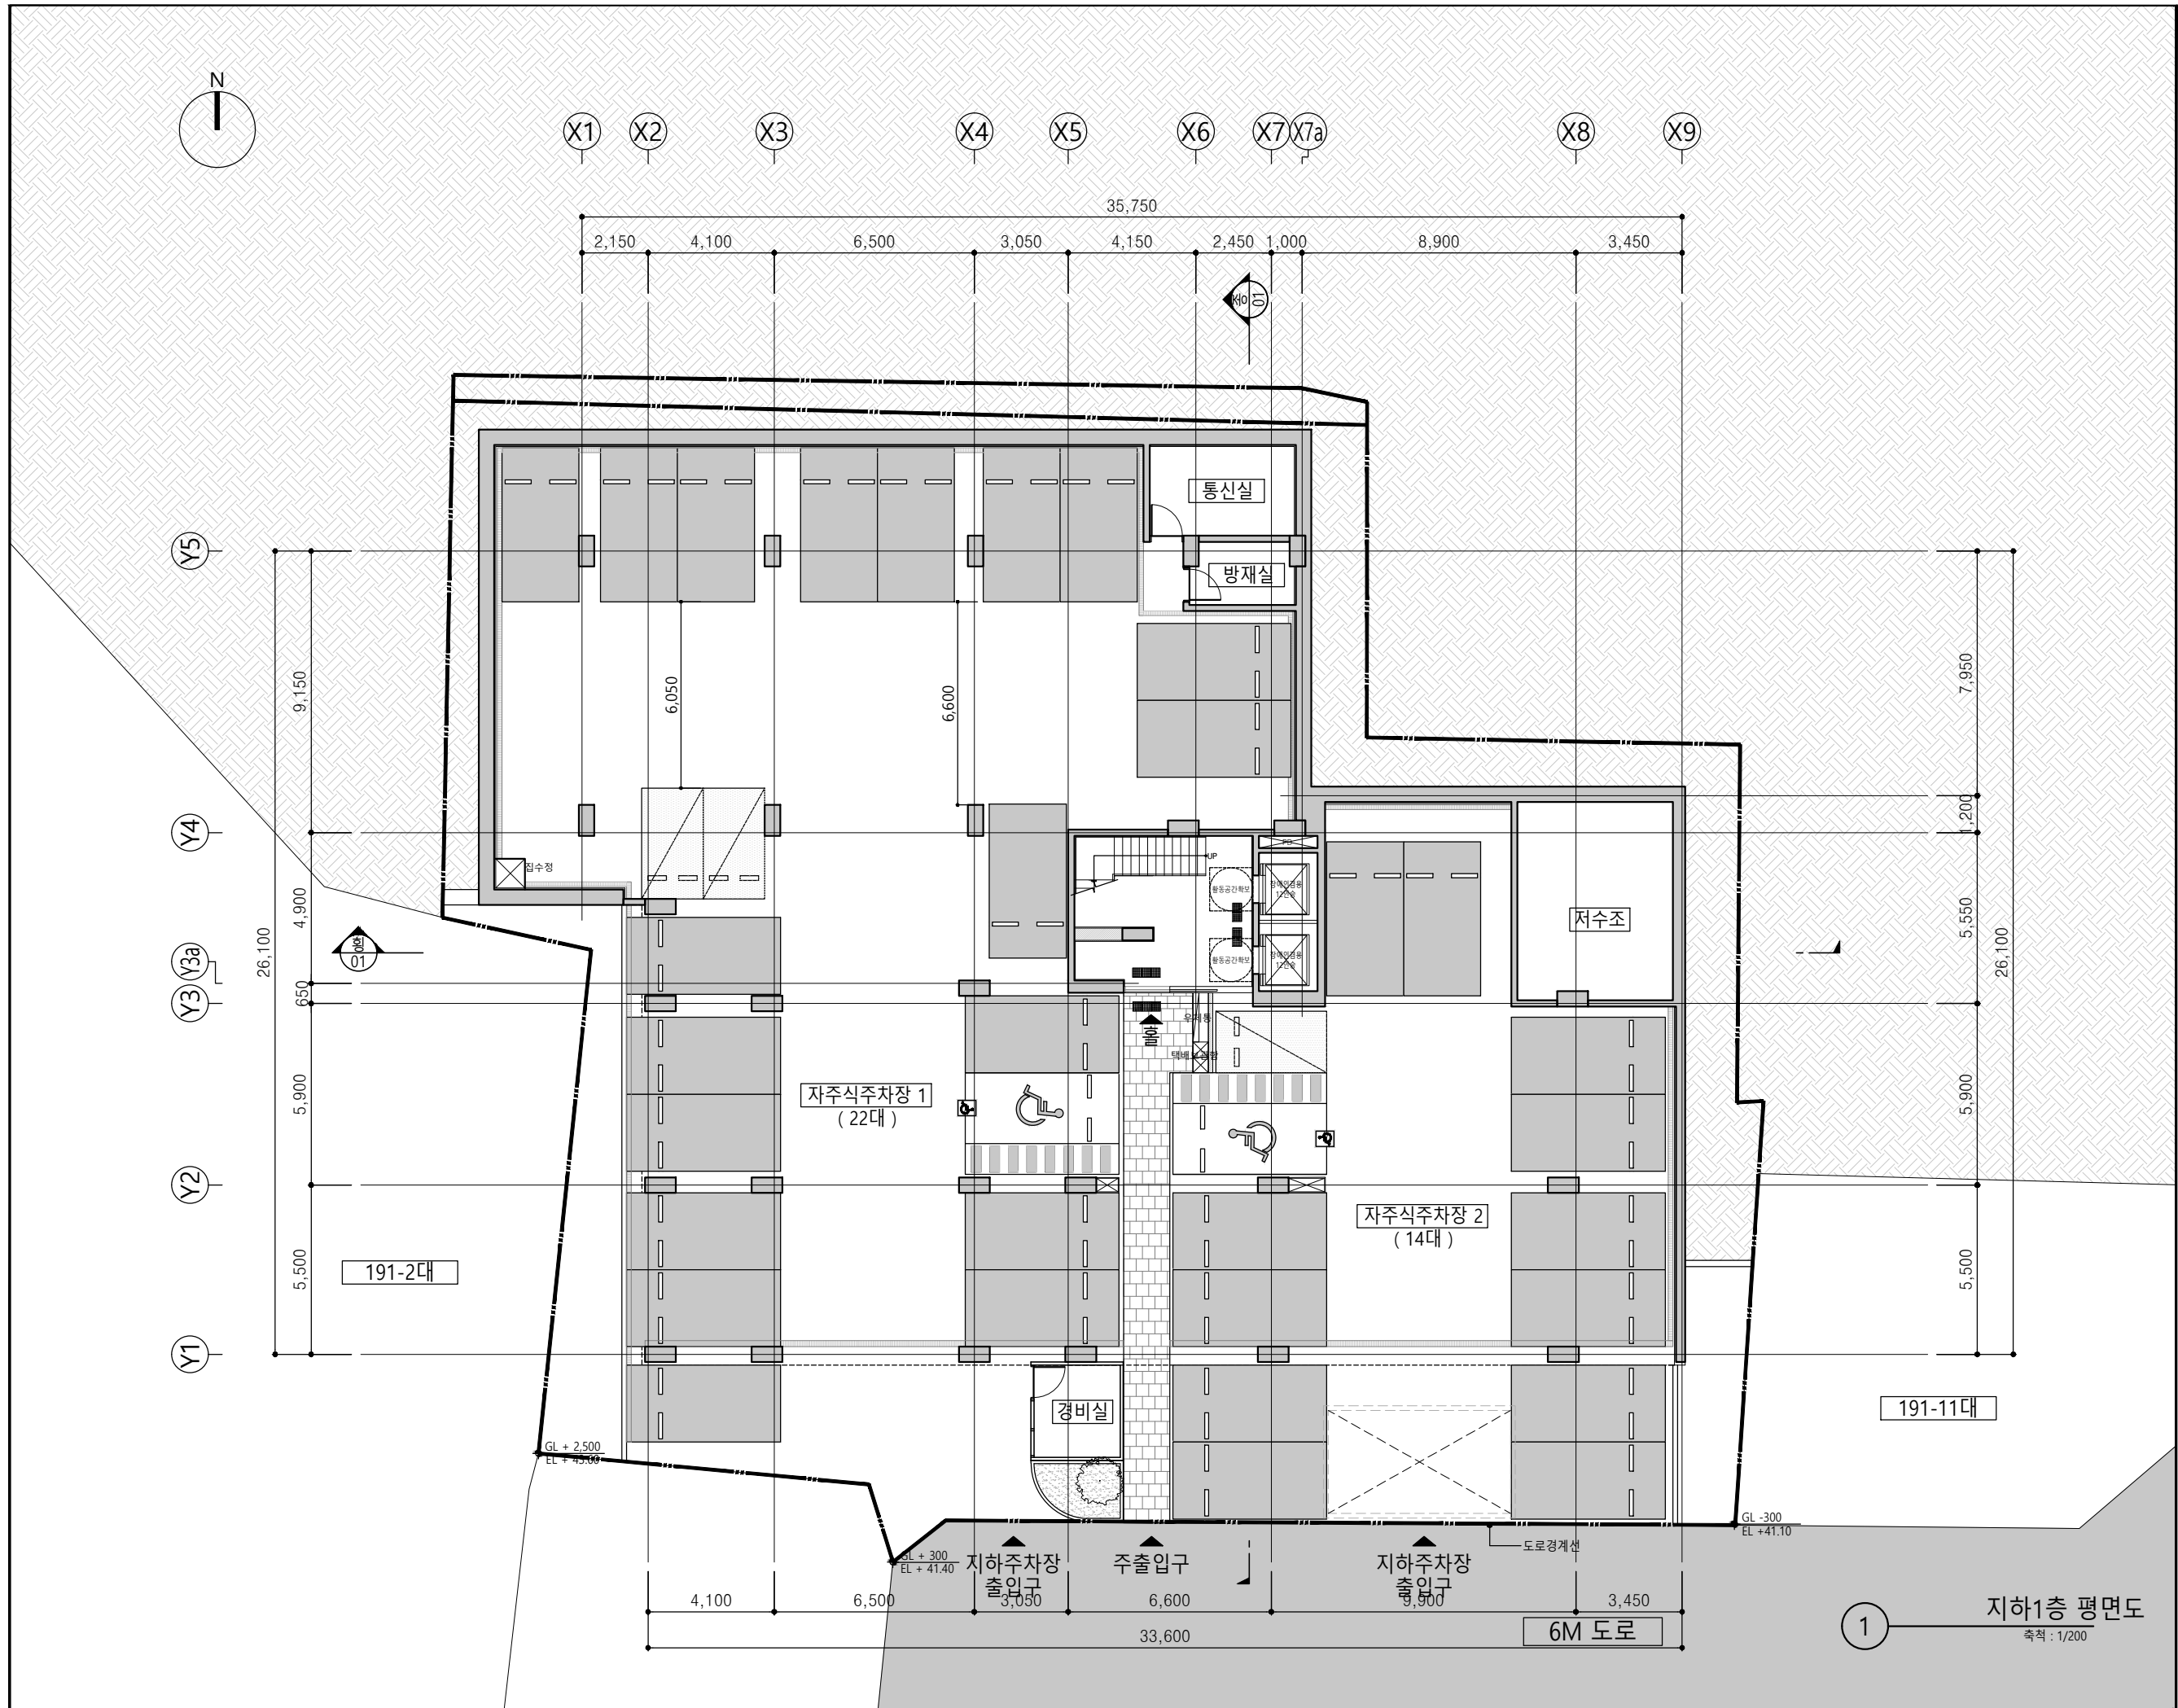

제로투엔  
건축사사무소

서울특별시 강남구 테헤란로 77길 13, 10층 (삼성동, 청초빌딩)  
T 02 6925 0745  
zero-to-n.com a@zero-to-n.com

project name

구산동 191-10 외7필지  
도시형생활주택 신축공사

revisions

| no. | date | note |
|-----|------|------|
|     |      |      |
|     |      |      |
|     |      |      |
|     |      |      |

note

title


지상1층 평면도

scale

1/200

number

A3 - 02

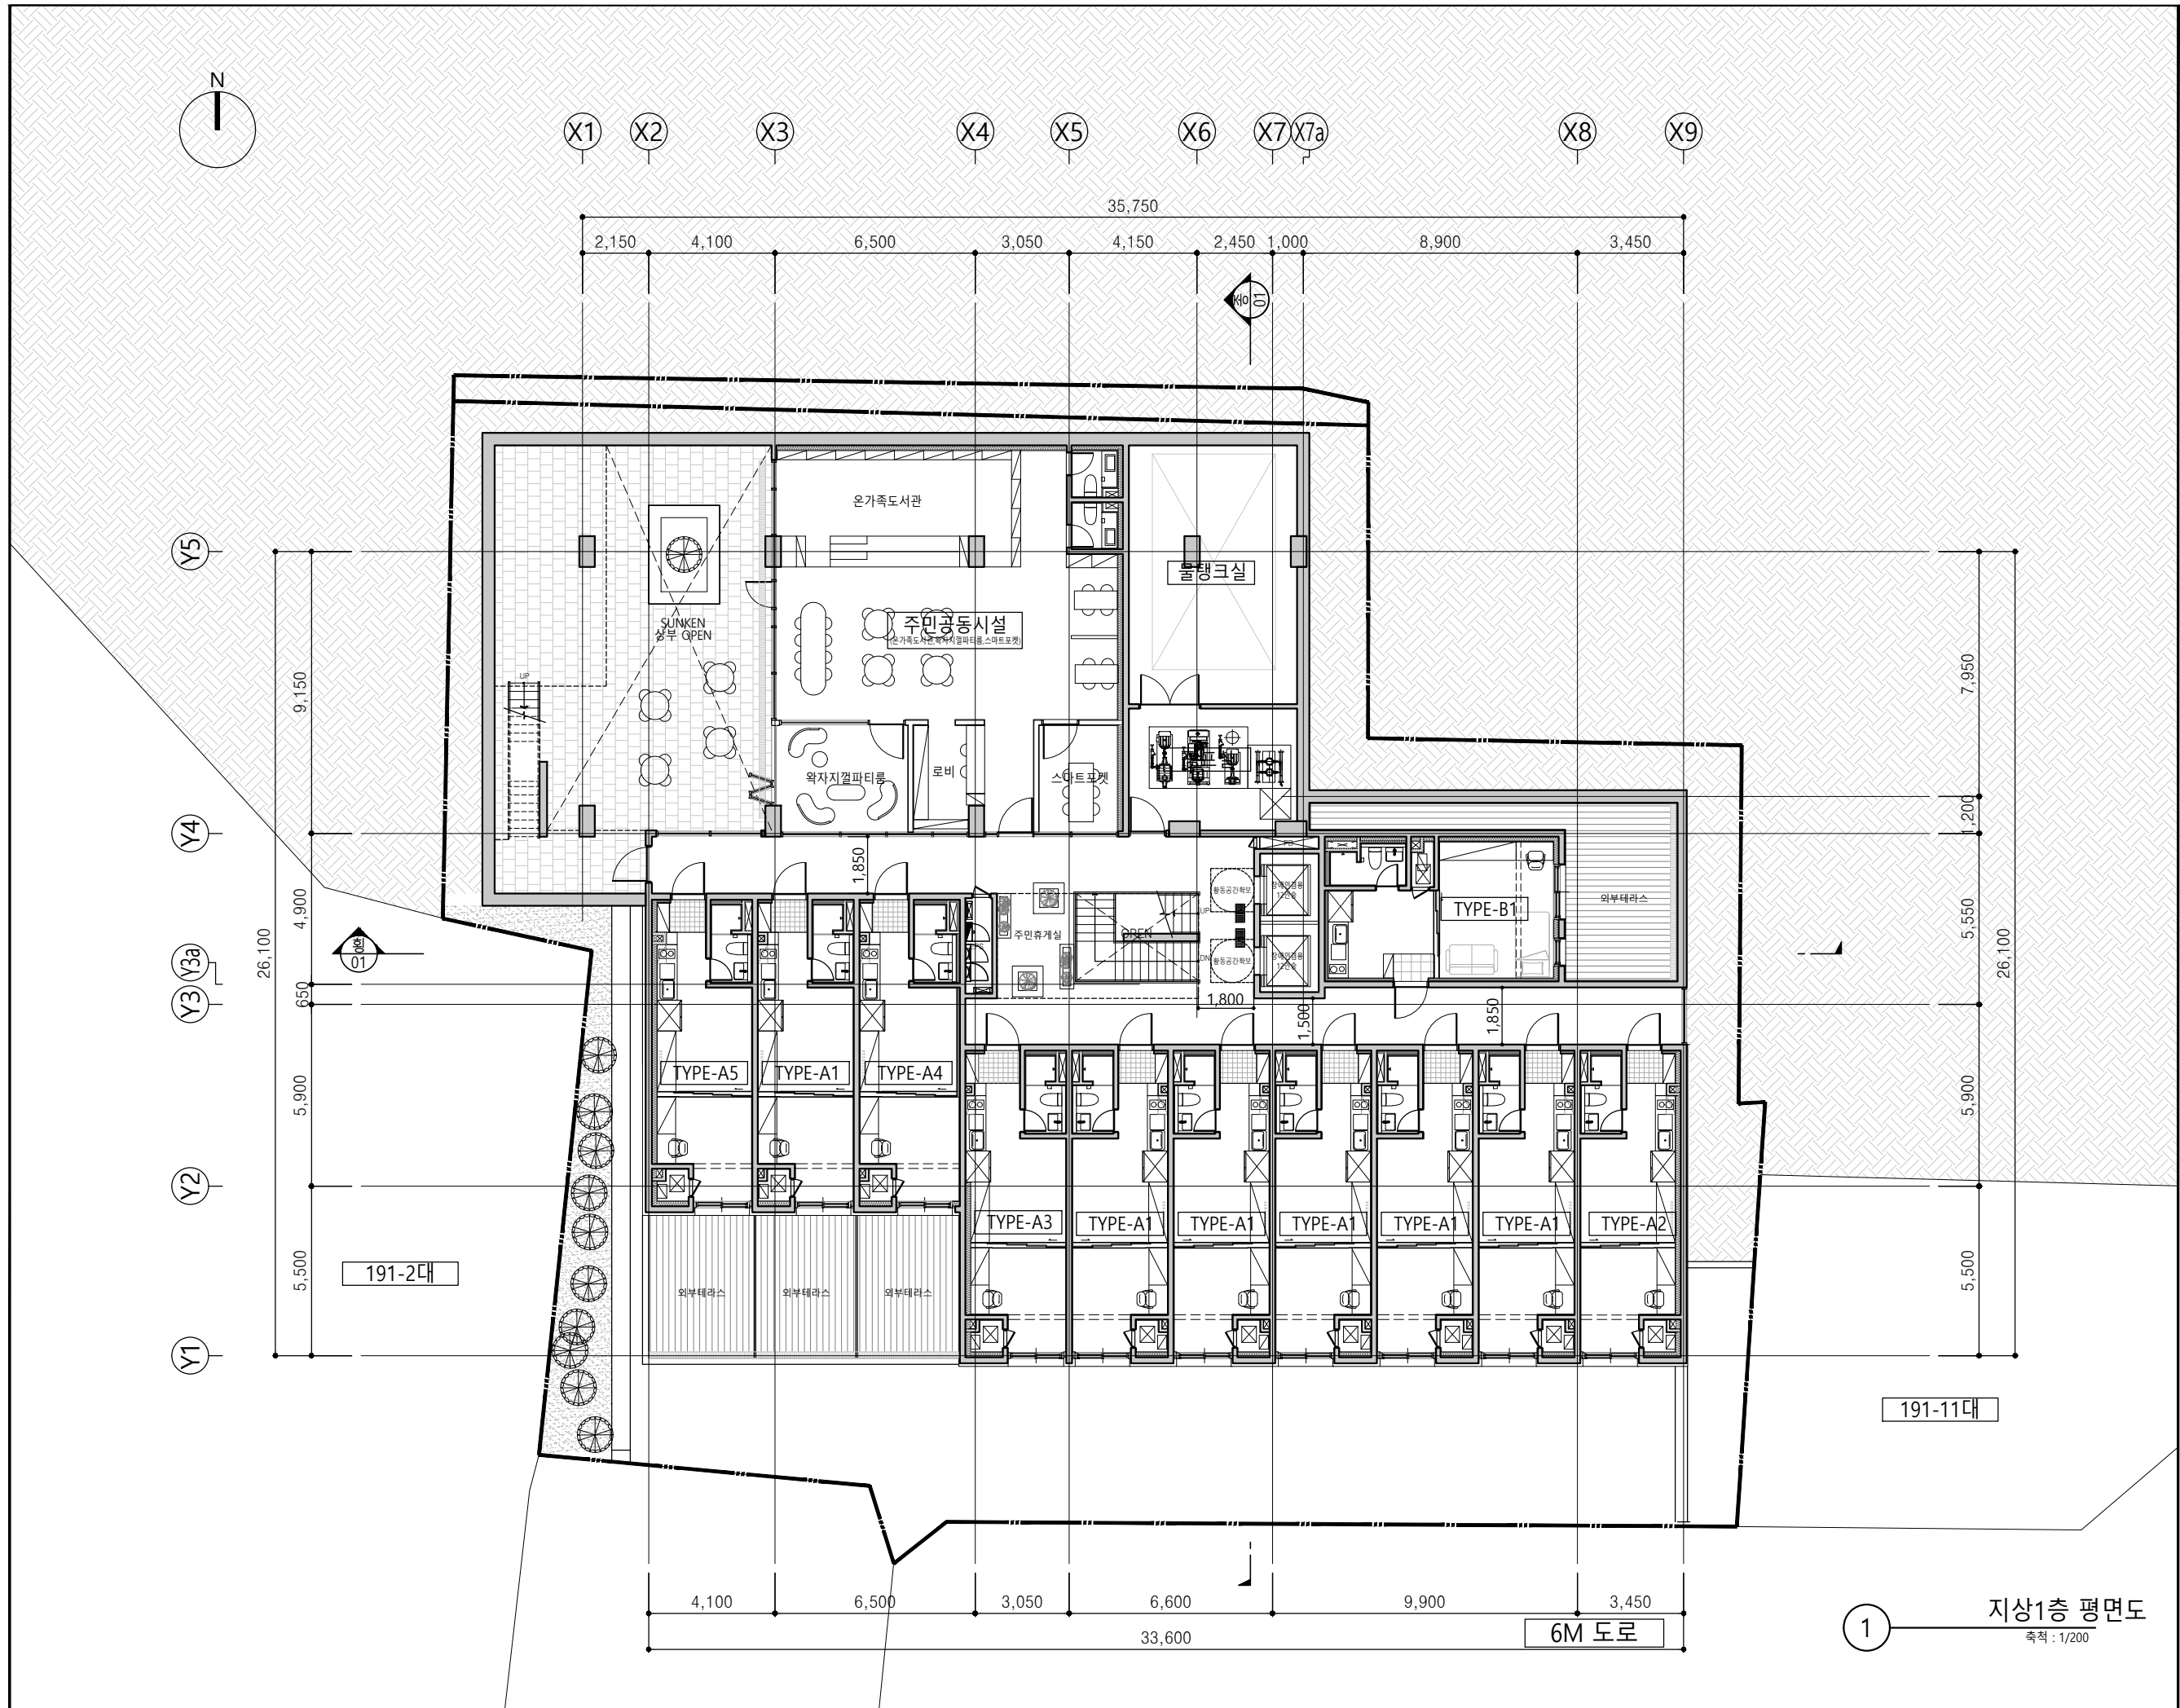



제로투엔  
건축사사무소

서울특별시 강남구 테헤란로 77길 13, 10층 (삼성동, 창조빌딩)  
T 02 6925 0745  
zero-to-n.com a@zero-to-n.com

project name

구산동 191-10 외7필지  
도시형생활주택 신축공사

revisions

| no. | date | note |
|-----|------|------|
|     |      |      |
|     |      |      |
|     |      |      |
|     |      |      |

note



title


지상2층 평면도

scale

1/200

number

A3 - 03

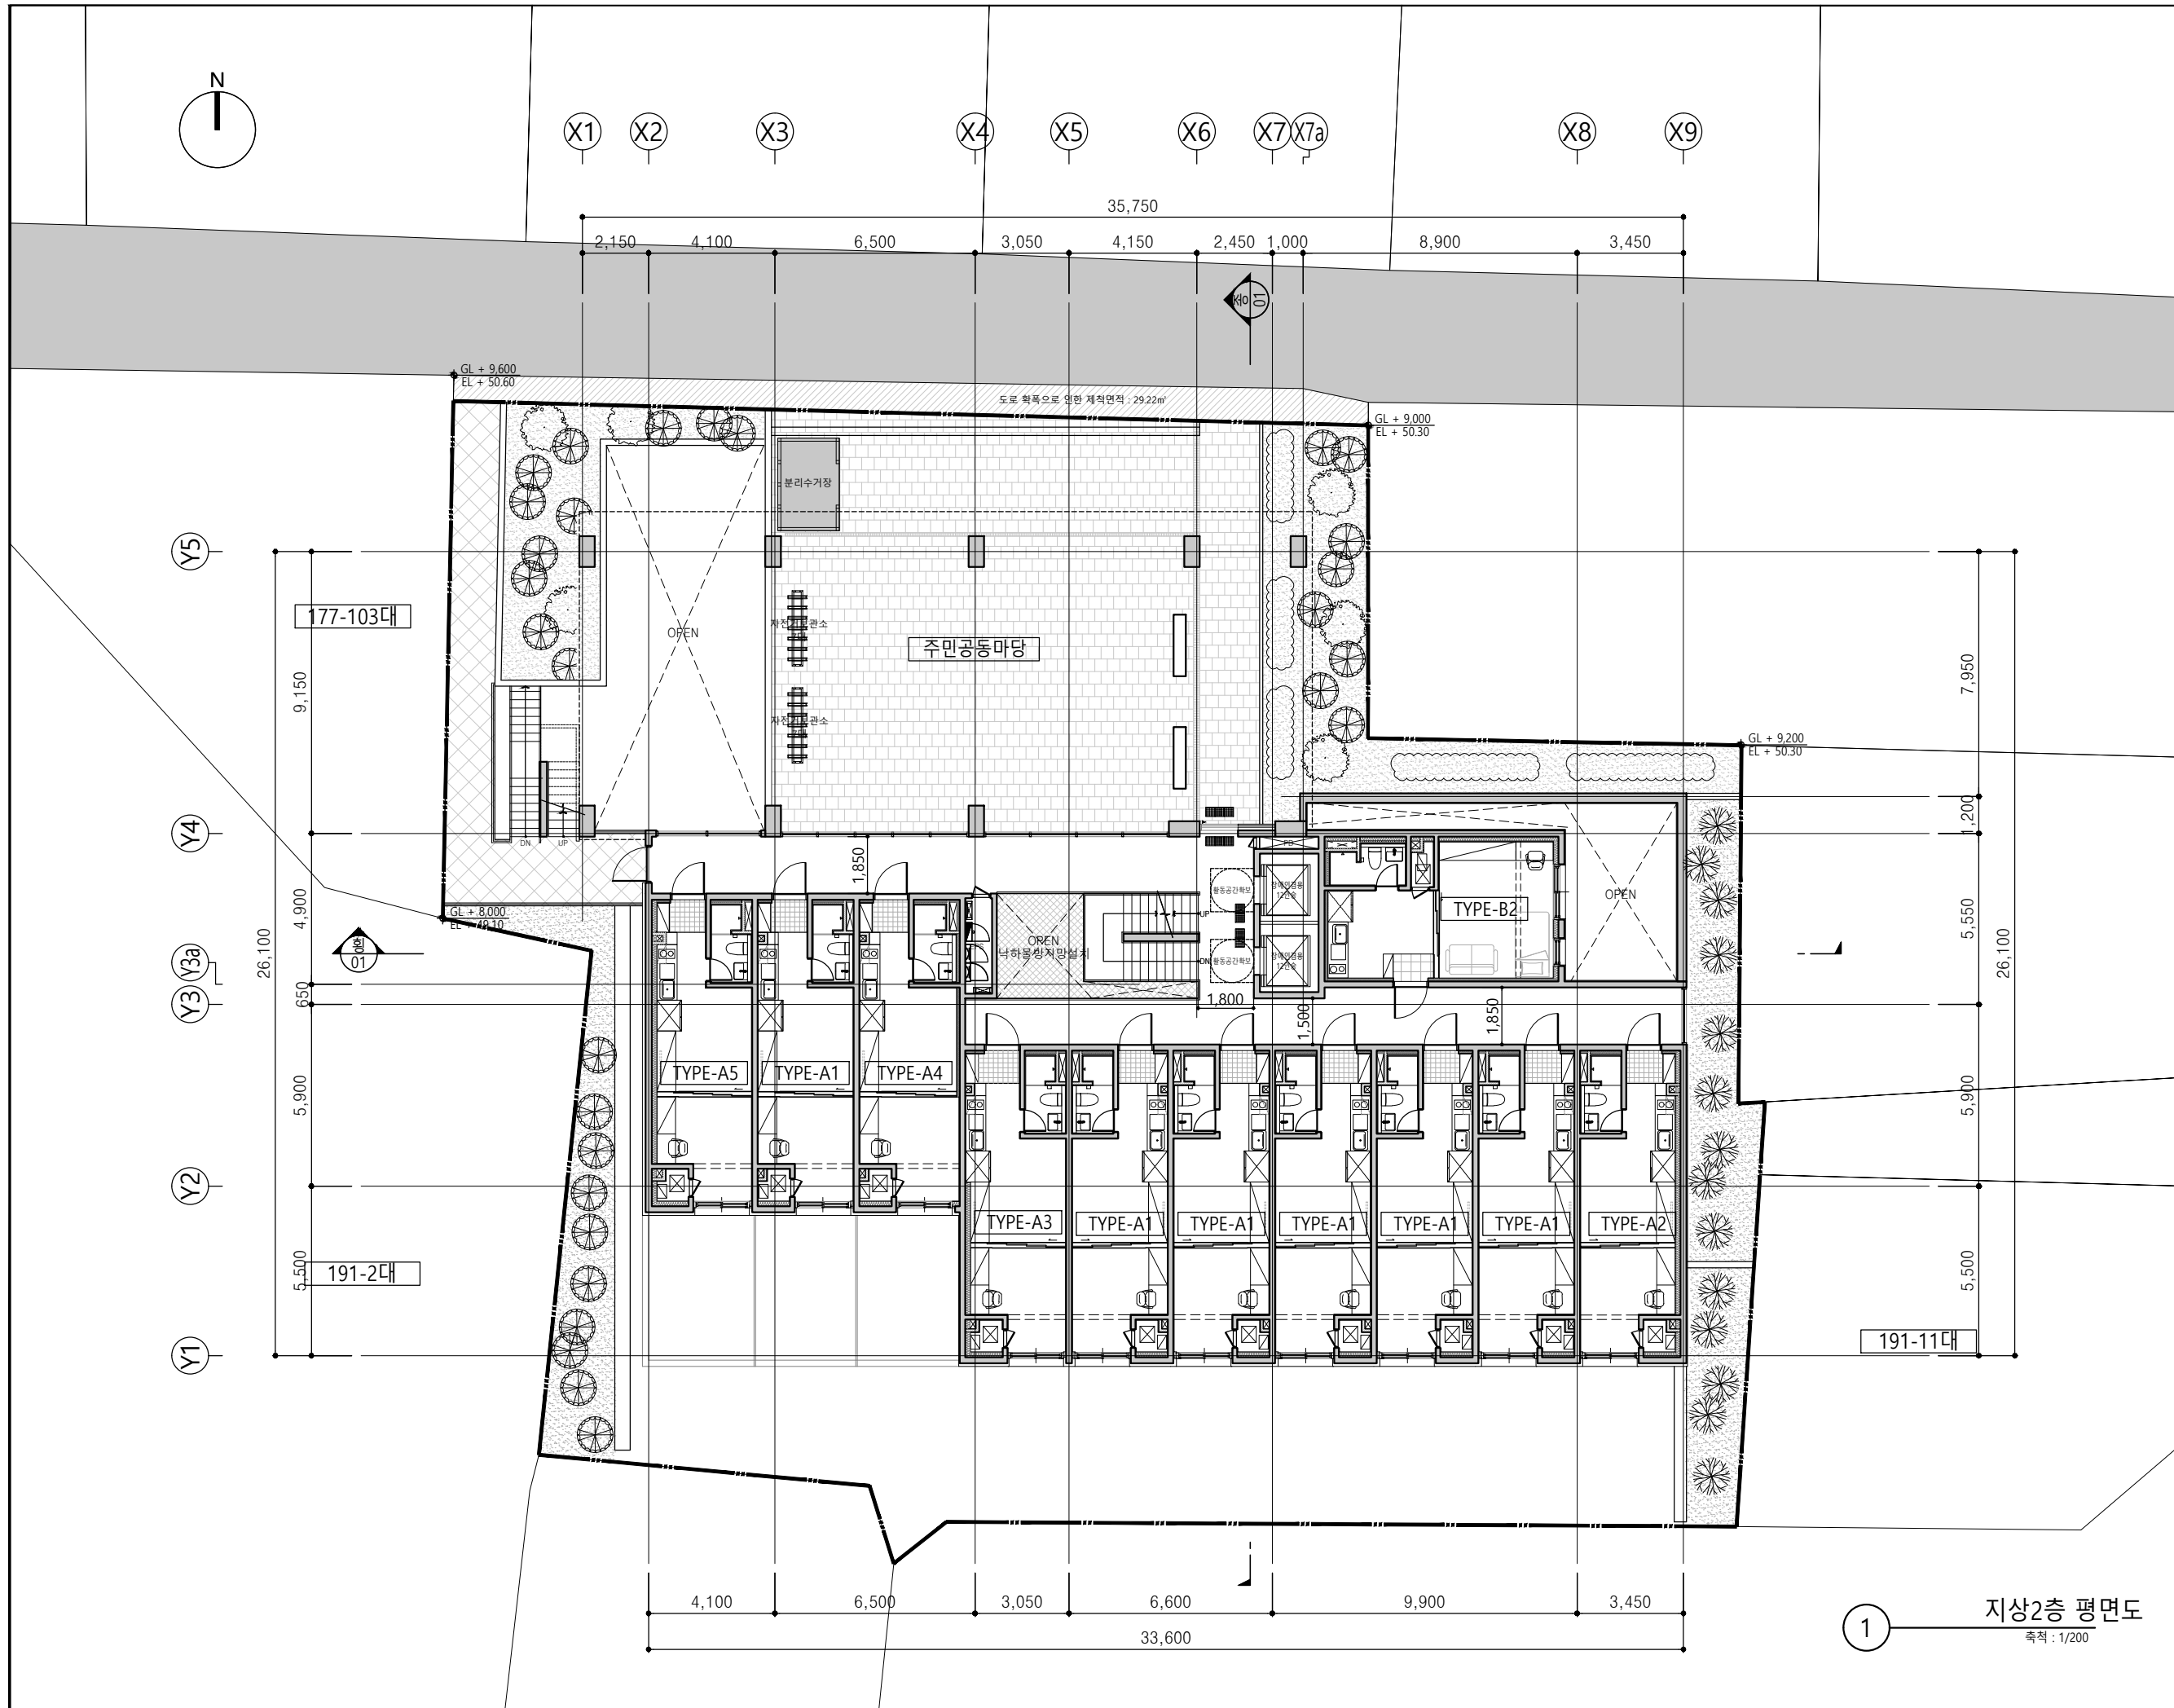

제로투엔  
건축사사무소

서울특별시 강남구 테헤란로 77길 13, 10층 (삼성동, 창조빌딩)  
T 02 6925 0745  
zero-to-n.com a@zero-to-n.com

project name

구산동 191-10 외7필지  
도시형생활주택 신축공사

revisions

| no. | date | note |
|-----|------|------|
|     |      |      |
|     |      |      |
|     |      |      |
|     |      |      |

note

title



지상3층 평면도

scale

1/200

number

A3 - 04

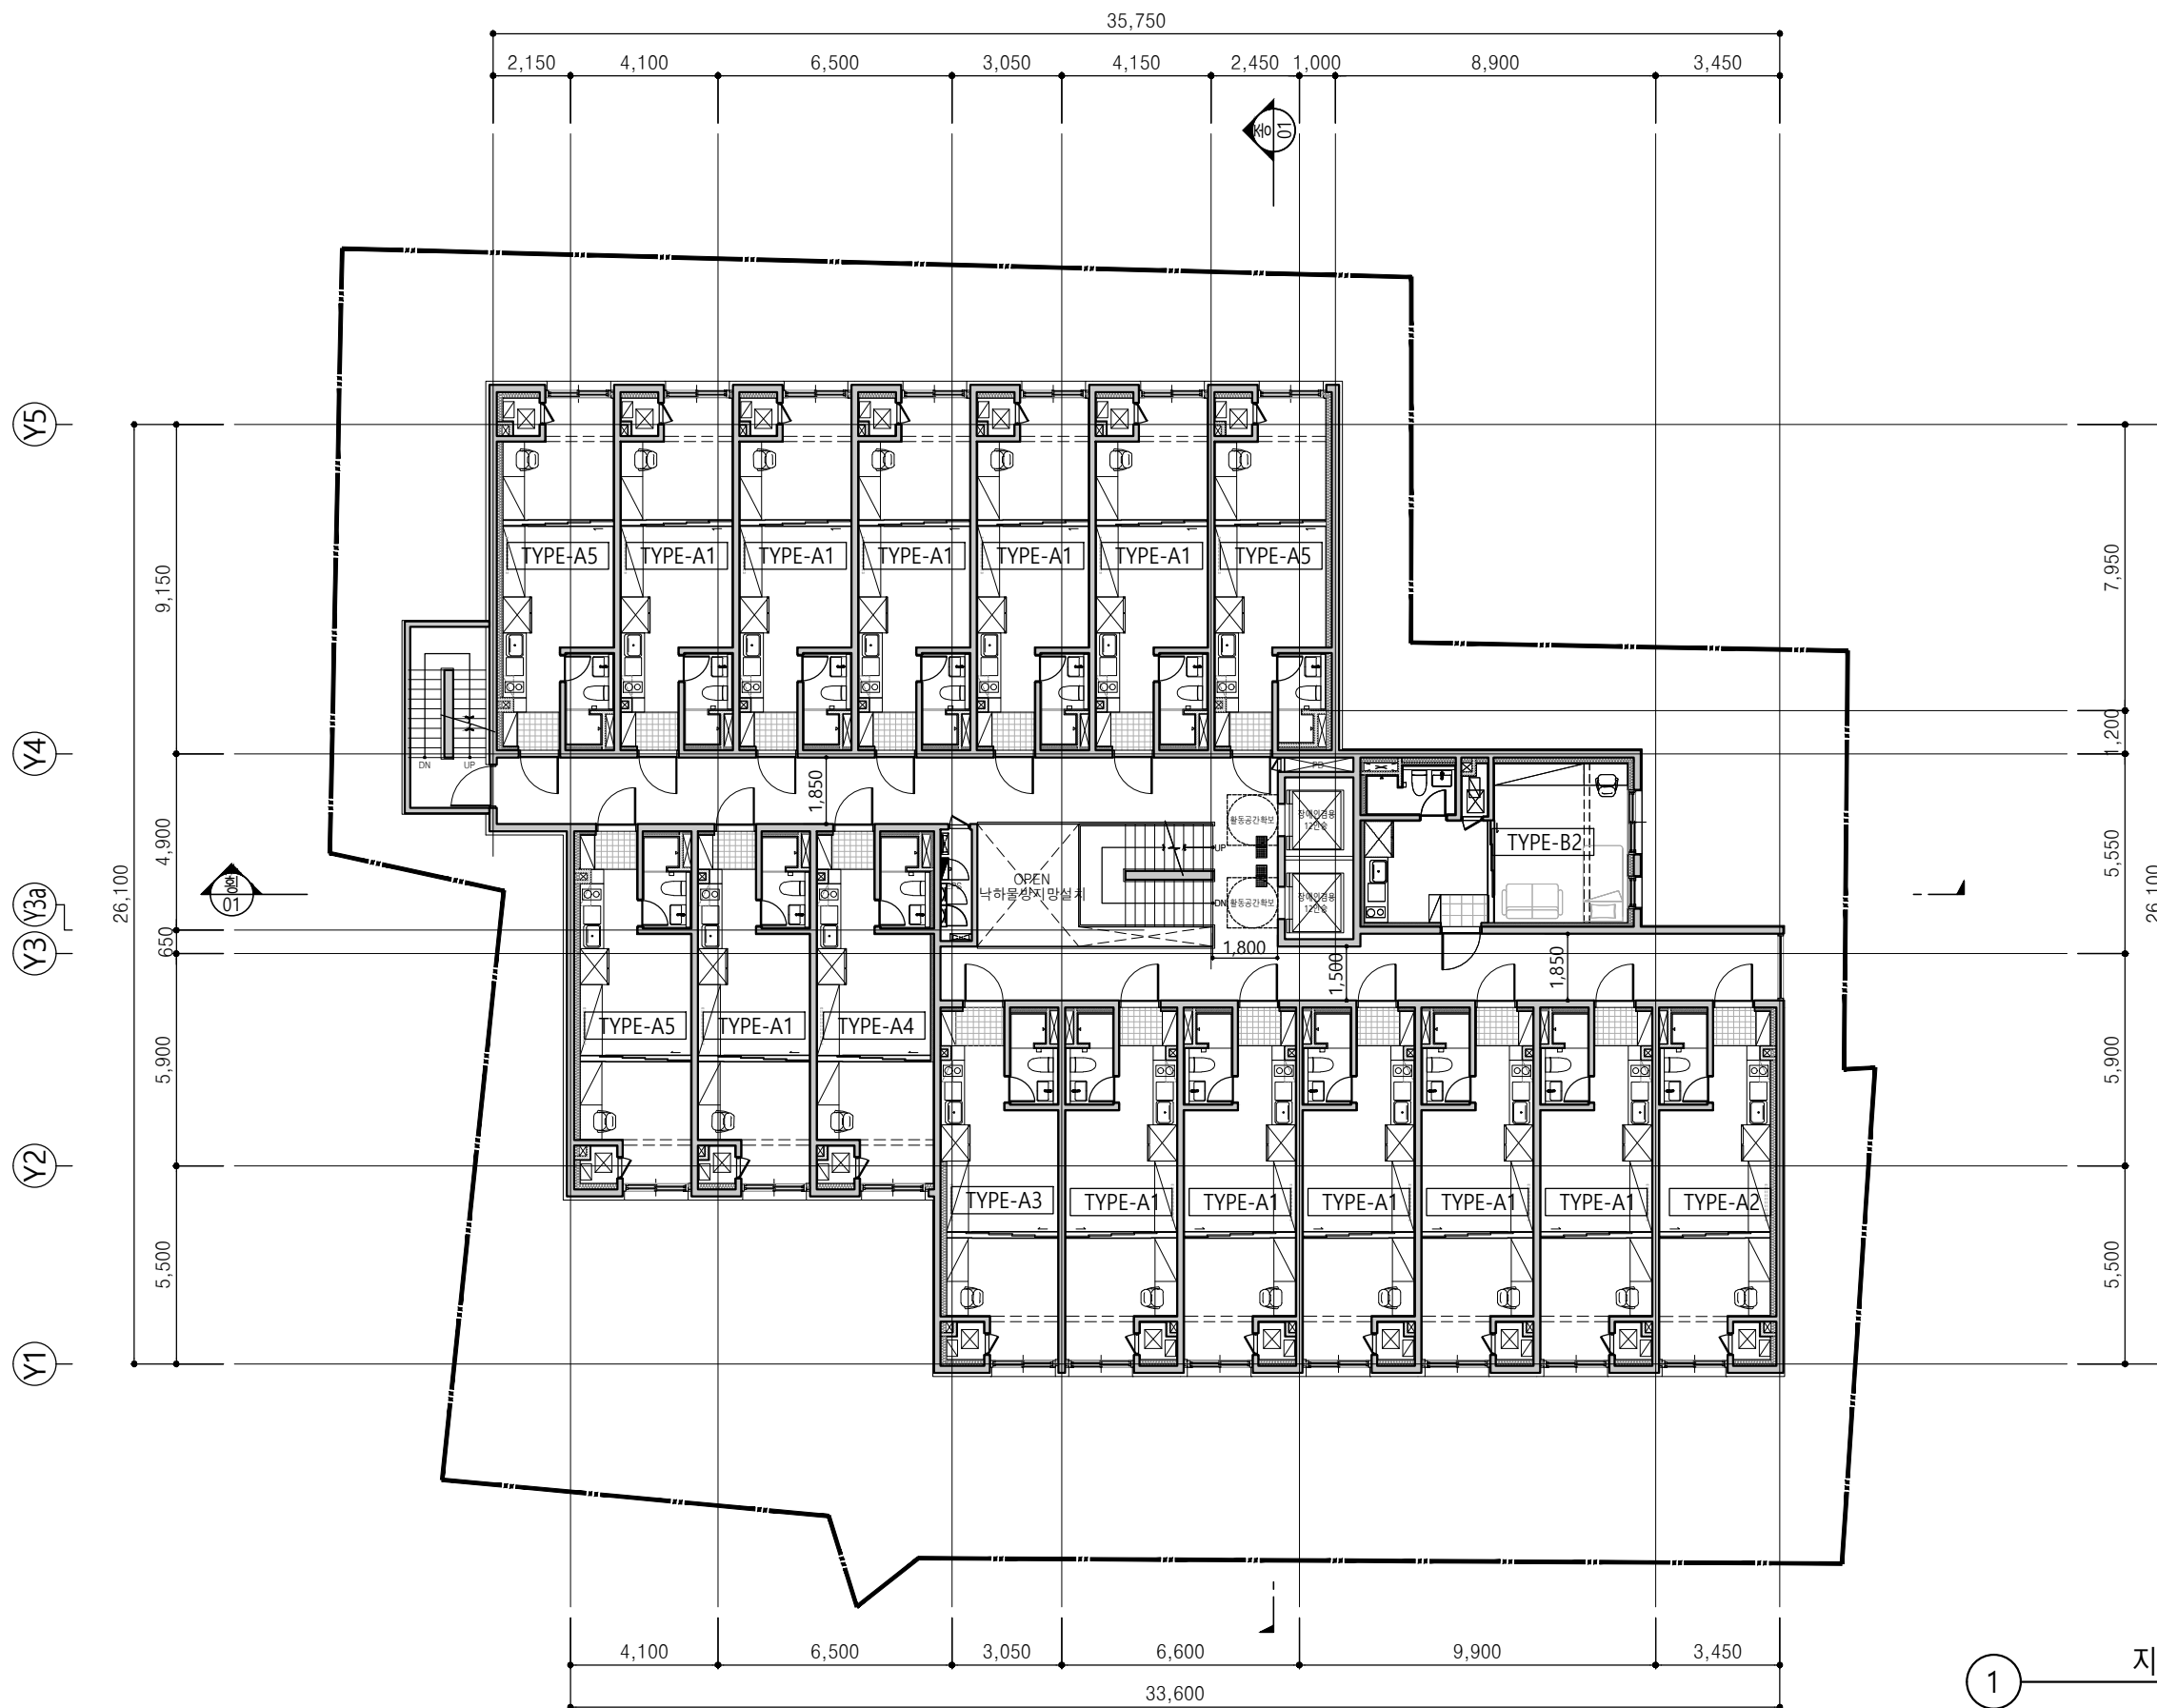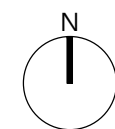

1

지상3층 평면도

축척 : 1/200

제로투엔  
건축사사무소

서울특별시 강남구 테헤란로 77길 13, 10층 (삼성동, 창조빌딩)  
T 02 6925 0745  
zero-to-n.com a@zero-to-n.com

project name

구산동 191-10 외7필지  
도시형생활주택 신축공사

revisions

| no. | date | note |
|-----|------|------|
|     |      |      |
|     |      |      |
|     |      |      |
|     |      |      |

note

title



지상4층 평면도

scale

1/200

number

A3 - 05

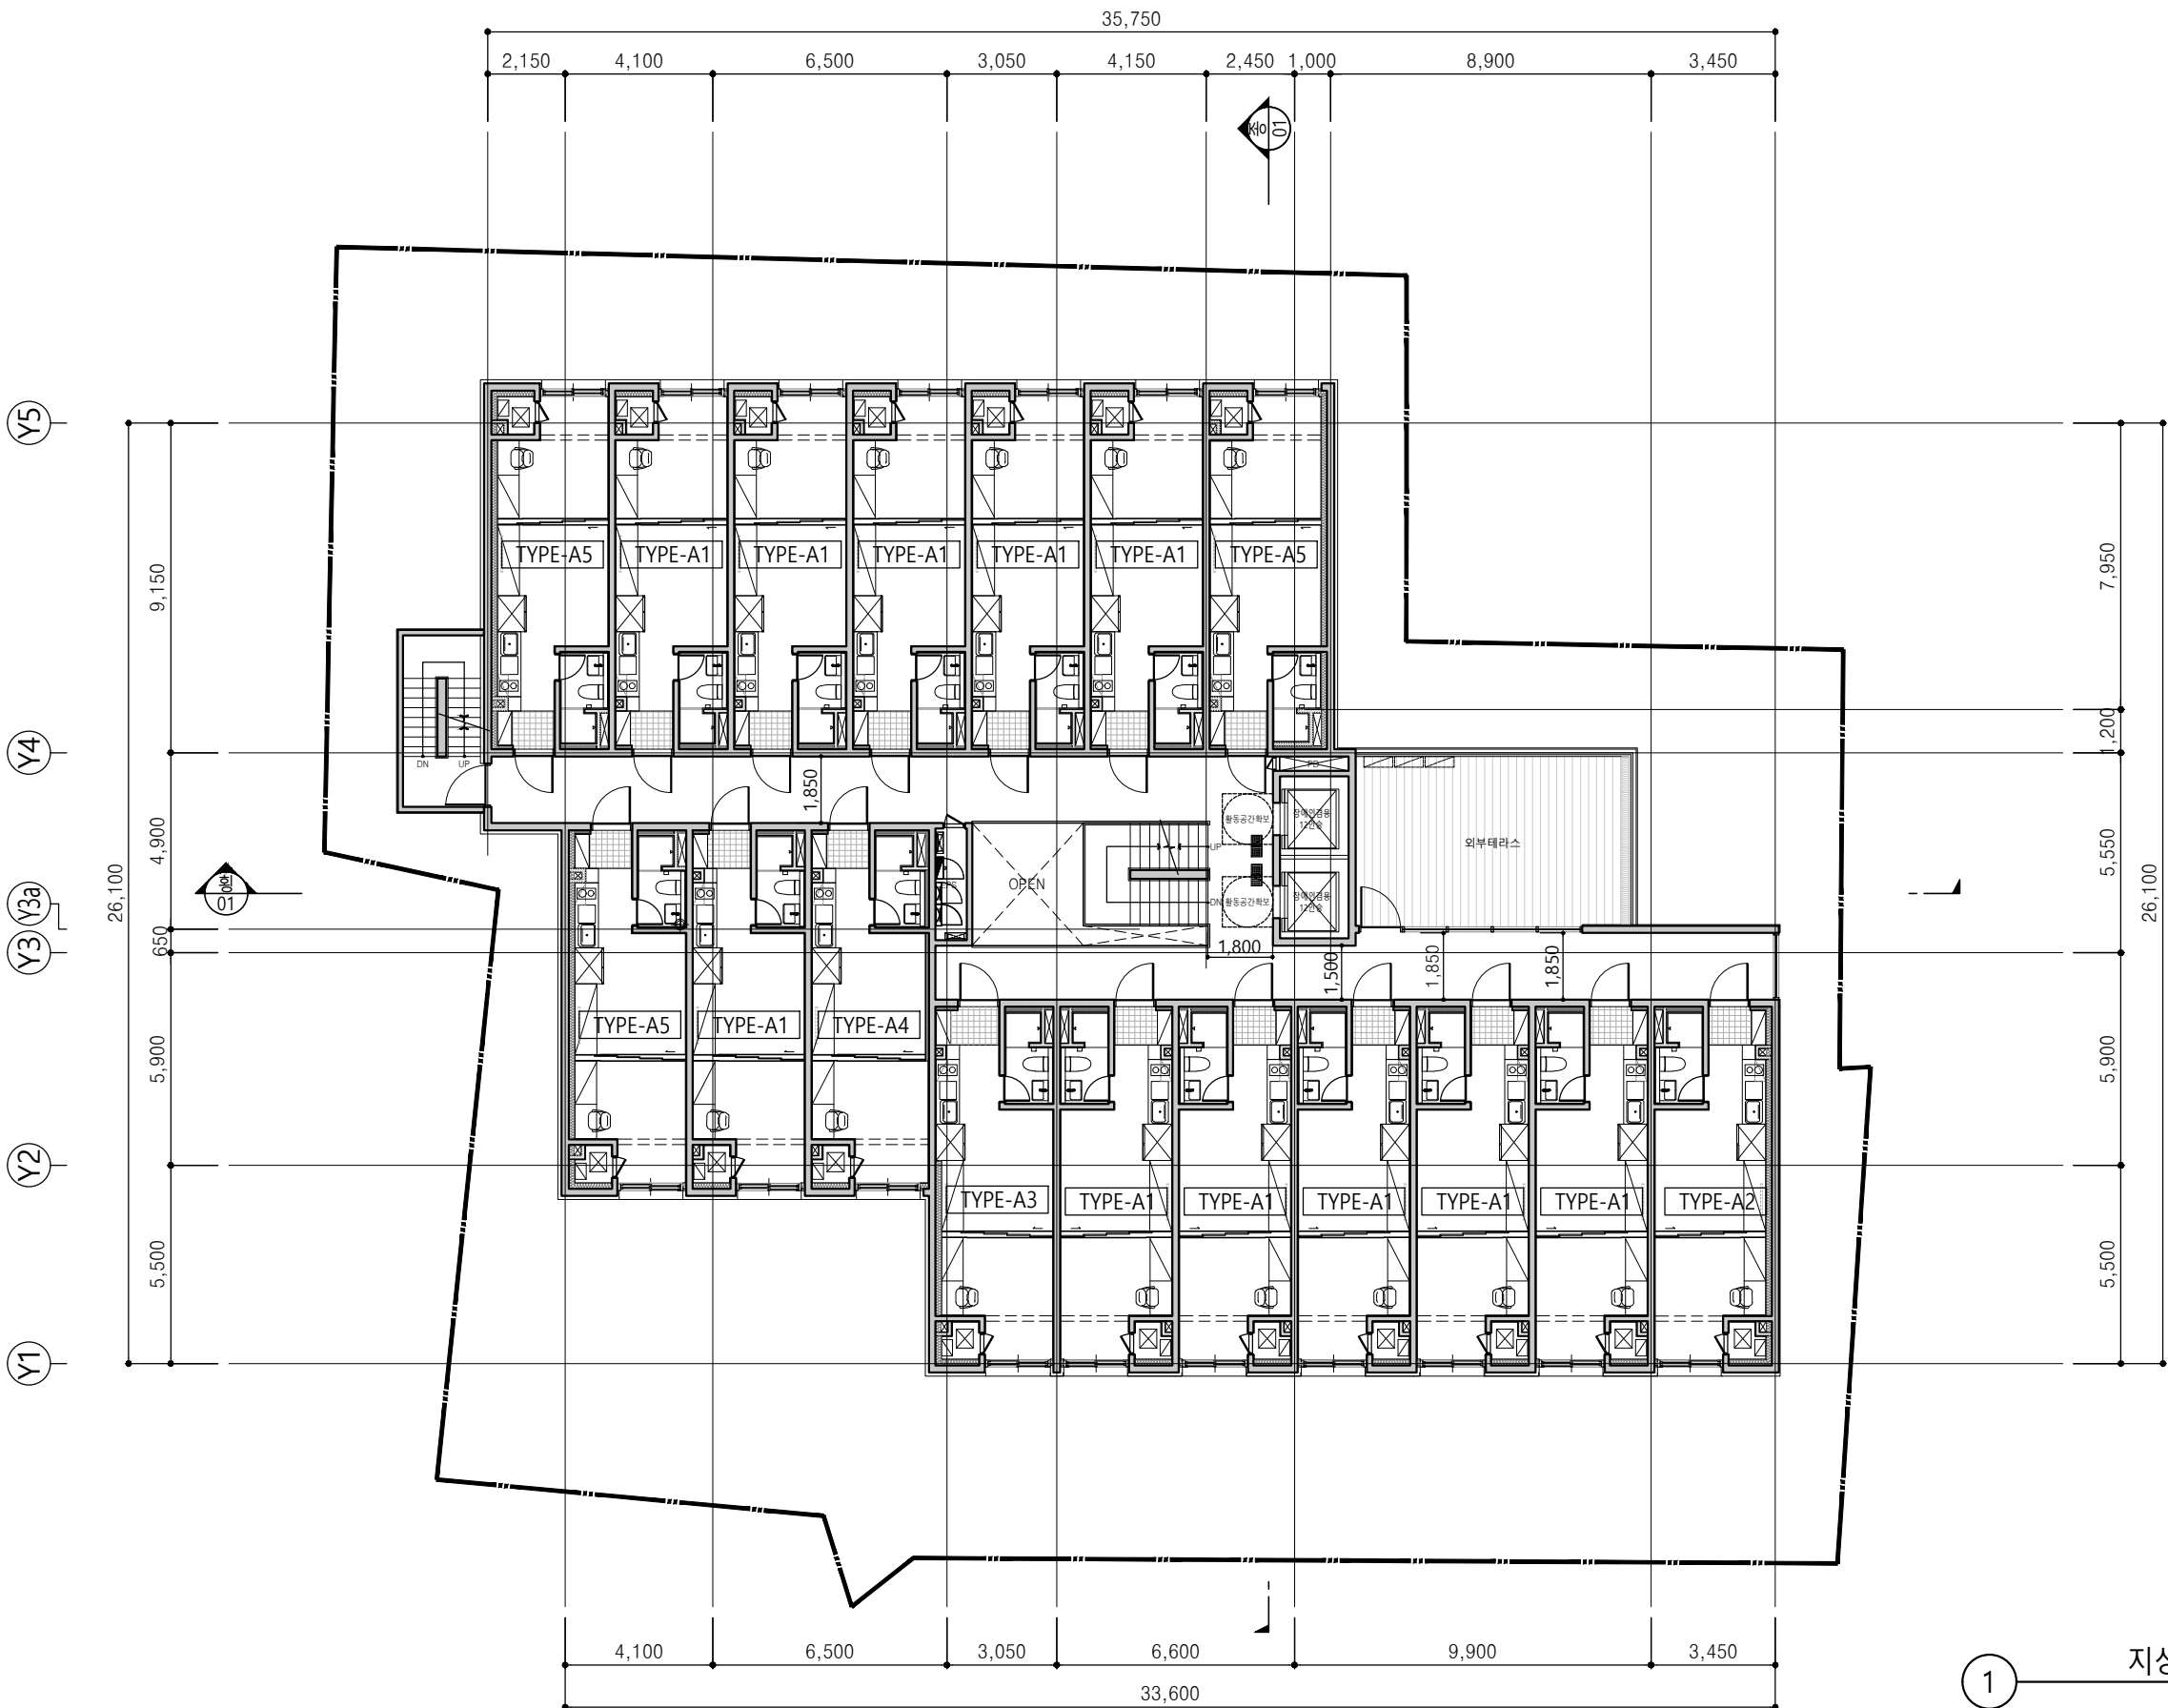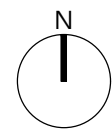

1 지상4층 평면도  
축척 : 1/200

제로투엔  
건축사사무소

서울특별시 강남구 테헤란로 77길 13, 10층 (삼성동, 창조빌딩)  
T 02 6925 0745  
zero-to-n.com a@zero-to-n.com

project name

구산동 191-10 외7필지  
도시형생활주택 신축공사

revisions

| no. | date | note |
|-----|------|------|
|     |      |      |
|     |      |      |
|     |      |      |
|     |      |      |

note

title



지상5층 평면도

scale

1/200

number

A3 - 06

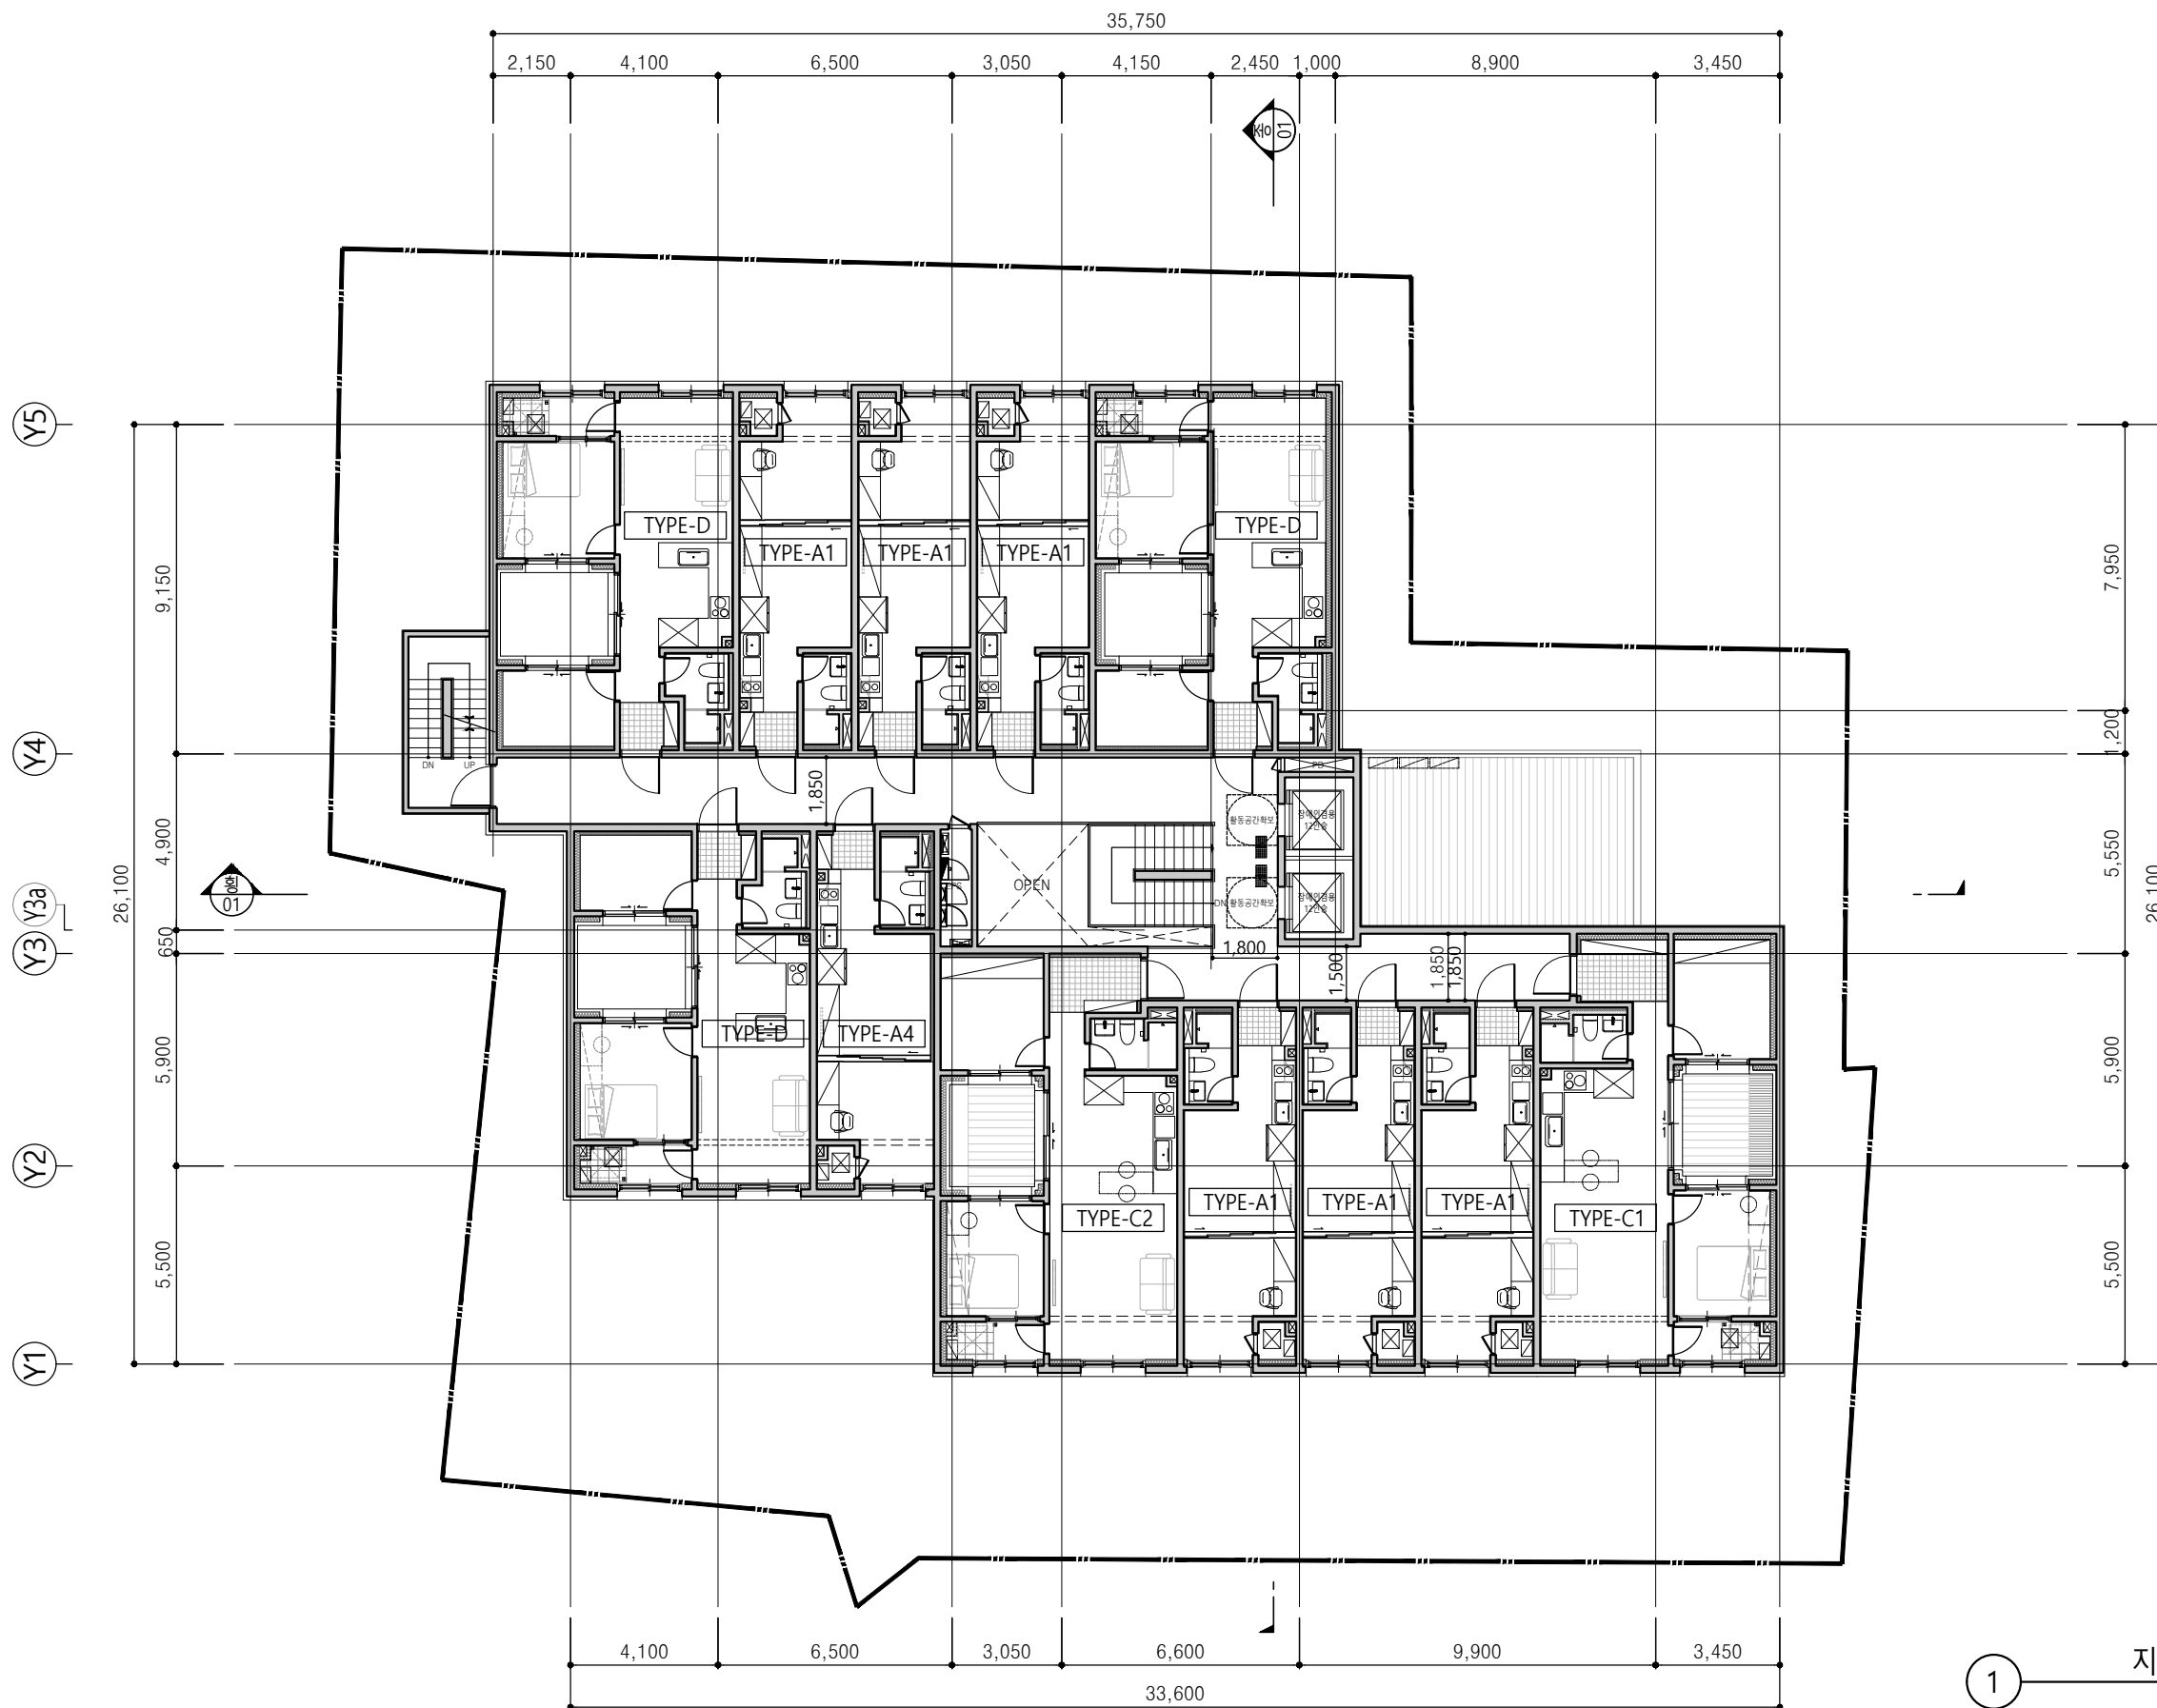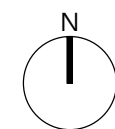

1 지상5층 평면도  
축척 : 1/200

제로투엔  
건축사사무소

서울특별시 강남구 테헤란로 77길 13, 10층 (삼성동, 창조빌딩)  
T 02 6925 0745  
zero-to-n.com a@zero-to-n.com

project name

구산동 191-10 외7필지  
도시형생활주택 신축공사

revisions

| no. | date | note |
|-----|------|------|
|     |      |      |
|     |      |      |
|     |      |      |
|     |      |      |

note

title


지붕층 평면도

scale

1/200

number

A3 - 07

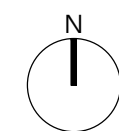

1

지붕층 평면도

축척 : 1/200