



PHONE : (02)3494-3323/3324
FAX : (02)3494-3329
E-MAIL : soo2004s@hanmail.net

PROJECT NO.
사업번호

NOTE

REMARKS
주 기 사 항

△		
△		
△		
△		
△		
△		

SYM.	DESCRIPTION OF REVISION	REVISED BY DATE
------	-------------------------	--------------------

ARCHITECTURAL DESIGNED BY
건 축 설 계 조 주 혜

STRUCTURAL DESIGNED BY
구 조 설 계

CIVIL DESIGNED BY
건 축 설 계

MECHANICAL DESIGNED BY
기 계 설 계

ELECTRICAL DESIGNED BY
전 기 설 계

LANDSCAPE DESIGNED BY
조 경 설 계

DRAWN BY
제 도

CHEKED BY 심 사	APPROVED BY 승 인
------------------	--------------------

DATE
일 자 2025. 01.

PROJECT TITEL
사 업 명 칭
신사동 16-25번지
다세대주택 신축공사

NAME OF
도 면 명

조감도

SCALE
축 적 NONE

SHEET NO.
일 련 번 호

DRAWING NO.
도 면 번 호 A-016

△		
△		
△		
△		
△		
△		
SYMBOL	DESCRIPTION OF REVISION	REVISED BY DATE

ARCHITECTURAL DESIGNED BY
조 주 혜

STRUCTURAL DESIGNED BY
구 조 설 계

CIVIL DESIGNED BY
건 축 설 계

MECHANICAL DESIGNED BY
기 계 설 계

ELECTRICAL DESIGNED BY
전 기 설 계

LANDSCAPE DESIGNED BY
조 경 설 계

DRAWN BY
제 도

CHECKED BY
상 사

APPROVED BY
승 인

DATE
일 자 2025. 01.

PROJECT TITLE
사 업 명 칭

신사동 16-25번지
다세대주택 신축공사

NAME OF
도 면 명

지상 1층 평면도

SCALE
축 척 1/100

SHEET NO.
일련번호

DRAWING NO.
도면번호 A-201

4M미만 막다른도로

4M 도로

6M 도로

지상 1층 평면도

축척 : 1/100

방화유리창 방

*방화유리창 [건축물의 피난·방화구조 등의 기준에 관한 규칙 제24조9항]
-건축물의 인접 대지경계선에 접하는 외벽에 설치하는 창호와 인접대지 경계선 간의 거리가 1.5미터 이내인 경우 설치해야함.
-한국산업표준 KS F 2845(유리구조 부분의 내화 시험방법)에 규정된 방법에 따라 시험한 결과 비잔열 20분 이상의 성능이 있는 유리창일 것.

범례

소	ABC분말소화기(3.3kg)
S	단독경보형감지기(연기)
S2	단독경보형감지기(열)
S3	가스누설경보기 (주방 및 보일러실)

△		
△		
△		
△		
△		
△		

SYM.	DESCRIPTION OF REVISION	REVISED BY DATE
------	-------------------------	-----------------

ARCHITECTURAL DESIGNED BY
조 주 혜

STRUCTURAL DESIGNED BY
구 조 설 계

CIVIL DESIGNED BY
건 축 설 계

MECHANICAL DESIGNED BY
기 계 설 계

ELECTRICAL DESIGNED BY
전 기 설 계

LANDSCAPE DESIGNED BY
조 경 설 계

DRAWN BY
제 도

CHECKED BY
상 사

APPROVED BY
승 인

DATE
일 자 2025. 01.

PROJECT TITEL
사 업 명 칭

신사동 16-25번지
다세대주택 신축공사



NAME OF
도 면 명

지상 2층 평면도

SCALE
축 척 1/100

SHEET NO.
일련번호

DRAWING NO.
도면번호 A-202

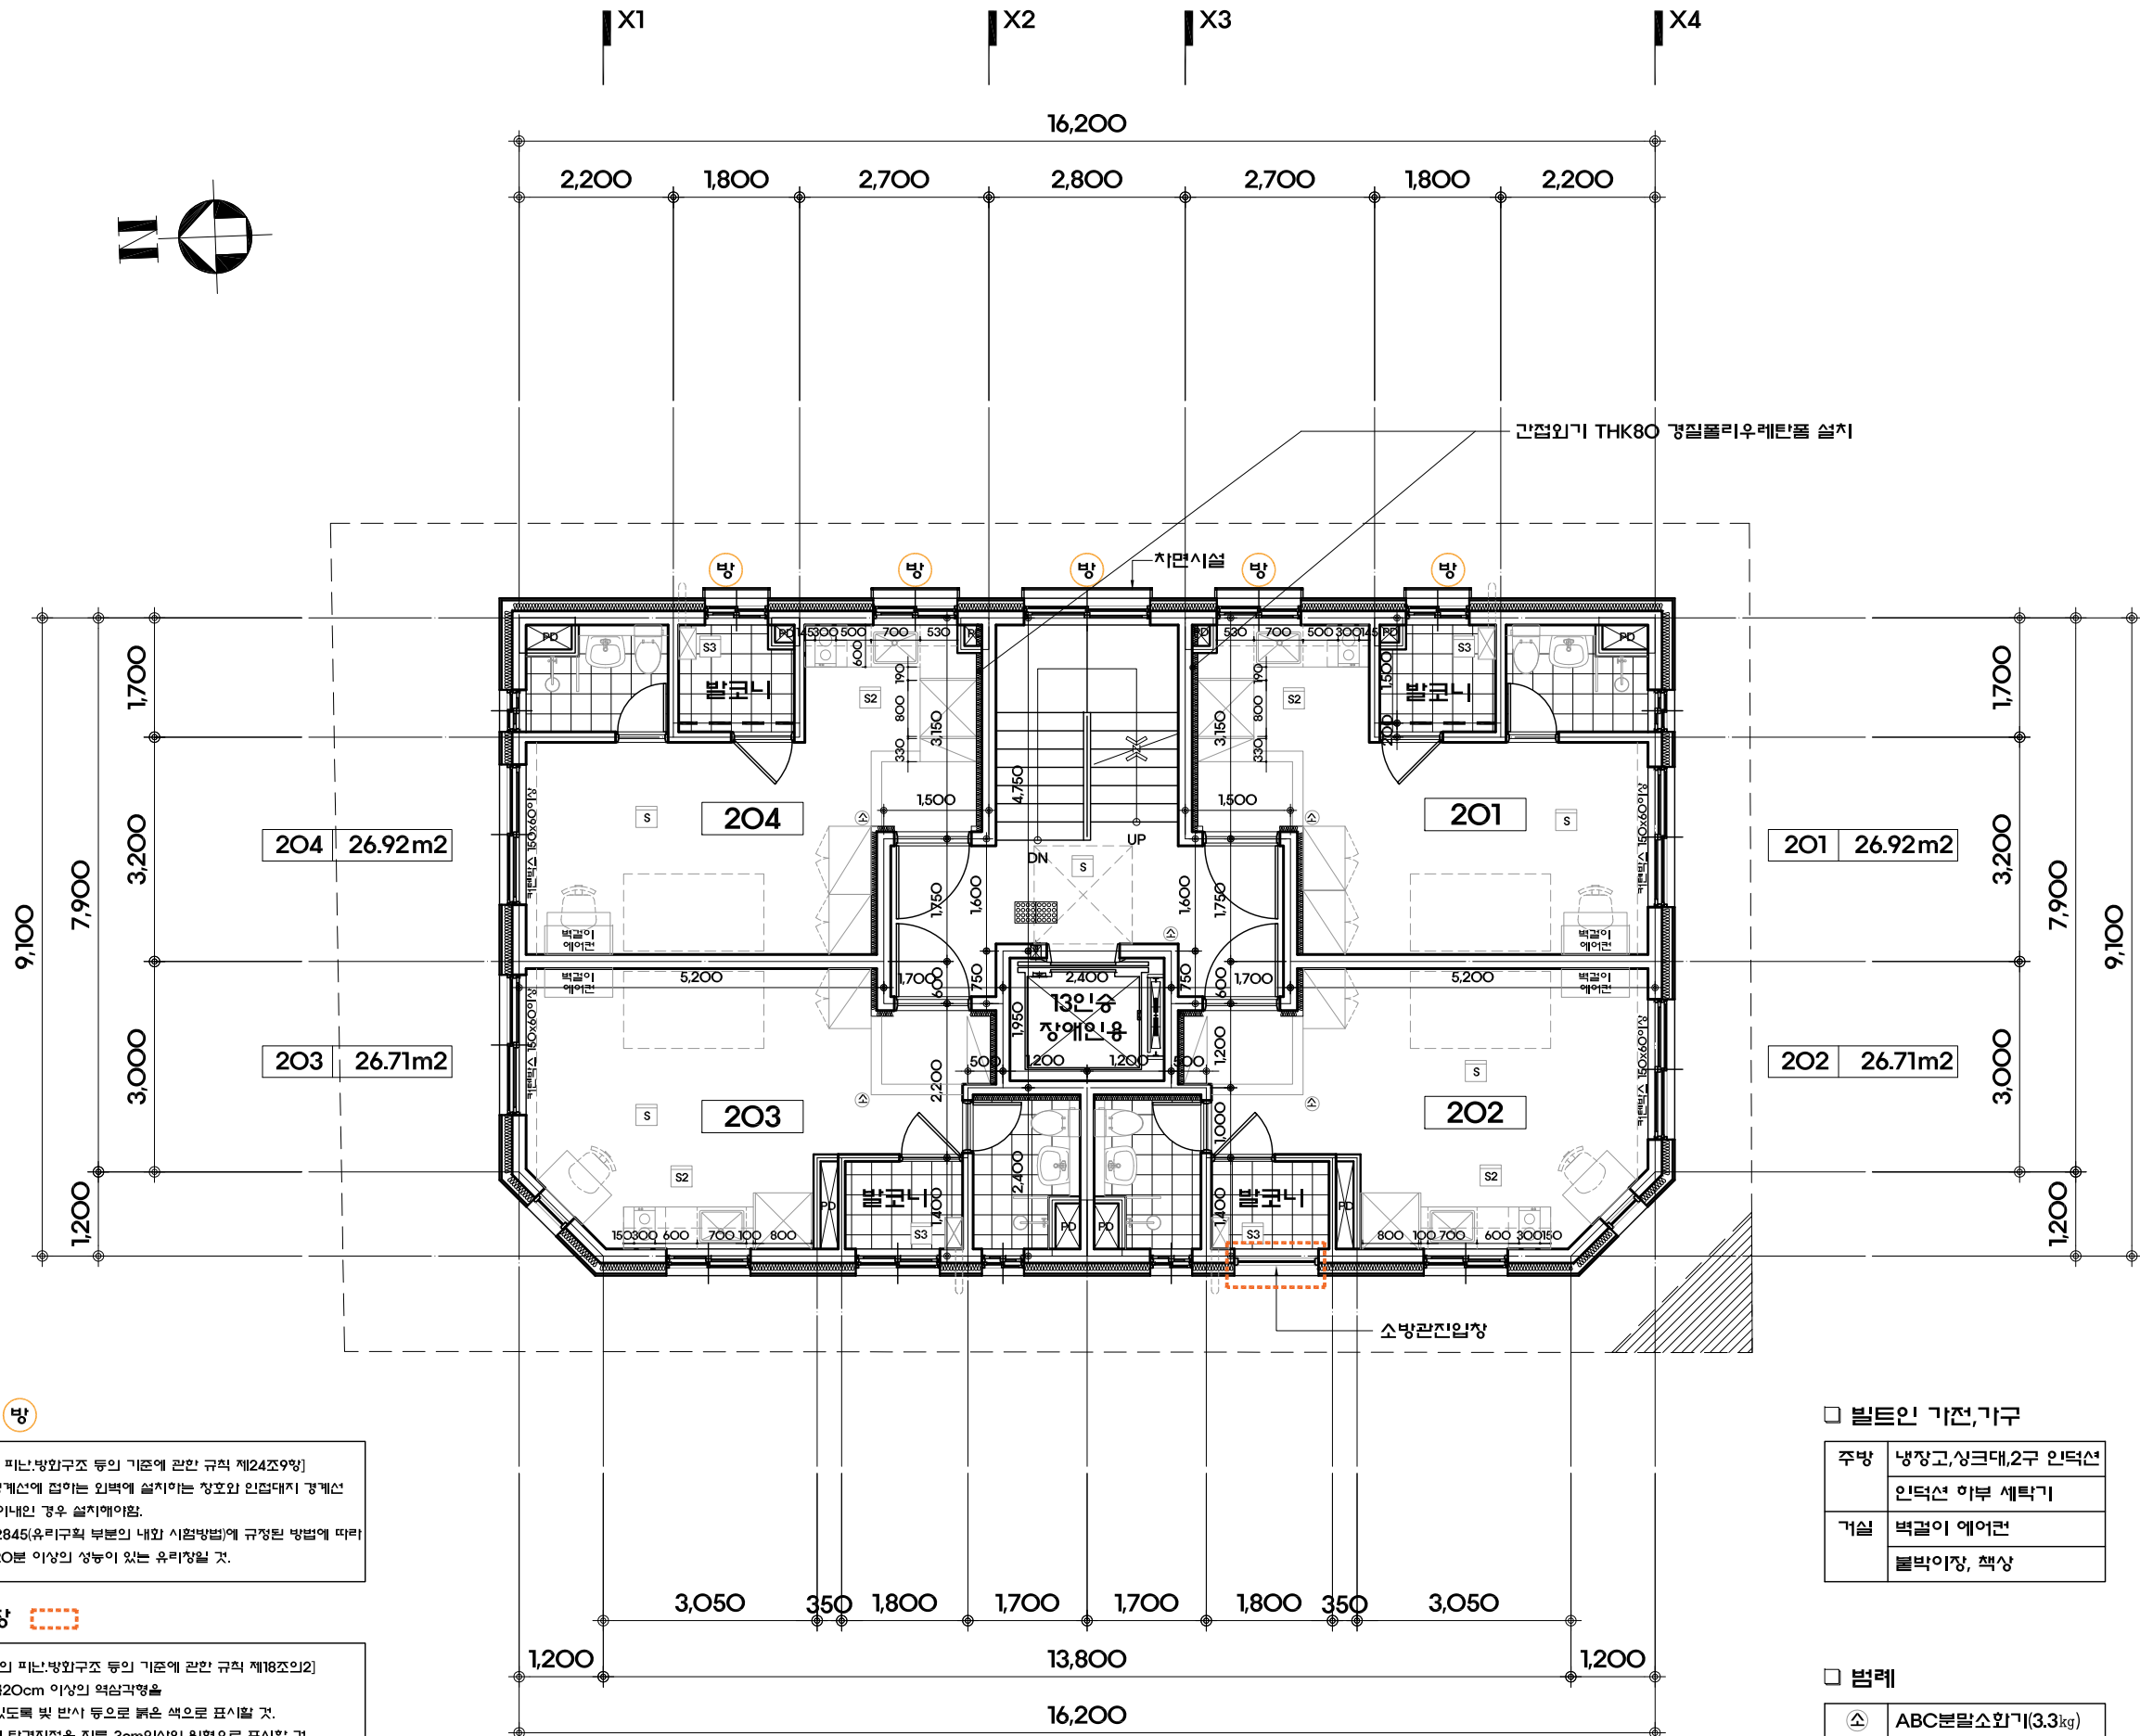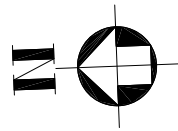

지상 2층 평면도

축척 : 1/100

방화유리창 방

*방화유리창 [건축물의 피난·방화구조 등의 기준에 관한 규칙 제24조9항]
-건축물의 인접 대지경계선에 접하는 외벽에 설치하는 창호와 인접대지 경계선 간의 거리가 1.5미터 이내인 경우 설치해야함.
-한국산업표준 KS F 2845(유리구획 부분의 내화 시험방법)에 규정된 방법에 따라 시험한 결과 비자질 20분 이상의 성능이 있는 유리창일 것.

소방관진입창

*소방관진입창 [건축물의 피난·방화구조 등의 기준에 관한 규칙 제18조의2]
-창문의 기둥에 제18조의2 이상의 역삼각형을 이간에도 알아볼 수 있도록 빛 반사 등으로 붉은 색으로 표시할 것.
-창문의 왼쪽 모서리에 타격지점을 지름 3cm이상의 원형으로 표시할 것.
-창문의 크기는 폭 90cm이상, 높이 1.2m 이상으로 하고, 실내 바닥면으로부터 창 상의 아랫부분까지의 높이는 80cm 이내로 할 것.
-1) 플로트판유리로서 그 두께가 6mm이상이란 것.
2) 강화유리 또는 배강도유리로서 그 두께가 5mm이상이란 것.
위의 2가지에 해당하는 유리로 구성된 이중유리로서 그 두께가 24mm이상이란 것.

발트인 가전,가구

주방	냉장고,싱크대,2구 인덕션
	인덕션 하부 세탁기
거실	벽걸이 에어컨
	불박이장, 책상

범례

△	ABC분말소화기(3.3kg)
S	단독경보감지기(연기)
S2	단독경보감지기(열)
S3	가스누설경보기(보일러실)

△		
△		
△		
△		
△		
△		

SYM.	DESCRIPTION OF REVISION	REVISED BY DATE
------	-------------------------	-----------------

ARCHITECTURAL DESIGNED BY
조 주 혜

STRUCTURAL DESIGNED BY
구 조 설 계

CIVIL DESIGNED BY
건 축 설 계

MECHANICAL DESIGNED BY
기 계 설 계

ELECTRICAL DESIGNED BY
전 기 설 계

LANDSCAPE DESIGNED BY
조 경 설 계

DRAWN BY
제 도

CHECKED BY 상 사	APPROVED BY 승 인
-------------------	--------------------

DATE
일 자 2025. 01.

PROJECT TITEL
사 업 명 칭

신사동 16-25번지
다세대주택 신축공사



NAME OF
도 면 명

지상 3층 평면도

SCALE
축 척 1/100

SHEET NO.
일련번호

DRAWING NO.
도면번호 A-203

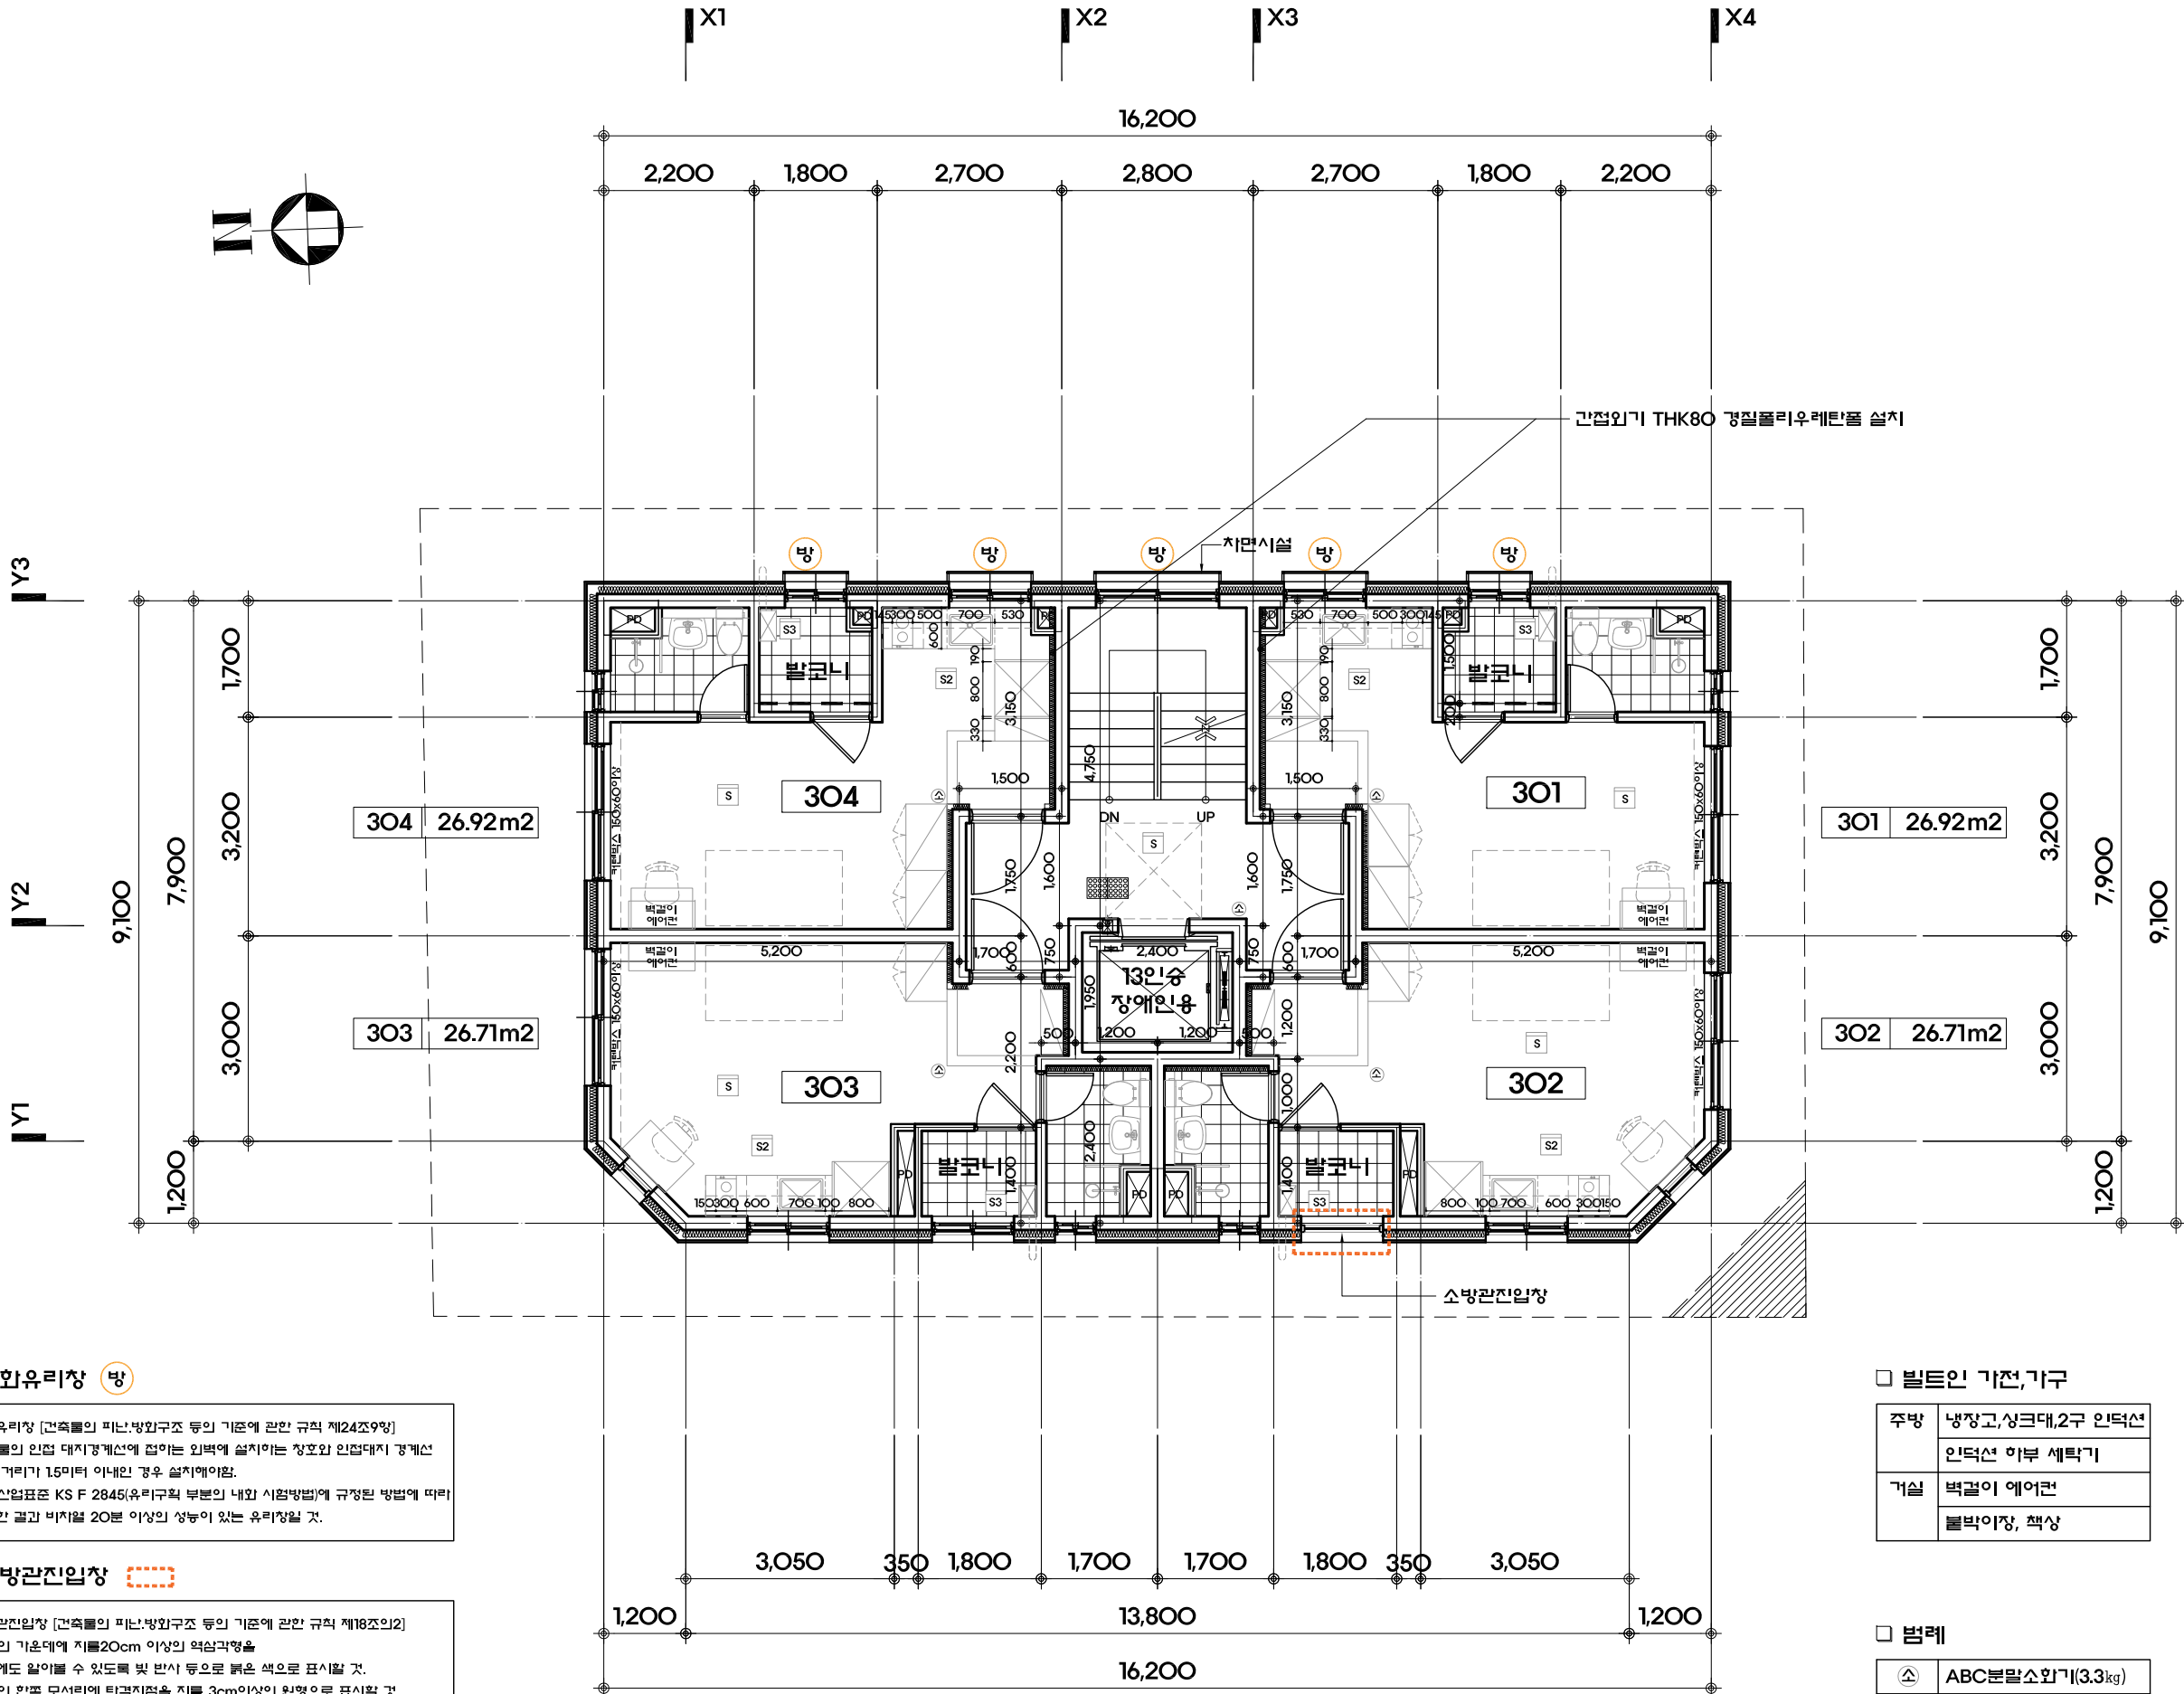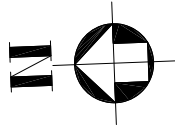

방화유리창 방

*방화유리창 [건축물의 피난·방화구조 등의 기준에 관한 규칙 제24조9항]
-건축물의 인접 대지경계선에 접하는 외벽에 설치하는 창호와 인접대지 경계선 간의 거리가 1.5미터 이내인 경우 설치해야함.
-한국산업표준 KS F 2845(유리구획 부분의 내화 시험방법)에 규정된 방법에 따라 시험한 결과 비자질 20분 이상의 성능이 있는 유리창일 것.

소방관진입창

*소방관진입창 [건축물의 피난·방화구조 등의 기준에 관한 규칙 제18조의2]
-창문의 기둥에 제18조의2 이상의 역삼각형을 이간에도 알아볼 수 있도록 빛 반사 등으로 붉은 색으로 표시할 것.
-창문의 왼쪽 모서리에 타격지점을 지름 3cm이상의 원형으로 표시할 것.
-창문의 크기는 폭 90cm이상, 높이 1.2m 이상으로 하고, 실내 바닥면으로부터 창 상의 아랫부분까지의 높이는 80cm 이내로 할 것.
-가) 플로트판유리로서 그 두께가 6mm이상이란 것.
2) 강화유리 또는 배강도유리로서 그 두께가 5mm이상이란 것.
위의 2가지에 해당하는 유리로 구성된 이중유리로서 그 두께가 24mm이상이란 것.

발트인 가전,가구

주방	냉장고,싱크대,2구 인덕션 인덕션 하부 세탁기
거실	벽걸이 에어컨 불박이장, 책상

범례

△	ABC분말소화기(3.3kg)
S	단독경보감지기(연기)
S2	단독경보감지기(열)
S3	가스누설경보기(보일러실)



지상 3층 평면도

축척 : 1/100

△		
△		
△		
△		
△		
△		
SYM.	DESCRIPTION OF REVISION	REVISED BY DATE

ARCHITECTURAL DESIGNED BY
조 주 혜

STRUCTURAL DESIGNED BY
구 조 설 계

CIVIL DESIGNED BY
건 축 설 계

MECHANICAL DESIGNED BY
기 계 설 계

ELECTRICAL DESIGNED BY
전 기 설 계

LANDSCAPE DESIGNED BY
조 경 설 계

DRAWN BY
제 도

CHECKED BY 상 사	APPROVED BY 승 인
-------------------	--------------------

DATE 일 자	2025. 01.
-------------	-----------

PROJECT TITLE
사 업 명 칭

신사동 16-25번지
다세대주택 신축공사

NAME OF
도 면 명



지상 4층 평면도

SCALE
축 척

SHEET NO.
일련번호

DRAWING NO.
도면번호

A-204

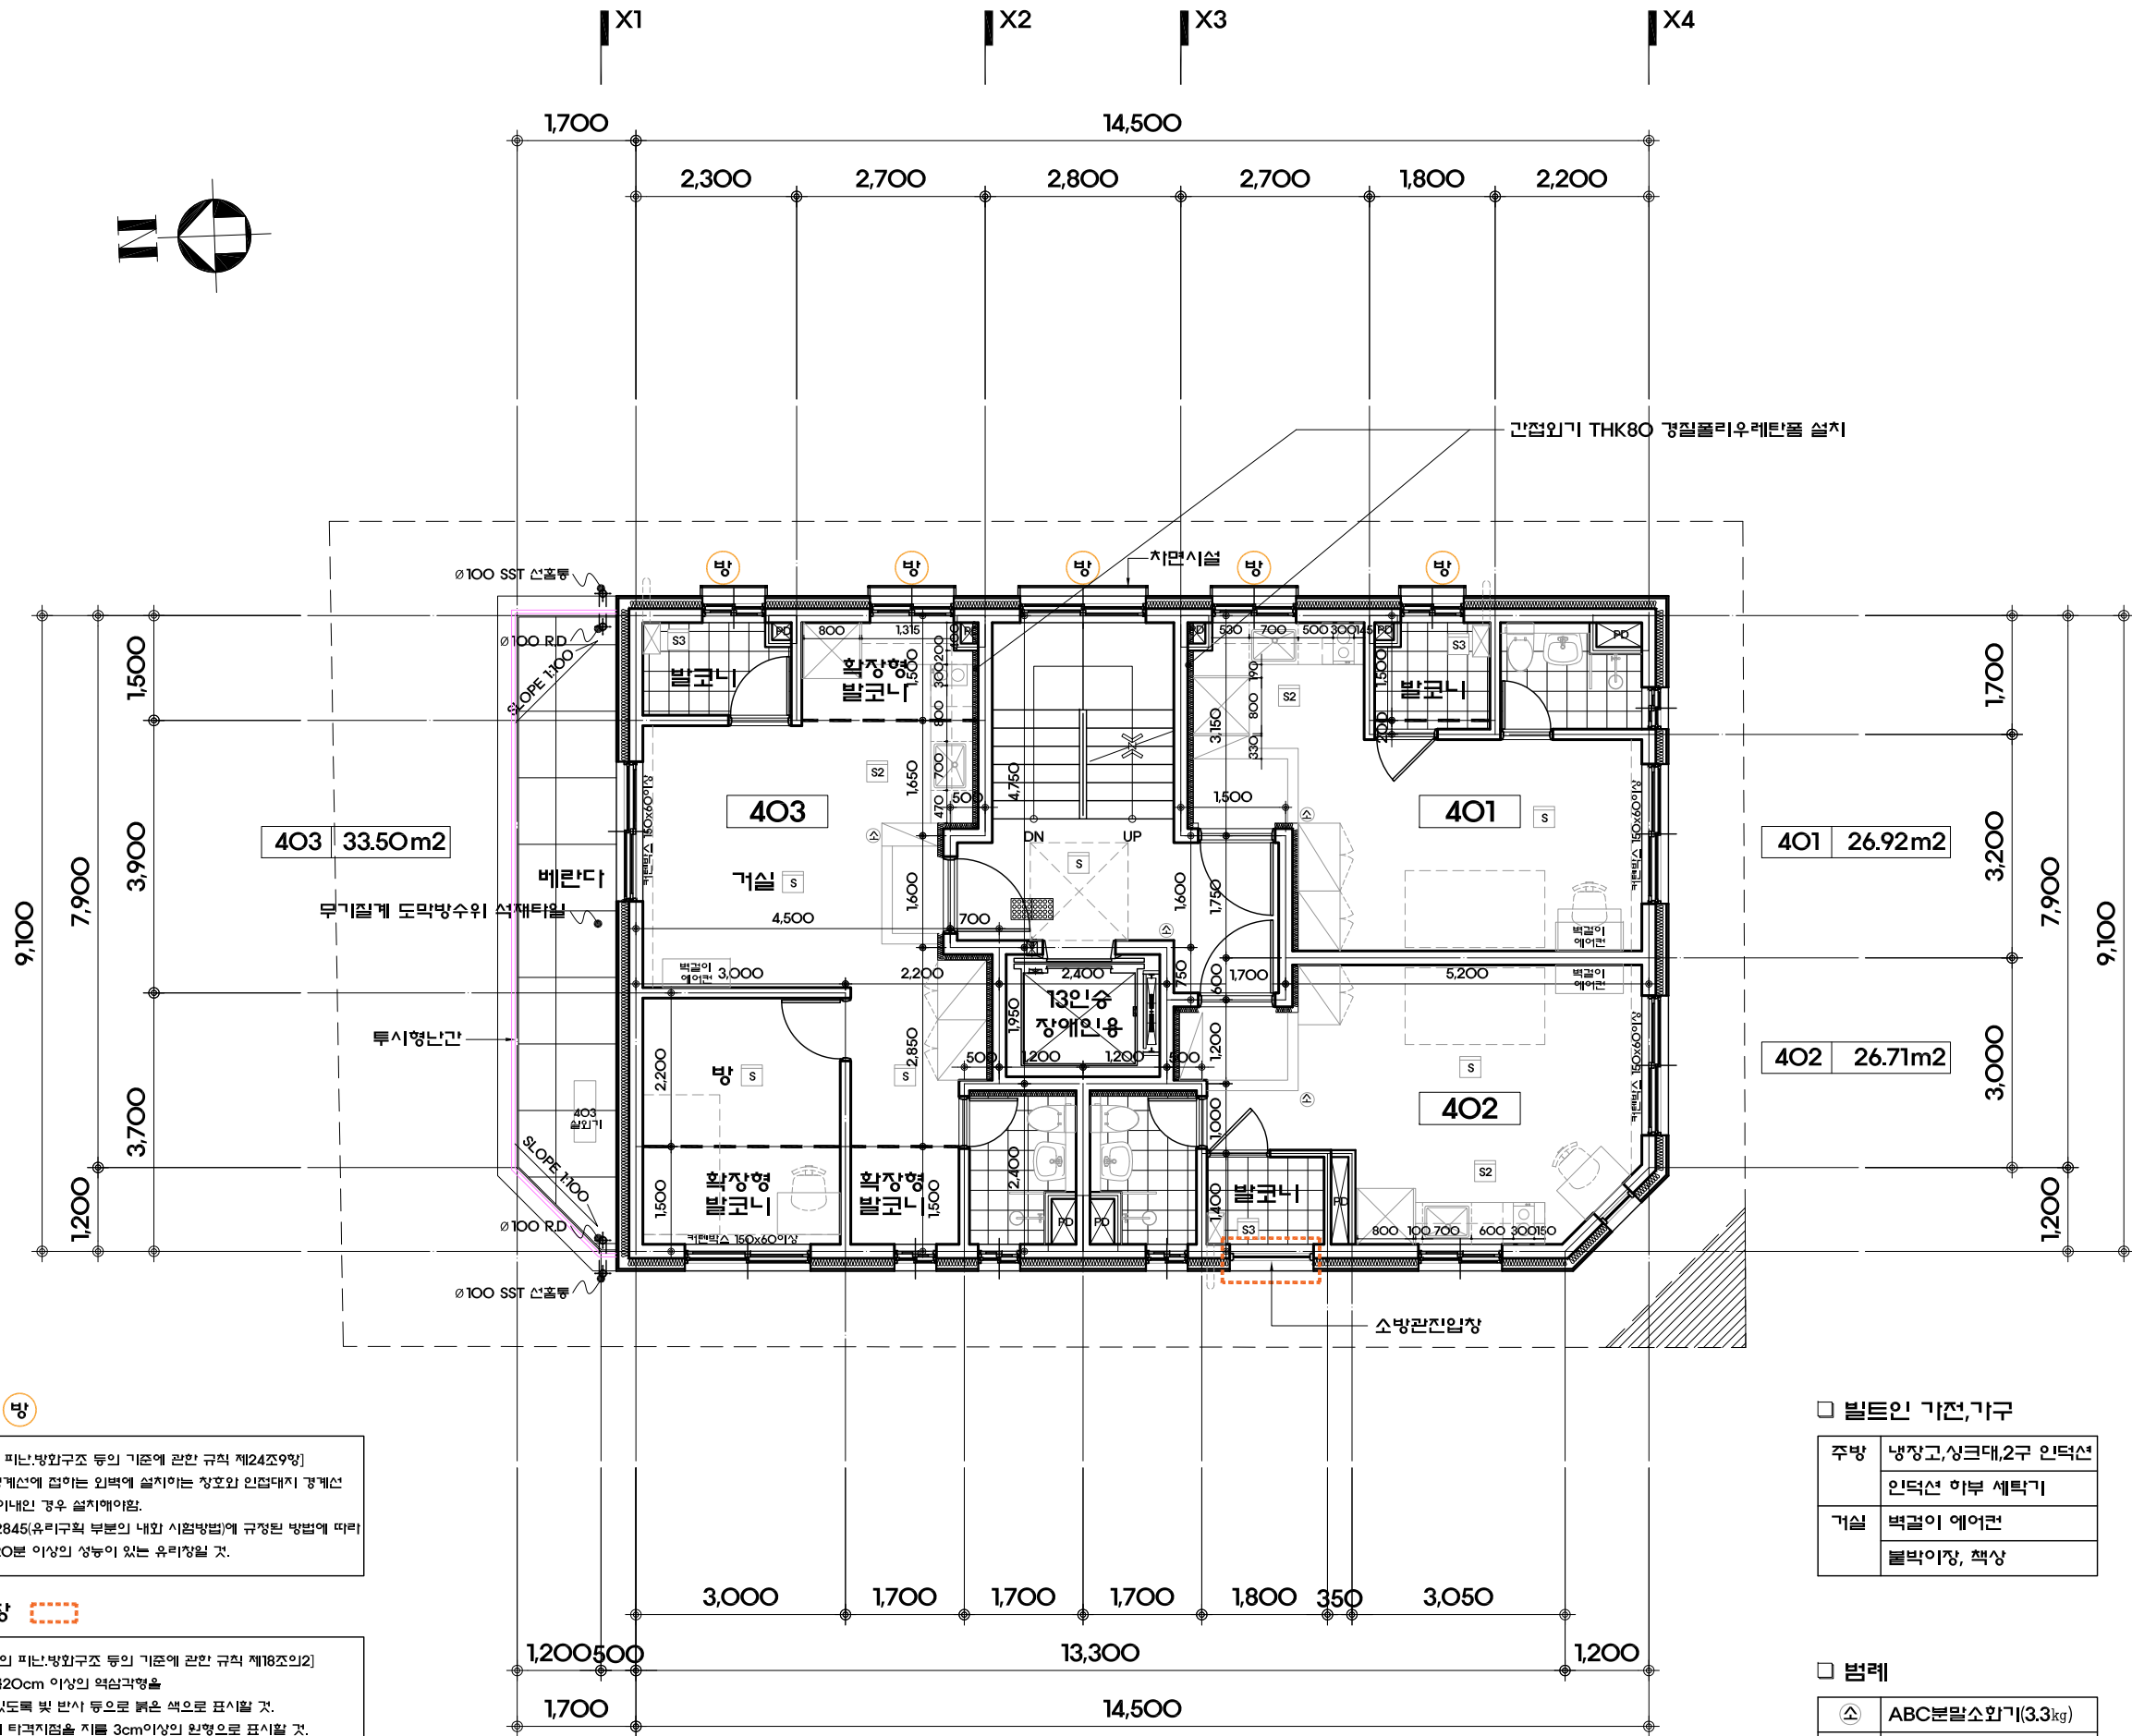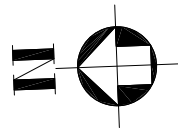

□ 방화유리창 방

*방화유리창 [건축물의 피난·방화구조 등의 기준에 관한 규칙 제24조9항]
-건축물의 인접 대지경계선에 접하는 외벽에 설치하는 창호와 인접대지 경계선 간의 거리가 1.5미터 이내인 경우 설치해야함.
-한국산업표준 KS F 2845(유리구조 부분의 내화 시험방법)에 규정된 방법에 따라 시험한 결과 비잔열 20분 이상의 성능이 있는 유리창일 것.

□ 소방관진입장

*소방관진입장 [건축물의 피난·방화구조 등의 기준에 관한 규칙 제18조의2]
-창문의 기둥에 지름20cm 이상의 역삼각형을 이간에도 알아볼 수 있도록 빛 반사 등으로 붉은 색으로 표시할 것.
-창문의 한쪽 모서리에 타격지점을 지름 3cm이상의 원형으로 표시할 것.
-창문의 크기는 폭 90cm이상, 높이 1.2m 이상으로 하고, 실내 바닥면으로부터 창 상의 아랫부분까지의 높이는 80cm 이내로 할 것.
-1) 플로트판유리로서 그 두께가 6mm이상이면 것.
2) 강화유리 또는 배강도유리로서 그 두께가 5mm이상이면 것.
위의 2가지에 해당하는 유리로 구성된 이중유리로서 그 두께가 24mm이상이면 것.

□ 발트인 가전,가구

주방	냉장고,싱크대,2구 인덕션 인덕션 하부 세탁기
거실	벽걸이 에어컨 불박이장, 책상

□ 범례

△	ABC분말소화기(3.3kg)
S	단독경보감지기(전기)
S2	단독경보감지기(열)
S3	가스누설경보기(보일러실)

지상 4층 평면도

축척 : 1/100

△		
△		
△		
△		
△		
△		
SYM.	DESCRIPTION OF REVISION	REVISED BY DATE

ARCHITECTURAL DESIGNED BY
조 주 혜

STRUCTURAL DESIGNED BY
구 조 설 계

CIVIL DESIGNED BY
건 축 설 계

MECHANICAL DESIGNED BY
기 계 설 계

ELECTRICAL DESIGNED BY
전 기 설 계

LANDSCAPE DESIGNED BY
조 경 설 계

DRAWN BY
제 도

CHECKED BY 상 사	APPROVED BY 승 인

DATE
일 자 2025. 01.



PROJECT TITLE
사 업 명 칭
신사동 16-25번지
다세대주택 신축공사

NAME OF
도 면 명
지상 5층 평면도

SCALE
축 척 1/100

SHEET NO.
일련번호

DRAWING NO.
도면번호 A-205

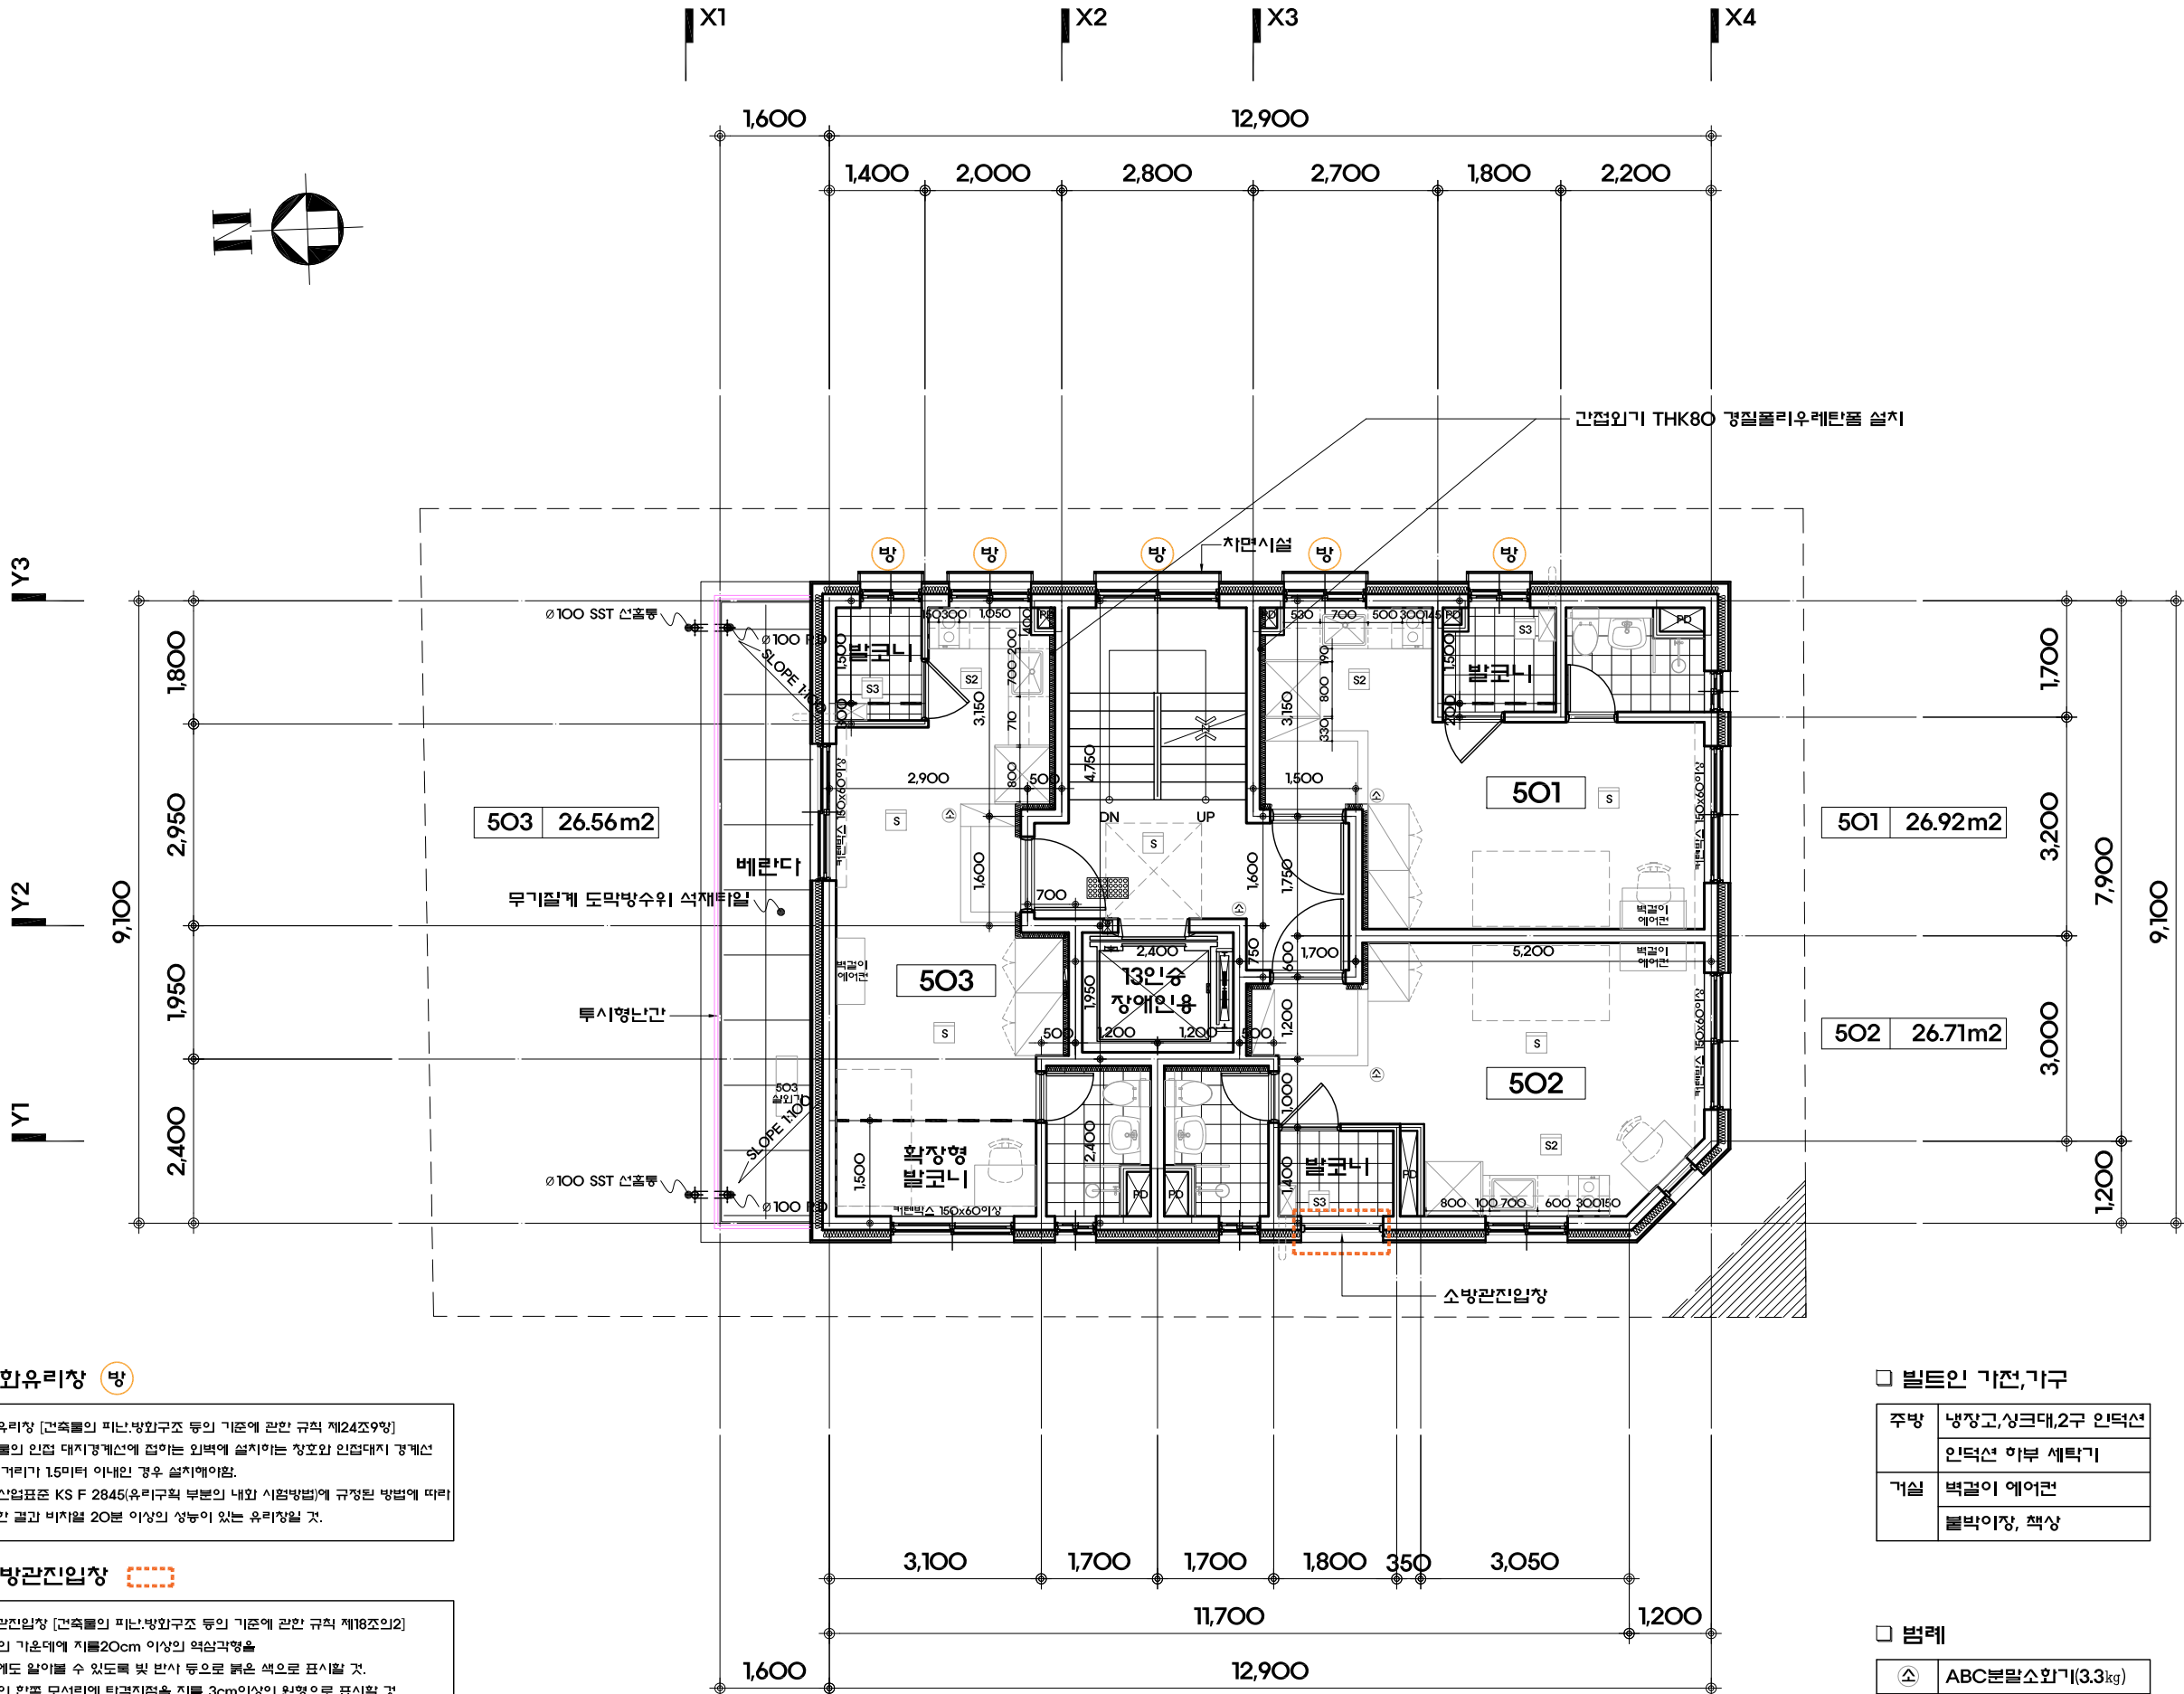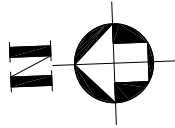

방화유리창 방

*방화유리창 [건축물의 피난·방화구조 등의 기준에 관한 규칙 제24조9항]
-건축물의 인접 대지경계선에 접하는 외벽에 설치하는 창호와 인접대지 경계선 간의 거리가 1.5미터 이내인 경우 설치해야함.
-한국산업표준 KS F 2845(유리구조 부분의 내화 시험방법)에 규정된 방법에 따라 시험한 결과 비파괴 20분 이상의 성능이 있는 유리창일 것.

소방관진입창

*소방관진입창 [건축물의 피난·방화구조 등의 기준에 관한 규칙 제18조2]
-창문의 기둥에 지름20cm 이상의 역삼각형을 이간에도 알아볼 수 있도록 빛 반사 등으로 붉은 색으로 표시할 것.
-창문의 왼쪽 모서리에 타격지점을 지름 3cm이상의 원형으로 표시할 것.
-창문의 크기는 폭 90cm이상, 높이 1.2m 이상으로 하고, 실내 바닥면으로부터 창 상의 아랫부분까지의 높이는 80cm 이내로 할 것.
-1) 플로트유리로서 그 두께가 6mm이었던 것.
2) 강화유리 또는 배강도유리로서 그 두께가 5mm이었던 것.
위의 2가지에 해당하는 유리로 구성된 이중유리로서 그 두께가 24mm이었던 것.



발트인 가전,가구

주방	냉장고,싱크대,2구 인덕션 인덕션 하부 세탁기
거실	벽걸이 에어컨 불박이장, 책상

범례

△	ABC분말소화기(3.3kg)
S	단독경보감지기(전기)
S2	단독경보감지기(열)
S3	가스누설경보기(보일러실)

지상 5층 평면도
축척 : 1/100

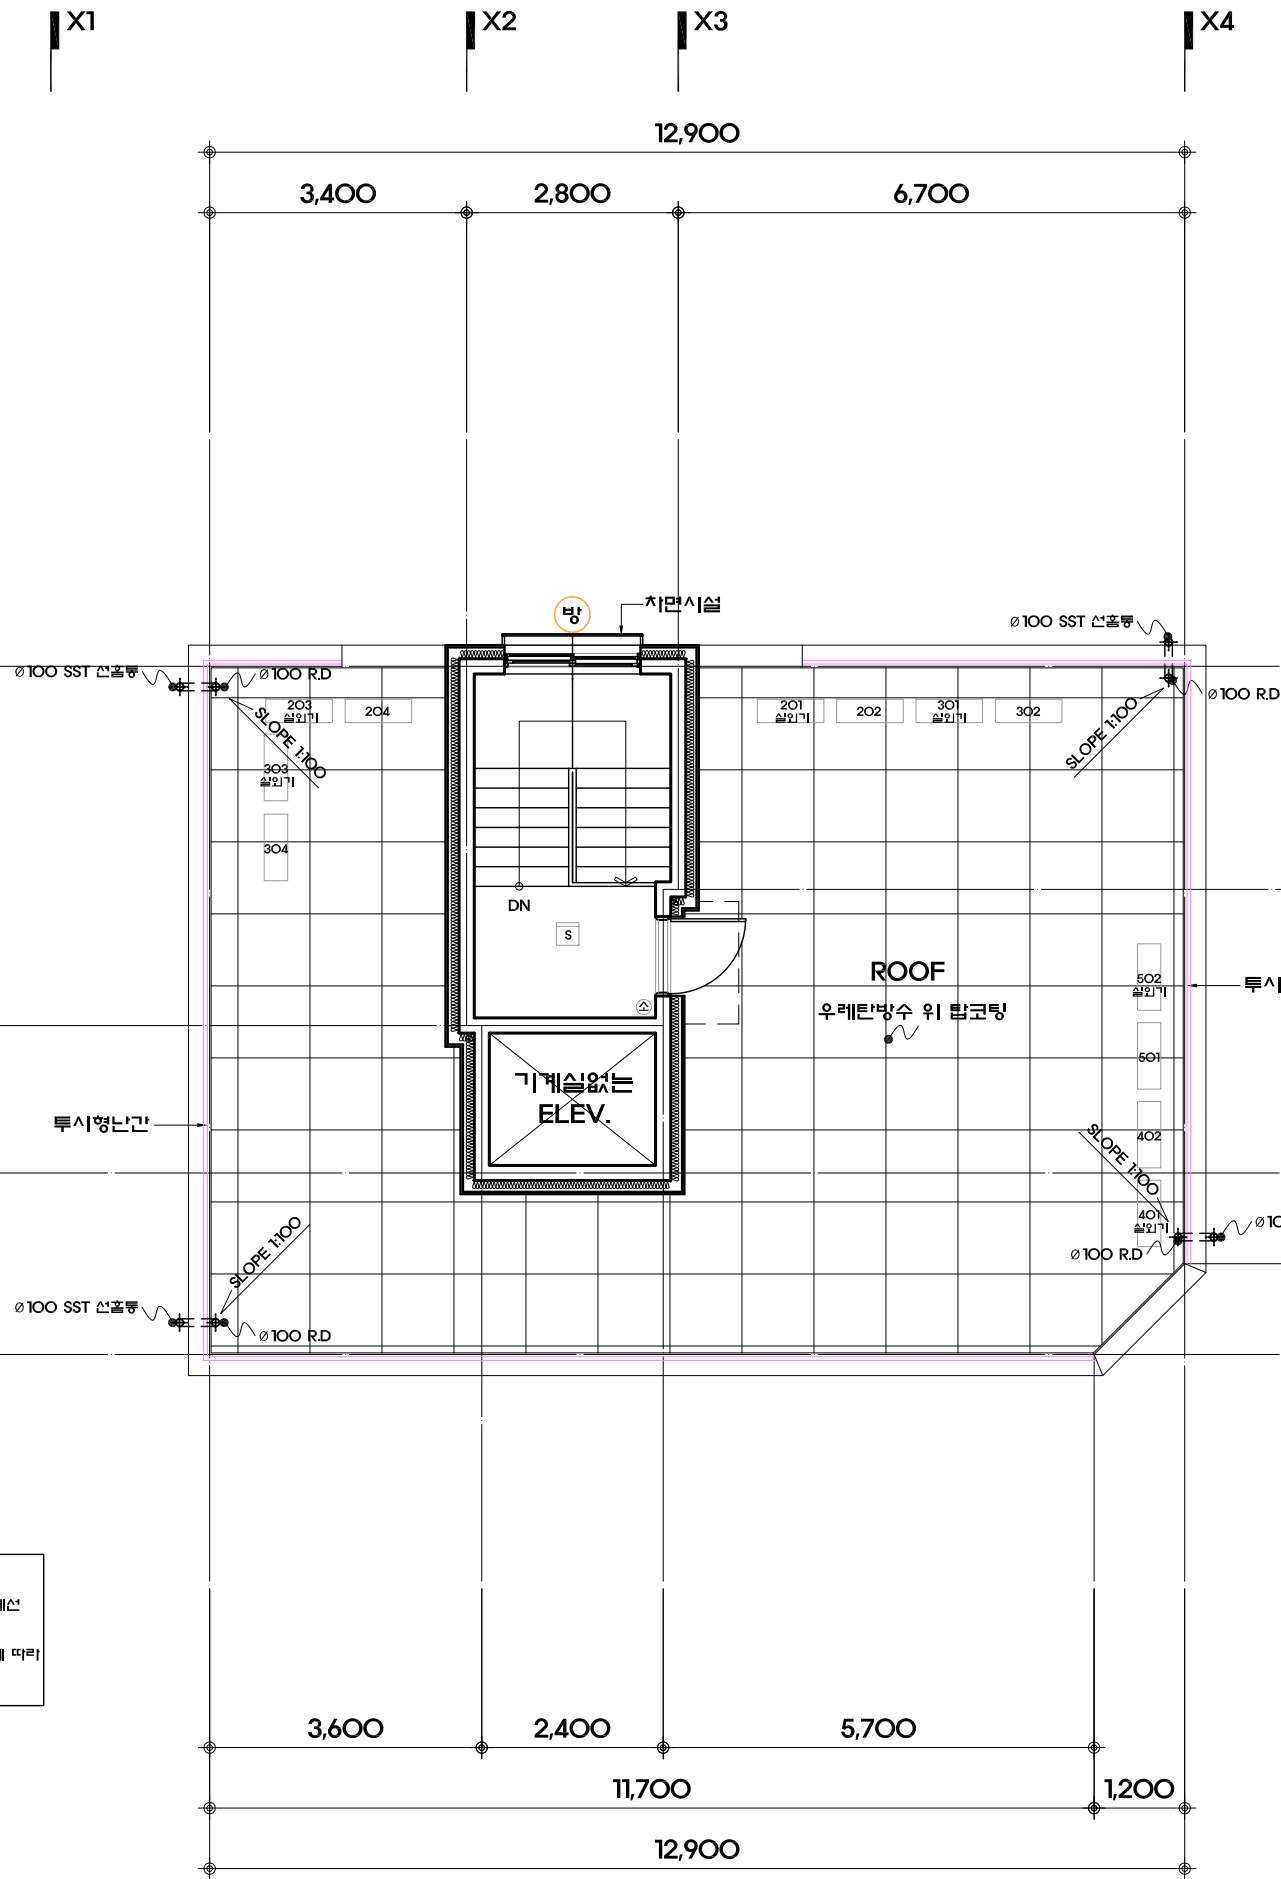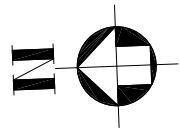

□ 방화유리창 방

*방화유리창 [건축물의 피난·방화구조 등의 기준에 관한 규칙 제24조9항]
-건축물의 인접 대지경계선에 접하는 인벽에 설치하는 창호와 인접대지 경계선 간의 거리가 1.5미터 이내인 경우 설치해야함.
-한국산업표준 KS F 2845(유리구조 부분의 내화 시험방법)에 규정된 방법에 따라 시험한 결과 비자질 20분 이상의 성능이 있는 유리창일 것.



옥탑층 평면도

축척 : 1/100

□ 범례

△	ABC분말소화기(3.3kg)
□	단독경보형감지기(연기)



옥탑지붕층 평면도

축척 : 1/100



PHONE : (02)3494-3323/3324
FAX : (02)3494-3329
E-MAIL : soo2004s@hanmail.net

PROJECT NO.
사업번호

NOTE
노 트

REMARKS
주 기 사 랑

△		
△		
△		
△		
△		
△		
SYMBOL	DESCRIPTION OF REVISION	REVISED BY DATE

ARCHITECTURAL DESIGNED BY
건축 설계 조 주 혜

STRUCTURAL DESIGNED BY
구조 설계

CIVIL DESIGNED BY
건축 설계

MECHANICAL DESIGNED BY
기계 설계

ELECTRICAL DESIGNED BY
전기 설계

LANDSCAPE DESIGNED BY
조경 설계

DRAWN BY
제 도

CHECKED BY 상 사	APPROVED BY 승 인
-------------------	--------------------

DATE
일 자 2025. 01.

PROJECT TITLE
사 업 명 칭
신사동 16-25번지
다세대주택 신축공사

NAME OF
도 면 명

옥탑층 평면도

SCALE
축 척 1/100

SHEET NO.
일련번호

DRAWING NO.
도면번호 A-206

△		
△		
△		
△		
△		
△		

SYM.	DESCRIPTION OF REVISION	REVISED BY DATE
------	-------------------------	-----------------

ARCHITECTURAL DESIGNED BY
조 주 혜

STRUCTURAL DESIGNED BY
구 조 실 계

CIVIL DESIGNED BY
건 축 실 계

MECHANICAL DESIGNED BY
기 계 실 계

ELECTRICAL DESIGNED BY
전 기 실 계

LANDSCAPE DESIGNED BY
조 경 실 계

DRAWN BY
제 도

CHECKED BY 상 사	APPROVED BY 승 인
-------------------	--------------------

DATE
일 자 2025. 01.



PROJECT TITLE
사 업 명 칭
신사동 16-25번지
다세대주택 신축공사

NAME OF
도 면 명
정면도 및 우측면도

SCALE
축 적 1/150

SHEET NO.
일련번호

DRAWING NO.
도면번호 A-207

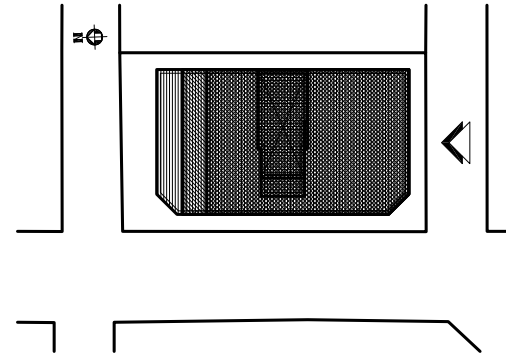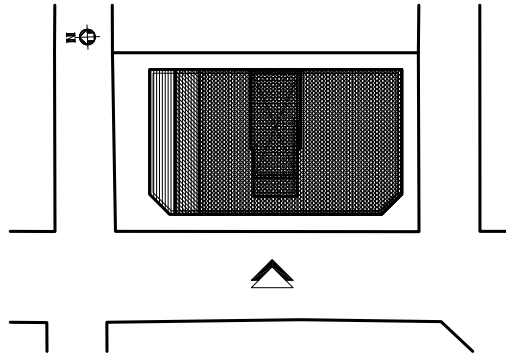

X1

X2


X3

X4

Y1

Y2

Y3

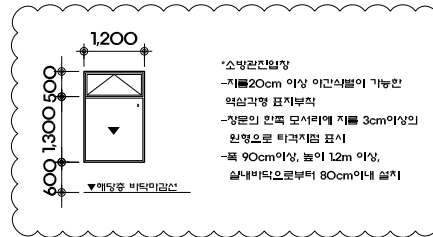

THK10 STEEL PLATE
아연도금위 함마톤도장

마천석 버너구이
포천석 고운다듬

THK24 복층유리(소방관진입창)
THK39 단열삼중유리

THK22 Low-E 복층유리

포천석 고운다듬

옥탑지붕층

최고높이

옥탑층

지상 5층

지상 4층

지상 3층

지상 2층

지상 1층
G.L±0.0

포천석 고운다듬

Ø100 SST 선홀통

정면도(서측)

축척 : 1/150

우측면도(남측)

축척 : 1/150

△		
△		
△		
△		
△		
△		
SYM.	DESCRIPTION OF REVISION	REVISED BY DATE

ARCHITECTURAL DESIGNED BY
조 주 혜

STRUCTURAL DESIGNED BY
구 조 실 계

CIVIL DESIGNED BY
건 축 실 계

MECHANICAL DESIGNED BY
기 계 실 계

ELECTRICAL DESIGNED BY
전 기 실 계

LANDSCAPE DESIGNED BY
조 경 실 계

DRAWN BY
제 도

CHECKED BY 상 사	APPROVED BY 승 인
-------------------	--------------------

DATE
일 자 2025. 01.


PROJECT TITEL
사 업 명 칭
신사동 16-25번지
다세대주택 신축공사

NAME OF
도 면 명
배면도 및 좌측면도

SCALE
축 척 1/150

SHEET NO.
일련번호

DRAWING NO.
도면번호 A-208

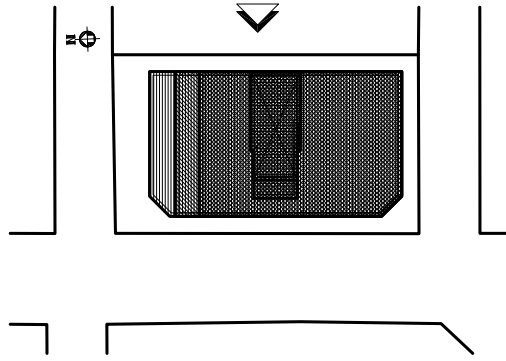

X4

X3

X2

X1

THK22 Low-E 복층유리
포천석 고운다툼

THK10 STEEL PLATE
아연도금위 합마톤도장
마천석 버너구이

옥탑지붕층

최고높이

옥탑층

지상 5층

지상 4층

지상 3층


지상 2층

지상 1층
G.L±0.0

Ø100 SST 선홀통

배 면 도(동측)

축척 : 1/150

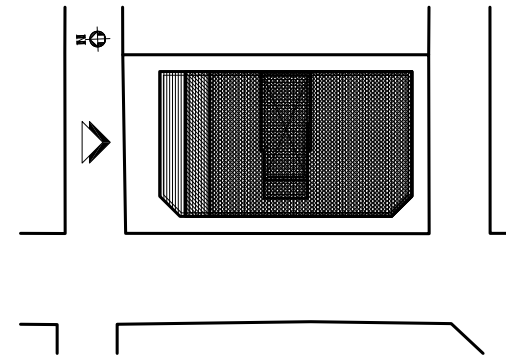

Y3

Y2

Y1

THK22 Low-E 복층유리

포천석 고운다툼
마천석 버너구이
포천석 고운다툼

Ø100 SST 선홀통

좌 측 면 도(북측)

축척 : 1/150