

1. 조감도



2. 건축개요 및 현황도

■ 건축개요

- 설 계 명 : 은평구 구산동 24-13 도시형생활주택(원룸형) 신축공사
- 대 지 위 치 : 서울특별시 은평구 구산동 24-13
- 지 역 지 구 : 제2종일반주거지역
- 건 물 용 도 : 도시형생활주택(원룸형)
- 건 물 규 모 : 지상5층
- 대 지 면 적 : 236.34 m²
- 건 축 면 적 : 141.36 m²
- 연 면 적 : 471.43 m²
- 건 폐 율 : 60%(법규) / 59.81%
- 용 적 율 : 200%(법규) / 199.47%
- 최 고 높 이 : 14.70m
- 건 물 구 조 : 철근콘크리트구조
- 주 차 대 수 : 6.8대(법정) / 7대
- 조 경 면 적 : 12.30 m² 이상(5%) / 15.82 m² (6.69%)



■ 위치도




■ 주변현황도

3. 입면도




* 본 상기도면은 디자인심의시 제출된 심의도면이며 설계도면과 일부 상이한 참조용이며 설계도면이 우선함

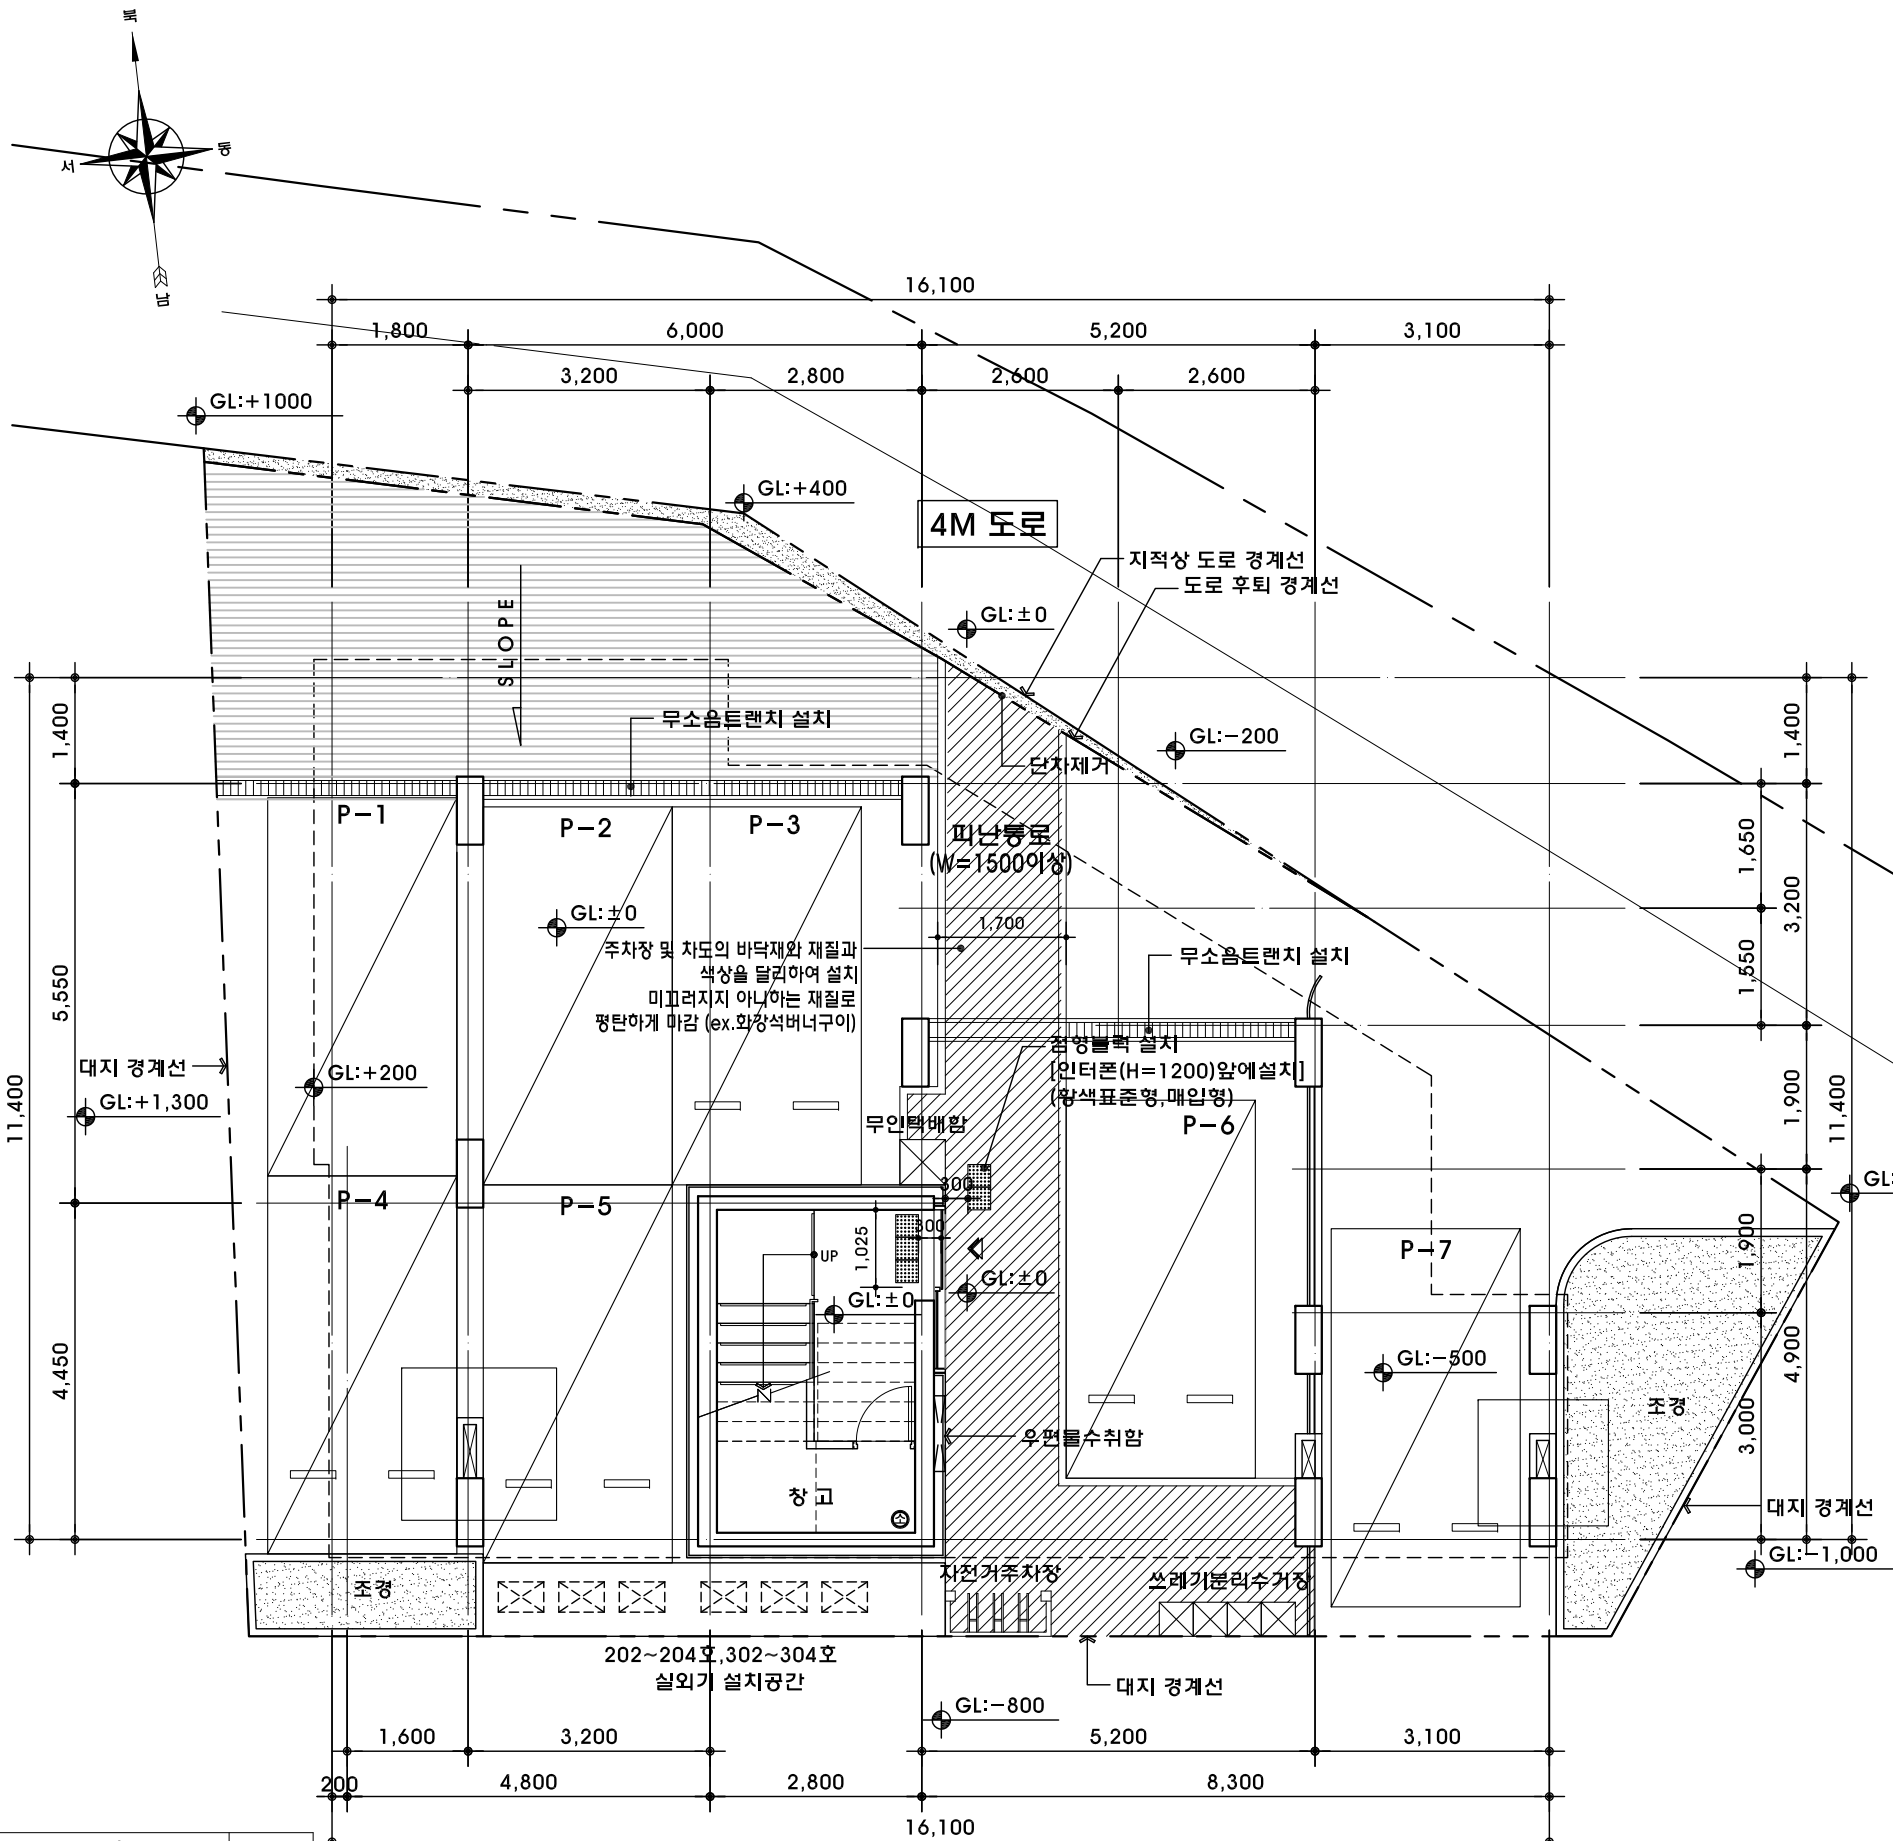

■ 주 기

건	1 (외부)	주차장내 CCTV,쓰레기분리수거,자전거보관대 설치
		우편함 설치 (세대전용, 공용, 반송용, 폐건전지함 구분 설치)
		세대 테라스 설치시 세대간 분리벽 계획
		세대 발코니 설치시 차양시설 설치
		세대내 비디오폰 설치
축	2 (계단실)	세대 현관문 도어체크 및 스톱퍼 설치
		계단참의 현관과 계단 이격거리 (최소600mm이상)
		세대내 욕실, 휴지걸이 매립형 설치
축	3 (내부)	불박이 가구 내부 다용도 수납가능토록 수평 이동 칸막이 설치
		에어컨 실외기 설치위치 및 에어컨 콘센트, 냉매 및 배수관 위치 도면표기
		⊙ - 에어컨 콘센트 표기
축	4 (시공)	콘크리트 폼타이 제거 후 마감공사 시공 (방수, 단열재 시공 등)
		욕실 & 다용도실 스위치 : 문 열리는 방향으로 시공
		주차장 차량 진출입구간,화장실 무소음트렌치 시공
축	5 (마감)	-직접외기(외벽)에 면한 실내벽면 단열재
		[아이소핑크(10mm) + 석고보드 마감도면 표기]
		-간접외기(계단실,복도)에 면한 실내벽면 단열재
		[경질우레탄폼(80mm) + 석고보드 마감도면 표기]
구	조	*기타 실내 벽면 시멘트 미장 마감
		1 철근 : fy=400Mpa
		콘크리트 : fck=24Mpa
		2 스라브두께 : 210mm (복배근)
전	기	외벽벽두께 : 180mm (복배근)
		코아벽두께 : 180mm (복배근)
		세대벽두께 : 180mm (복배근)
		1 -콘센트 설치 (바닥 마감선 기준)
전	기	[거실] 스탠드형 에어컨 : 350
		[안방] 벽걸이형 에어컨 : 1900
		[화장실] 양변기 옆 : 900
		[주방] 조리대 : 중양 / 냉장고 : 350 / 후드 : 2100
비	고	2 -비디오폰(VP),보일러온도조절기(B), 스위치(S) 설치 (거실 아트홀 위치)
		3 -위치 표기
		에어컨 실외기
		에어컨 콘센트
비	고	냉매, 배수관
		우편함 규격은 관련법규에 맞추어 적절한 위치에 설치하고
		세대전용,공용,반송용,폐건전지함으로 구분 설치한다.
		난간대에 국기봉을 설치한다
비	고	Ⓢ : 확장형 발코니

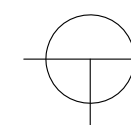


지상 1층 평면도

SCALE = 1/100


* 주 기 *

심볼	내 용	비 고
○	열식 단독경보형 감지기 (형식승인품)	
□	연기식 단독경보형 감지기 (형식승인품)	
⊙	가스누출 경보기	
⊕	ABC 분말 소화기	
Ⓐ	차면시설	
♥	소방관 진입장	

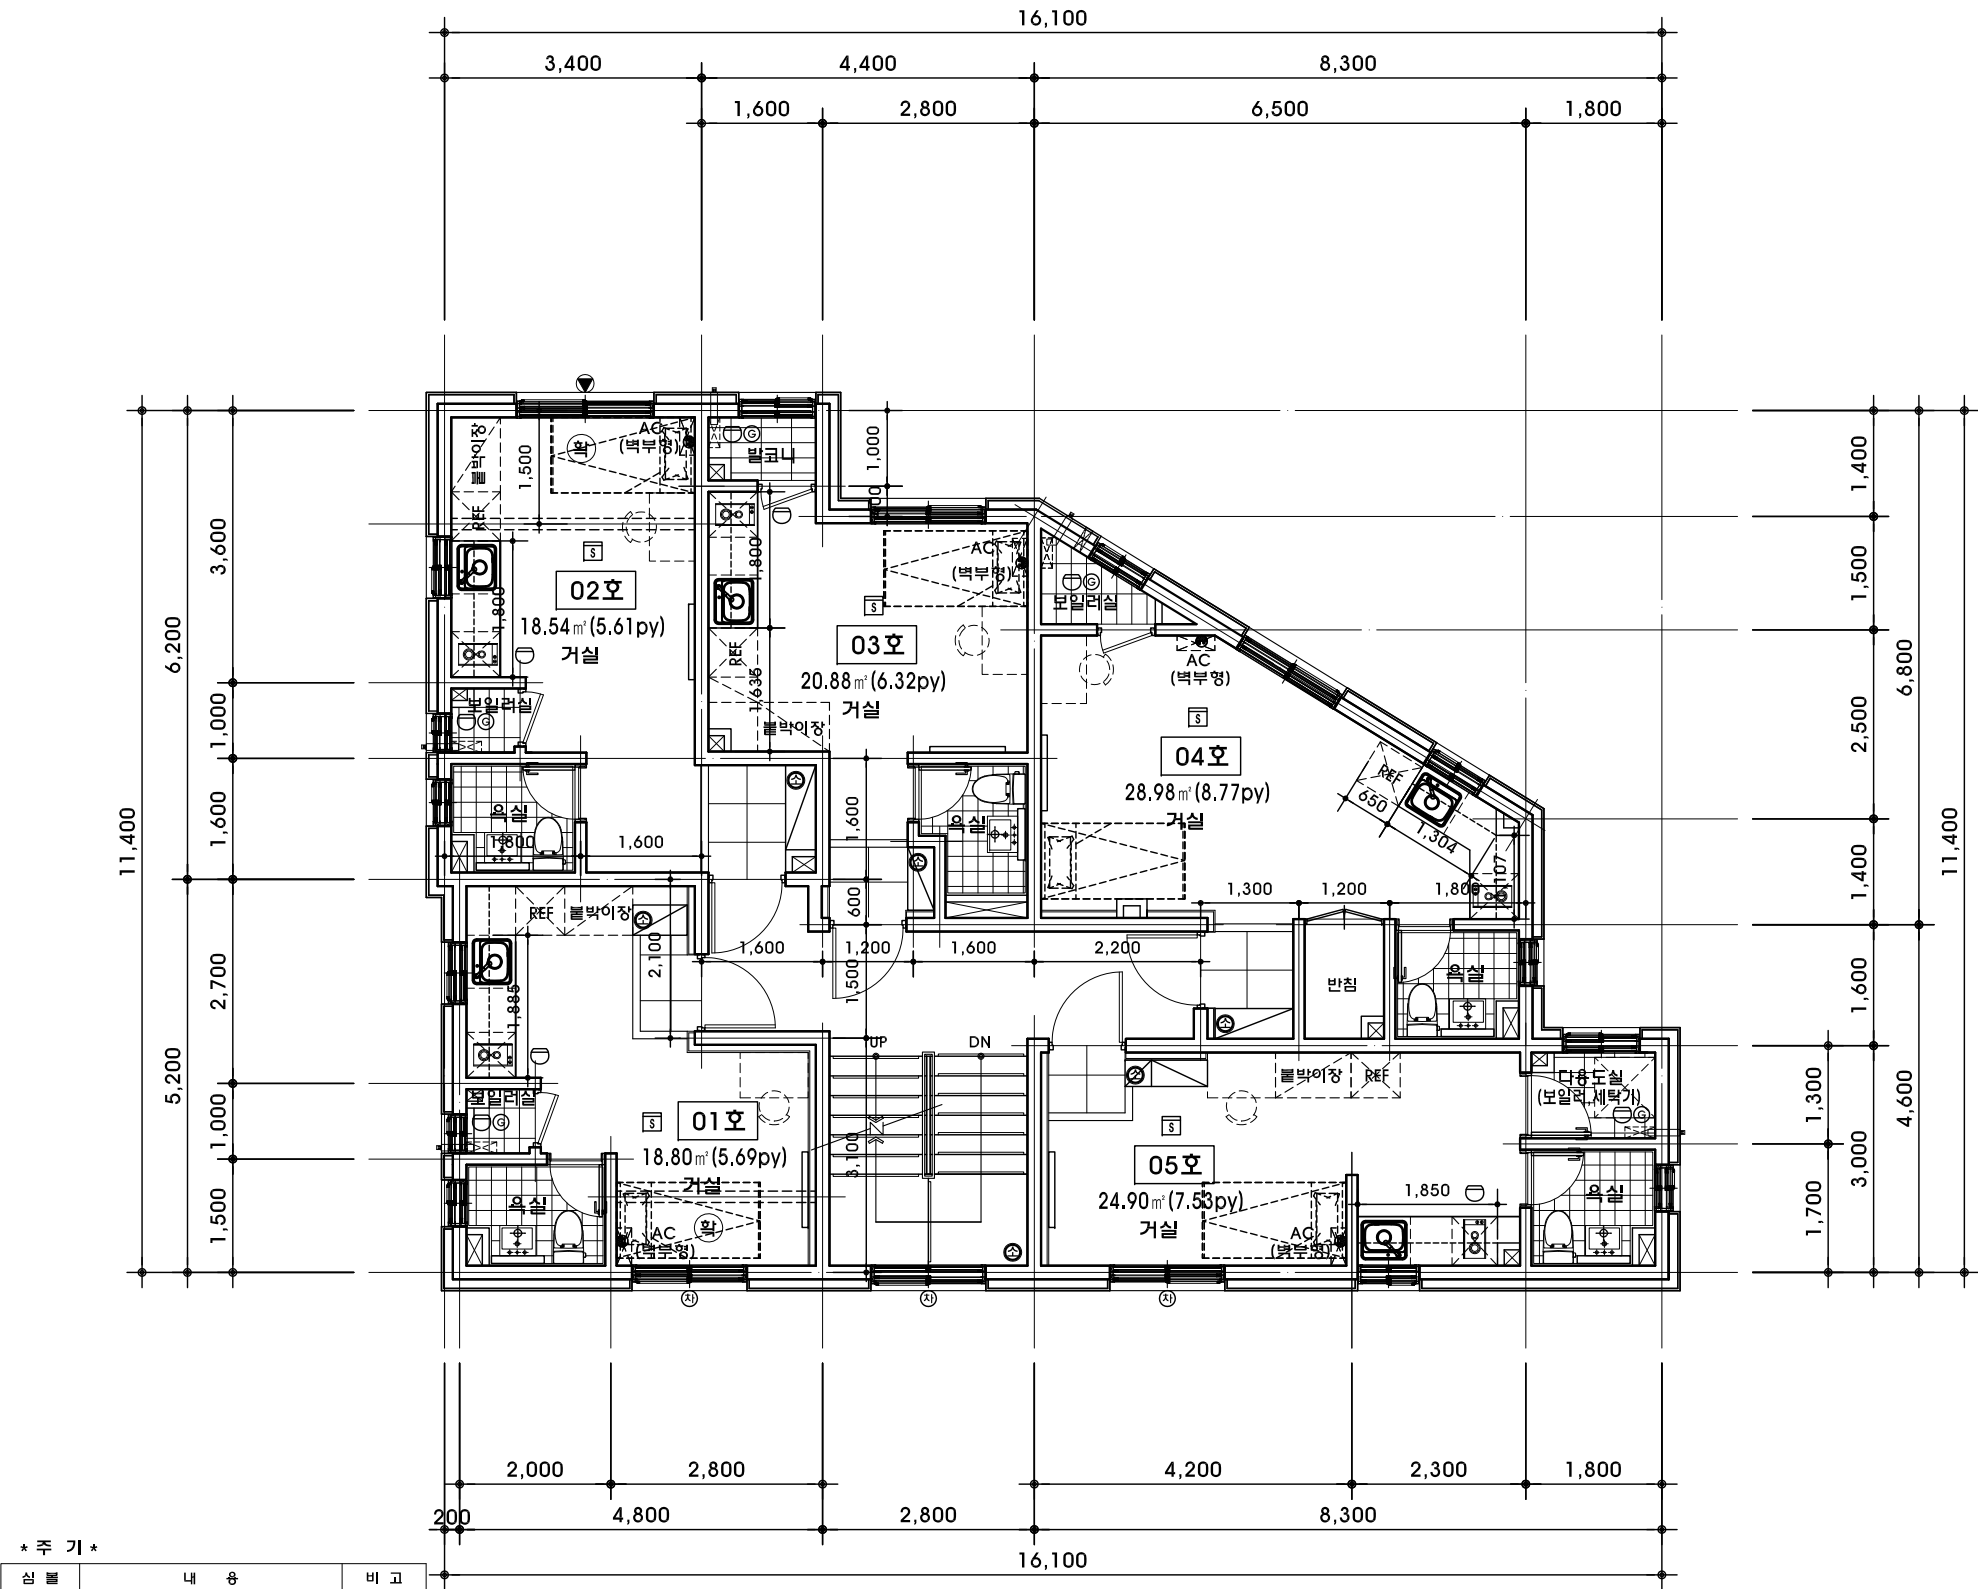


* 주 기 *		
심볼	내 용	비 고
○	열식 단독경보형 감지기 (형식승인품)	
㉑	연기식 단독경보형 감지기 (형식승인품)	
㉒	가스누출 경보기	
㉓	ABC 분말 소화기	
㉔	차면시설	
▼	소방관 진입장	

■ 주 기

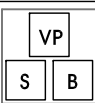
건 축	1 (외부)	주차장내 CCTV,쓰레기분리수거,자전거보관대 설치	
		우편함 설치 (세대전용, 공용, 반송용, 폐건전지함 구분 설치)	
		세대 테라스 설치시 세대간 분리벽 계획	
		세대 발코니 설치시 차양시설 설치	
		세대내 비디오폰 설치	
	2 (계단실)	세대 현관문 도어체크 및 스톱퍼 설치	
		계단참의 현관과 계단 이격거리 (최소600mm이상)	
	3 (내부)	세대내 욕실, 휴지걸이 매립형 설치	
		불박이 가구 내부 다용도 수납가능토록 수평 이동 칸막이 설치	
	구 조	4 (시공)	에어컨 실외기 설치위치 및 에어컨 콘센트, 냉매 및 배수관 위치 도면표기
☹ - 에어컨 콘센트 표기			
콘크리트 폼타이 제거 후 마감공사 시공 (방수, 단열재 시공 등)			
욕실 & 다용도실 스위치 : 문 열리는 방향으로 시공			
주차장 차량 진출입구간,화장실 무소음트렌치 시공			
5 (마감)		-직접외기(외벽)에 면한 실내벽면 단열재	
		[아이소핑크(10mm) + 석고보드 마감도면 표기]	
		-간접외기(계단실,복도)에 면한 실내벽면 단열재	
		[경질우레탄폼(80mm) + 석고보드 마감도면 표기]	
		*기타 실내 벽면 시멘트 미장 마감	
1	철근 : fy=400Mpa		
	콘크리트 : fck=24Mpa		
	2	스라브두께 : 210mm (복배근)	
		외벽벽두께 : 180mm (복배근)	
		코아벽두께 : 180mm (복배근)	
세대벽두께 : 180mm (복배근)			
전 기	1	-콘센트 설치 (바닥 마감선 기준)	
		[거실] 스탠드형 에어컨 : 350	
		[안방] 벽걸이형 에어컨 : 1900	
		[화장실] 양변기 옆 : 900	
		[주방] 조리대 : 중앙 / 냉창고 : 350 / 후드 : 2100	
	2	-비디오폰(VP),보일러온도조절기(B), 스위치(S) 설치 (거실 아트홀 위치)	
			
	3	-위치 표기	
		에어컨 실외기	
		에어컨 콘센트	
냉매, 배수관			
비 고	우편함 규격은 관련법규에 맞추어 적절한 위치에 설치하고		
	세대전용,공용,반송용,폐건전지함으로 구분 설치한다.		
	난간대에 국기봉을 설치한다		
	(확) : 확장형 발코니		


지상 2~3층 평면도
SCALE = 1/100

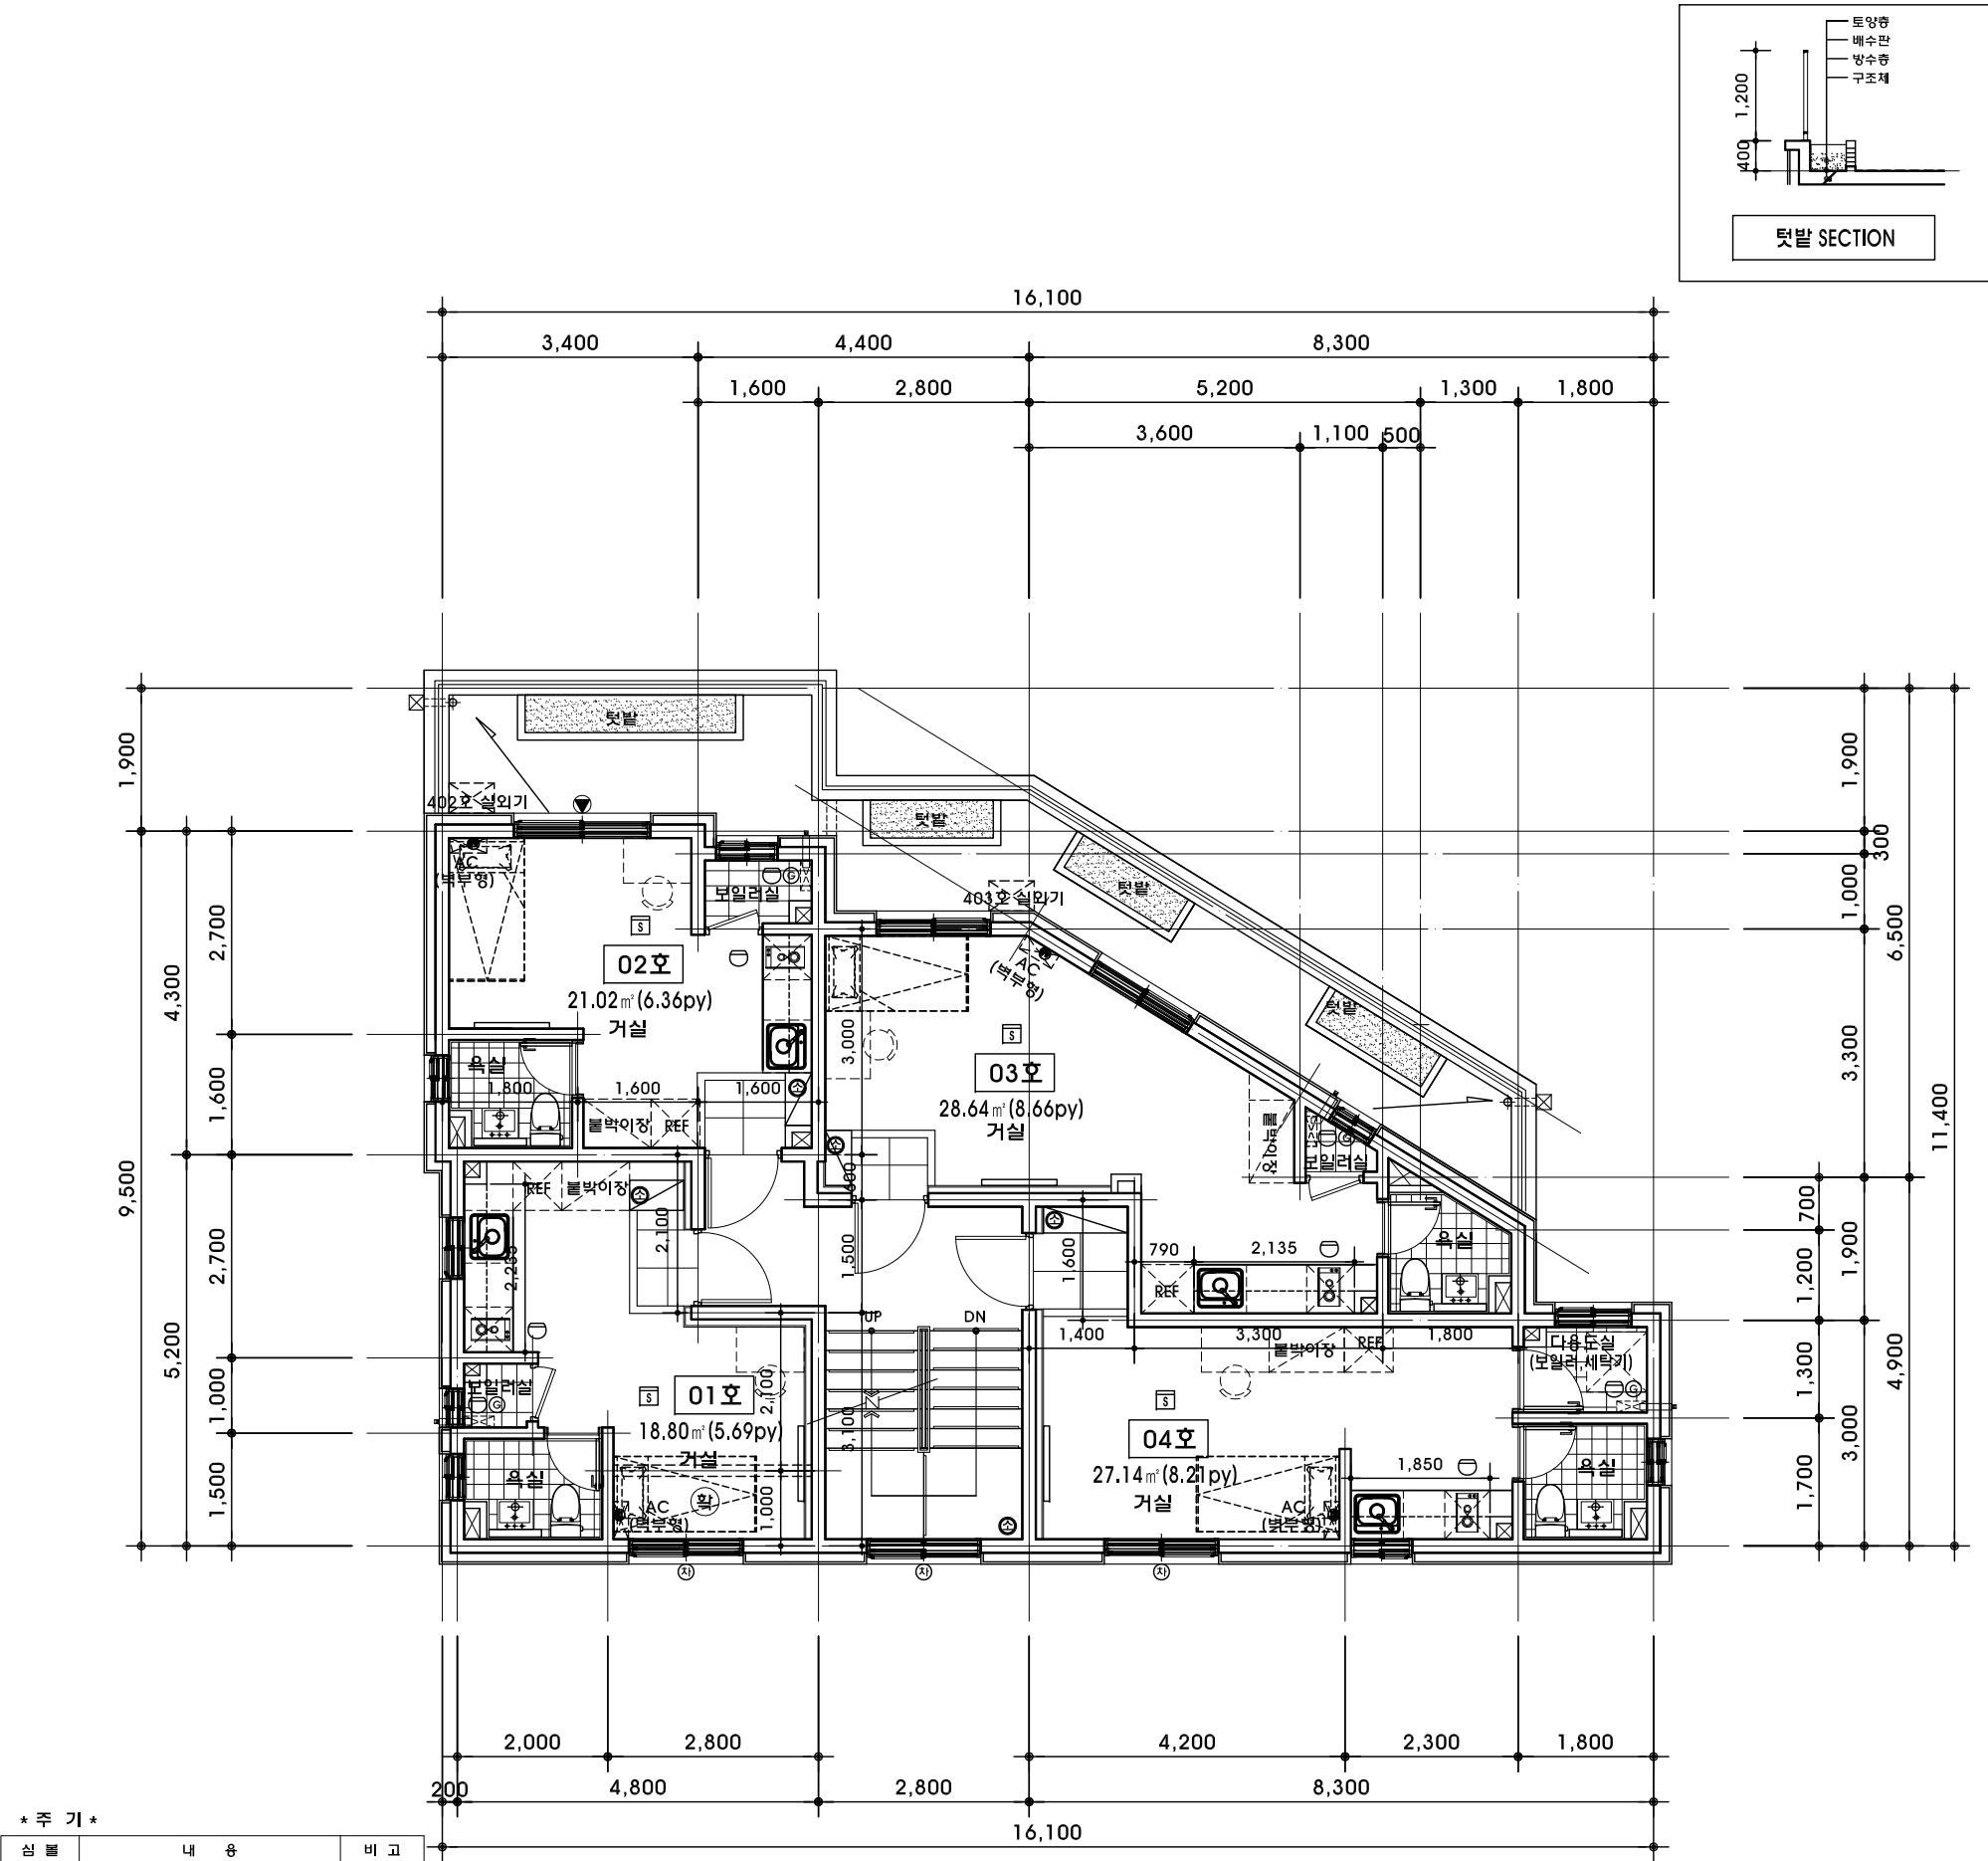


* 주 기 *		
○	열식 단독경보형 감지기 (형식승인품)	
㉑	연기식 단독경보형 감지기 (형식승인품)	
㉒	가스누출 경보기	
㉓	ABC 분말 소화기	
㉔	차면시설	
㉕	소방관 진입창	

■ 주 기

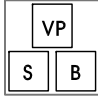
건	1 (외부)	주차장내 CCTV,쓰레기분리수거,자전거보관대 설치	
		우편함 설치 (세대전용, 공용, 반송용, 폐건전지함 구분 설치)	
		세대 테라스 설치시 세대간 분리벽 계획	
		세대 발코니 설치시 차양시설 설치	
		세대내 비디오폰 설치	
	2 (계단실)	세대 현관문 도어체크 및 스톱퍼 설치	
		계단참의 현관과 계단 이격거리 (최소600mm이상)	
	3 (내부)	세대내 욕실, 휴지걸이 매립형 설치	
		불박이 가구 내부 다용도 수납가능토록 수평 이동 칸막이 설치	
		에어컨 실외기 설치위치 및 에어컨 콘센트, 냉매 및 배수관 위치 도면표기  - 에어컨 콘센트 표기	
축	4 (시공)	콘크리트 폼타이 제거 후 마감공사 시공 (방수, 단열재 시공 등)	
		욕실 & 다용도실 스위치 : 문 열리는 방향으로 시공	
		주차장 차량 진출입구간,화장실 무소음트렌치 시공	
	5 (마감)	-직접외기(외벽)에 면한 실내벽면 단열재 [아이소핑크(10mm) + 석고보드 마감도면 표기]	
		-간접외기(계단실,복도)에 면한 실내벽면 단열재 [경질우레탄폼(80mm) + 석고보드 마감도면 표기]	
		*기타 실내 벽면 시멘트 미장 마감	
구 조	1	철근 : fy=400Mpa	
		콘크리트 : fck=24Mpa	
	2	스라브두께 : 210mm (복배근)	
		외벽벽두께 : 180mm (복배근)	
		코아벽두께 : 180mm (복배근) 세대벽두께 : 180mm (복배근)	
전 기	1	-콘센트 설치 (바닥 마감선 기준)	
		[거실] 스탠드형 에어컨 : 350	
		[안방] 벽걸이형 에어컨 : 1900	
		[화장실] 양변기 옆 : 900	
		[주방] 조리대 : 중앙 / 냉창고 : 350 / 후드 : 2100	
	2	-비디오폰(VP),보일러온도조절기(B) 스위치(S) 설치 (거실 아트홀 위치)	
		-위치 표기	
	3	에어컨 실외기	
		에어컨 콘센트	
		냉매, 배수관	
비 고	우편함 규격은 관련법규에 맞추어 적절한 위치에 설치하고		
	세대전용,공용,반송용,폐건전지함으로 구분 설치한다.		
	난간대에 국기봉을 설치한다		
	㉠ : 확장형 발코니		


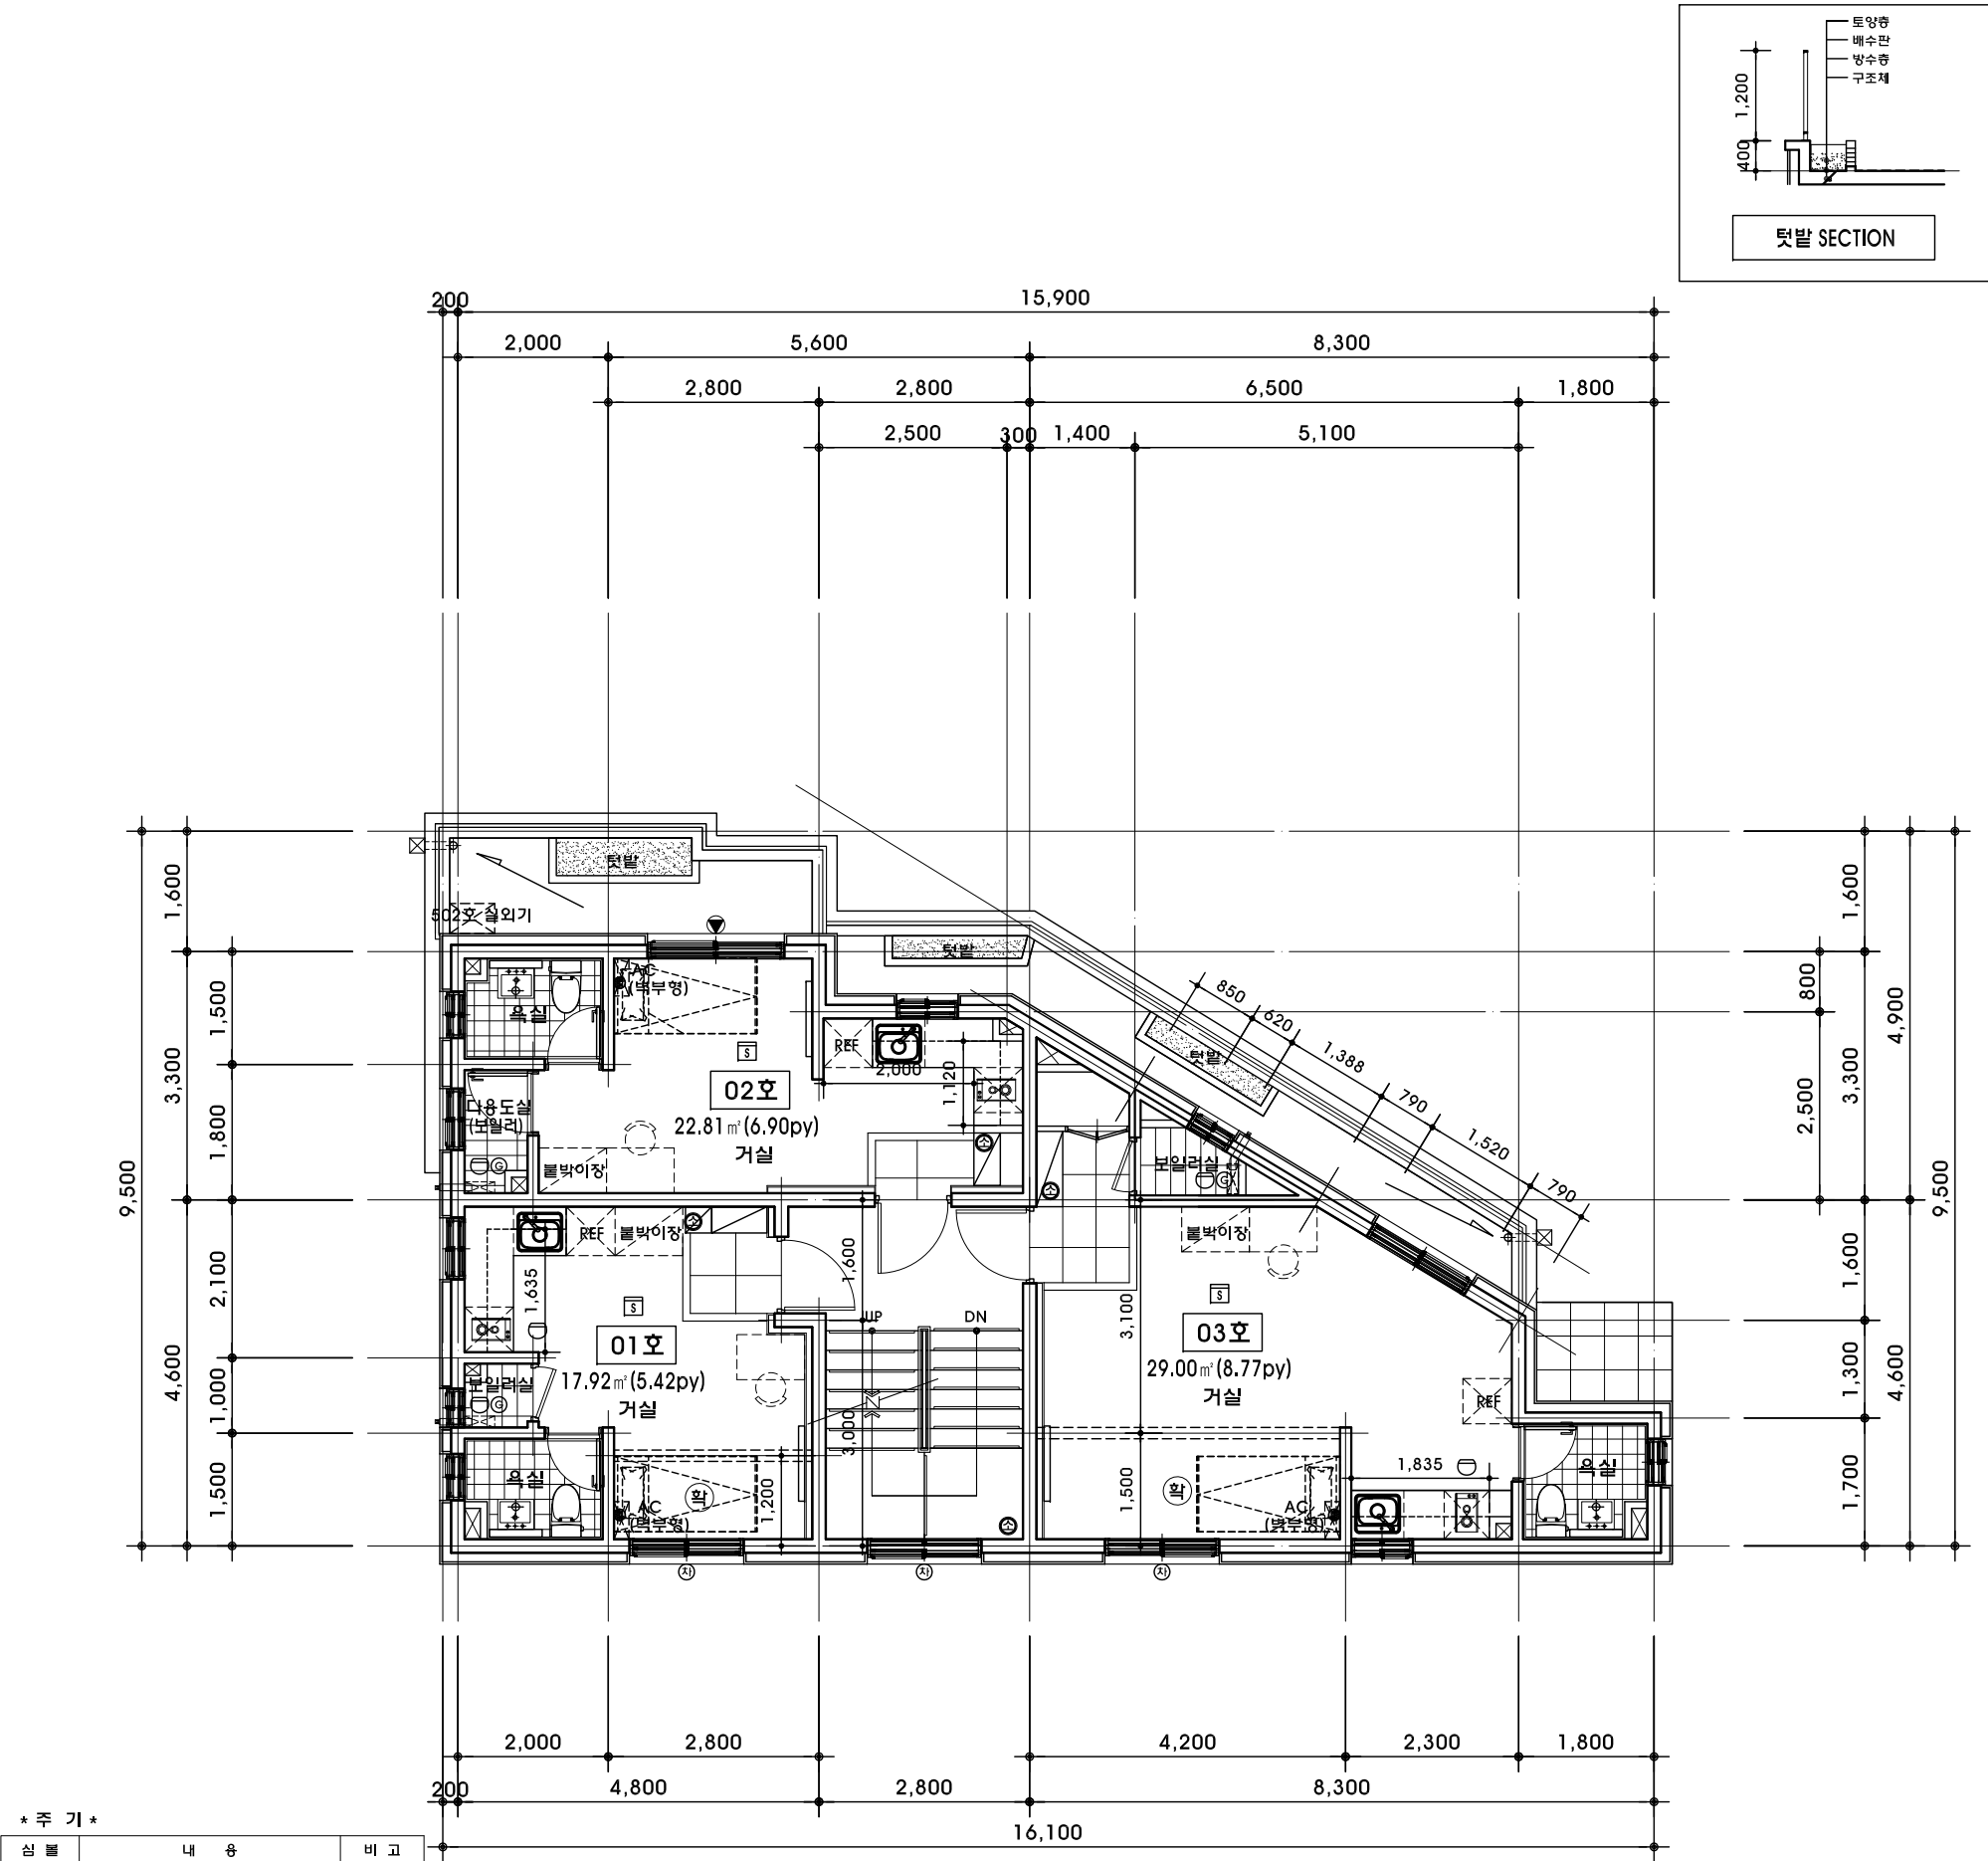


* 주 기 *		
심볼	내용	비고
○	열식 단독경보형 감지기 (형식승인품)	
㉑	연기식 단독경보형 감지기 (형식승인품)	
㉒	가스누출 경보기	
㉓	ABC 분말 소화기	
㉔	차면시설	
㉕	소방관 진입창	

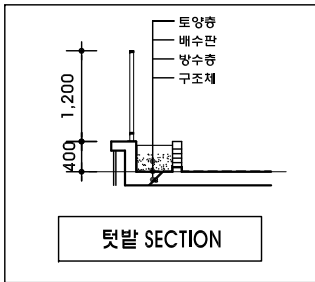


■ 주 기

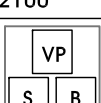건축	1 (외부)	주차장내 CCTV,쓰레기분리수거,자전거보관대 설치		
		우편함 설치 (세대전용, 공용, 반송용, 폐건전지함 구분 설치)		
		세대 테라스 설치시 세대간 분리벽 계획		
		세대 발코니 설치시 차양시설 설치		
		세대내 비디오폰 설치		
	2 (계단실)	세대 현관문 도어체크 및 스톱퍼 설치		
		계단참의 현관과 계단 이격거리 (최소600mm이상)		
	3 (내부)	세대내 욕실, 휴지걸이 매립형 설치		
		불박이 가구 내부 다용도 수납가능토록 수평 이동 칸막이 설치		
		에어컨 실외기 설치위치 및 에어컨 콘센트, 냉매 및 배수관 위치 도면표기  - 에어컨 콘센트 표기		
	4 (시공)	콘크리트 폼타이 제거 후 마감공사 시공 (방수, 단열재 시공 등)		
		욕실 & 다용도실 스위치 : 문 열리는 방향으로 시공		
		주차장 차량 진출입구간,화장실 무소음트렌치 시공		
		5 (마감)	-직접외기(외벽)에 면한 실내벽면 단열재	
			[아이소핑크(10mm) + 석고보드 마감도면 표기]	
	-간접외기(계단실,복도)에 면한 실내벽면 단열재			
	[경질우레탄폼(80mm) + 석고보드 마감도면 표기]			
*기타 실내 벽면 시멘트 미장 마감				
구조	1	철근 : fy=400Mpa		
		콘크리트 : fck=24Mpa		
	2	스라브두께 : 210mm (복배근)		
		외벽벽두께 : 180mm (복배근)		
		코아벽두께 : 180mm (복배근)		
세대벽두께 : 180mm (복배근)				
전기	1	-콘센트 설치 (바닥 마감선 기준)		
		[거실] 스탠드형 에어컨 : 350		
		[안방] 벽걸이형 에어컨 : 1900		
		[화장실] 양변기 옆 : 900		
		[주방] 조리대 : 중앙 / 냉장고 : 350 / 후드 : 2100		
	2	-비디오폰(VP),보일러온도조절기(B) 스위치(S) 설치 (거실 아트홀 위치)		
				
	3	-위치 표기		
		에어컨 실외기		
		에어컨 콘센트		
냉매, 배수관				
비고	우편함 규격은 관련법규에 맞추어 적절한 위치에 설치하고			
	세대전용,공용,반송용,폐건전지함으로 구분 설치한다.			
	난간대에 국기봉을 설치한다			
	(확) : 확장형 발코니			

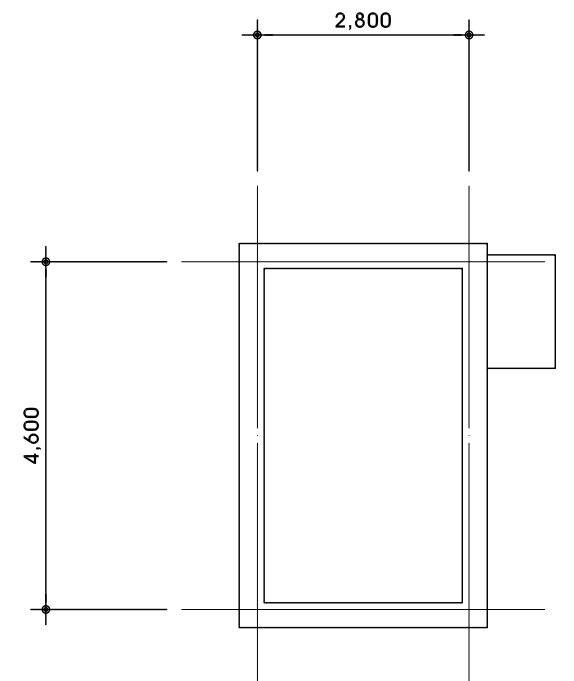
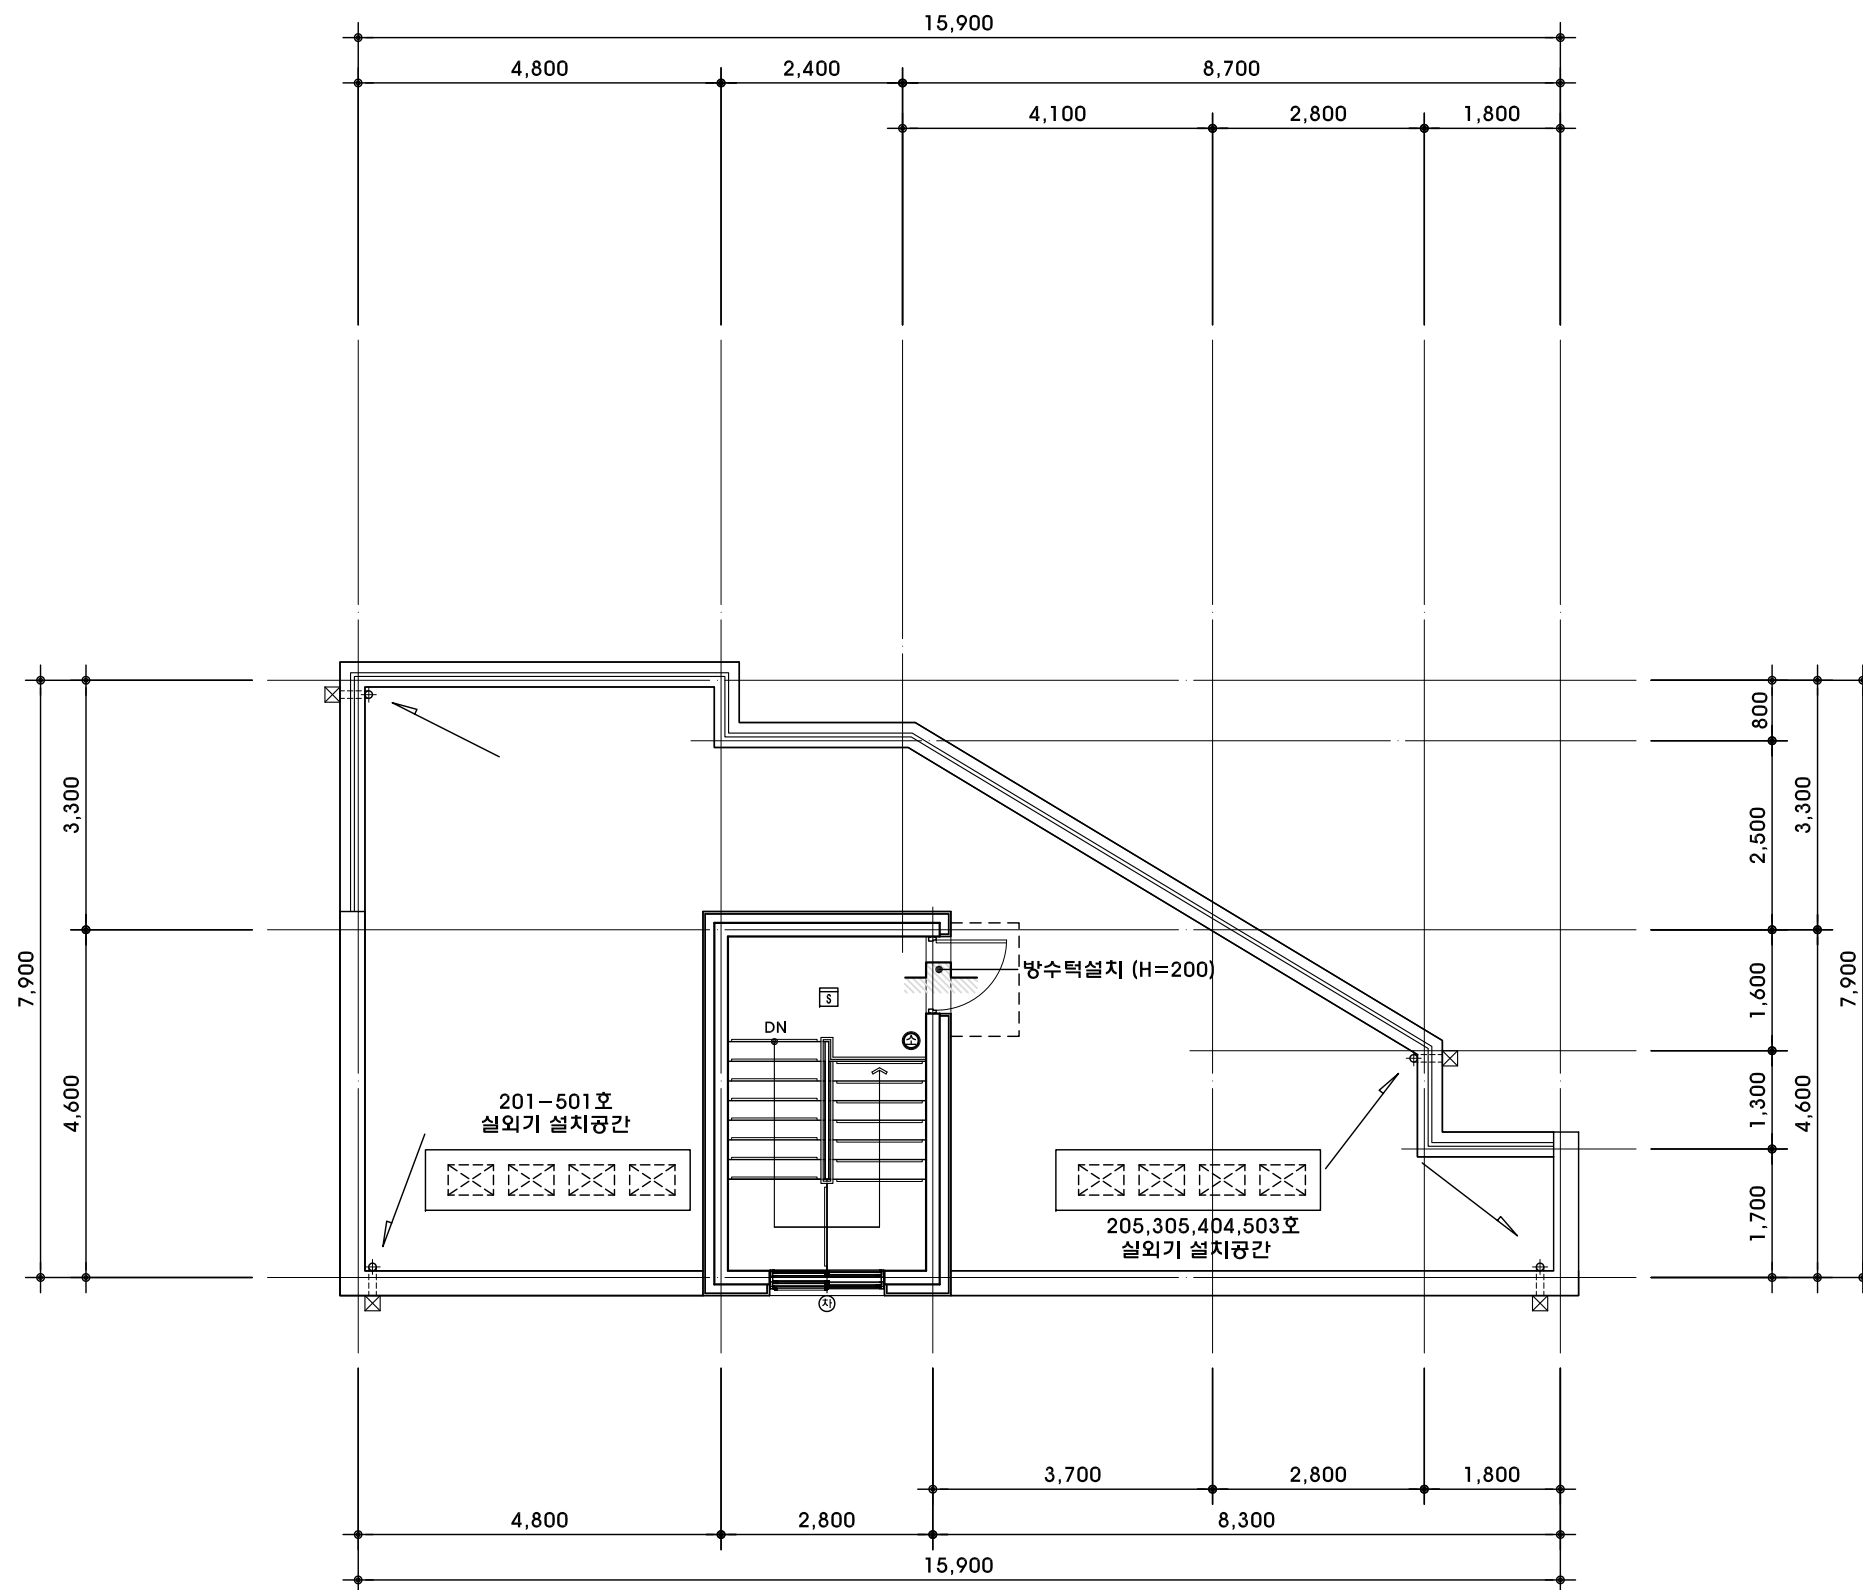


옥탐지붕층 평면도

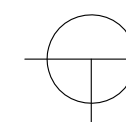



지붕층 및 옥탐지붕층 평면도

SCALE = 1/100

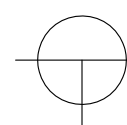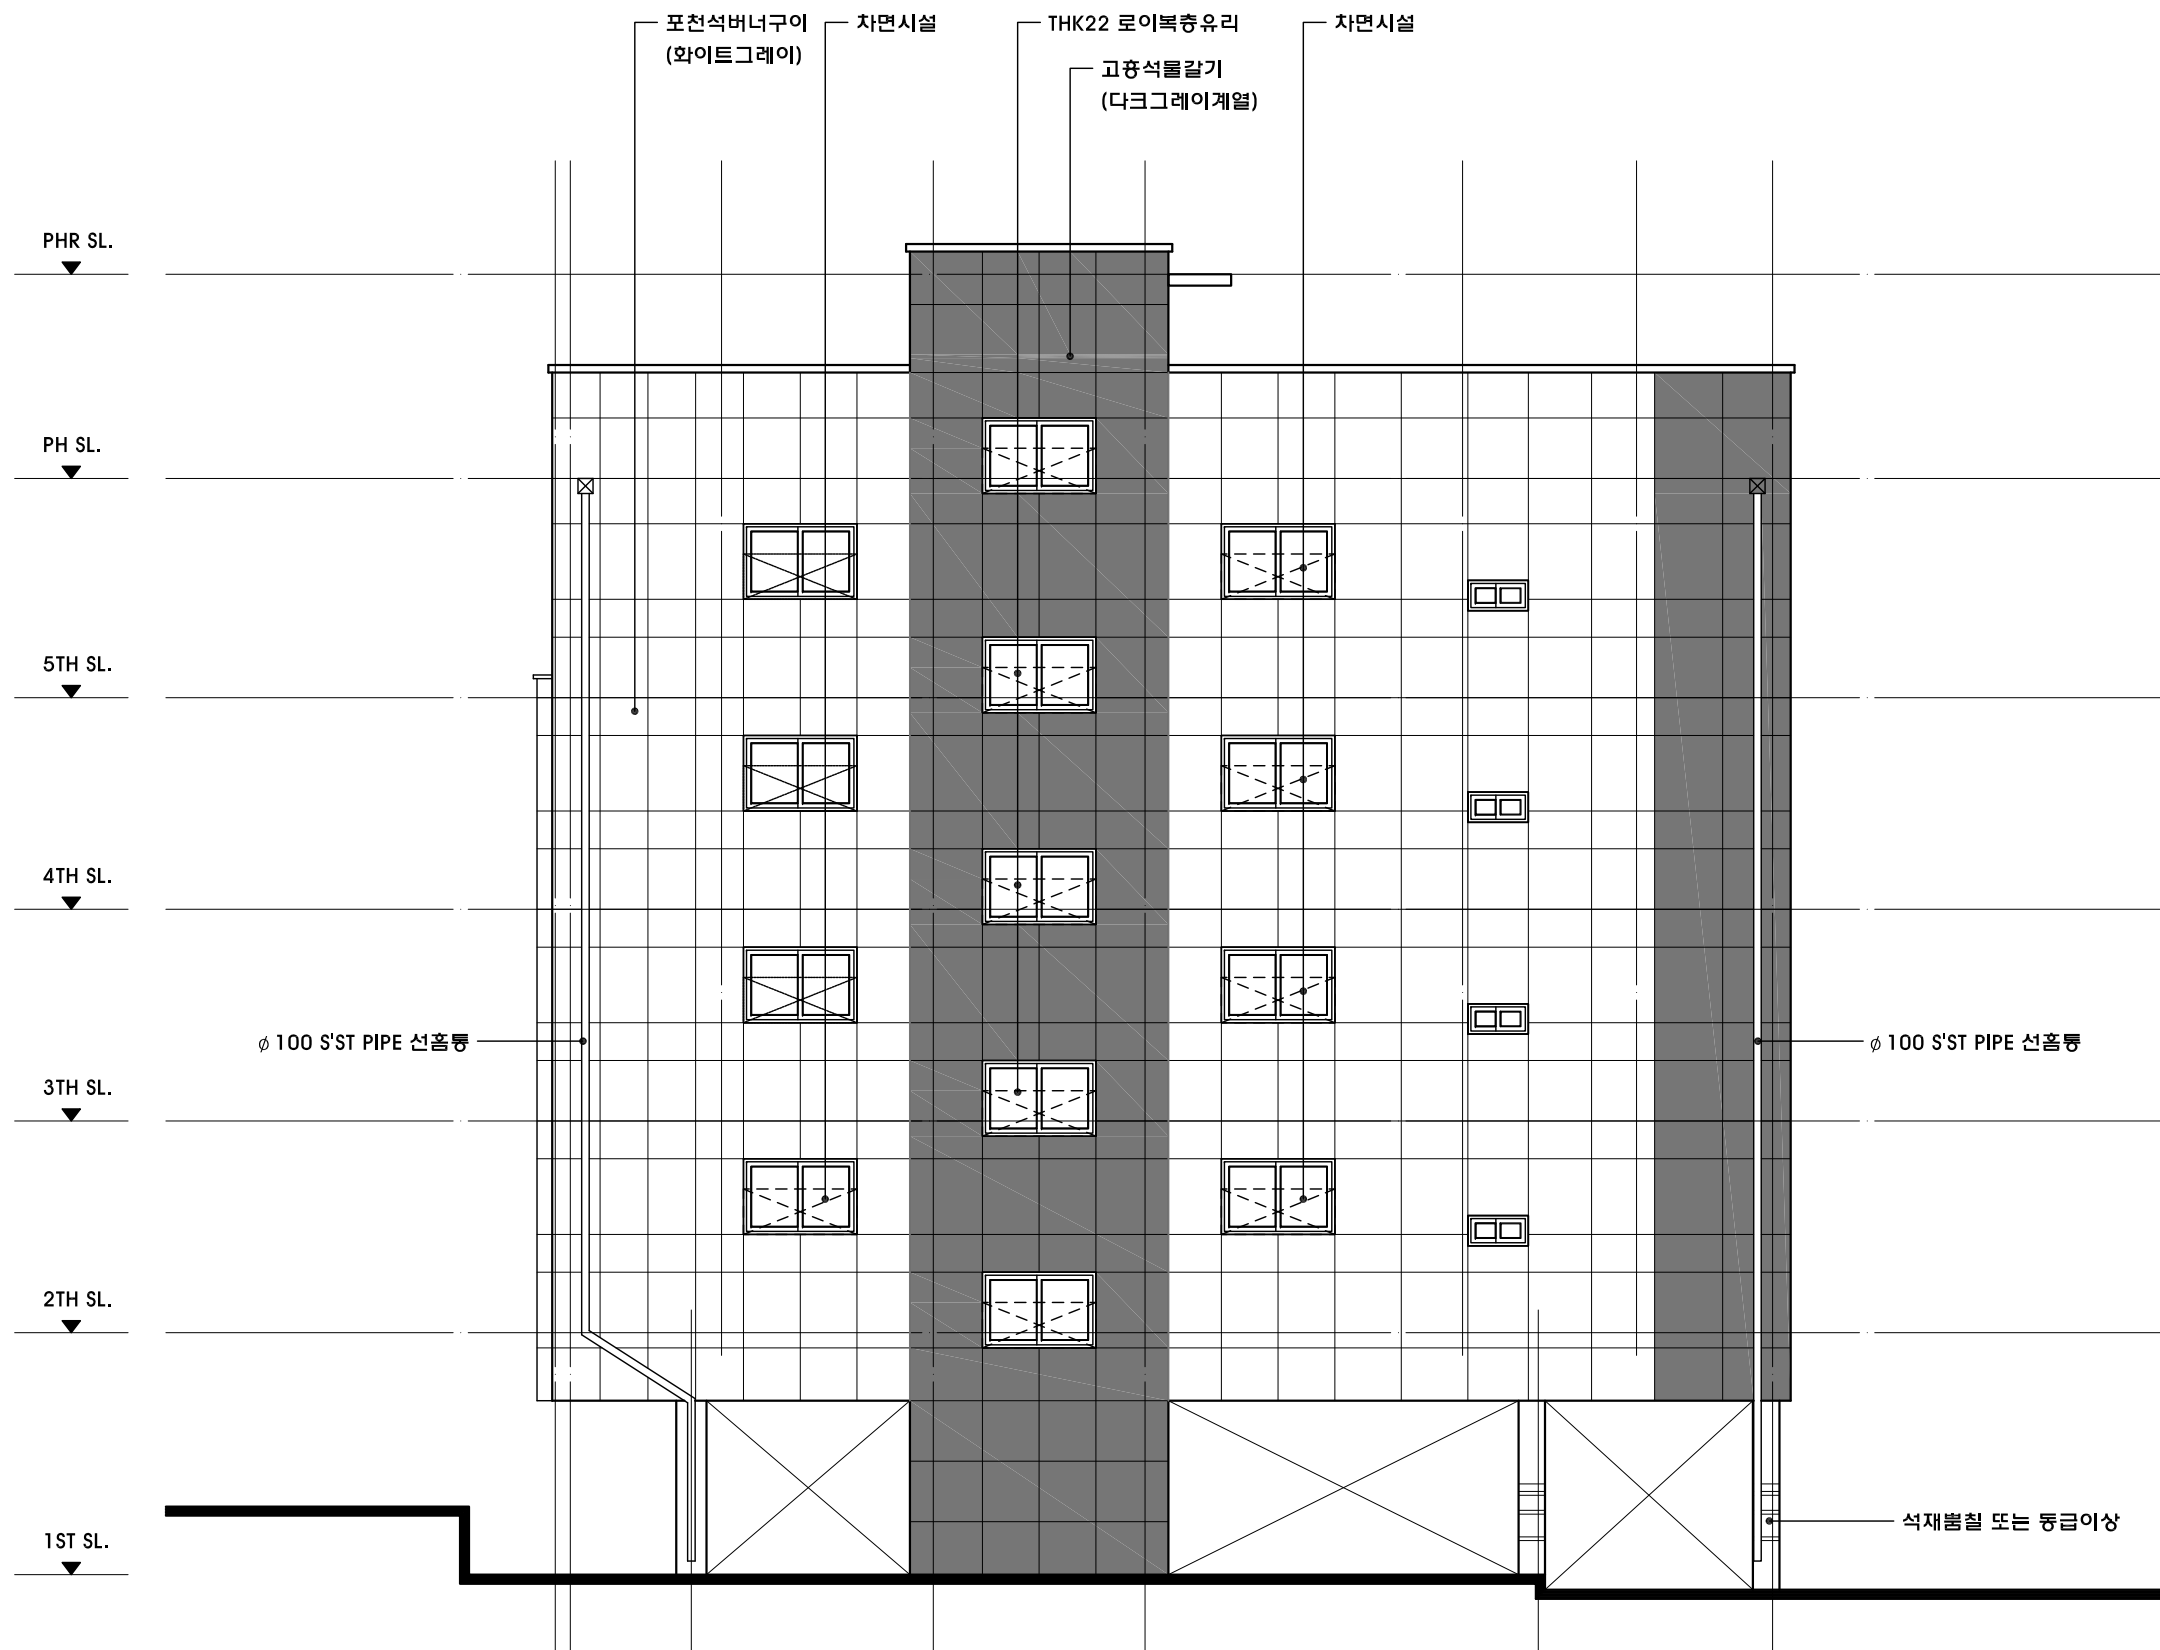

남 측 입 면 도

SCALE = 1/100

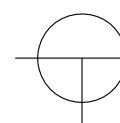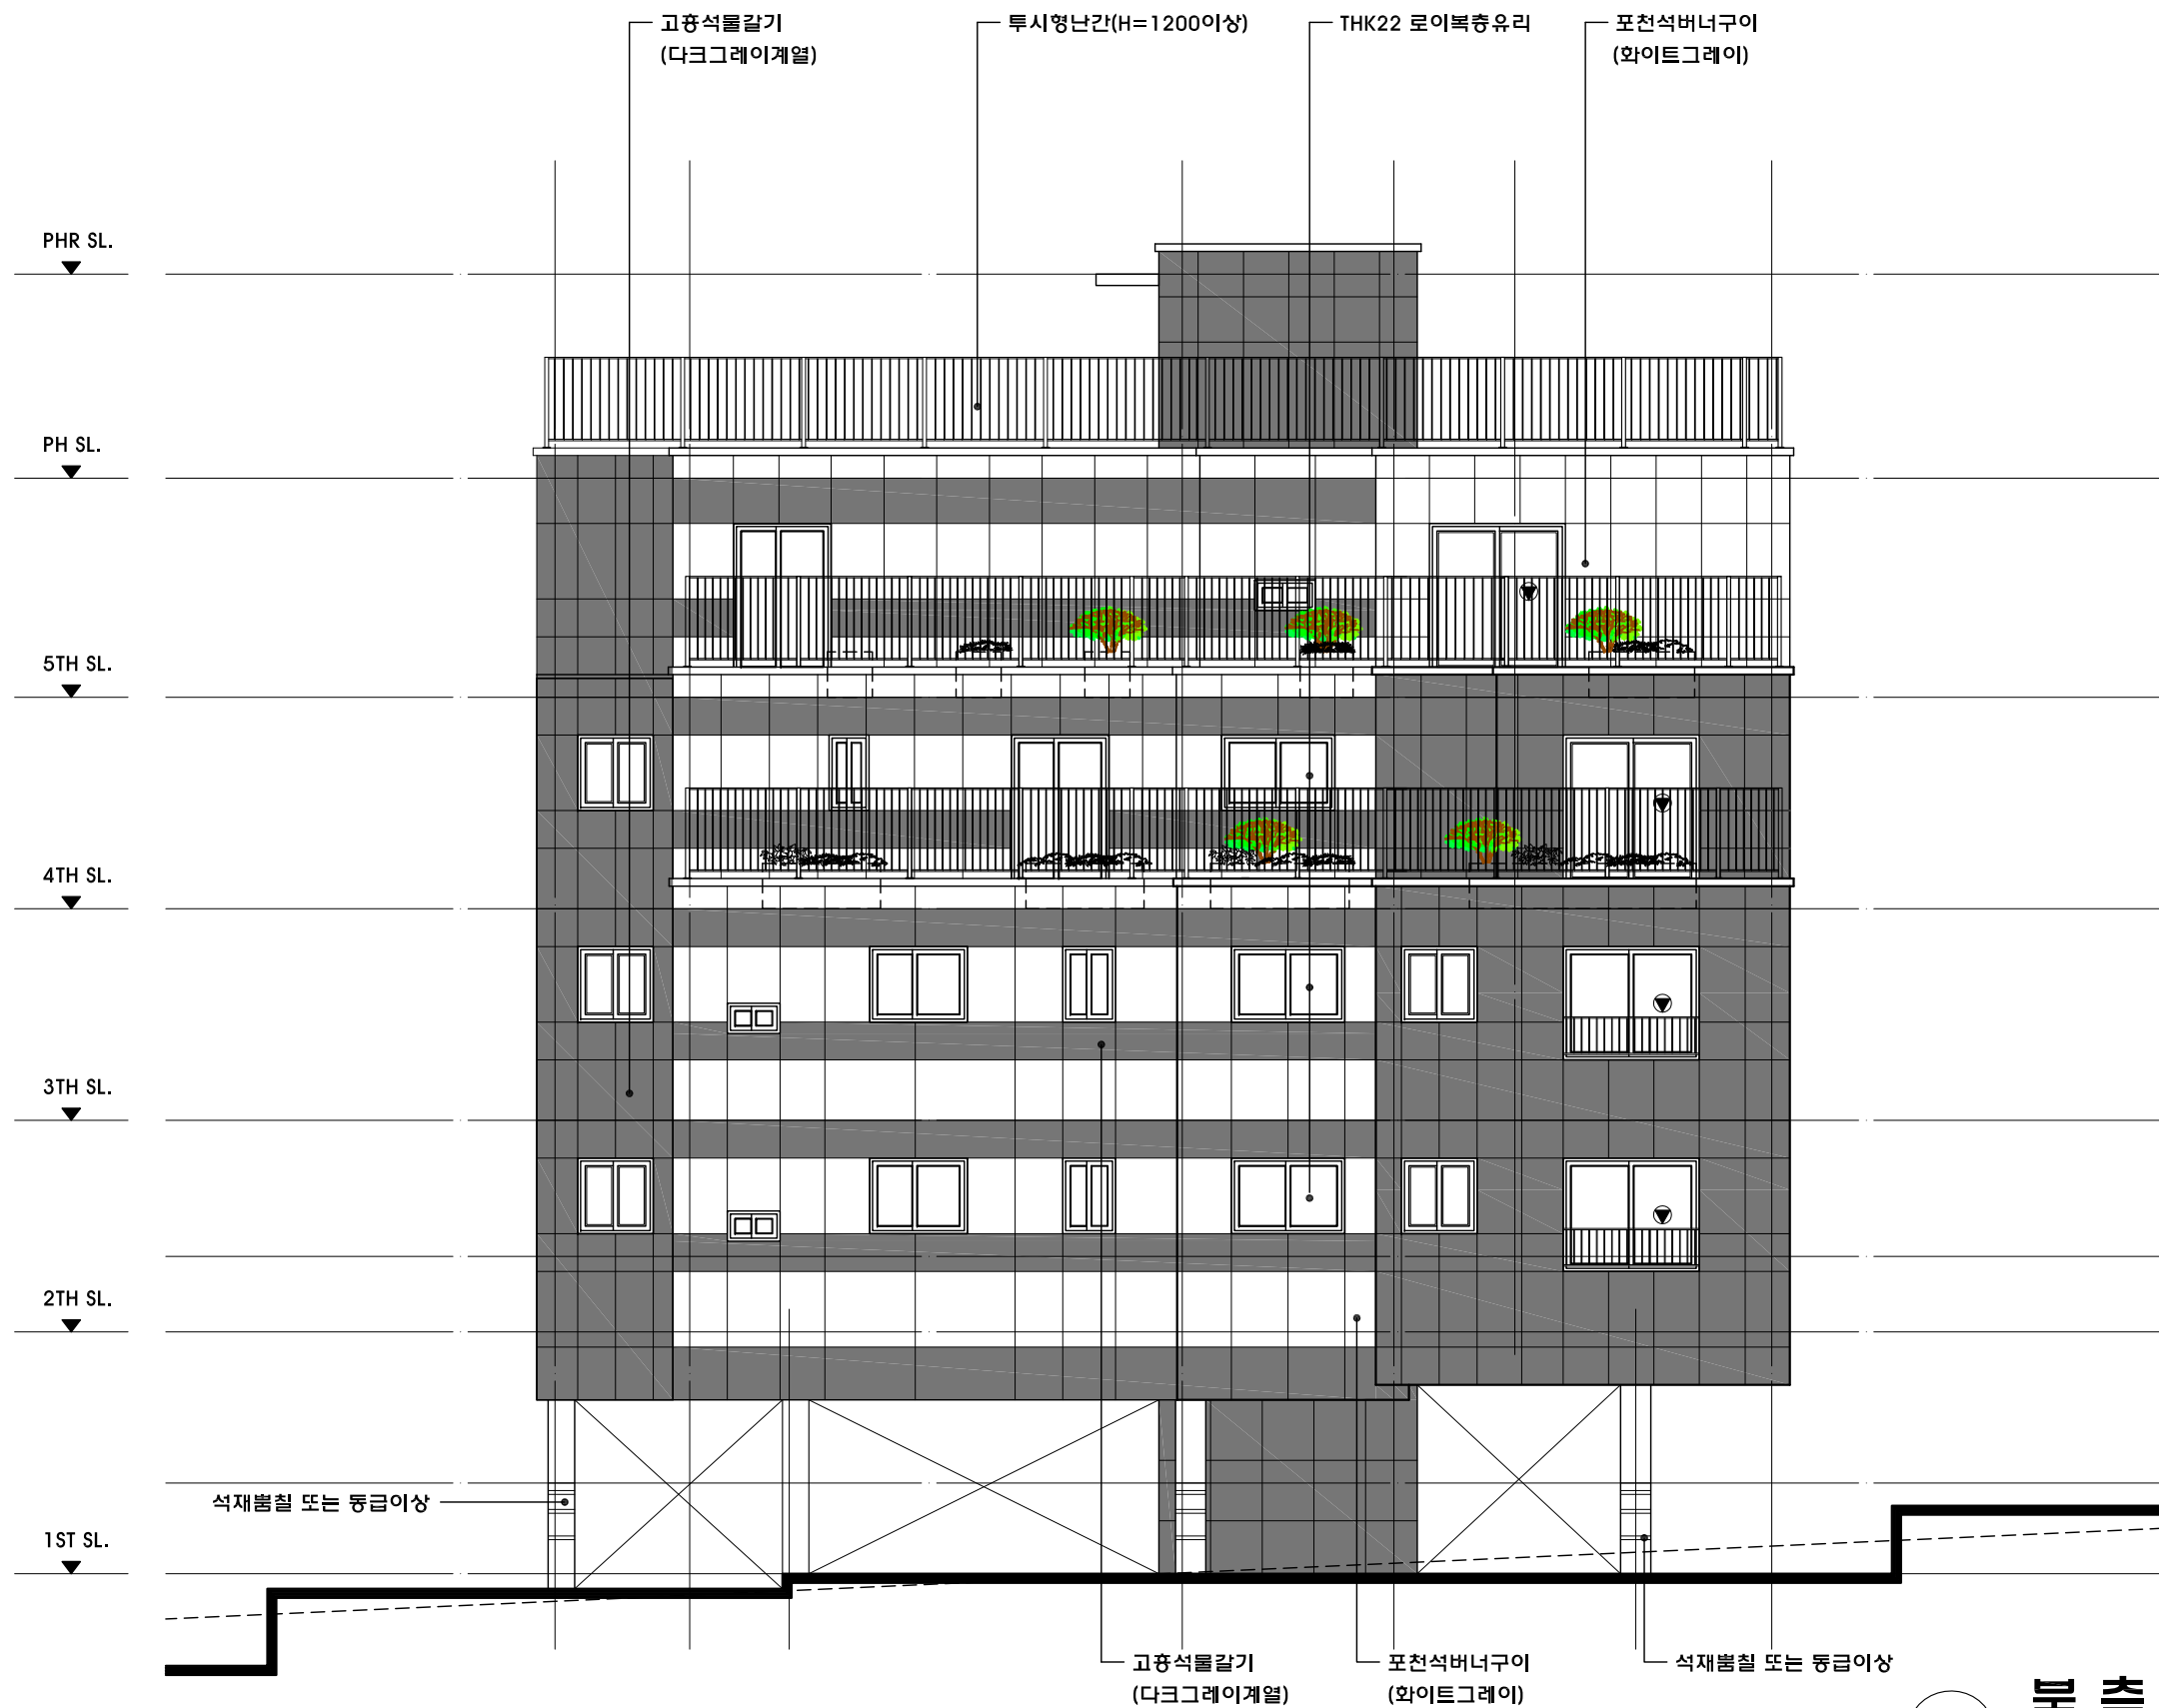

북측입면도

SCALE = 1/100



동측입면도
SCALE = 1/100



서측입면도
SCALE = 1/100



【 본 건 전 경 】



【 주 변 전 경 】