



송인동 오피스텔
신축공사



제이케이건축사사무소(주)
Architects & Planners
TEL : 02-533-9431 FAX : 02-532-9431

NOTE

설 계 변 경 DESCRIPTION OF REVISION				
번 호	내 용			
일 자	설계	검토	심사	승인
	2021.05			
승인 APPROVED BY				
축척 SCALE	A1	1 / NONE		
	A3	1 / NONE		
도면명 DRAWING TITLE				
조감도				
도면번호 DRAWING NO.				
A 00 - 003				

PROJECT TITLE



송인동 오피스텔
신축공사



제이케이건축사사무소(주)
Architects & Planners

TEL : 02-533-9431 FAX : 02-532-9431

NOTE

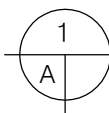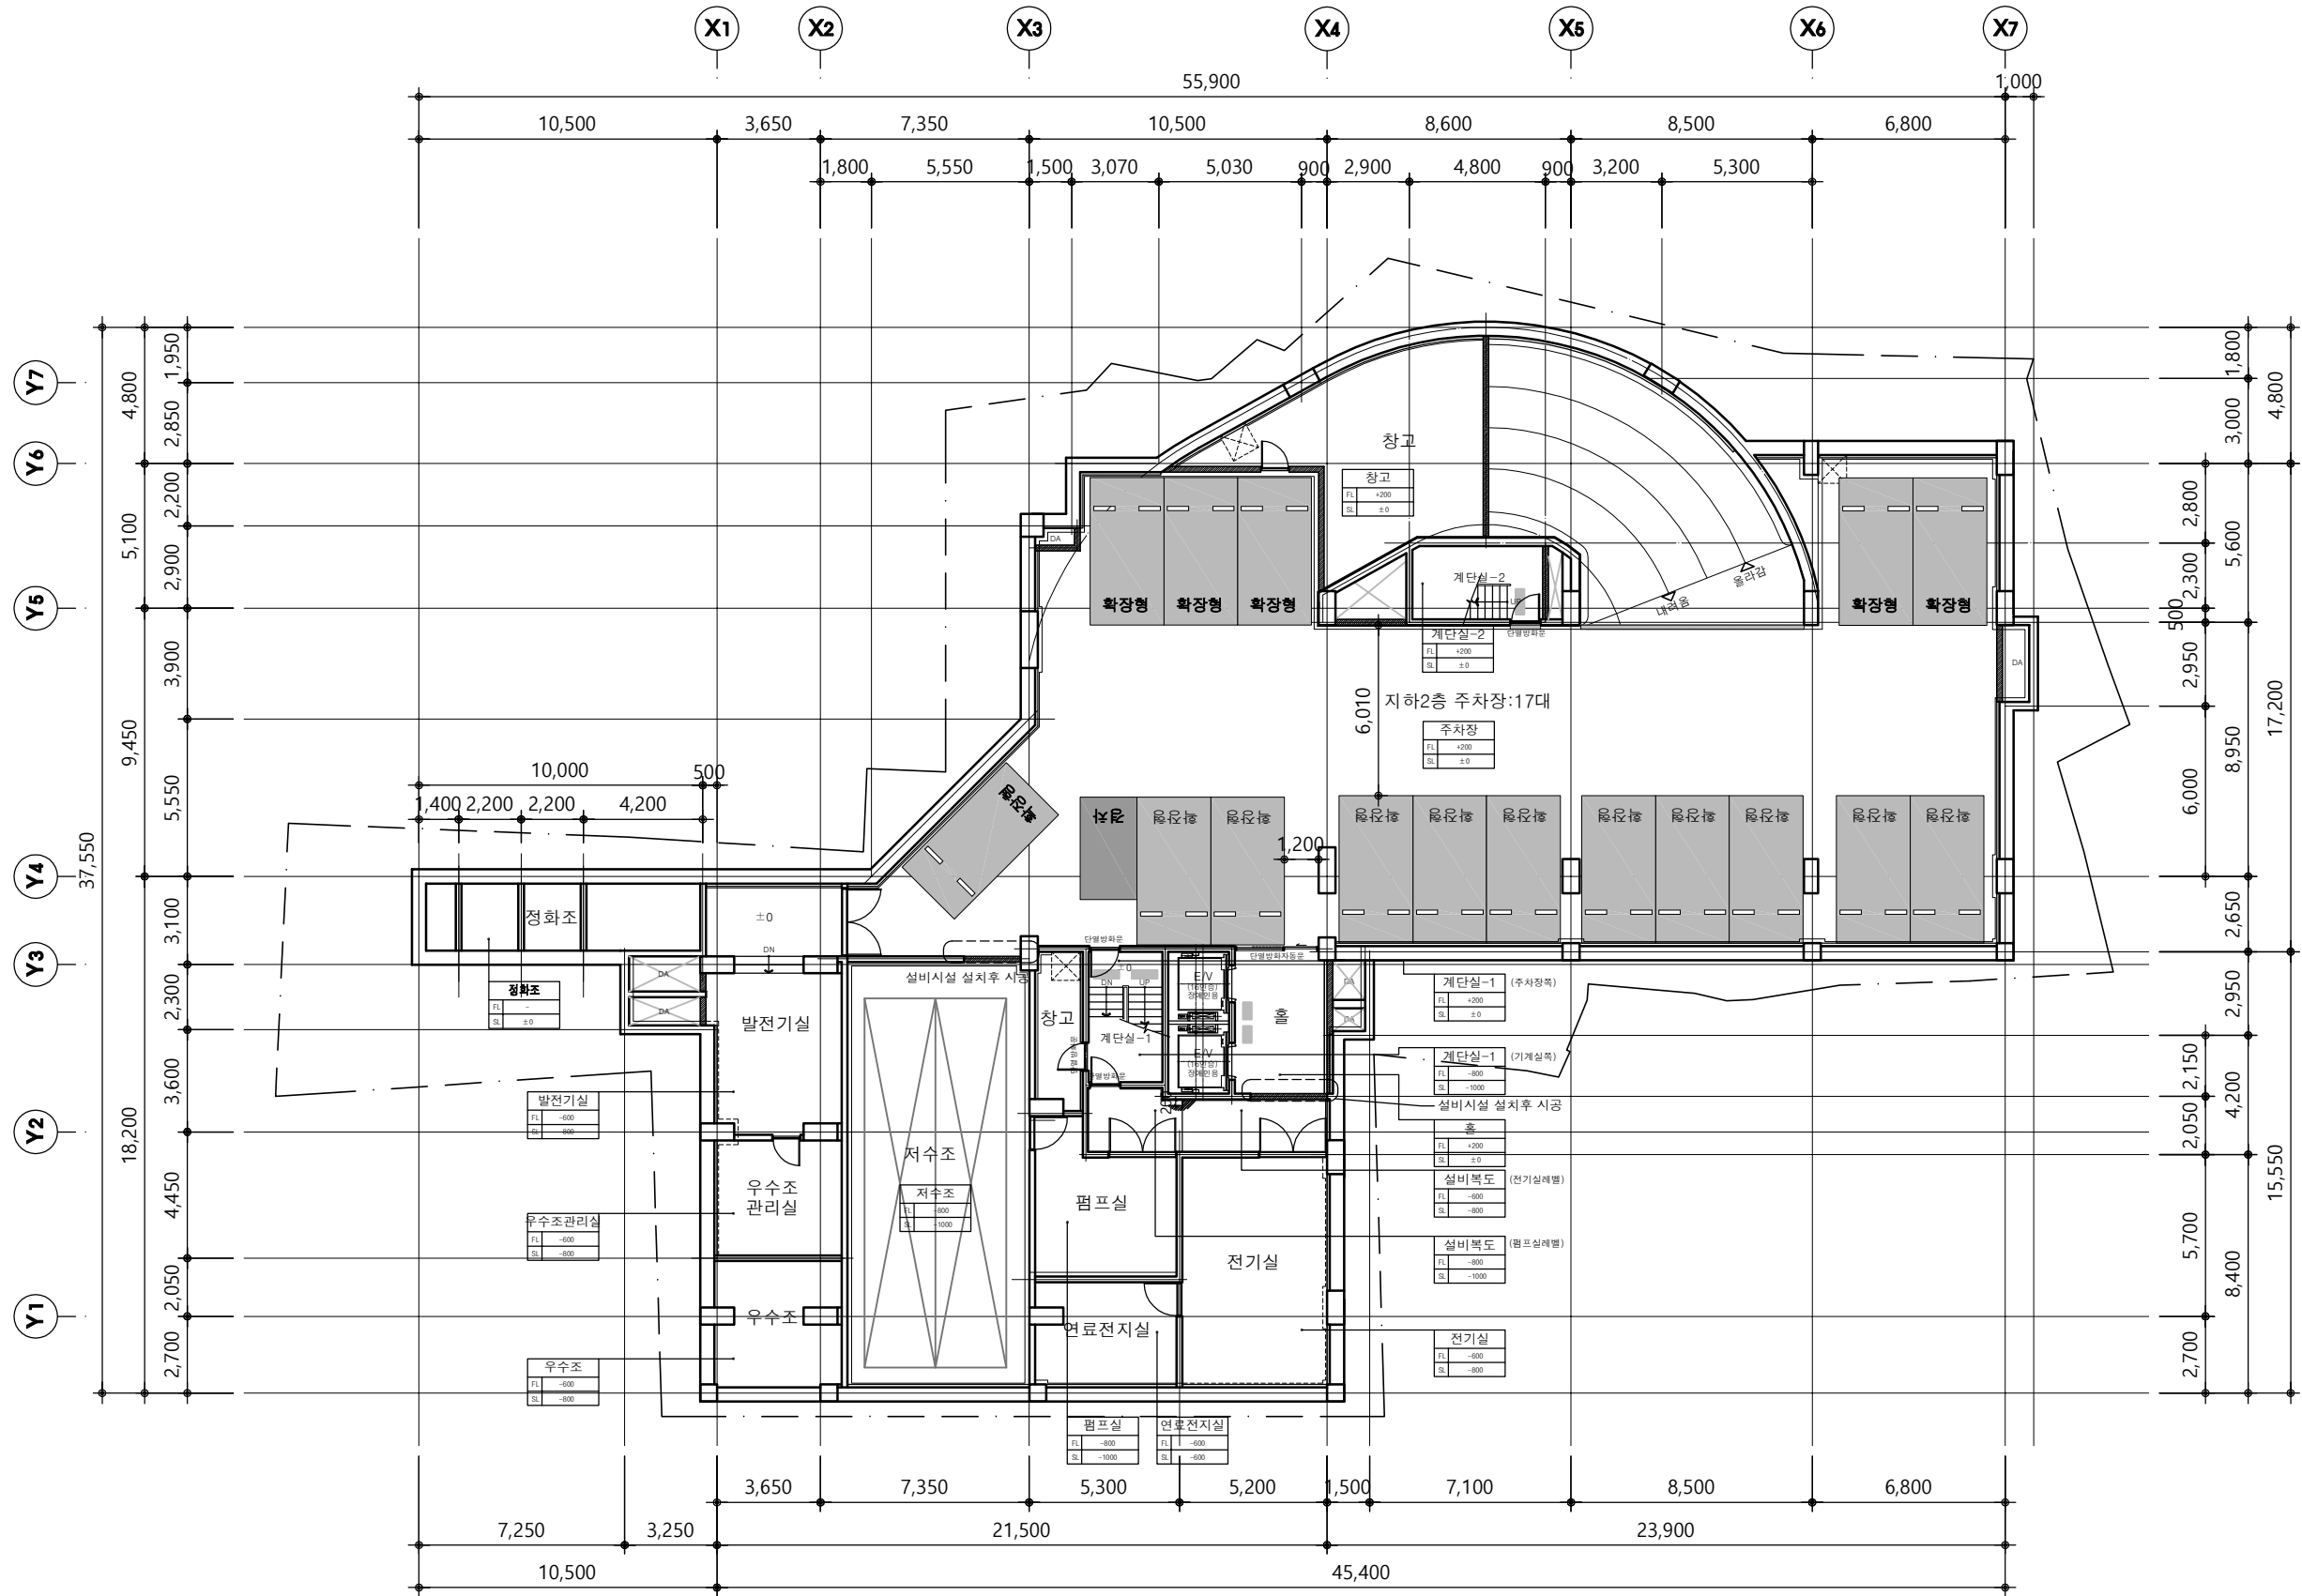

지하2층 평면도

축척 : 1 / 250

설 계 변 경
DESCRIPTION OF REVISION

번 호	내 용
일 자	설 계 경 토 심 사 승 인
2021.05	
승 인 APPROVED BY	

축 척 SCALE	A1	1 / 125
	A3	1 / 250

도면명 DRAWING TITLE

지하2층 평면도

도면번호 DRAWING NO.
A 30 - 001

PROJECT TITLE


송인동 오피스텔
신축공사



제이케이건축사사무소(주)
Architects & Planners

TEL : 02-533-9431 FAX : 02-532-9431

NOTE

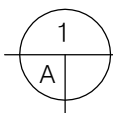

지하1층 평면도

축척 : 1 / 250

설 계 변 경
DESCRIPTION OF REVISION

번 호	내 용
일 자	설 계 경 토 심 사 승 인
2021.05	


승인 APPROVED BY

축 척 SCALE	A1	1 / 125
	A3	1 / 250

도면명 DRAWING TITLE

지하1층 평면도

도면번호 DRAWING NO.
A 30 - 002

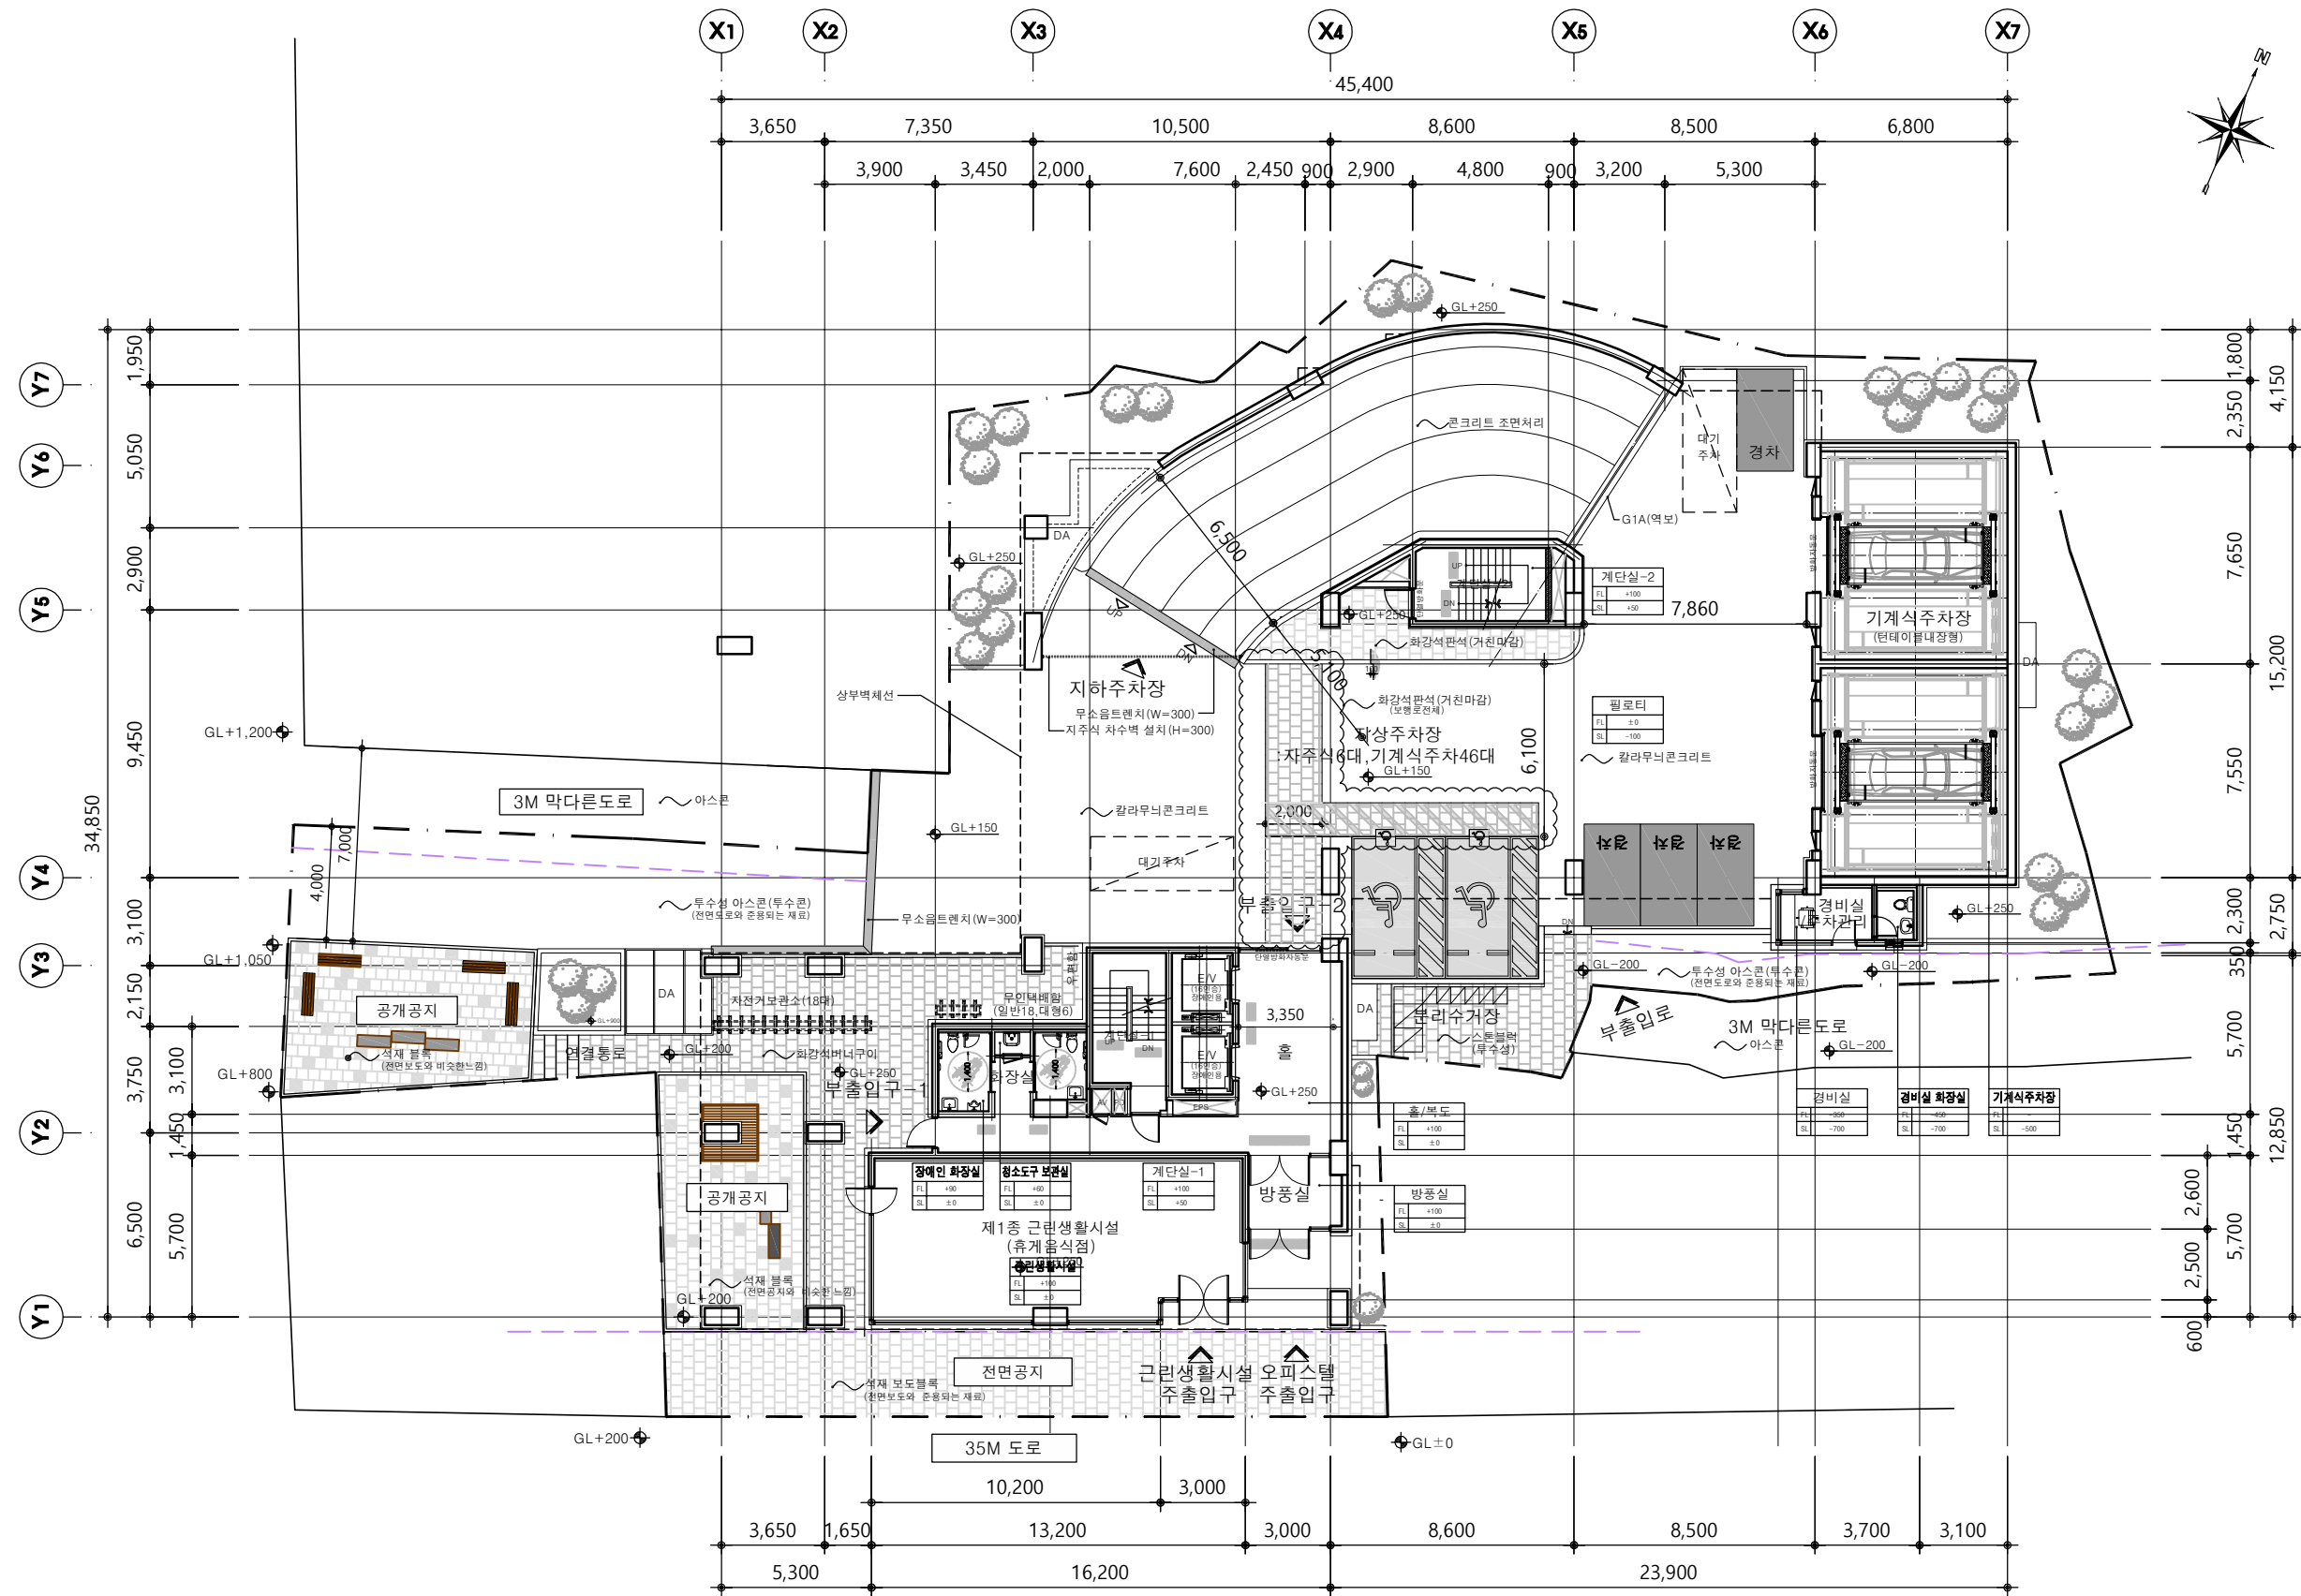

PROJECT TITLE

송인동 오피스텔
신축공사



제이케이건축사사무소(주)
Architects & Planners
TEL : 02-533-9431 FAX : 02-532-9431

NOTE

설 계 변 경
DESCRIPTION OF REVISION

번 호	내 용
일 자	설 계 경 토 심 사 승 인
2021.05	
승 인	APPROVED BY

축 척 SCALE	A1	1 / 125
	A3	1 / 250


도면명 DRAWING TITLE



지상1층 평면도

도면번호 DRAWING NO.
A 30 - 003

지상1층 평면도

축척 : 1 / 250

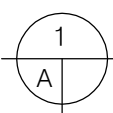

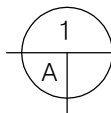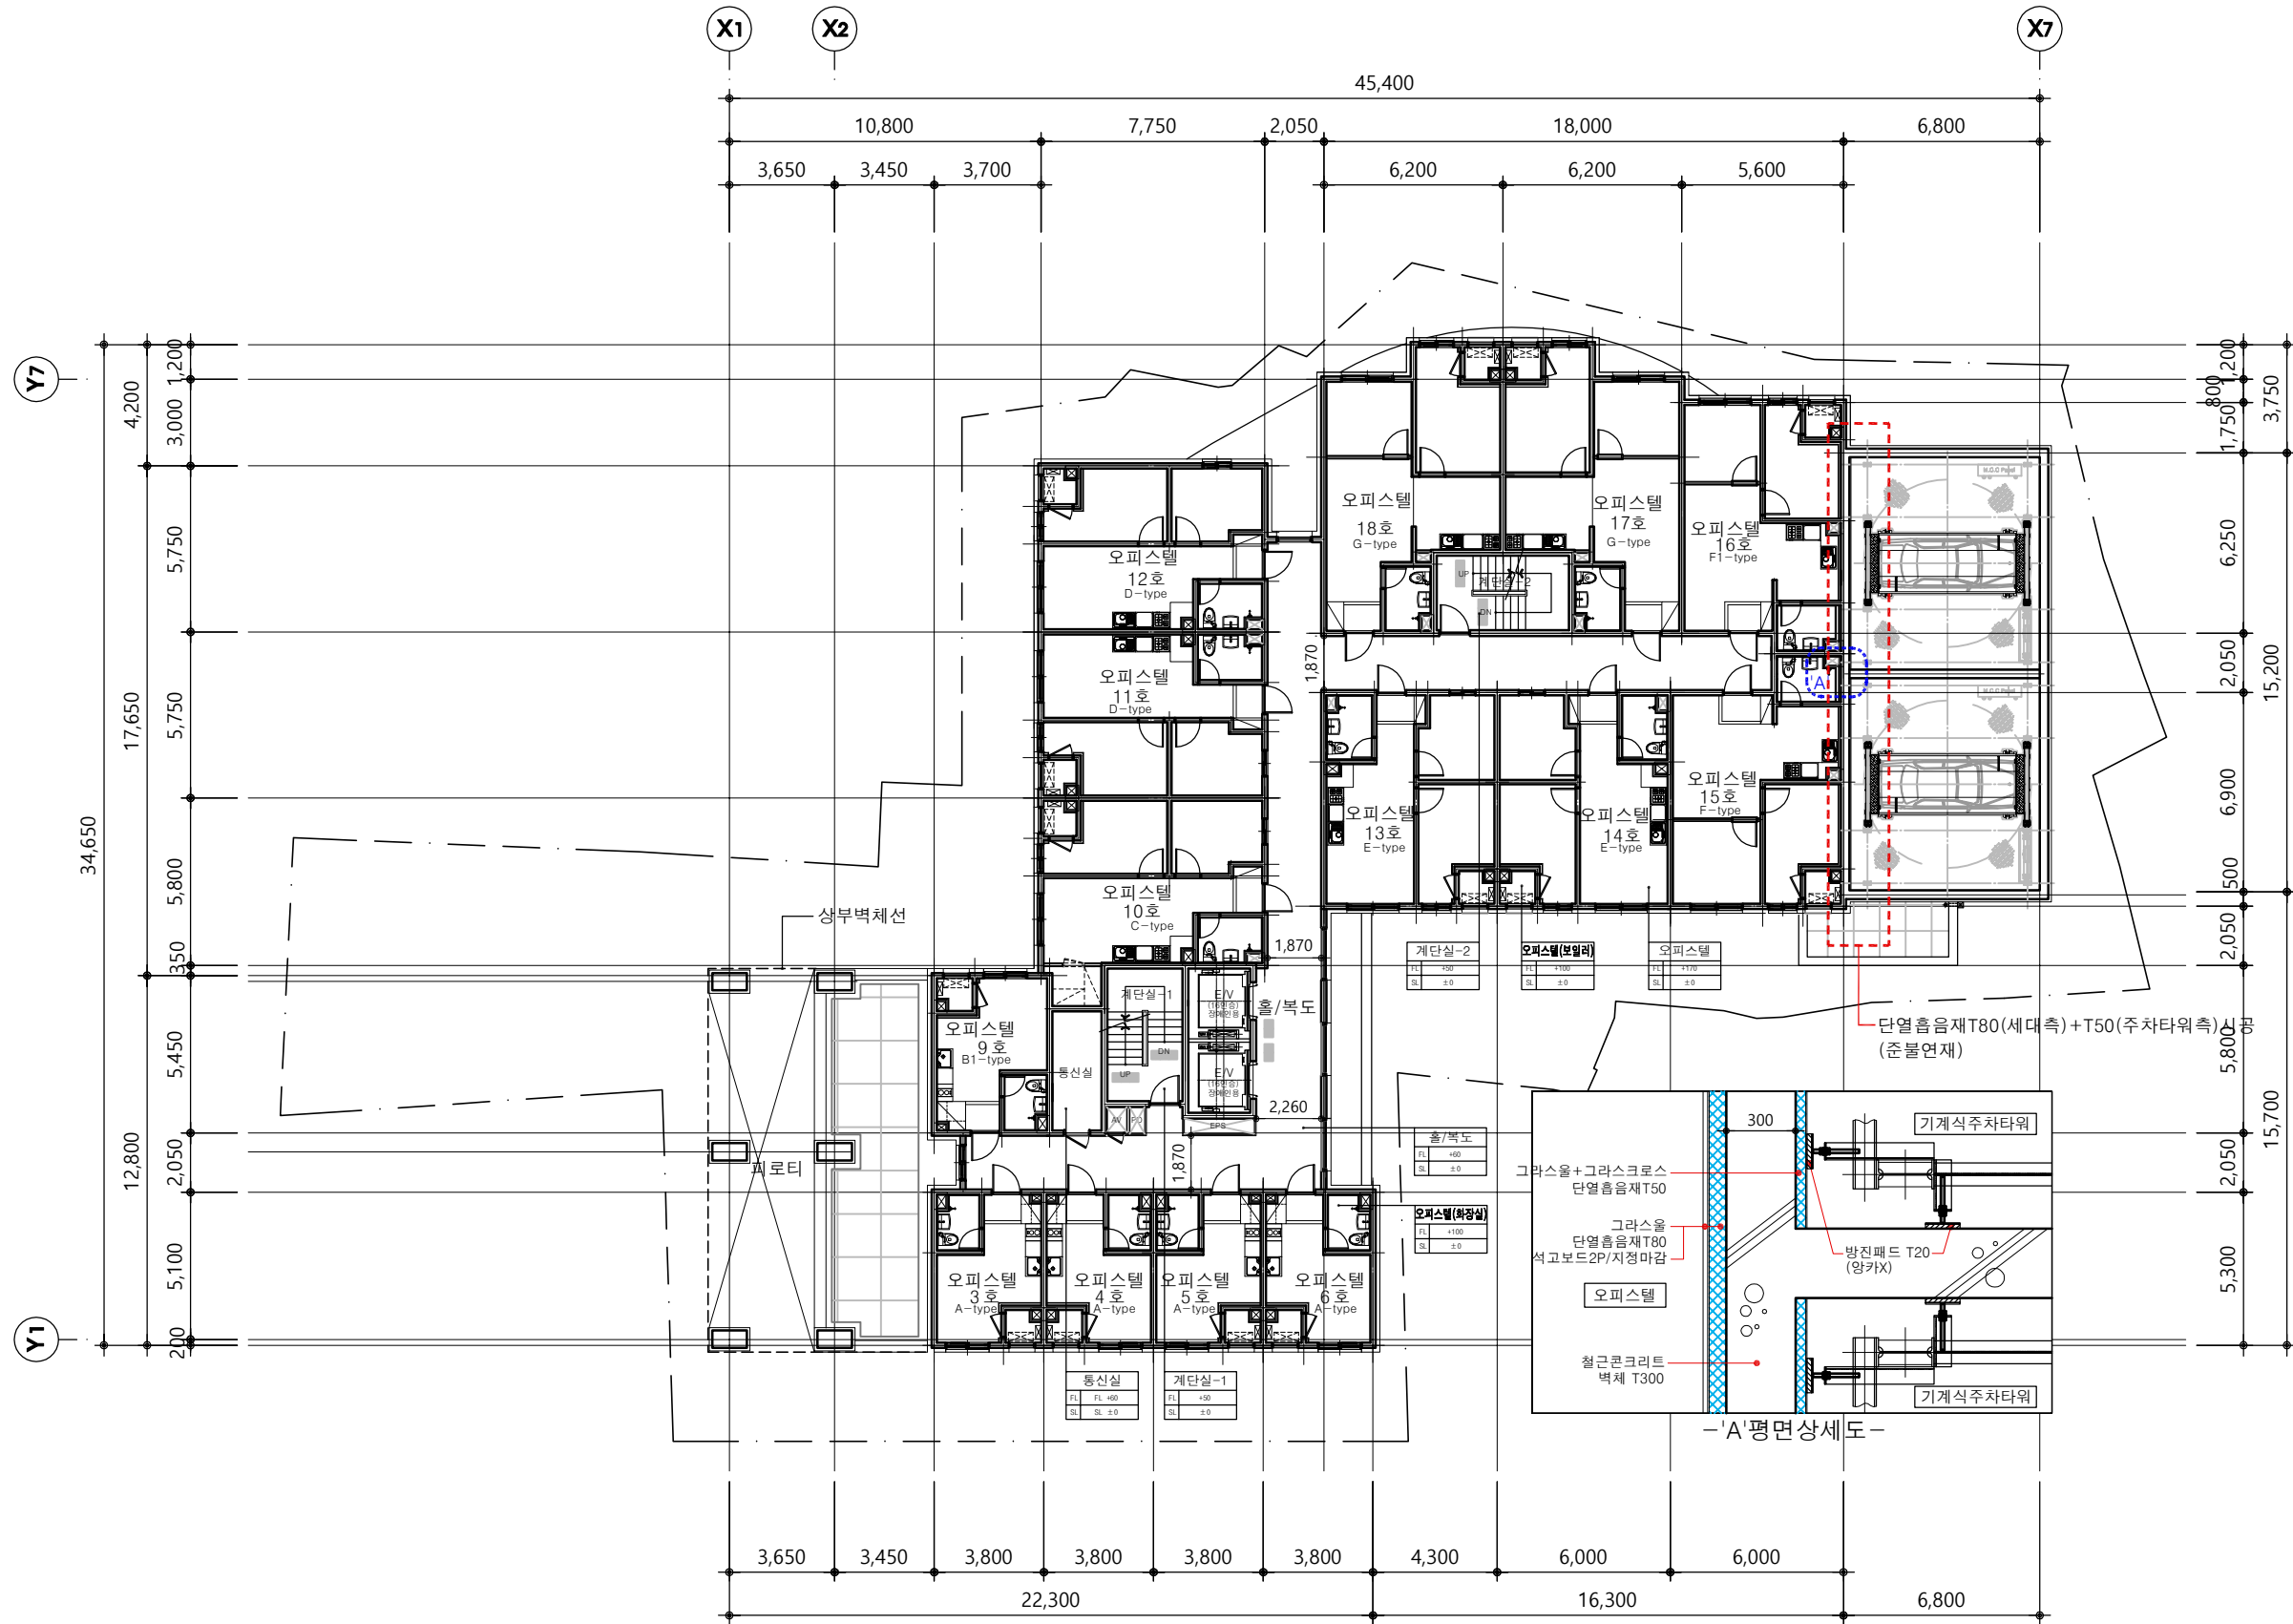

지상2층 평면도
축척 : 1 / 250

PROJECT TITLE

송인동 오피스텔
신축공사



제이케이건축사사무소(주)
Architects & Planners
TEL : 02-533-9431 FAX : 02-532-9431

NOTE

설 계 변 경
DESCRIPTION OF REVISION

번 호	내 용
일 자	설 계 경 토 심 사 승 인
2021.05	
승 인	APPROVED BY

축 척	SCALE	1 / 125
축 척	SCALE	1 / 250

도면명 DRAWING TITLE

지상2층 평면도

도면번호 DRAWING NO.

A 30 - 004

PROJECT TITLE

송인동 오피스텔
신축공사



제이케이건축사사무소(주)
Architects & Planners

TEL : 02-533-9431 FAX : 02-532-9431

NOTE

설 계 변 경
DESCRIPTION OF REVISION

번 호	내 용
일 자	설 계 경 토 심 사 승 인
2021.05	
승인 APPROVED BY	


축척 SCALE	A1	1 / 125
	A3	1 / 250

도면명 DRAWING TITLE

지상3-9층 평면도
(기준층)

도면번호 DRAWING NO.

A 30 - 005

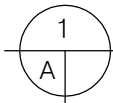

(기준층)
지상3-9층 평면도

축척 : 1 / 250

PROJECT TITLE

송인동 오피스텔
신축공사



제이케이건축사사무소(주)
Architects & Planners

TEL : 02-533-9431 FAX : 02-532-9431

NOTE

설 계 변 경
DESCRIPTION OF REVISION

번 호	내 용
일 자	설 계 경 토 심 사 승 인
2021.05	
승인 APPROVED BY	


축척 SCALE	A1	1 / 125
	A3	1 / 250

도면명 DRAWING TITLE

지상10층 평면도


도면번호 DRAWING NO.

A 30 - 006

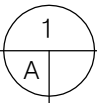

지상10층 평면도

축척 : 1 / 250

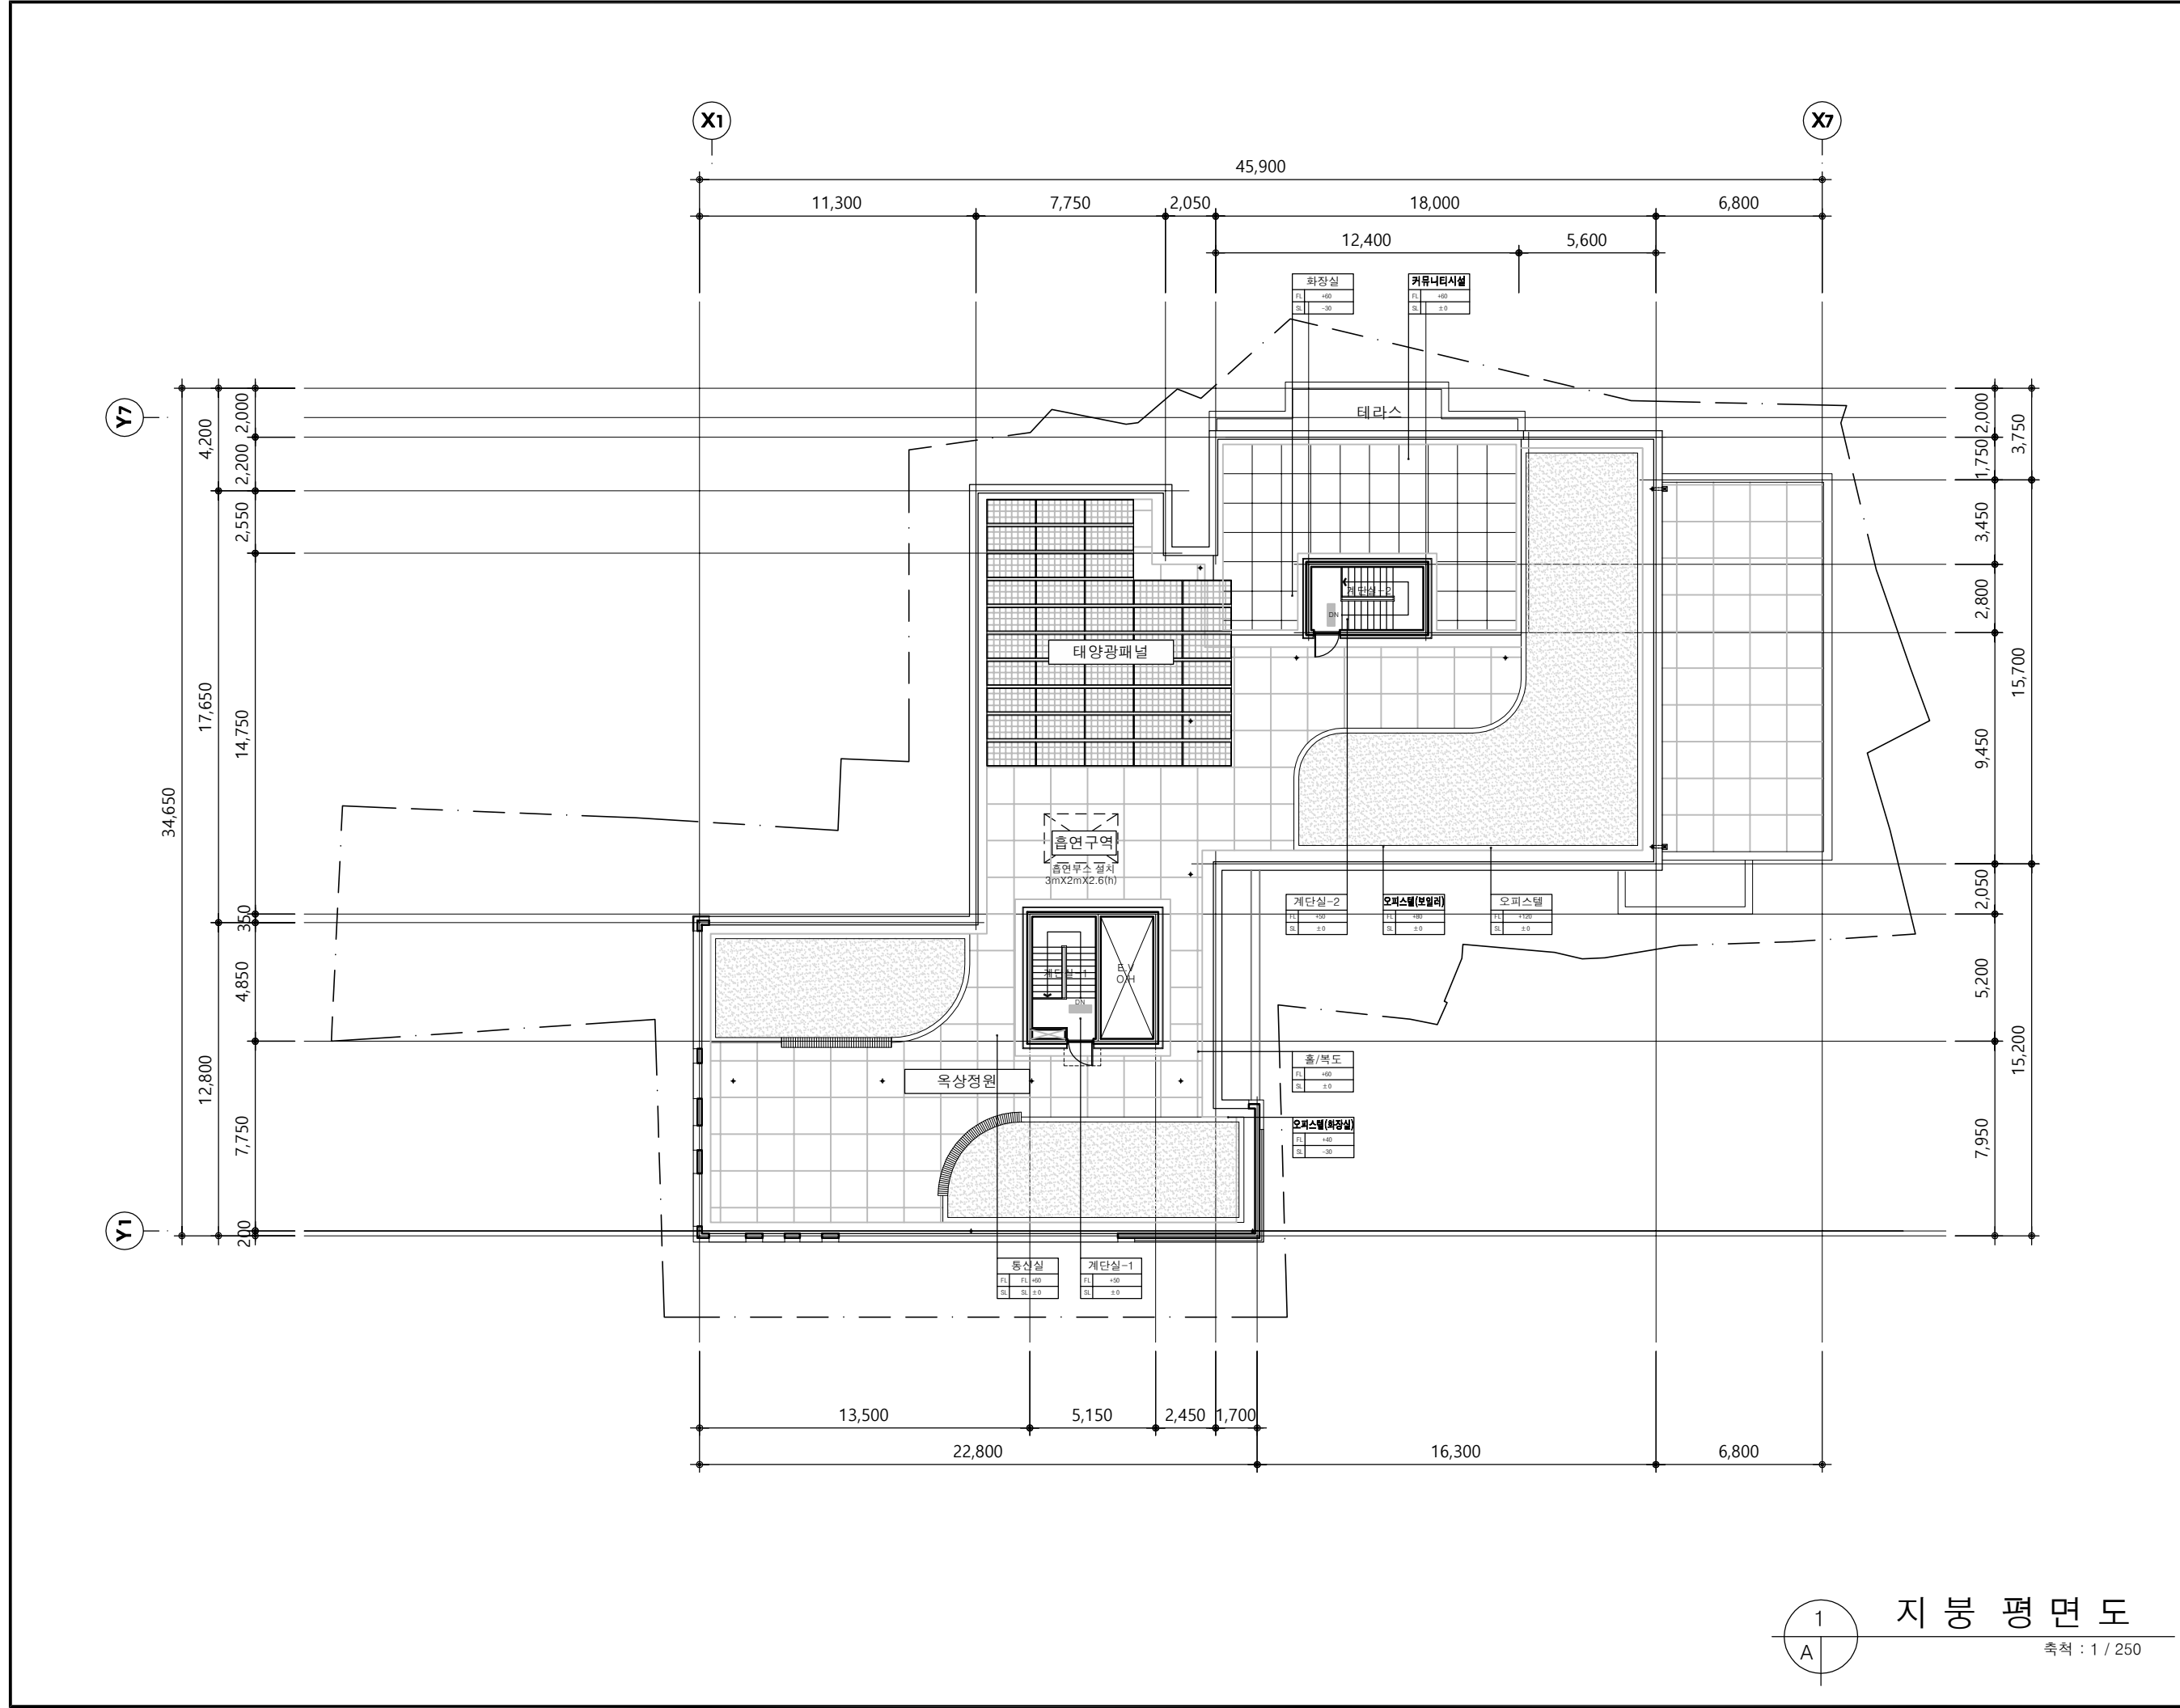

PROJECT TITLE

송인동 오피스텔
신축공사



제이케이건축사사무소(주)
Architects & Planners
TEL : 02-533-9431 FAX : 02-532-9431

NOTE

설 계 변 경
DESCRIPTION OF REVISION

번 호	내 용
일 자	설 계
2021.05	경 토
	심 사
	승 인

승인 APPROVED BY


축척 SCALE	A1	1 / 125
	A3	1 / 250

도면명 DRAWING TITLE



지 붕 평 면 도

도면번호 DRAWING NO.

A 30 - 007

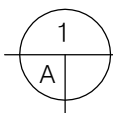

지 붕 평 면 도
축척 : 1 / 250

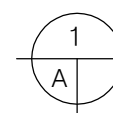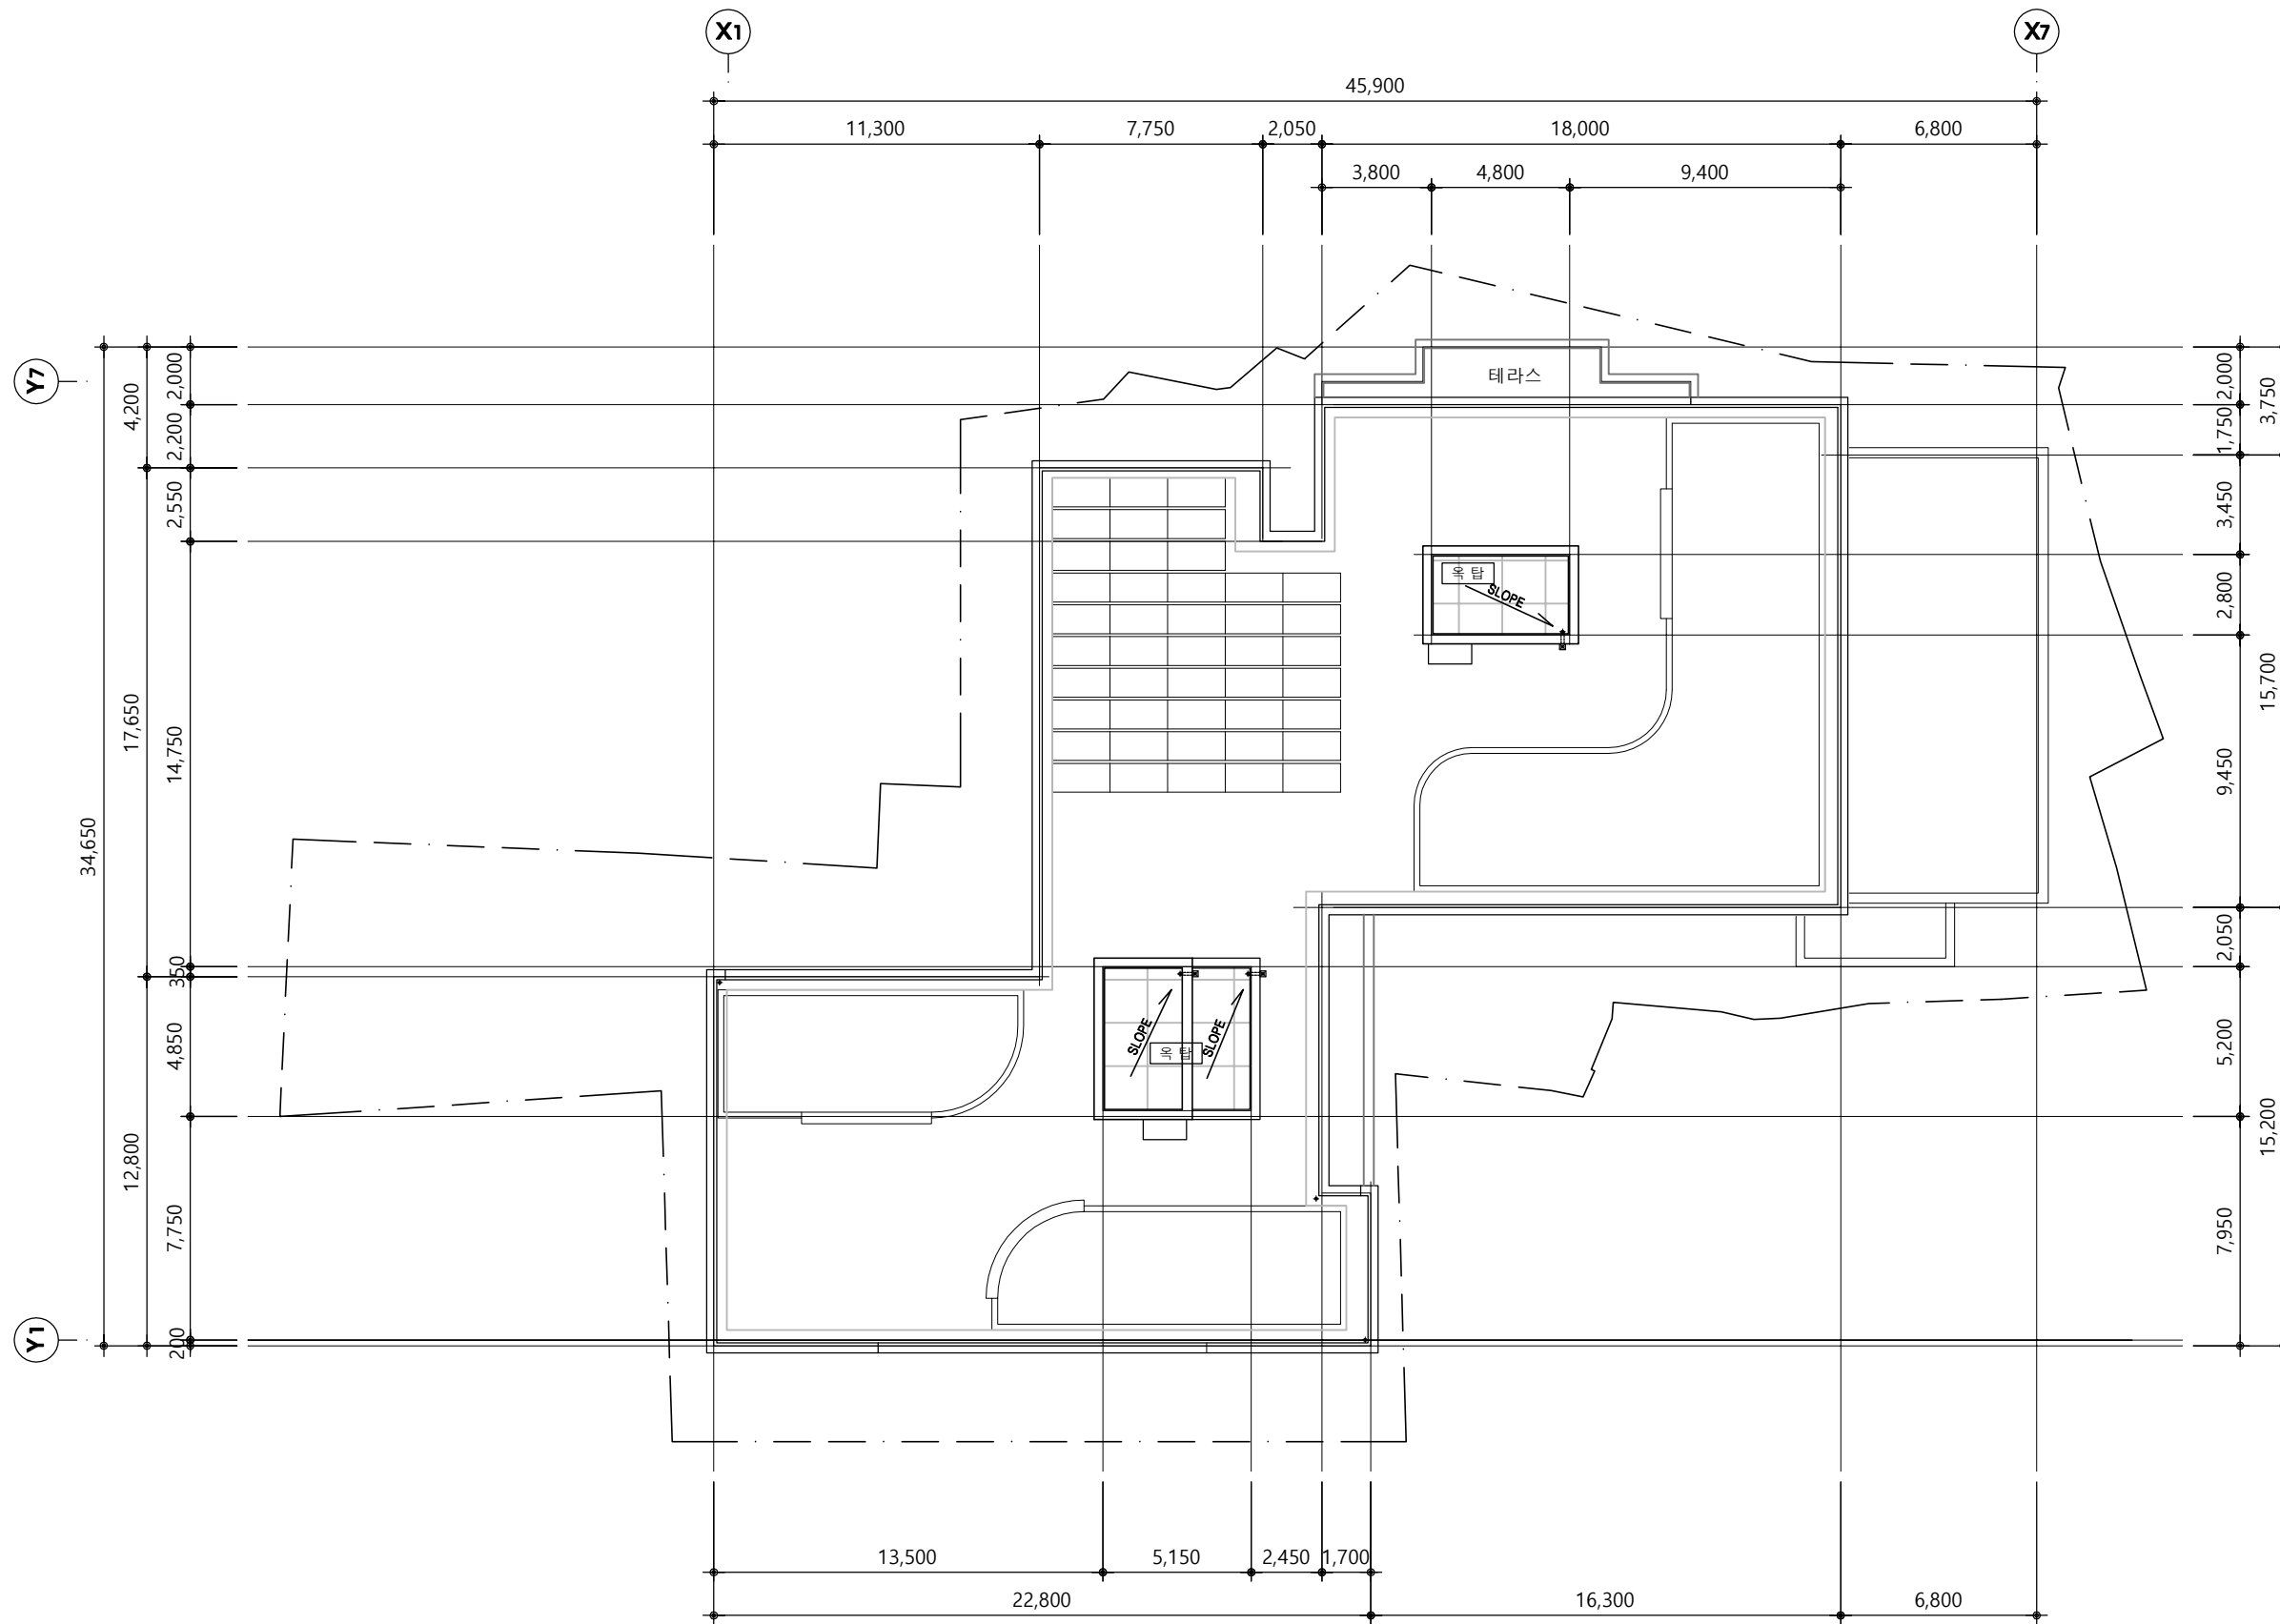

옥탑 지붕평면도
축척 : 1 / 250

PROJECT TITLE
송인동 오피스텔
신축공사

제이케이건축사사무소(주)
Architects & Planners
TEL : 02-533-9431 FAX : 02-532-9431

NOTE

실 계 변 경
DESCRIPTION OF REVISION

번 호	내 용
일 자	설 계 경 토 심 사 승 인
△	2021.05

승 인 APPROVED BY



축 척
SCALE

A1	1 / 125
A3	1 / 250

도면명 DRAWING TITLE

옥탑 지붕평면도

도면번호 DRAWING NO.
A 30 - 008

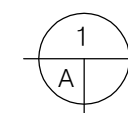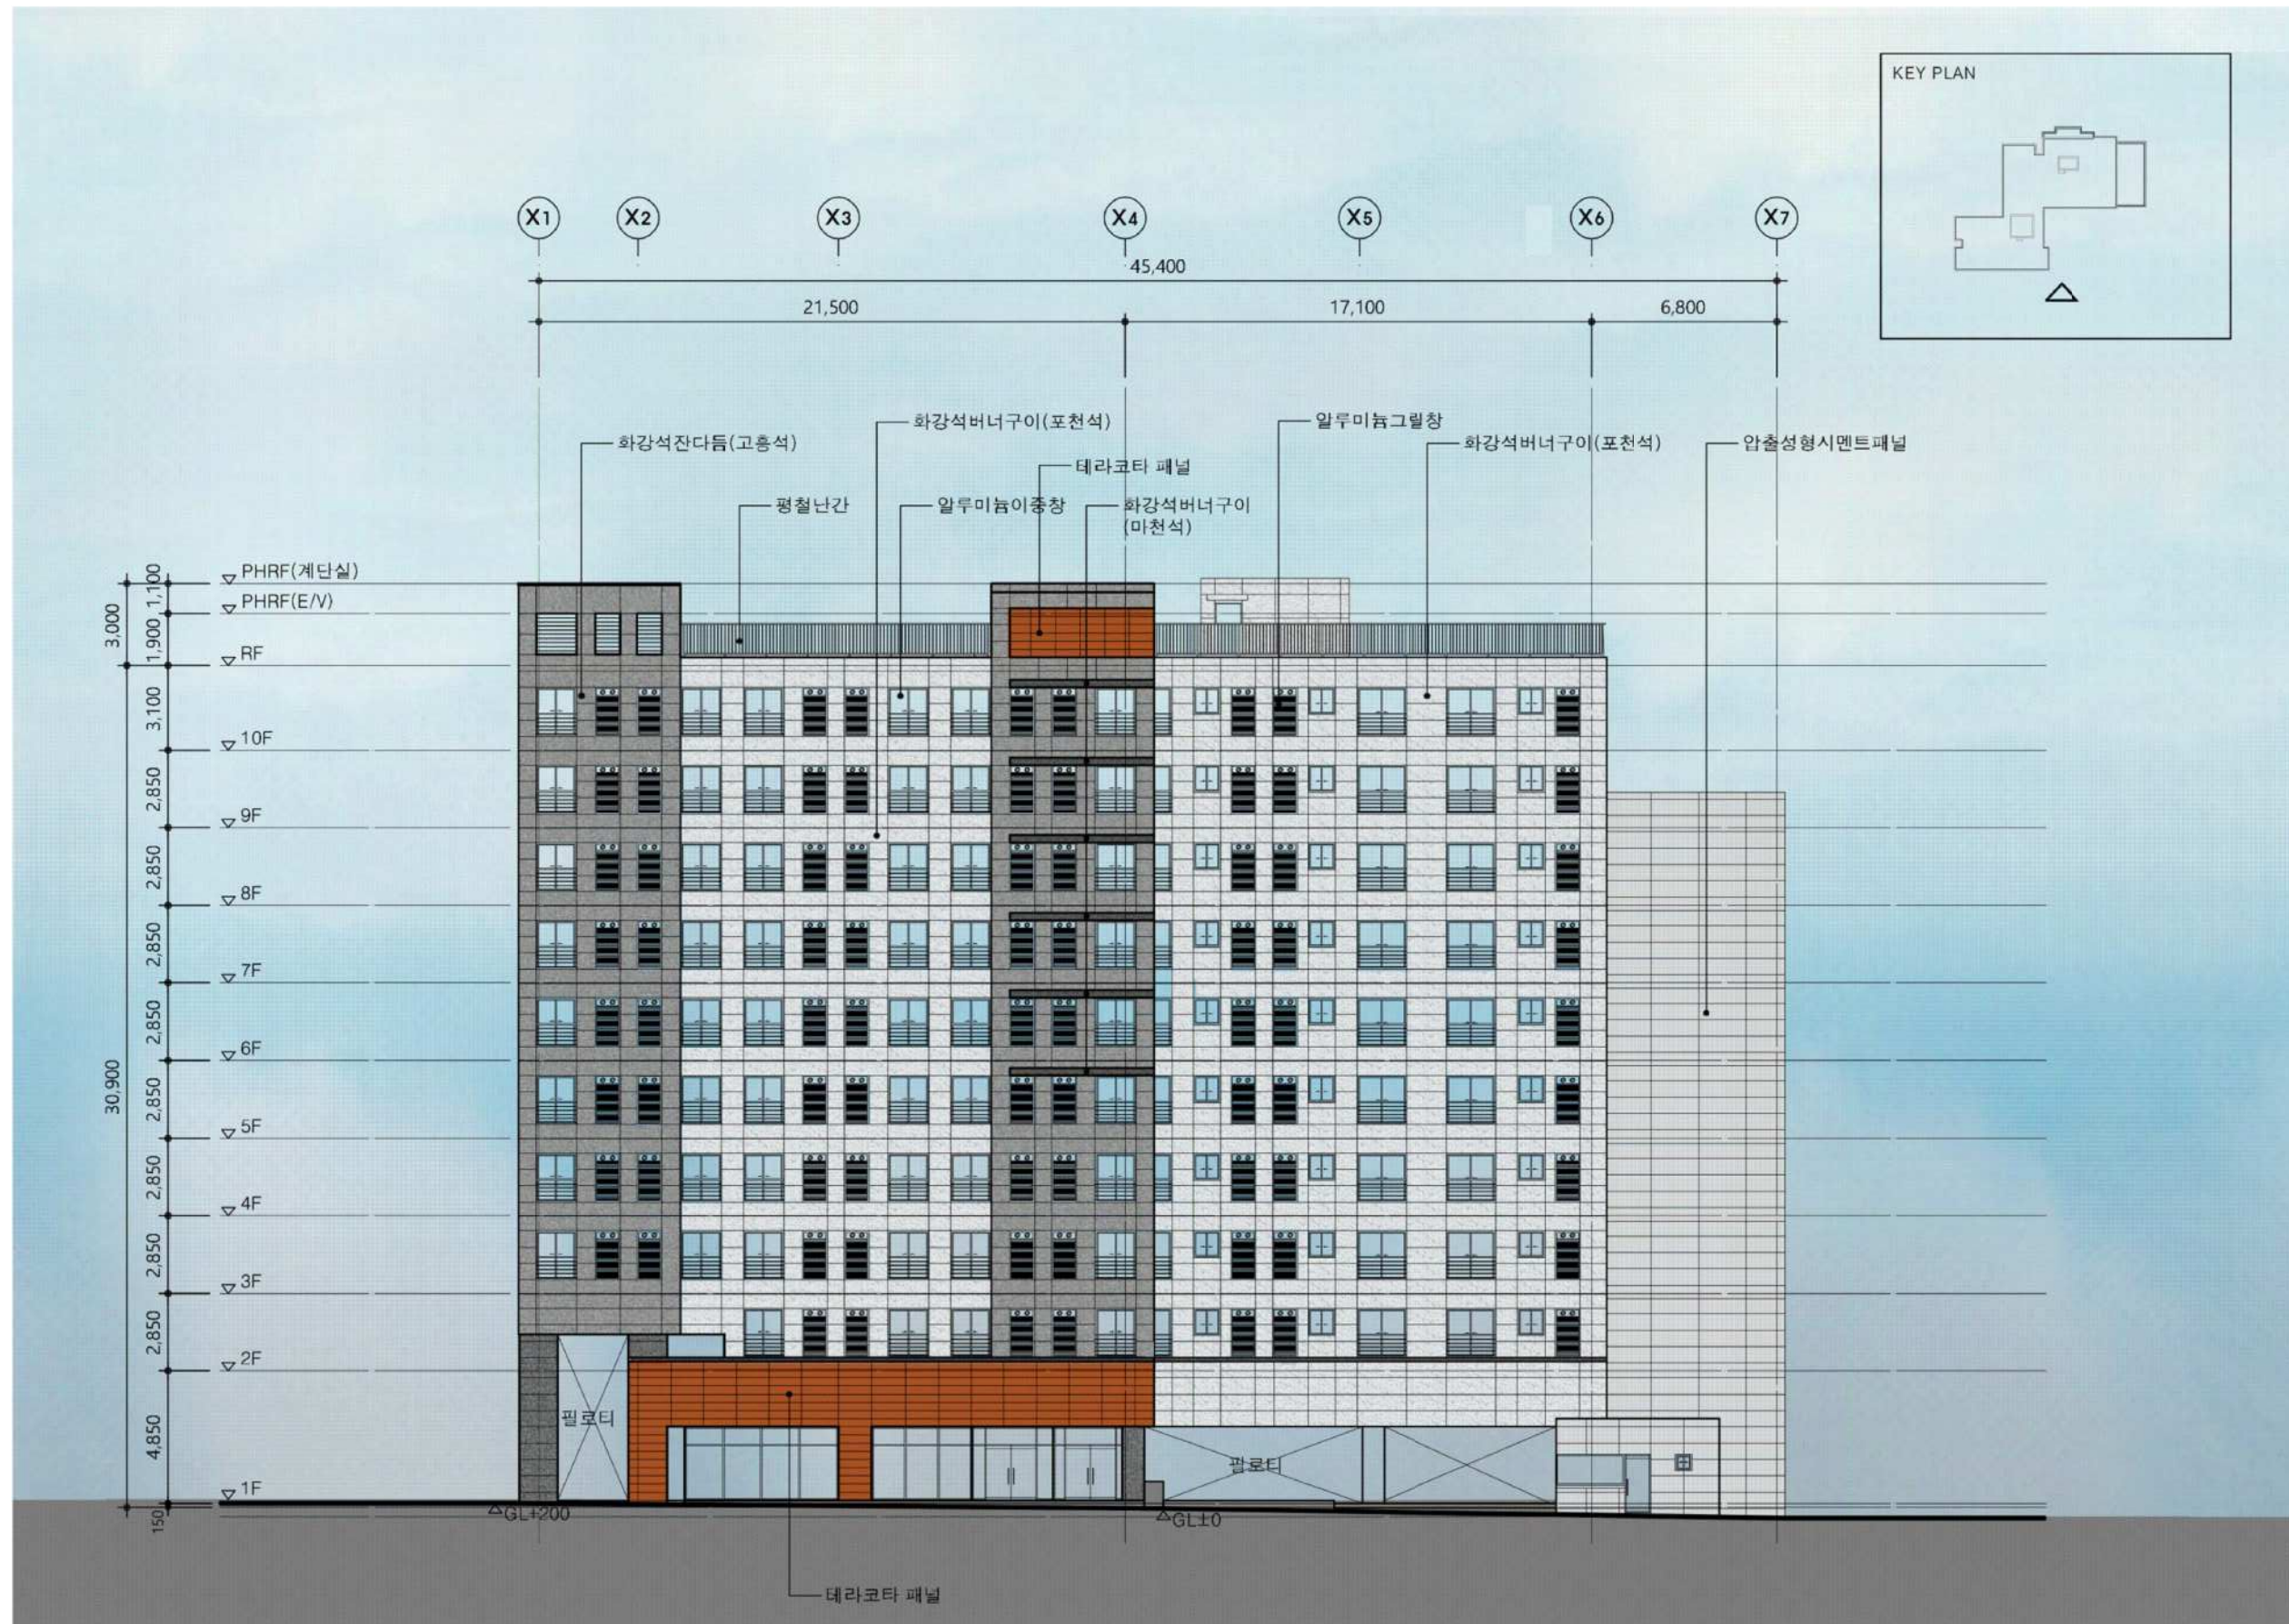

정 면 도

축척 : 1 / 250

설 계 변 경
DESCRIPTION OF REVISION

번 호	내 용
일 자	설 계 경 토 심 사 승 인
2021.05	

승인 APPROVED BY

축 척	A1	1 / 125
SCALE	A3	1 / 250


도면명 DRAWING TITLE

정 면 도

도면번호 DRAWING NO.
A30 - 009

제이케이건축사사무소(주)
Architects & Planners
TEL : 02-533-9431 FAX : 02-532-9431

NOTE

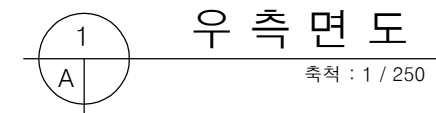

축척 : 1 / 250

설 계 변 경 DESCRIPTION OF REVISION				
번 호	내 용			
일 자	설계	검토	심사	승인
 2021.05				
승인 APPROVED BY				

측척 SCALE	A1	1 / 125
	A3	1 / 250

도면명	DRAWING TITLE
-----	---------------

우 측 면 도


도면번호 DRAWING NO.
A30 - 010

제이케이건축사사무소(주)
Architects & Planners
TEL : 02-533-9431 FAX : 02-532-9431

설 계 변 경

축척 SCALE	A1	1 / 125
	A3	1 / 250


도면번호 DRAWING NO.
A30 - 011

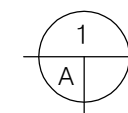

축척 : 1 / 250

jk
제이케이건축사사무소(주)
Architects & Planners
TEL : 02-533-9431 FAX : 02-532-9431

NOTE

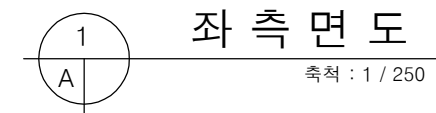

축척 : 1 / 250

설 계 변 경 DESCRIPTION OF REVISION				
번 호	내 용			
일 자	설 계	검 토	심 사	승 인
	2021.05			
승인 APPROVED BY				

종 척 SCALE	A1	1 / 125
	A3	1 / 250

도면명 DRAWING TITLE

좌 측 면 도

도면번호 DRAWING NO.
A30 - 012