



PROJECT TITLE
사 업 명 칭
(만족동 456-55,56)

면목동 도시형생활주택
신축공사

NAME OF DRAWING
도 면 명

투 시 도

NOTE
주 기

▼ ▼

DATE ▲ REVISIONS ▲ NO.
일 자 수 정

DESIGNED BY
설 계

CHECKED BY
심 사

APPROVED BY
승 인




CONSULTANTS
협 동 설 계

SCALE
축 척 NONE

DATE
일 자 2023 . 11

DWG NO.
도 면 번 호 A - 002



FILE NAME.
화 일 명

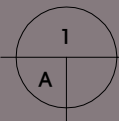

투 시 도
SCALE : none

TECH 1 테크원
건축사사무소

TECHONE ARCHITECTS & ENGINEERS
CO., LTD
TEL. 02)482-2466(대)
FAX. 02)488-2466

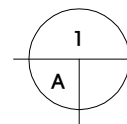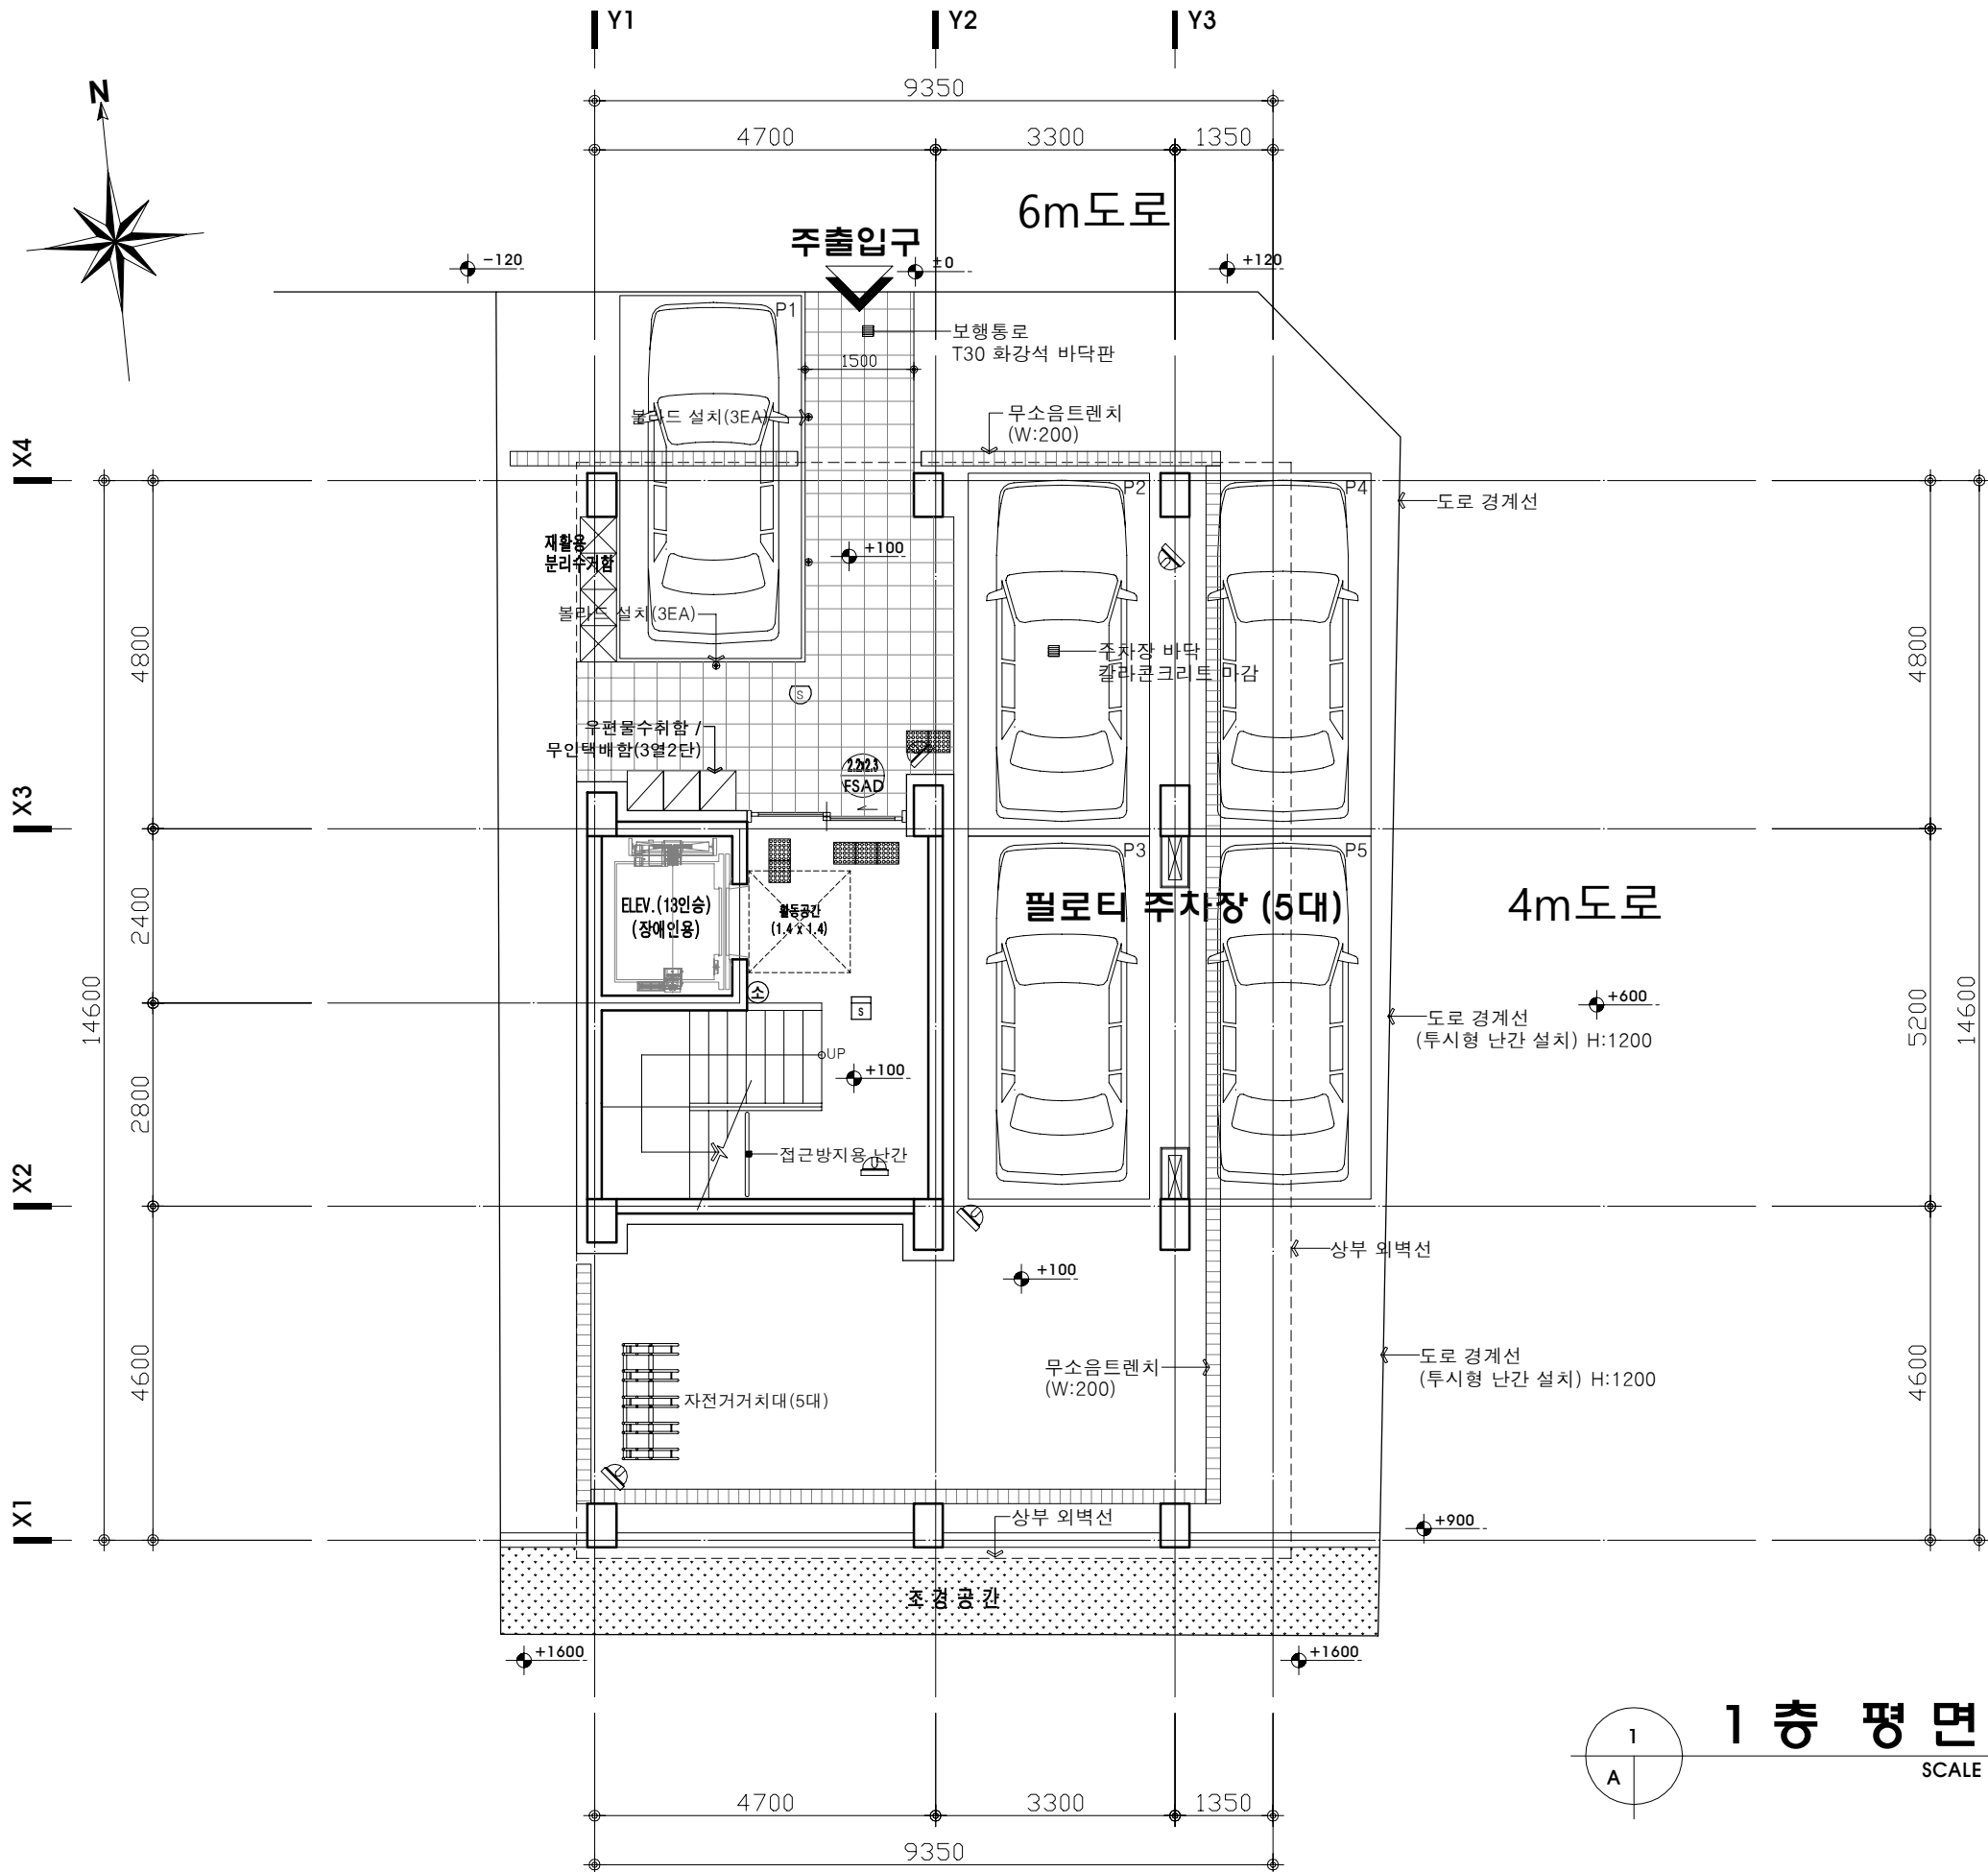

1 층 평면도

SCALE : 1/100

PROJECT TITLE
사 업 명 칭
(면적: 456-55,56)

면적: 456-55,56
신축공사

NAME OF DRAWING
도 면 명

1 층 평면도

NOTE
주 기

- 단독경보감지기(연기)
- 단독경보감지기(열)
- ABC분말소화기(2.5KG)
- 가스누설경보기
- 일산화탄소경보기
- CCTV : 필로티내 4개소
(CCTV 설비평면도 참조)

- 1.콘크리트: fck = 27 MPa
- 2.철근 : fy = 400 MPa
- 3.세대간벽두께:180mm(복배근)
- 4.외벽두께:200mm(복배근)
- 5.코아벽두께:180mm(복배근)

DATE
일 자

REVISIONS
수 정

NO.

DESIGNED BY
설 계

CHECKED BY
심 사

APPROVED BY
승 인

CONSULTANTS
협 동 설 계

SCALE
축 척

1 / 100

DATE
일 자

2025 . 01

DWG NO.
도 면 번 호



A - 201

FILE NAME.
파 일 명

TECH 1 테크원
건축사사무소

TECHONE ARCHITECTS & ENGINEERS
CO., LTD


TEL. 02)482-2466(대)
FAX. 02)488-2466

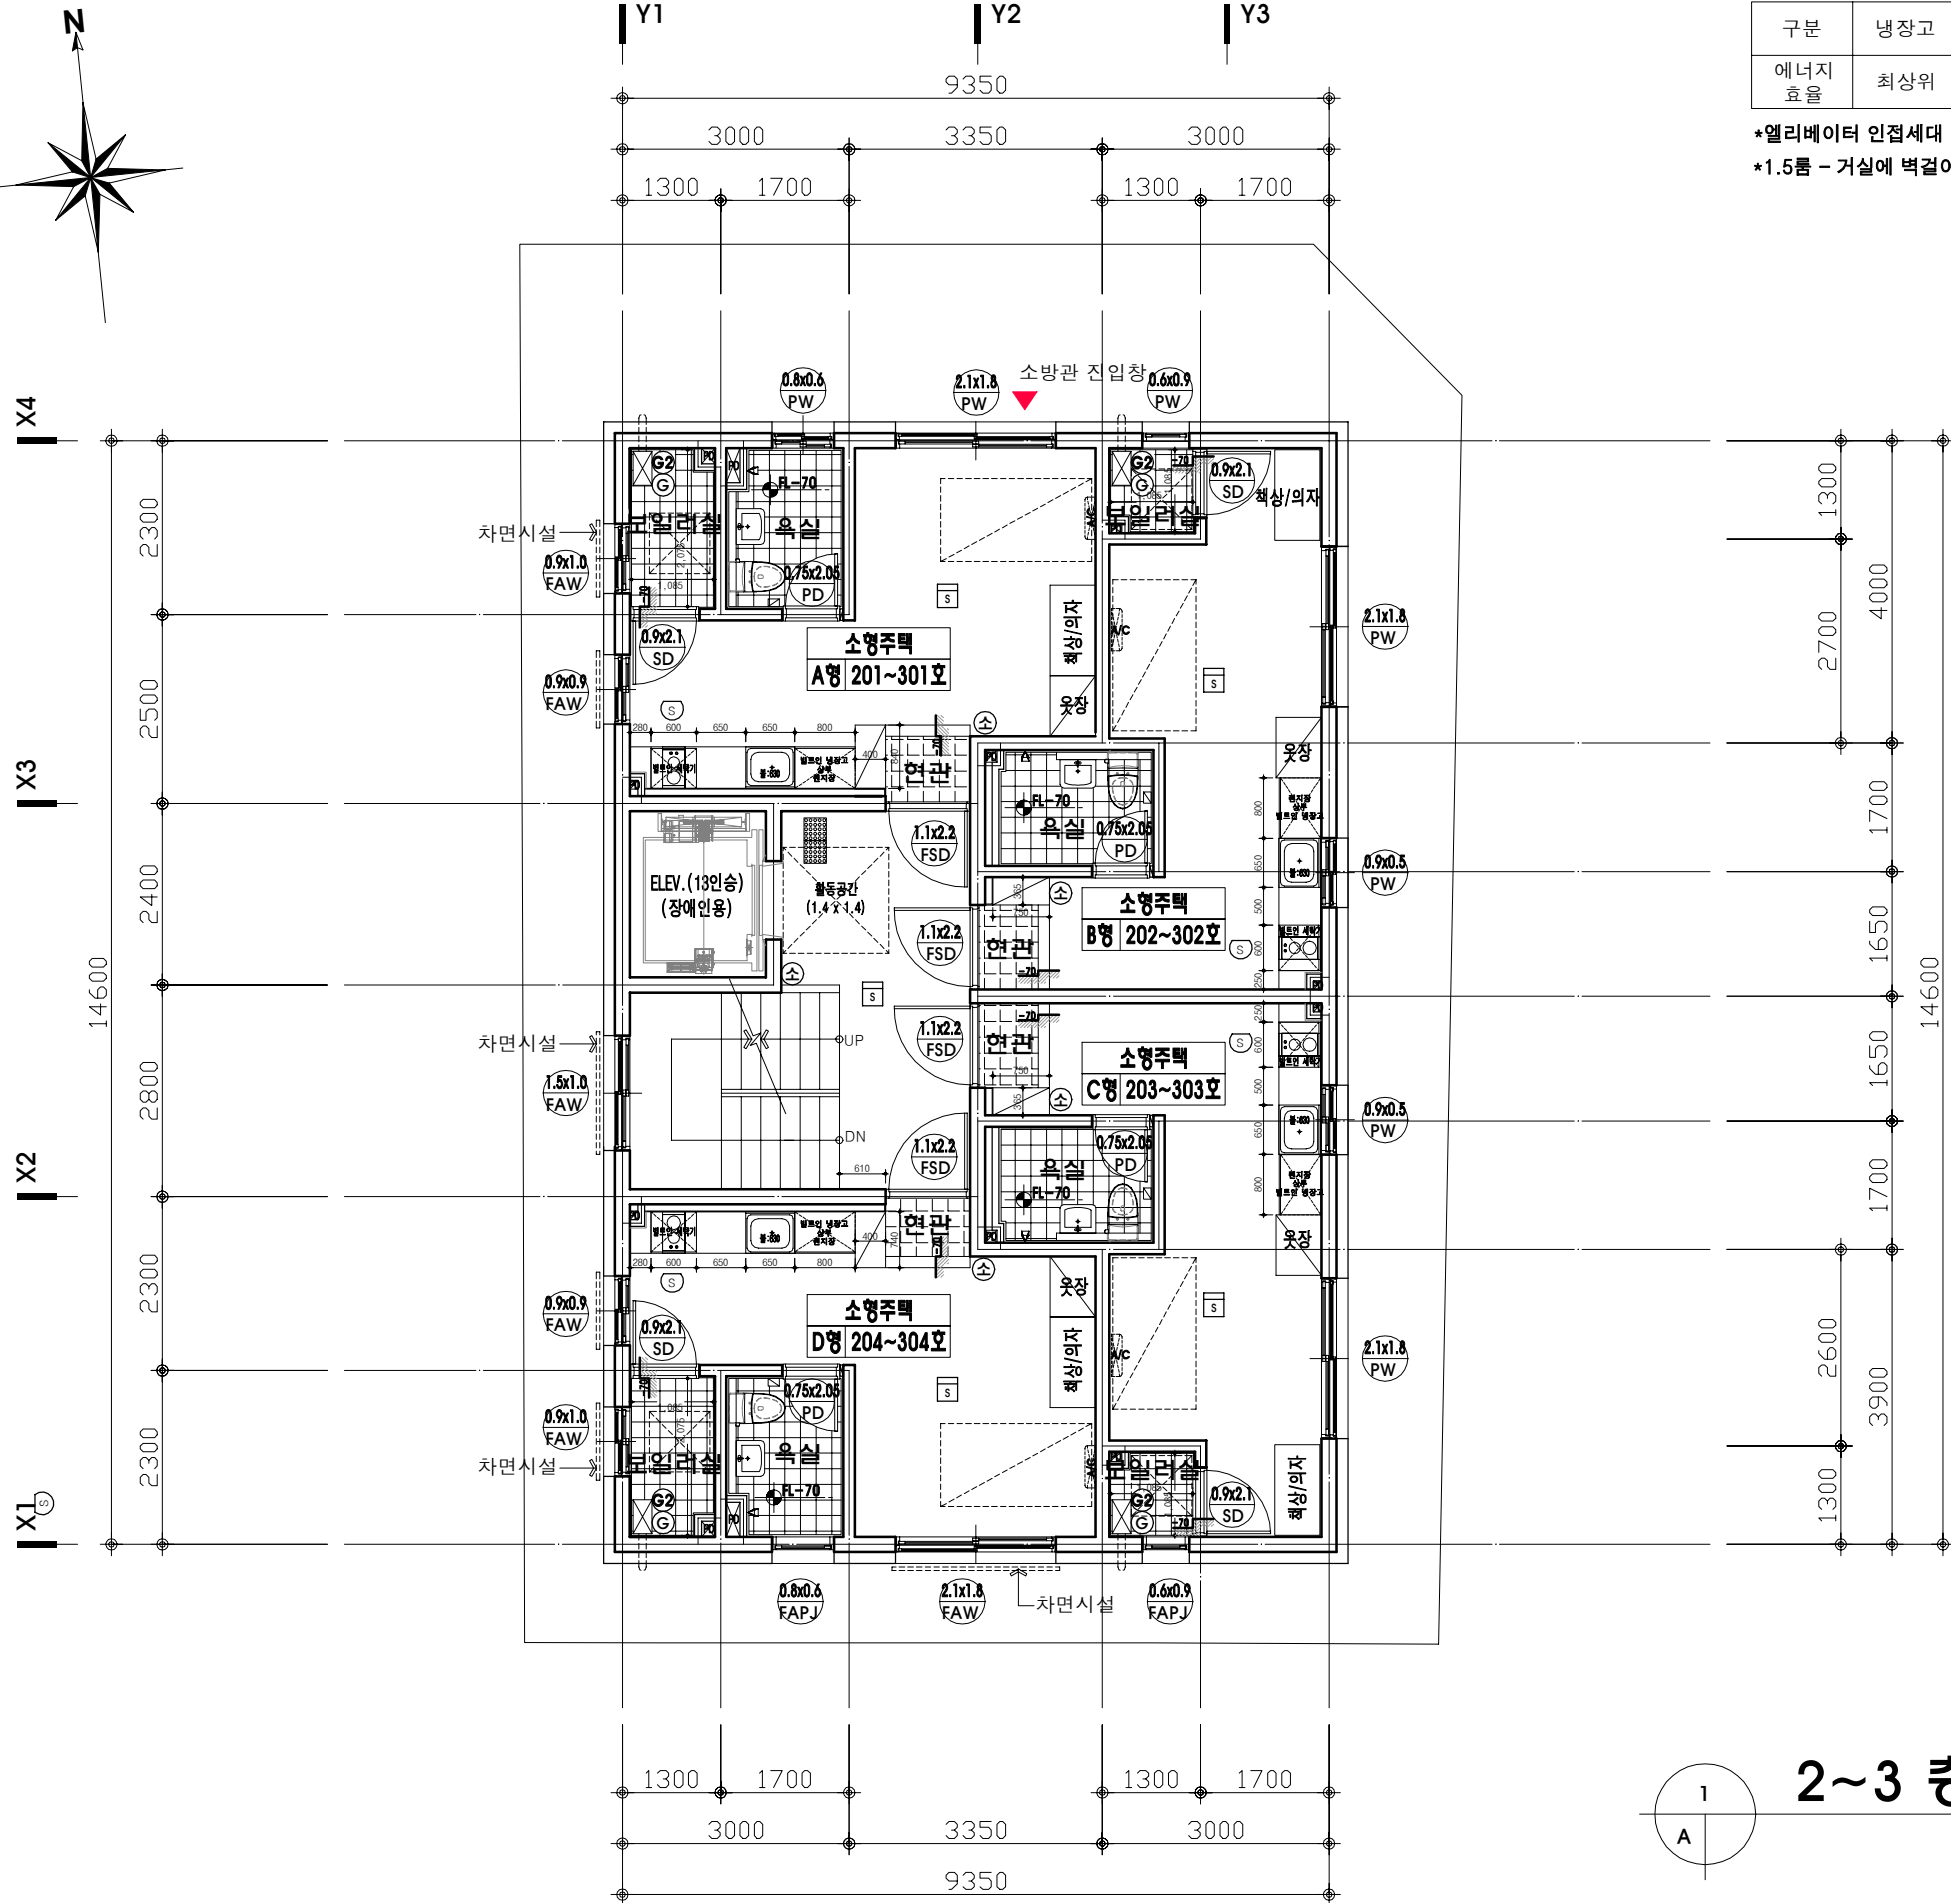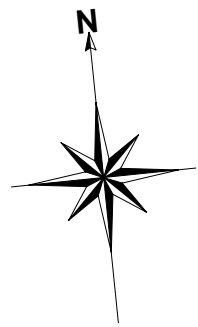

*빌트인 필수 품목

구분	냉장고	벽걸이 에어컨	세탁기	책상	이동식옷장
에너지 효율	최상위	최상위	최상위	-	-

- *엘리베이터 인접세대 벽체에 차음시트(3T) 부착
- *1.5룸 - 거실에 벽걸이 에어컨 빌트인 설치 + 방에 에어컨 배관 설치

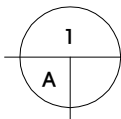

2~3 층 평 면 도

SCALE : 1/100

PROJECT TITLE
사 업 명 칭
(만족동 456-55,56)

면목동 도시형생활주택
신축공사

NAME OF DRAWING
도 면 명

2~3 층 평 면 도

- NOTE
주 기
- 단독경보감지기(연기)

단독경보감지기(열)

ABC분말소화기(2.5KG)

가스누설경보기

일산화탄소경보기

보일러

벽걸이 에어컨

에어컨 실외기

차면시설
- 1.콘크리트: fck = 27 MPa
2.철근 : fy = 400 MPa
3.세대간벽두께:180mm(복배근)
4.외벽두께:200mm(복배근)
5.코아벽두께:180mm(복배근)
6.스라브두께:210mm(복배근)
(최상층은180mm)
7.욕실, 다용도실-50슬라브다운

DATE	REVISIONS	NO.
일 자	수 정	

DESIGNED BY
설 계

CHECKED BY
심 사

APPROVED BY
승 인

CONSULTANTS
협 동 설 계

SCALE
축 척 1 / 100



DATE
일 자 2025 . 01

DWG NO.
도 면 번 호 A - 202

FILE NAME.
화 일 명



TECHONE ARCHITECTS & ENGINEERS
CO., LTD
TEL. 02)482-2466(대)
FAX. 02)488-2466

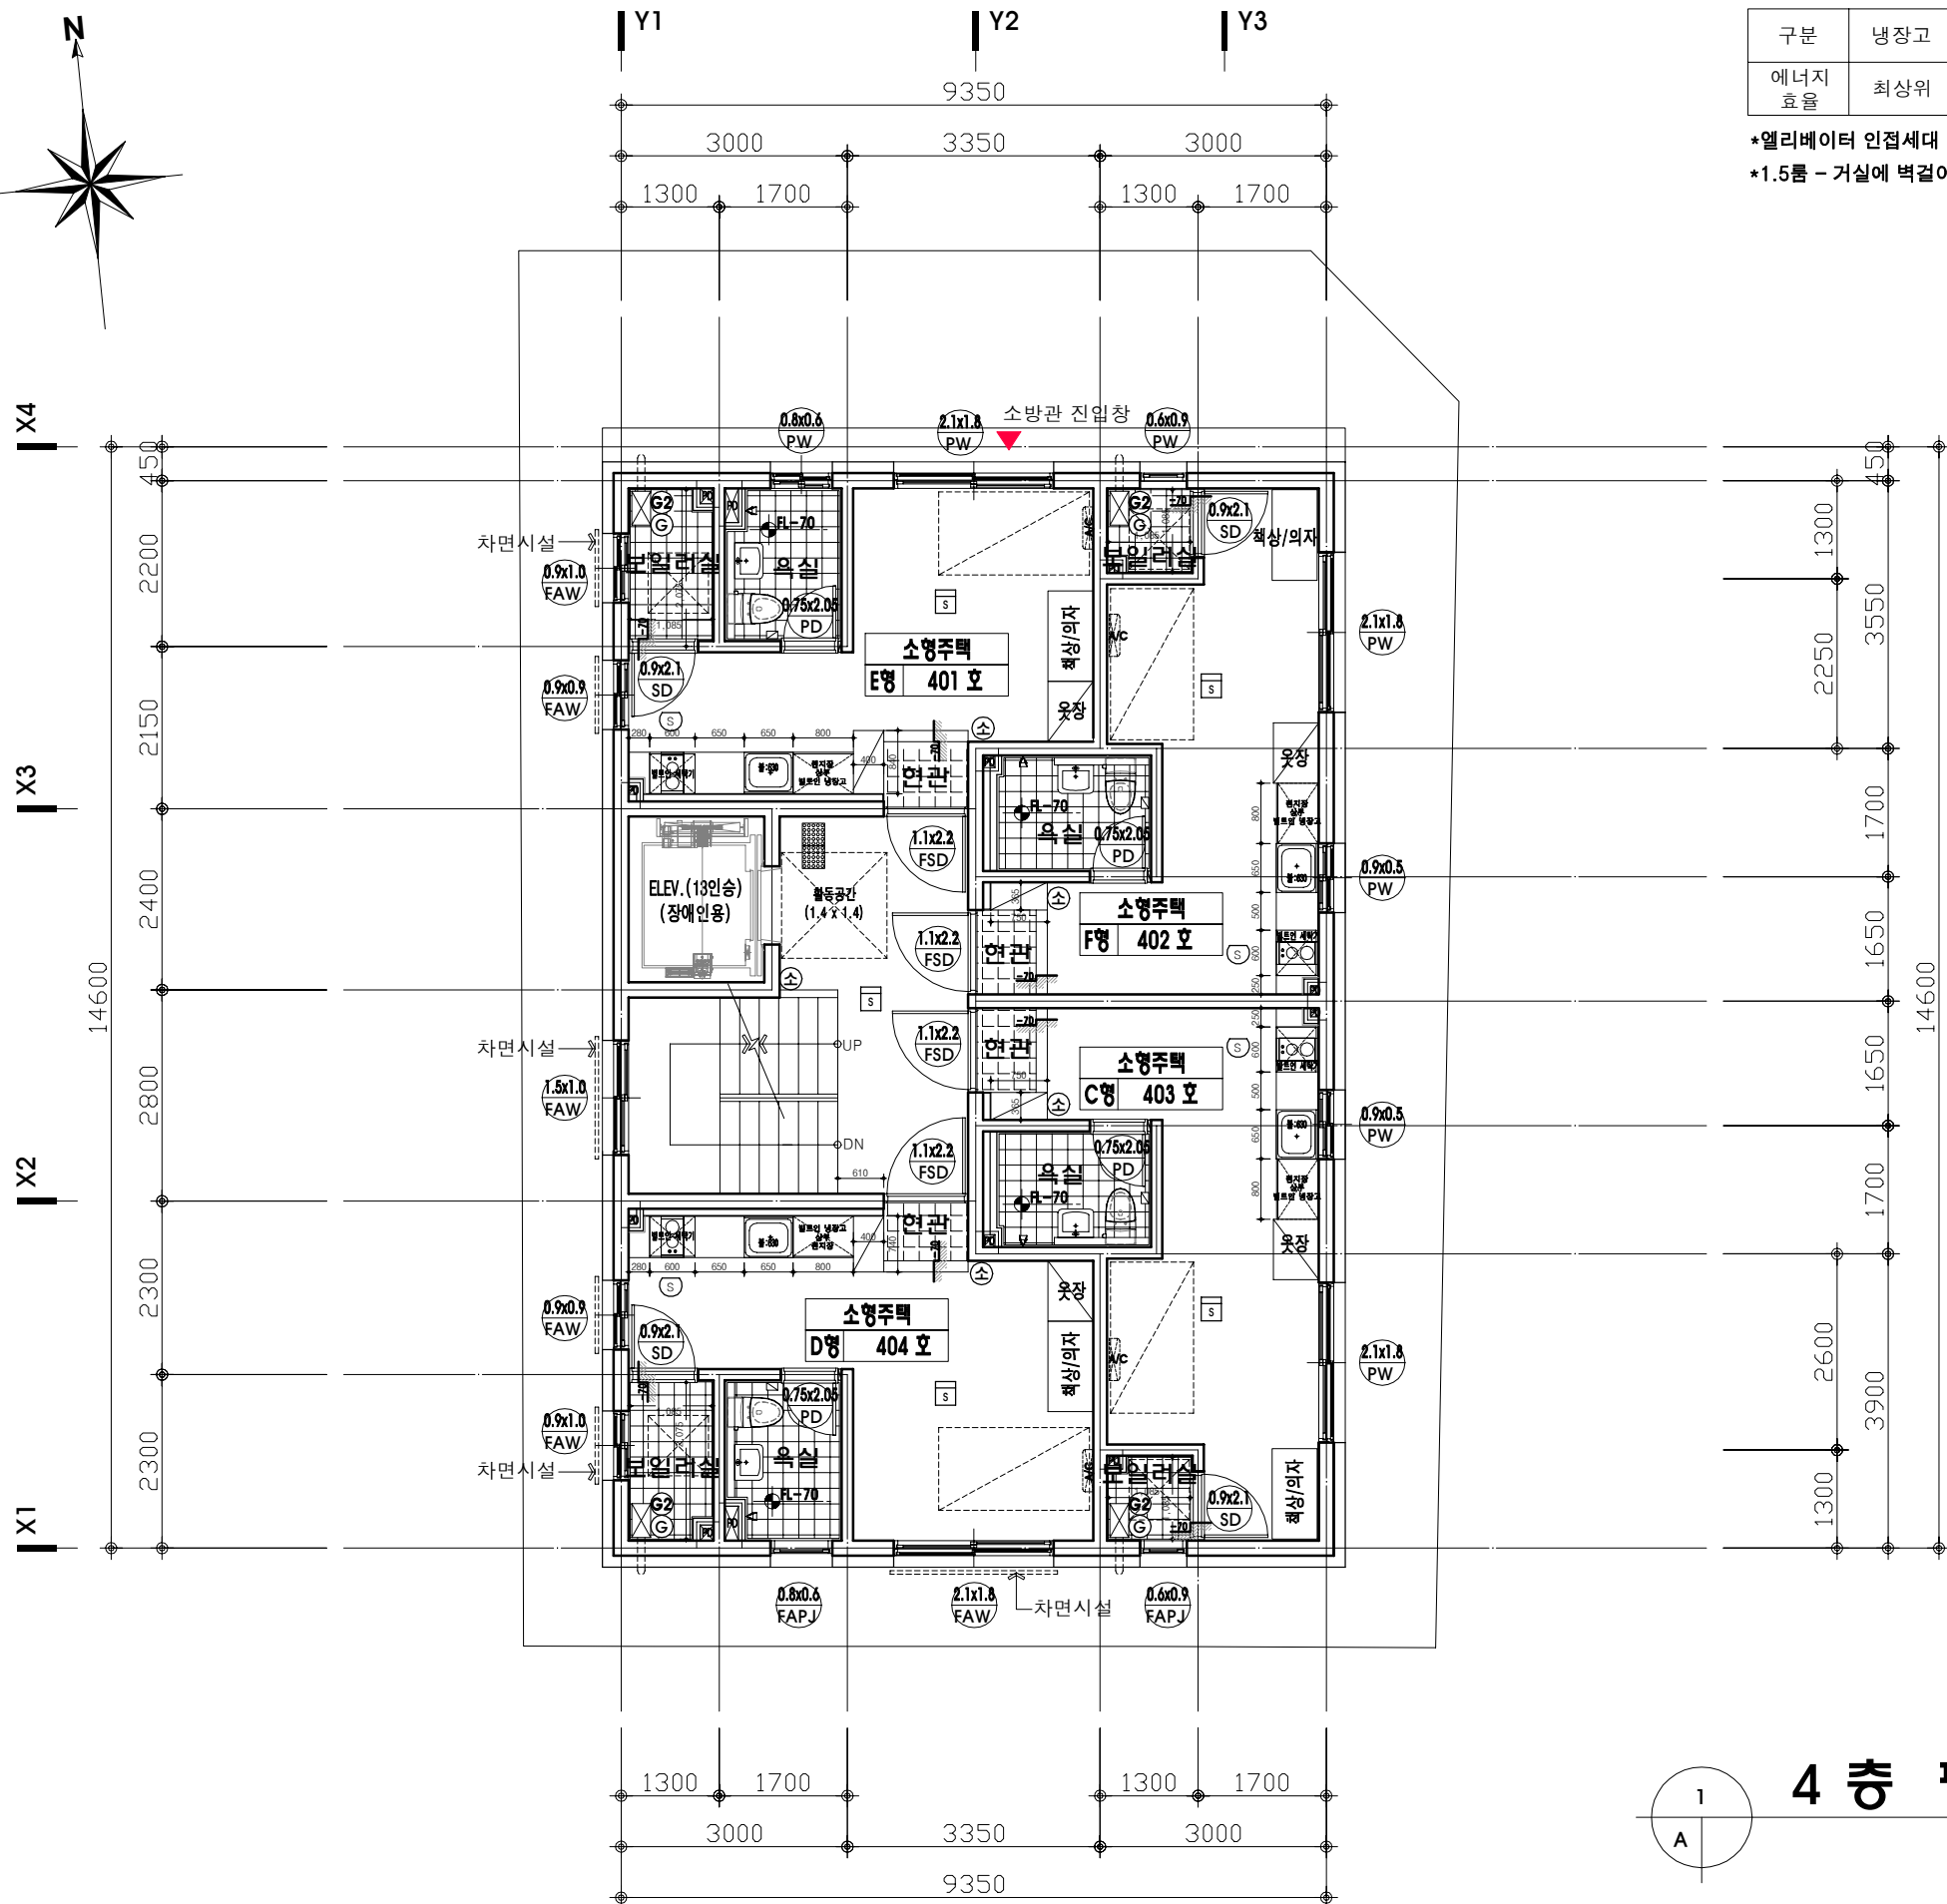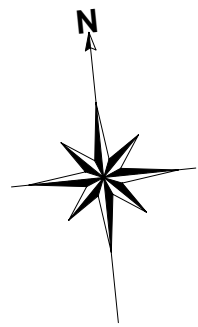


*빌트인 필수 품목

구분	냉장고	벽걸이 에어컨	세탁기	책상	이동식옷장
에너지 효율	최상위	최상위	최상위	-	-

*엘리베이터 인접세대 벽체에 차음시트(3T) 부착

*1.5룸 - 거실에 벽걸이 에어컨 빌트인 설치 + 방에 에어컨 배관 설치

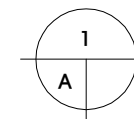

4 층 평 면 도

SCALE : 1/100

PROJECT TITLE
사 업 명 칭
(만족동 456-55,56)

면목동 도시형생활주택
신축공사

NAME OF DRAWING
도 면 명

4 층 평 면 도

NOTE
주 기

- 단독경보감지기(연기)
- 단독경보감지기(열)
- ABC분말소화기(2.5KG)
- 가스누설경보기
- 일산화탄소경보기
- 보일러
- 벽걸이 에어컨
- 에어컨 실외기
- 차면시설
- 1.콘크리트: fck = 27 MPa
- 2.철근 : fy = 400 MPa
- 3.세대간벽두께:180mm(복배근)
- 4.외벽두께:200mm(복배근)
- 5.코아벽두께:180mm(복배근)
- 6.스라브두께:210mm(복배근)
- (최상층은180mm)
- 7.욕실, 다용도실-50슬라브다운

DATE ▲ REVISIONS ▲ NO.
일 자 수 장

DESIGNED BY
설 계

CHECKED BY
심 사

APPROVED BY
승 인

CONSULTANTS
협 동 설 계

SCALE
축 척 1 / 100

DATE
일 자 2025 . 01


DWG NO.
도 면 번 호 A - 203

FILE NAME.
화 일 명

TECH 1 테크원
건축사사무소

TECHONE ARCHITECTS & ENGINEERS
CO., LTD

TEL. 02)482-2466(대)
FAX. 02)488-2466

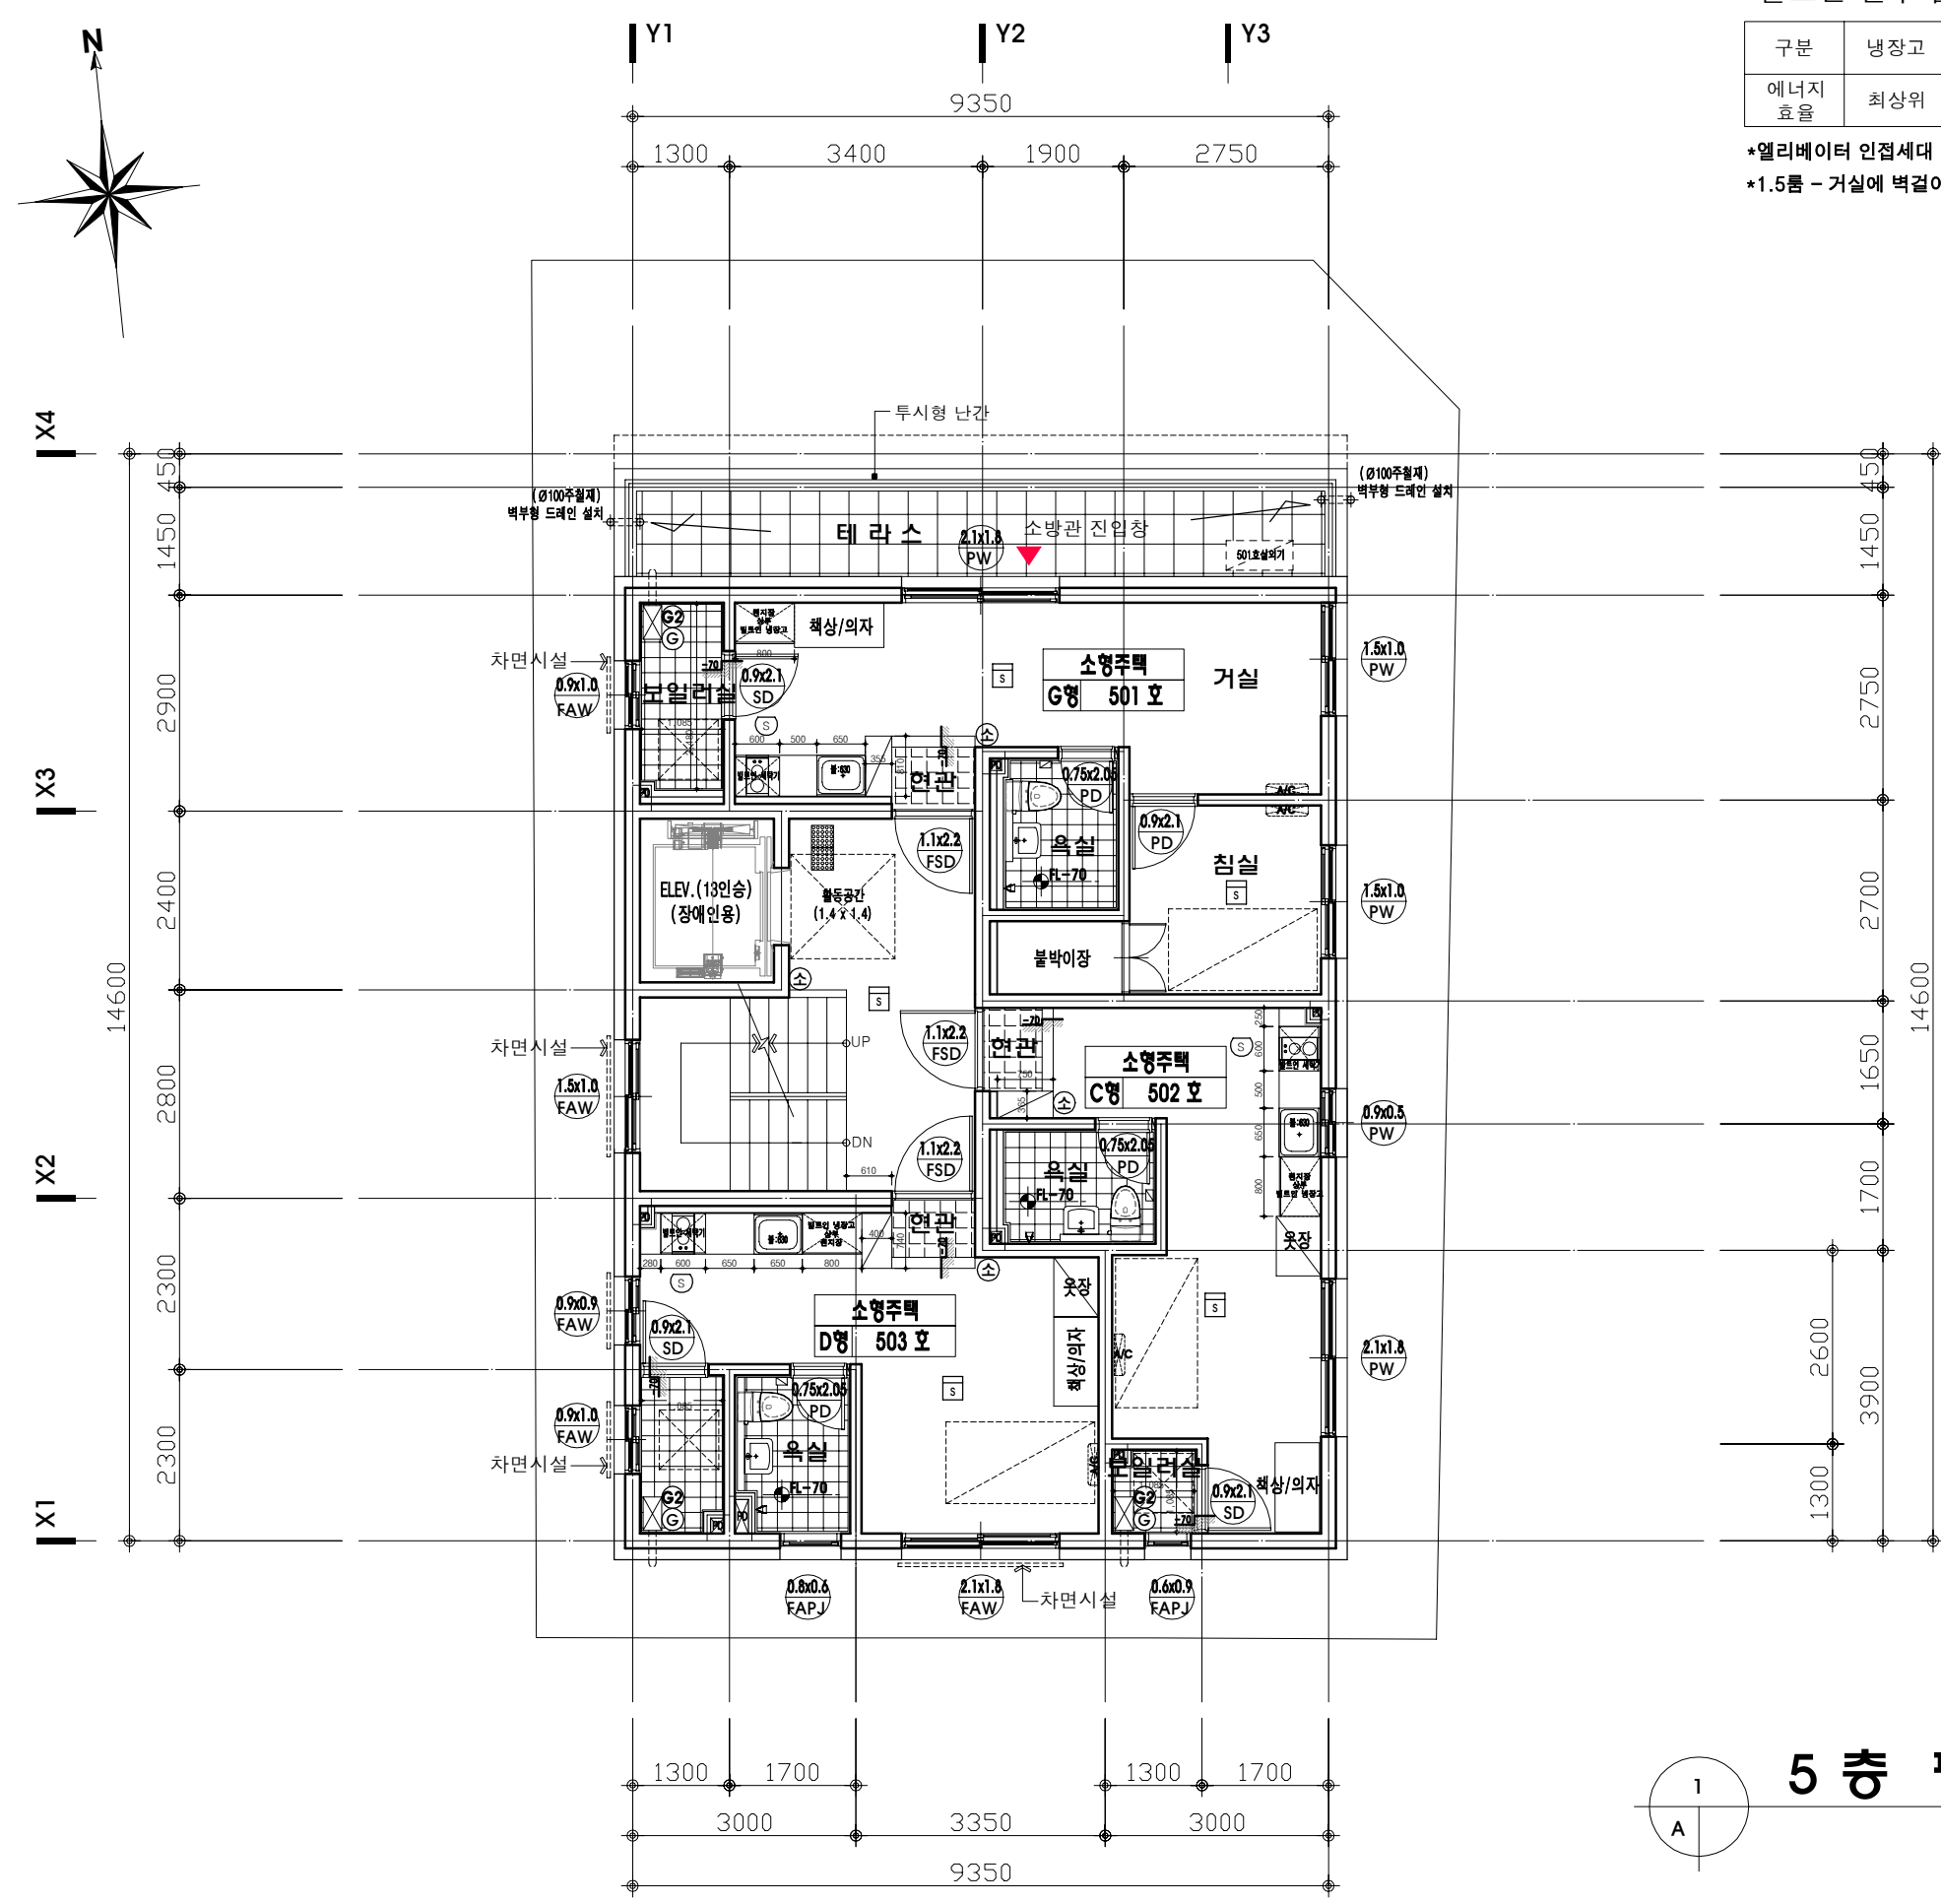

*빌트인 필수 품목

구분	냉장고	벽걸이 에어컨	세탁기	책상	이동식옷장
에너지 효율	최상위	최상위	최상위	-	-

*엘리베이터 인접세대 벽체에 차음시트(3T) 부착
*1.5룸 - 거실에 벽걸이에어컨 빌트인 설치 + 방에 에어컨 배관 설치

1
A

5 층 평면도

SCALE : 1/100

PROJECT TITLE
사 업 명 칭
(만족동 456-55,56)

면목동 도시형생활주택
신축공사

NAME OF DRAWING
도 면 명

5 층 평면도

NOTE
주 기

단독경보감지기(연기)

단독경보감지기(열)

ABC분말소화기(2.5KG)

가스누설경보기

일산화탄소경보기

보일러

벽걸이에어컨

에어컨 실외기

차면시설

1.콘크리트: fck = 27 MPa

2.철근 : fy = 400 MPa

3.세대간벽두께:180mm(복배근)

4.외벽두께:200mm(복배근)

5.코아벽두께:180mm(복배근)

6.스라브두께:210mm(복배근)

(최상층은180mm)

7.욕실, 다용도실-50슬라브다운

DESIGNED BY
설 계

CHECKED BY
심 사

APPROVED BY
승 인

CONSULTANTS
협 동 설 계

SCALE
축 척 1 / 100

DATE
일 자 2025 . 01


DWG NO.
도 면 번 호 A - 204

FILE NAME.
화 일 명

TECH 1 테크원
건축사사무소

TECHONE ARCHITECTS & ENGINEERS
CO., LTD

TEL. 02)482-2466(대)
FAX. 02)488-2466

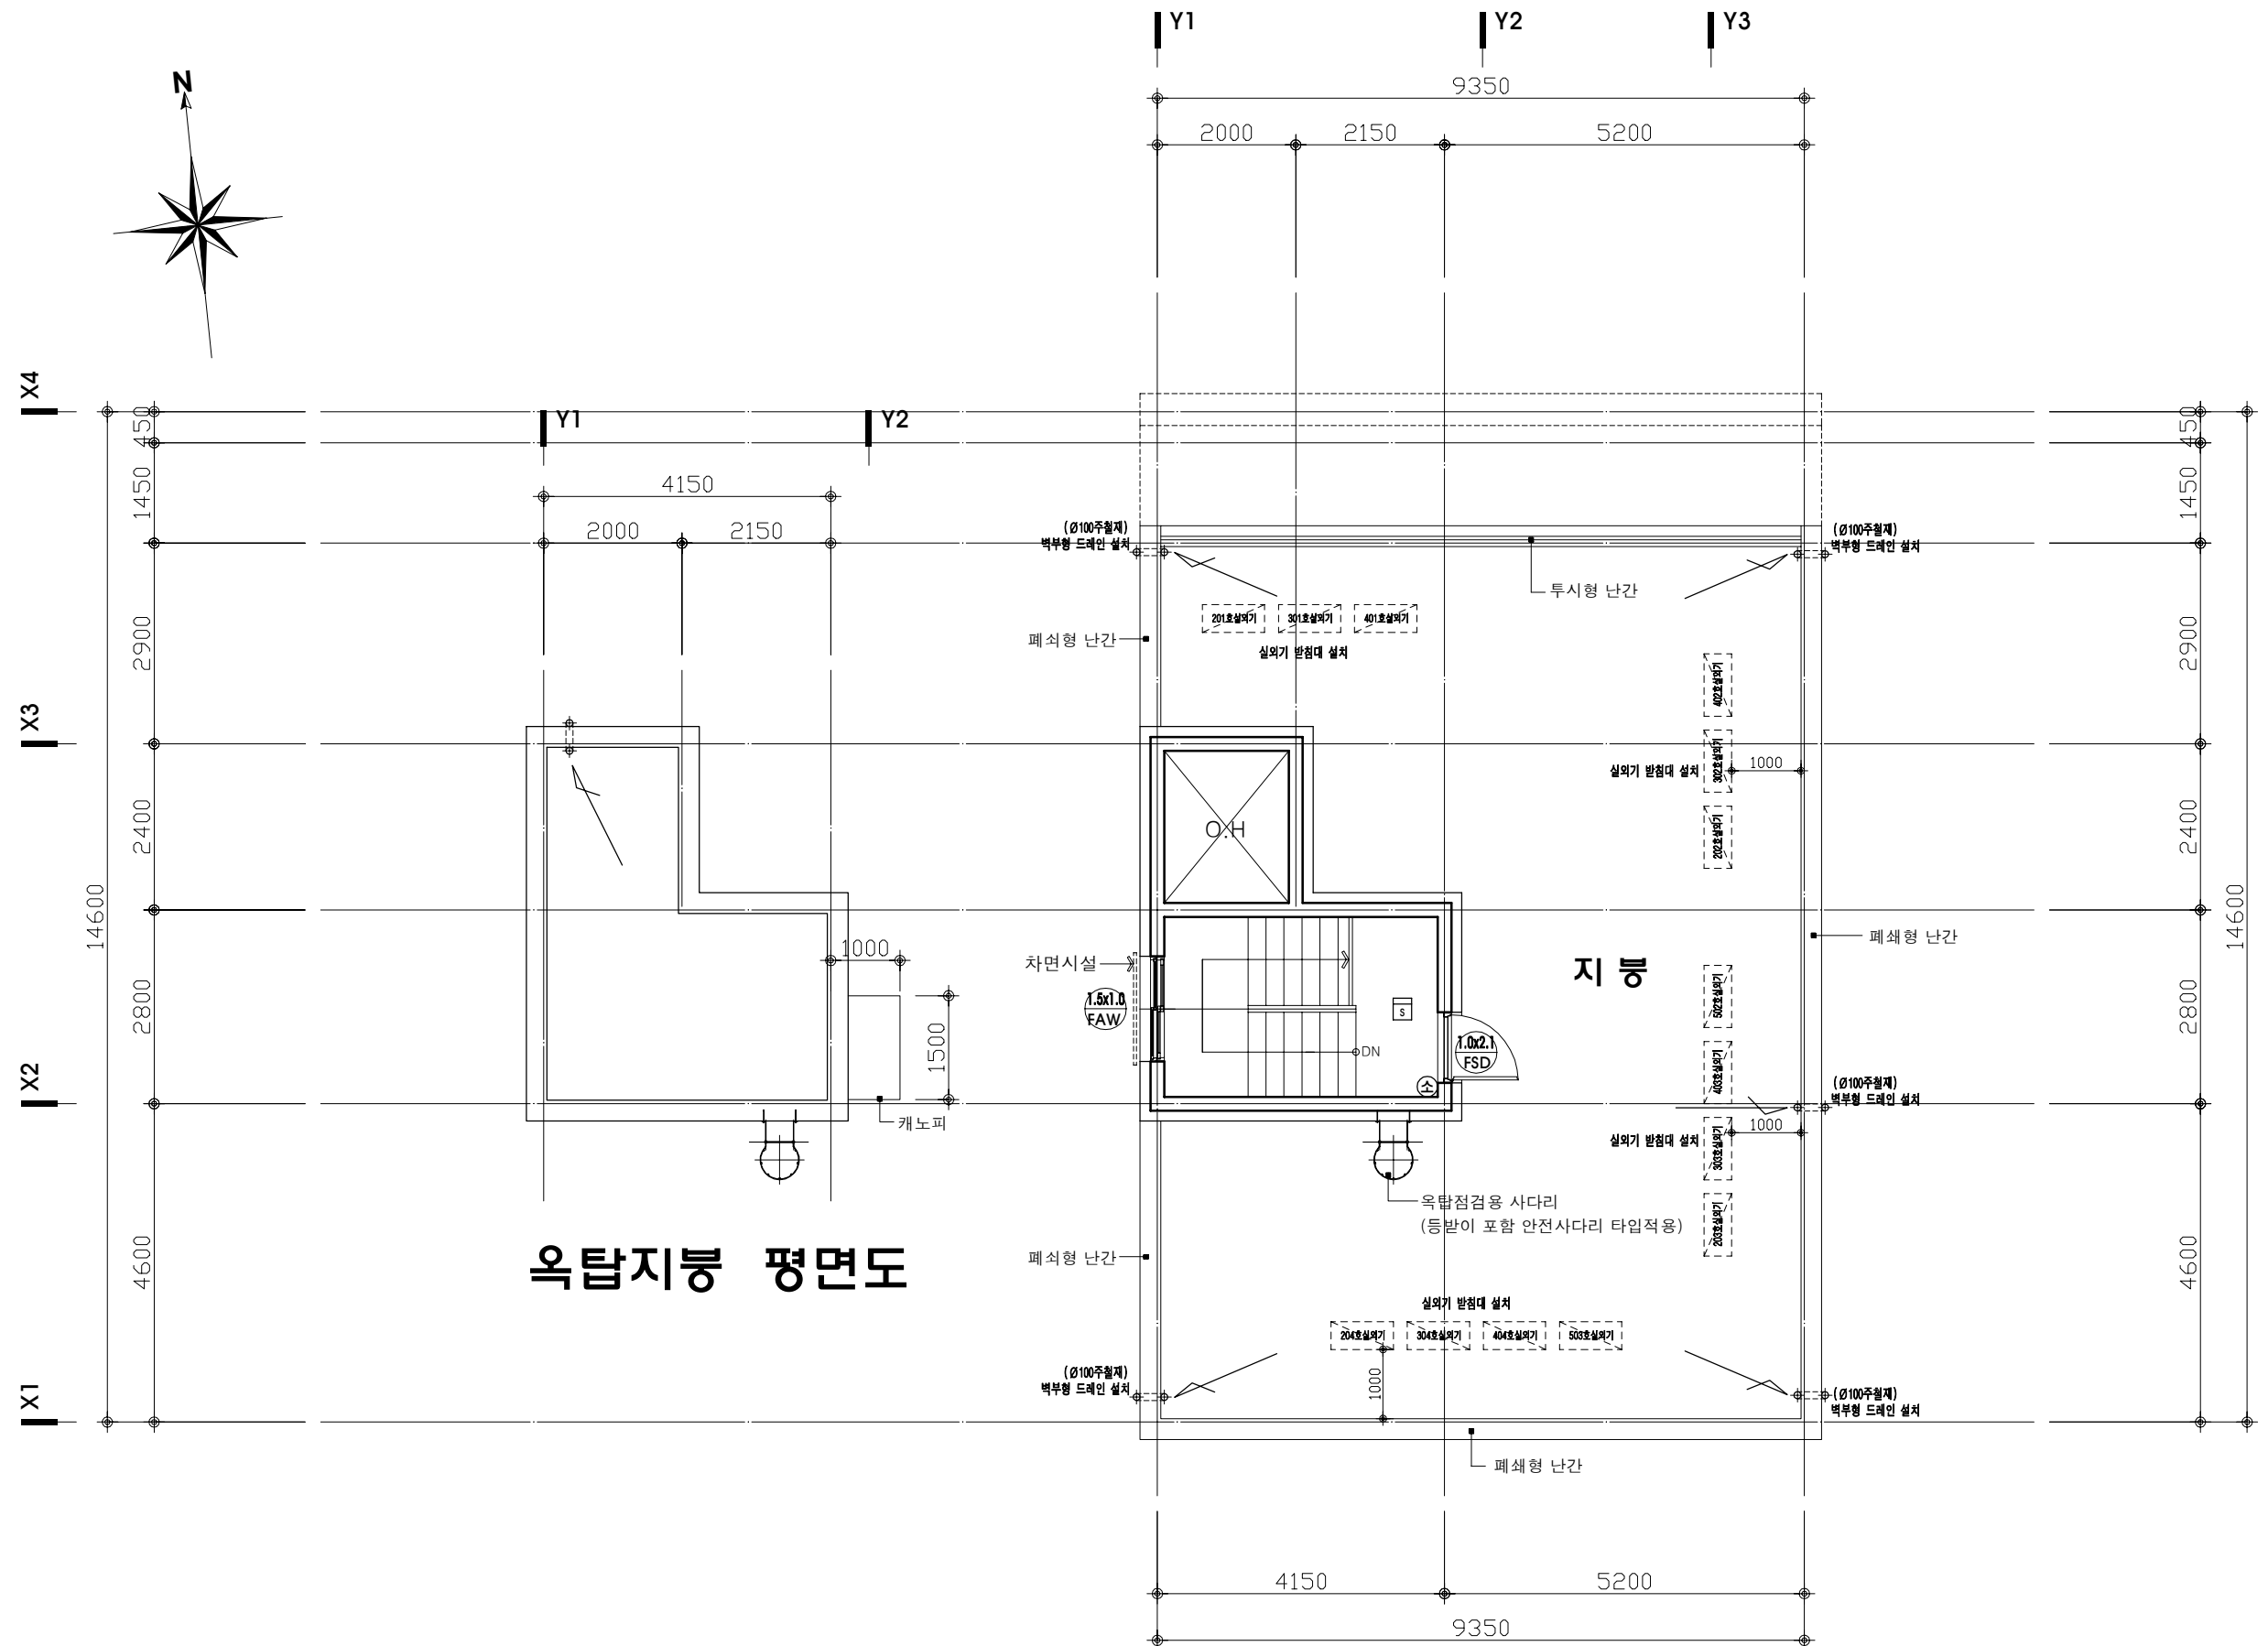

옥탑지붕 평면도

지붕 및 옥탑층 평면도
SCALE : 1/100

PROJECT TITLE
사 입 평
(면적 456-55,56)

면적용 도시형생활주택
신축공사

NAME OF DRAWING
도 면 평

지붕 및 옥탑층 평면도

NOTE
주 기

단독경보감지기(연기)

단독경보감지기(열)

ABC분말소화기(2.5KG)

가스누설경보기

일산화탄소경보기

1.콘크리트: fck = 27 MPa

2.철근 : fy = 400 MPa

3.세대간벽두께:180mm(복배근)

4.외벽두께:200mm(복배근)

5.코아벽두께:180mm(복배근)

DATE
일 자

REVISIONS
수 정

NO.

DESIGNED BY
설 계

CHECKED BY
심 사

APPROVED BY
승 인

CONSULTANTS
합 동 설 계

SCALE
축 척 1 / 100

DATE
일 자 2025 . 01




DWG NO.
도 면 번 호 A - 205

FILE NAME.
파 일 명

TECH 1 테크원
건축사사무소




TECHONE ARCHITECTS & ENGINEERS
CO., LTD

TEL. 02)482-2466(대)
FAX. 02)488-2466

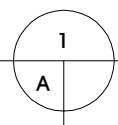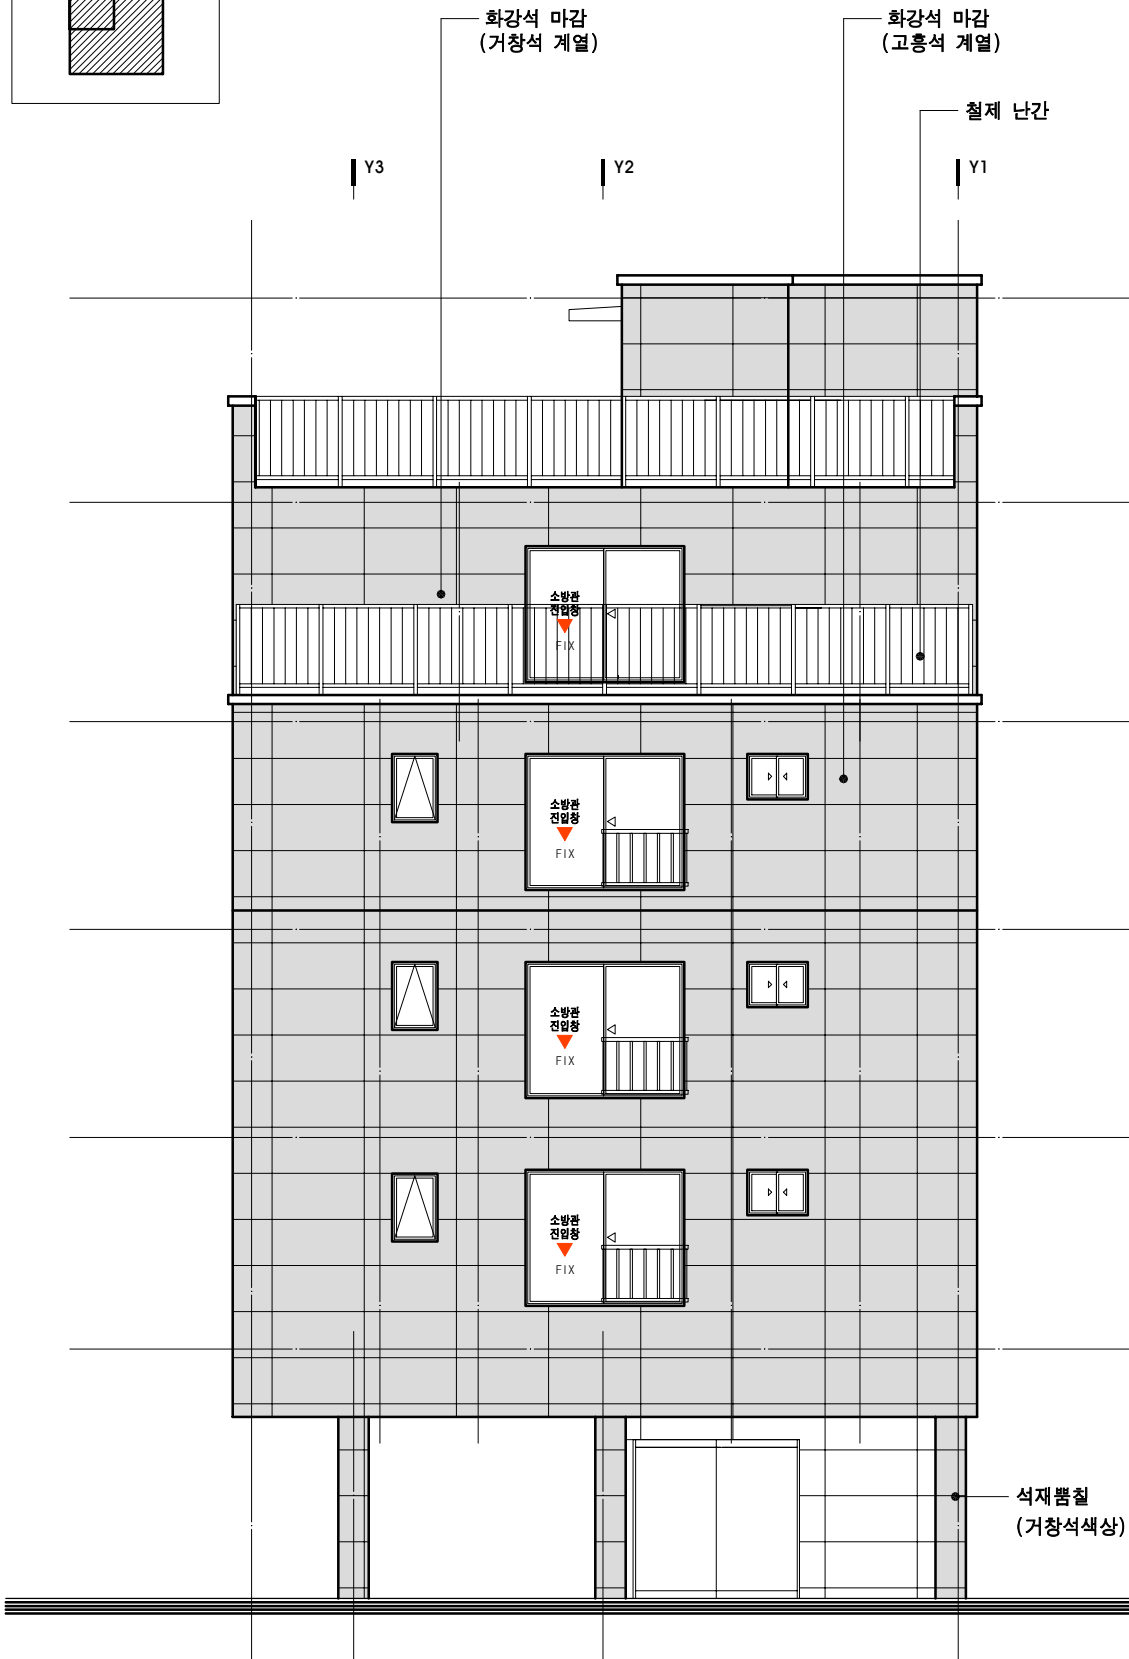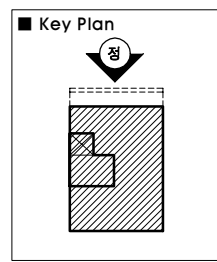

정면도 (북측)


SCALE : 1/100

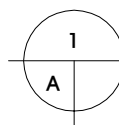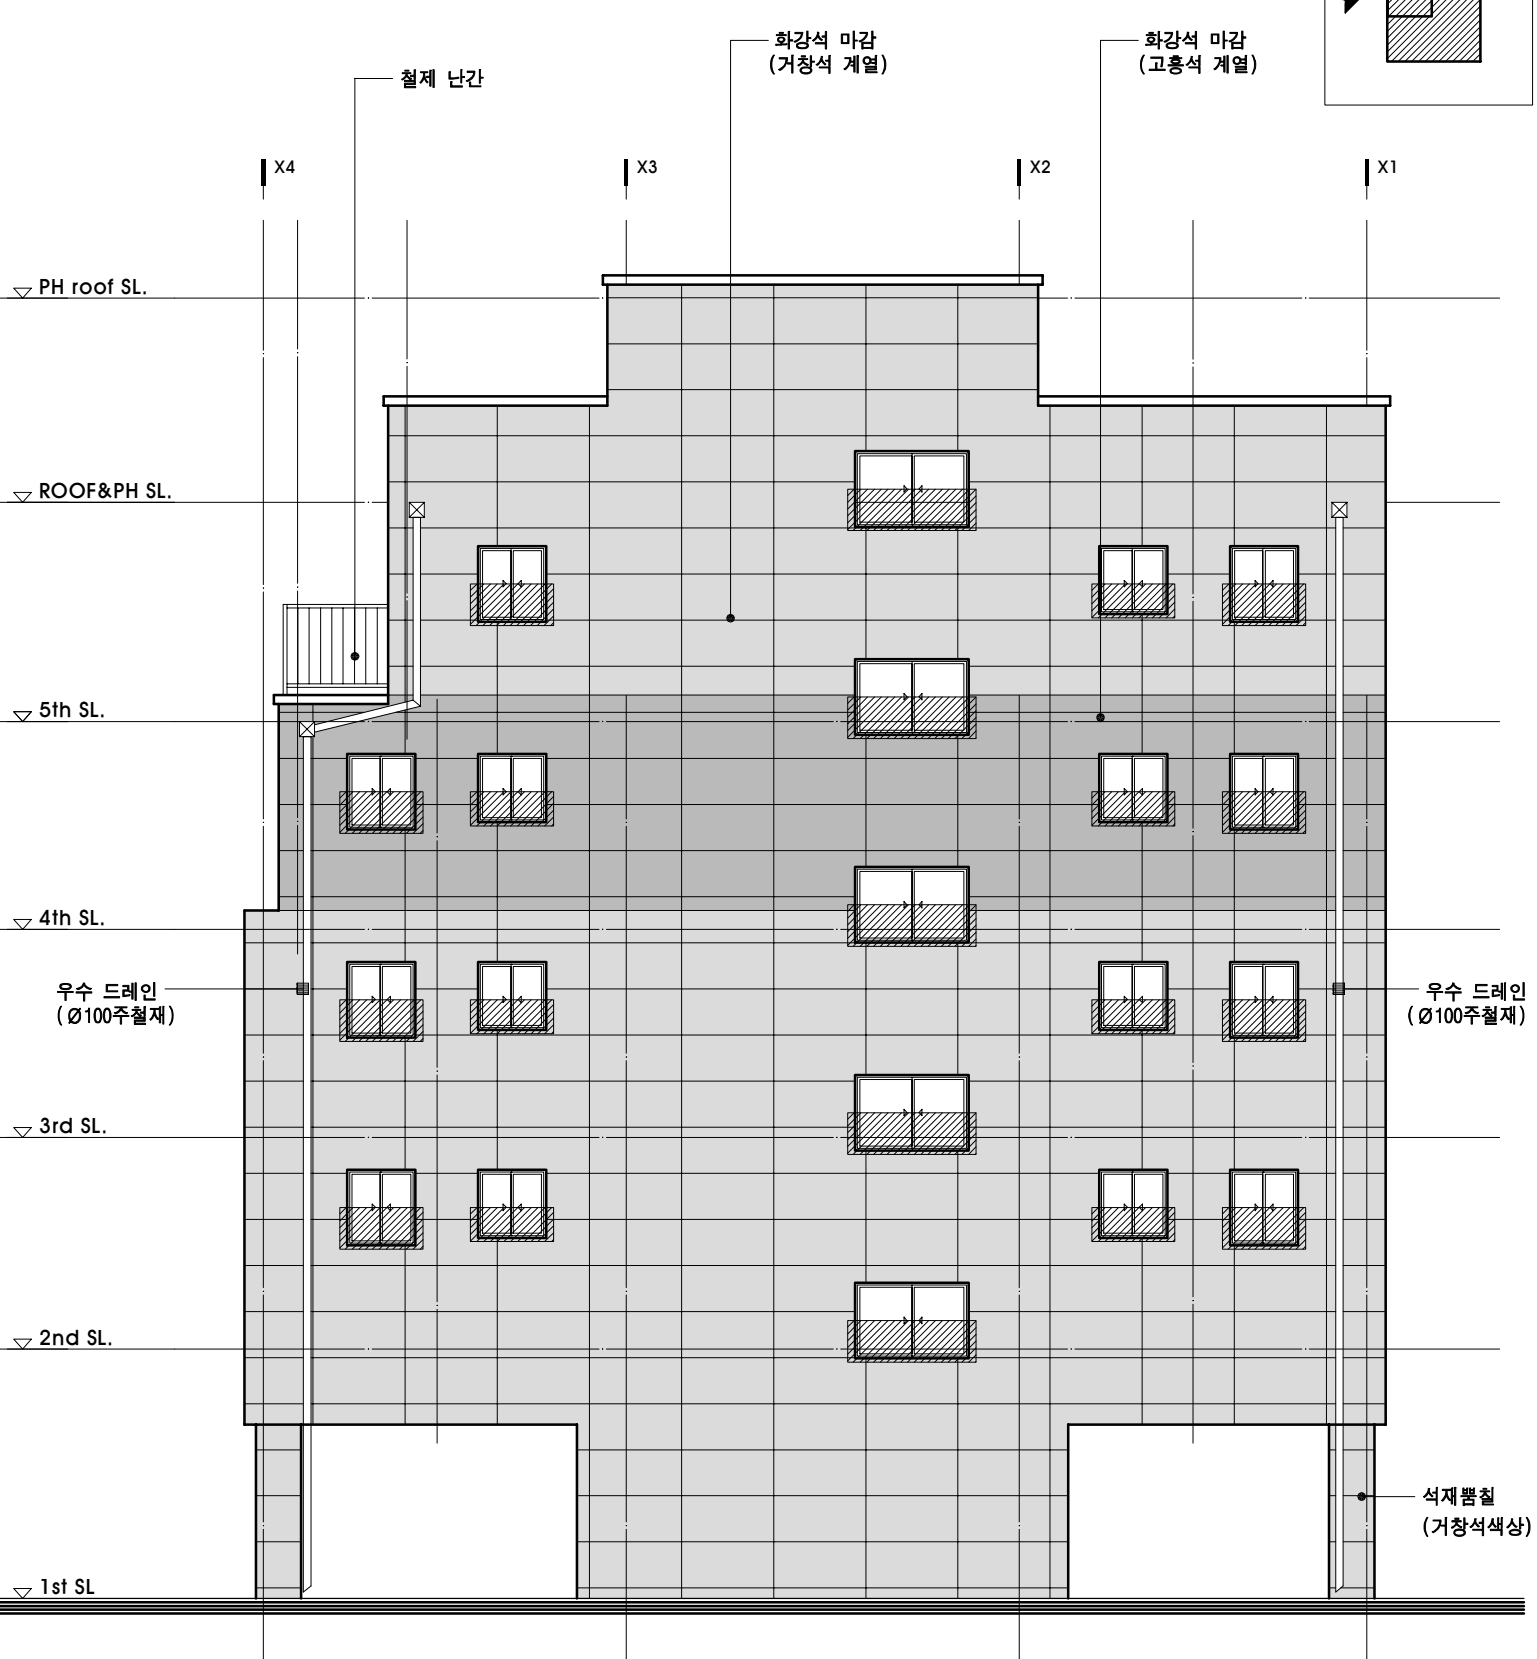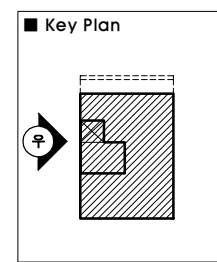



우측면도 (서측)

SCALE : 1/100


PROJECT TITLE 사 입 명 칭 (면적 456-55,56)		
면적 456-55,56		
면적 456-55,56		
NAME OF DRAWING 도 면 명		
정면도 , 우측면도		
NOTE 주 기		
▼ ▼		
창호 PVC 블랙		
소방관전입창 - 스티커부착		

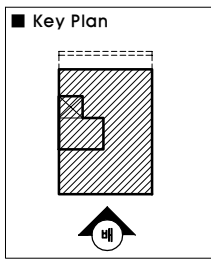

화강석 마감
(거창석 계열)

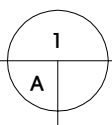
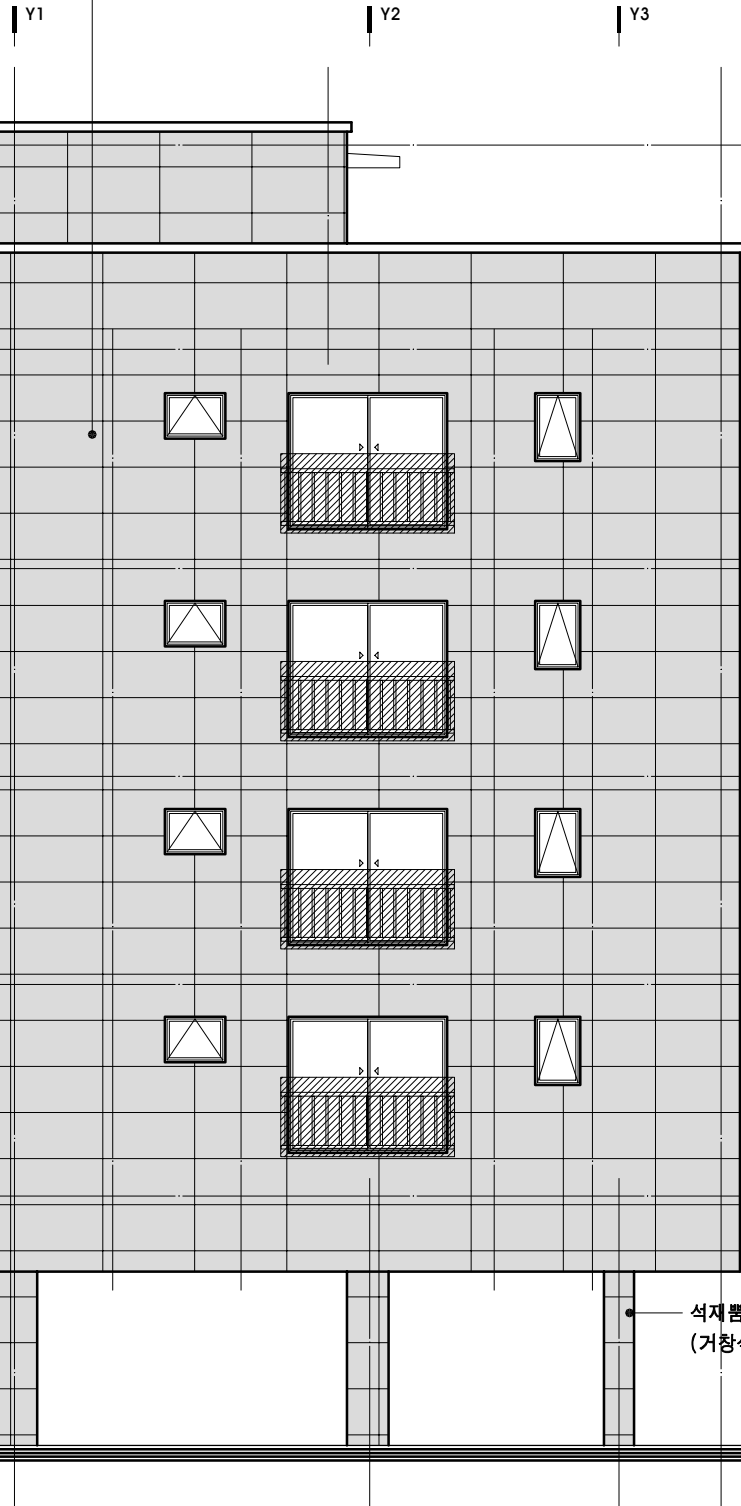


배 면 도 (남측)
SCALE : 1/100

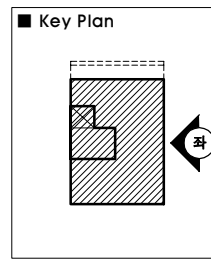

화강석 마감
(거창석 계열)

화강석 마감
(고흥석 계열)

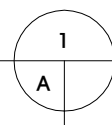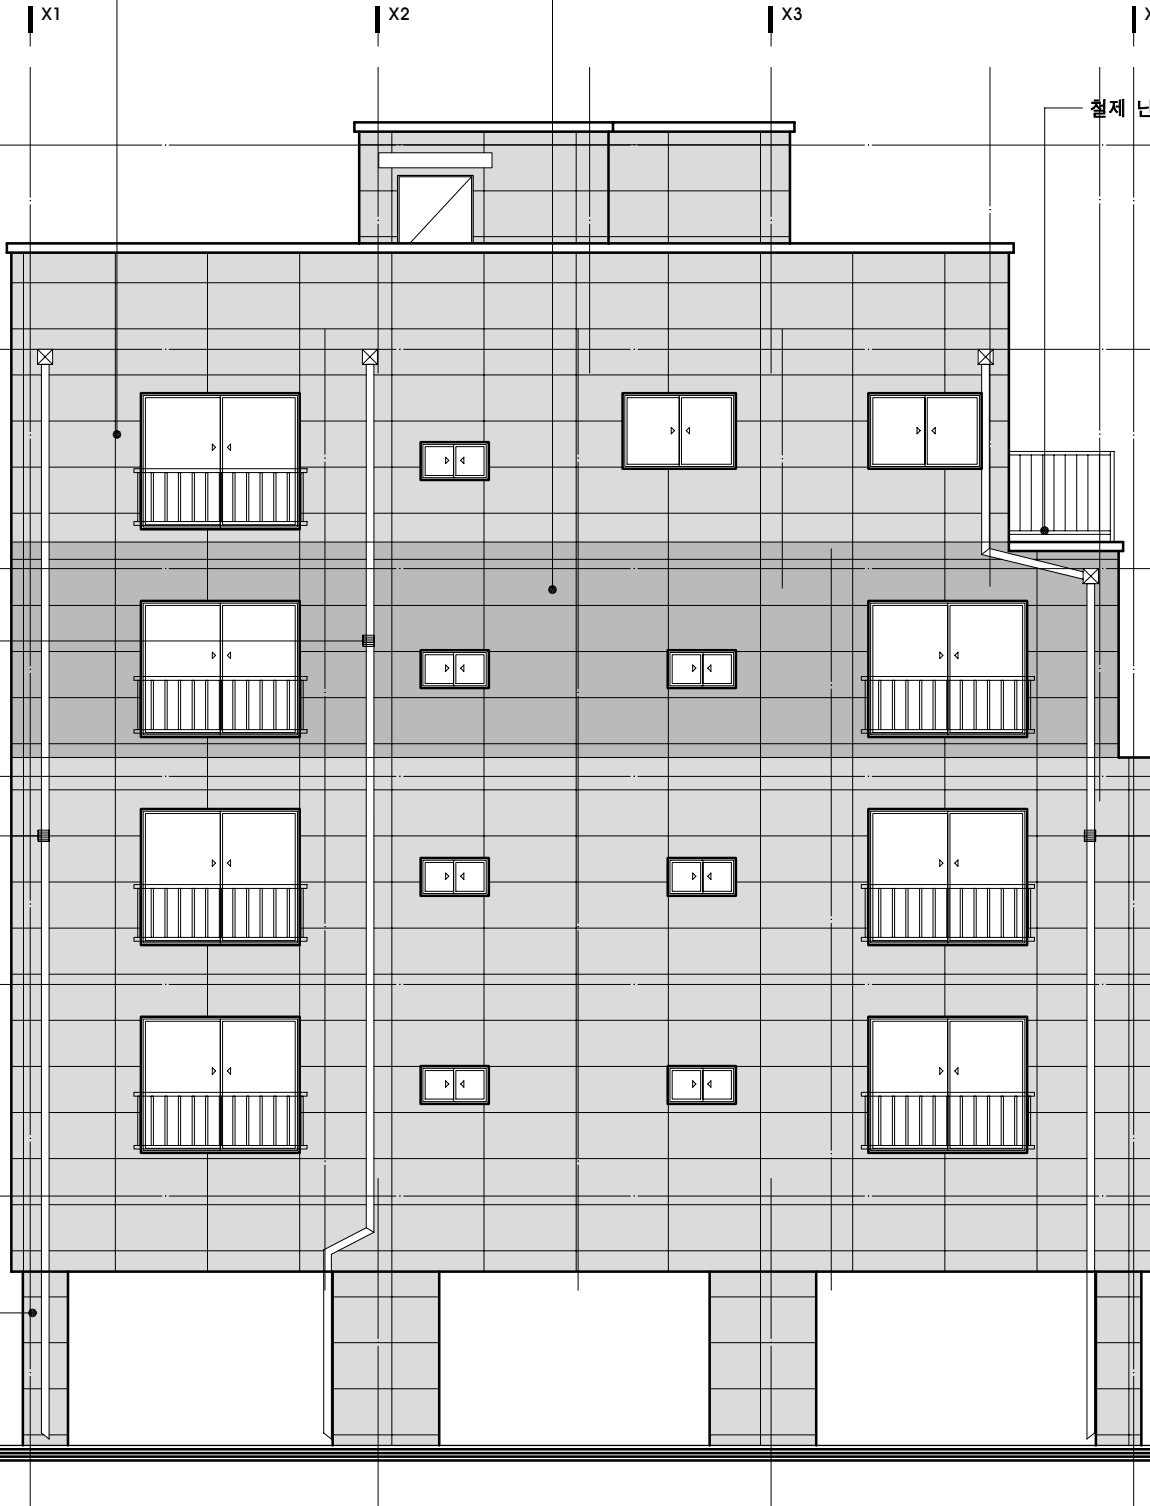

좌 측 면 도 (동측)
SCALE : 1/100

PROJECT TITLE
사 명 명 칭
(면적 456-55,56)

면적동 도시형생활주택
신축공사

NAME OF DRAWING
도 면 명

배면도, 좌측면도

NOTE
주 기

창호 PVC 블랙
소방관진입창 - 스티커 부착

DATE
일 자
REVISIONS
수 정
NO.

DESIGNED BY
설 계

CHECKED BY
심 사

APPROVED BY
승 인

CONSULTANTS
협 동 설 계

SCALE
축 척
1 / 100

DATE
일 자
2025 . 01

DWG NO.
도 면 번 호
A - 302

FILE NAME
화 일 명

TECH 1 테크원
건축사사무소

TECHONE ARCHITECTS & ENGINEERS
CO., LTD.
TEL. 02)482-2466(대)
FAX. 02)488-2466